
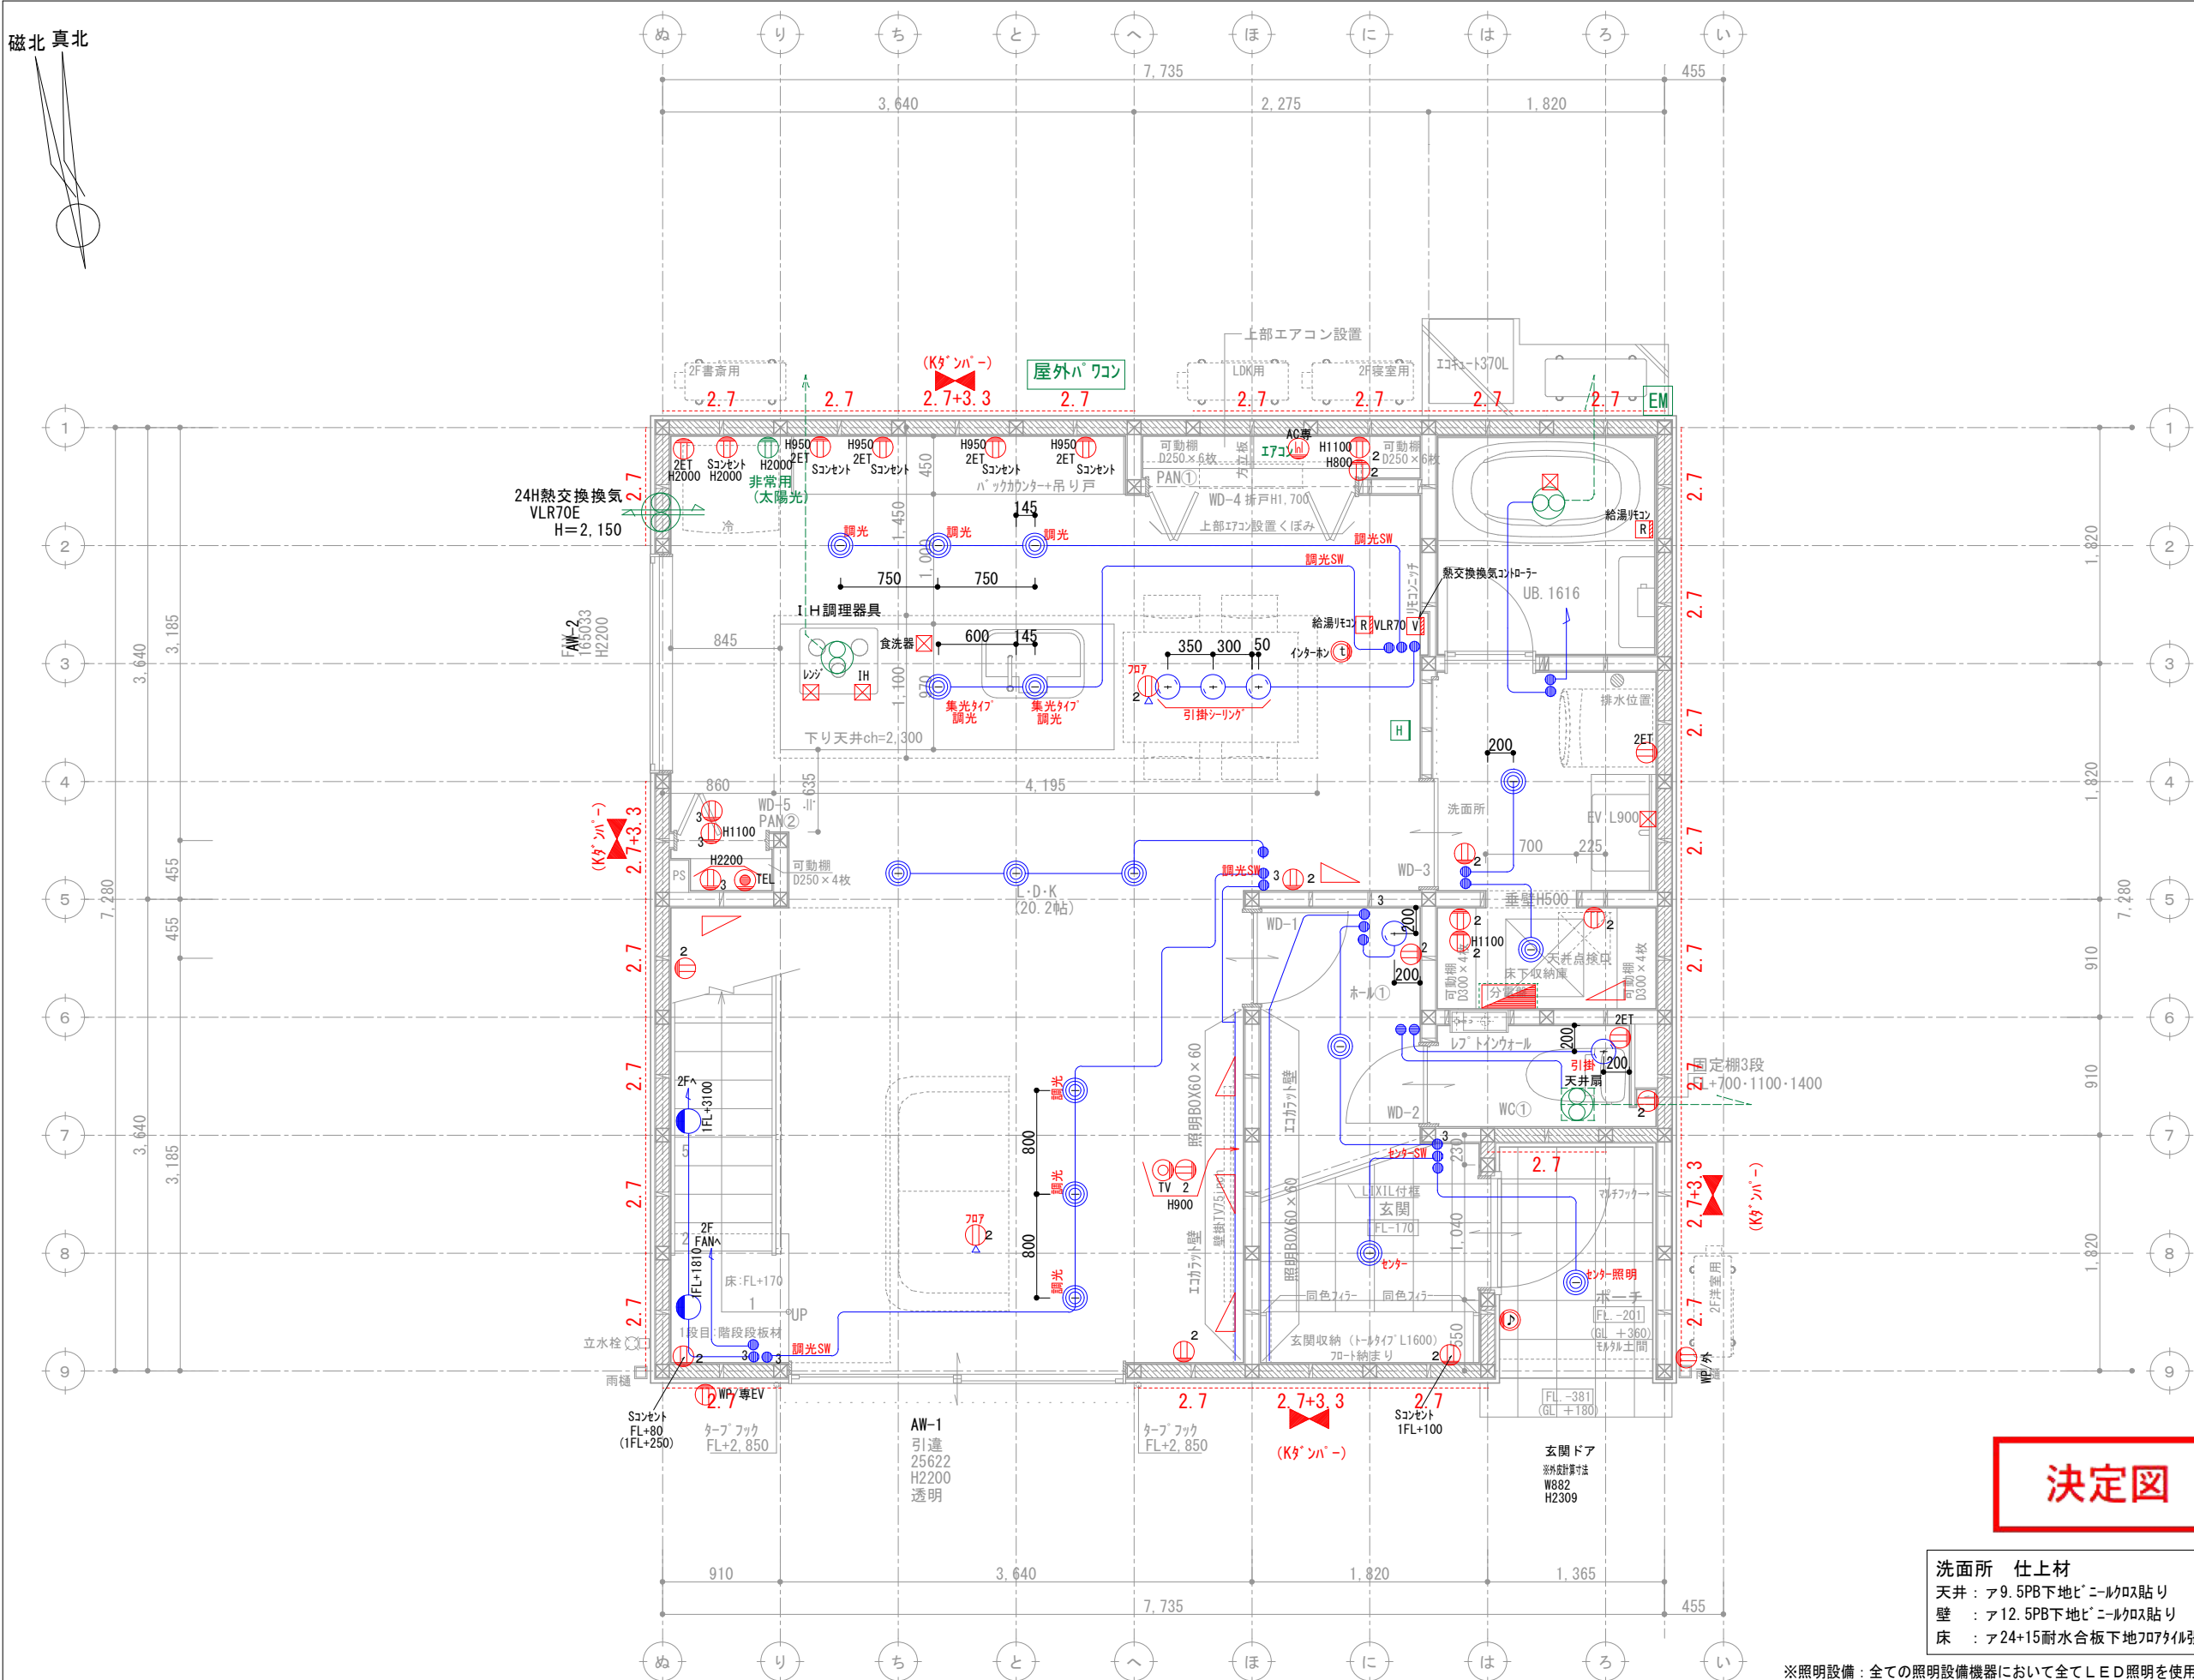


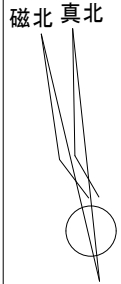

壁付 住宅用火災報知器			数量
H 熱感知	熱感知器	電池式(単独型)	
		露出型	
壁付 住宅用火災報知器			数量
S 煙感知	煙感知器	電池式(単独型)	
		露出型	

※ 煙感知器は壁・梁より600mm以上離す
壁に取付ける場合、
天井から150mm以上500mm以内離す
換気扇・エアコン吹出口から1500mm以上離す
※ 全室LED照明とする。
※ 標準天井高さ2,400

- * 凡例**
- 管柱 (105×105)
 - K'ンバー (3.30倍 FRM-0641)
 - 片筋違い (2.00倍 45×90)
(例 左:柱脚 右:柱頭)
 - たすき掛筋違い (4.00倍 45×90)
 - 構造用合板 (2.70倍)
(t=9 タイプ EXハイパー)
 - 床点検口
 - 天井点検口
 - 換気扇
 - 熱交換換気扇VLR-70

※表記なきガラスは型ガラス

アドバンスシリーズ		
スマートデザイン (外部)		
凡例	1	コンセント 1ヶロ
2	コンセント 2ヶロ	
3	コンセント 3ヶロ	
1ET	コンセント1ヶロ接地ターミナル付	
2ET	コンセント2ヶロ接地ターミナル付	
WP	コンセント 防水型	
エアコン	エアコン用コンセント	
200V	200V用コンセント	
WP	防雨入線プレート	
WP	防雨入線プレート	
スイッチ	スイッチ	
3	3路スイッチ	
4	4路スイッチ	
直結電源	直結電源	
TV	テレビ取出口 (テレビホリ)	
TEL	電話取出口 (テレビホリ)	
LAN	LAN取出口 (テレビホリ)	
壁照明	壁照明	
リモコン	リモコン (給湯関係・ルフロ)	
メーター	メーター	
分電盤	分電盤	
チャイム	チャイム	

※ACコンセント天井付け
※TVアンテナ工事
※スイッチはFL+1100、コンセントはFL+200

決定図

洗面所 仕上材
天井 : ア9.5PB下地ビニールクロス貼り
壁 : ア12.5PB下地ビニールクロス貼り
床 : ア24+15耐水合板下地フロアタイル張り

※照明設備 : 全ての照明設備機器において全てLED照明を使用している