


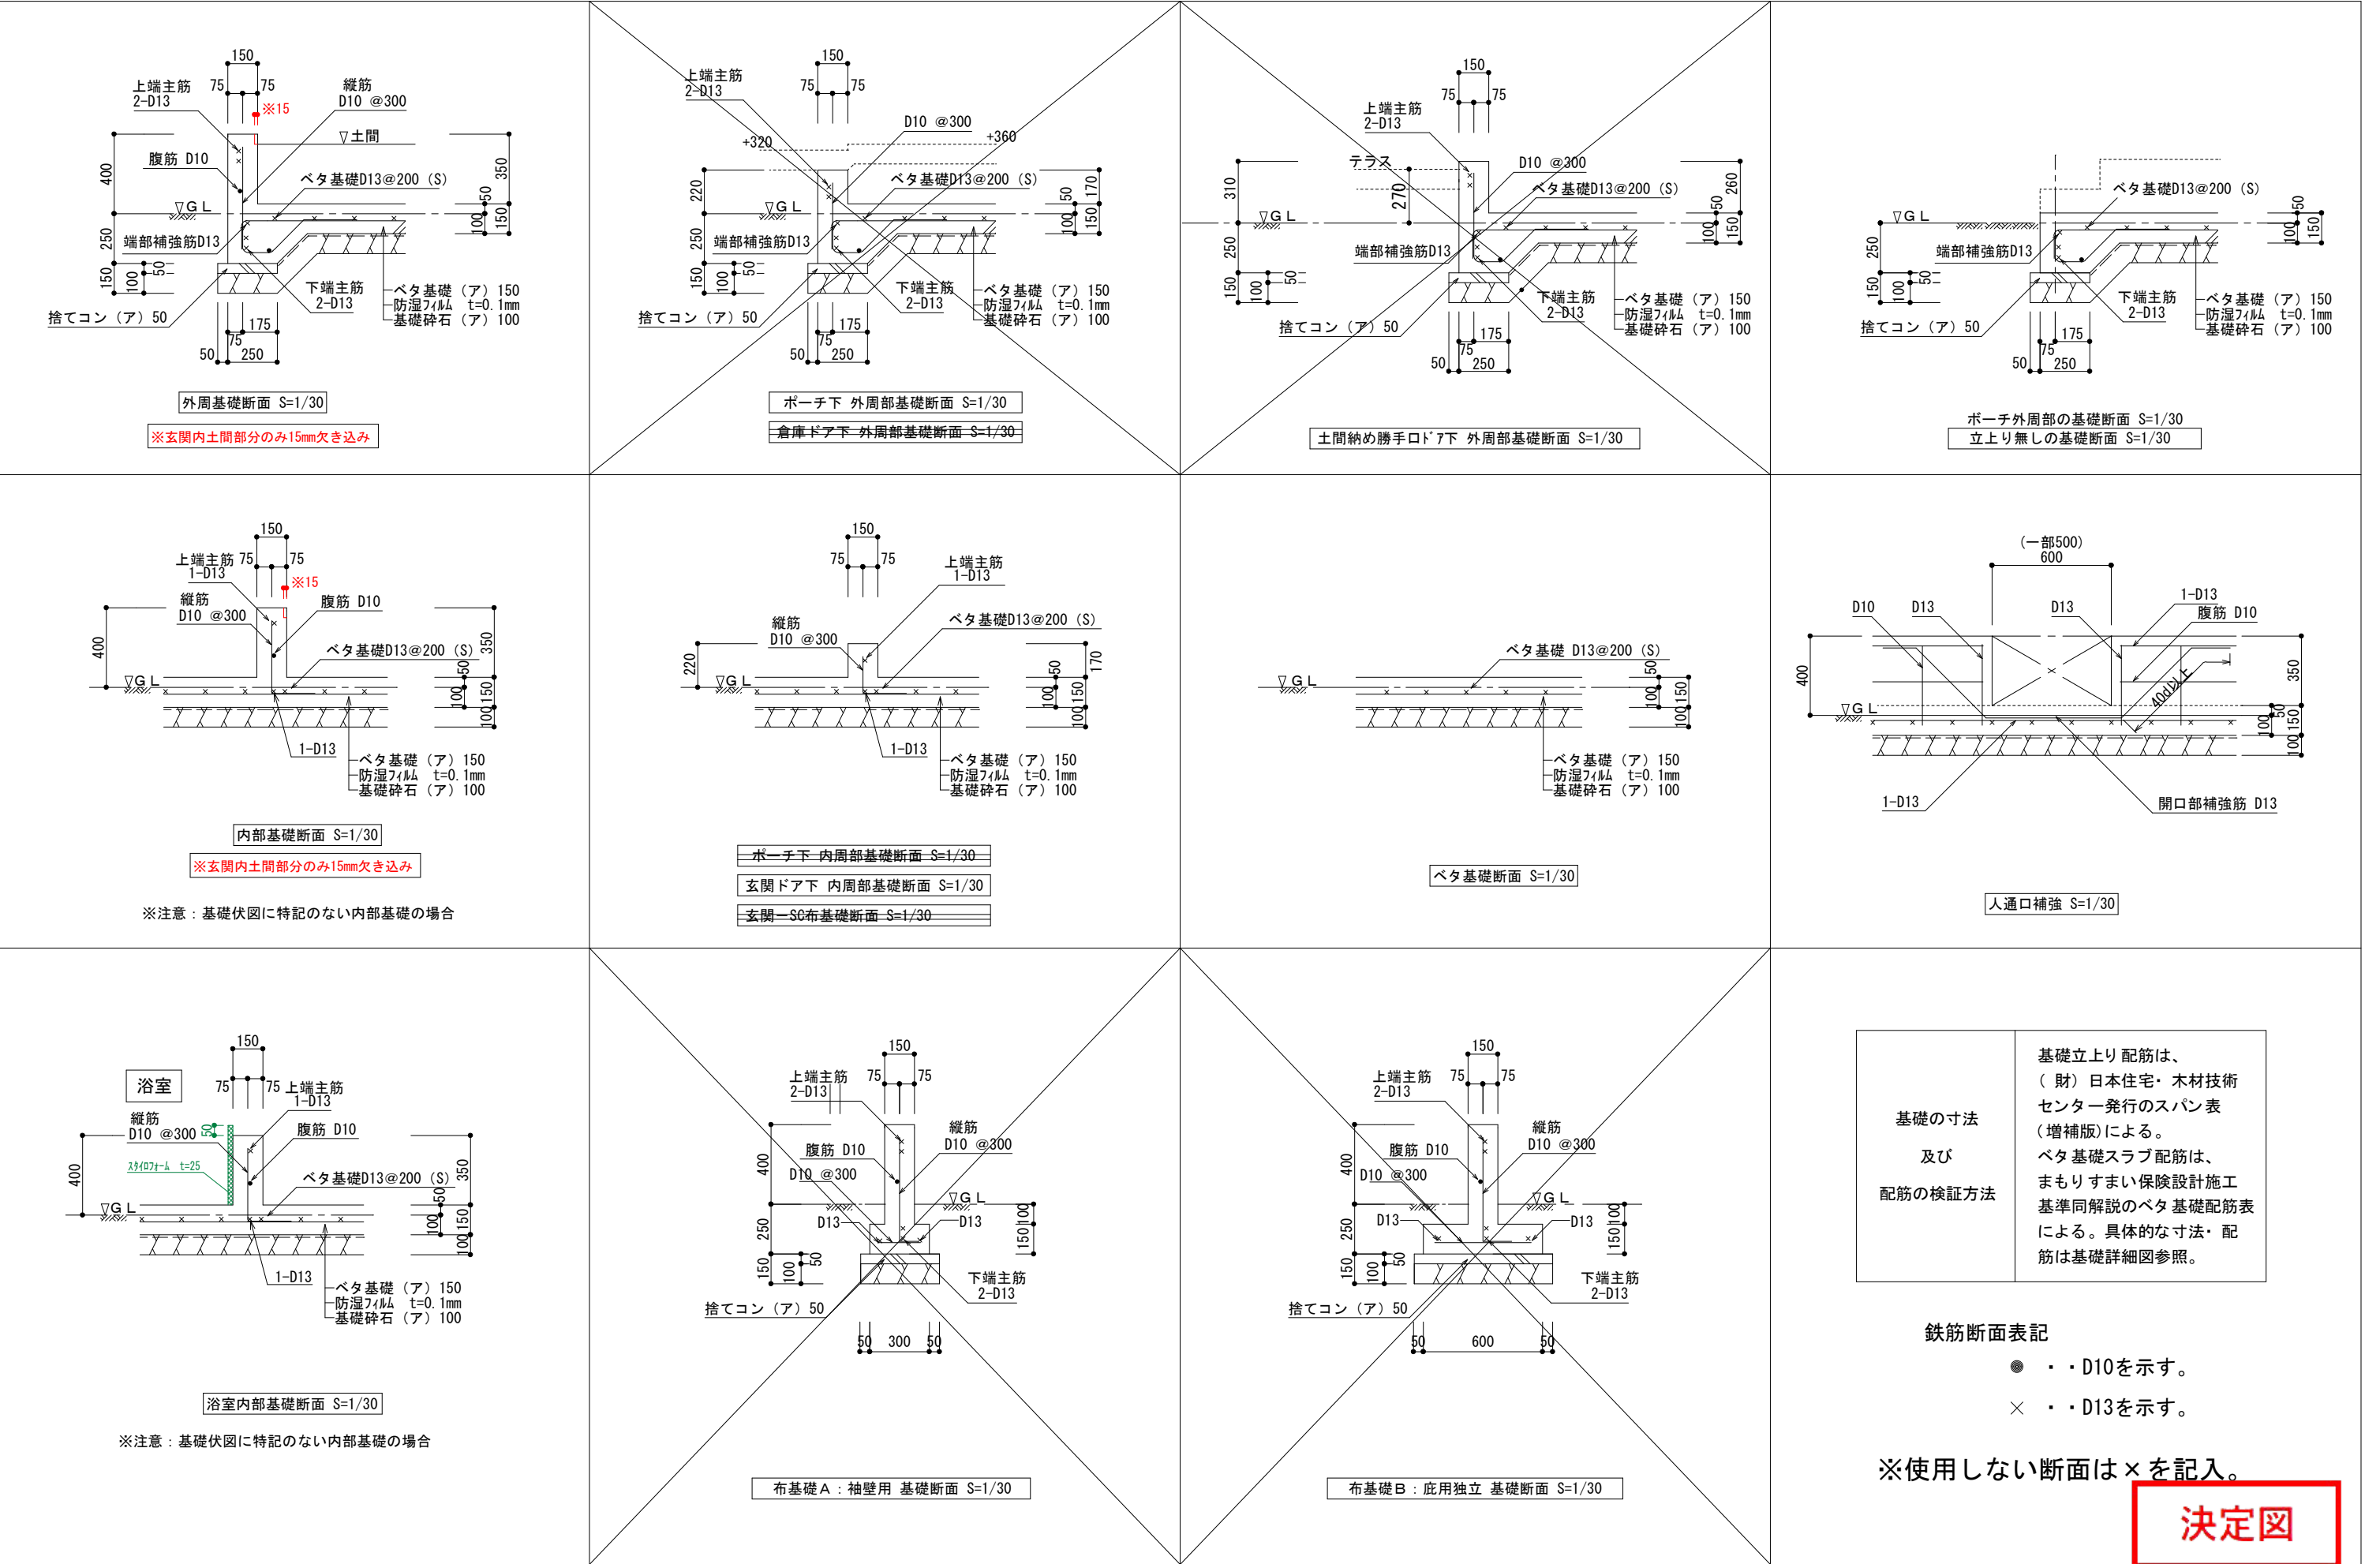

訂 正	浜 岡 一 級 総 合 設 計 事 務 所		株式会社 LIFEFUND InDesign office	一級建築士事務所	年 月 日	件 名		設計	I C	工務	図 番
	一級建築士事務所 静岡県知事登録第 (10)2441 号		事務所登録 (2)第7595号	一級建築士登録 第179770号	鈴木 達男	2024. 12. 10		竹内優太郎様邸 新築工事	倉田	青島	B-2
	一級建築士 大臣登録第 365879 号 西原利昌		〒432-8023 静岡県浜松市中央区鴨江3丁目7番23号		縮 尺	図 名		基礎断面リスト			
					1/30						

決定図