


基準線



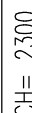


【 ご注意 】 ●記載のキャビネット寸法は扉前面までの呼び寸法です。キャビネット本体の寸法・扉厚み等は商品ガイドの巻末資料をご確認ください。 ●記載のワークトップ、カウンター、エンドパネル、サイドパネルの寸法は呼び寸法です。詳細寸法は商品ガイドの巻末資料をご確認ください。 ●レンジフード電源プラグ仕様：3芯電源プラグ（アース工事が必要です。） ●VVFケーブルの太さにつきましては、内線規程に準じてください。				
案件No.	図面名	担当	図面	図番：
09DD0E4U3C	レイアウト図	栗野 友仁		株式会社 LIXIL
見積No.	縮尺	日付		
05149774-008-2	1/30	2024.10.29		


面

C面

D面

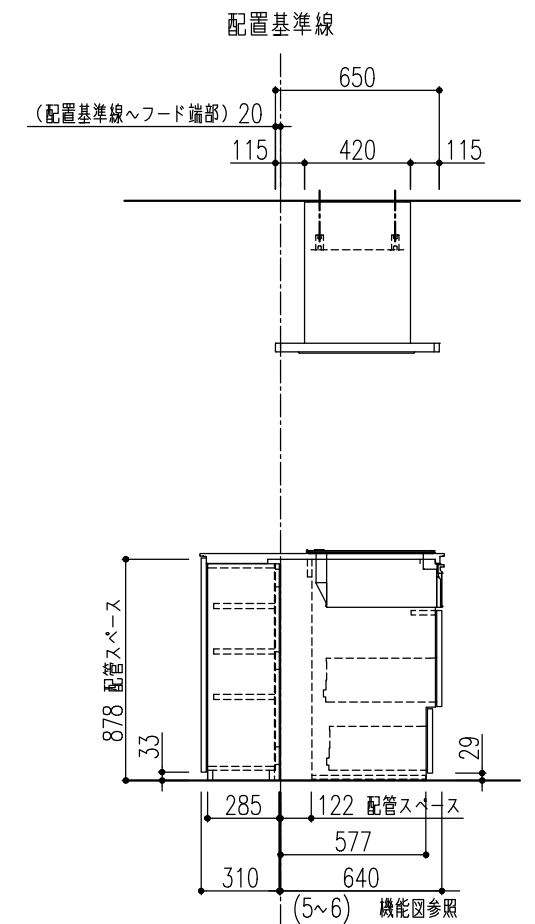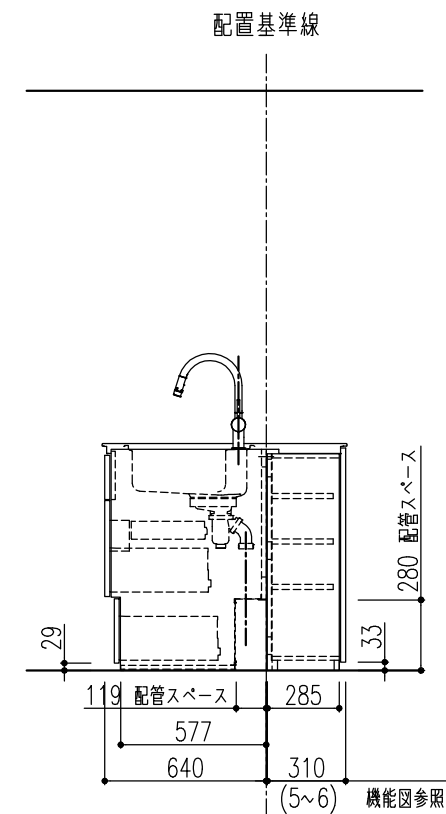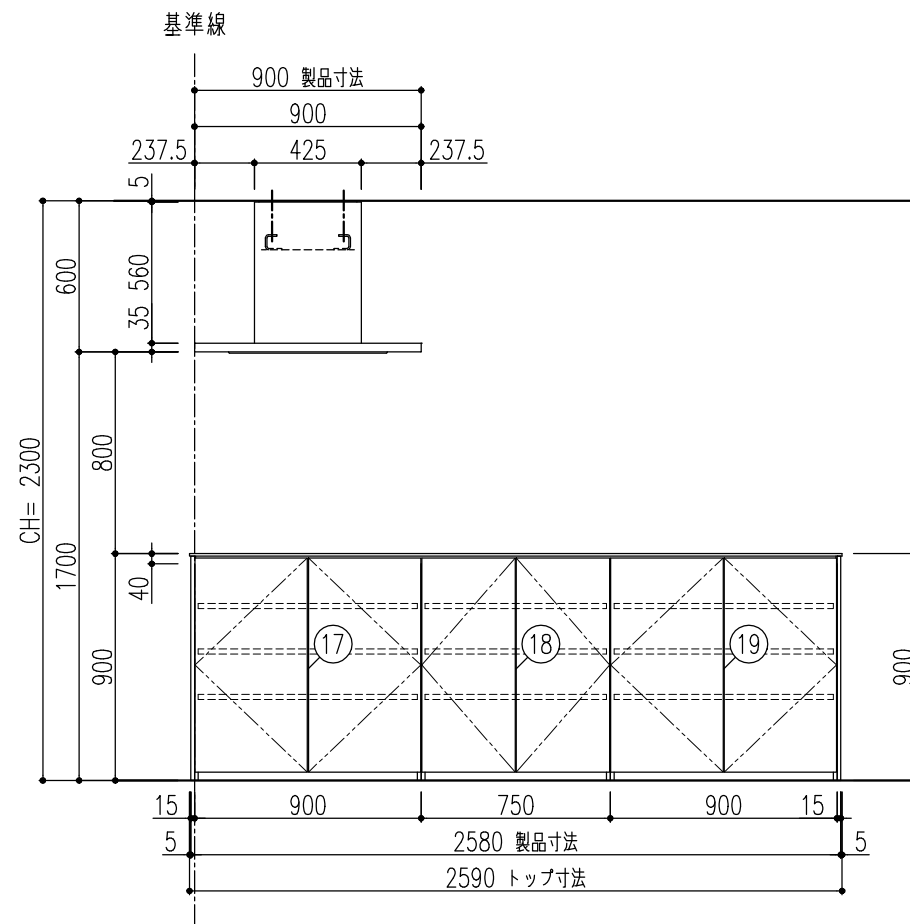

特記事項 扉色 KL1:ソリッドブラック 取手 [S]ミドル取手S (ブラック) ワークトップカラー 【BK】ブラックストーン	物件名	竹内陽子 様邸【10/29ご来館】	案件No.	図面名	担当	図面	図番
			A2409DDD0E4U3C	レイアウト図	栗野 友仁		
	仕様	ND23	見積No.	縮尺	日付		株式会社 LIXIL
			M24095149774-008-2	1/30	2024.10.29		

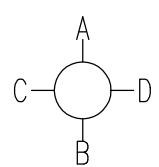[illegible]

注1) 100V・15A 電源線取出し推奨位置(3.0M出し)【専用】※配管スペース内であれば他位置でも可
【ご注意】



- 記載のキャビネット寸法は扉前面までの呼び寸法です。キャビネット本体の寸法・扉厚み等は商品ガイドの巻末資料をご確認ください。
- 記載のワークトップ、カウンター、エンドパネル、サイドパネルの寸法は呼び寸法です。詳細寸法は商品ガイドの巻末資料をご確認ください。
- 電気・ガス・給排水・換気等は法令・規定に従って有資格者が行ってください。
- 水道工事は排水配管工事となります。
- 取付・設置に際し、各製品の取付・設置説明書や図面の機能図を必ずお読み下さい。
- レンジフード用の下地処理工事と吊ボルトの設置工事は大工事になります。
- 内線規程上、各機器のプラグ仕様に関わらず建築側には接地極付コンセントを推奨しています。
- レンジフード電源プラグ仕様：3芯電源プラグ（アース工事が必要です。）
- 食器洗い乾燥機配管は、給水接続か給湯接続かお客様に確認したうえで施工願います。
- 食洗機内配管の詳細については必ず別添の機能図をご確認ください。
- VVFケーブルの太さにつきましては、内線規程に準じてください。

特記事項 扉色 KL1:ソリッドブラック 取手 [S]ミドル取手S(ブラック) ワークトップカラー 【BK】ブラックストーン	物件名 竹内陽子 様邸【10/29ご来館】	案件No.	図面名	担当	図面	図番 : 株式会社 LIXIL
		A2409DDD0E4U3C	納まり図	栗野 友仁		
	仕様 ND23	見積No.	縮尺	日付		
		M24095149774-008-2	1/30	2024.10.29		

A面

B面



- 注2) 125V・15A 2極接地極付アースターミナル付コンセント 【専用】（フード用）
注3) 125V・15A 2極接地極付アースターミナル付コンセント 【専用】
注4) 250V・30A 2極接地極付コンセント（側板取付）【専用】

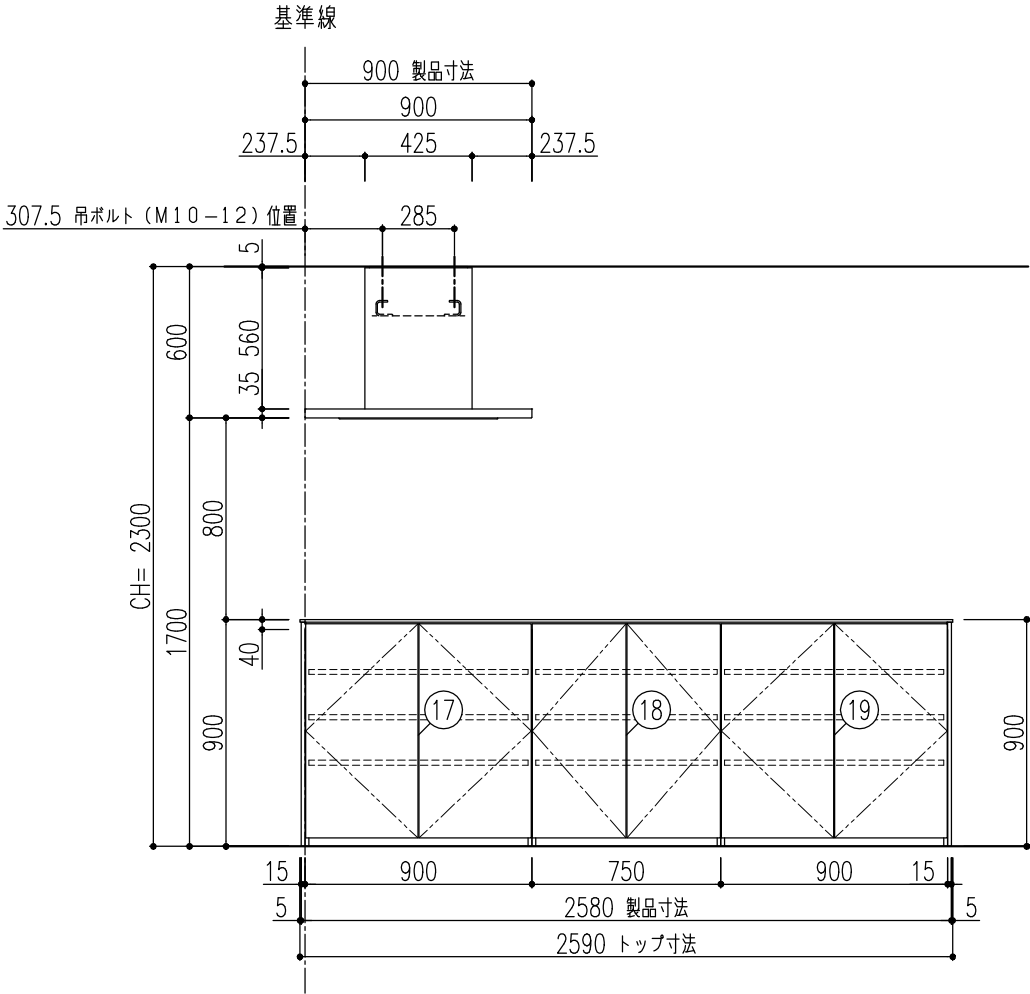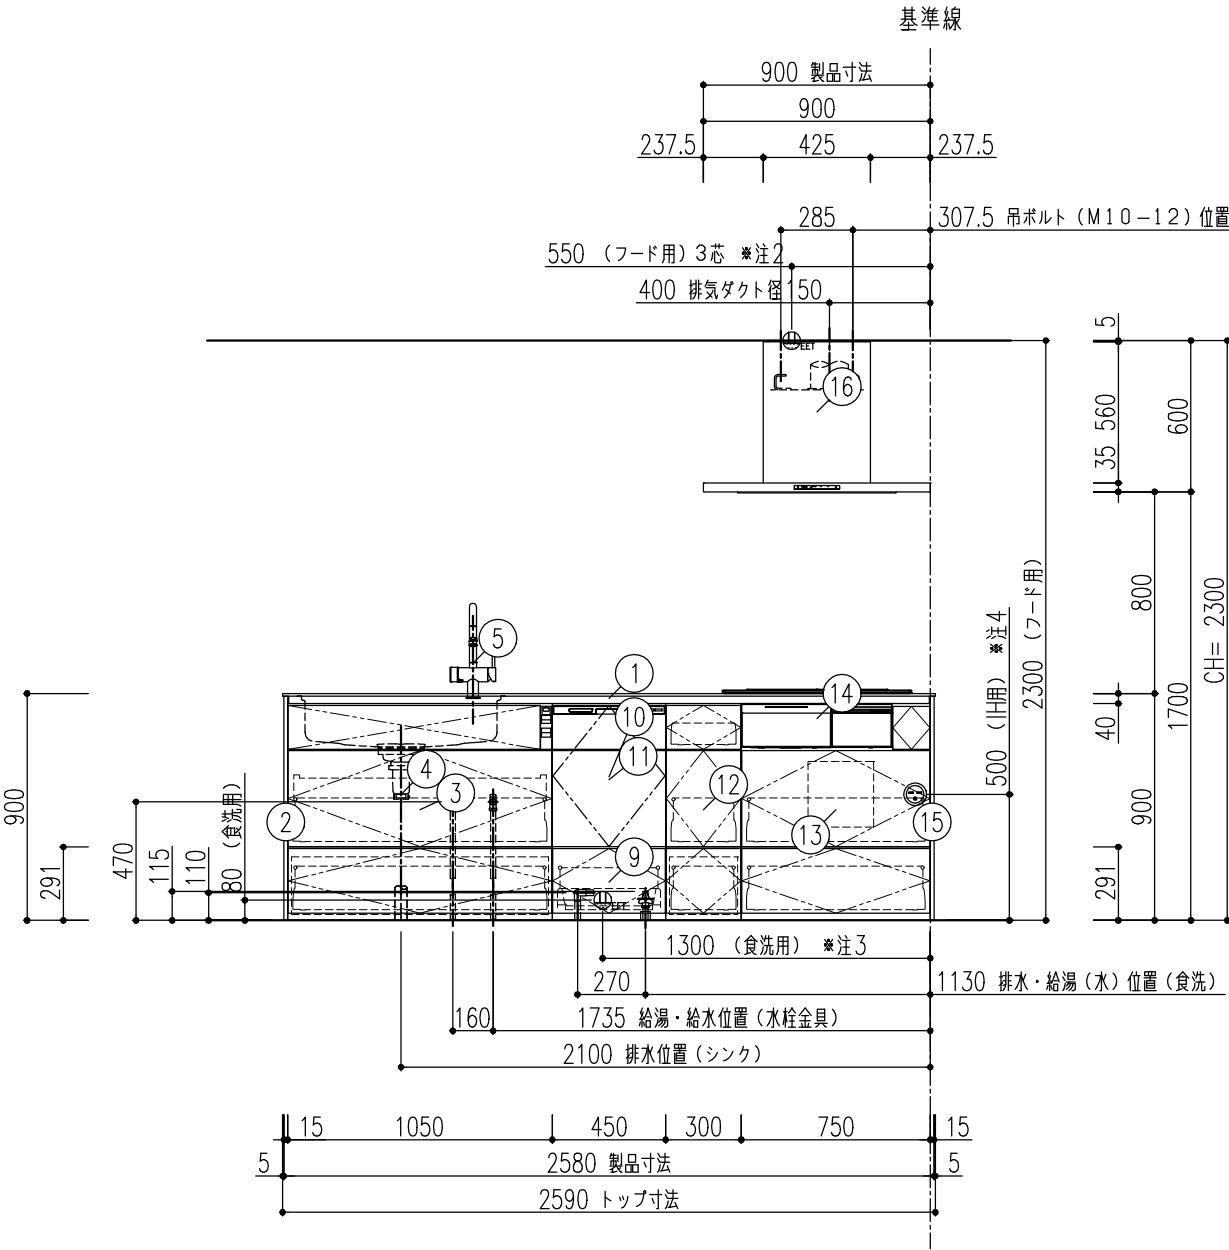

	特記事項 扉色 KL1:ソリッドブラック 取手 [S]ミドル取手S (ブラック) ワークトップカラー 【BK】ブラックストーン	物件名	竹内陽子 様邸【10/29ご来館】	案件No.	図面名	担当	図面	図番
				A2409DDD0E4U3C	納まり図	栗野 友仁		株式会社 LIXIL
		仕様	ND23	見積No.	縮尺	日付		
				M24095149774-008-2	1/30	2024.10.29		


C面

D面

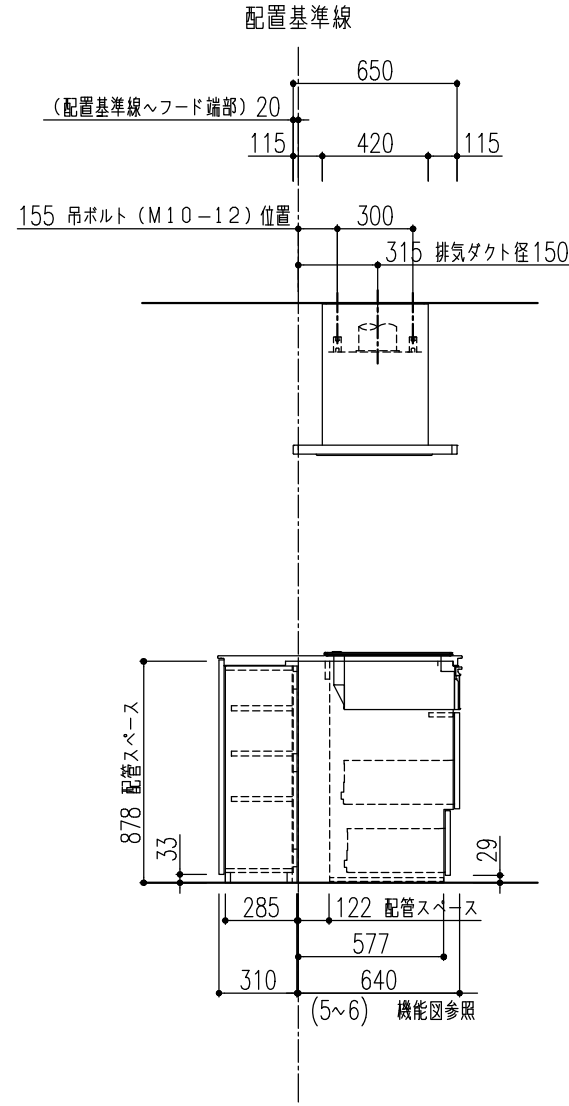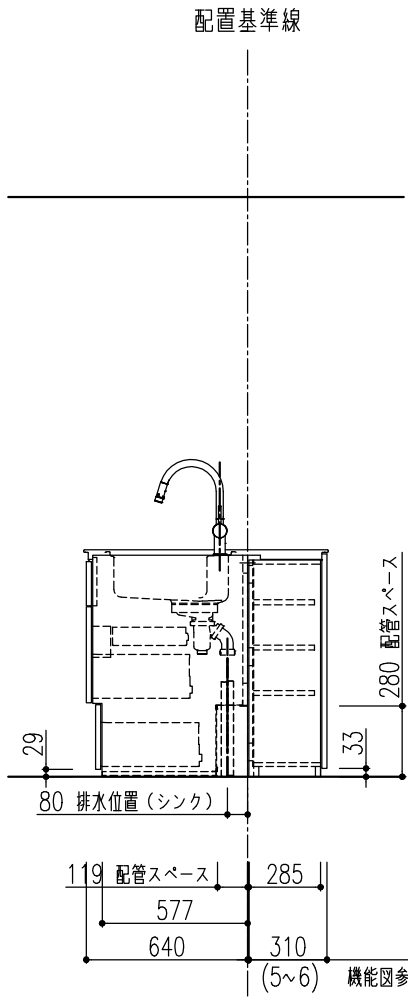

特記事項 扉色 KL1:ソリッドブラック 取手 [S]ミドル取手S (ブラック) ワークトップカラー 【BK】ブラックストーン	物件名	竹内陽子 様邸【10/29ご来館】 ND23	案件No.	図面名	担当	図面	図番
	仕様		A2409DDDD0E4U3C	納まり図	栗野 友仁		株式会社 LIXIL
			見種No.	縮尺	日付		
			M24095149774-008-2	1/30	2024.10.29		




■ 床の不陸に関して

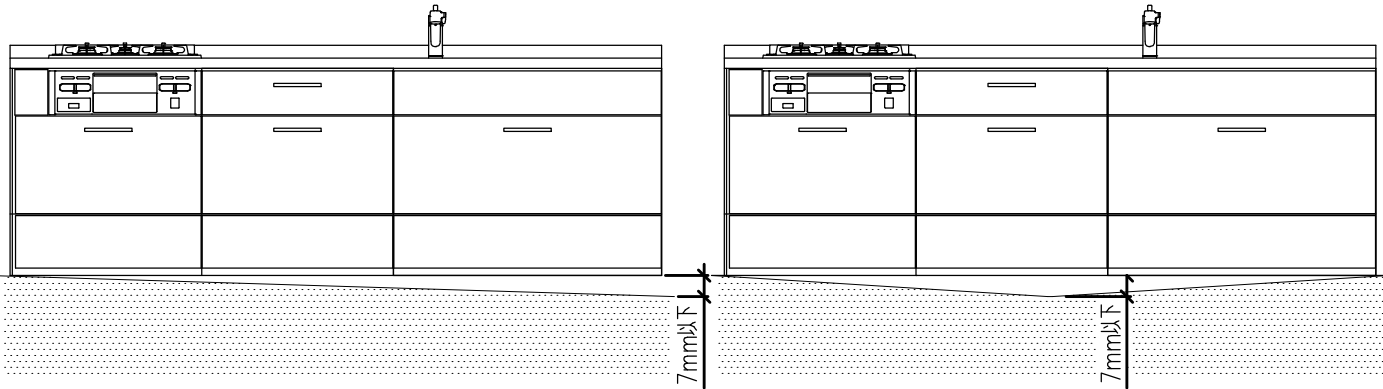


床の不陸は、7mm以下に抑えるようにしてください。不陸が大きい場合は、現場責任者に床の修正を依頼してください。
※キャビネット取付時には不陸調整スペーサー等で水平になるように設置してください。

■ 裏面キャビネット納まりについて


(キッチン側キャビネット背面) 配置基準▽

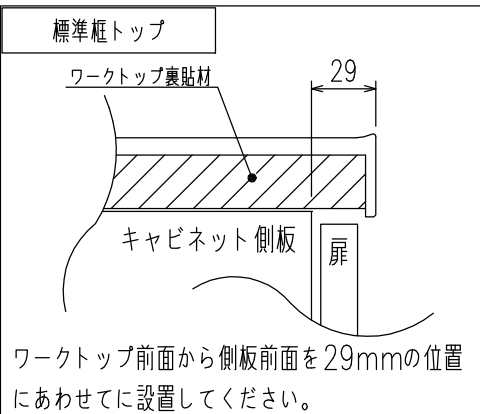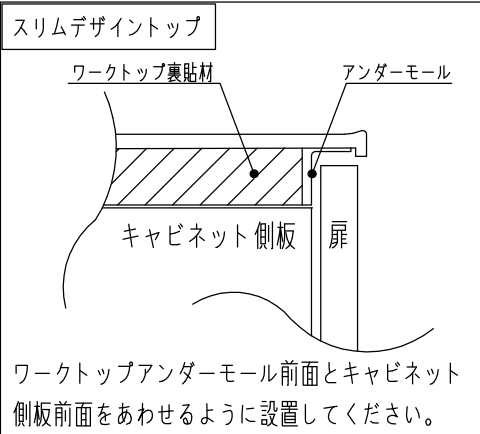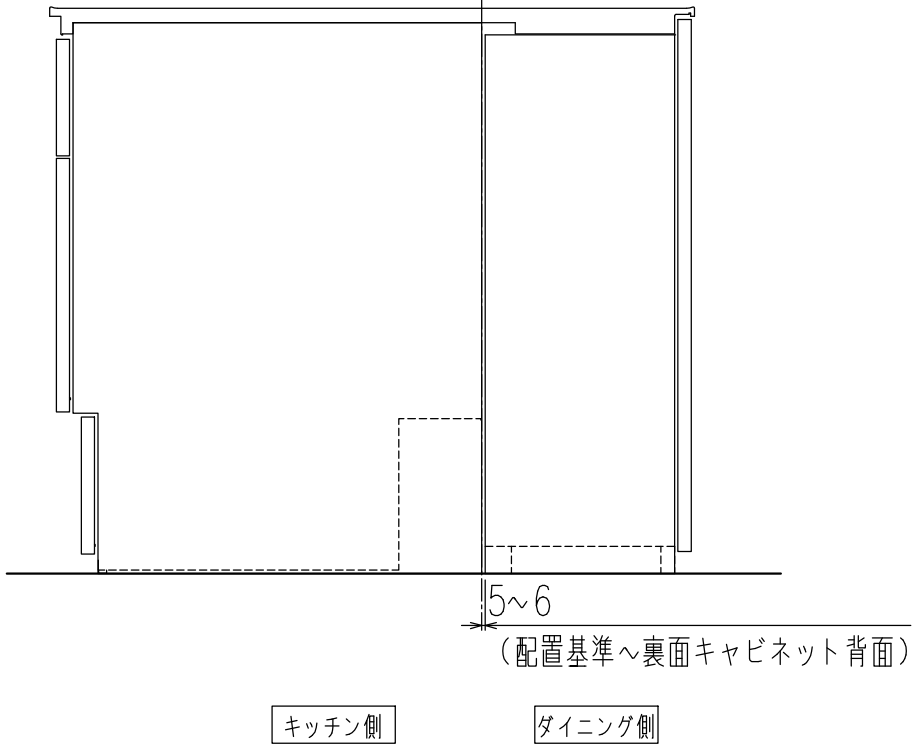

■ MCCLSフード

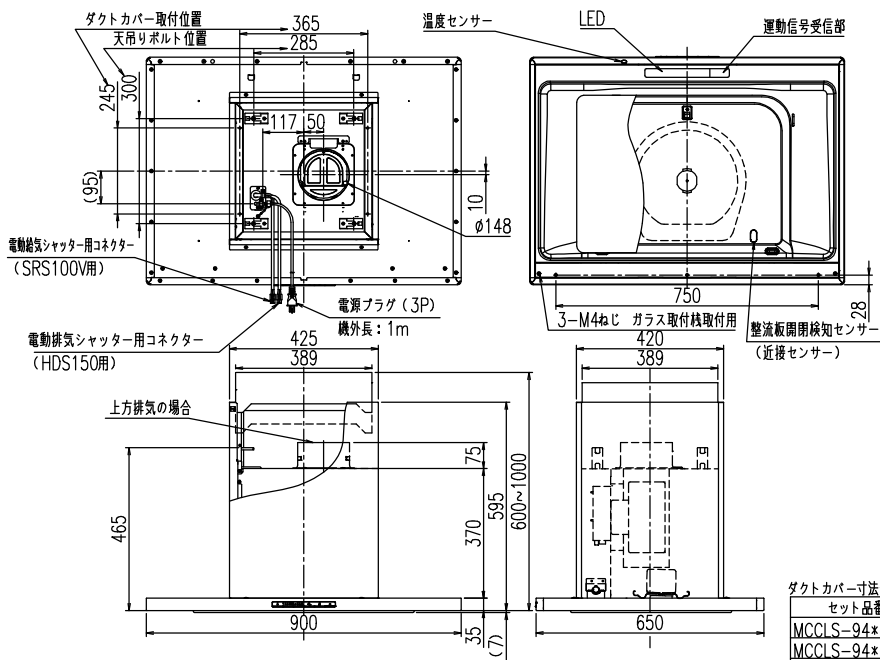


特 性 表									
型 名	定格電圧 (V)	ノット 定格周波数 (Hz)	消費電力 (W)	風 量 (m³/h) 0 Pa 0~130Pa	騒 音 (dB)	製品質量 (kg)			
MCCLS-94* SI/W/TBK	100	強	50	62	—	420	46	32.0	
		中	50	32	300	—	38		
		弱	50	16	210	—	33		
		常時	50	10	160	—	29		
			60						
			60						
電動機形式	8極DCブラシレス モーター	絶縁抵抗	10M以上 (500Vメガー)	定格電圧	AC1000V 1分 耐	絶縁区分	E 種		
風量値はJIS C 9603 チャンバー法による。									

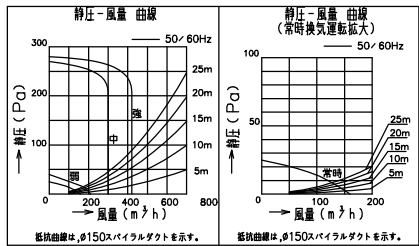


ダクトカバー寸法一覧	ダクトカバー	高さ範囲
セット品番	MCCLS-A-400*	920~1000
MCCLS-94*F*	MCCLS-A-320*	840~920
MCCLS-94*D*	MCCLS-A-240*	760~840
MCCLS-94*C*	MCCLS-A-160*	680~760
MCCLS-94*B*	MCCLS-A-080*	600~680

- 付 属 品
- ＋トラスねじ (M4×6) 4本
 - ＋ナベねじ (M5×10) 8本
 - フード固定金具 1個
 - ソフトテープ 1本
 - ワッシャー (φ5×φ16) 3個
 - ※ガラス取付枠取付用

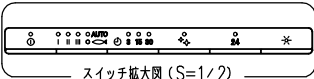

6. 本商品の機能である「風量おまかせ運転」を正常に機能させるために、加熱機器と本商品の離隔距離を800mm未満で設置することはできません。
5. 品番のSI/W/TBKは色調を示します。(SI: シルバー, W: ホワイト, TBK: テクチャーブラック)
4. ダクトカバーは品番によって寸法が異なります。
3. 設置には別売のダクトカバーが必要です。
2. 赤外線連動レンジフードです。単独でも使用できます。
注) 1. 排気方向は上方のみ可能です。


■ センターフード (MCCLS) 取付要領図

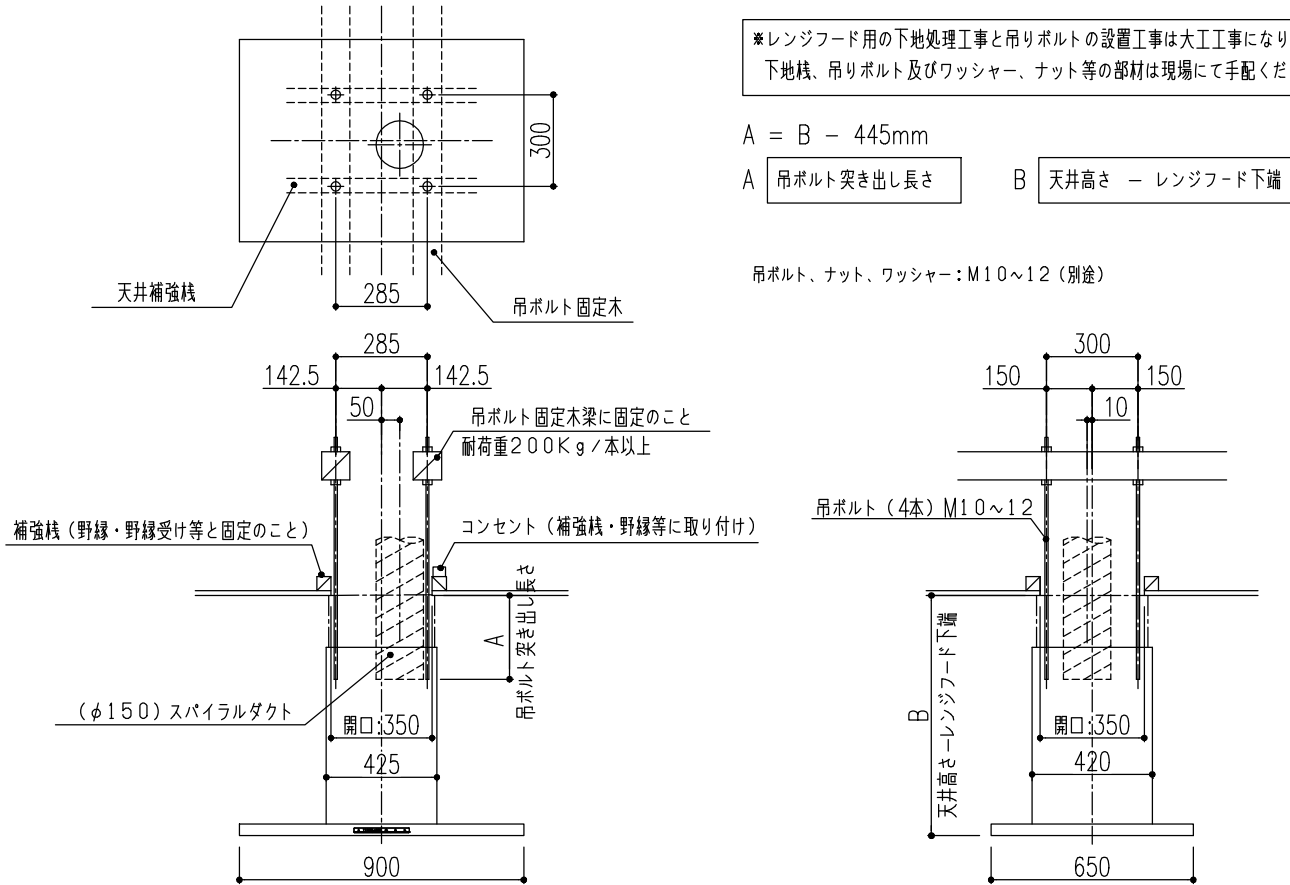


A3	特記事項 扉色 KL1:ソリッドブラック 取手 [S]ミドル取手S (ブラック) ワークトップカラー 【BK】ブラックストーン	物件名 仕様	竹内陽子 様邸【10/29ご来館】 ND23	案件No.	図面名	担当	図面	図番
				A2409DDDD0E4U3C	機能図	栗野 友仁		株式会社 LIXIL
				見積No.	縮尺	日付		
				M24095149774-008-2		2024.10.29		

- ※ コンセントはキャビネットの奥側（背板より65 mm）に取り付けてください。
- ※ コンセントや電源プラグが、引き出しおよびIHヒーター用仕切板（オプション）に接触しないように注意してください。
- ※ ロングスライドキャビネットの場合は、電源コードが引き出しおよびIHヒーター用仕切板（オプション）に接触しないように、キャビネットに付属の固定バンドで背板に固定してください。

※ () 内はD650/3□IHゲリルレスの場合

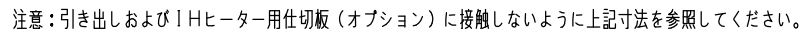

配管立ち上げ寸法は、止水栓芯までの高さを示しています。

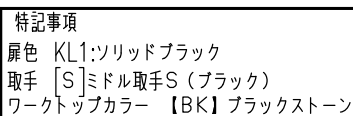

物件名	仕様
-----	----

竹内陽子 様邸【10/29ご来館】

ND 23

A2409DDD0E4U3C

M24095149774-008-2

機能図

縮尺

栗野 友仁

日付

2024.10.29

0.29

株式会社

INDEX

株式会社 LIXIL

※給水接続か給湯接続かお客様に確認したうえで施工願います。


③断熱材 (Φ48)



⑤HTエルボ



■ キッチン取付者さま向け 動画コンテンツ ■

商品取付けの注意点を2次元コードでご視聴いただけます。
取付日より前に、是非ご確認ください。





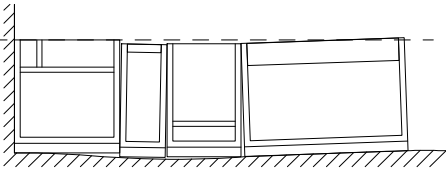
荷扱い・搬入	カウンター開梱搬入「養生ツール」	不陸の確認と調整	マグネットキッチンパネル
荷扱い・搬入	カウンター開梱搬入 「養生ツール」のご紹介		マグネット キッチンパネル 「取付・設置」ポイント
作成日：2024年10月01日	作成日：2024年10月01日	作成日：2024年02月07日	作成日：2024年03月06日

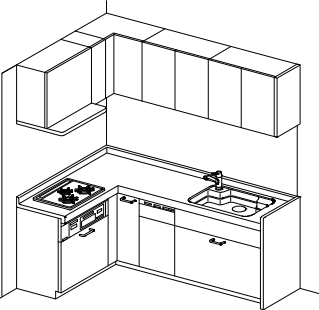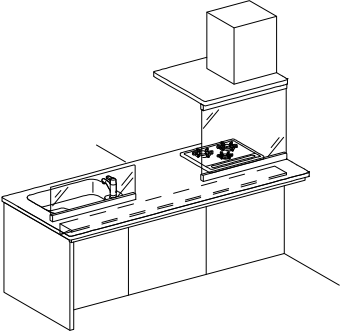人造大理石カウンターL型キッチン	センターキッチン（ペニンシュラ型）		
			
作成日：2024年02月07日	作成日：2024年02月07日		

	特記事項 扉色 KL1:ソリッドブラック 取手 [S]ミドル取手S（ブラック） ワークトップカラー 【BK】ブラックストーン	物件名	竹内陽子 様邸【10/29ご来館】		案件No.	図面名	担当	図面	図番 : 株式会社 LIXIL
					A2409DDD0E4U3C	機能図	栗野 友仁		
		仕様	ND23	見積No.	縮尺	日付			
				M24095149774-008-2		2024.10.29			

■ キッチン取付者さま向け 動画コンテンツ ■

商品取付けの注意点を2次元コードでご視聴いただけます。
取付日より前に、是非ご確認ください。

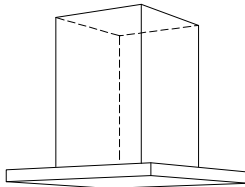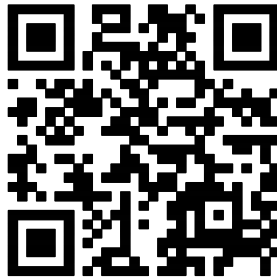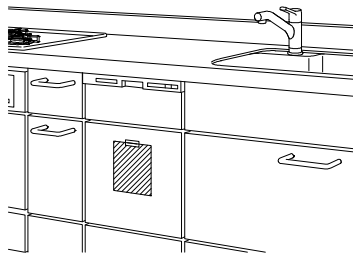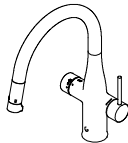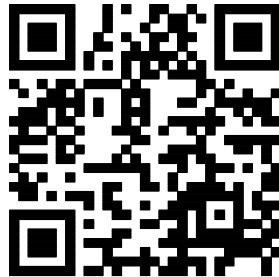センターフード型レンジフード (天吊りフード)  作成日：2024年06月03日 		I H加熱機器関連 I H加熱機器 仕切り板 作成日：2024年02月07日 		食器洗い乾燥機  作成日：2024年02月07日 		ミネラル浄水栓 Greentap  作成日：2024年06月03日 		
	特記事項 扉色 KL1:ソリッドブラック 取手 [S]ミドル取手S (ブラック) ワークトップカラー 【BK】ブラックストーン	物件名 竹内陽子 様邸【10/29ご来館】 仕様 ND23	案件No.		図面名	担当	図面	図番
			A2409DDD0E4U3C		機能図	栗野 友仁		株式会社 LIXIL
			見積No.		縮尺	日付		
			M24095149774-008-2			2024.10.29		