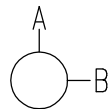
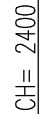




面



A面



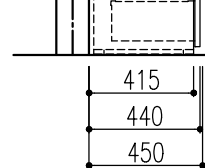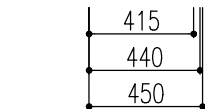
面

[illegible]


【 ご注意 】

- 記載のキャビネット寸法は扉前面までの呼び寸法です。キャビネット本体の寸法・扉厚み等は商品ガイドの巻末資料をご確認ください。
- 記載のワークトップ、カウンター、エンドパネル、サイドパネルの寸法は呼び寸法です。詳細寸法は商品ガイドの巻末資料をご確認ください。

特記事項	物件名	竹内陽子 様邸【10/29ご来館】	案件No.	図面名	担当	図面	図番
扉色 KL1:ソリッドブラック			A2409DDD0E4U3C	レイアウト図	栗野 友仁		株式会社 LIXIL
取手 [S]ミドル取手S (ブラック)	仕様	ND23	見積No.	縮尺	日付		
			M24095149774-008-4	1/30	2024.10.29		

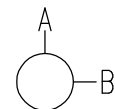

A面

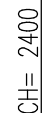
[illegible]

【ご注意】


- 記載のキャビネット寸法は扉前面までの呼び寸法です。キャビネット本体の寸法・扉厚み等は商品ガイドの巻末資料をご確認ください。
- 記載のワークトップ、カウンター、エンドパネル、サイドパネルの寸法は呼び寸法です。詳細寸法は商品ガイドの巻末資料をご確認ください。
- 取付・設置に際し、各製品の取付・設置説明書や図面の機能図を必ずお読み下さい。

特記事項 扉色 KL1:ソリッドブラック 取手 [S]ミドル取手S (ブラック)	物件名	竹内陽子 様邸【10/29ご来館】	案件No.	図面名	担当	図面	図番 : 株式会社 LIXIL
			A2409DDD0E4U3C	納まり図	栗野 友仁		
	仕様	ND23	見積No.	縮尺	日付		
			M24095149774-008-4	1/30	2024.10.29		

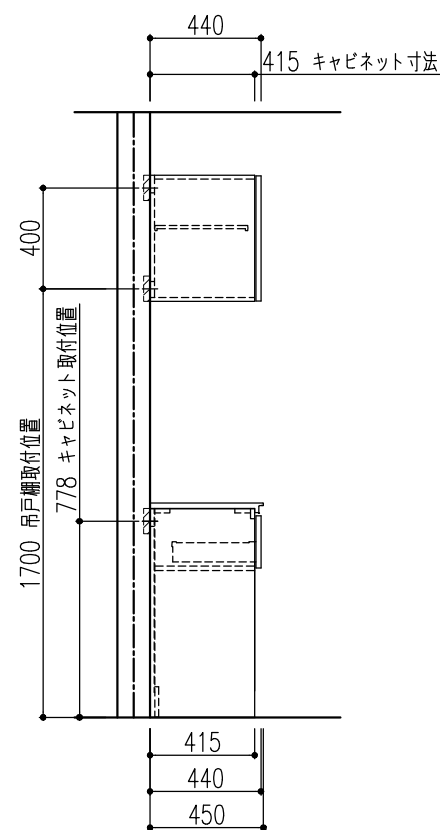B面





B面

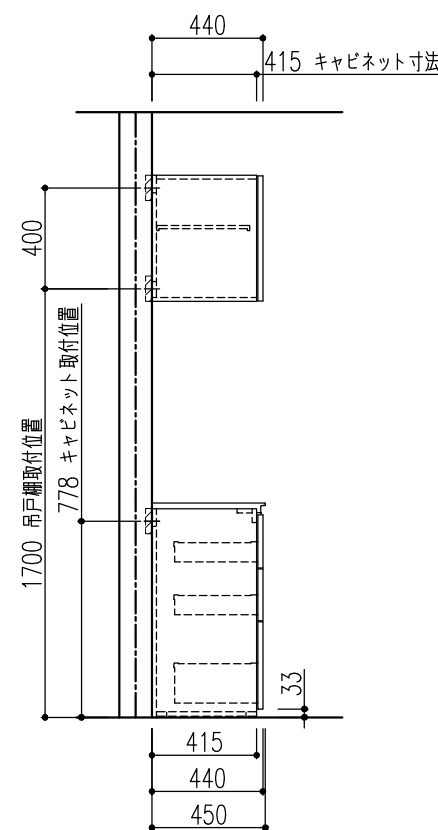

特記事項 扉色 KL1:ソリッドブラック 取手 [S]ミドル取手S (ブラック)	物件名	竹内陽子 様邸【10/29ご来館】	案件No.	図面名	担当	図面	図番
			A2409DDD0E4U3C	納まり図	栗野 友仁		株式会社 LIXIL
	仕様	ND23	見積No.	縮尺	日付		
			M24095149774-008-4	1/30	2024.10.29		

吊戸棚が落下する恐れがありますので、下記事項をお守りください。

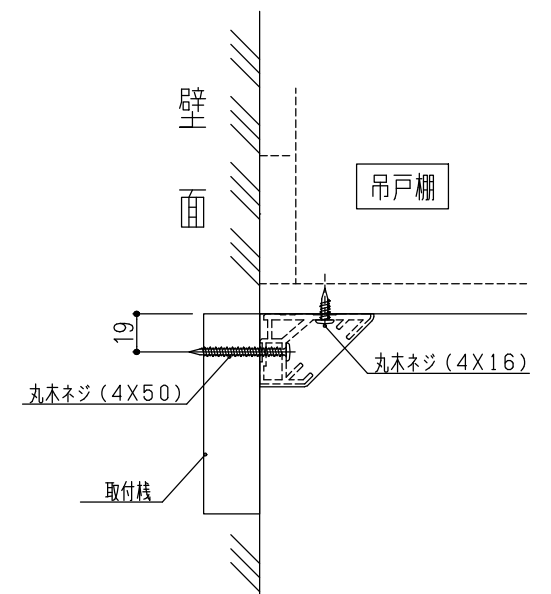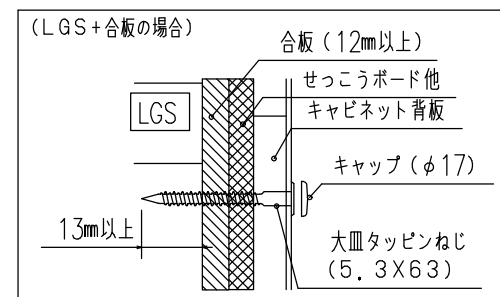- アイレベルレールの設置に関しては 下記要領で取付棧（下地）を御用意願います。



■ 床の不陸に関して

を設置する場合、横にキャビネットが
板は床固定金具を用いて床に固定する
。時
に床暖房パネル等、ネジ固定に支障
認ください。

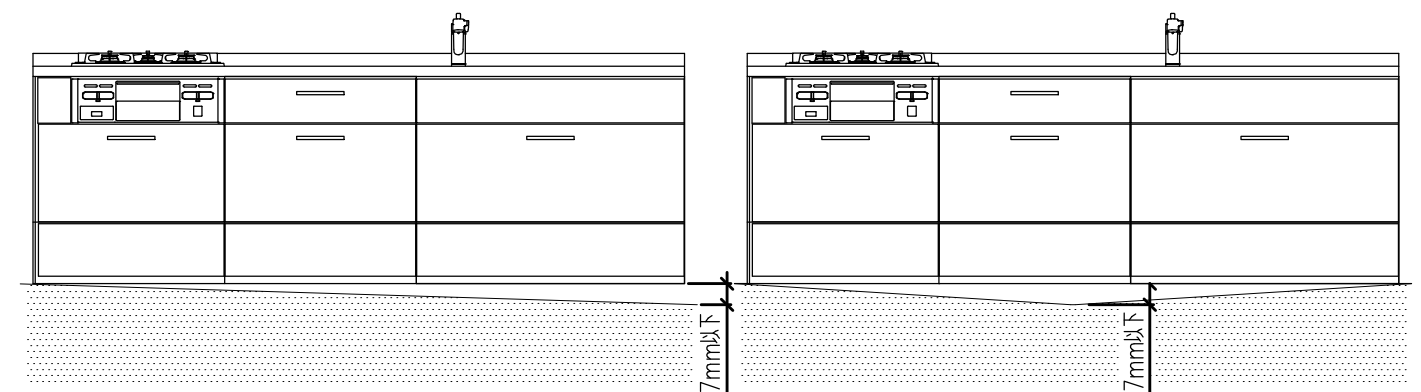
オープン側

床固定金具

キャビネット側は取り付け不要




床固定金具

皿タッピンねじ
3.5×16






床の不陸は、7mm以下に抑えるようにしてください。不陸が大きい場合は、現場責任者に床の修正を依頼してください。
※キャビネット取付時には不陸調整スペーサー等で水平になるように設置してください。

特記事項 扉色 KL1:ソリッドブラック 取手 [S]ミドル取手S（ブラック）	物件名	竹内陽子 様邸【10/29ご来館】	案件No.	図面名	担当	図面	図番
	仕様		A2409DDD0E4U3C	機能図	栗野 友仁		株式会社 LIXIL
		ND23	見積No.	縮尺	日付		
			M24095149774-008-4			2024.10.29	

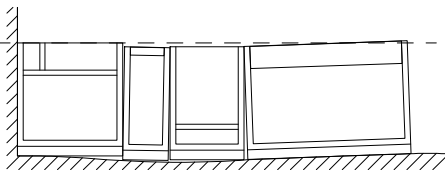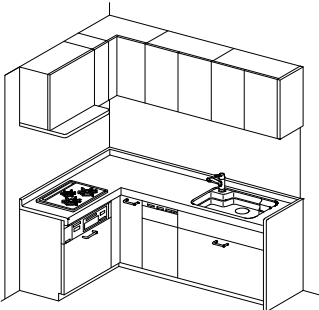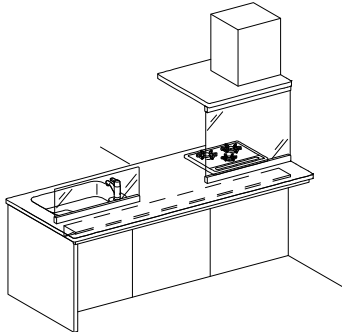■ キッチン取付者さま向け 動画コンテンツ ■ 商品取付けの注意点を2次元コードでご視聴いただけます。 取付日より前に、是非ご確認ください。												1 ページ目	
荷扱い・搬入 荷扱い・搬入 作成日：2024年10月01日			カウンター開梱搬入「養生ツール」 カウンター開梱搬入 「養生ツール」のご紹介 作成日：2024年10月01日			不陸の確認と調整  作成日：2024年02月07日			マグネットキッチンパネル マグネット キッチンパネル 「取付・設置」ポイント 作成日：2024年03月06日				
人造大理石カウンターL型キッチン  作成日：2024年02月07日			センターキッチン（ペニンシュラ型）  作成日：2024年02月07日										
		特記事項 扉色 KL1:ソリッドブラック 取手 [S]ミドル取手S（ブラック）	物件名 仕様	竹内陽子 様邸【10/29ご来館】 ND23		案件No.		図面名	担当	図面	図番		
						A2409DDD0E4U3C		機能図	栗野 友仁		株式会社 LIXIL		
						見積No.		縮尺	日付				
						M24095149774-008-4			2024.10.29				

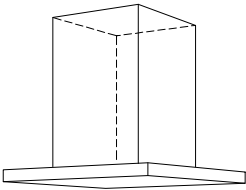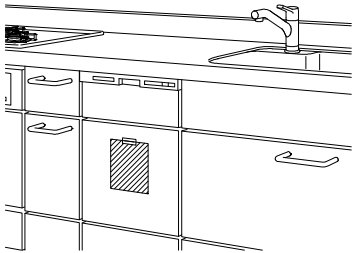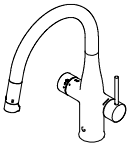■ キッチン取付者さま向け 動画コンテンツ ■
商品取付けの注意点を2次元コードでご視聴いただけます。
取付日より前に、是非ご確認ください。

センターフード型レンジフード (天吊りフード)  作成日：2024年06月03日 	I H加熱機器関連 I H加熱機器 仕切り板 作成日：2024年02月07日 	食器洗い乾燥機  作成日：2024年02月07日 	ミネラル浄水栓 Greentap  作成日：2024年06月03日 
---	--	--	---

--	--	--	--

--	--	--	--

特記事項 扉色 KL1:ソリッドブラック 取手 [S]ミドル取手S (ブラック)	物件名	竹内陽子 様邸【10/29ご来館】	案件No.	図面名	担当	図面	図番
			A2409DDD0E4U3C	機能図	栗野 友仁		株式会社 LIXIL
	仕様	ND23	見積No.	縮尺	日付		
			M24095149774-008-4		2024.10.29		