





面

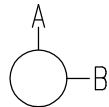

A面

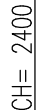


面

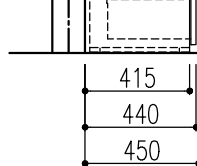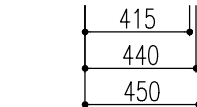[illegible]

【 ご注意 】

- 記載のキャビネット寸法は扉前面までの呼び寸法です。キャビネット本体の寸法・扉厚み等は商品ガイドの巻末資料をご確認ください。
- 記載のワークトップ、カウンター、エンドパネル、サイドパネルの寸法は呼び寸法です。詳細寸法は商品ガイドの巻末資料をご確認ください。

特記事項 原色 KL1:ソリッドブラック 取手 [S]ミドル取手S(ブラック)	物件名	竹内陽子 様邸【10/29ご来館】	案件No.	図面名	担当	図面	図番
			A2409DDD0E4U3C	レイアウト図	葉野 友仁		株式会社 LIXIL
	仕様	ND23	見積No.	縮尺	日付		
			M24095149774-008-5	1/30	2024.10.29		

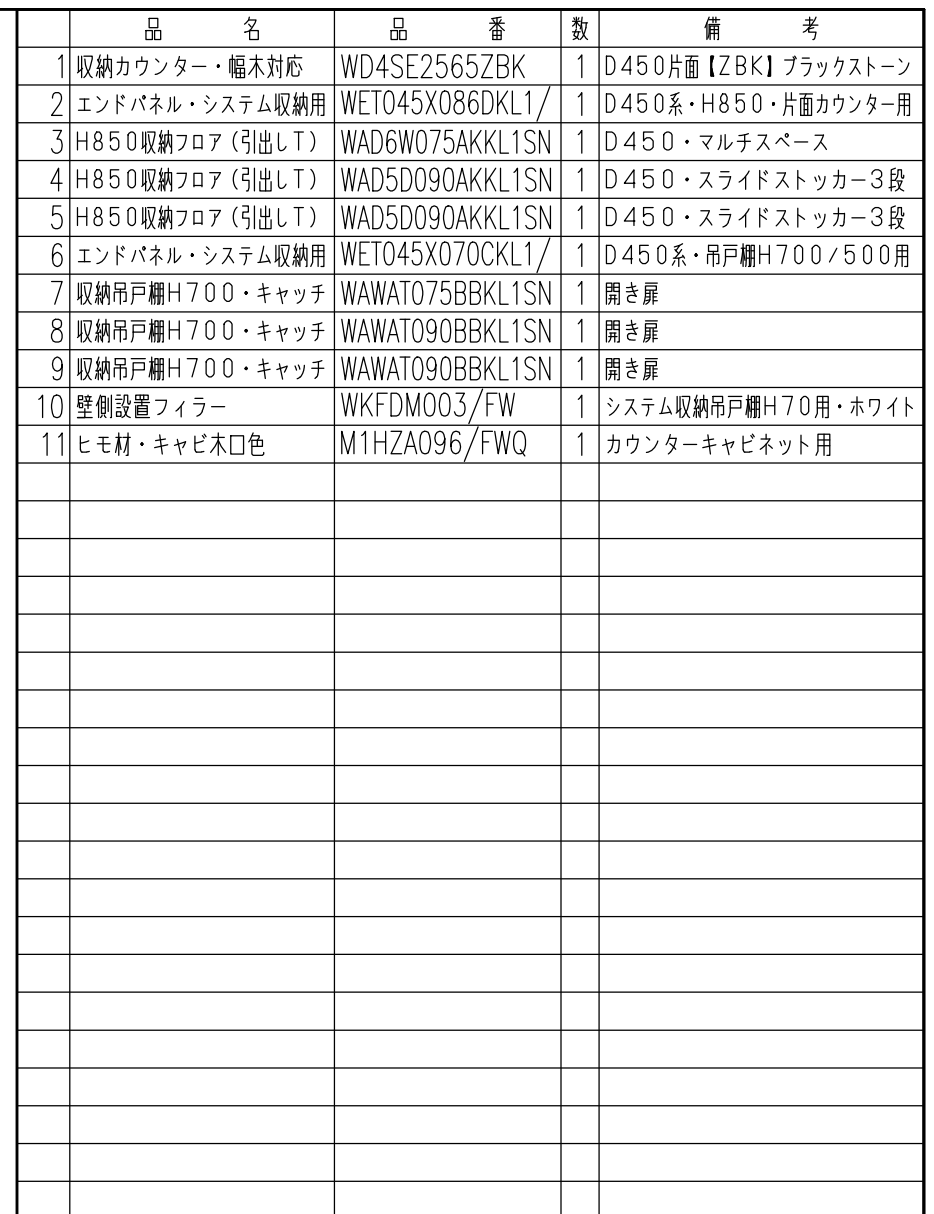


●記載のキャビネット寸法は扉前面までの呼び寸法です。キャビネット本体の寸法・扉厚み等は商品ガイドの巻末資料をご確認ください。

●記載のワークトップ、カウンター、エンドパネル、サイドパネルの寸法は呼び寸法です。詳細寸法は商品ガイドの巻末資料をご確認ください。


●取付・設置に際し、各製品の取付・設置説明書や図面の機能図を必ずお読み下さい。

特記事項 扉色 KL1:ソリッドブラック 取手 [S]ミドル取手S (ブラック)	物件名	竹内陽子 様邸【10/29ご来館】	案件No.	図面名	担当	図面	図番
	仕様		A2409DDD0E4U3C	納まり図	栗野 友仁		株式会社 LIXIL
		ND23	見積No.	縮尺	日付		
			M24095149774-008-5	1/30	2024.10.29		

B面

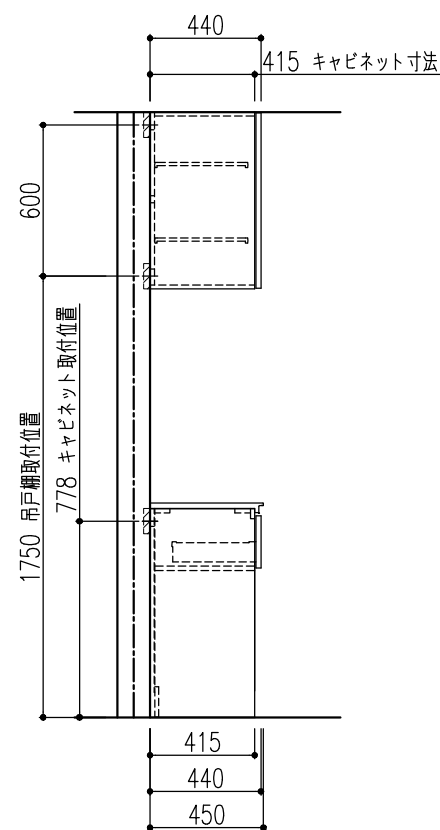

B面

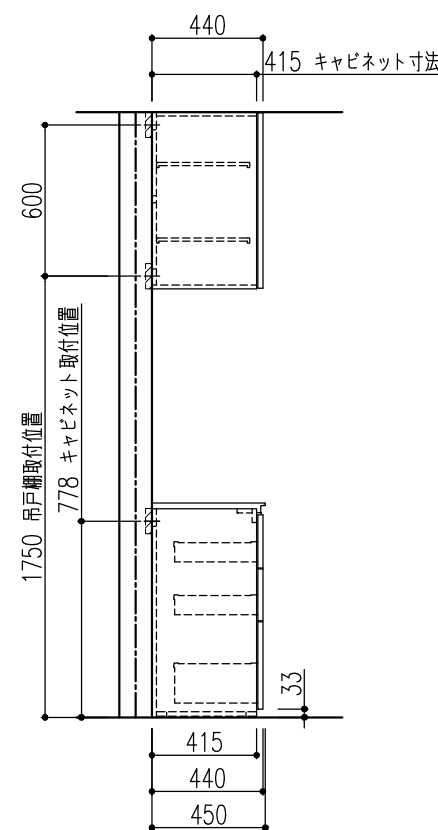


特記事項 扉色 KL1:ソリッドブラック 取手 [S]ミドル取手S (ブラック)	物件名	竹内陽子 様邸【10/29ご来館】	案件No.	図面名	担当	図面	図番
			A2409DDD0E4U3C	納まり図	栗野 友仁		株式会社 LIXIL
	仕様	ND23	見積No.	縮尺	日付		
			M24095149774-008-5	1/30	2024.10.29		


■吊戸棚 取付注意事項

吊戸棚が落下する恐れがありますので、下記事項をお守りください。


- 本体重量と収納重量の荷重に対して、取付棧（下地）が落ちないだけの強度をもたせてください。
最大300kg/1キャビネット当たりの強度がもつように柱・間柱に確実に固定してください。
- キャビネットを取付・設置する壁面には、取付棧（下地）を取付けるか、埋め込みます。
- 取付棧（下地）は広葉樹、マツ・ツガ等の強度のある針葉樹いずれかの無垢材を使用します。
また、厚さ30mm以上、幅100mm以上が必要です。
- 合板を取付棧（下地）として使用する場合は、ラワン合板などの硬い材質の普通合板
（表面が平滑でフシがない、虫くいや、くされのないもの）を使用します。
また、必ず厚さ12mm以上のものを使用してください。
- せっこうボードで仕上げる壁面は、せっこうボードの内側に取付棧（下地）を取付けます。

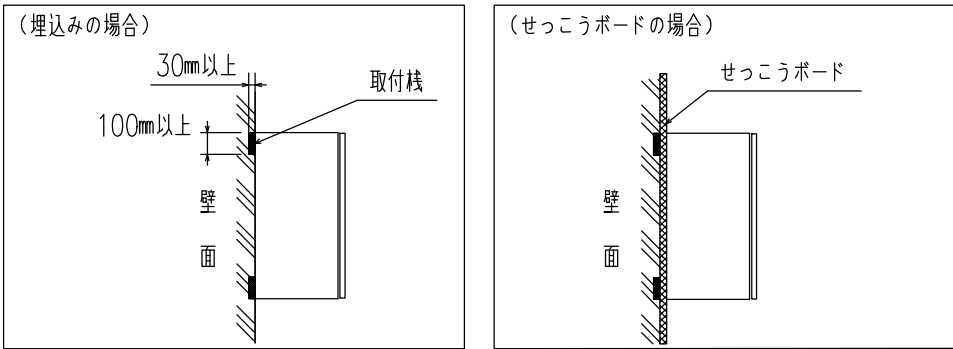

- 吊戸棚の取付けは、必ず商品同梱の専用ネジ（大皿タッピンねじ5.3X63）を使用し、取付棧（下地）に25mm以上かかるようにしてください。
- 合板下地の場合は、下地からのネジ貫通しを13mm以上としてください。
- 合板下地はネジ箇所だけではなく、全面下地（吊戸棚全体）を原則とします。

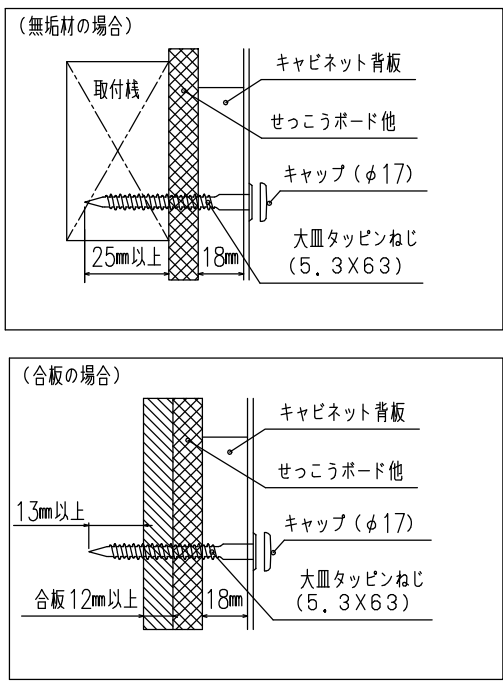


- 鋼板下地の場合 ・鋼板の変形を防ぐため必ずせっこうボード等で覆ってください。
・下地からのネジ貫通しを25mm以上としてください。
- 鋼板下地でせっこうボード2枚貼りの場合、その内側に下地を敷設する事は、
上記のネジ貫通しが確保出来ないため設置できません。
- 鋼板の厚みは必ず0.8mm以上のものを使用してください。
- 軽量鉄骨躯体（LGS）の設置間隔は300mm以下を守ってください。

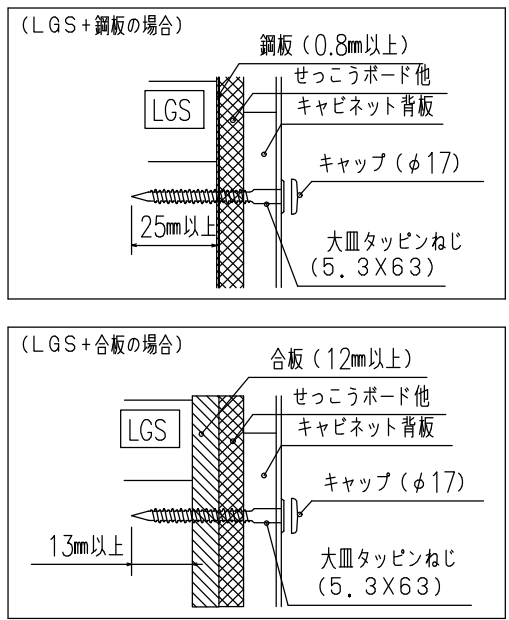

■アイレベルレール 取付注意事項

- ※ アイレベルレール設置の場合
- アイレベルレールの設置に関しては 下記要領で取付棧（下地）
を御用意願います。

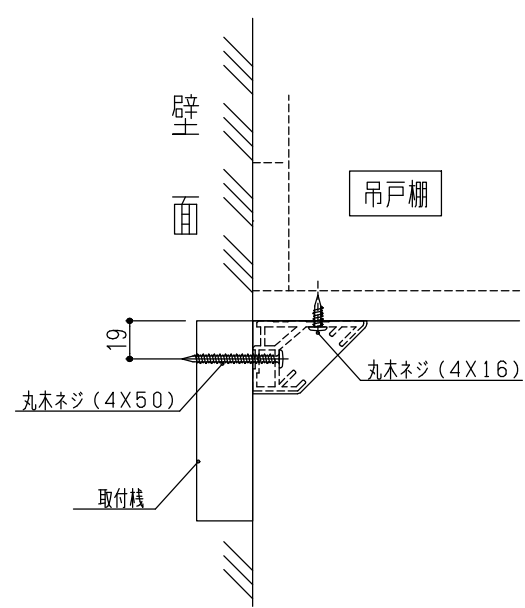


■ 床の不陸に関して

床の不陸は、7mm以下に抑えるようにしてください。不陸が大きい場合は、現場責任者に床の修正を依頼してください。
※キャビネット取付時には不陸調整スペーサー等で水平になるように設置してください。




■オープンタイプ設置注意

■設置上の注意

オープンタイプを設置する場合、横にキャビネットが設置されない側板は床固定金具を用いて床に固定する必要があります。
レイアウト決定時に床暖房パネル等、ネジ固定に支障がないかをご確認ください。



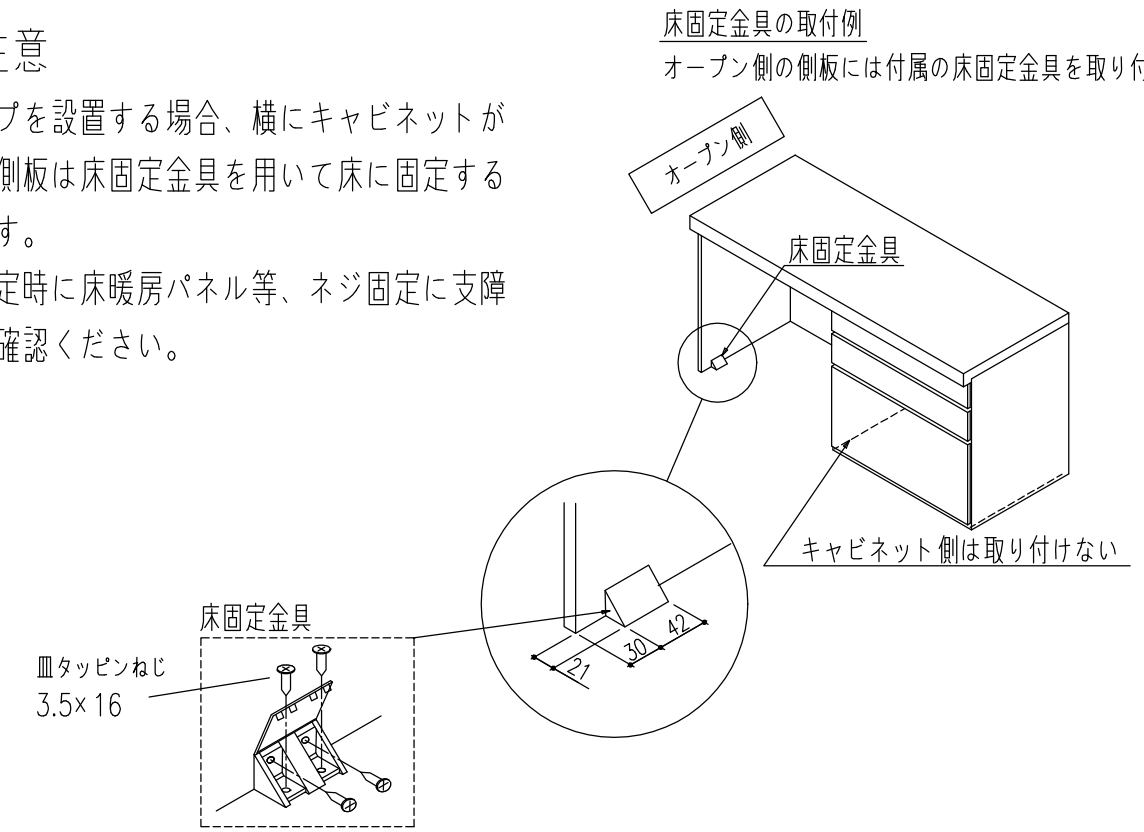


	特記事項 扉色 KL1:ソリッドブラック 取手 [S]ミドル取手 S（ブラック）	物件名	竹内陽子 様邸【10/29ご来館】	案件No.	図面名	担当	図面	図番 :
--	--	-----	-------------------	-------	-----	----	----	--

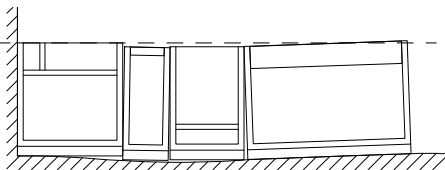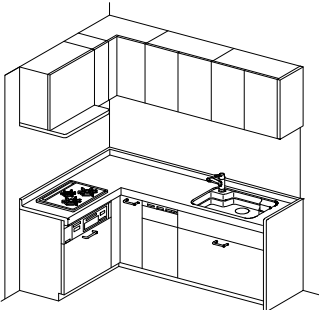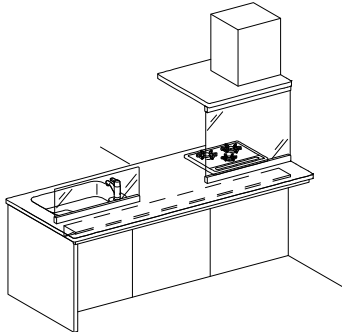■ キッチン取付者さま向け 動画コンテンツ ■ 商品取付けの注意点を2次元コードでご視聴いただけます。 取付日より前に、是非ご確認ください。										1 ページ目	
荷扱い・搬入 荷扱い・搬入 作成日：2024年10月01日			カウンター開梱搬入「養生ツール」 カウンター開梱搬入 「養生ツール」のご紹介 作成日：2024年10月01日			不陸の確認と調整  作成日：2024年02月07日			マグネットキッチンパネル マグネット キッチンパネル 「取付・設置」ポイント 作成日：2024年03月06日		
人造大理石カウンターL型キッチン  作成日：2024年02月07日			センターキッチン（ペニンシュラ型）  作成日：2024年02月07日								
		特記事項 扉色 KL1:ソリッドブラック 取手 [S]ミドル取手S（ブラック）	物件名 仕様	竹内陽子 様邸【10/29ご来館】 ND23		案件No.		図面名	担当	図面	図番
						A2409DDD0E4U3C		機能図	栗野 友仁		株式会社 LIXIL
						見積No.		縮尺	日付		
						M24095149774-008-5			2024.10.29		

■ キッチン取付者さま向け 動画コンテンツ ■

商品取付けの注意点を2次元コードでご視聴いただけます。
取付日より前に、是非ご確認ください。

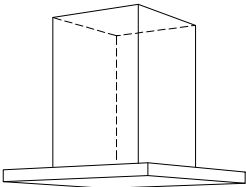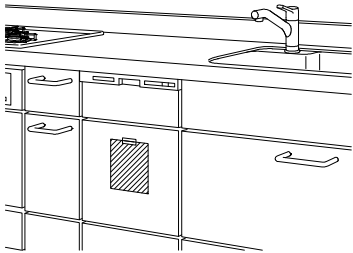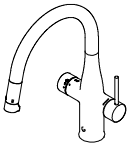センターフード型レンジフード (天吊りフード)  作成日：2024年06月03日 	I H加熱機器関連 I H加熱機器 仕切り板 作成日：2024年02月07日 	食器洗い乾燥機  作成日：2024年02月07日 	ミネラル浄水栓 Greentap  作成日：2024年06月03日 
---	--	--	---

--	--	--	--

--	--	--	--

特記事項 扉色 KL1:ソリッドブラック 取手 [S]ミドル取手S (ブラック)	物件名	竹内陽子 様邸【10/29ご来館】	案件No.	図面名	担当	図面	図番
			A2409DDD0E4U3C	機能図	栗野 友仁		株式会社 LIXIL
	仕様	ND23	見積No.	縮尺	日付		
			M24095149774-008-5		2024.10.29		