


■ 仕 様		■ HEAT20 G1
断熱工事	■ 床:カネライトフォーム t65 ■ 土間床等の外周:スタイロフォームAT t25 ■ 壁:アクアフォームLITE吹付 t85 ■ 天井:アクファフォームLITE吹付 t170	
床下換気	■ 基礎パッキン JOTO (玄関・UB周り:気密基礎パッキン)	
防虫防蟻	■ 土壌処理・木部 ガントナーMC	

■ 外 部 仕 上 表			■ 22条地域
部位		仕上・仕様・メーカー	色番・品番
屋根		■ ガルバリウム鋼板(t0.35)UK立平 ニスクカラーPro GH 軒先通気金物 日本住環境株式会社【REV-15】	GHK01 Sブラック
パラペット笠木		■ なし	
破風・鼻隠		■ なし	
雨樋	(軒樋)	■ Panasonic サーフeskエアFS-I型	ブラック
	(縦樋)	■ Panasonic S30角樋	ブラック
軒天	屋根軒	■ なし	
	ポーチ軒	■ 神島化学 t= 6mm 軒天ボード エンボス	Wチャコールブラック
	バルコニー軒	■ なし	
オーバーハング水切り		■ ガルバリウム鋼板 ※外壁合わせ JOTO:HF-A3550	ブラック
外壁	通気金物(15mm)	■メイン ニチハ エモンエクセラード16 Vシリーズ リーガストーン調V	ランダムMGブラック
	※下地面材:タイガーEXハイパー	■アクセントA なし	
	防火認定 PC030BE-4028	■アクセントB なし	
玄関ポーチ		■ 床 玄関床に同じ	-
基礎		■ 立上り巾木: モルタル刷毛引き	-
基礎水切り金物		■ JOTO鋼板製 防鼠材付き水切り JOTO:WMF-N35	ブラック
バルコニー	床・内壁	■ なし	-
	笠木	■ なし	
外部建具		■ LIXIL EW(アルゴンガス高遮熱仕様LowE複層ガラス クリーン) ・SD、TSで記載がないものは、オペレーターハンドルとする ・オペレーター付サッシは固定網戸とする ・グレモンハンドル式サッシの選択箇所は可動網戸とする	外観 ブラック 内観 ショルダーオークforDesign ※樹脂パッキン・網戸付
シャッター		■ なし	
玄関扉		■ LIXIL ジエスタ2 K2仕様 LIXILファミロック タグキー×3 (電池式)	ドア型: M17 型 ドア色: カームブラック ハンドル: S型ハンドル 色 ブラック
外部物干し金物		■	
換気フード		■ 局所換気扇(トイレ 浴室 キッチンフード) 防火ダンパー無 ■ ダクトレス熱交換換気システム (日本スティーベル株式会社) VLR-70E 防火ダンパー無	外気フード: ブラック 外気フード: B ブラック 室内パネル マッドブラック


■ 構 造 概 要			
基礎	■ RCベタ基礎コンクリート		
通し柱・管柱	■ 構造用集成材 105×105		間柱 ■ 集成材
土台	■ 桧 105×105	大引き ■ 桧 90*90	筋交い ■ 構造用製材 火打梁 ■ 鋼製火打(当社基準により米松あり)
桁・梁	■ 構造用製材及び集成材		制震装置 ■ Kダンパー (株)アイ・エム・エー

■ 設 備 装 着 品				
住宅設備	部位	メーカー	商品名 ※ 詳細は見積り、プレゼン参照	見積りNo. (日付)
	キッチン	LIXIL	■ ND アイランド型	見積り番号 : M24095149774-008-2 (日付) 2024/10/30
	バックカウンタ	LIXIL	■ ND L2550	見積り番号 : M24095149774-008-4 (日付) 2024/10/30
	浴室	LIXIL	■ AX1616	見積り番号 : M24095149774-008-1 (日付) 2024/10/30
	1Fトイレ	LIXIL	■ ベーシアハーモJタイプ 白 ● タオル掛け: なし(支給品取付) タンク手洗 無し ● 紙巻き器: なし(支給品取付)	見積り番号 : M24095149774-008-7 (日付) 2024/10/30
	2Fトイレ	LIXIL	■ ベーシアシャワートイレ 白 ● タオル掛け: なし(支給品取付) タンク手洗 有り ● 紙巻き器: なし(支給品取付)	見積り番号 : M24095149774-008-6 (日付) 2024/10/30
	洗面台	LIXIL	■ EV W900(D500タイプ) 扉:クリエダーク その他 ● タオル掛け: なし(支給品取付)	見積り番号 : M24095149774-008-8 (日付) 2024/10/30
	トイレ手洗	ミラック	■ レプトインウォール ブラック LEP050LS	-
給排水設備	給湯器		■ エコキュート370L Panasonic NSシリーズ スタンダードモデル 追い焚きフルオート	
	排水		■ 下水	
	外水栓		■ 1 カ所 (平面図参照) ■ 外部立栓柱: PVC製 水栓柱12型【前澤化成工業】	
	外部ガーデンパン		■ 無し	
	その他		■ 洗濯機用単水栓: 緊急止水弁付 ■ 洗濯機用排水: トラップ金物(標準)	
ガス配管設備			■ なし (配置図・平面図参照)	
電気設備	インターホン		■ パナソニック VL-SZ30KL	
	TVアンテナ		■ UHF + BS・110度CS／CSアンテナ [2K・4K・8K対応] ■ブラック ※電波状況によりホワイトになる可能性あり	
			■	
	ソーラー ※標準搭載		■ あり(Qセルズ) 12 枚 5.28 KW Re.RISE-G3 440 (1722×1134×30) ■ 屋外パワコン	
その他	エアコン		■ 新設 LDK リソラ S633ATSP(20帖) 寝室 CV-MSZ—GV2224 ■ 移設 書斎 既存移設 洋室 既存移設	決定図

	浜 岡 一 級 総 合 設 計 事 務 所	株式会社 LIFEFUND InDesign office 一級建築士事務所	年 月 日 2024.11.20	件名 竹内優太郎様邸 新築工事		設計 IC 工務 図 番
	一級建築士事務所 静岡県知事登録第 (10)2441 号	事務所登録 (2)第7595号 一級建築士登録 第179770号 鈴木 達男	縮尺	図面 仕上表 1		倉田 青島 1-1
	一級建築士 大臣登録第 365879 号 西原利昌	〒432-8023 静岡県浜松市中央区鴨江3丁目70番23号				

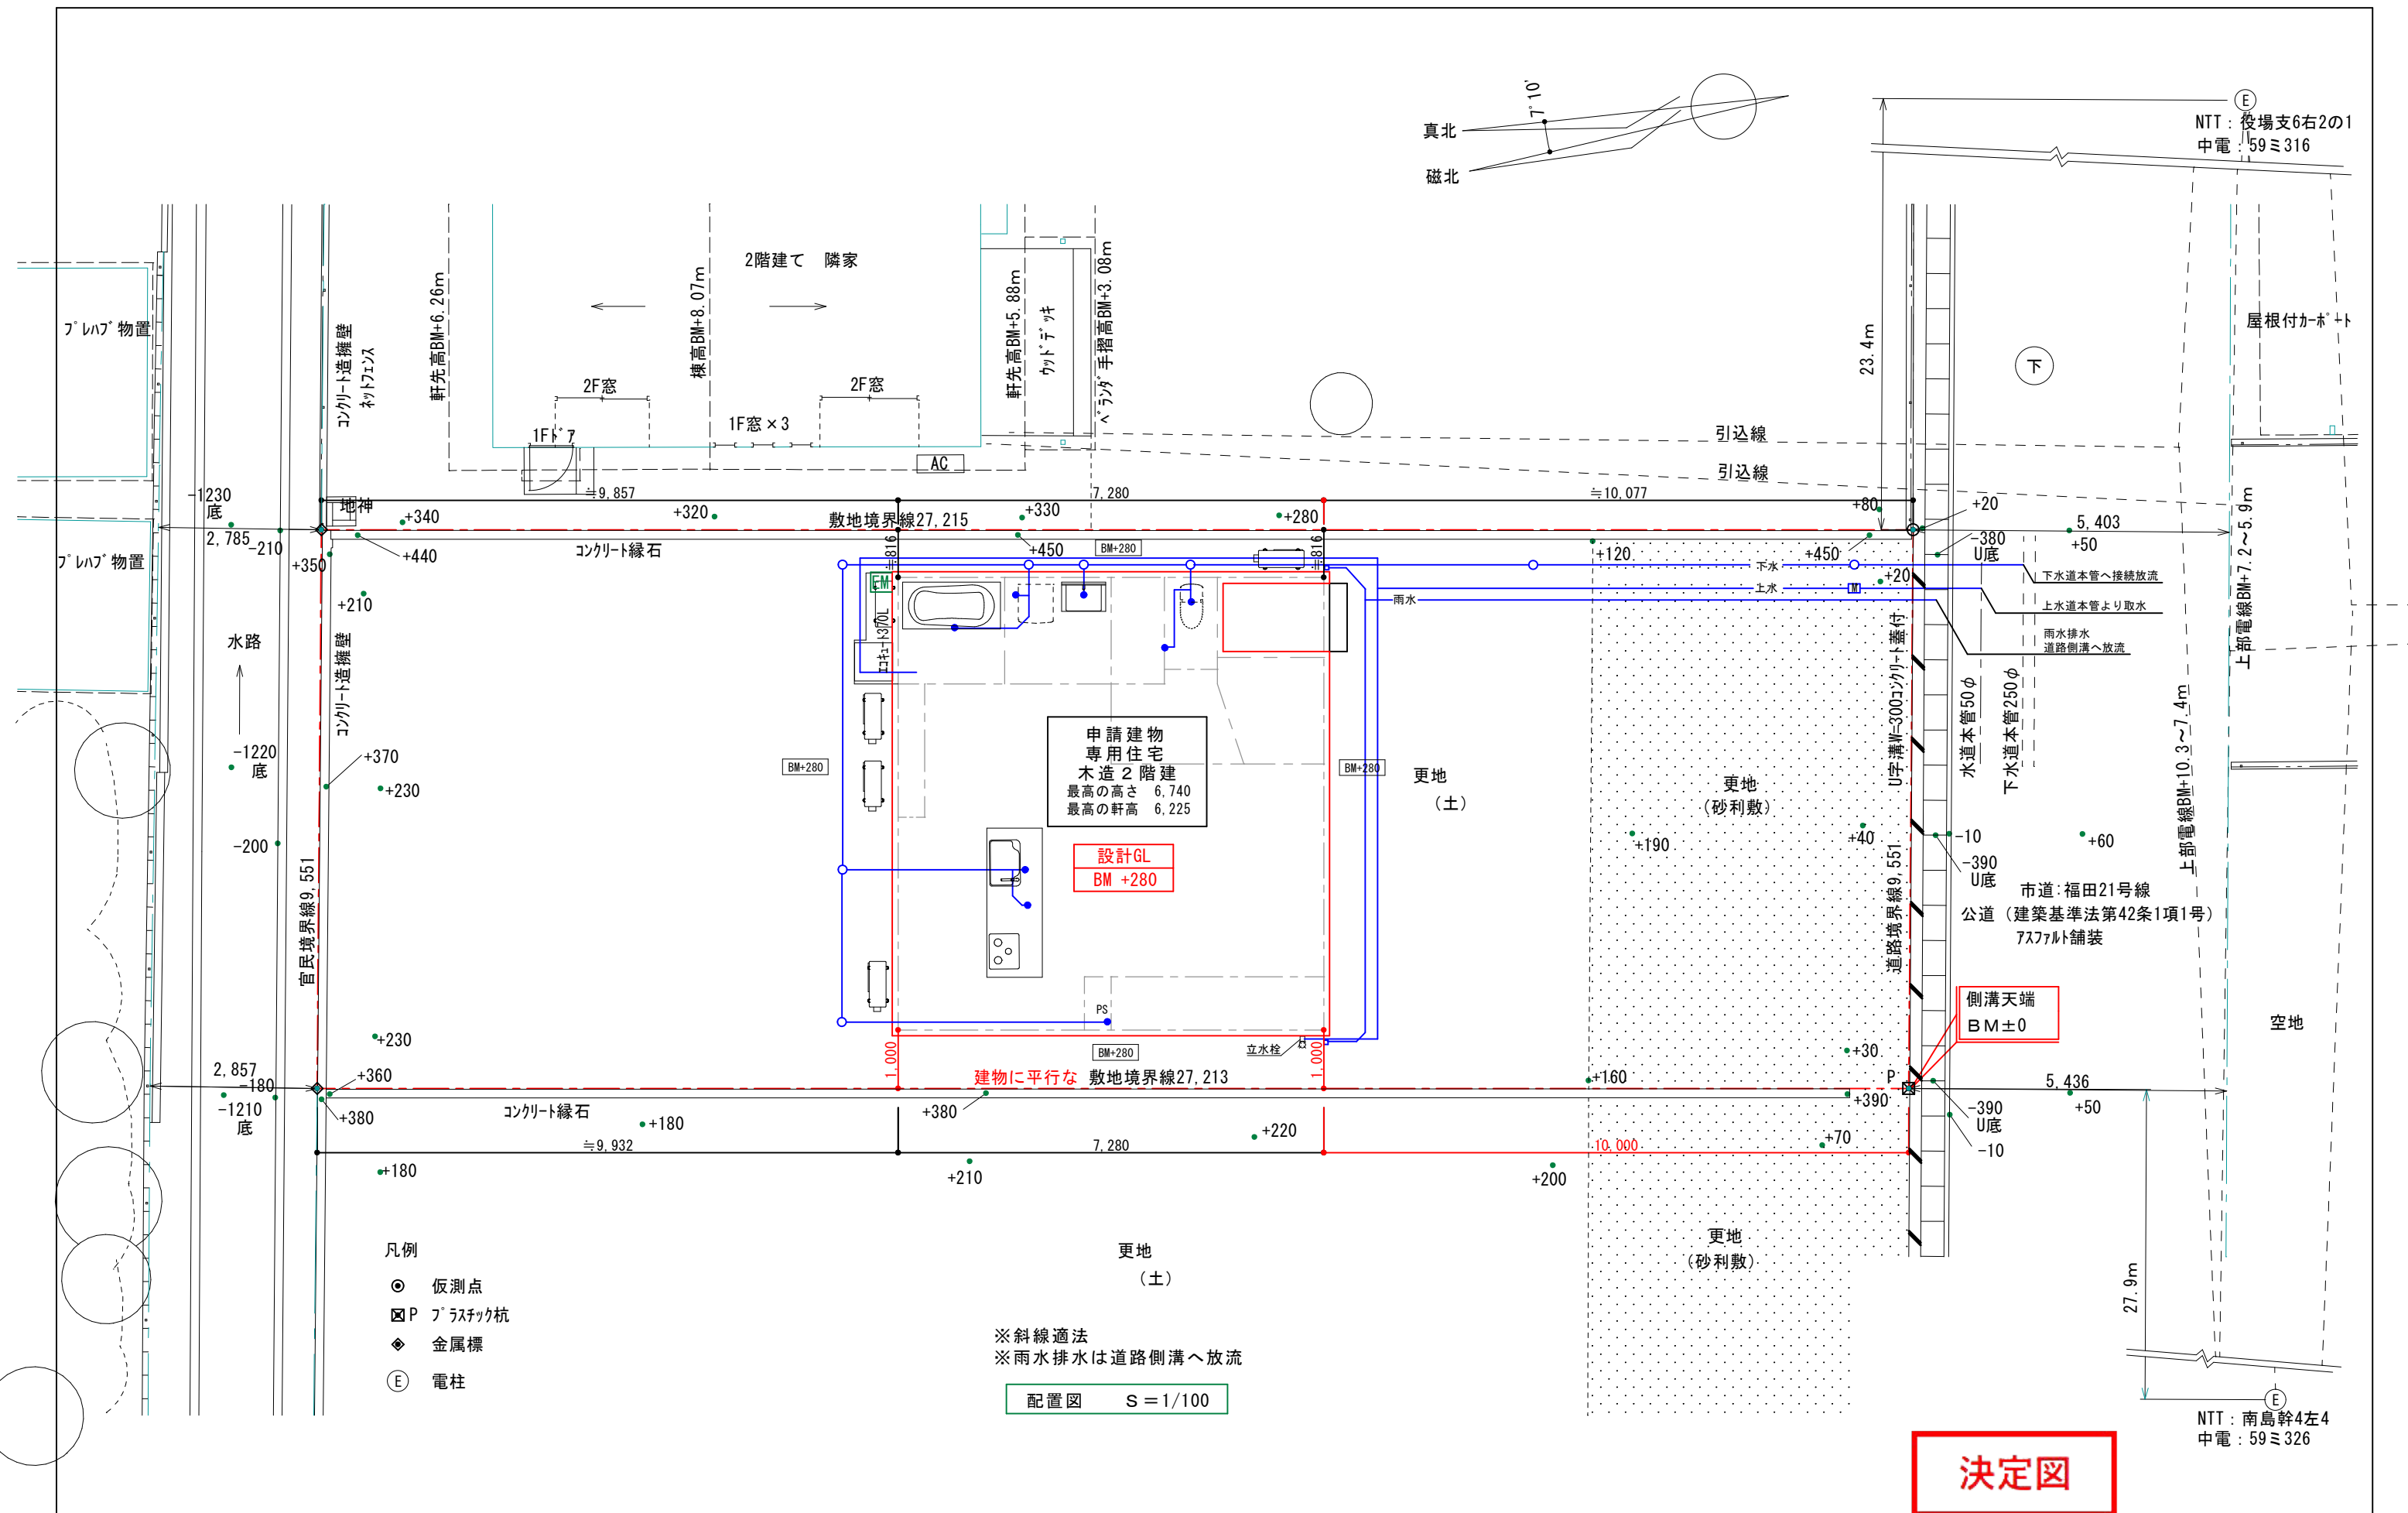

訂正	浜岡一級総合設計事務所 一級建築士事務所 静岡県知事登録第(10)2441号 一級建築士 大臣登録第 365879号 西原利昌	LIFEFUND PG HOUSE	株式会社 LIFEFUND InDesign office 一級建築士事務所 事務所登録(2)第7595号 一級建築士登録 第179770号 鈴木 達男 〒432-8023 静岡県浜松市中央区鴨江3丁目70番23号	年月日 2024.12.10	件名 竹内優太郎様邸 新築工事		設計	IC	工事	図番
				縮尺 1/100	図名 配置図		倉田		青島	2-1

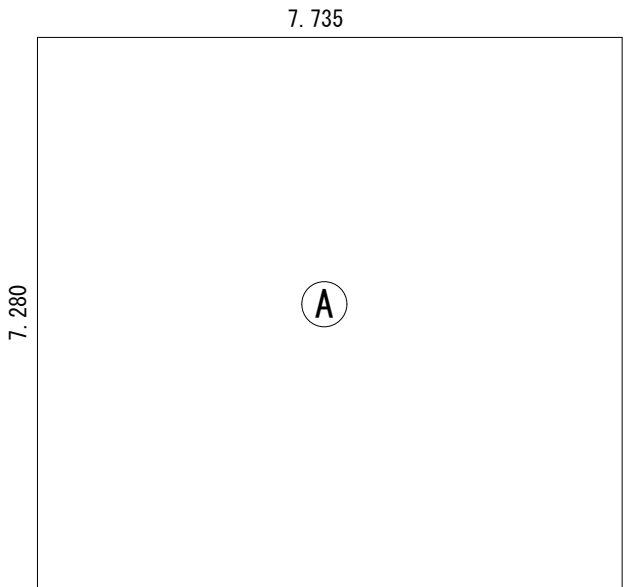


建築面積求積図 S=1/100

建築面積求積表

番号	計算式	(m)	面積 (㎡)
Ⓐ	7.735 × 7.280		56.3108
合計			56.3108 56.31

(17.0坪)

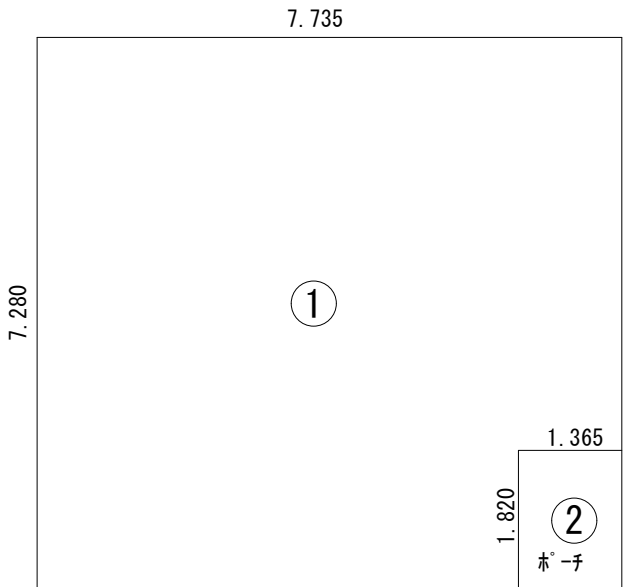


1階床面積図 S=1/100

1階床面積求積表

番号	計算式	(m)	面積 (㎡)
①	7.735 × 7.280		56.3108
②	1.365 × 1.820		-2.4843
合計			53.8265 53.82

(16.3坪)

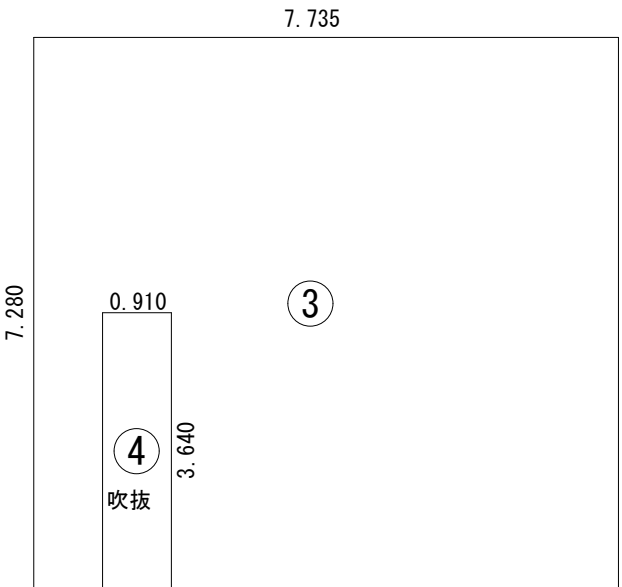

2階床面積図 S=1/100

2階床面積求積表

番号	計算式	(m)	面積 (㎡)
③	7.735 × 7.280		56.3108
④	0.910 × 3.640		-3.3124
合計			52.9984 52.99


(16.0坪)

延べ床面積表

	番号	(m)	面積 (㎡)
1階床面積	① - ②		53.82
2階床面積	③ + ④		52.99
合計			106.81

(32.3坪)

決定図

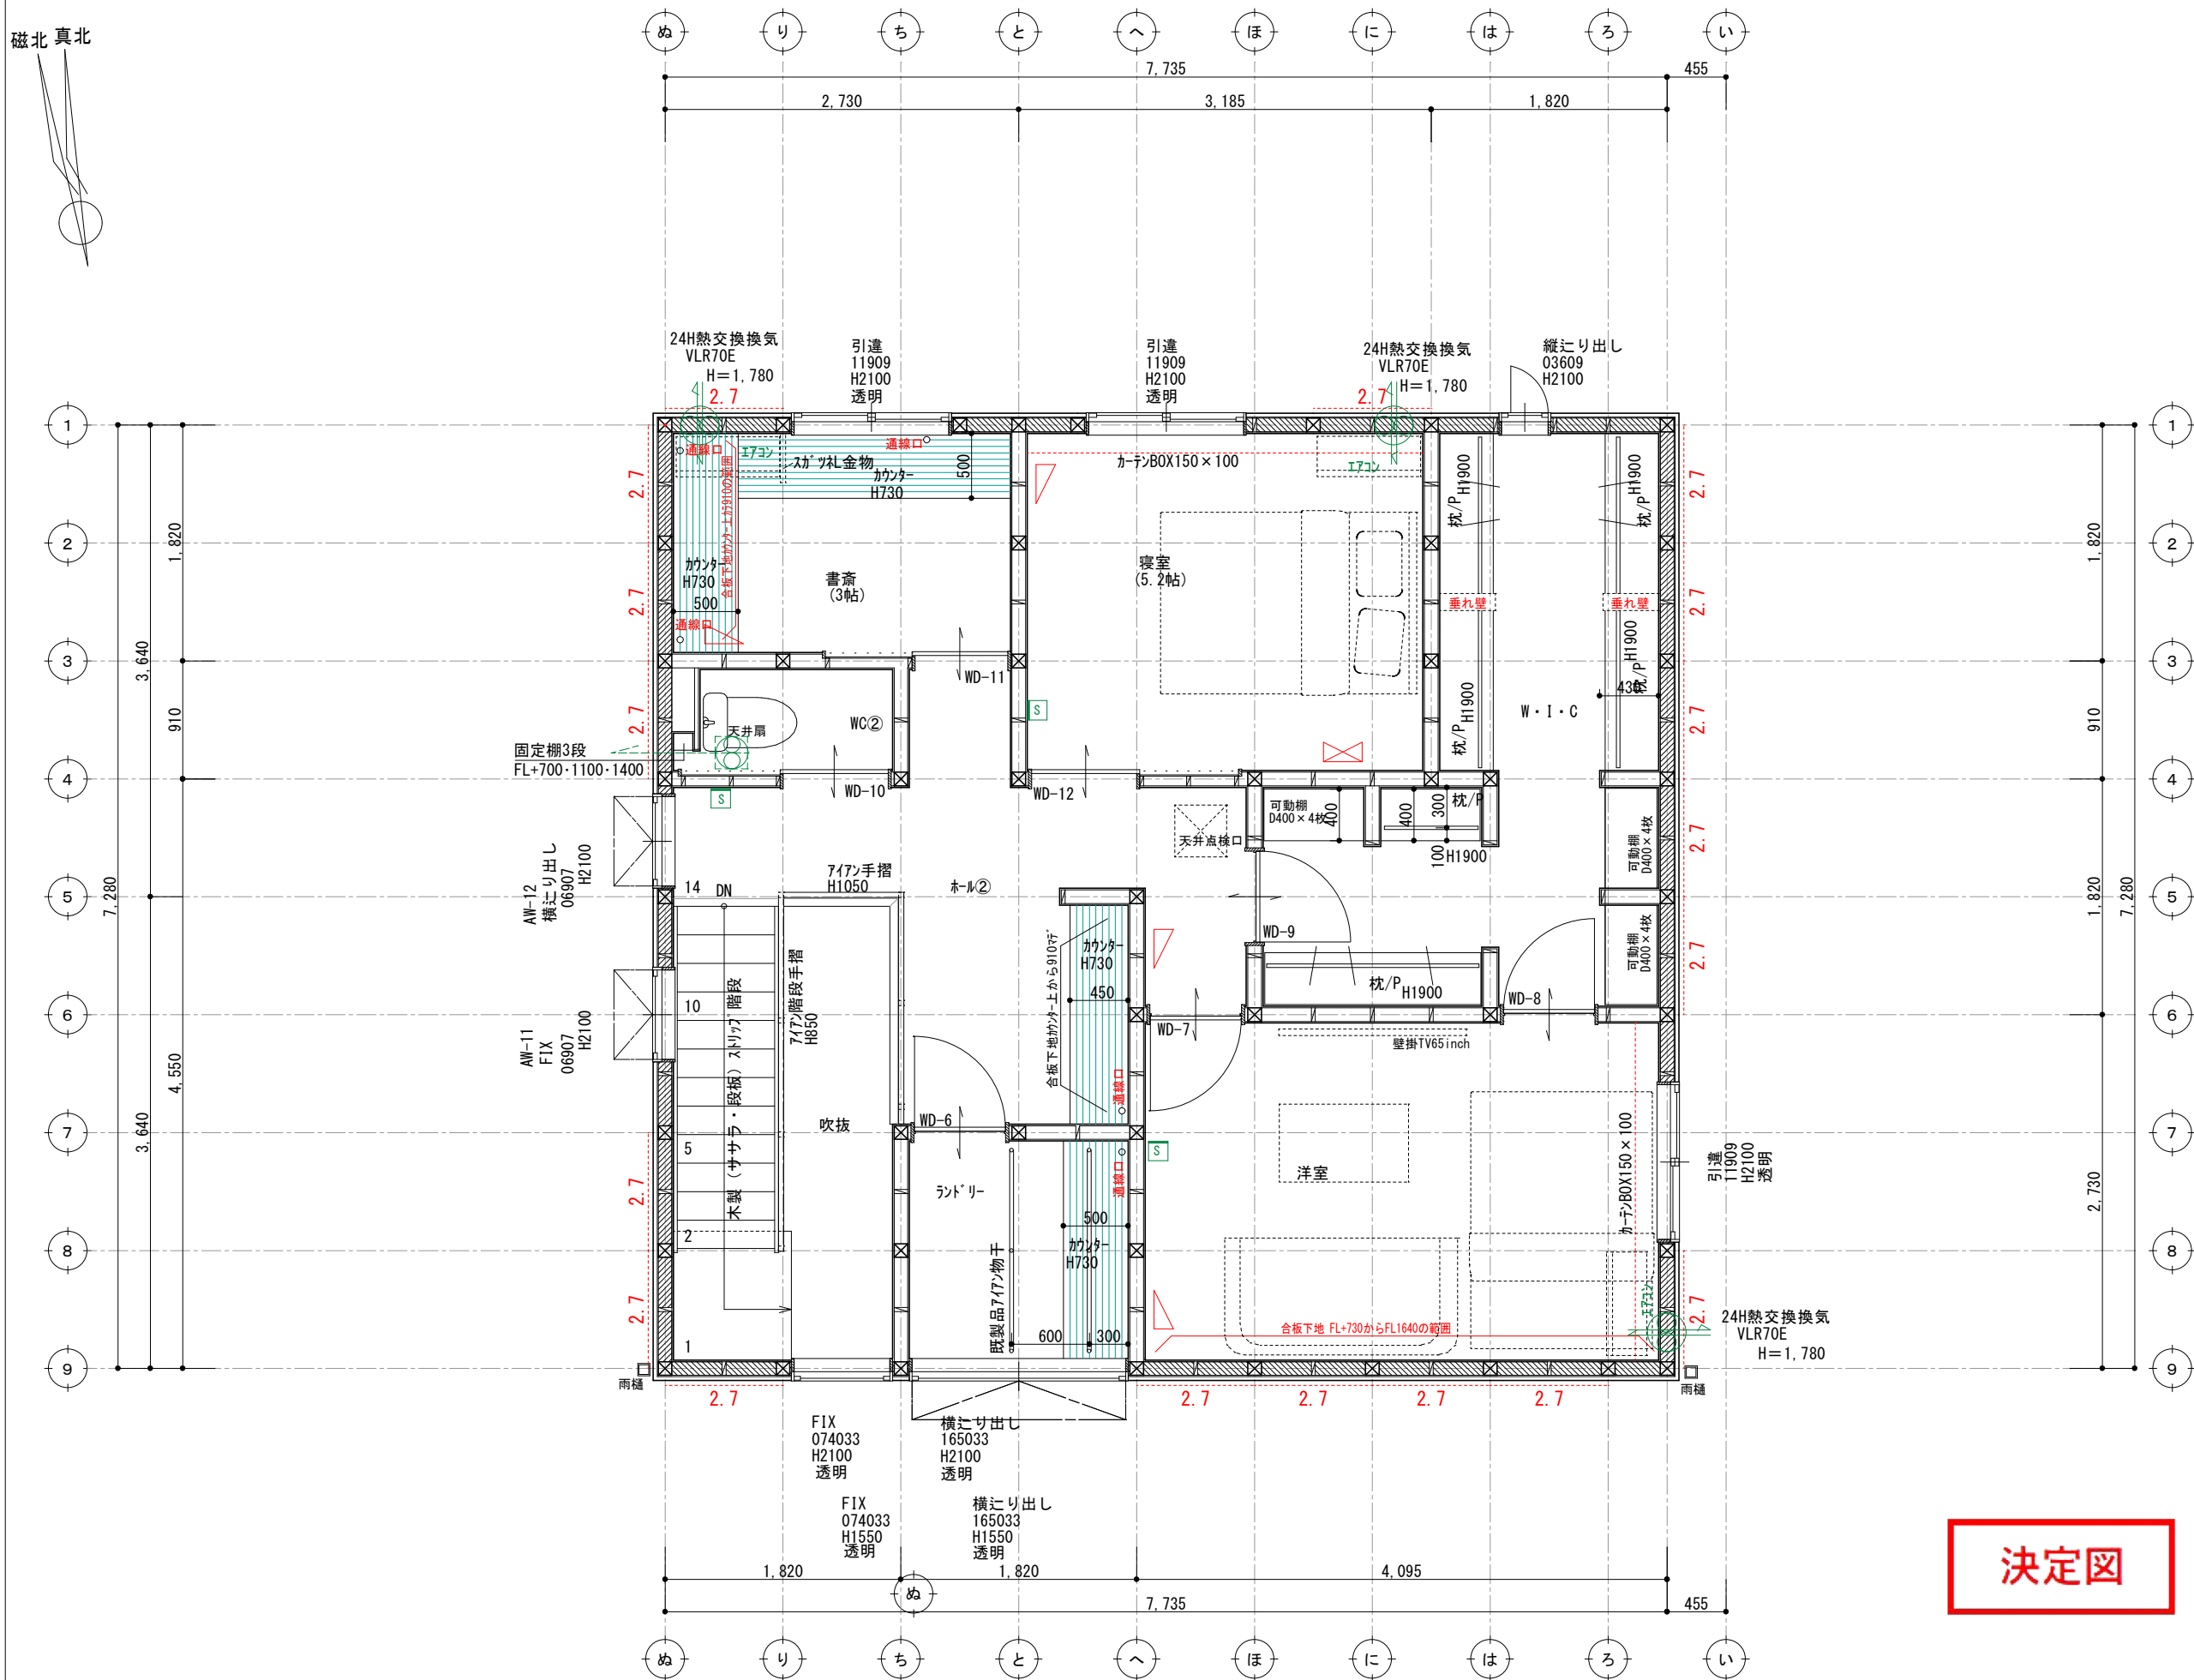

壁付け 住宅用火災報知器			数量
H 熱感知	電池式(単独型)		
	露出型		
壁付け 住宅用火災報知器			数量
S 煙感知	電池式(単独型)		
	露出型		

※ 煙感知器は壁・梁より600mm以上離す
壁に取付ける場合、
天井から150mm以上500mm以内離す
換気扇・エアコン吹出口から1500mm以上離す
※ 全室LED照明とする。
※ 標準天井高さ2,400

* 凡例

- 管柱 (105×105)
- Kダンパー (3.30倍 FRM-0641)
- 片筋違い (2.00倍 45×90)
(例 左:柱脚 右:柱頭)
- たすき掛筋違い (4.00倍 45×90)
- 構造用合板 (2.70倍)
(t=9 3枚 -EXハイパー-)
- 床点検口
- 天井点検口
- 換気扇
- 熱交換換気扇VLR-70


※表記なきガラスは型ガラス

アドバンスシリーズ		
スマートデザイン (外部)		
凡例	1	コンセント 1ヶ所
2	コンセント 2ヶ所	
3	コンセント 3ヶ所	
1ET	コンセント1ヶ所接地ターミナル付	
2ET	コンセント2ヶ所接地ターミナル付	
WP	コンセント 防水型	
エアコン	エアコン用コンセント	
200V	200V用コンセント	
WP	防雨入線プレート	
スイッチ	スイッチ	
3	3路スイッチ	
4	4路スイッチ	
直結電源	直結電源	
TV	テレビ取出口	
TEL	電話取出口 (テレホンガイド)	
LAN	LAN取出口 (テレホンガイド)	
壁照明	壁照明	
リモコン	リモコン (給湯関係・ルフロ)	
メーター	メーター	
分電盤	分電盤	
チャイム	チャイム	

※ACコンセント天井付け
※TVアンテナ工事
※スイッチはFL+1100、コンセントはFL+200

決定図



磁北 真北

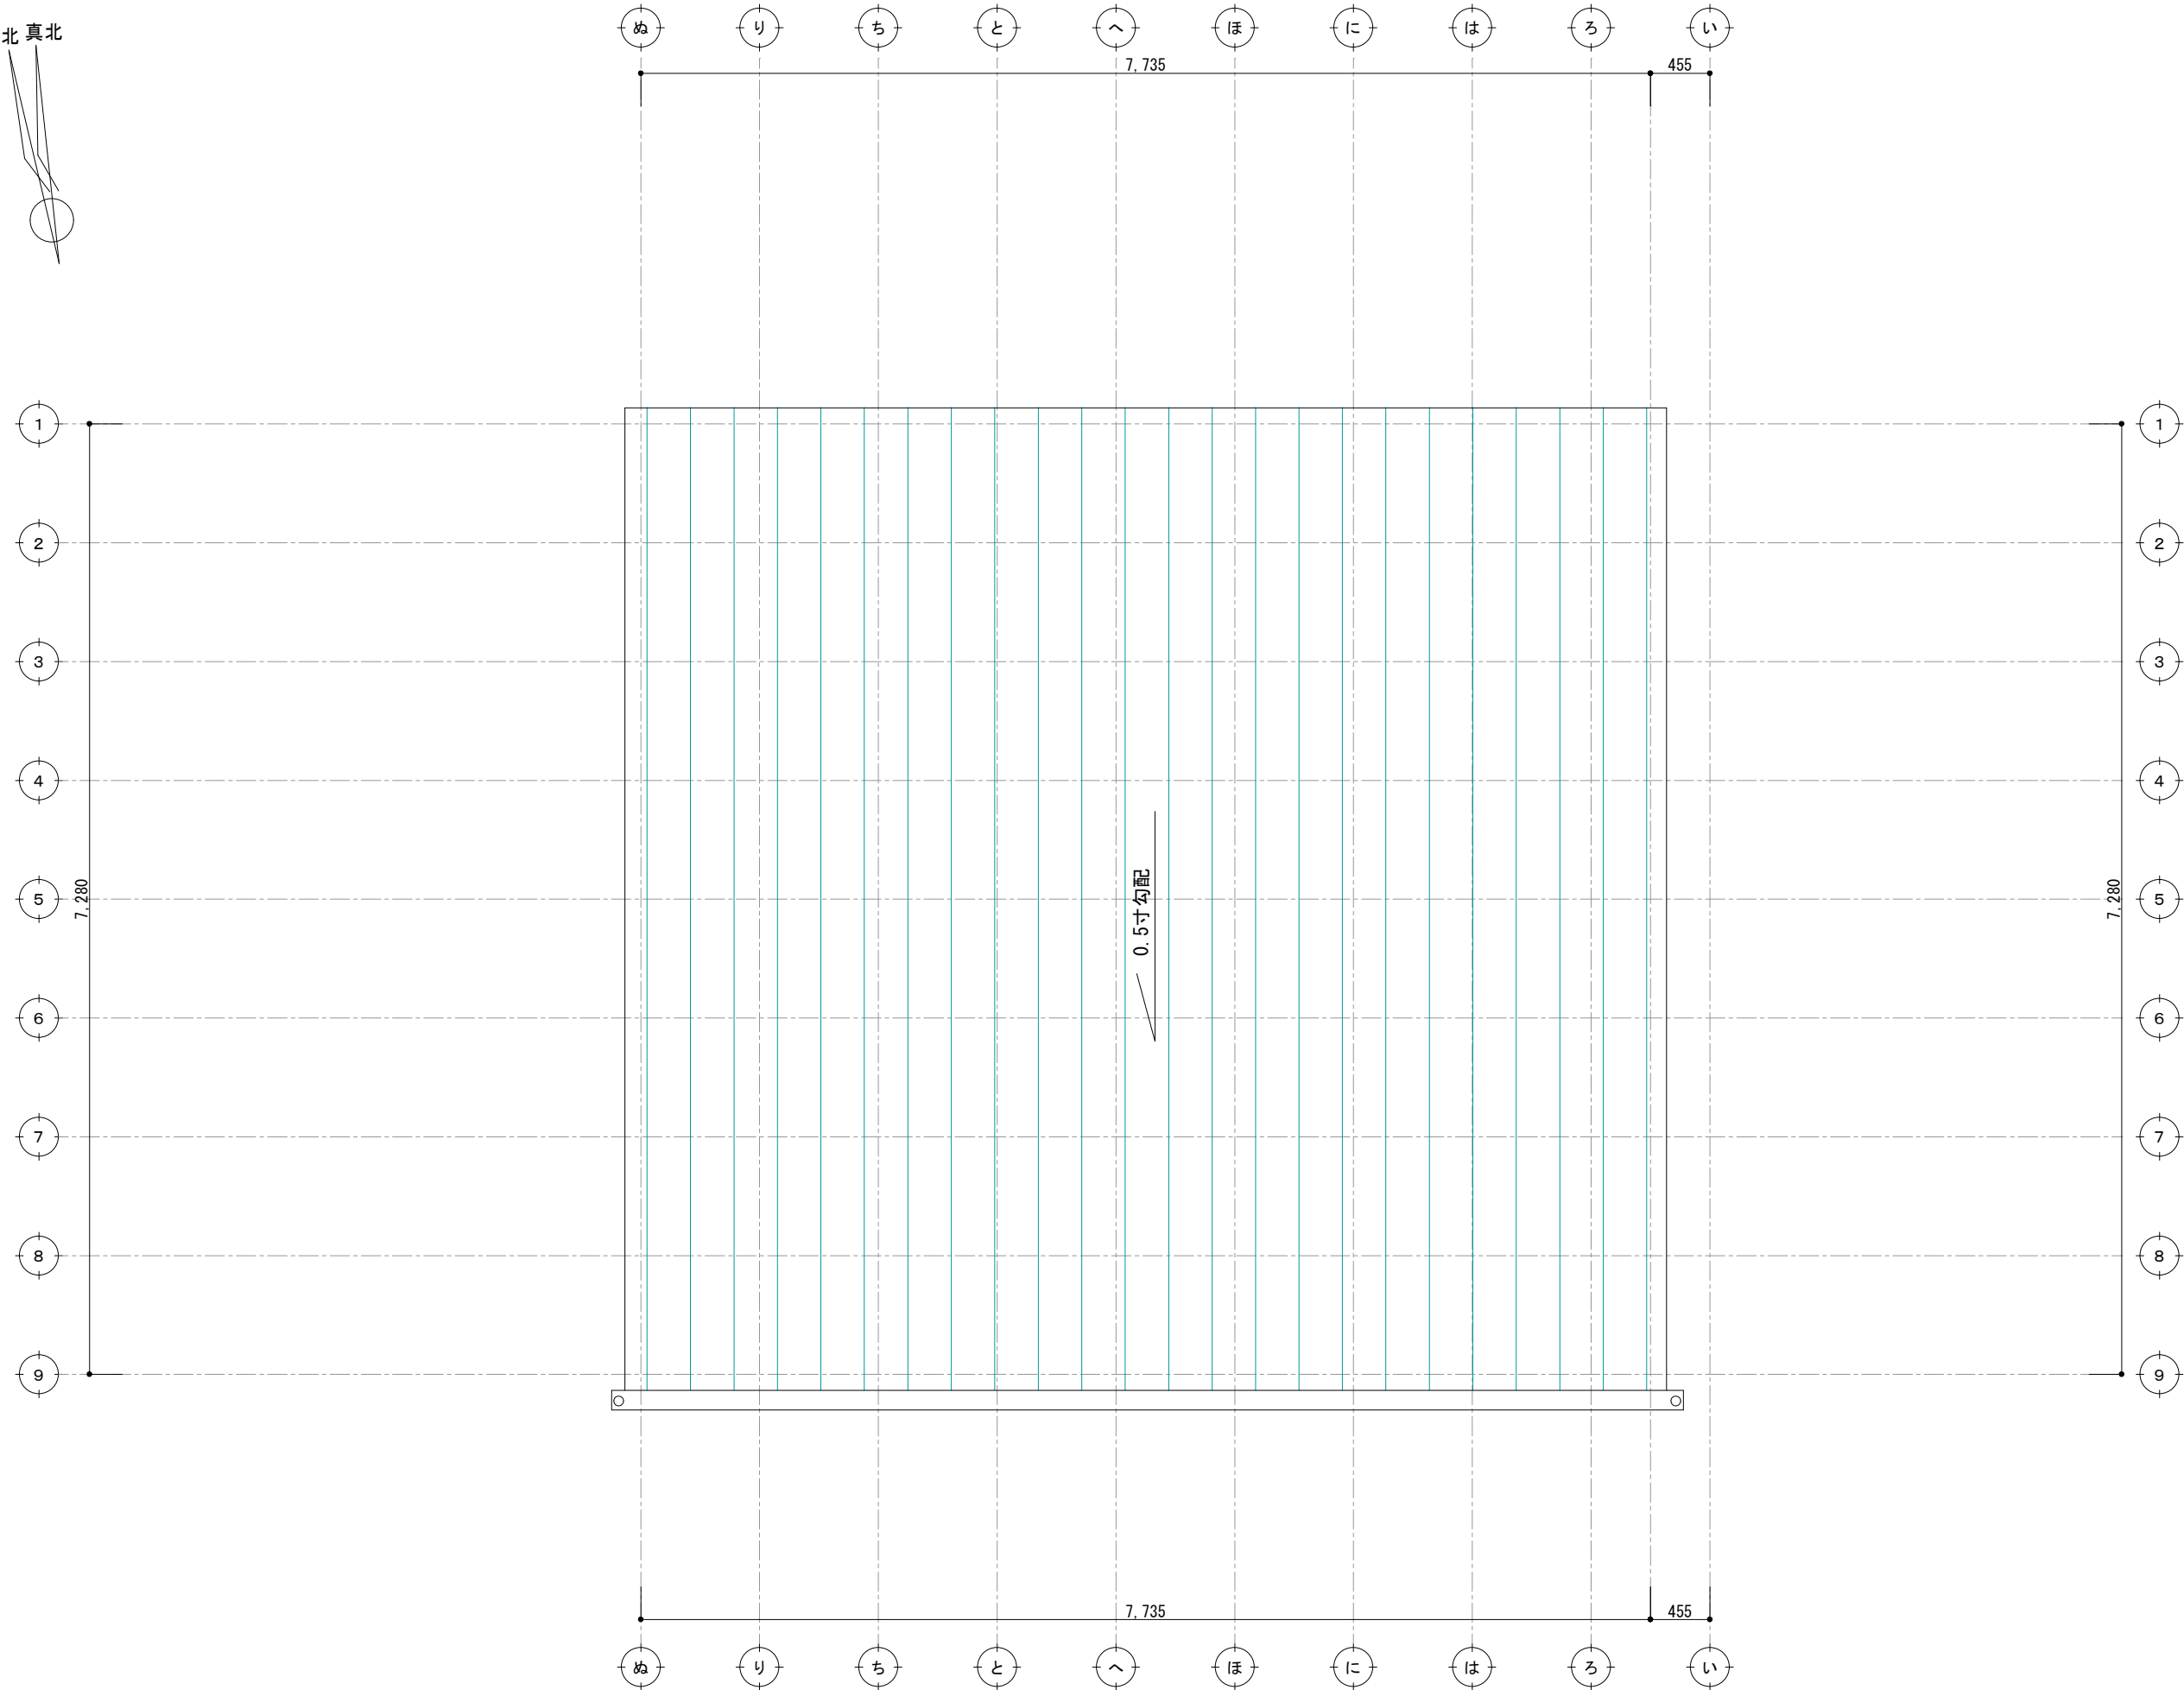

太陽光あり


決定図

訂正	浜岡一級総合設計事務所 一級建築士事務所 静岡県知事登録第 (10)2441 号 一級建築士 大臣登録第 365879 号 西原利昌		 ピージーハウス	株式会社 LIFEFUND InDesign office 一級建築士事務所 事務所登録 (2) 第7595号 一級建築士登録 第179770号 鈴木 達男 〒432-8023 静岡県浜松市中央区鴨江3丁目70番23号	年月日 2024. 11. 09 縮尺 1/100	件名 竹内優太郎様邸 新築工事 図名		設計	IC	工事	図番
								倉田		青島	

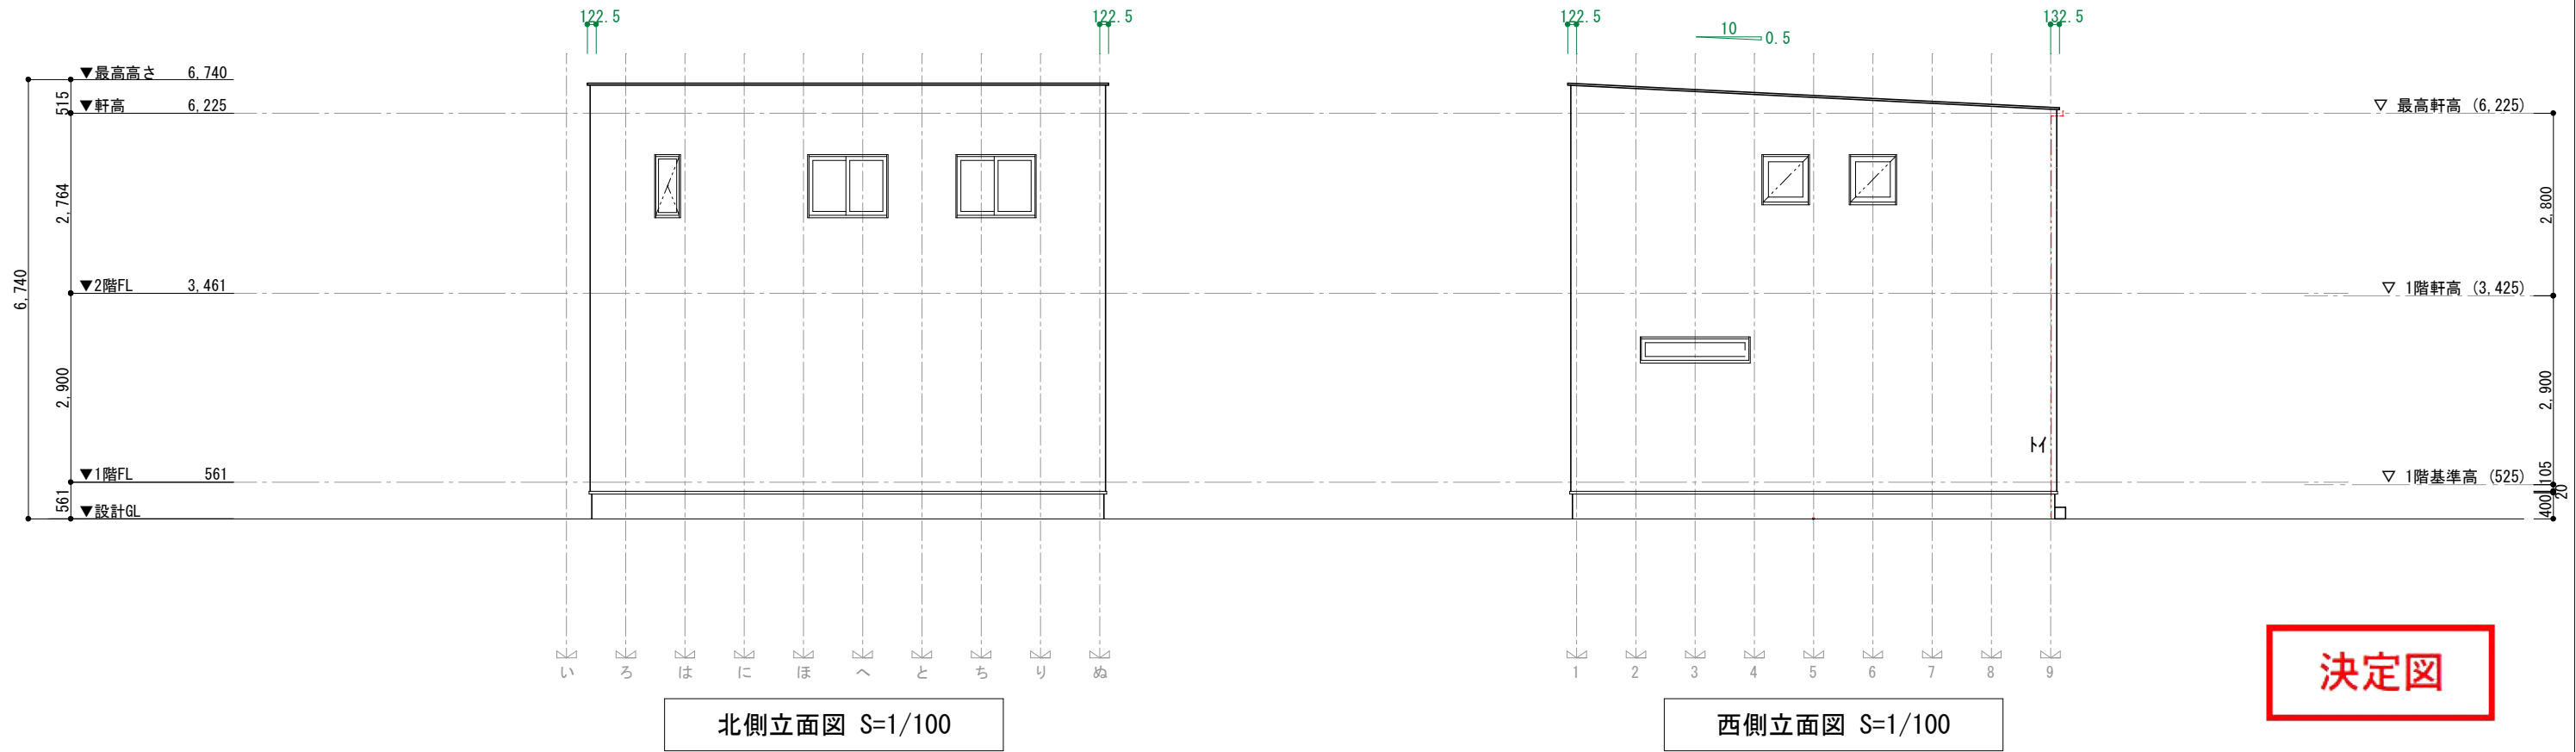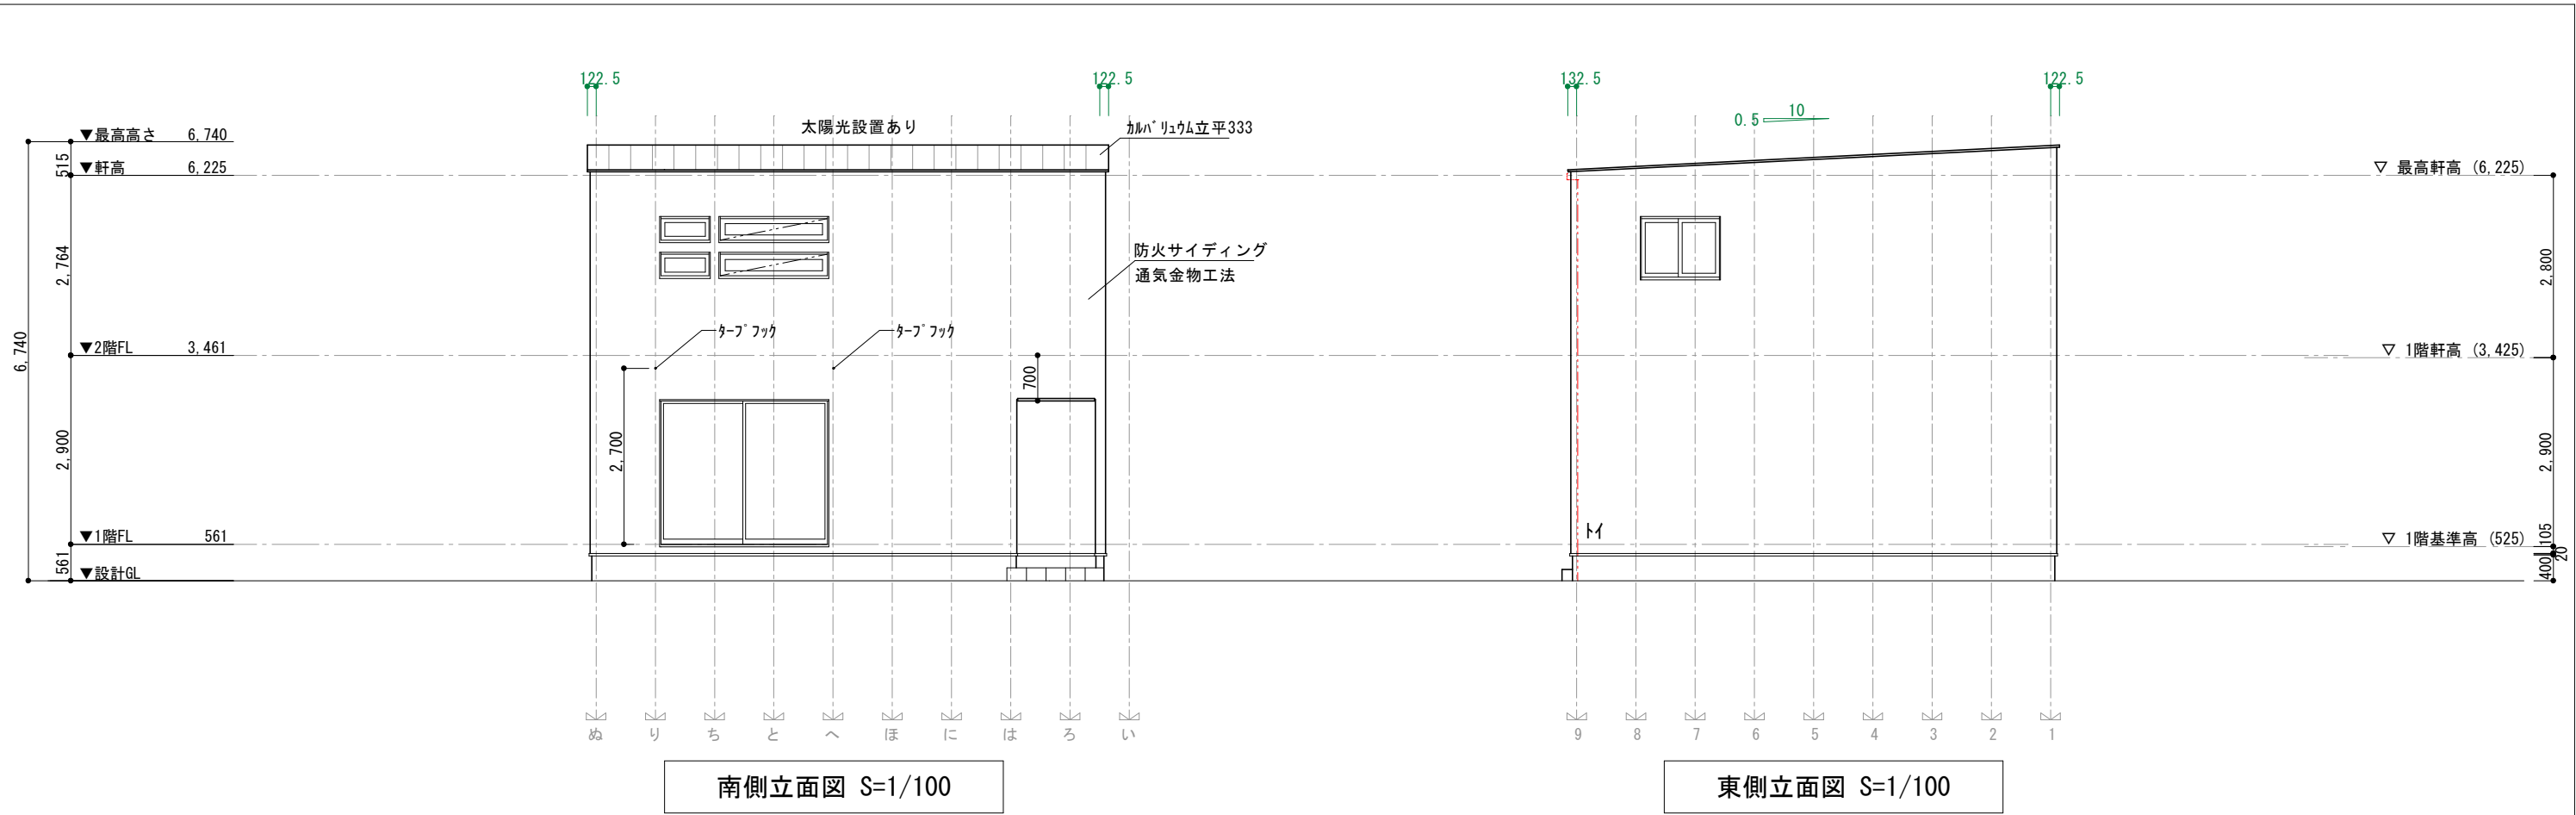


決定図

訂正	浜岡一級総合設計事務所 一級建築士事務所 静岡県知事登録第 (10)2441 号 一級建築士 大臣登録第 365879 号 西原利昌		株式会社 LIFEFUND InDesign office 一級建築士事務所 事務所登録 (2) 第7595号 一級建築士登録 第179770号 鈴木 達男 〒432-8023 静岡県浜松市中央区鴨江3丁目70番23号	年月日	件名		設計	IC	工事	図番
				2024.11.17	竹内優太郎様邸 新築工事		倉田		青島	4
				縮尺	図名					




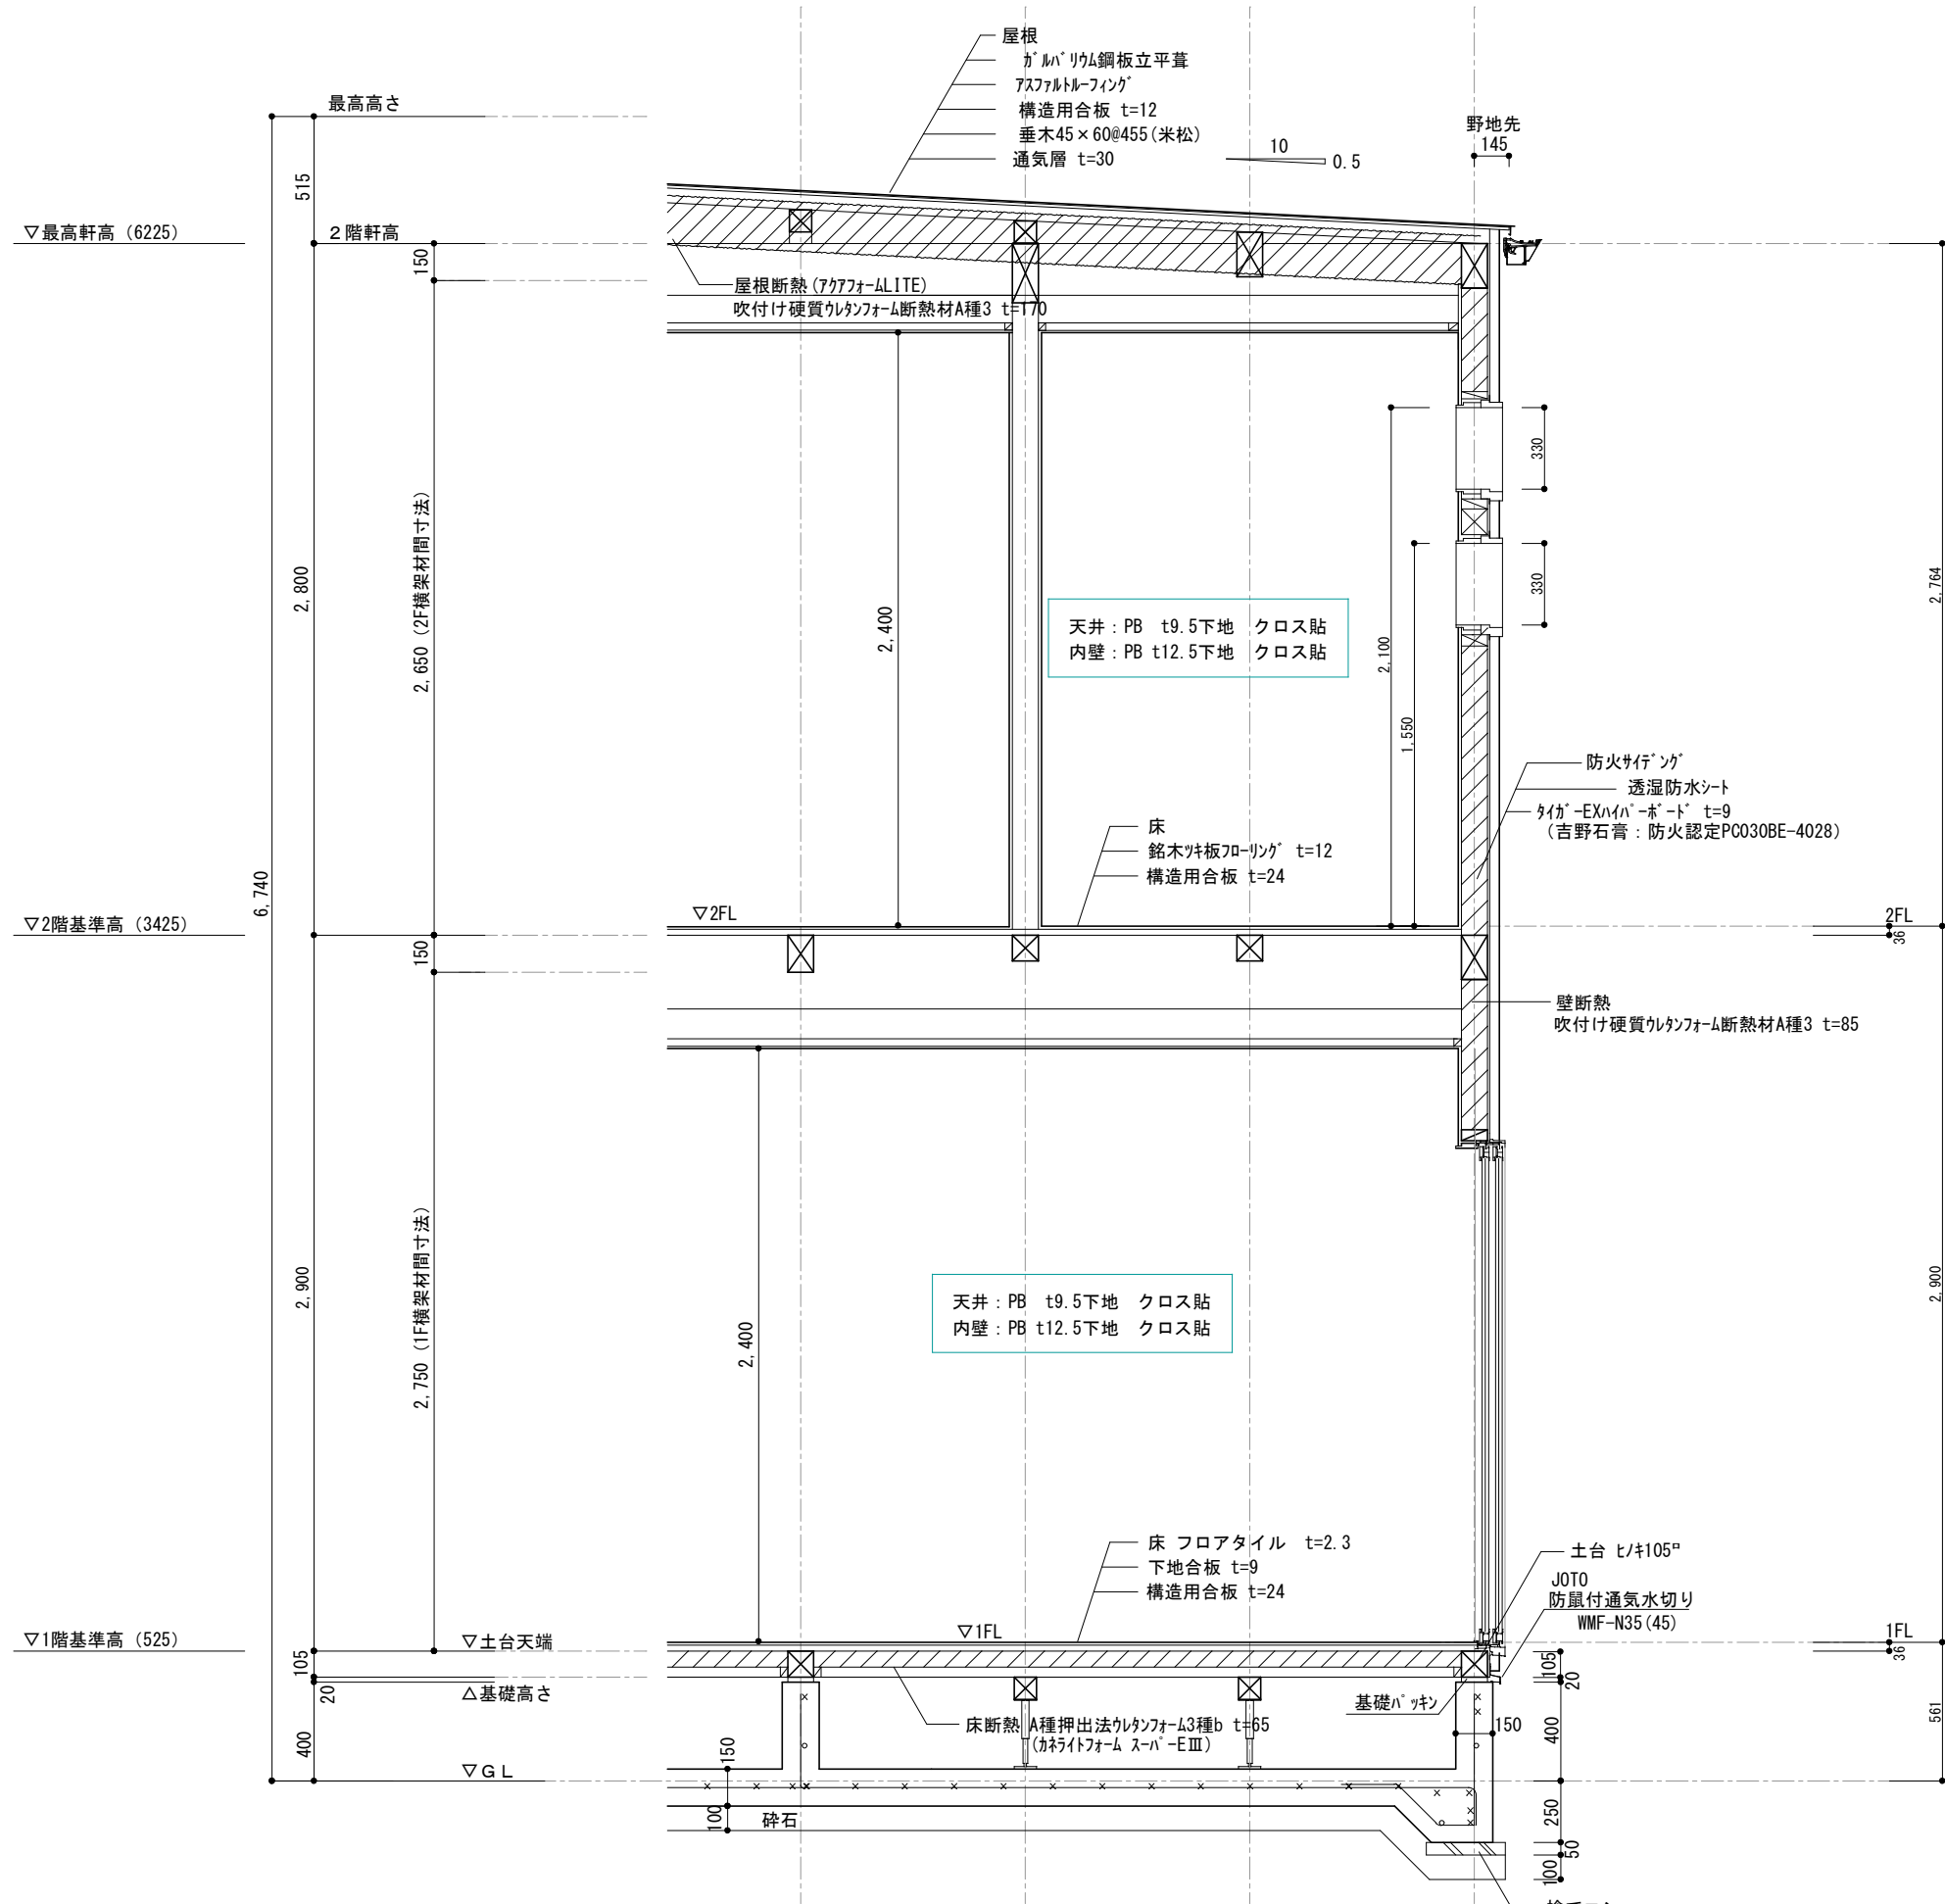


決定図





訂正	浜岡一級総合設計事務所 一級建築士事務所 静岡県知事登録第 (10)2441 号 一級建築士 大臣登録第 365879 号 西原利昌		株式会社 LIFEFUND InDesign office 一級建築士事務所 事務所登録 (2) 第7595号 一級建築士登録 第179770号 鈴木 達男 〒432-8023 静岡県浜松市中央区鴨江3丁目70番23号	年月日 2024. 11. 20	件名 竹内優太様邸 新築工事	設計 IC 工事 図番	倉田	青島	A-5
				縮尺 1/100	図名 矩計図				

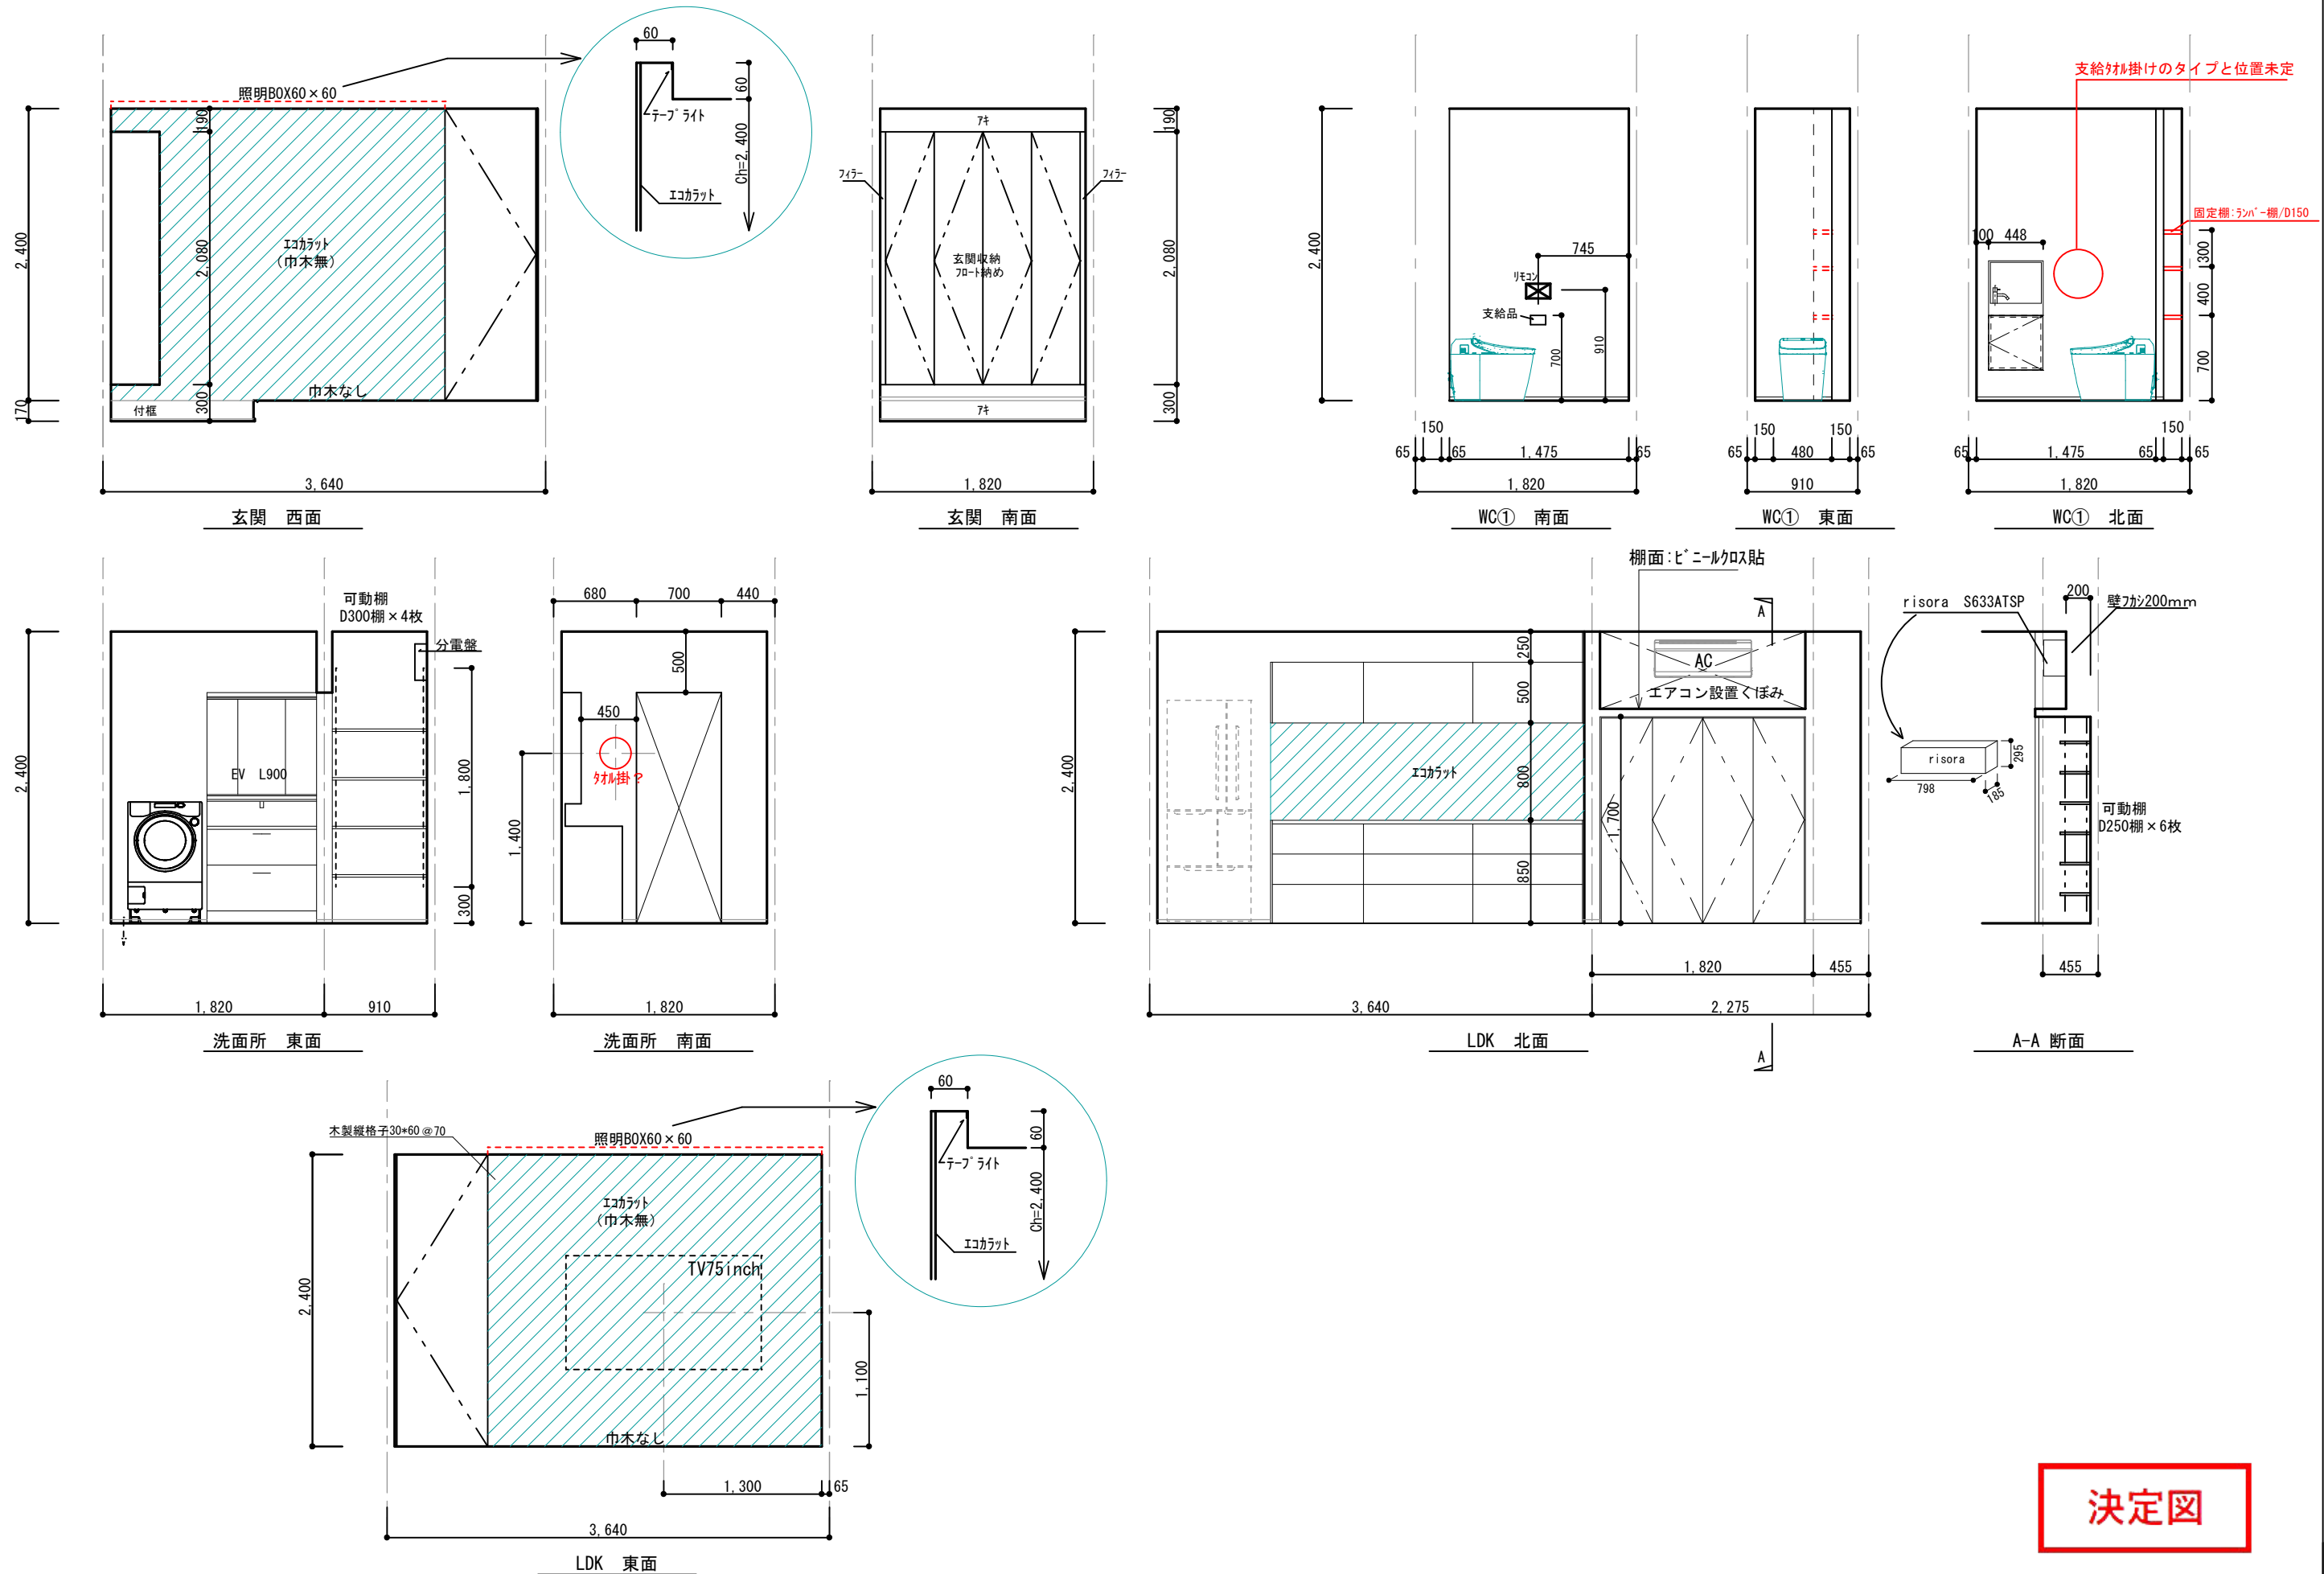



訂正	浜岡一級総合設計事務所 一級建築士事務所 静岡県知事登録第 (10)2441 号 一級建築士 大臣登録第 365879 号 西原利昌	LIFEFUND PG HOUSE	株式会社 LIFEFUND InDesign office 一級建築士事務所 事務所登録 (2)第7595号 一級建築士登録 第179770号 鈴木 達男 〒432-8023 静岡県浜松市中央区鴨江3丁目70番23号	年月日 2024.11.20	件名 竹内優太郎様 新築工事	設計 倉田	IC	工事 青島	図番 6-1
				縮尺 1/50	図名 展開図-1				

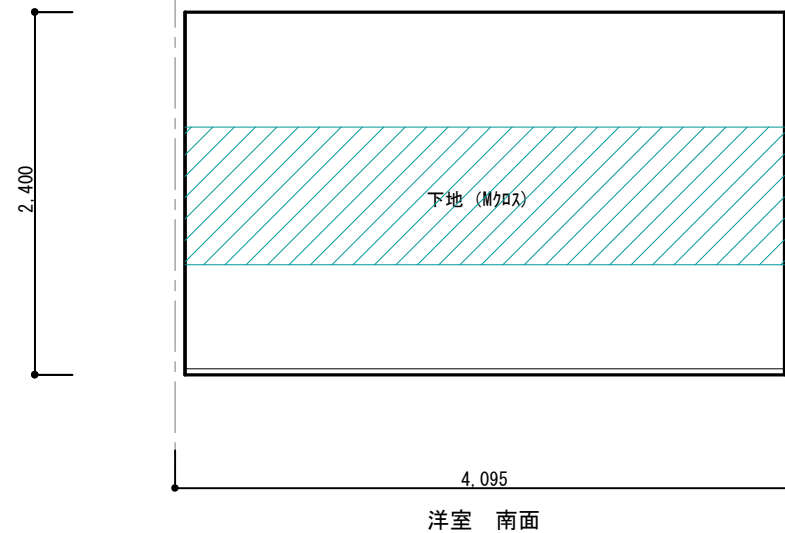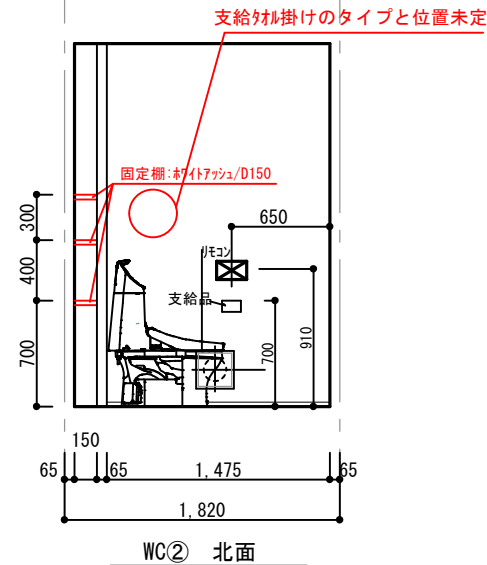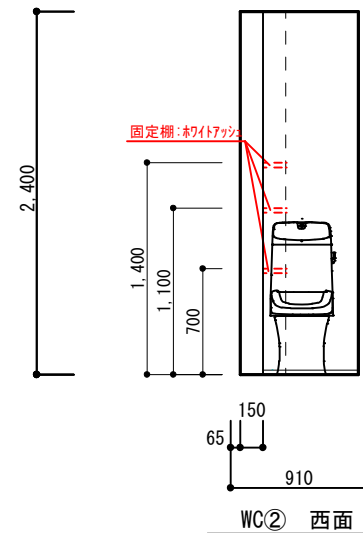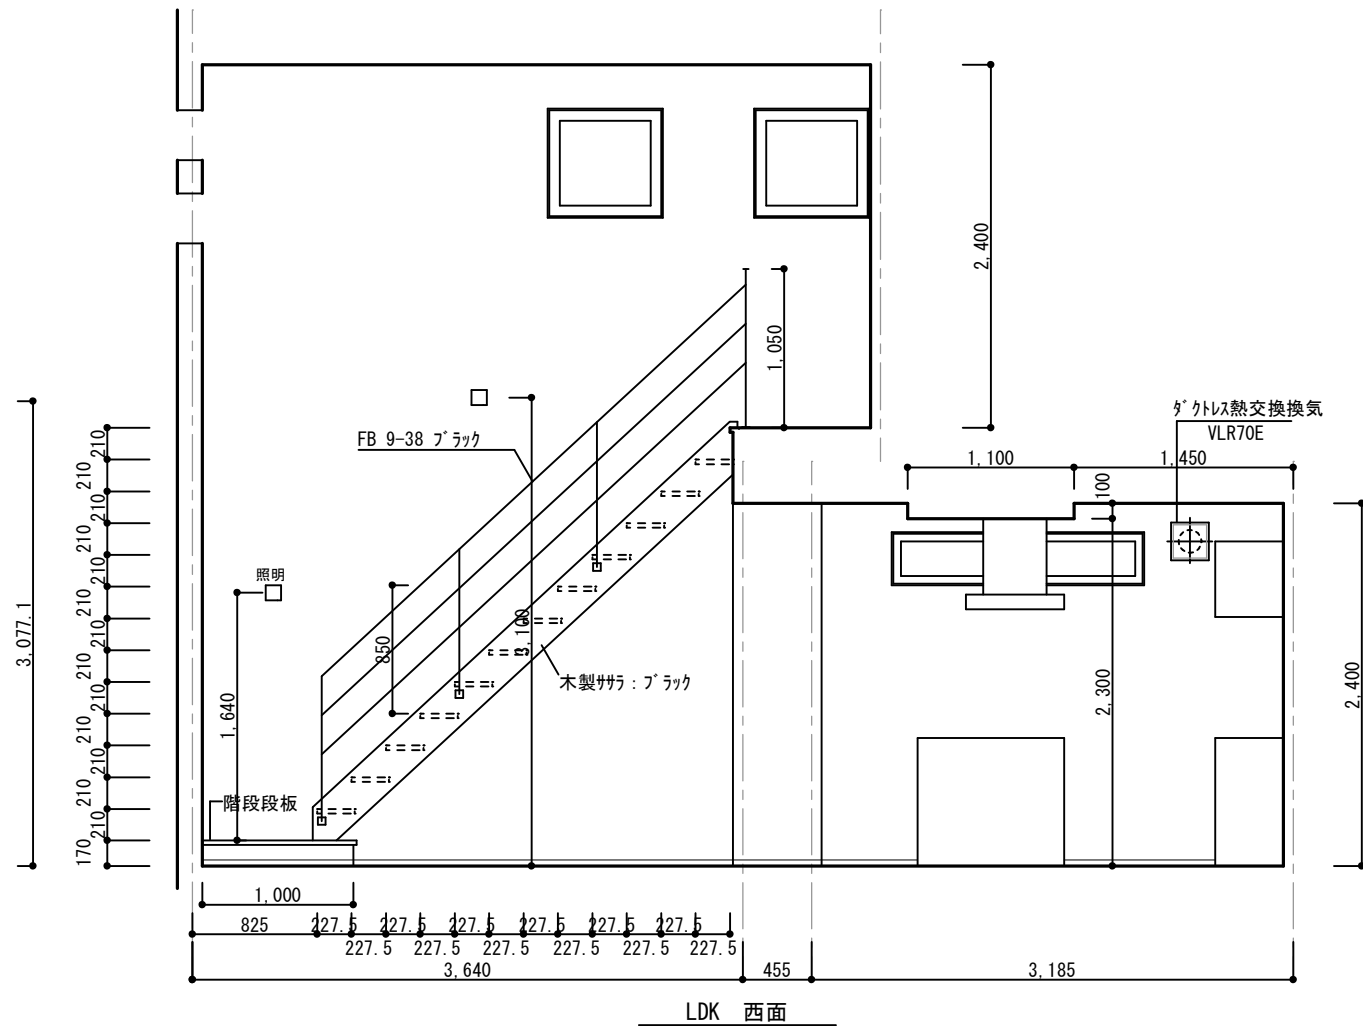

決定図

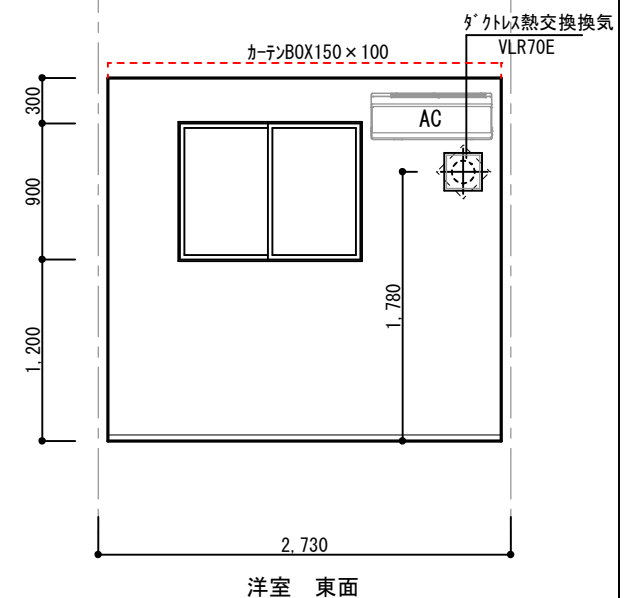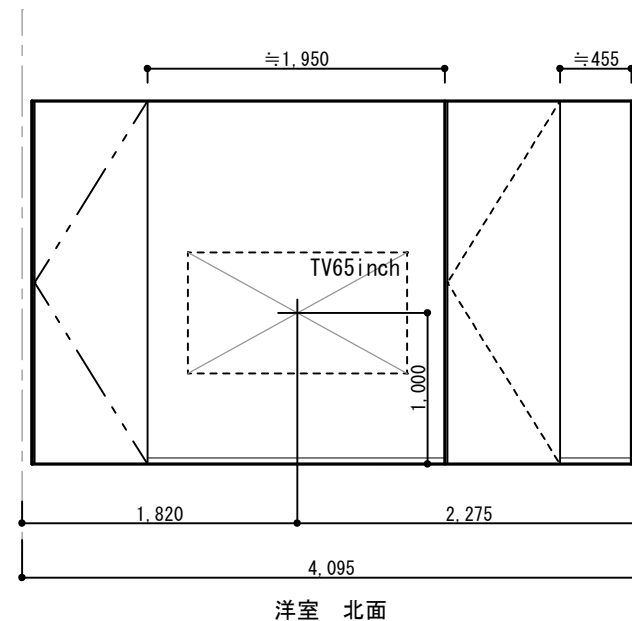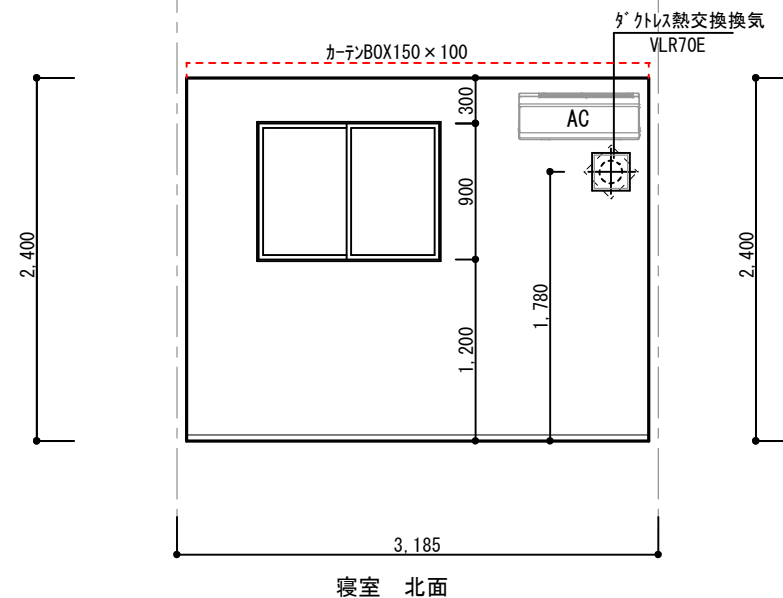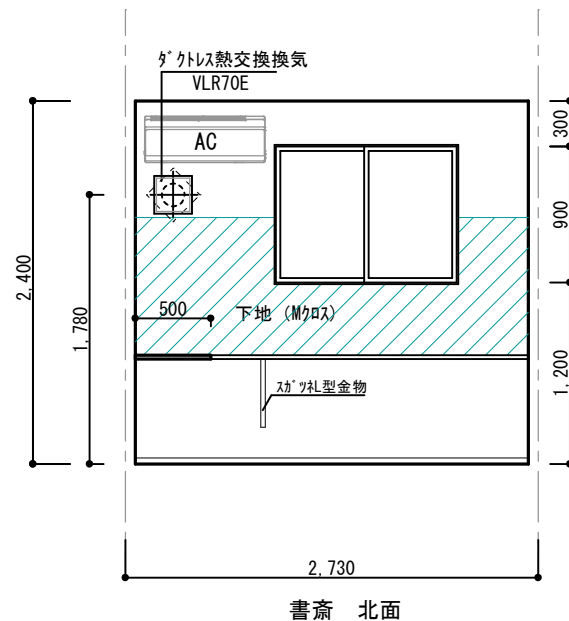

訂正	浜岡一級総合設計事務所 一級建築士事務所 静岡県知事登録第 (10) 2441 号 一級建築士 大臣登録第 365879 号 西原利昌	LIFEFUND PG HOUSE	株式会社 LIFEFUND InDesign office 一級建築士事務所 事務所登録 (2) 第7595号 一級建築士登録 第179770号 鈴木 達男 〒432-8023 静岡県浜松市中央区鴨江3丁目70番23号	年月日 2024.12.11 縮尺 1/50	件名 竹内優太郎様 新築工事 図名 展開図-2		設計 倉田	IC	工事 青島	図番 6-2
----	---	----------------------	---	---------------------------------	----------------------------------	--	----------	----	----------	-----------

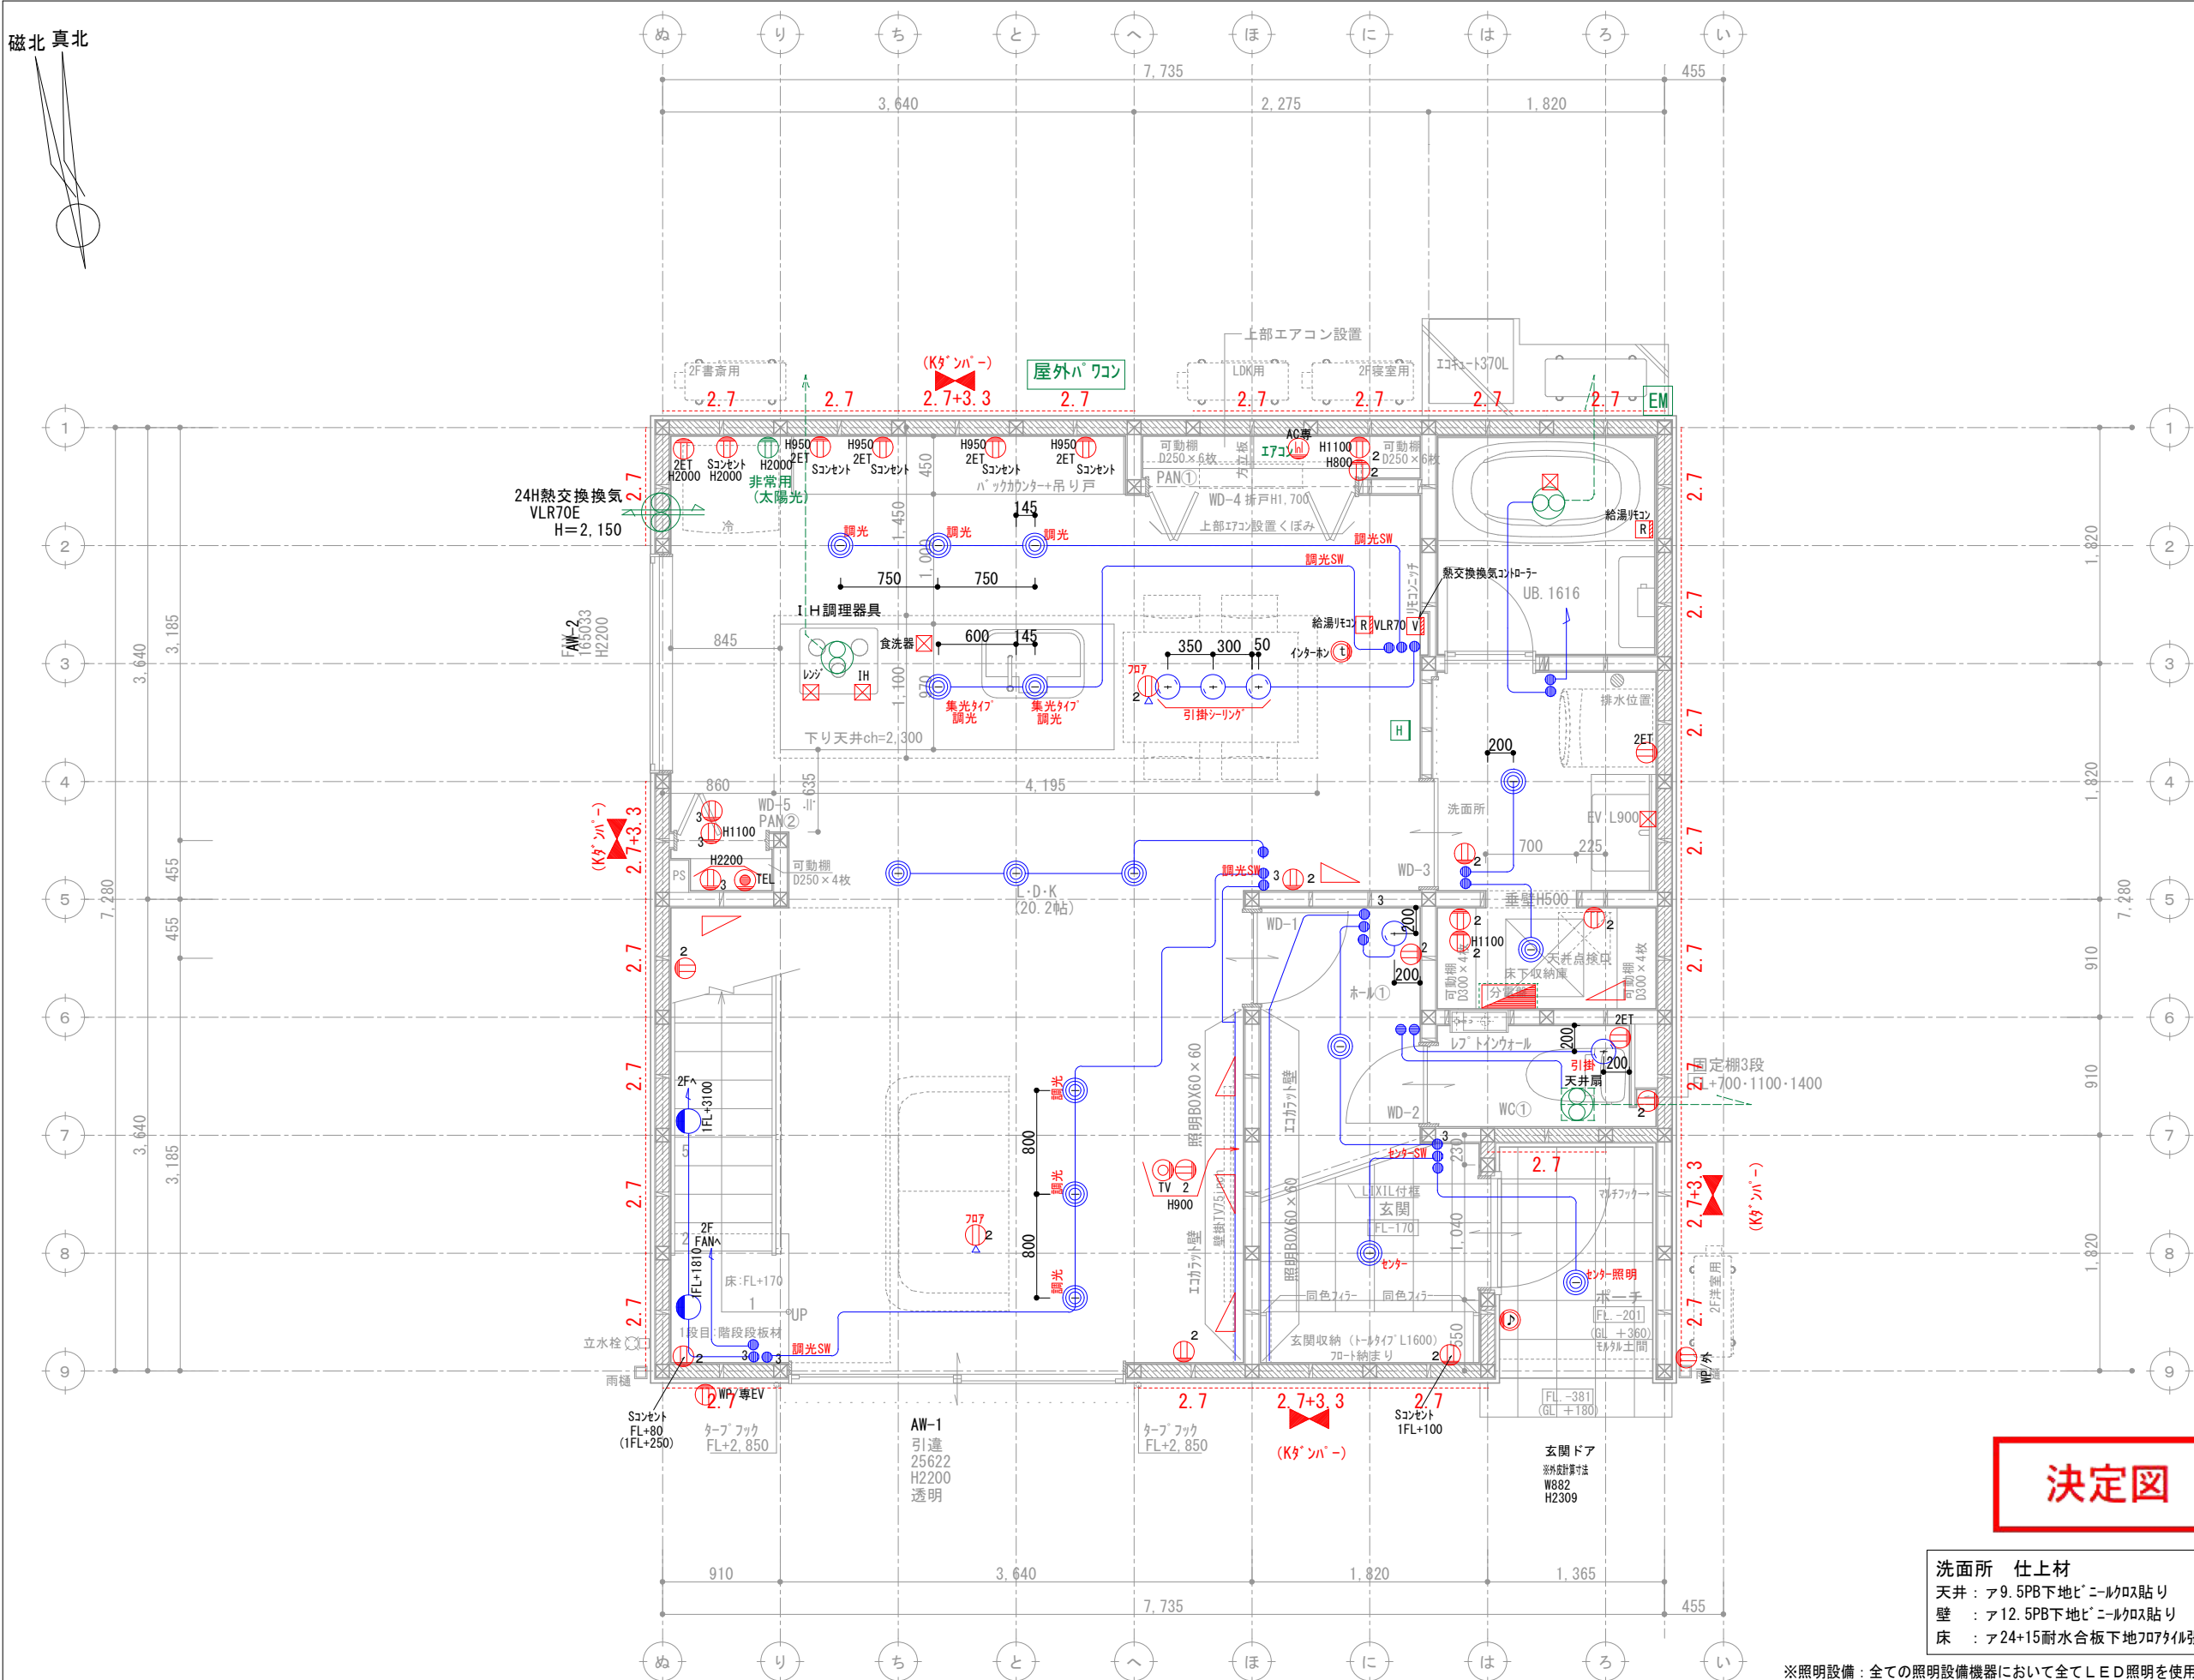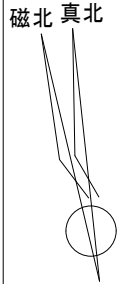

壁付 住宅用火災報知器			数量
H 熱感知	熱感知器	電池式(単独型)	
		露出型	
壁付 住宅用火災報知器			数量
S 煙感知	煙感知器	電池式(単独型)	
		露出型	

※ 煙感知器は壁・梁より600mm以上離す
壁に取付ける場合、
天井から150mm以上500mm以内離す
換気扇・エアコン吹出口から1500mm以上離す
※ 全室LED照明とする。
※ 標準天井高さ2,400

- * 凡例
- 管柱 (105×105)
- K's Paner
(3.30倍 FRM-0641)
- 片筋違い
(2.00倍 45×90)
(例 左:柱脚 右:柱頭)
- たすき掛筋違い
(4.00倍 45×90)
- 構造用合板 (2.70倍)
(t=9 タイフ EXハイパー)
- 床点検口
- 天井点検口
- 換気扇
- 熱交換換気扇VLR-70

※表記なきガラスは型ガラス


アドバンスシリーズ		
スマートデザイン (外部)		
凡例	1	コンセント 1ヶロ
2	コンセント 2ヶロ	
3	コンセント 3ヶロ	
1ET	コンセント1ヶロ接地ターミナル付	
2ET	コンセント2ヶロ接地ターミナル付	
WP	コンセント 防水型	
エアコン	エアコン用コンセント	
200V	200V用コンセント	
WP	防雨入線プレート	
WP	防雨入線プレート	
スイッチ	スイッチ	
3	3路スイッチ	
4	4路スイッチ	
直結電源	直結電源	
TV	テレビ取出口 (テレビホリガイド)	
TEL	電話取出口 (テレビホリガイド)	
LAN	LAN取出口 (テレビホリガイド)	
壁照明	壁照明	
リモコン	リモコン(給湯関係・ルフロ)	
メーター	メーター	
分電盤	分電盤	
チャイム	チャイム	

※ACコンセント天井付け
※TVアンテナ工事
※スイッチはFL+1100、コンセントはFL+200

決定図

洗面所 仕上材
天井 : ア9.5PB下地ビニールクロス貼り
壁 : ア12.5PB下地ビニールクロス貼り
床 : ア24+15耐水合板下地フロアタイル張り

※照明設備 : 全ての照明設備機器において全てLED照明を使用している

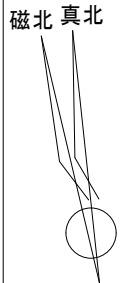

壁付け 住宅用火災報知器			数量
H 熱感知	熱感知器	電池式(単独型)	
		露出型	
壁付け 住宅用火災報知器			数量
S 煙感知	煙感知器	電池式(単独型)	
		露出型	

※ 煙感知器は壁・梁より600mm以上離す
壁に取付ける場合、
天井から150mm以上500mm以内離す
換気扇・エアコン吹出口から1500mm以上離す
※ 全室LED照明とする。
※ 標準天井高さ2,400

* 凡例

管柱 (105×105)

K&P (3.30倍 FRM-0641)

片筋違 (2.00倍 45×90)
(例 左:柱脚 右:柱頭)

たすき掛筋違 (4.00倍 45×90)

構造用合板 (2.70倍)
(t=9 3枚 EXハイバ)

床点接合

天井点接合

換気扇


熱交換換気扇VLR-70

※表記なきガラスは型ガラス


アドバンスシリーズ		
スマートデザイン (外部)		
凡例	1	コンセント 1ヶロ
	2	コンセント 2ヶロ
	3	コンセント 3ヶロ
	1ET	コンセント1ヶロ接地ターミナル付
	2ET	コンセント2ヶロ接地ターミナル付
	WP	コンセント 防水型
		エアコン用コンセント
		200V用コンセント
	WP	防雨入線プレート
		スイッチ
	3	3路スイッチ
	4	4路スイッチ
		直結電源
	TV	テレビ取出口
	TEL	電話取出口 (テレホンガイド)
	LAN	LAN取出口 (テレホンガイド)
		壁照明
		リモコン(給湯関係・ルフロ)
		メーター
		分電盤
		チャイム

※ACコンセント天井付け
※TVアンテナ工事
※スイッチはFL+1100、コンセントはFL+200

決定図

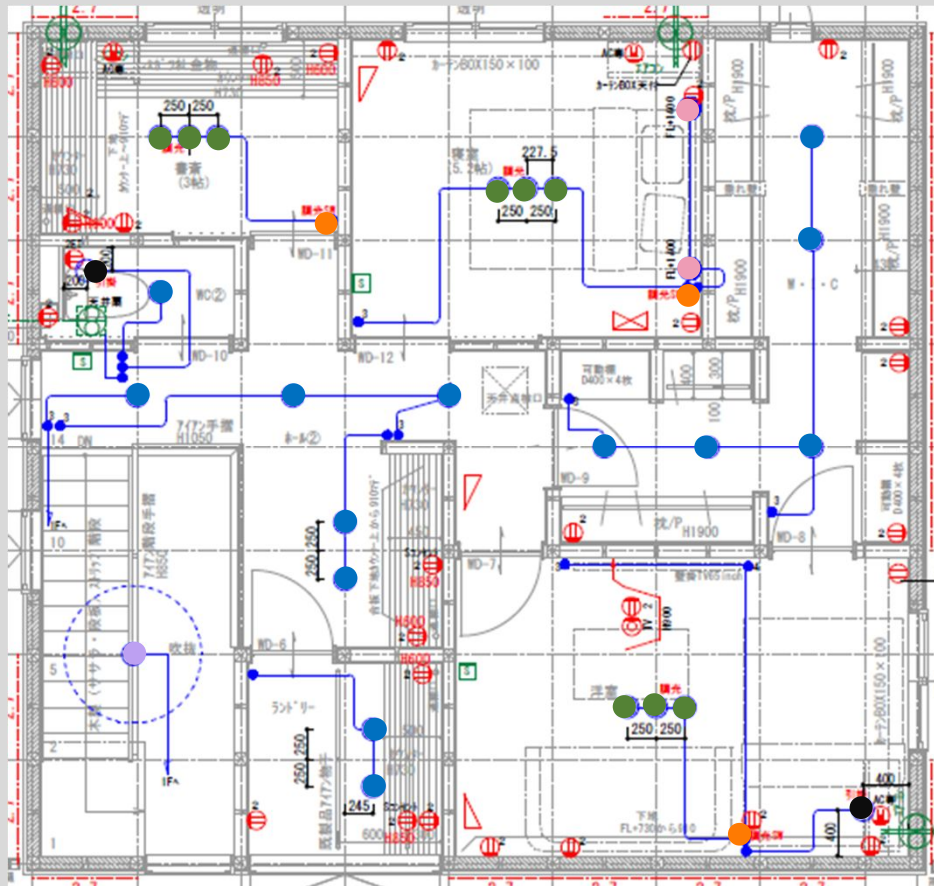

2階

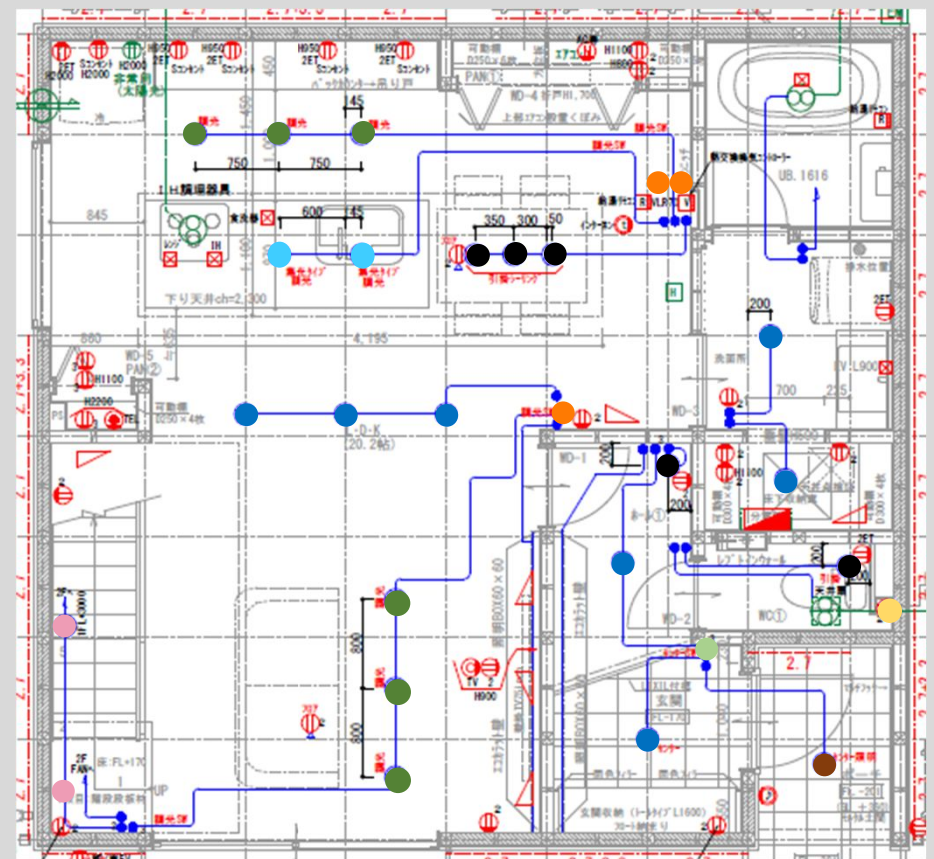

1階

階段/寝室 ● × 4

DBK41130YG



DBK-41130 YG

電球色 / 2700K・Ra83

定格光束 消費電力 固有エネルギー消費効率
93lm 6.1W 15.2lm/W

¥15,800-(税抜) (LED内蔵)

LED LED 6.1W

白熱灯60W相当

- 鋼板 黒塗装
- 径・100 出65mm 0.5kg
- 11VA
- 上下面開放 ● AC100V
- 調光可能(1%~100%)
- 調光にはLED専用調光器(別売)を
ご使用ください。
- 光源寿命40,000時間

調光

LED交換
不可



集光ダウンライト ● × 2

DDL-4787YBG



DDL-4787 YBG

電球色 / 2700K・Ra83

定格光束 消費電力 固有エネルギー消費効率
400lm 5.8W 68.9lm/W

¥7,500-(税抜) (LED内蔵)

LED

LED 5.8W

白熱灯60W相当

- アルミダイカスト 黒塗装
- アクリル 透明
- 径φ111 埋込穴φ100 埋込深78mm 0.4kg
- 7VA ● 別売レンズ付 ● AC100V
- 調光可能(1%~100%)
- 調光にはLED専用調光器(別売)を
ご使用ください。
- 光源寿命60,000時間
- 取付可能天井厚5~25mm

LED交換
不可

防雨形

温度保護
機能付

埋込
必要高

80

傾斜天井
55°

標準耐火

準耐火

標準耐火

標準耐火

基本ダウンライト

● × 20 (7+13)

DDL6102YB



DDL-6102 YB

電球色 / 2700K・Ra83

定格光束 消費電力 固有エネルギー消費効率
370lm 4.6W 80.4lm/W

¥3,600-(税抜) (LED内蔵)

LED

LED 4.6W

白熱灯60W相当

- 鋼板 黒塗装
- アクリル 乳白(マット)
- 径φ116 埋込穴φ100 埋込深70mm 0.3kg
- 8VA
- 拡散パネル付
- AC100V
- 光源寿命60,000時間
- 取付可能天井厚5~25mm
- 調光器併用不可

LED交換
不可

防雨形

温度保護
機能付

埋込
必要高

100

傾斜天井
55°

標準耐火

標準耐火

調光ダウンライト

● × 15

DDL6004YBG



DDL-6004 YBG

電球色 / 2700K・Ra83

定格光束 消費電力 固有エネルギー消費効率
600lm 7.8W 76.9lm/W

¥7,000-(税抜) (LED内蔵)

LED

LED 7.8W

白熱灯100W相当

- 鋼板 黒塗装
- アクリル 乳白(マット)
- 径φ116 埋込穴φ100 埋込深71mm 0.3kg
- 8VA
- 拡散パネル付
- AC100V
- 光源寿命60,000時間
- 取付可能天井厚5~25mm
- 調光器併用不可

LED交換
不可

防雨形

温度保護
機能付

埋込
必要高

100

傾斜天井
55°

標準耐火

標準耐火

ペンダント灯 ● × 7

ホール①/ダイニング/WC①②/洋室

引掛けシーリングのみ
※引き渡し後お客様持込

ドアホン：VL-SZ30KL

(Panasonic)



★オプション

内部：アドバンス
マッドブラック



外部：スマートデザイン



外壁色に合わせ。

シーリングファン

● × 1



リモコン

DP-40332 F

¥43,000-(税抜)

- 鋼板・鋼管・アルミダイカスト 黒塗装
- プラスチック・シリコン 黒
- 径φ800 高301mm 3.7kg
- リモコンスイッチ付 正転逆転切替・風量3段切替
- AC100V
- 別売延長パイプ使用時傾斜天井使用可能
- チャンネル切替不可

簡易取付式






DP-40334

¥2,500-(税抜)

- 鋼管 黒塗装
- 径φ20 長400mm 0.4kg
- 傾斜天井にも使用可能(25°まで)
- 注)延長パイプの加工は別注にて承ります。


決定図

2024.12.11.

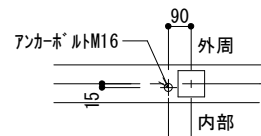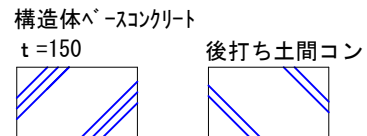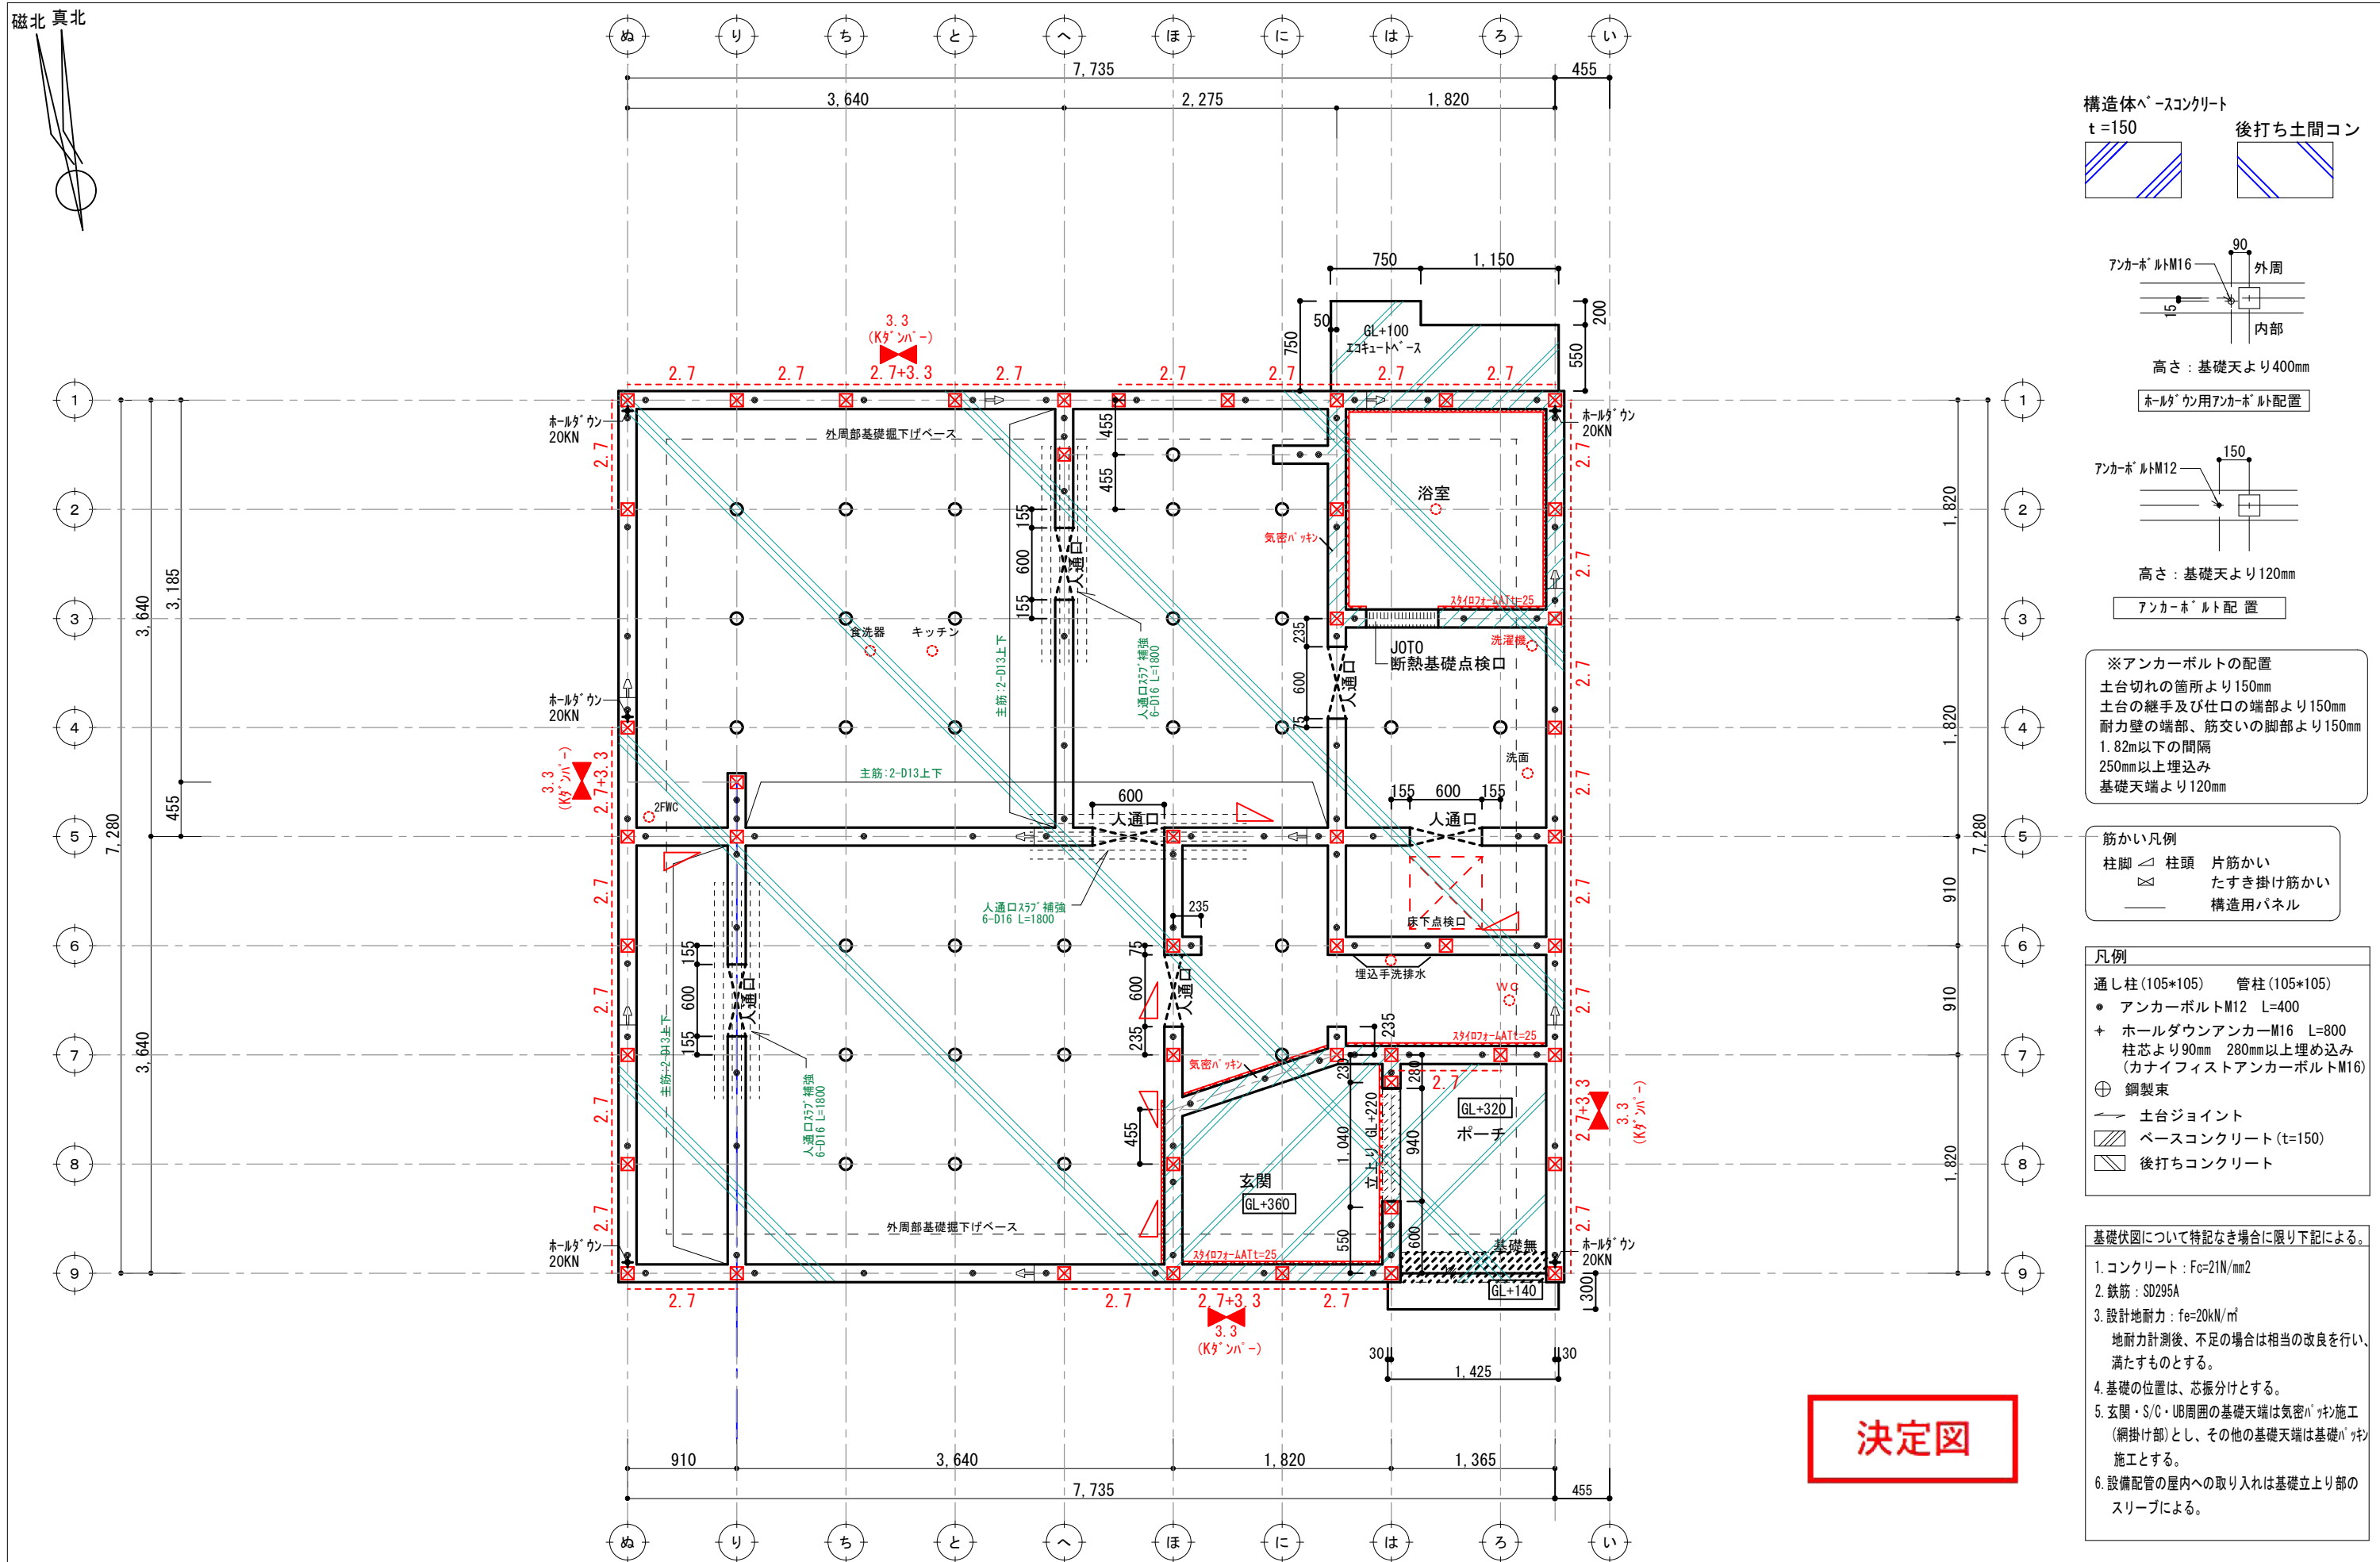

高さ：基礎天より400mm

ホールダウンアンカーボルト配置

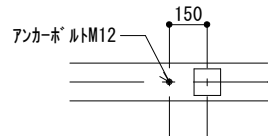

高さ：基礎天より120mm


アンカーボルト配置

※アンカーボルトの配置
土台切れの箇所より150mm
土台の継手及び仕口の端部より150mm
耐力壁の端部、筋交いの脚部より150mm
1.82m以下の間隔
250mm以上埋込み
基礎天端より120mm

筋かい凡例
柱脚 柱頭 筋かい
たすき掛け筋かい
構造用パネル


凡例
通し柱(105*105) 管柱(105*105)
● アンカーボルトM12 L=400
+ ホールダウンアンカーM16 L=800
柱芯より90mm 280mm以上埋め込み
(カナフィーストアンカーボルトM16)
⊕ 鋼製束
→ 土台ジョイント
ベースコンクリート(t=150)
後打ちコンクリート

基礎伏図について特記なき場合に限り下記による。
1. コンクリート：Fc=21N/mm²
2. 鉄筋：SD295A
3. 設計地耐力：fe=20kN/m²
地耐力計測後、不足の場合は相当の改良を行い、
満たすものとする。
4. 基礎の位置は、芯振分けとする。
5. 玄関・S/C・UB周囲の基礎天端は気密パッキン施工
(網掛け部)とし、その他の基礎天端は基礎パッキン
施工とする。
6. 設備配管の屋内への取り入れは基礎立上り部の
スリーブによる。

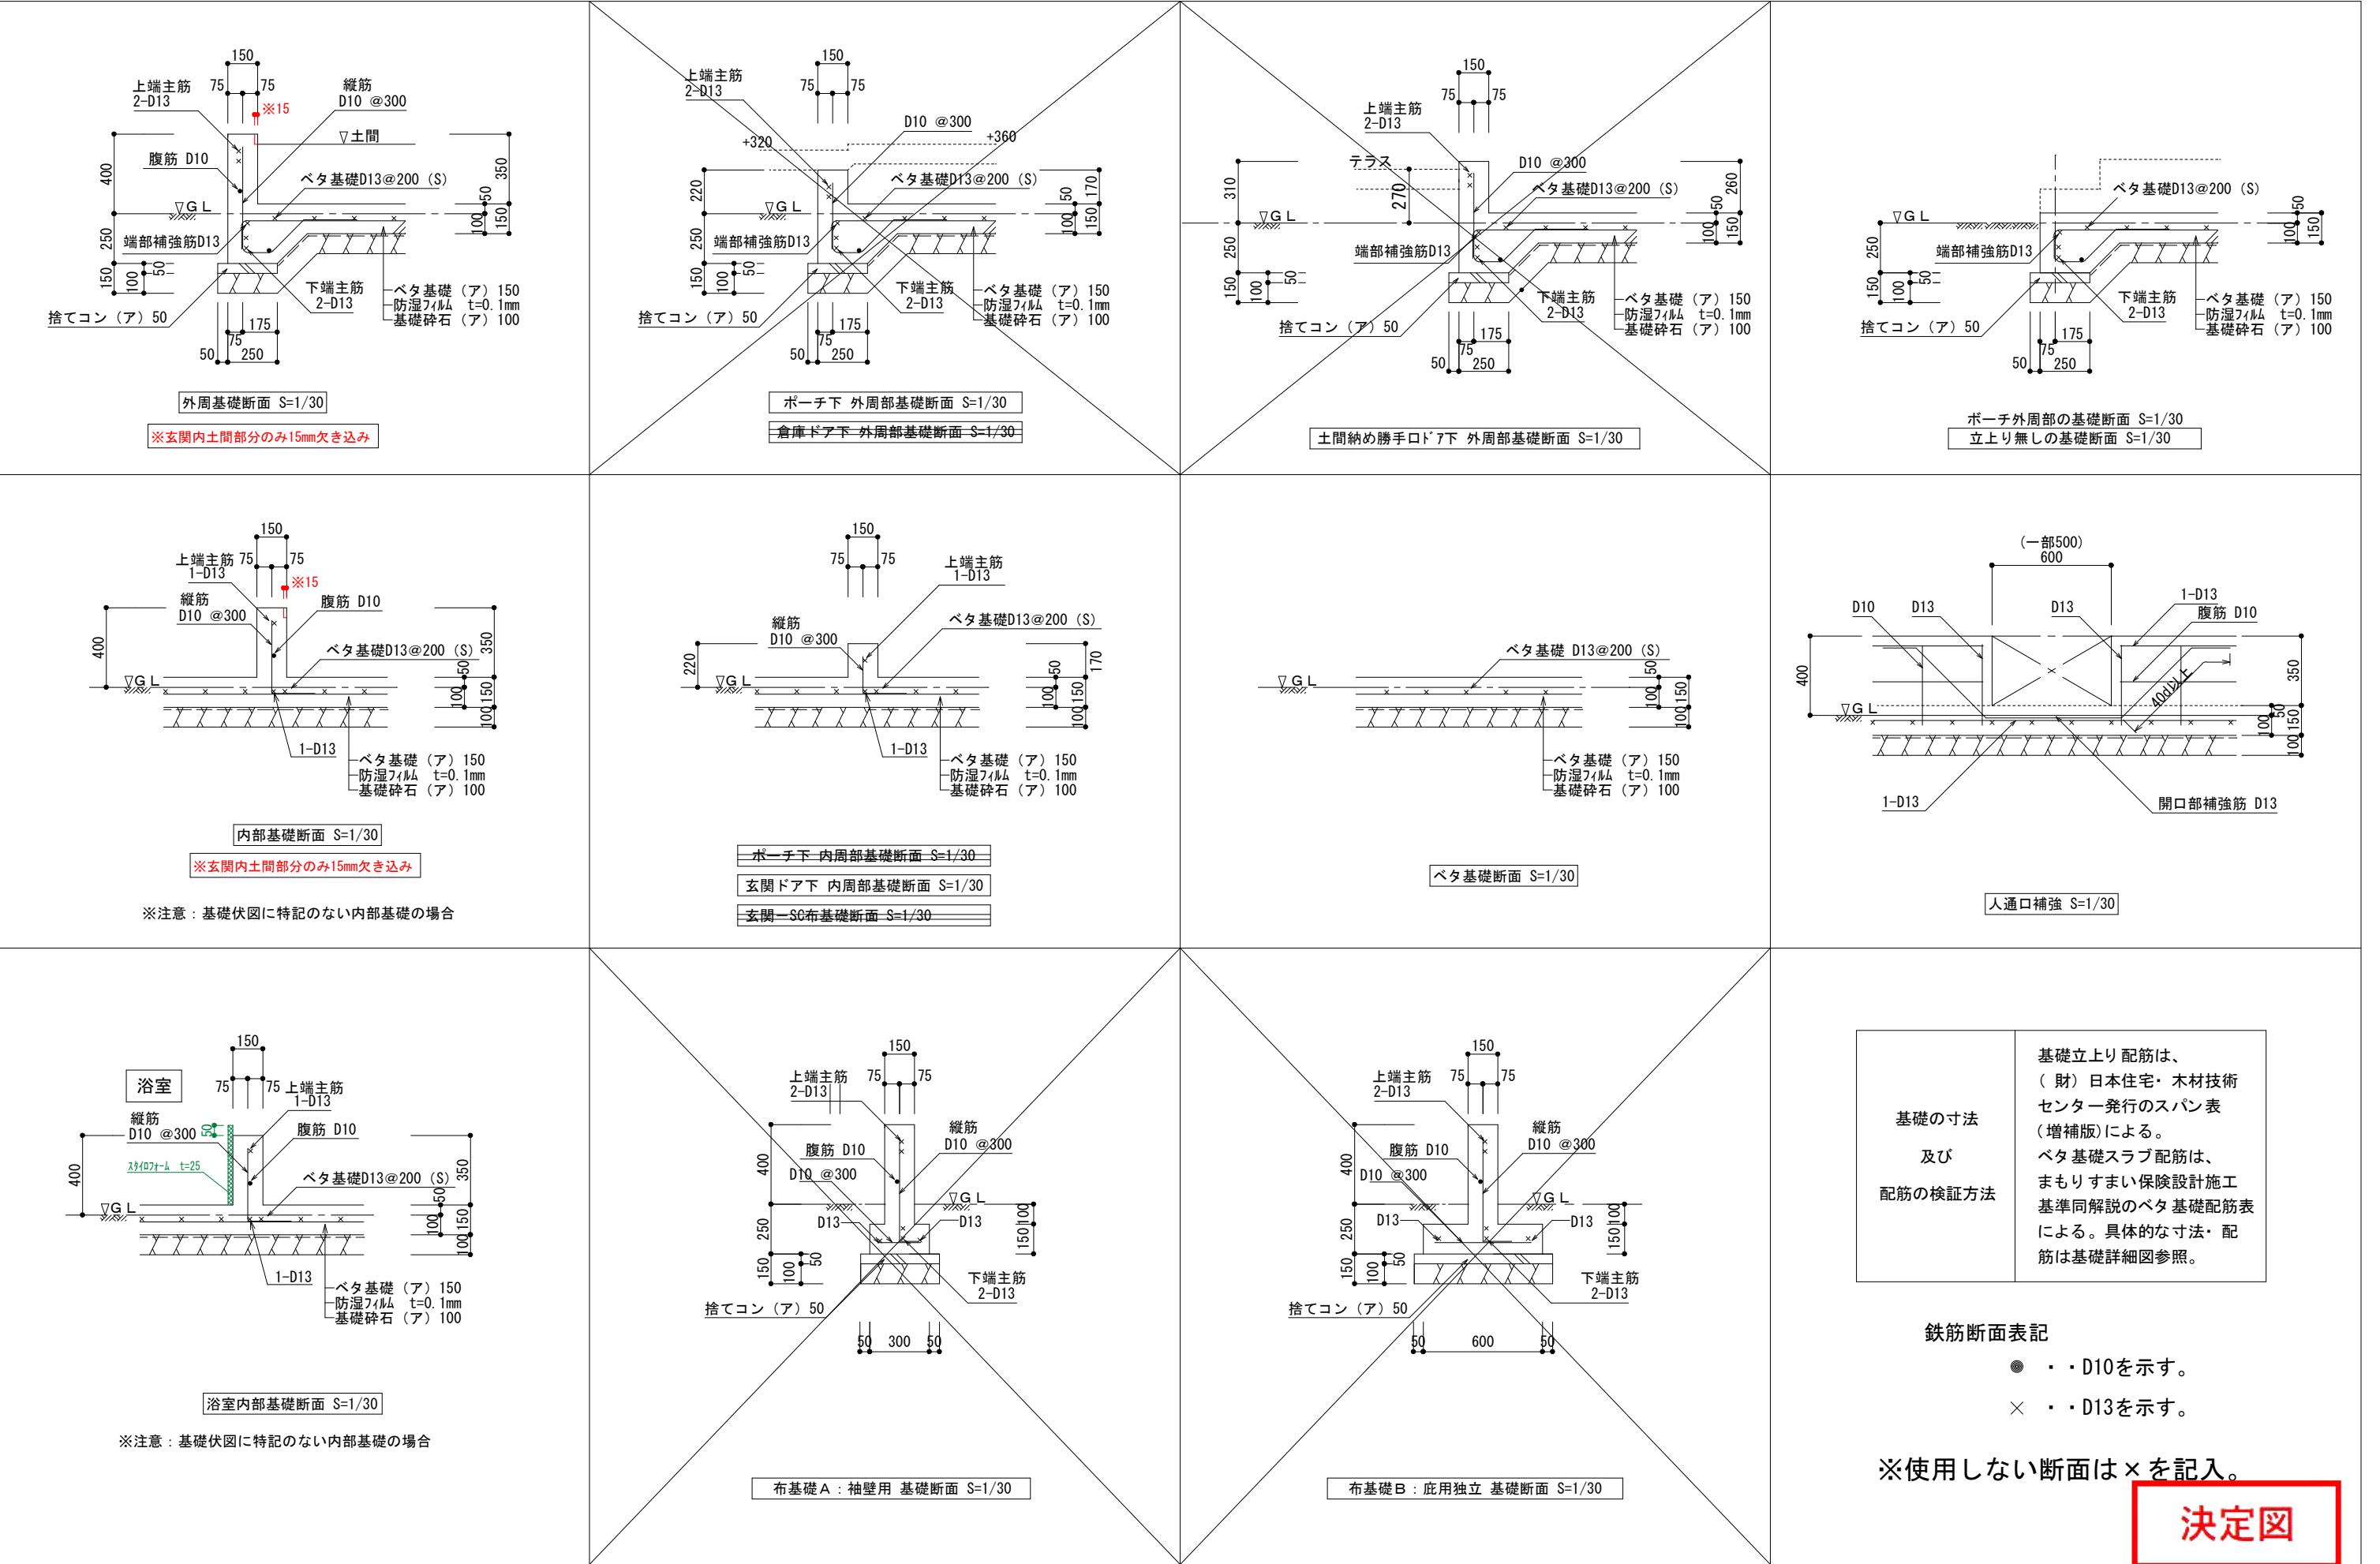


訂 正	浜 岡 一 級 総 合 設 計 事 務 所			株式会社 LIFEFUND InDesign office		一級建築士事務所		年 月 日	件 名		設計	I C	工務	図 番
	一級建築士事務所 静岡県知事登録第 (10)2441 号			事務所登録 (2)第7595号		一級建築士登録 第179770号		2024. 12. 10	竹内優太郎様邸 新築工事					
	一級建築士 大臣登録第 365879 号 西原利昌			〒432-8023 静岡県浜松市中央区鴨江3丁目7番23号		鈴木 達男		縮 尺	図 名					
								1/30	基礎断面リスト		倉田		青島	B-2

決定図

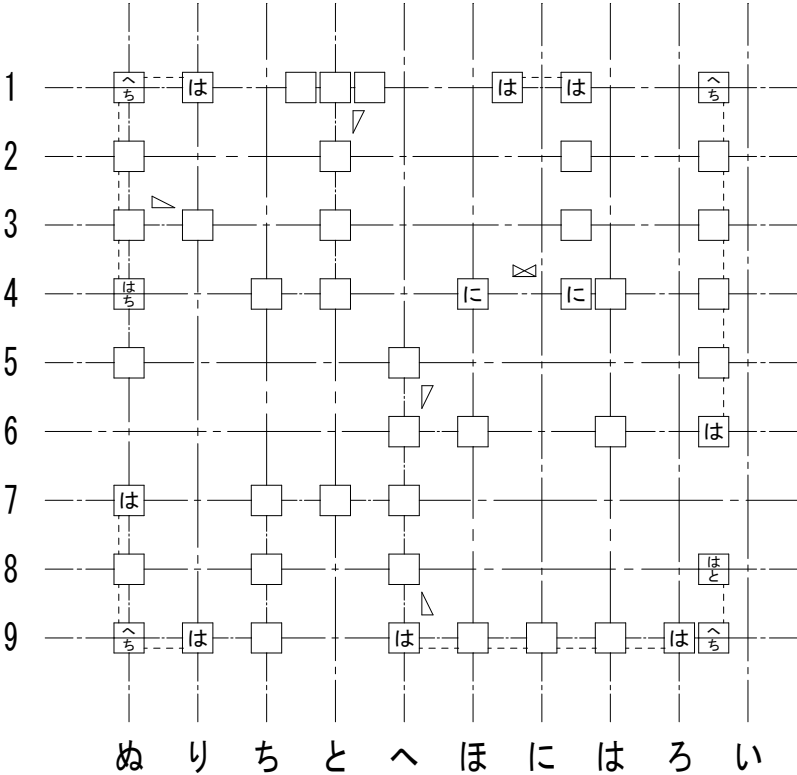

2階柱壁伏図

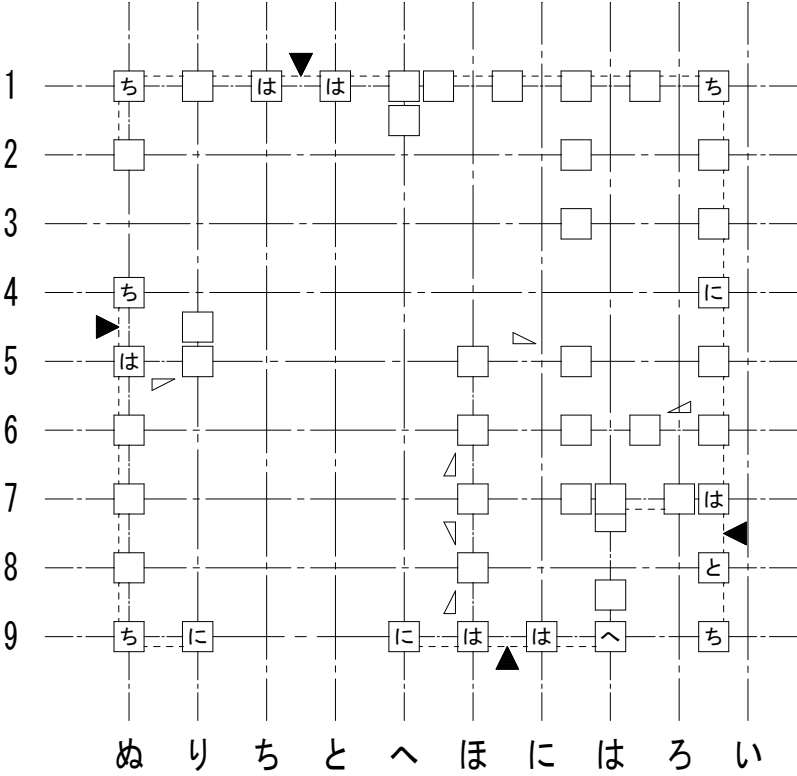

1階柱壁伏図

接合部凡例				*接合部凡例はユーザ設定されたものです。	
記号	仕様（カナイ金物）		N	倍率	
SBCP	スリムビルドコーナー75		0.00	1.00	
SBCP	スリムビルドコーナー75		0.65	1.00	
SBCP	は	スリムビルドコーナー75	1.00	1.00	
ARCG	に	アレントコーナー合板用	1.40	2.20	
ARCG	ほ	アレントコーナー合板用	1.60	2.20	
ARCG	へ	アレントコーナー合板用	1.80	2.20	
HD15	と	ブレイブホールダウン B-HD15	2.80	3.60	
HD20	ち	ブレイブホールダウン B-HD20	3.70	4.70	
HD25	り	ブレイブホールダウン B-HD25	4.70	4.80	
HD30	ぬ	ブレイブホールダウン B-HD30	5.60	7.20	
J1	る	腰掛け蟻若しくは大入れ蟻掛け+羽子板ボルト、短冊金物		1.90	梁継手・仕口用
J2	を	腰掛け蟻若しくは大入れ蟻掛け+羽子板ボルト、短冊金物×2		3.00	梁継手・仕口用

※表示なき金物は「は」とする。

接合部凡例				*接合部凡例はユーザ設定されたものです。	
記号	仕様（タナカ金物）		N	倍率	
FCP	フックコーナー		0.00	1.00	
FCP	フックコーナー		0.65	1.00	
FCP	は	フックコーナー	1.00	1.00	
GCP	に	シナコーナー	1.40	2.20	
GCP	ほ	シナコーナー	1.60	2.20	
GCP	へ	シナコーナー	1.80	2.20	
HD15	と	ビス止めホールダウンU HD15	2.80	3.60	
HD20	ち	ビス止めホールダウンU HD20	3.70	4.70	
HD25	り	ビス止めホールダウンU HD25	4.70	4.80	
HD30	ぬ	ビス止めホールダウンU HD15×2 (HD35)	5.60	7.20	
J1	る	腰掛け蟻若しくは大入れ蟻掛け+羽子板ボルト、短冊金物		1.90	梁継手・仕口用
J2	を	腰掛け蟻若しくは大入れ蟻掛け+羽子板ボルト、短冊金物×2		3.00	梁継手・仕口用

※表示なき金物は「は」とする。

筋かいの種類に応じた筋かいの端部の接合部の仕様		
	筋かいの種類	接合部の仕様（構造方法）
イ	鉄筋φ9	柱又は横架材を貫通し、三角座金を介してナット締め、又は鋼板添え板を用い鋼板を柱及び横架材にCN90, 8本平打ち
ロ	筋かい:15×90	柱・横架材を欠き込み、柱・横架材双方に対してN65, 5本平打ち
ハ	筋かい:30×90	鋼板添え板t=1.6mmを筋かいに対してボルトφ12及びCN65, 3本平打ち、柱に対してCN65, 3本平打ち、横架材に対してCN65, 4本平打ち。筋かいプレートBP同等品
ニ	筋かい:45×90	鋼板添え板t=2.3mmを筋かいに対してボルトφ12及びスクリュー釘φ4.5L50, 7本平打ち、柱及び横架材に対してスクリュー釘φ4.5L50, 5本平打ち。筋かいプレートBP-2同等品
ホ	筋かい:90×90	柱又は横架材にボルトφ12mmを用いて一面剪断接合


胴差と通し柱の接合部の仕様		
	胴差と通し柱の条件	仕口
T1	通し柱の片側に胴差が来る場合	胴差を柱にかたぎ大入れ短ほぞ差しの上、羽子板ボルト、かね折り金物又は同等以上の仕口
T2	通し柱の両側に胴差が来る場合	胴差を柱にかたぎ大入れ短ほぞ差しの上、短冊金物又は、同等以上の仕口で胴差相互を緊結
T3	通し柱と胴差の接合部の近くに90×90以上の筋かいが来る場合(通し柱が建物の出隅にあるか、筋かい壁が外壁と直交して接する場合)	胴差を通し柱に、15KN用引き寄せ金物を水平に用いて緊結

決定図

磁北 真北

1F床

フロアタイル全て目地棒有り 目地棒品番 MB-56-S
IS-2071-C

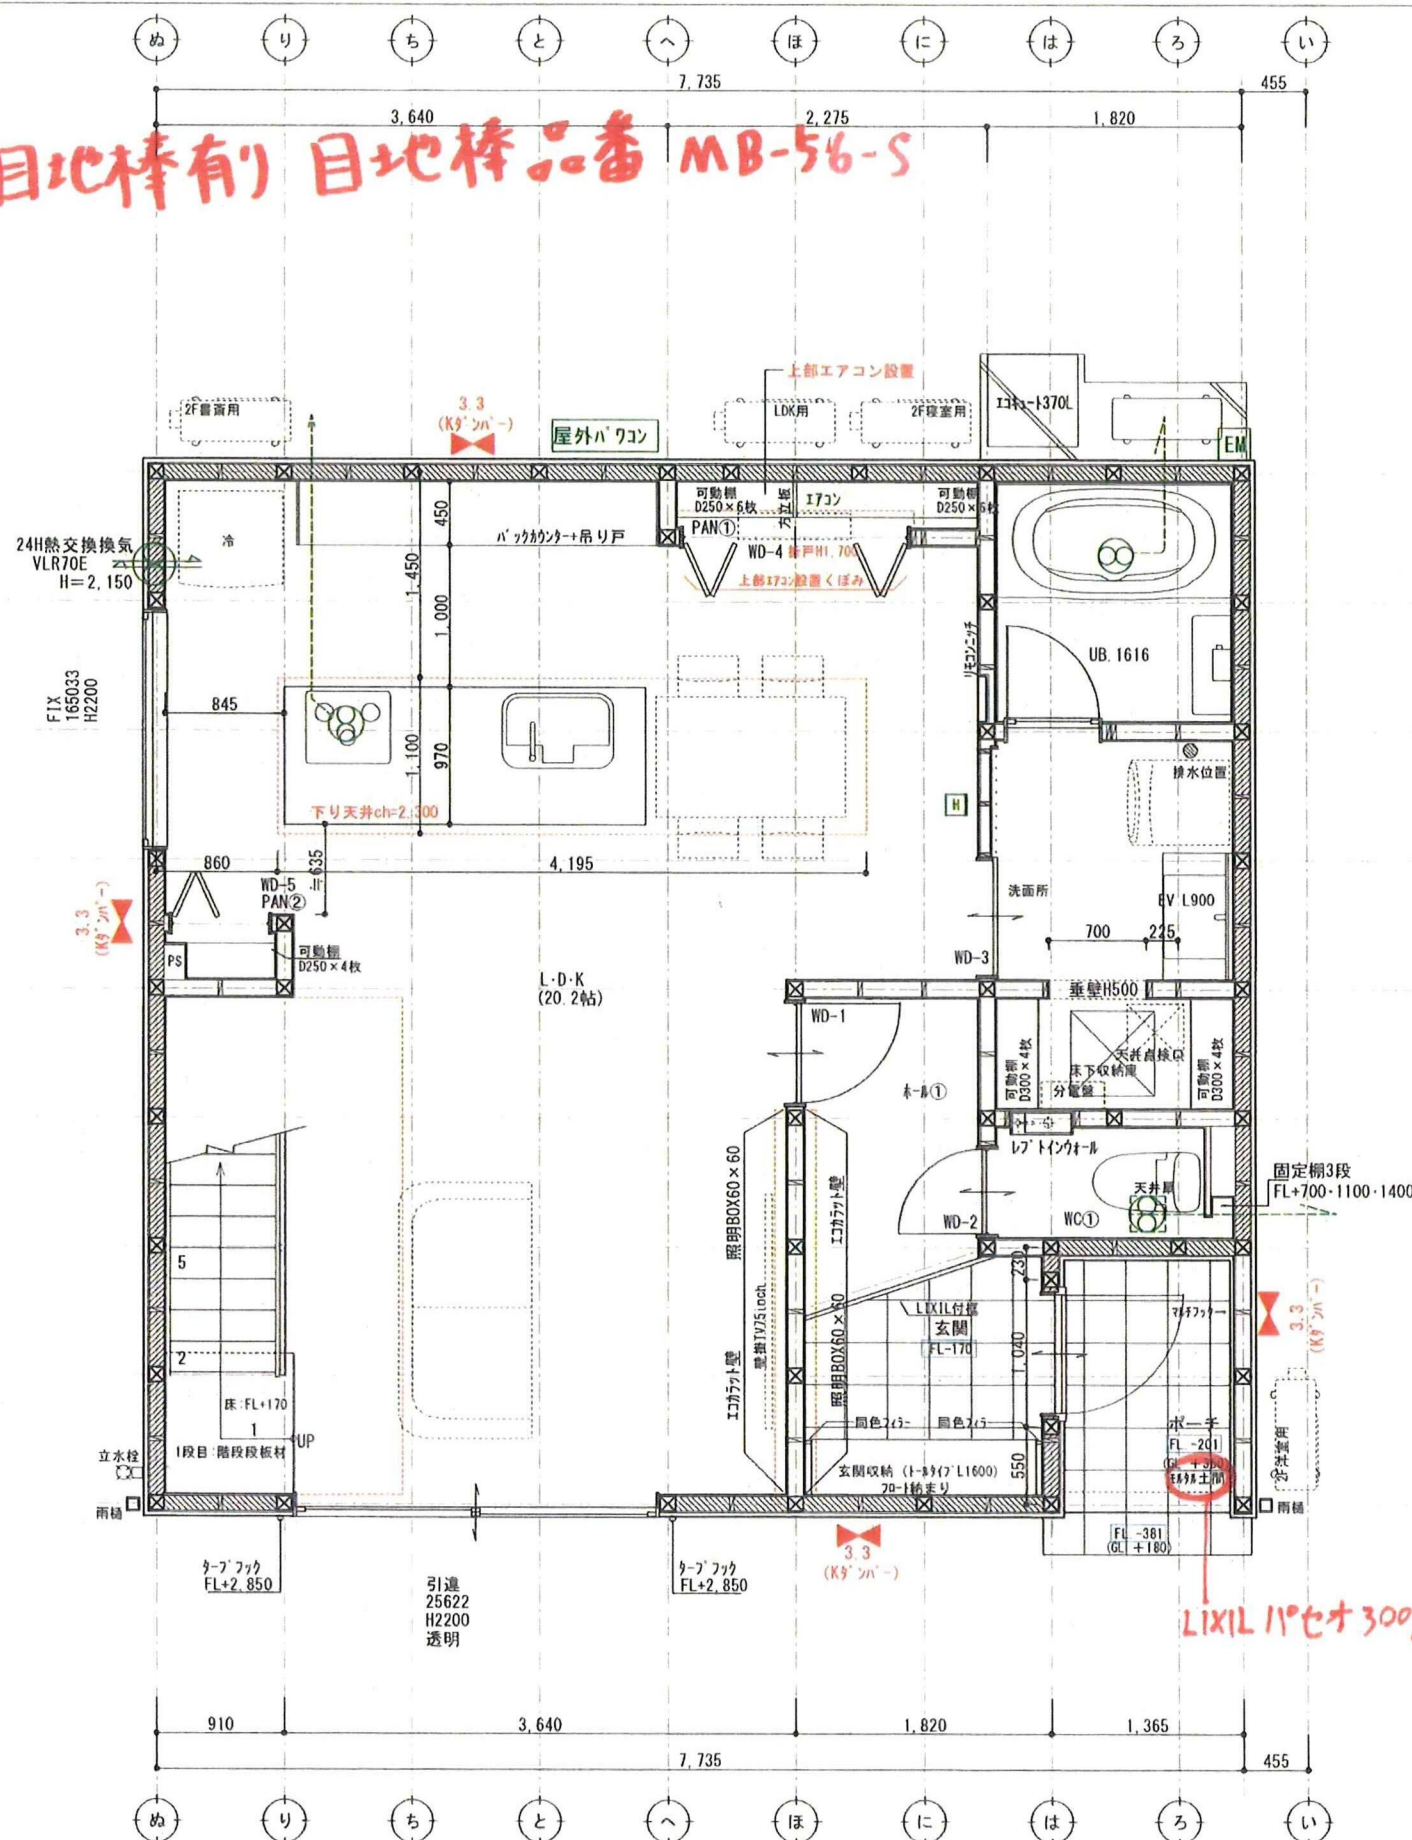

壁付け 住宅用火災報知器	数量
[H] 熱感知器 電池式(単独型) 露出型	
壁付け 住宅用火災報知器	数量
[S] 煙感知器 電池式(単独型) 露出型	

※ 煙感知器は壁・梁より600mm以上離す
壁に取付ける場合、
天井から150mm以上500mm以内離す
換気扇・170吹出口から1500mm以上離す
※ 全室LED照明とする。
※ 標準天井高さ2,400

* 凡例

☒ 管柱 (105×105)

◀▶ K9'ンバー (3.30倍 FRM-0641)

△ 片筋違い (2.00倍 45×90)
(例 左:柱脚 右:柱頭)

⊠ たすき掛筋違い (4.00倍 45×90)

構造用合板 (2.50倍)
(t=9 タ行付)

△ 床点検口

⊠ 天井点検口

⊕ 換気扇

⊕ 熱交換換気扇VLR-70

※表記なきガラスは型ガラス

アドバンスシリーズ

スマートデザイン (外部)

- ① コンセント 1ヶ所
- ② コンセント 2ヶ所
- ③ コンセント 3ヶ所
- ④ 1ET コンセント1ヶ所接地ターミナル付
- ⑤ 2ET コンセント2ヶ所接地ターミナル付
- ⑥ WP コンセント 防水型
- ⑦ エアコン用コンセント
- ⑧ 200V用コンセント
- ⑨ WP 防雨入替プレート
- ⑩ スイッチ
- ⑪ 3路スイッチ
- ⑫ 4路スイッチ
- ⑬ 直結電源
- ⑭ TV テレビ取出口
- ⑮ TEL 電話取出口 (テレホンガイド)
- ⑯ LAN LAN取出口 (テレホンガイド)
- ⑰ 照明
- ⑱ リモコン (給湯関係・ルフロ)
- ⑲ マーダー
- ⑳ 分電盤
- ㉑ チャイム

※ACコンセント天井付け

※TVアンテナ工事

※スイッチはFL+1100、コンセントはFL+200

訂正

浜岡一級総合設計事務所
一級建築士事務所 静岡県知事登録第 (10)2441 号
一級建築士 大庭登輝 365879 号 西原利品

PG HOUSE
ピージーハウス

株式会社 LIFEFUND InDesign office 一級建築士事務所
事務所登録 (2)第7595号 一級建築士登録 第179770号 鈴木 達男
〒432-8023 静岡県浜松市中央区鴨江3丁目70番23号


年月日
2024.11.20
縮尺
1/50

姓名
竹内優太郎様邸 新築工事
図名
1階平面図

設計	IC	工事	図番
倉田		青島	3-1

樹北真北

1F 天井

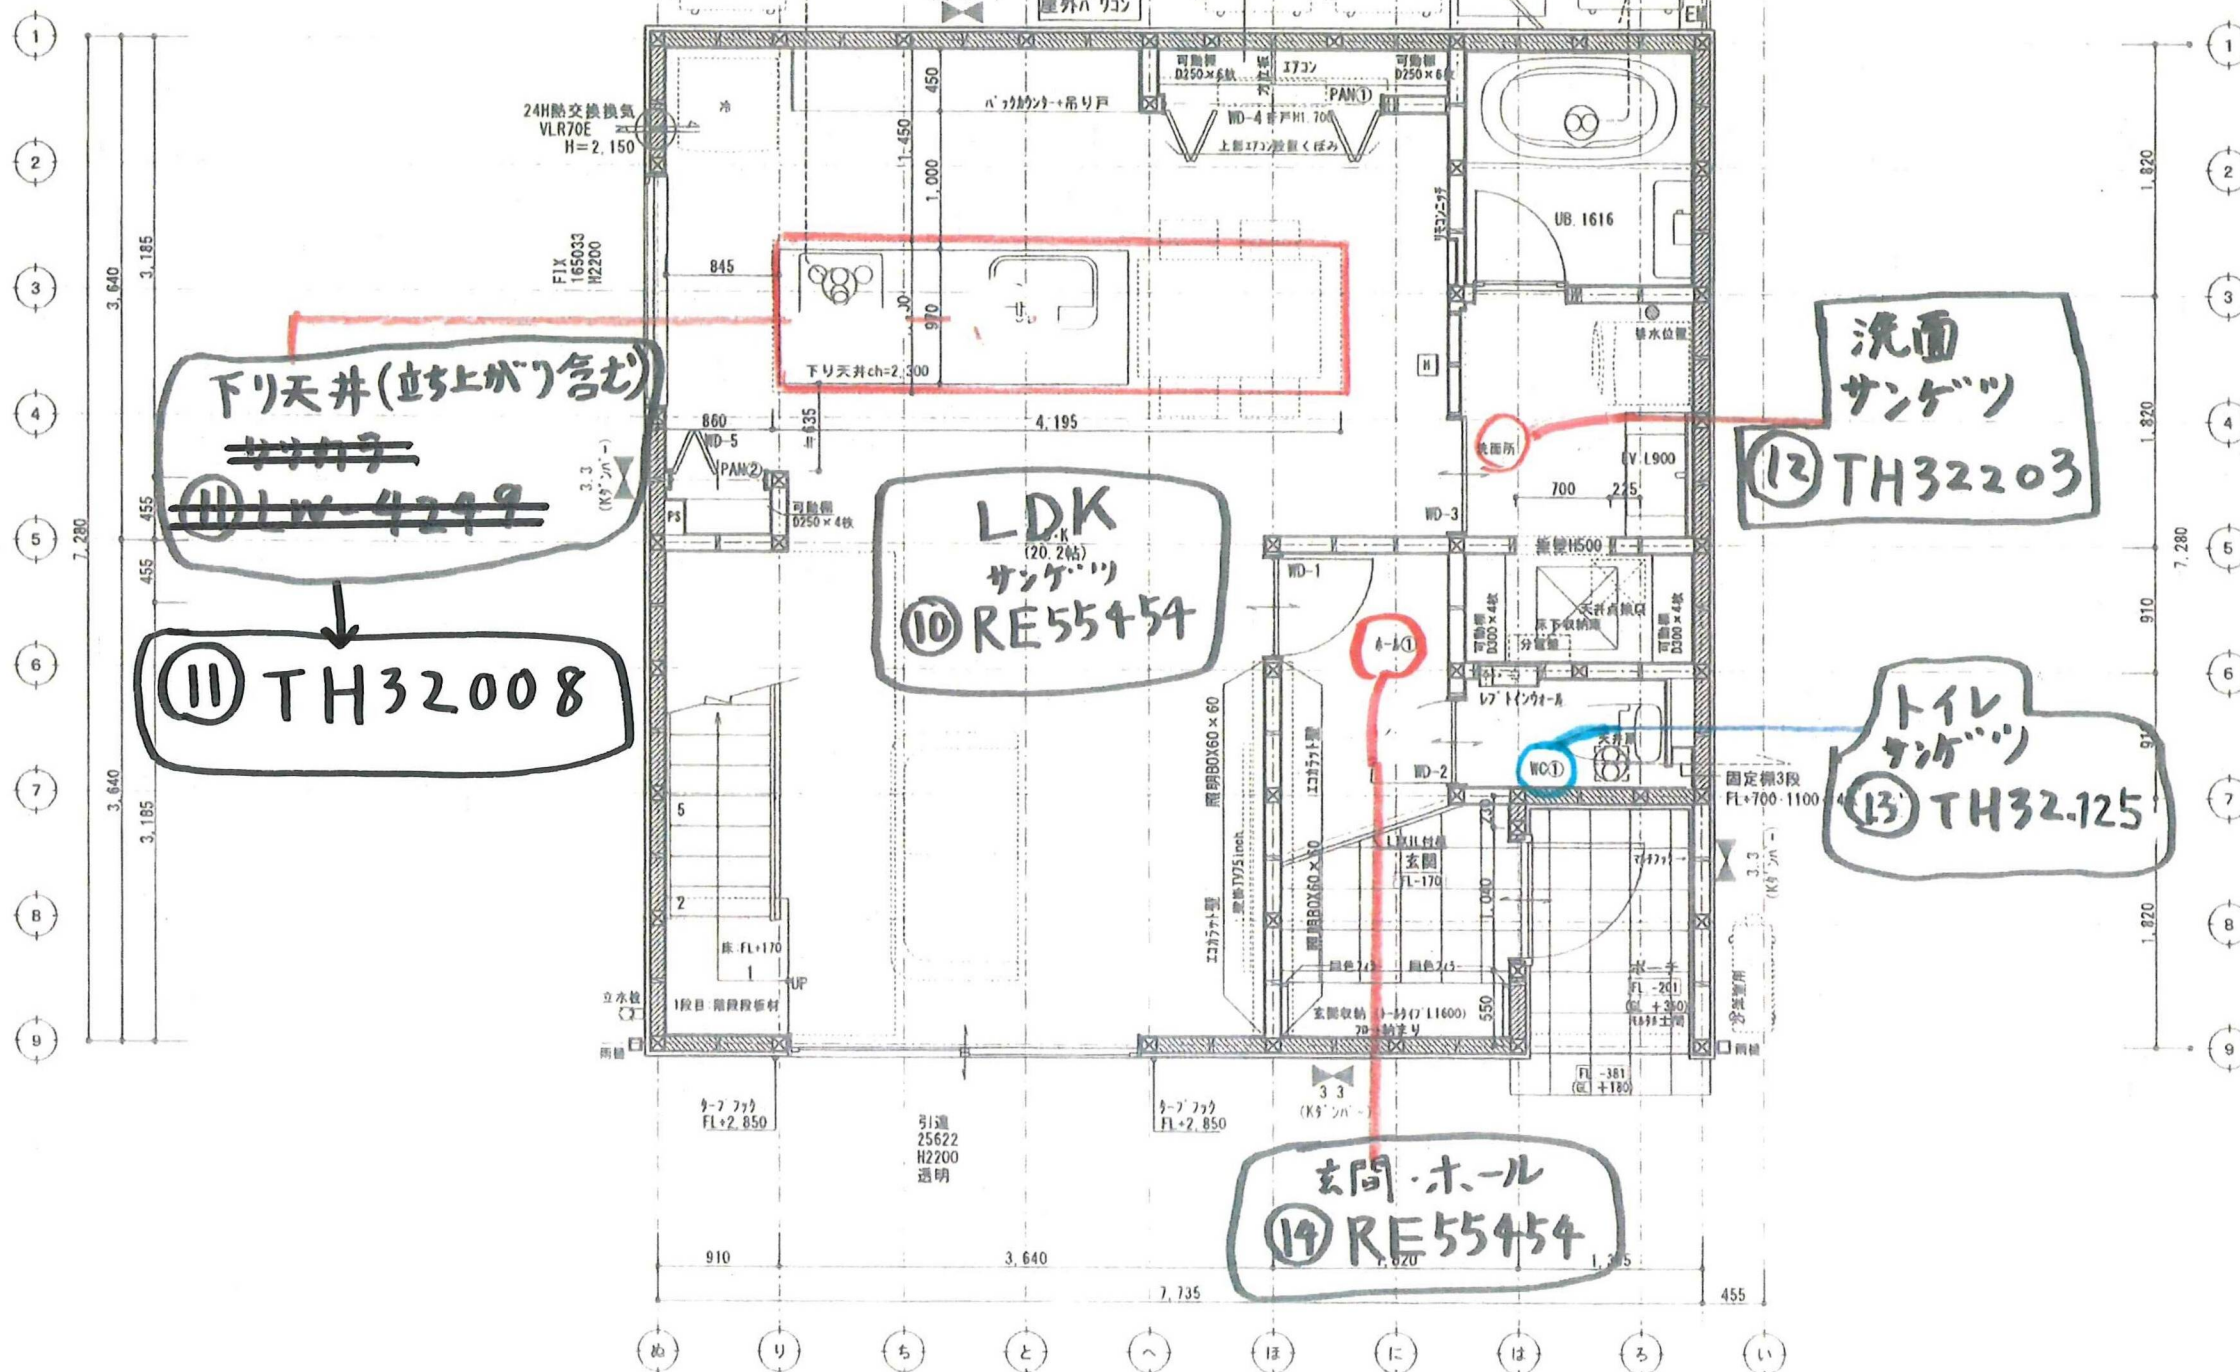

壁付け	住宅用火災警報器	数量
[H]	熱感知器	電池式(単独型)
[S]	煙感知器	電池式(単独型)
		高出型

※ 煙感知器は壁・床より600mm以上離す
壁に取付ける場合、
天井から150mm以上500mm以内離す
換気扇・170吹出口から1500mm以上離す
※ 全室LED照明とする。
※ 標準天井高さ2.400

* 凡例

- ☒ 管柱 (105 × 105)
- ≡ 片筋通い (3.30倍 FRM-0641)
- △ 片筋通い (2.00倍 45 × 90) (例 左:柱脚 右:柱頭)
- ⊗ たすき筋通い (4.00倍 45 × 90)
- 構造用合板 (2.50倍) (t=9 9'行付)
- △ 床点検口
- ☒ 天井点検口
- ⊕ 換気扇
- ⊕ 熱交換換気扇VLR-70

※表記なきガラスは型ガラス

アドバンスシリーズ

スマートデザイン (内装)

- ① コンセント 1ヶ所
- ② コンセント 2ヶ所
- ③ コンセント 3ヶ所
- ④E1 コンセント1ヶ所口埋めタミナル付
- ⑤E1 コンセント2ヶ所口埋めタミナル付
- ⑥E1 コンセント 新着型
- ⑦E1 コンセントコンセント
- ⑧E1 200Wコンセント
- ⑨E1 防雨入替プレート
- ⑩E1 スイッチ
- ⑪E1 3路スイッチ
- ⑫E1 4路スイッチ
- ⑬E1 音感電灯
- ⑭E1 テレビ取付口
- ⑮E1 電話取付口 (テレビホンガイド)
- ⑯E1 LAN取付口 (テレビホンガイド)
- ⑰E1 照明
- ⑱E1 リモコン(調光器・ムフロ)
- ⑲E1 マーダー
- ⑳E1 分電盤
- ㉑E1 チャイム

※ACコンセント天井付

※TVアンテナ

※スリッパはFL+1100、コンセントはFL+200

訂正

浜岡一総合設計事務所
一級建築士事務所 静岡県静岡市清水区 100-2441 号
一級建築士 大庭健太郎 305375 号 西原利典

PG HOUSE


株式会社 LIFEFUND InDesign office 一級建築士事務所
事務所静岡 (TEL 7595号) 一級建築士事務所 第179170号 鈴木 達男
〒432-8023 静岡県浜松市中央区鶴江3丁目70番23号

年月日
2024.11.20
縮尺
1/50

氏名 竹内優太郎様邸 新築工事
図名 1階平面図

設計	IC	工事	図集
倉田		野島	3-1

1Fクロス
(壁)

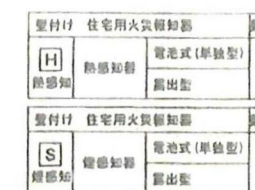

* 凡例

- ※表記なきガラスは型ガラス

※ACコンクリート天井付け
※TVアンテナ工事
※入り方はFL+1100。コンクリートはFL+200

2F床

フロアタイル

(24) IS-2072-C

フロアタイル

75 IS-2071-C


②未記入

ウオールナット

ウオールナット

設計	IC	工事	図 番
倉田		青島	3-2

2F天井

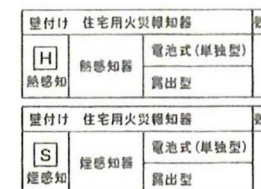

- ※ 煙感感知器は壁・梁より600mm以上離す
壁に取付ける場合、
天井から150mm以上500mm以内離す
換気扇・エアコン吹出口から1500mm以上離す
- ※ 全室LED照明とする。
- ※ 標準天井高さ2.400

* 凡例

☒ 管柱 (105×105)

 K9-Sha-
(3.30倍 FRM-0641)


 片筋違
 (2.00倍 45×90)
 (例 左:柱脚 右:柱頭)

 たすき掛筋違い
(4.00倍 45×90)

構造用合板 (2.50倍)
(t=9 5' 15' 11)

 床点検口

 天井点検口

 換氣扇 熱交換機氮素VLR-70

※表記なきガラスは型ガラス

アドバンスシリーズ

スマートデザイン（外部）

凡例	
①	コンセント 1φ口
②	コンセント 2φ口
③	コンセント 3φ口
①②	コンセント1φ口接地ターミナル付
②③	コンセント2φ口接地ターミナル付
WP	コンセント 防湿型
⑤	エアコン用コンセント
⑥	200V用コンセント
WP	防湿入扉プレート
□	スイッチ
●	3路スイッチ
●	4路スイッチ
⊗	直結盤蓋
TV	テレビ放送口
TEL	電話線取出口 (テレホンガイド)
LAN	LAN取出口 (テレホンガイド)
	照明用
	リモコン(感測関係・ルーフ)
	メーター
	分電盤
⑦	チャイム

※ACコンセント天井付け
※TVアンテナ工事
※スイッチはFL+1100、コンセントはFL+200

訂 正

浜岡一級総合設計事務所
一級建築士事務所 静岡県知事登録第 (10)2441 号
一級建築士 大臣登録第 365879 号 西原利昌



株式会社 LIFEFUND InDesign office 一級建築士事務所
事務所登録 (2) 第7595号 一級建築士登録 第179770号 鈴木 達男
〒432-8023 静岡県浜松市中央区鶴江3丁目70番23号

年月日	2024.11.20
幢尺	1/50

件名	竹内優太郎様邸 新築工事
図名	2階平面図

設計	IC	工事	國 番
倉田		青島	3-2

