



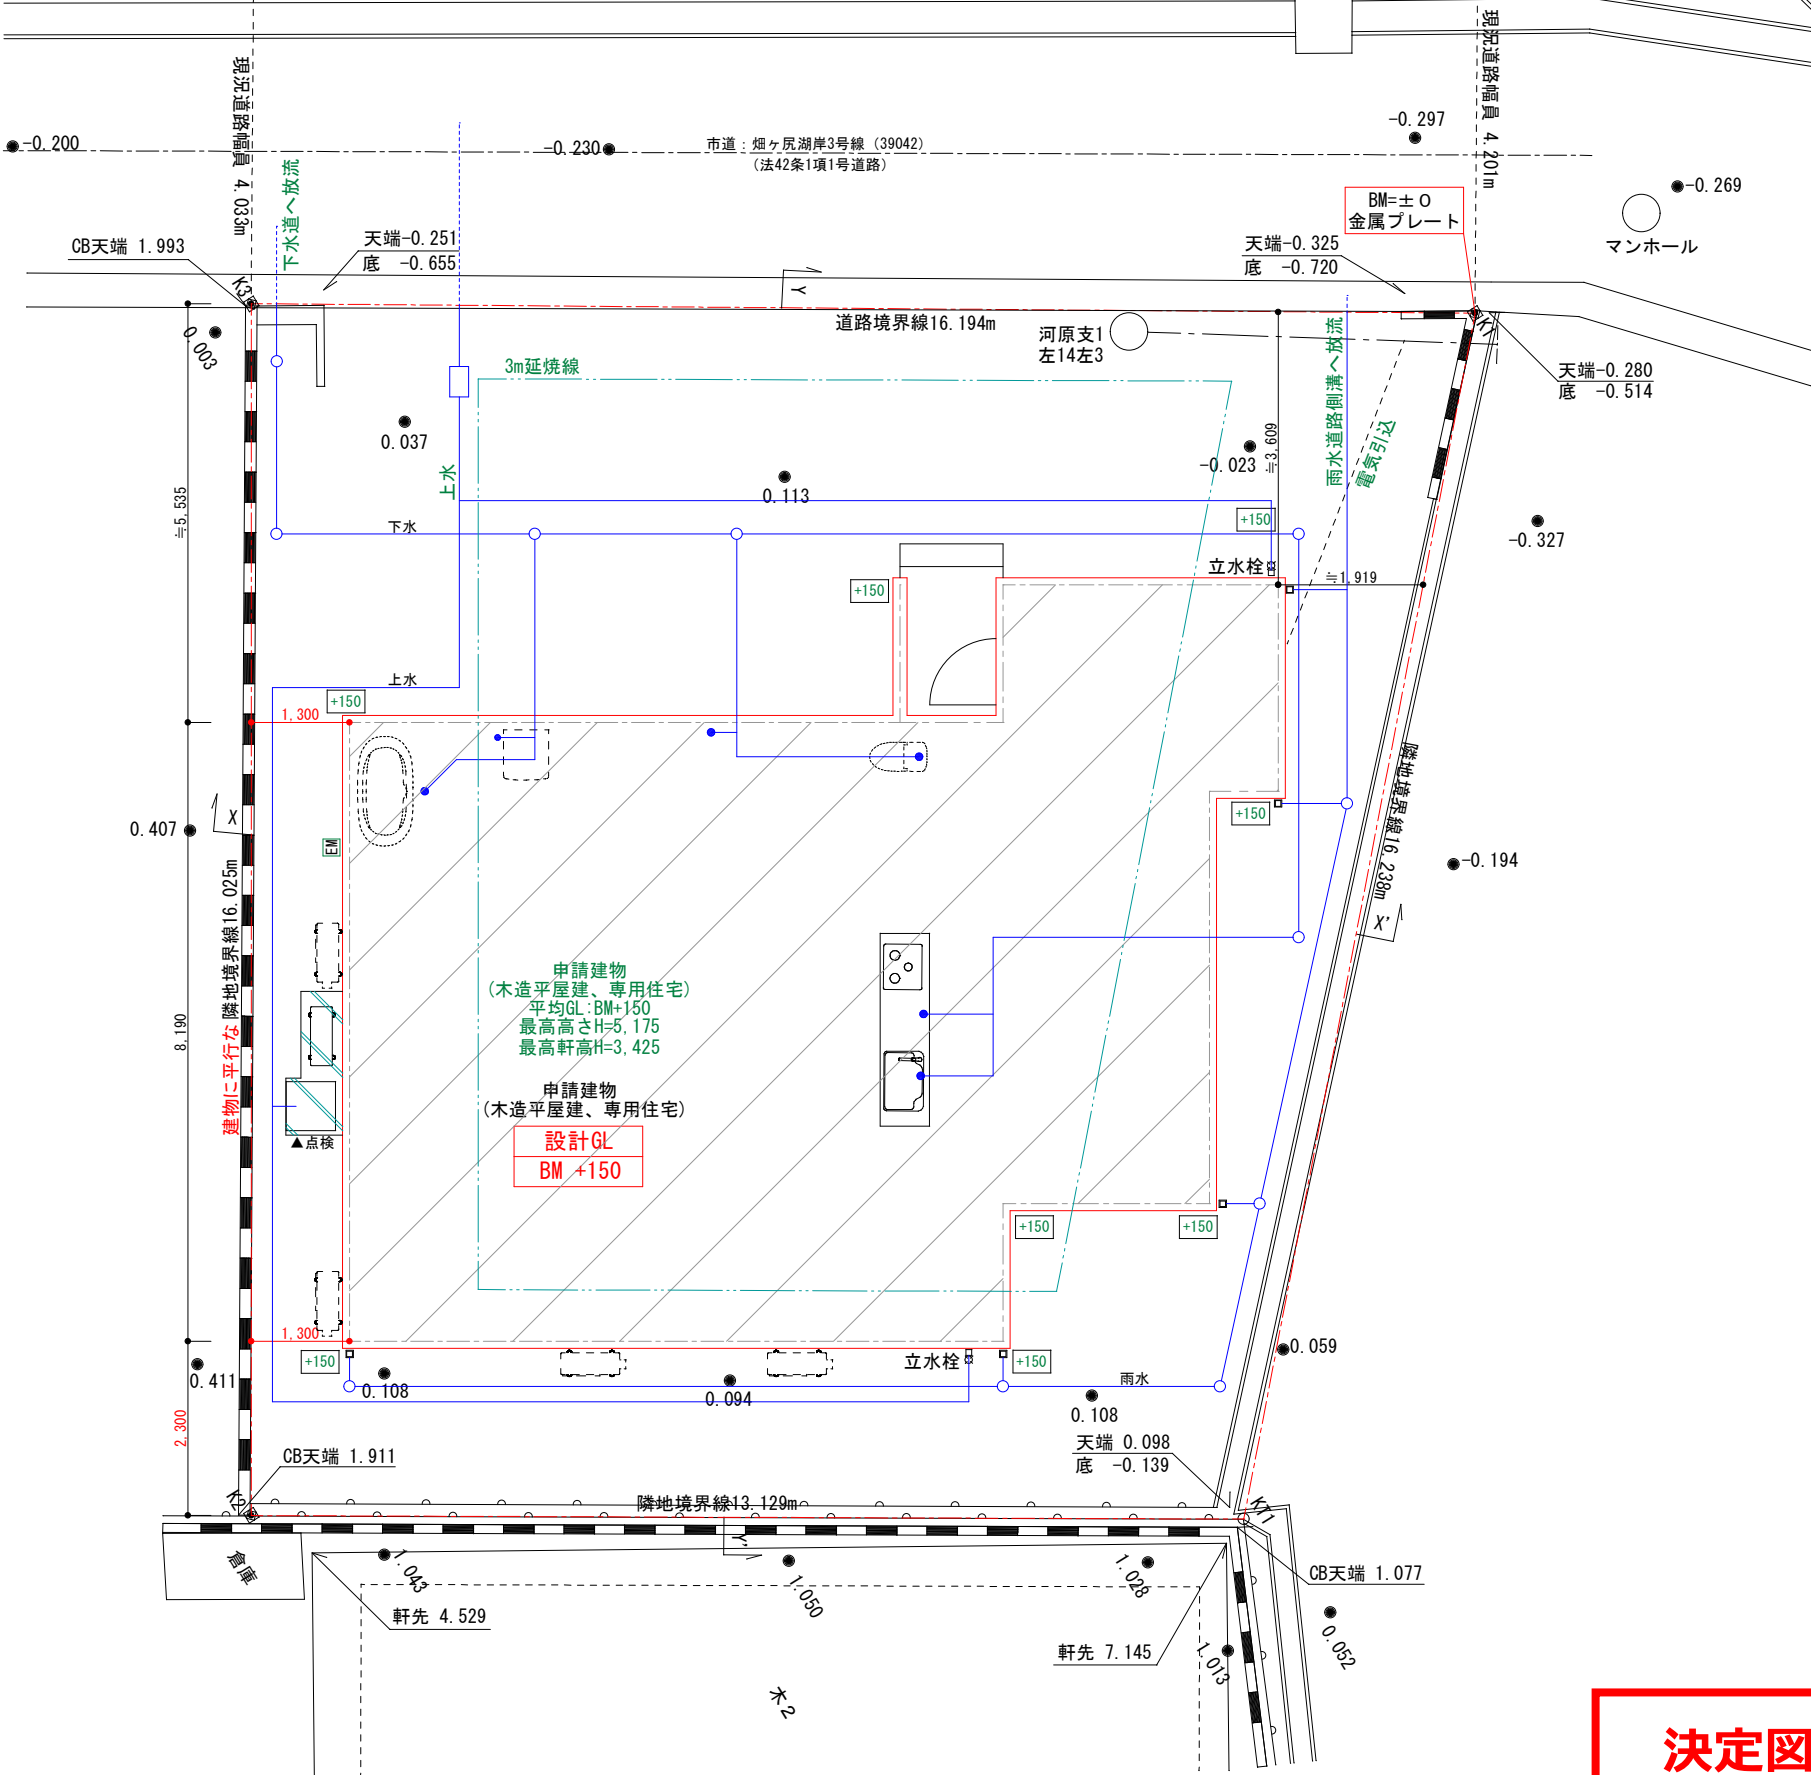

盛土規制法による切土盛土無し  
道路斜線制限については、明らかに適合する。  
北側斜線制限については、明らかに適合する。  
平均地盤面について  
申請建物の周囲の平均地盤面高さをBM+150とする。

| トータル面積表 (㎡) |                                    |
|-------------|------------------------------------|
| 敷地面積        | 234.51                             |
| 建築面積        | 98.12                              |
| 床面積 1階      | 95.64                              |
| 延床面積        | 95.64                              |
| 建蔽率         | $(98.12/234.51) \times 100$ 41.85% |
| 容積率         | $(95.64/234.51) \times 100$ 40.79% |

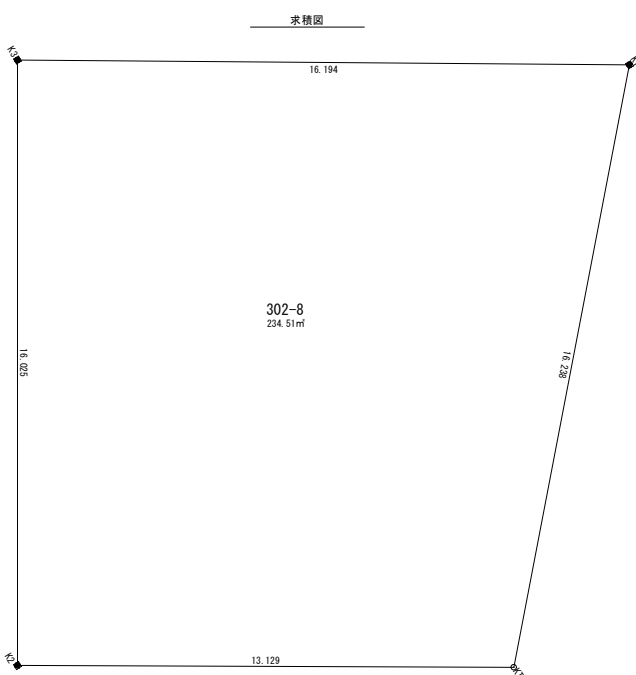

| 求積表  |                |                |                                     |                                                         |
|------|----------------|----------------|-------------------------------------|---------------------------------------------------------|
| 地番   | 302-8          |                |                                     |                                                         |
| N O  | X <sub>n</sub> | Y <sub>n</sub> | Y <sub>n+1</sub> - Y <sub>n-1</sub> | X <sub>n</sub> * (Y <sub>n+1</sub> - Y <sub>n-1</sub> ) |
| K1   | 5.958          | 4.298          | 20.572                              | 122.567976                                              |
| KT1  | -5.017         | 16.266         | 5.039                               | -25.280663                                              |
| K2   | -16.169        | 9.337          | -20.572                             | 332.628668                                              |
| K3   | -7.762         | -4.306         | -5.039                              | 39.112718                                               |
| 合計   |                |                |                                     | 469.028699                                              |
| 合計面積 |                |                |                                     | 234.5143495                                             |
| 地積   |                |                |                                     | 234.51 ㎡                                                |

決定図