
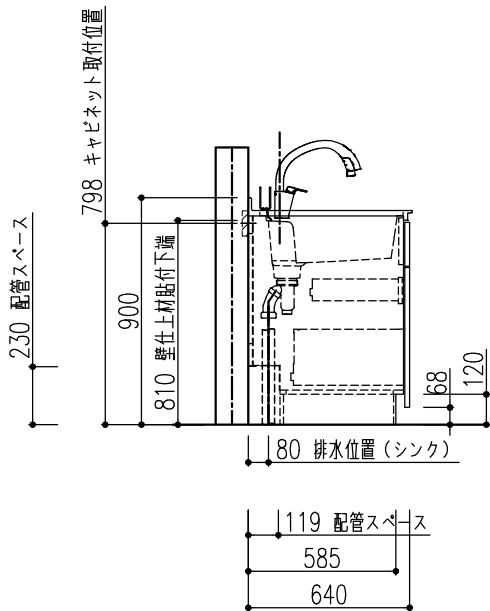


B面

C面

注6) 125V・15A 2極接地極付アースターミナル付コンセント 【専用】（フード用）

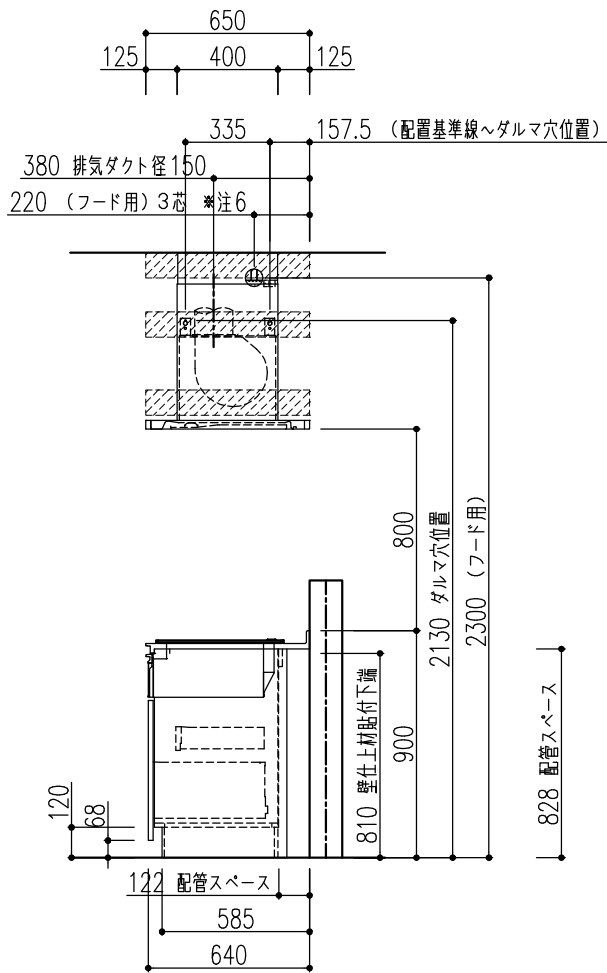


特記事項 扉色 VL2:グレージュスタッコ 取手 [S]ミドル取手S (ブラック) ワークトップカラー 【BN】 ブラウンストーン	物件名	小原徳晃 様邸	案件No.	図面名	担当	図面	図番 : 株式会社 LIXIL
			A2511DDD0EYYHZ	納まり図	栗野 友仁		
	仕様	ND23	見積No.	縮尺	日付		
			M25119443182-013-2	1/30	2026.02.03		

■壁面仕上材（キッチンパネル）取付注意事項〔貼付向き〕

●キッチンパネルの貼付向き

キッチンパネルの貼付向きにご注意ください。

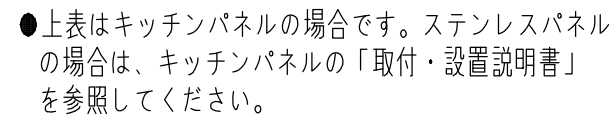


《バックガード：なし、ワークトップ高さ：850mm、ウォールキャビ高さ：700mmの場合》


	ウォールキャビ		
	開き扉		クイックポケット クイックパレット
	H700	H600 H500	H700 (620) H600 (520)
キッチンパネル 貼付方向	横	縦	

【ご注意】
リシエル以外のクイックパレットは、
キャビネットの背板高さがショート
（-80mm）してありませんので、
『開き扉』のキッチンパネル貼付方向
に合せてください。

【床立上げ】
・止水栓はアングル式が必要となります。

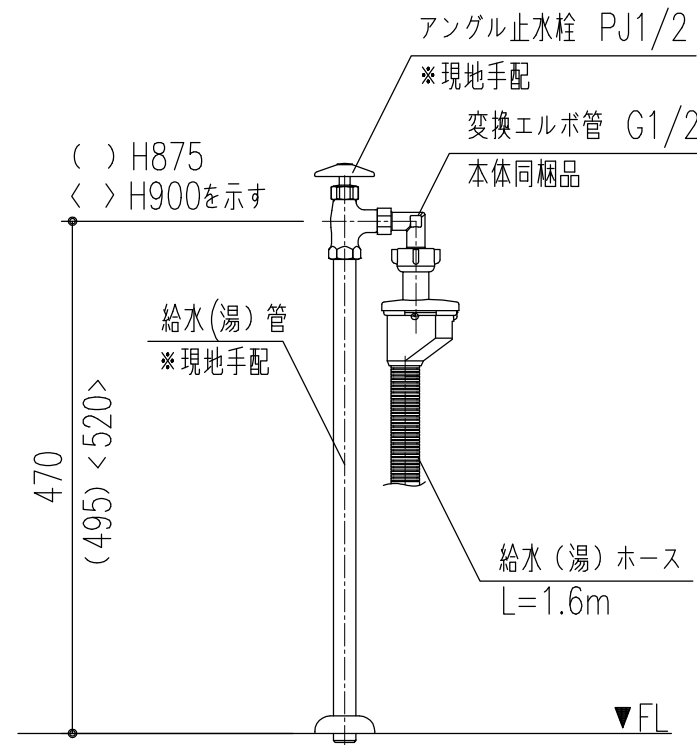


- ・必ずパナソニック製フロントオープン食洗機専用のコンセントにしてください。
- ・コンセントは水滴が飛ばないように必ず500mm以上の位置に取り付けてください。
- ・必ずシンクキャビネット内に設置してください。
- ・シンクキャビネットの側板を切り欠いてください。

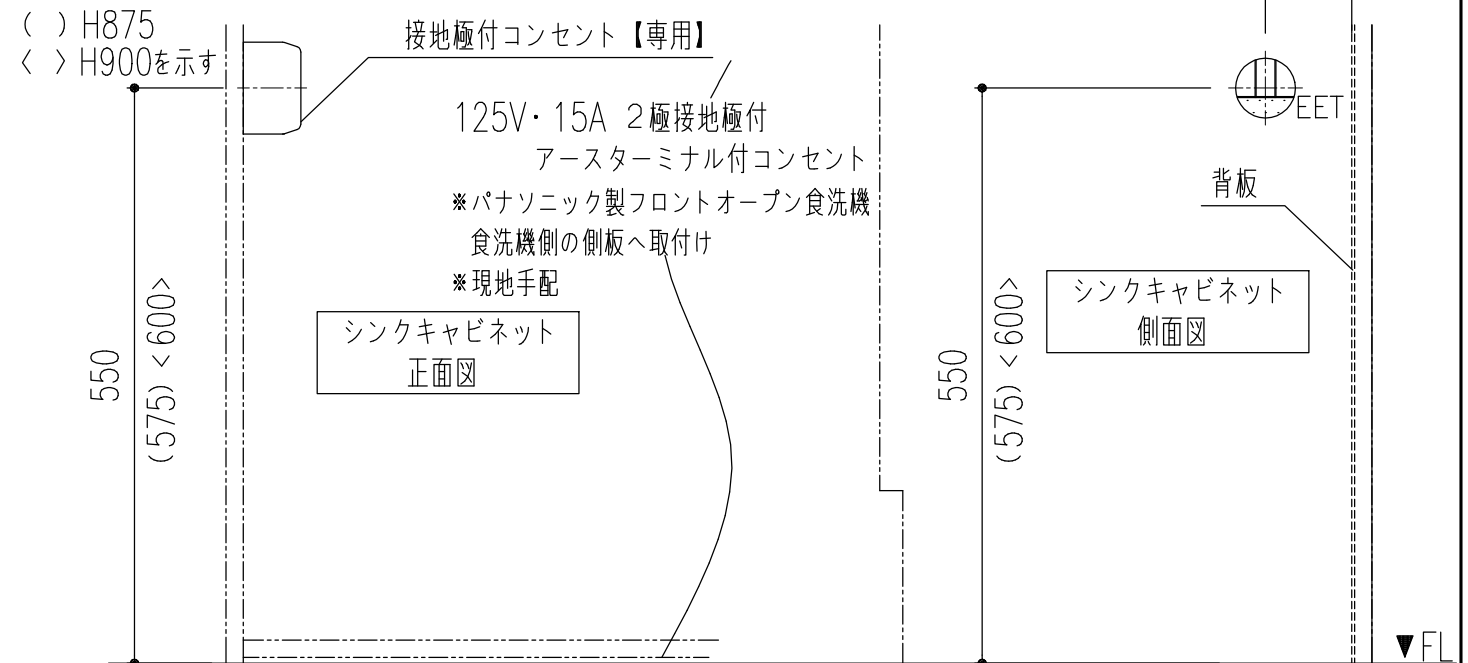

20260203M9HP-01

■ 床の不陸に関して

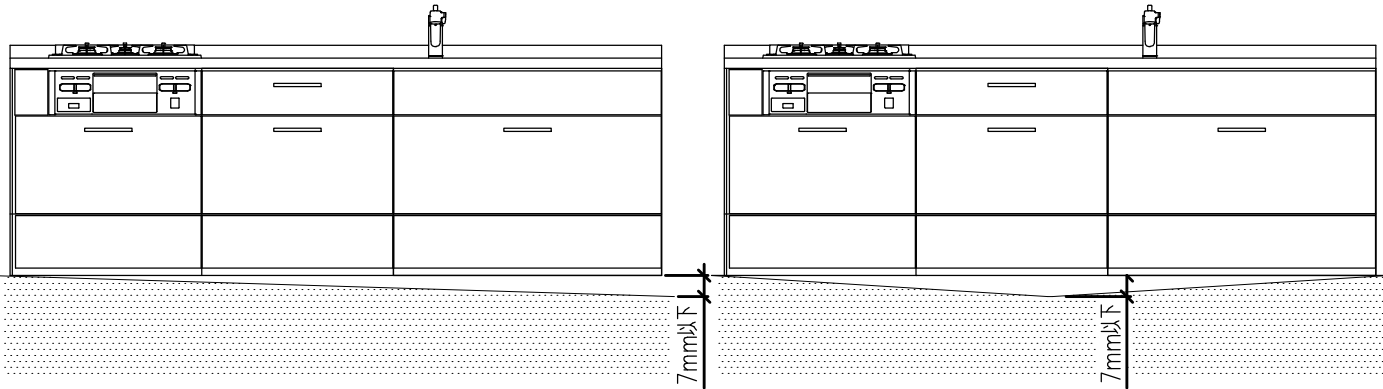


床の不陸は、7mm以下に抑えるようにしてください。不陸が大きい場合は、現場責任者に床の修正を依頼してください。
※キャビネット取付時には不陸調整スペーサー等で水平になるように設置してください。

■レンジフード取付注意事項（壁面取付時）


レンジフードを取付ける場合は下地の材が厚み30mm以上、幅100mm以上、ビス固定位置が材の端部から25mm以上であることを確認してください。
また、壁強度などの詳細は「レンジフード設置説明書」を必ず事前に確認してください。

取付位置については、取付設置図を確認してください。


参考図_FED、HVR、NSDシリーズ（サイドマントルタイプ）

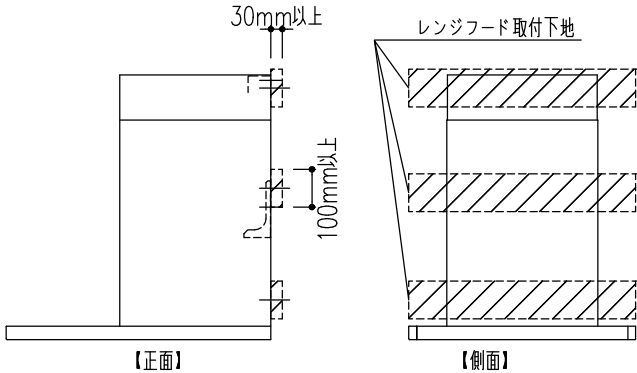


参考図_CLS、SER、NST、ASR、ADR、RVJ、GSR、BFRS、TARシリーズ
（※RVJ、GSRシリーズの場合はレンジフードパネルの取付下地は不要です。）

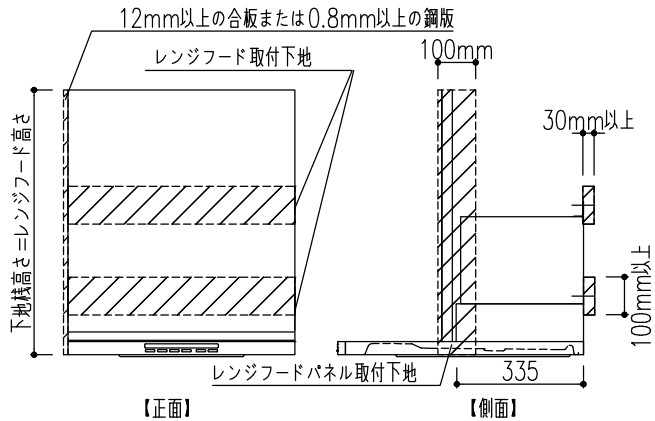


参考図_NBHシリーズ

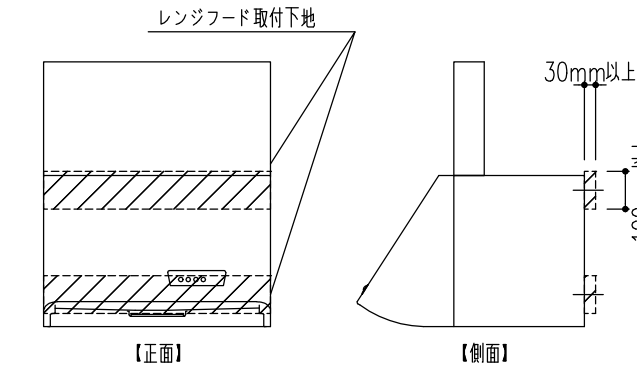

■SMHVRフード

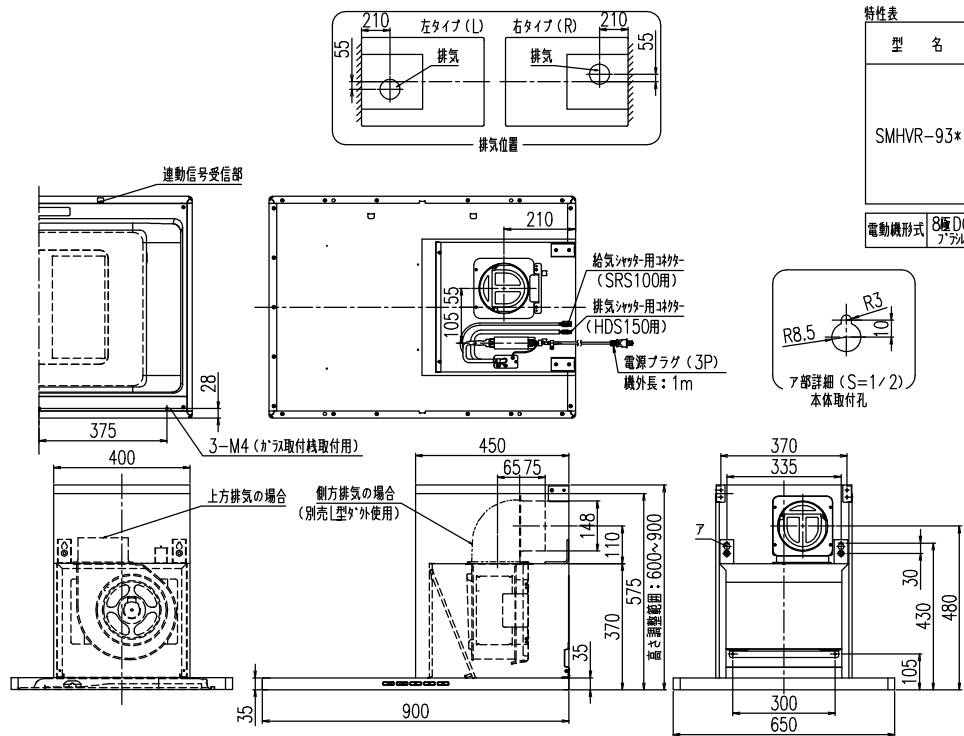


特性表									
型 名	定格電圧 (V)	/r/min	定格周波数 (Hz)	消費電力 (W)	風 量 0Pa100Pa	騒 音 (dB)	製品質量 (Kg)		
SMHVR-93*	100	強	50	70	530	435	48	26.5	
		中	30	28	370	—	39		
		弱	30	11	220	—	28		
		常時	30	7	155	—	22		
			60						
			60						
電動機形式	8極DC ブラシレスモーター	絶縁抵抗	10MΩ以上 (500V時)		耐電圧	AC1000V 1分間	絶縁区分	E種	
風量値はJIS C9603「ファン」法による									

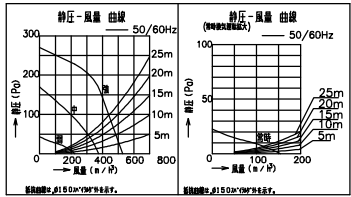

- 付 属 品
- 座付ねじ (φ5.1×45) 10本
 - 化粧ねじ (M4×8) 2本
 - トラスねじ (M4×10) 2本
 - ソフトテープ 1本


品 番	色 調
SMHVR-93*SL(R/L)	シルバー塗装
SMHVR-93*W(R/L)	ホワイト塗装

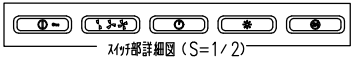

■IHヒーター用コンセント推奨位置図 / 壁付設置の場合

※コンセントや電源プラグが、引き出しおよびIHヒーター用仕切板（オプション）に接触しないように注意してください。
※木製キャビネットの配管スペース付キャビネットを使用する場合は点検口裏の配管スペース内にコンセントを設置してください。

キッチン高さ	電源線高さ
800	400
850	450
900	500

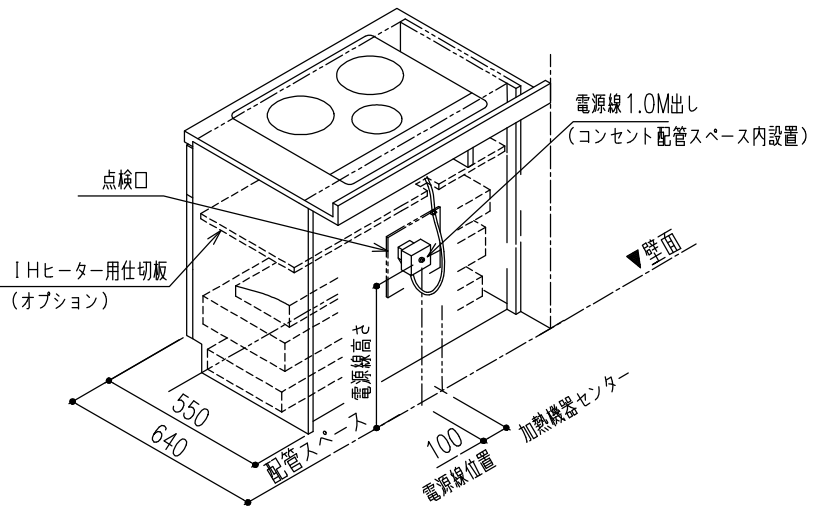

注意：引き出しおよびIHヒーター用仕切板（オプション）に接触しないように上記寸法を参照してください。

4. 製品名の末尾の（L）にはワザリス'によって記号が入る場合があります。
3. 電動シャッター（HDS150）（別売）を使用時は、中継ユニットを外して取り付けてください。
2. 赤外線連動型リモコンです。単独でも使用できます。
注）1. 排気方向は側方（L型が外使用：別売）と上方です。



特記事項
扉色 VL2:グレイジュスタック
取手 [S]ミドル取手S（ブラック）
ワークトップカラー 【BN】ブラウンストーン

物件名 小原徳晃 様邸
仕様 ND23


案件No.	図面名	担当	図面	図番
A2511DDD0EYYHZ	機能図	栗野 友仁		
見積No.	縮尺	日付		
M25119443182-013-2		2026.02.03		

株式会社 LIXIL

■止水栓図（床立上げ）

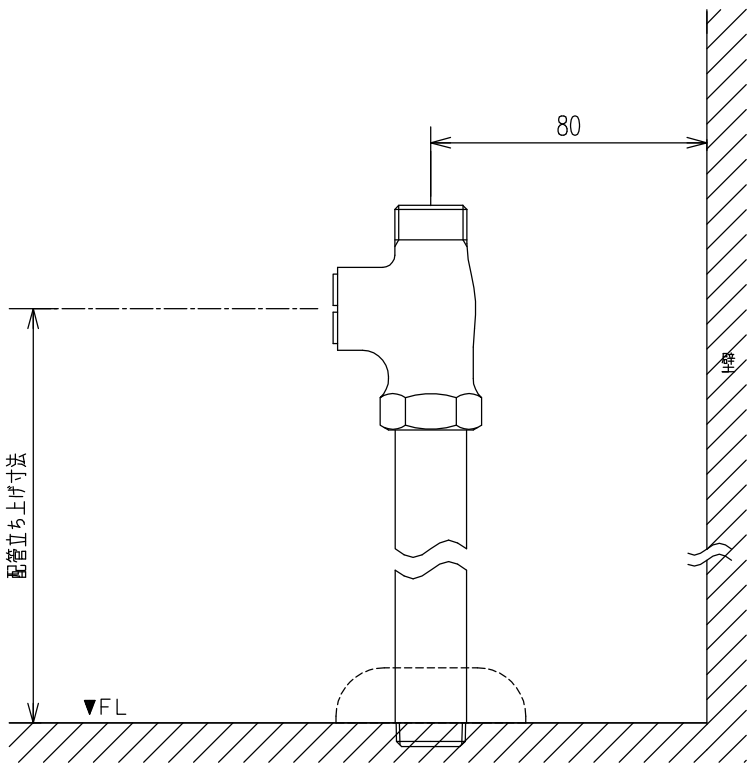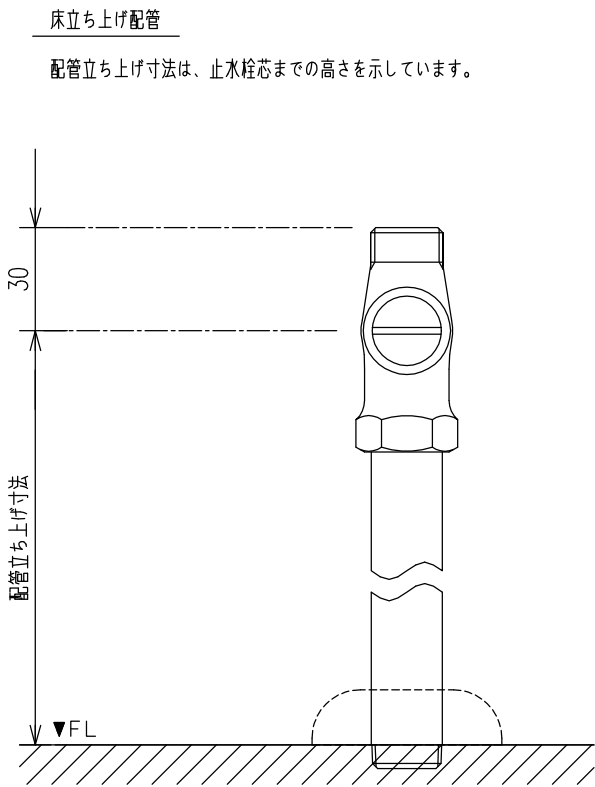

■タッチレス水栓ナビッシュ 推奨電源位置図

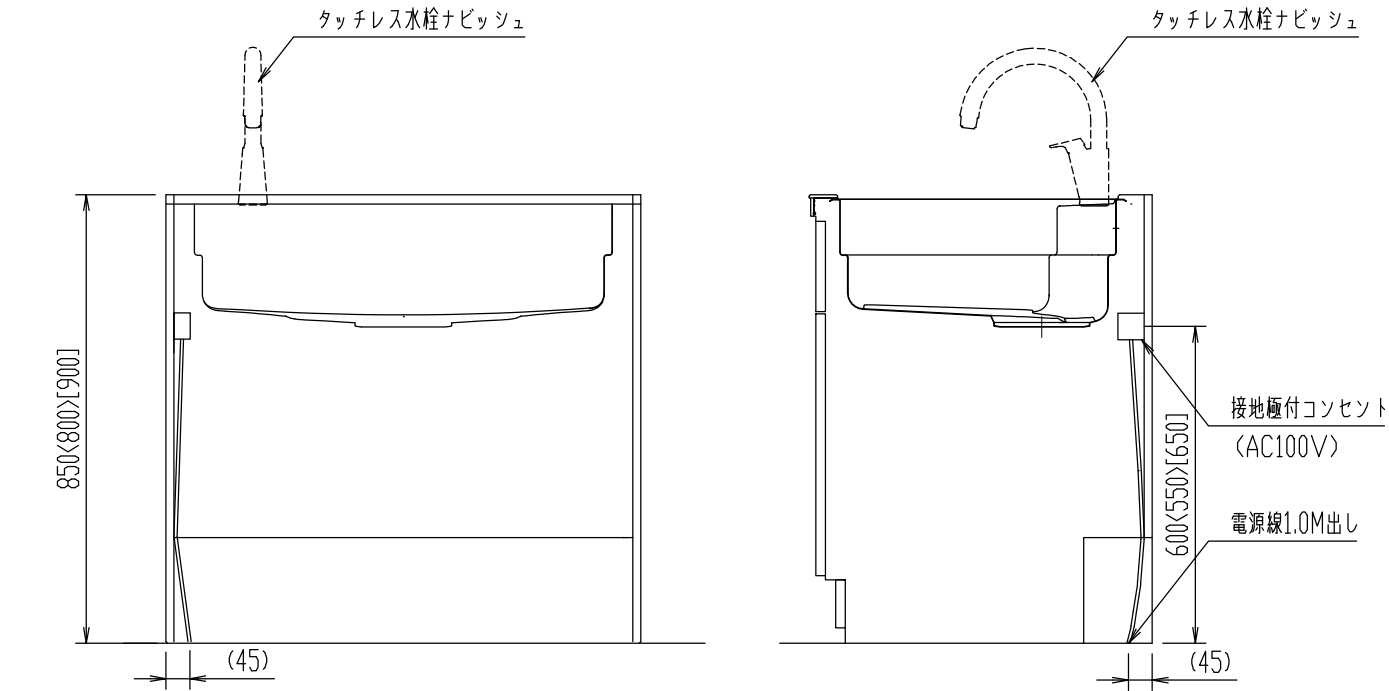


○水栓がシンク右側の場合、電源位置は左右対象の位置にしてください。
○水栓がシンク中央の場合、電源位置は左右どちらでも構いません。
○< >内寸法はワークトップ高さ80cmの場合、[]内寸法はワークトップ高さ90cmの場合。

■ キッチン取付者さま向け 動画コンテンツ ■

商品取付けの注意点を2次元コードでご視聴いただけます。
取付日より前に、是非ご確認ください。

荷扱い・搬入


荷扱い・搬入

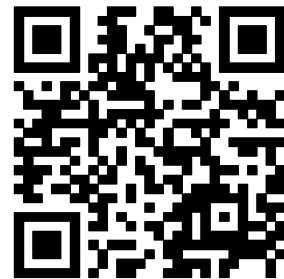

作成日：2024年10月01日



カウンター開梱搬入「養生ツール」

カウンター開梱搬入 「養生ツール」のご紹介

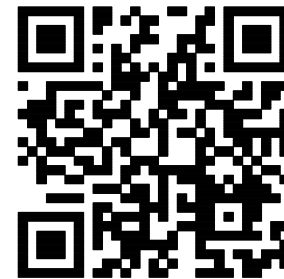

作成日：2024年10月01日

不陸の確認と調整

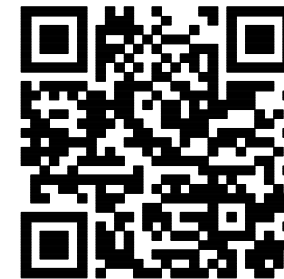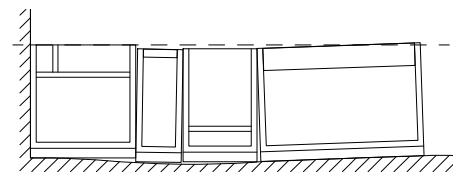

作成日：2024年02月07日



マグネットキッチンパネル

マグネット キッチンパネル 「取付・設置」ポイント





作成日：2024年03月06日

人造大理石カウンターL型キッチン

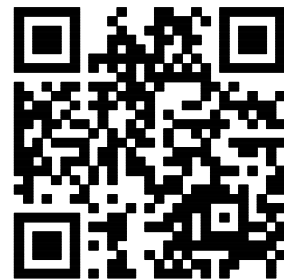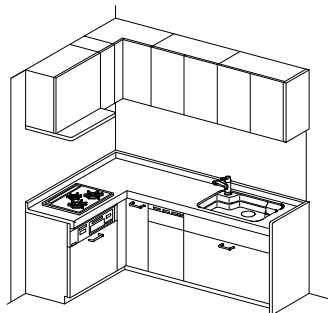

作成日：2024年02月07日




センターキッチン（ペニンシュラ型）

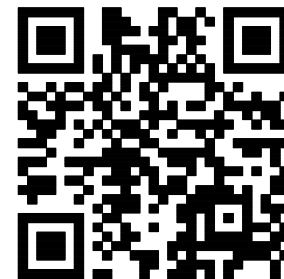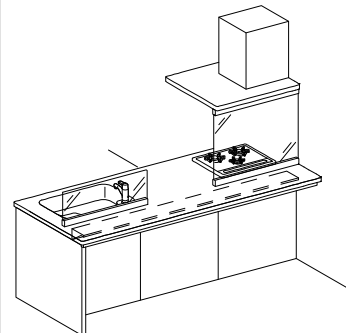

作成日：2024年02月07日

特記事項 扉色 VL2:グレイジュスタック 取手 [S]ミドル取手S (ブラック) ワークトップカラー 【BN】 ブラウンストーン	物件名	小原徳晃 様邸	案件No.	図面名	担当	図面	図番
	仕様		A2511DDD0EYYHZ	機能図	栗野 友仁		株式会社 LIXIL
		ND23	見積No.	縮尺	日付		
			M25119443182-013-2			2026.02.03	

■ キッチン取付者さま向け 動画コンテンツ ■
商品取付けの注意点を2次元コードでご視聴いただけます。
取付日より前に、是非ご確認ください。

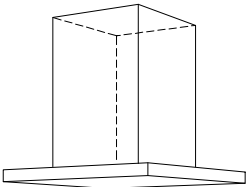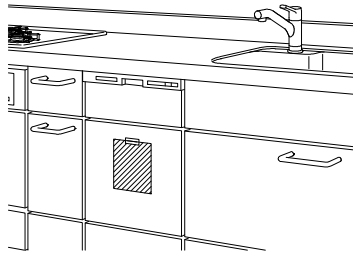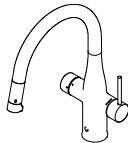センターフード型レンジフード (天吊りフード)  作成日：2024年06月03日 	I H加熱機器関連 I H加熱機器 仕切り板 作成日：2024年02月07日 	食器洗い乾燥機  作成日：2024年02月07日 	ミネラル浄水栓 Greentap  作成日：2024年06月03日 
---	--	--	---

食器洗い機 ミーレ製 フロントオープン食洗器 作成日：2025年10月31日 	食器洗い機 パナソニック製 フロントオープン食洗器 作成日：2025年10月31日 		
--	---	--	--

--	--	--	--

特記事項 扉色 VL2:グレージュスタッコ 取手 [S]ミドル取手S (ブラック) ワークトップカラー 【BN】 ブラウンストーン	物件名	小原徳晃 様邸	案件No.	図面名	担当	図面	図番
			A2511DDD0EYYHZ	機能図	栗野 友仁		株式会社 LIXIL
	仕様	ND23	見積No.	縮尺	日付		
			M25119443182-013-2		2026.02.03		