



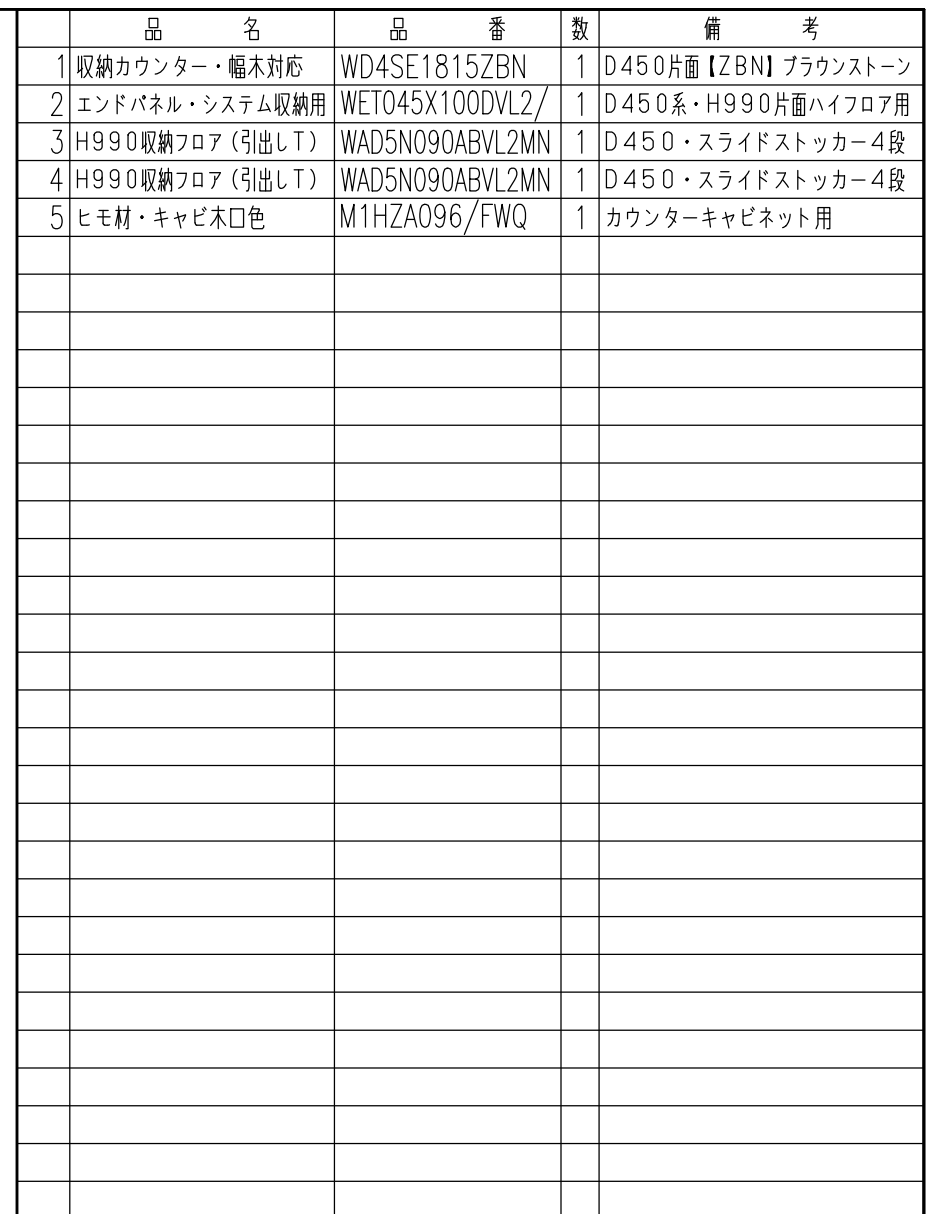


特記事項 扉色 VL2:グレイジュスタック 取手 [M]スリム取手M (ブラック)	物件名	小原徳晃 様邸	案件No.	図面名	担当	図面	図番 : 株式会社 LIXIL
			A2511DDD0EYYHZ	レイアウト図	葉野 友仁		
	仕様	ND23	見積No.	縮尺	日付		
			M25119443182-013-3	1/30	2026.02.03		

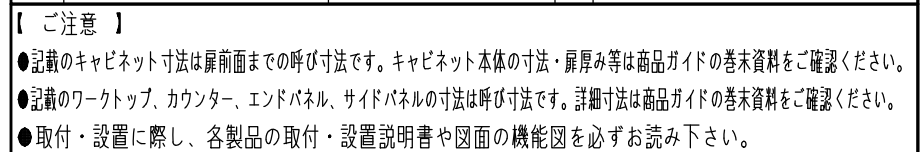

特記事項 扉色 VL2:グレージュスタック 取手 [M]スリム取手M (ブラック)	物件名	小原徳晃 様邸	案件No.	図面名	担当	図面	図番 : 株式会社 LIXIL
			A2511DDDD0EYYHZ	納まり図	栗野 友仁		
	仕様	ND23	見積No.	縮尺	日付		
			M25119443182-013-3	1/30	2026.02.03		

■ 床の不陸に関して

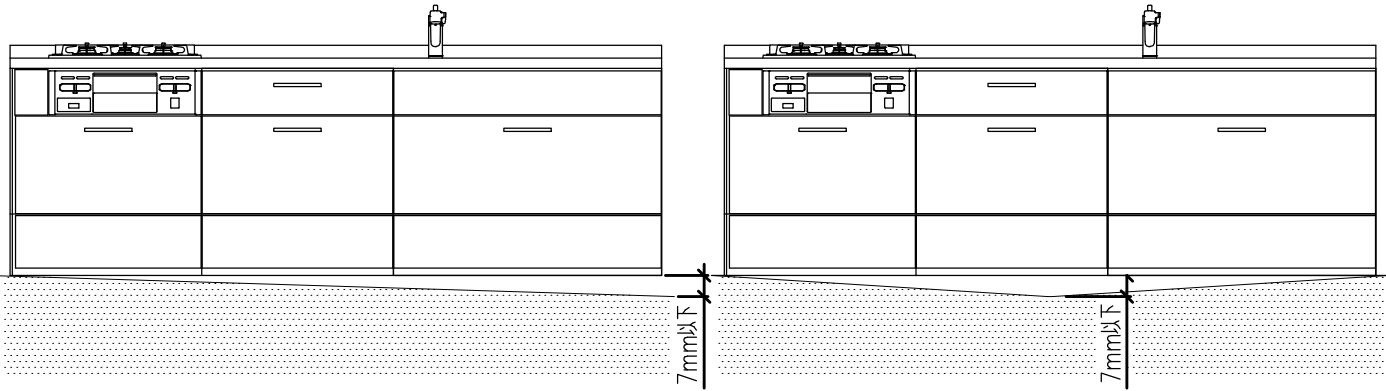

床の不陸は、7 m m 以下に抑えるようにしてください。不陸が大きい場合は、現場責任者に床の修正を依頼してください。
※キャビネット取付時には不陸調整スペーサー等で水平になるように設置してください。

特記事項 扉色 VL2:グレージュスタック 取手 [M]スリム取手M（ブラック）	物件名	小原徳晃 様邸	案件No.	図面名	担当	図面	図番
			A2511DDD0EYYHZ	機能図	栗野 友仁		株式会社 LIXIL
	仕様	ND23	見積No.	縮尺	日付		
			M25119443182-013-3		2026.02.03		

■ キッチン取付者さま向け 動画コンテンツ ■


商品取付けの注意点を2次元コードでご視聴いただけます。

取付日より前に、是非ご確認ください。

1  —  

荷扱い・搬入


荷扱い・搬入

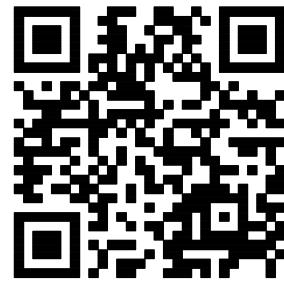

作成日：2024年10月01日



カウンター開梱搬入「養生ツール」

カウンター開梱搬入 「養生ツール」のご紹介

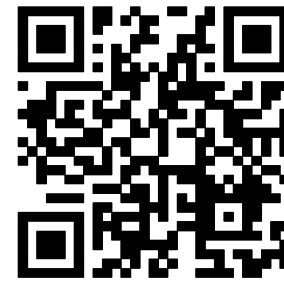

作成日：2024年10月01日

不陸の確認と調整

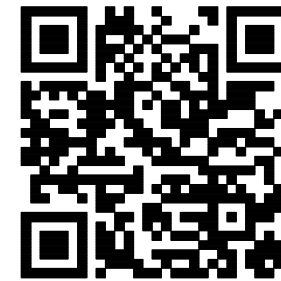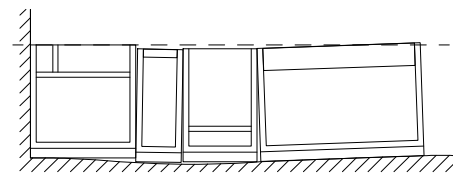

作成日：2024年02月07日



マグネットキッチンパネル

マグネット キッチンパネル 「取付・設置」ポイント





作成日：2024年03月06日

人造大理石カウンターL型キッチン

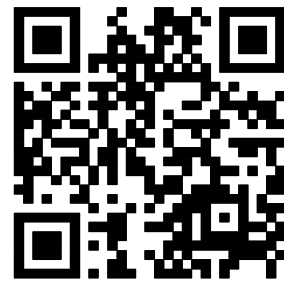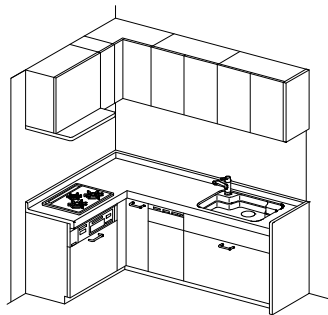

作成日：2024年02月07日




センターキッチン（ペニンシュラ型）

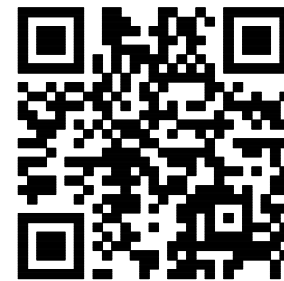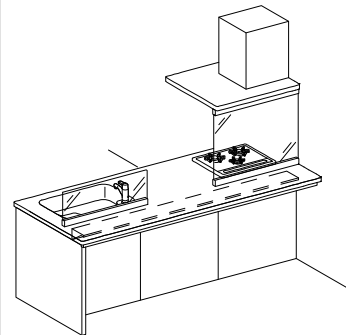

作成日：2024年02月07日

特記事項 扉色 VL2:グレージュスタッコ 取手 [M]スリム取手M(ブラック)	物件名	小原徳晃 様邸	案件No.	図面名	担当	図面	図番 :
			A2511DDD0EYYHZ	機能図	栗野 友仁		
	仕様	ND23	見積No.	縮尺	日付		株式会社 LIXIL
			M25119443182-013-3		2026.02.03		

■ キッチン取付者さま向け 動画コンテンツ ■
商品取付けの注意点を2次元コードでご視聴いただけます。
取付日より前に、是非ご確認ください。

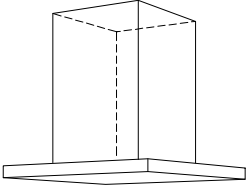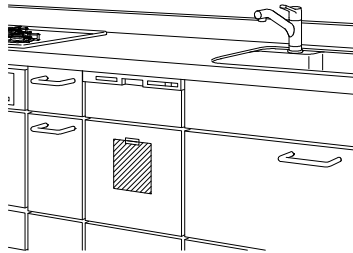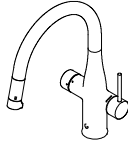センターフード型レンジフード (天吊りフード)  作成日：2024年06月03日 	I H加熱機器関連 I H加熱機器 仕切り板 作成日：2024年02月07日 	食器洗い乾燥機  作成日：2024年02月07日 	ミネラル浄水栓 Greentap  作成日：2024年06月03日 
---	--	--	---

食器洗い機 ミーレ製 フロントオープン食洗器 作成日：2025年10月31日 	食器洗い機 パナソニック製 フロントオープン食洗器 作成日：2025年10月31日 		
--	---	--	--

--	--	--	--

特記事項 扉色 VL2:グレージュスタッコ 取手 [M]スリム取手M (ブラック)	物件名	小原徳晃 様邸	案件No.	図面名	担当	図面	図番
			A2511DDD0EYYHZ	機能図	栗野 友仁		株式会社 LIXIL
	仕様	ND23	見積No.	縮尺	日付		
			M25119443182-013-3		2026.02.03		