


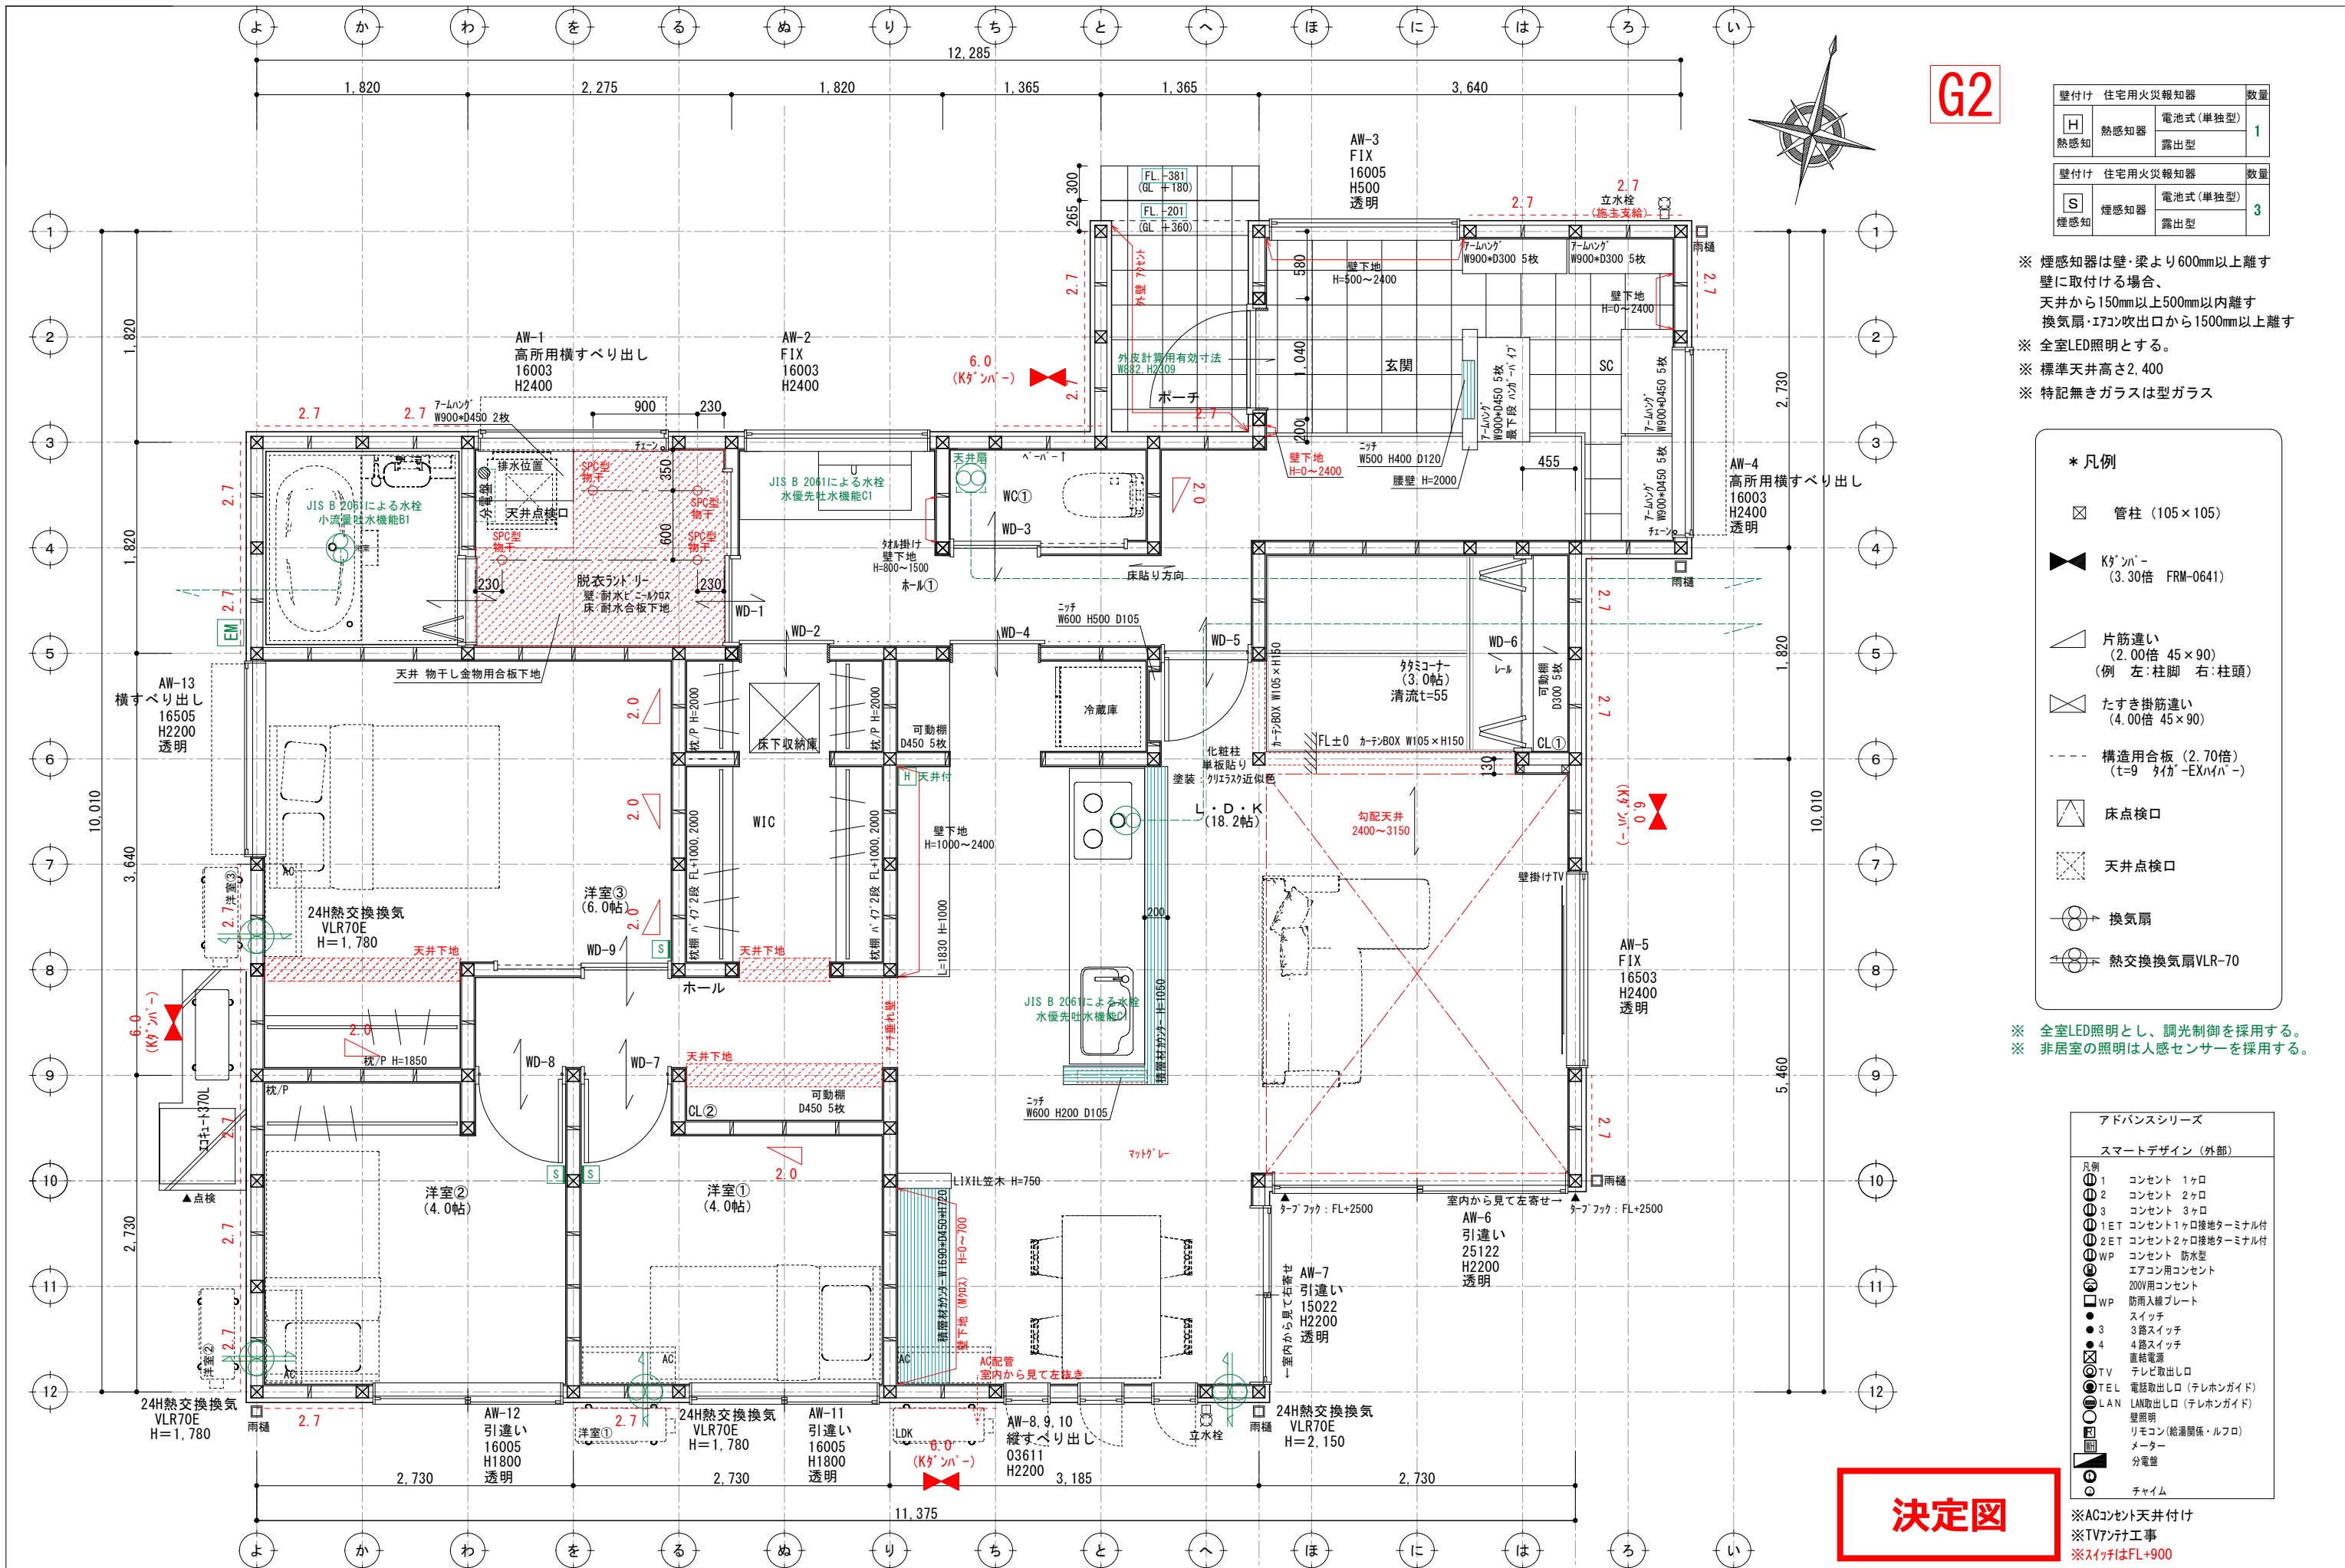

G2

壁付け 住宅用火災報知器		数量
H	熱感知器	電池式(単独型)
	熱感知器	露出型
1		
壁付け 住宅用火災報知器		数量
S	煙感知器	電池式(単独型)
	煙感知器	露出型
3		

- ※ 煙感知器は壁・梁より600mm以上離す壁に取付ける場合、天井から150mm以上500mm以内離す換気扇・エアコン吹出口から1500mm以上離す
- ※ 全室LED照明とする。
- ※ 標準天井高さ2,400
- ※ 特記無きガラスは型ガラス

* 凡例

- 管柱 (105×105)
- K's'n'p' (3.30倍 FRM-0641)
- 片筋違い (2.00倍 45×90) (例 左:柱脚 右:柱頭)
- たすき掛筋違い (4.00倍 45×90)
- 構造用合板 (2.70倍) (t=9 9'4'6"-EX'n'n')
- 床点検口
- 天井点検口
- 換気扇
- 熱交換換気扇VLR-70

- ※ 全室LED照明とし、調光制御を採用する。
- ※ 非居室の照明は人感センサーを採用する。

アドバンスシリーズ		
スマートデザイン (外部)		
凡例	1	コンセント 1ヶ所
2	コンセント 2ヶ所	
3	コンセント 3ヶ所	
1ET	コンセント1ヶ所接地ターミナル付	
2ET	コンセント2ヶ所接地ターミナル付	
WP	コンセント 防水型	
WP	エアコン用コンセント	
WP	200V用コンセント	
WP	防雨入線プレート	
WP	スイッチ	
3	3路スイッチ	
4	4路スイッチ	
直結電源	直結電源	
TV	テレビ取出口	
TEL	電話取出口 (テレビガイド)	
LAN	LAN取出口 (テレビガイド)	
壁照明	壁照明	
リモコン	リモコン (給湯関係・ルフロ)	
メーター	メーター	
分電盤	分電盤	
チャイム	チャイム	

- ※ACコンセント天井付け
- ※TVアンテナ工事
- ※スイッチはFL+900

決定図