


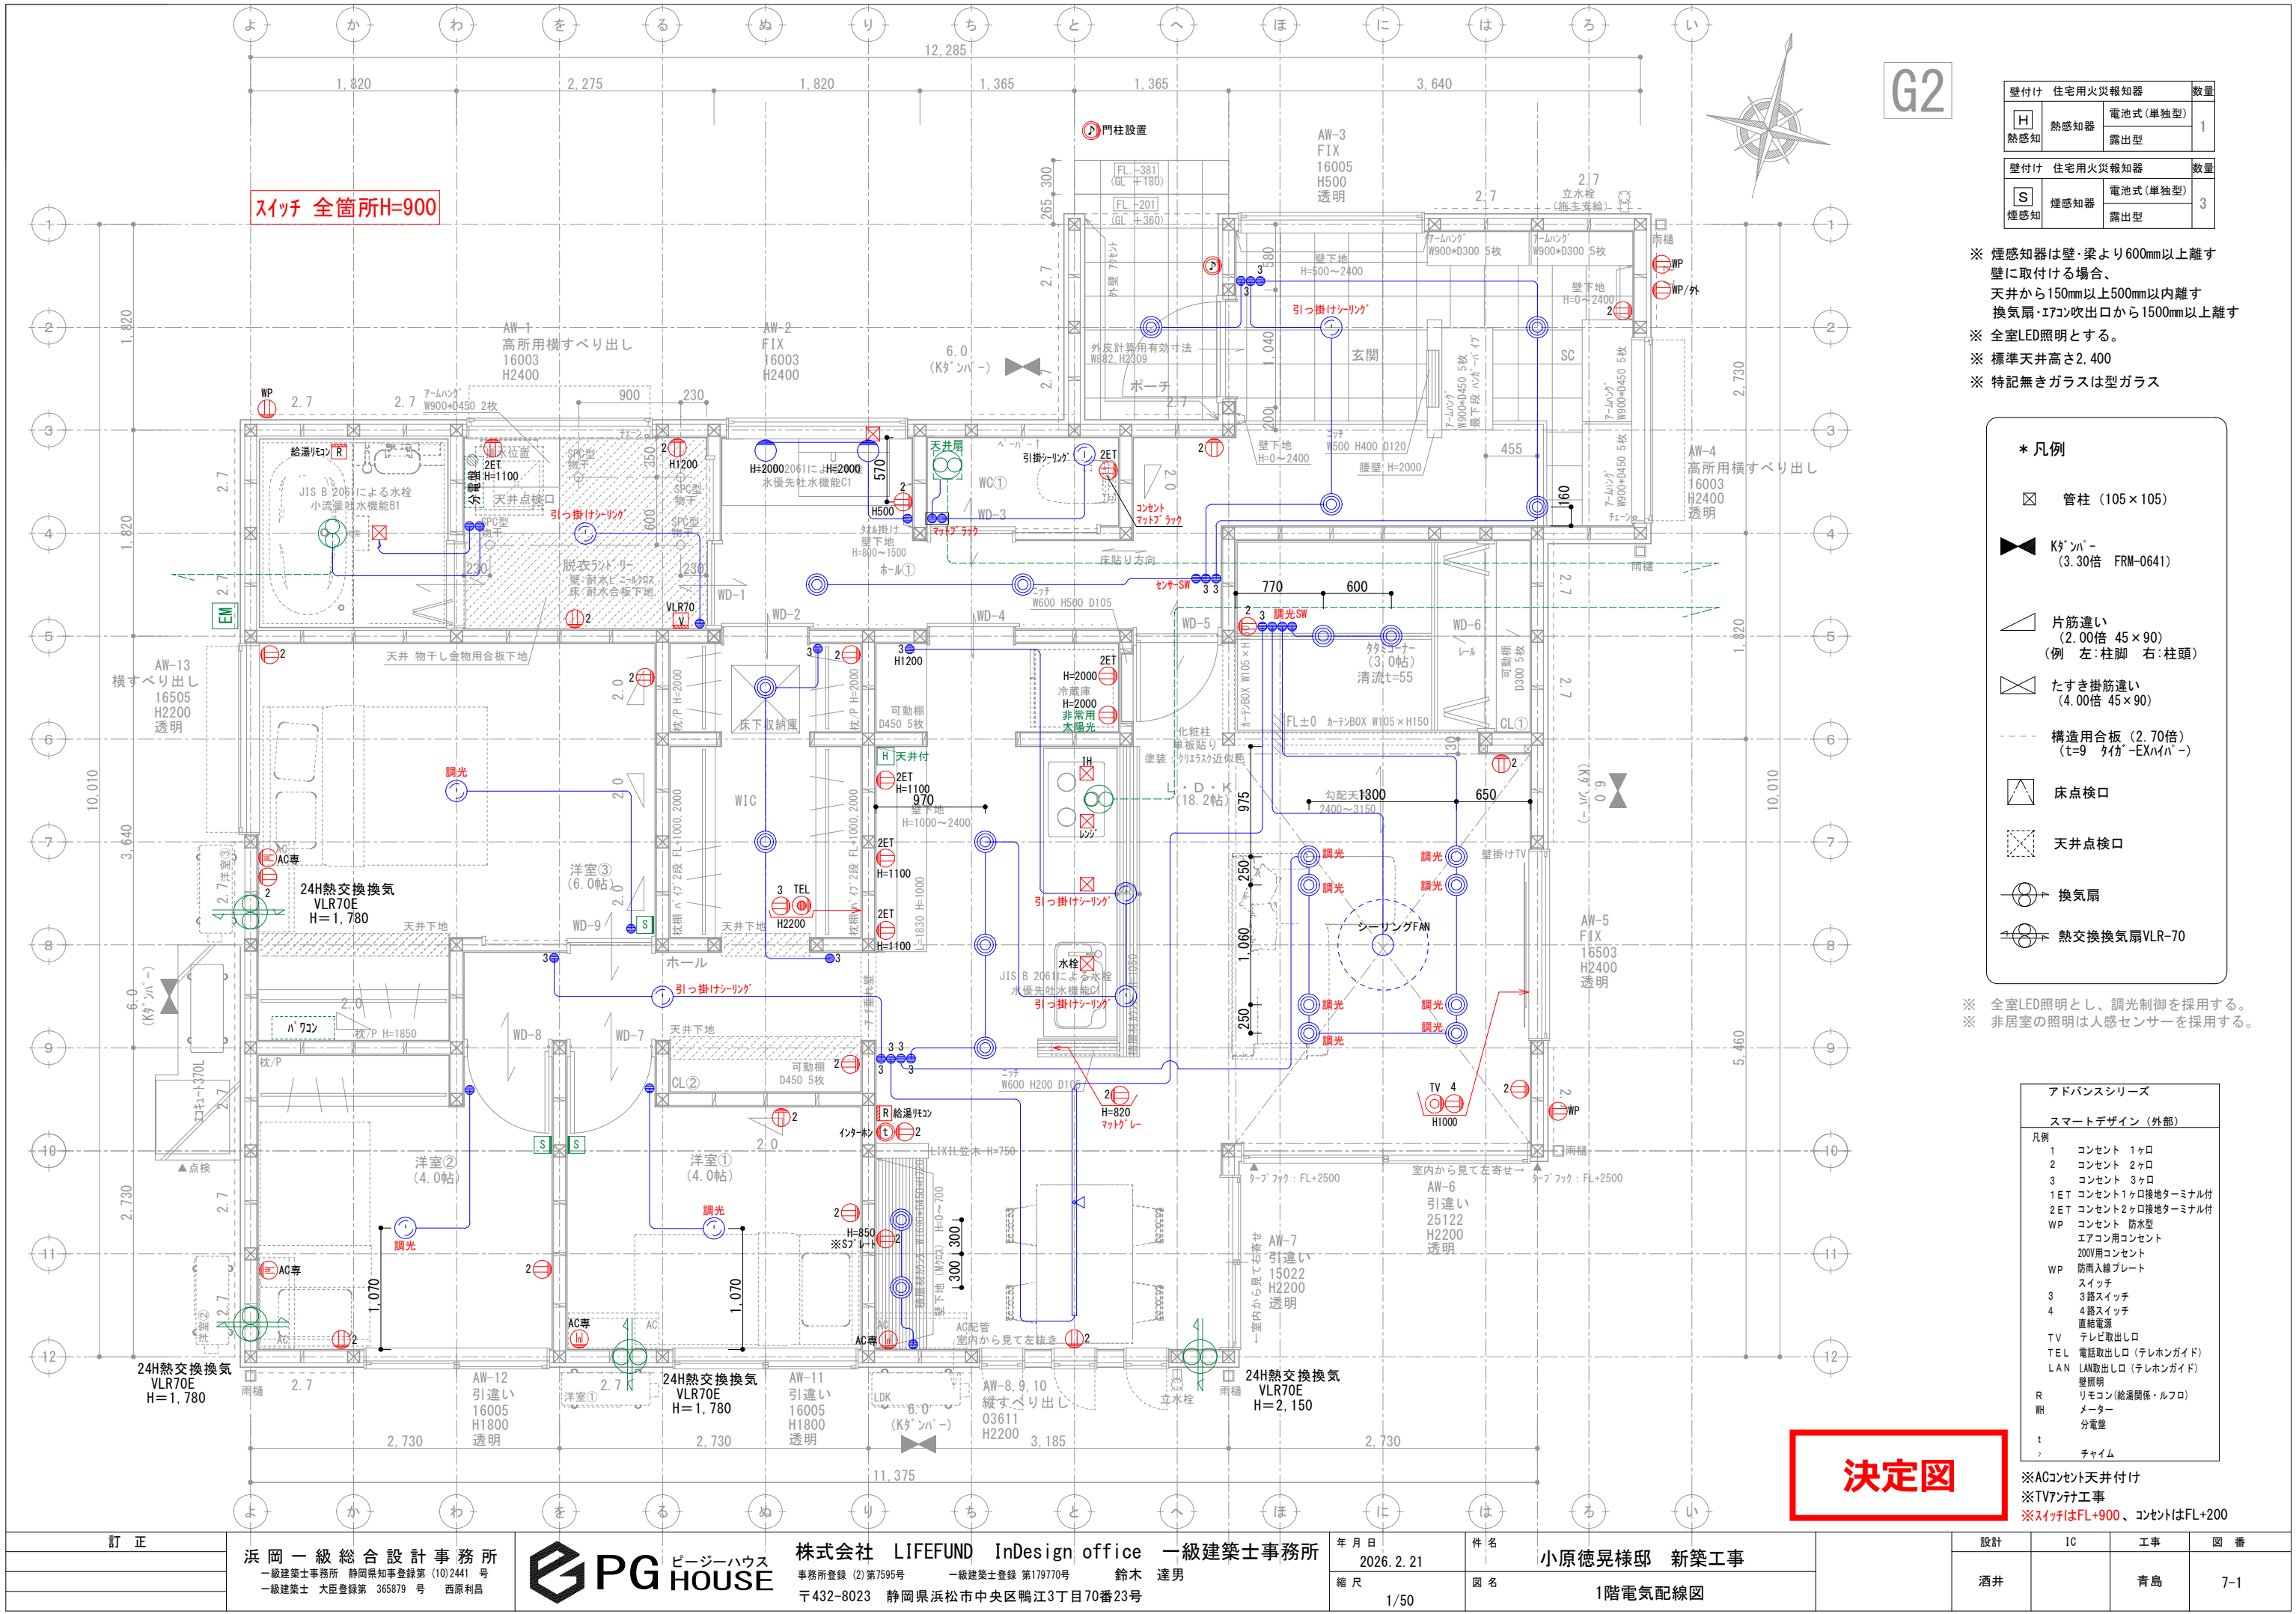

壁付け 住宅用火災報知器			数量
H	熱感知器	電池式(単独型)	1
	熱感知器	露出型	
壁付け 住宅用火災報知器			数量
S	煙感知器	電池式(単独型)	3
	煙感知器	露出型	

※ 煙感知器は壁・梁より600mm以上離す
壁に取付ける場合、
天井から150mm以上500mm以内離す
換気扇・エアコン吹出口から1500mm以上離す

※ 全室LED照明とする。

※ 標準天井高さ2,400

※ 特記無きガラスは型ガラス

- * 凡例
- 管柱 (105×105)
 - K's'ンバー (3.30倍 FRM-0641)
 - 片筋違い (2.00倍 45×90)
(例 左:柱脚 右:柱頭)
 - たすき掛筋違い (4.00倍 45×90)
 - 構造用合板 (2.70倍)
(t=9 9'付 -EX'n' -)
 - 床点検口
 - 天井点検口
 - 換気扇
 - 熱交換換気扇VLR-70

※ 全室LED照明とし、調光制御を採用する。

※ 非居室の照明は人感センサーを採用する。

アドバンスシリーズ	
スマートデザイン (外部)	
凡例	
1	コンセント 1ヶ所
2	コンセント 2ヶ所
3	コンセント 3ヶ所
1ET	コンセント1ヶ所接地ターミナル付
2ET	コンセント2ヶ所接地ターミナル付
WP	コンセント 防水型
	エアコン用コンセント
WP	200V用コンセント
WP	防雨入線プレート
	スイッチ
3	3路スイッチ
4	4路スイッチ
	直結電源
TV	テレビ取出口
TEL	電話取出口 (テレホンガイド)
LAN	LAN取出口 (テレホンガイド)
	壁照明
R	リモコン (給湯関係・ルフロ)
WH	メーター
t	分電盤
	チャイム

※ACコンセント天井付け

※TVアンテナ工事

※スイッチはFL+900、コンセントはFL+200