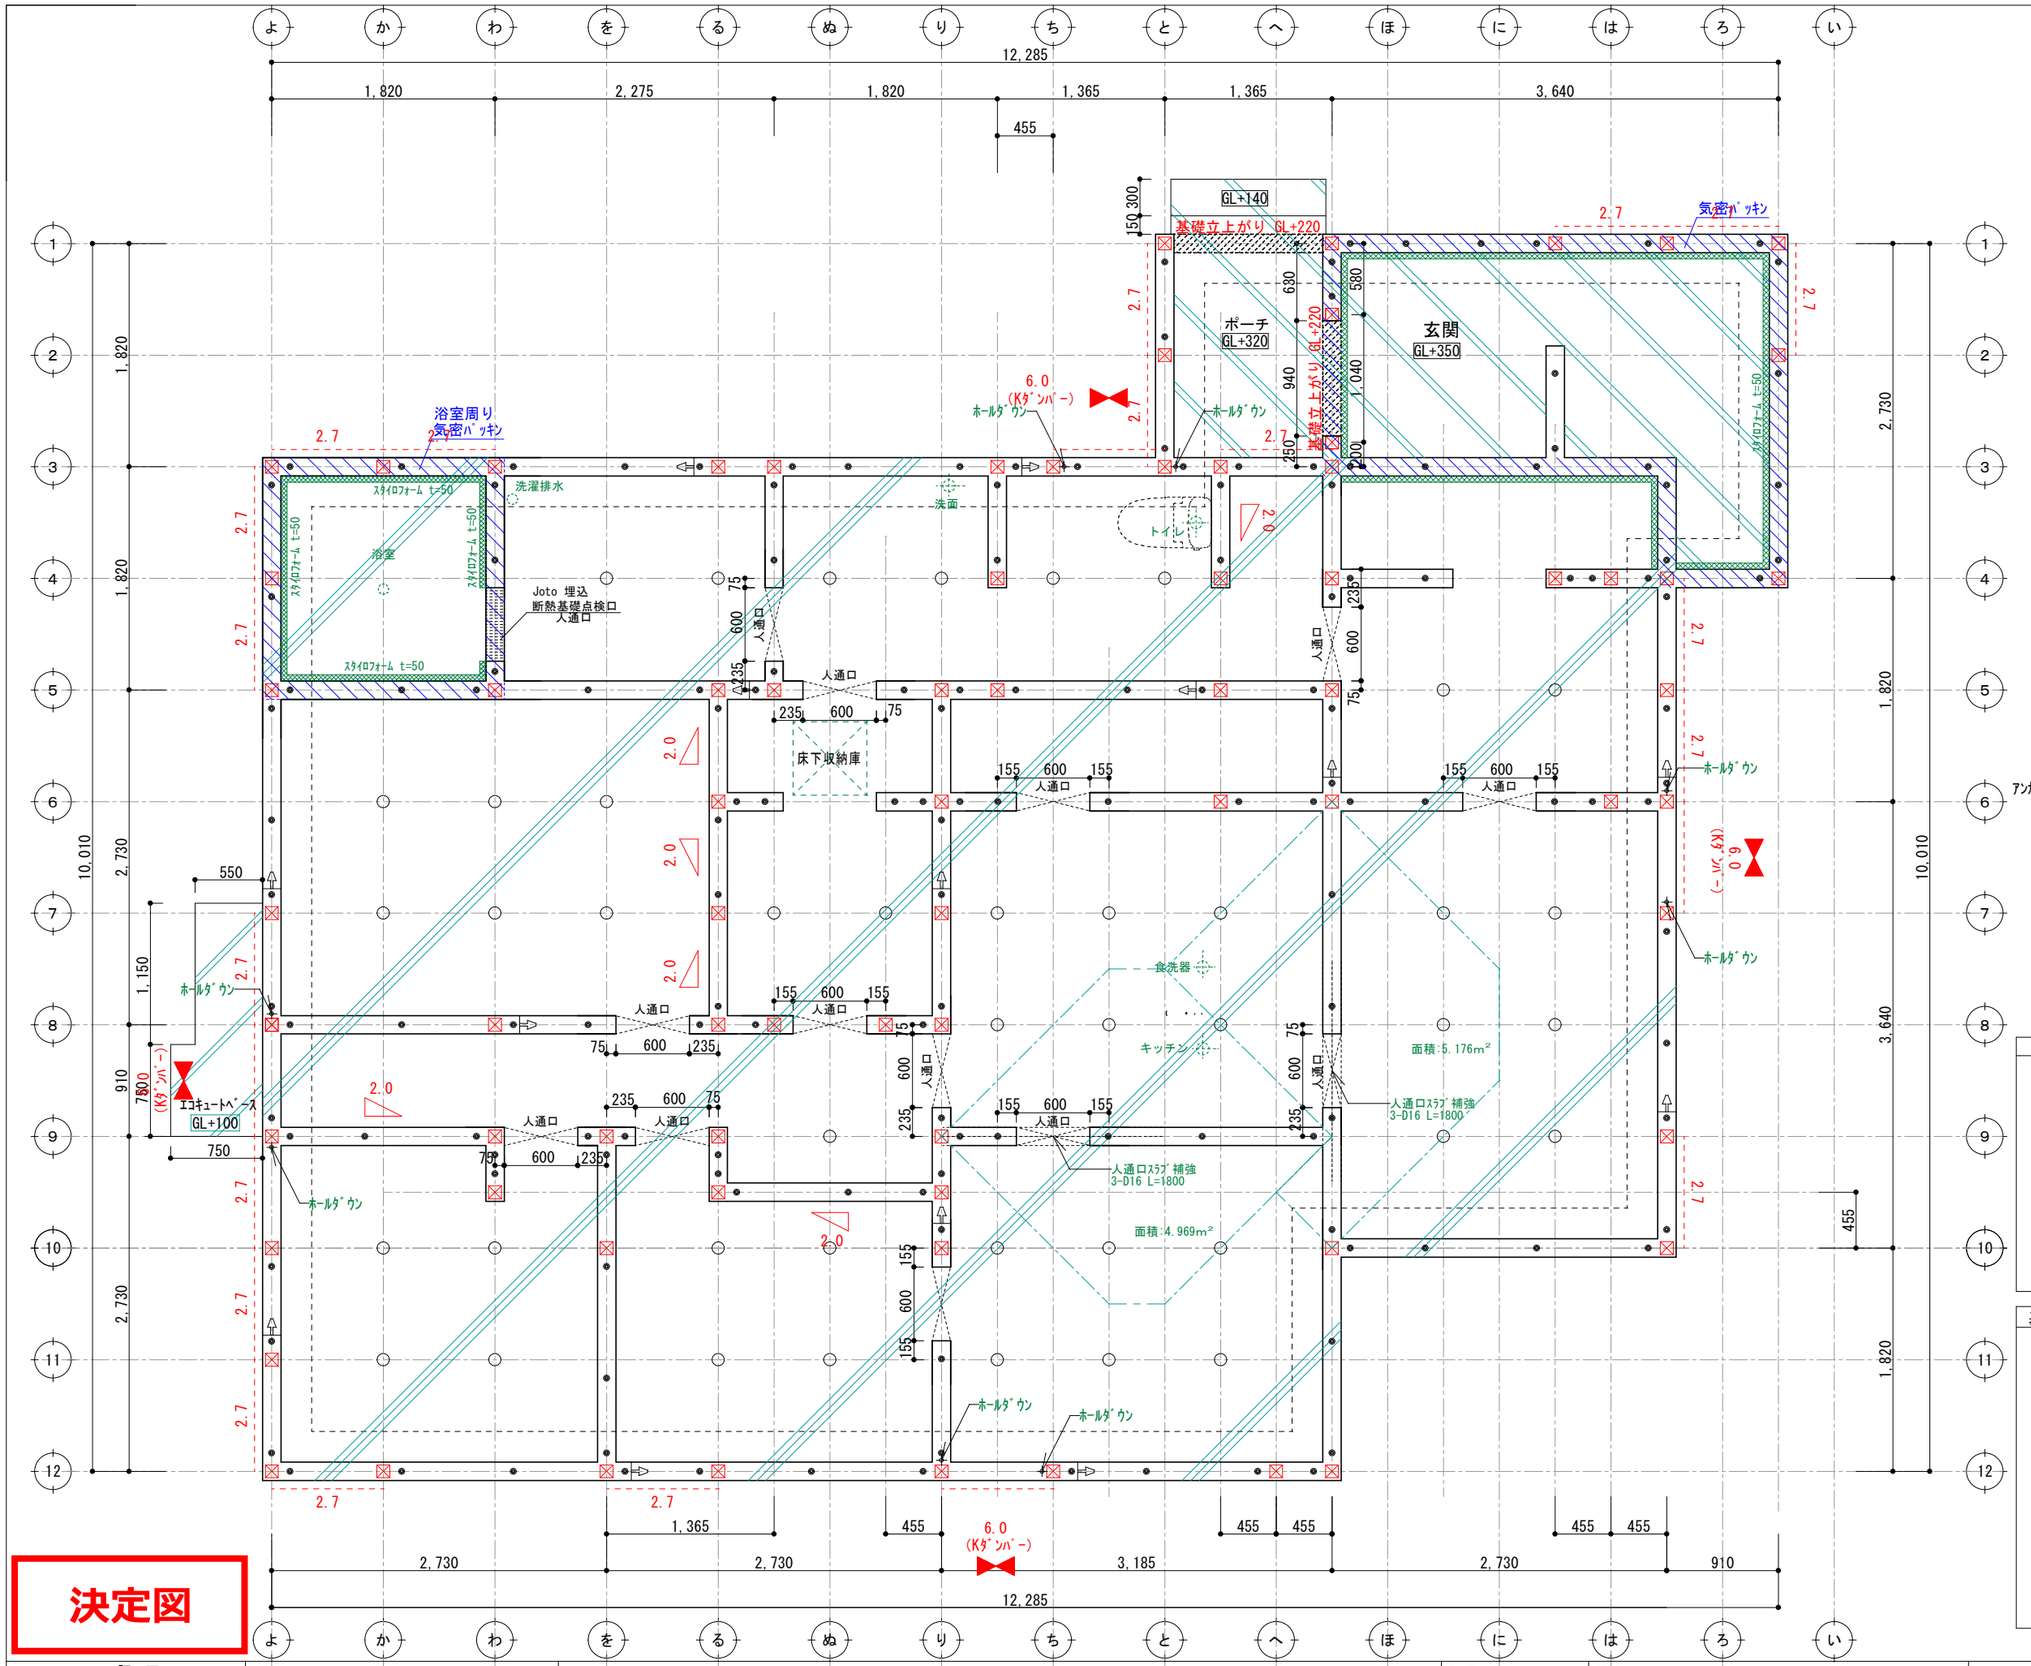

決定図

基礎伏図について特記なき場合に限り下記による。

1. コンクリート：呼び強度 21N/mm2
2. 鉄筋：SD295A
3. 設計地耐力：fe=20kN/㎡
   地耐力計測後、不足の場合は相当の改良を行い、満たすものとする。
4. 基礎の位置は、芯振分けとする。
5. 玄関・S/C・UB周囲の基礎天端は気密ﾊﾟｯｷﾝ施工(網掛け部)とし、その他の基礎天端は基礎ﾊﾟｯｷﾝ施工とする。
6. 設備配管の屋内への取り入れは基礎立上り部のスリーブによる。

訂正								
	浜岡一級総合設計事務所 一級建築士事務所 静岡県知事登録第(10)2441号 一級建築士 大臣登録第 365879 号 西原利昌	LIFEFUND PG HOUSE	株式会社 LIFEFUND InDesign office 一級建築士事務所 事務所登録 (2)第7595号 一級建築士登録 第179770号 鈴木 達男 〒432-8023 静岡県浜松市中央区鴨江3丁目70番23号	年月日 2026.2.21 縮尺 1/50	件名 小原徳晃様 邸新築工事 図名 基礎伏図		設計 酒井	IC	工事 青島	図番 B-1