

■ 仕 様				■ HEAT20 G2	
断熱工事		■ 床:ネオフォーム t90 ■ 土間床等の外周:スタイロフォームAT t50 ■ 壁:アクアフォームLITE吹付 t90 ■ 天井:アクファフォームLITE吹付 t220			
床下換気		■ 基礎パッキン JOTO (玄関・UB周り:気密基礎パッキン)			
防虫防蟻		■ 土壌処理・木部 ガントナーMC			
■ 外 部 仕 上 表				■ 22条地域	
部位		仕上・仕様・メーカー		色番・品番	
屋根		■ ガルバリウム鋼板(t0.35)UK立平 ニスカラーPro GH 軒先通気金物 日本住環境株式会社【REV-15】		GHK01 Sブラック	
パラペット笠木		■ なし			
破風・鼻隠		■ なし			
雨樋	(軒樋)	■ Panasonic サーフeskエアFS-I型		ブラック	
	(竖樋)	■ Panasonic S30角樋		ブラック	
軒天	屋根軒	■ 神島化学 t= 6mm 軒天ボード エンボス		Wチャコールブラック	
	ポーチ軒	■ なし			
	バルコニー軒	■ なし			
オーバーハング水切り		■ ガルバリウム鋼板 ※外壁合わせ JOTO:HF-A3550		ブラック	
外壁	通気金物(15mm)	■メイン	Kmewエクセレージ・シマンフラット	光セラ	ソイルチタンダークグレー
	※下地面材:タイガーEXハイパー	■アクセントA	Kmewエクセレージ・ルミナスウッド		QW7ガラスオレンジ
	防火認定 PC030BE-4028	■アクセントB	なし		
玄関ポーチ		■ 床 玄関タイルに同じ			
基礎		■ 立上り巾木: モルタル刷毛引き		-	
基礎水切り金物		■ JOTO鋼板製 防鼠材付き水切り JOTO:WMF-N35		ブラック	
バルコニー	床・内壁	■ なし		-	
	笠木	■ なし			
外部建具		■ LIXIL EW(アルゴンガス高遮熱仕様LowEトリプルガラス クリア) ・SD、TSは、メーカー設定による。 ・オペレーター付サッシの場合は固定網戸とする ・グレモンハンドル式サッシの場合は可動網戸とする		外観 ブラック 内観 ホワイト ※樹脂パッキン・網戸付	
シャッター		■ なし			
軒天通気金物				ブラック	
玄関扉		■ LIXIL ジエスタ2 K2仕様 LIXILファミロック タグキー×3 (電池式)		ドア型: M26 型 ドア色: チェリーウッド ハンドル: S型ハンドル 色 ブラック	
外部物干し金物		■ なし			
換気フード		■ 局所換気扇(トイレ 浴室 キッチンフード) 防火ダンパー無		外気フード: ブラック	
		■ ダクトレス熱交換換気システム (日本スティーベル株式会社) VLR-70E 防火ダンパー無		外気フード: B ブラック 室内パネル ホワイト	

■ 構 造 概 要					
基礎	■ RCベタ基礎コンクリート				
通し柱・管柱	■ 構造用集成材 105×105		間柱	■ 集成材	
土台	■ 桧 105×105	大引き	■ 桧 90*90	筋交い	■ 構造用製材 火打梁 ■ 鋼製火打(当社基準により米松あり)
桁・梁	■ 構造用製材及び集成材			制震装置	■ Kダンパー (株)アイ・エム・エー
■ 設 備 装 着 品					
住宅設備	部位	メーカー	商品名 ※ 詳細は見積り、プレゼン参照	見積りNo.	(日付)
	キッチン	LIXIL	■ ND	見積り番号 : M25119443182-014-2	(日付) 2026.02.04
	バックカウンタ ※オプション	LIXIL	■ ES L1800(W900スライドストッカー×2)	見積り番号 : M25119443182-014-3	(日付) 2026.02.04
	浴室	LIXIL	■ AX1616 PGハウス標準仕様	見積り番号 : M25119443182-014-1	(日付) 2026.02.04
	1Fトイレ	LIXIL	■ ベーシアシャワートイレ 白 ● タオル掛け: KF-AA70D(リンク) タンク手洗 無し ● 紙巻き器: CF-AA22H /WA	見積り番号 : M25119443182-014-5	(日付) 2026.02.04
	洗面台	LIXIL	■ カスタムバニティ	見積り番号 : M25119443182-014-4	(日付) 2026.02.04
			その他 ● タオル掛け:なし(支給品取付)		
給排水設備	給湯器	■ エコキュート370L Panasonic Sシリーズ スタンダードモデル 追い焚きフルオート			
	排水	■ 下水	■ 外部立柱柱: PVC製 水柱柱12型アイボリー【前澤化成工業】	施主支給 ジラーレW TK3-SAW ブラック	
	外水栓	■ 2 カ所 (平面図参照)			
	外部ガーデンパン	■ 無し			
	その他	■ 洗濯機用単水栓: 緊急止水弁付 ■ 洗濯機用排水:トラップ金物(標準) ■ 排水さや管(長期優良住宅仕様)			
ガス配管設備	■ なし (配置図・平面図参照) ■ガス使用器具				
電気設備	インターホン	■ パナソニック VL-SE31XL			
	TVアンテナ	■ UHF + BS・110度CS／CSアンテナ [2K・4K・8K対応] ■ブラック ※電波状況によりホワイトになる可能性あり			
	エアコン	■ 設置場所:			
	ソーラー	■ あり(Qセルズ) 12 枚 5.28 KW Re.RISE-G3 440 (1722×1134×30)			
	※標準搭載	※メーカーのモデルチェンジ等で後継品に変更される可能性あり ■ 屋内パワコン エネルギーマネジメントシステム Cube J			
その他					
決定図					

決定図


			株式会社 LIFEFUND InDesign office 一級建築士事務所 事務所登録 (2) 第7595号 一級建築士登録 第179770号 鈴木 達男 〒432-8023 静岡県浜松市中央区鴨江3丁目70番23号	年 月 日 2026.2.21 縮尺	件名 小原徳晃 様邸 新築工事 図面 仕上表 1		設計	IC	工務	図 番					
浜 岡 一 級 総 合 設 計 事 務 所															
一級建築士事務所 静岡県知事登録第 (10)2441 号															
一級建築士 大臣登録第 365879 号 西原利昌							酒井		青島	1-1					

内 部 仕 上 表 （壁下地:石膏ボード12.5mm/天井下地:9.5mm）※脱衣室:床合板特類 下地									
階		床	巾木	壁	品番	廻 縁	天 井	品番	特記事項
1F	ポーチ	LIXILパセオ300/PSO-FIO 4							
	玄関	LIXILパセオ300/PSO-FIO 4	ライン巾木(W)	ビニルクロス	SLP311	突付	ビニルクロス	SLP311	アクセントクロス 有
	ホール①	イタ銘木フロア-ラスティックt12 アカシア3P	ライン巾木(W)	ビニルクロス	SLP311	突付	ビニルクロス	SLP311	アクセントクロス 有
	LDK	イタ銘木フロア-ラスティックt12 アカシア3P	ライン巾木(W)	ビニルクロス	SLP311	突付	ビニルクロス	SLP311	アクセントクロス 有
	タミコーナー	健やかおもて 清流	ライン巾木(W)	ビニルクロス	SLP311	突付	ビニルクロス	SLP311	灰桜色
	脱衣ランドリー	フロアタイルt2.3 サンゲツIS-2018	ライン巾木(W)	ビニルクロス	SLP311	突付	ビニルクロス	SLP311	
	WC①	フロアタイルt2.3 サンゲツIS-2049	ライン巾木(W)	ビニルクロス		突付	ビニルクロス		アクセントクロス 有
	ホール②	イタ銘木フロア-ラスティックt12 アカシア3P	ライン巾木(W)	ビニルクロス	SLP311	突付	ビニルクロス	SLP311	
	洋室①	イタ銘木フロア-ラスティックt12 アカシア3P	ライン巾木(W)	ビニルクロス	SLP311	突付	ビニルクロス	SLP311	アクセントクロス 有
	洋室②	イタ銘木フロア-ラスティックt12 アカシア3P	ライン巾木(W)	ビニルクロス	SLP311	突付	ビニルクロス	SLP311	
	洋室③	イタ銘木フロア-ラスティックt12 アカシア3P	ライン巾木(W)	ビニルクロス	SLP311	突付	ビニルクロス	SLP311	
	WIC	イタ銘木フロア-ラスティックt12 アカシア3P	ライン巾木(W)	ビニルクロス	SLP311	突付	ビニルクロス	SLP311	
物入・収納・CL etc		※接続する部屋と同仕様とする							

上 框 ※	■ LIXILラシッサS 上框のみ30×150 色: クリエチェリー	
階 段	■ LIXIL なし	ササラ:
KA階段で対応できない場合、オプションにてラシッサS階段	段板 : ラウンド手摺: 上段框:	蹴込板: 手摺金物 長尺笠木156: LIXIL
窓 枠	■ LIXIL スマート10(玄関以外) 色 プレシャスホワイト ※浴室ドア枠 フクビ3方枠 [ホワイト]	
キッチン笠木 カウンター	■ ゴム集成カウンター(オスモカラー) 形状 L型(ジョイント加工)	色 クリエラスク(近似色) t=30
天井点検口	■ 天井アルミ点検口枠 450角 TAN45BW フクビ化学工業 ミルキーホワイト	
床下収納庫	■ 高気密型床下点検口断熱型 SPF-R6060 城東テクノ 収納付 (脱衣室) ミディアムブラウン(MB)	
トイレ棚	■ なし	
室内物干し金物	■ 川口技研SPC型 2セット	ブラック
LDK-カウンター	■ ゴム集成カウンター(オスモカラー) 形状:	色 クリエラスク(近似色) t=25
下足入 プッシュタイプ	■ なし	色 形状:


支給品	■ 洗面 タオル掛け JIAYU003 ■ 壁掛けTV金物 VA126 Mサイズ
備考	■ 付框は30×150 プレシャスホワイト ■ 可動棚:アートランバー 色: アッシュウォールナット(SC、パントリー、ランドリー) クリアホワイト(タミコーナー、CL②) ■ 棚受け金物類 色:ホワイト ■ ハンガーパイプ(SS-HPW9W) 色:ホワイト(SC) ■ 三面鏡:ミラタップ スミス W1500 ■ タミコーナー 化粧柱 単板貼り 塗装:クリエラスク近似色

内 部 建 具 表							
LIXIL		建具色：プレシャスホワイト		枠色：扉同色		※その他、下記特記による	
ラフィス		把手：スクエアL(シャインニッケル) 丁番 固定枠(156) 外付戸当り ガイドピン床色合せ 引戸のみ上吊Wソフトモーション					
階	No	室名	形式	枠外W サイズ	デザイン	枠色	特記事項
				枠外H サイズ	建具色	把手	
1	1	脱衣ランドリー	片引き戸	—	RAA	—	明かり窓・表示錠
	WD			2400		—	
	2	WIC	アウtセッt片引	—	RAA	—	
	WD			2400		—	
	3	WC①	片引き戸	—	RAA	—	明かり窓・表示錠
	WD			2400		—	
	4	LDK	アウtセッt片引	—	RAA	—	
	WD			2400		—	
	5	LDK	片開き戸	—	RZA	—	ガラス:クリア
	WD			2400		—	
6	CL①	折れ戸	—	RAA	—	埋込下枠レール	
WD			2400		—		
1	7	洋室①	片開き戸	—	RAA	—	
	WD			2400		—	
	8	洋室②	片開き戸	—	RAA	—	
	WD			2400		—	
	9	洋室③	片引き戸	—	RAA	—	
	WD			2400		—	

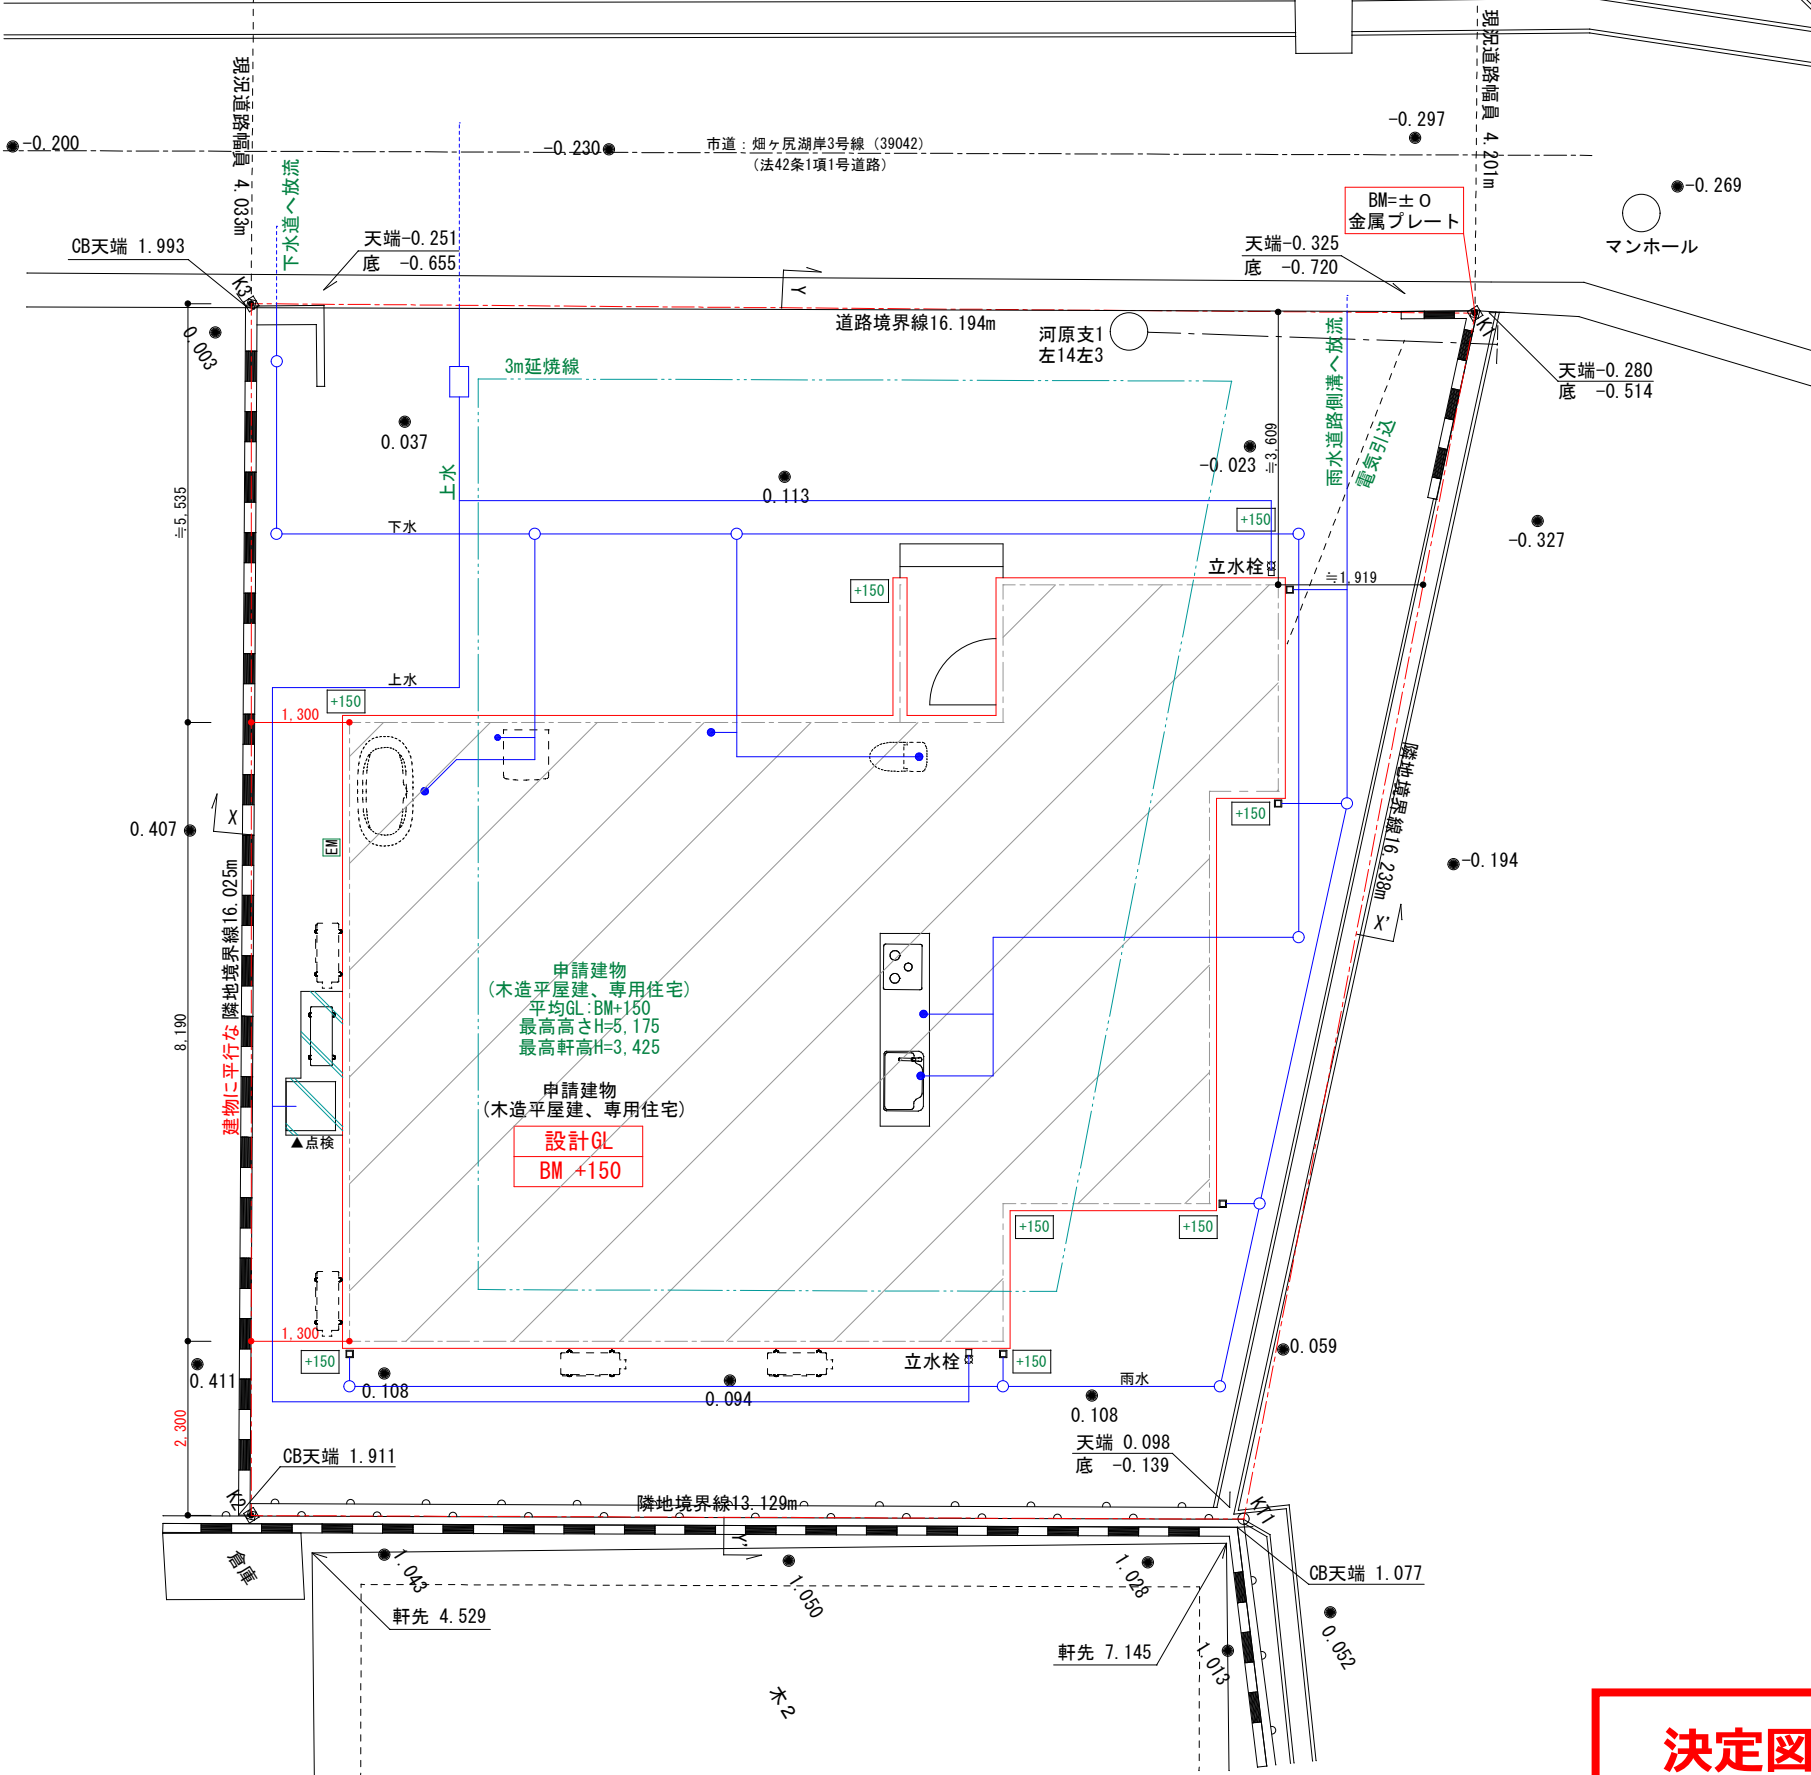


盛土規制法による切土盛土無し
道路斜線制限については、明らかに適合する。
北側斜線制限については、明らかに適合する。
平均地盤面について
申請建物の周囲の平均地盤面高さをBM+150とする。

トータル面積表 (㎡)	
敷地面積	234.51
建築面積	98.12
床面積 1階	95.64
延床面積	95.64
建蔽率	$(98.12/234.51) \times 100$ 41.85%
容積率	$(95.64/234.51) \times 100$ 40.79%

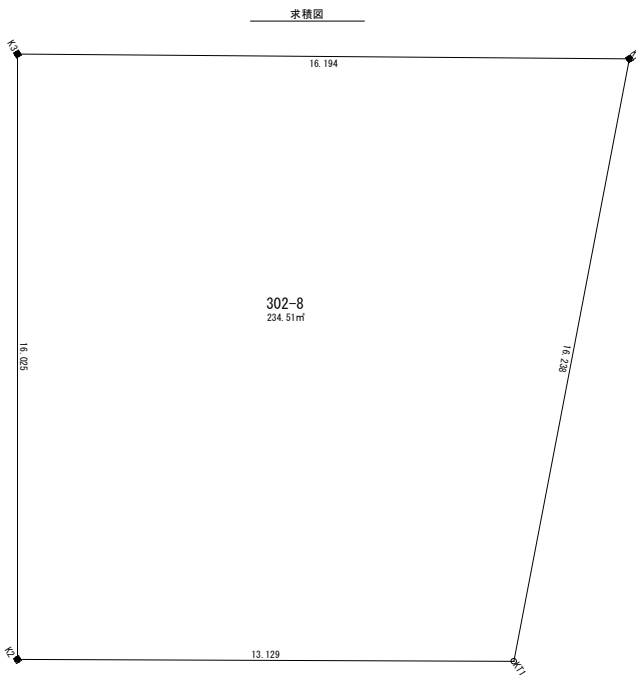


求積表				
地番	302-8			
N O	X _n	Y _n	Y _{n+1} - Y _{n-1}	X _n * (Y _{n+1} - Y _{n-1})
K1	5.958	4.298	20.572	122.567976
KT1	-5.017	16.266	5.039	-25.280663
K2	-16.169	9.337	-20.572	332.628668
K3	-7.762	-4.306	-5.039	39.112718
合計				469.028699
合計面積				234.5143495
地積				234.51 ㎡

決定図

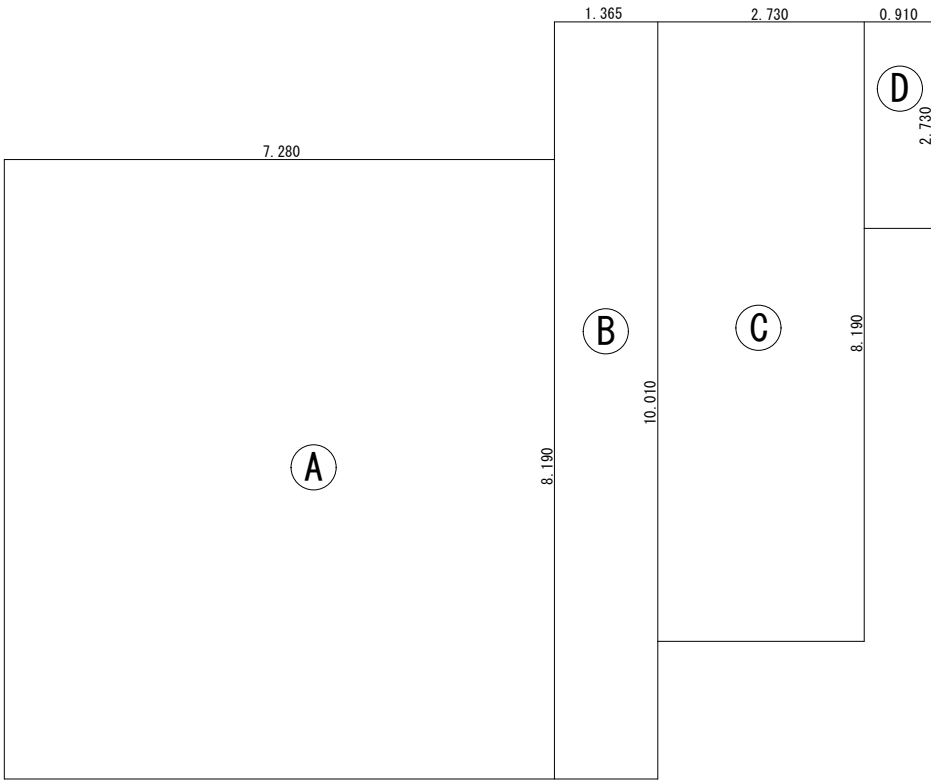

建築面積求積図 S=1/100

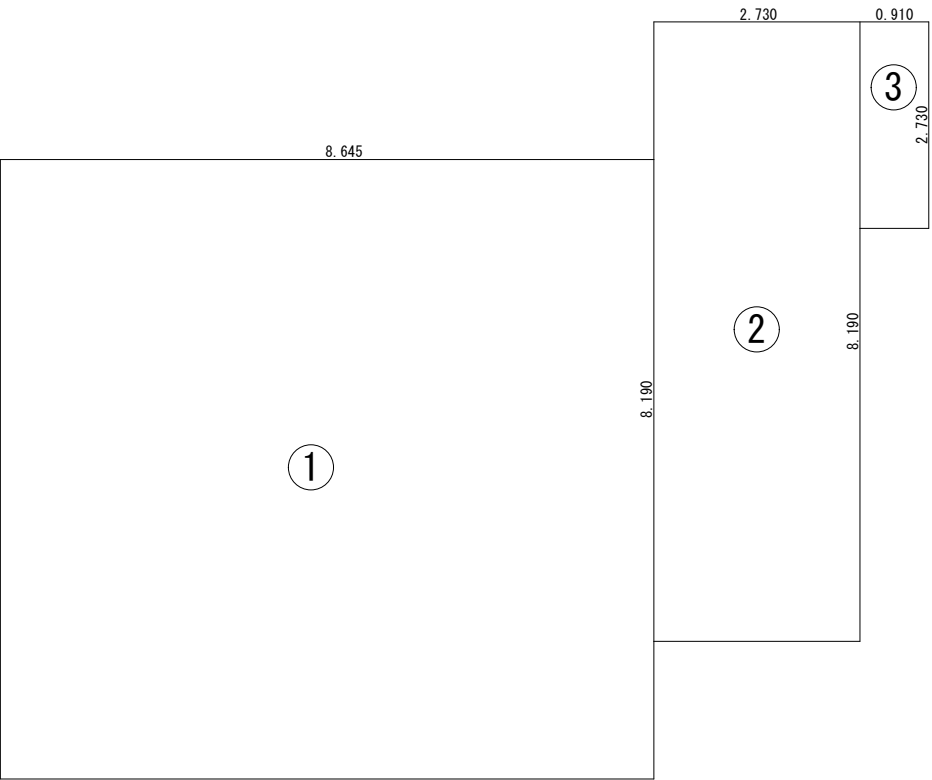

1階床面積図 S=1/100

建築面積求積表

番号	計算式	(m)	面積 (㎡)
Ⓐ	7.280 × 8.190		59.6232
Ⓑ	1.365 × 10.010		13.6637
Ⓒ	2.730 × 8.190		22.3587
Ⓓ	0.910 × 2.730		2.4843
合計			98.1299
			98.12

(29.6坪)

1階床面積求積表

番号	計算式	(m)	面積 (㎡)
①	8.645 × 8.190		70.8026
②	2.730 × 8.190		22.3587
③	0.910 × 2.730		2.4843
合計			95.6456
			95.64

(28.9坪)

延べ床面積表


	番号	(m)	面積 (㎡)
1階床面積	① ② ③		95.64
2階床面積			
合計			95.64

(28.9坪)

決定図

1/100

求積図

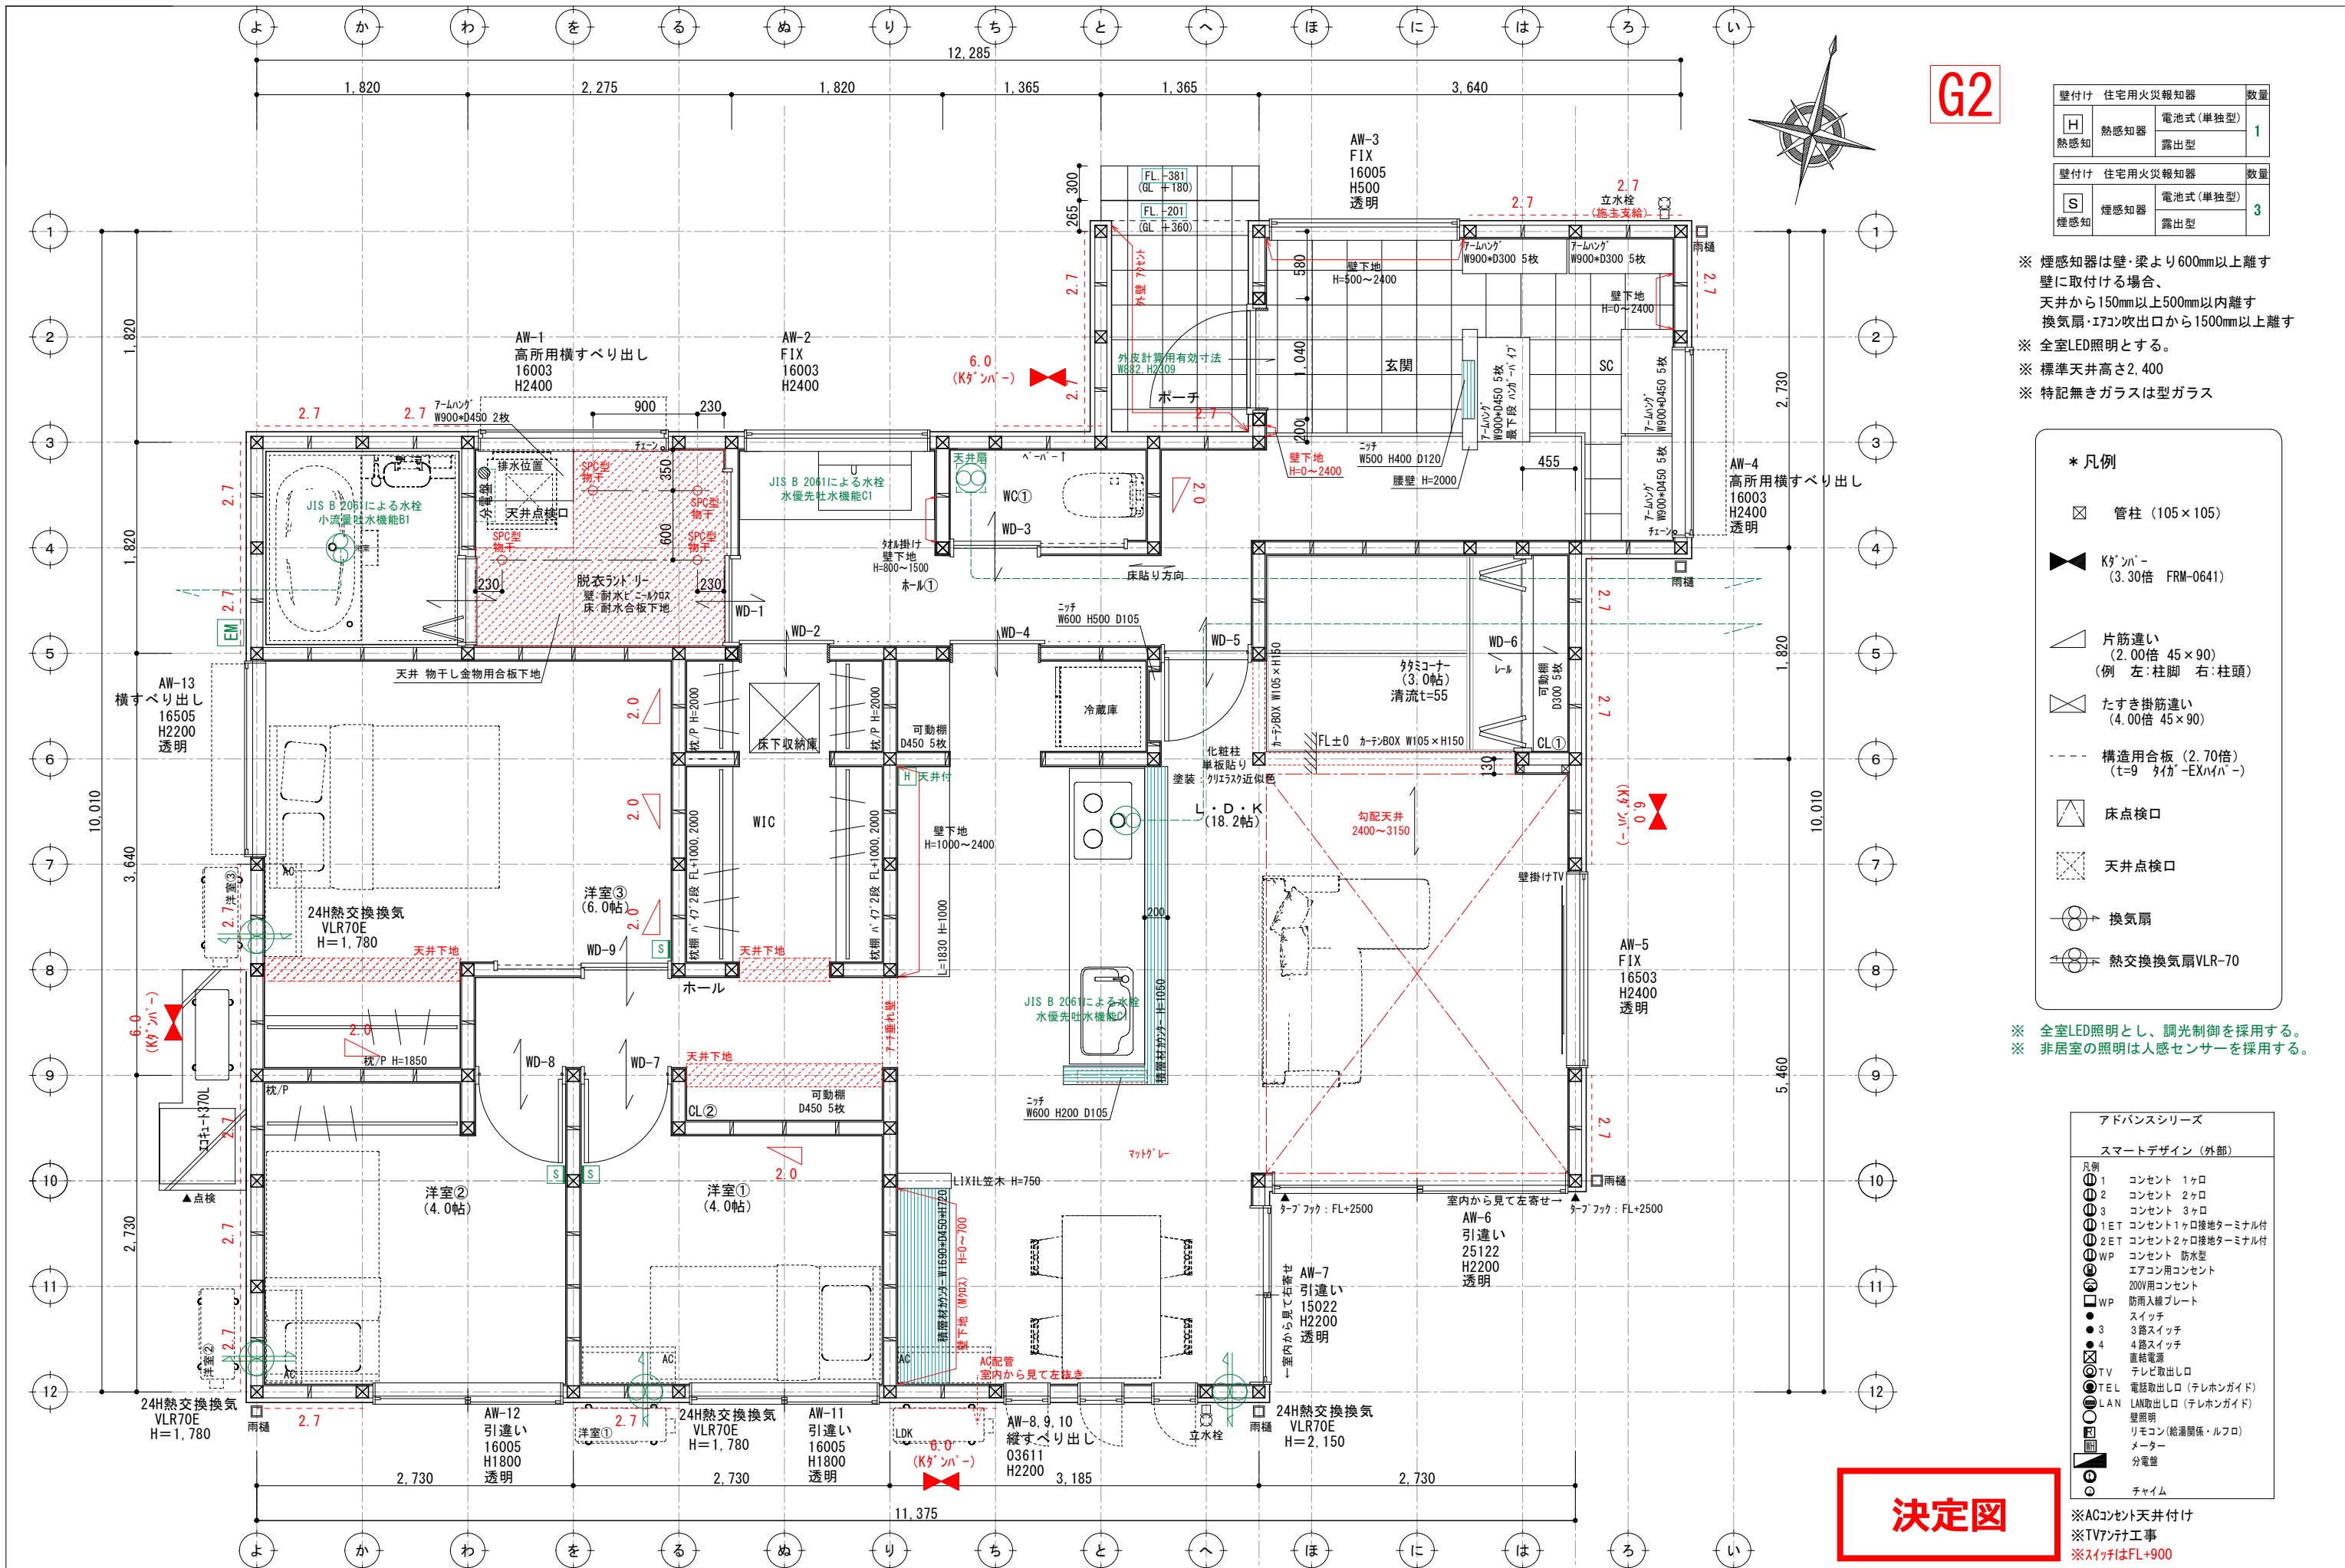

G2

壁付け 住宅用火災報知器		数量
H	熱感知器	電池式(単独型)
	熱感知器	露出型
1		
壁付け 住宅用火災報知器		数量
S	煙感知器	電池式(単独型)
	煙感知器	露出型
3		

※ 煙感知器は壁・梁より600mm以上離す
壁に取付ける場合、
天井から150mm以上500mm以内離す
換気扇・エアコン吹出口から1500mm以上離す
※ 全室LED照明とする。
※ 標準天井高さ2,400
※ 特記無きガラスは型ガラス

* 凡例


- 管柱 (105×105)
- K's'n'p' (3.30倍 FRM-0641)
- 片筋違い (2.00倍 45×90)
(例 左:柱脚 右:柱頭)
- たすき掛筋違い (4.00倍 45×90)
- 構造用合板 (2.70倍)
(t=9 9'4'6"-EX'n'n-)
- 床点検口
- 天井点検口
- 換気扇
- 熱交換換気扇VLR-70

※ 全室LED照明とし、調光制御を採用する。
※ 非居室の照明は人感センサーを採用する。



アドバンスシリーズ	
スマートデザイン (外部)	
凡例	
1	コンセント 1ヶ所
2	コンセント 2ヶ所
3	コンセント 3ヶ所
1ET	コンセント1ヶ所接地ターミナル付
2ET	コンセント2ヶ所接地ターミナル付
WP	コンセント 防水型
WP	エアコン用コンセント
WP	200V用コンセント
WP	防雨入線プレート
WP	スイッチ
3	3路スイッチ
4	4路スイッチ
直結電源	直結電源
TV	テレビ取出口
TEL	電話取出口 (テレビガイド)
LAN	LAN取出口 (テレビガイド)
壁照明	壁照明
リモコン	リモコン (給湯関係・ルフロ)
メーター	メーター
分電盤	分電盤
チャイム	チャイム


※ACコンセント天井付け
※TVアンテナ工事
※スイッチはFL+900

決定図

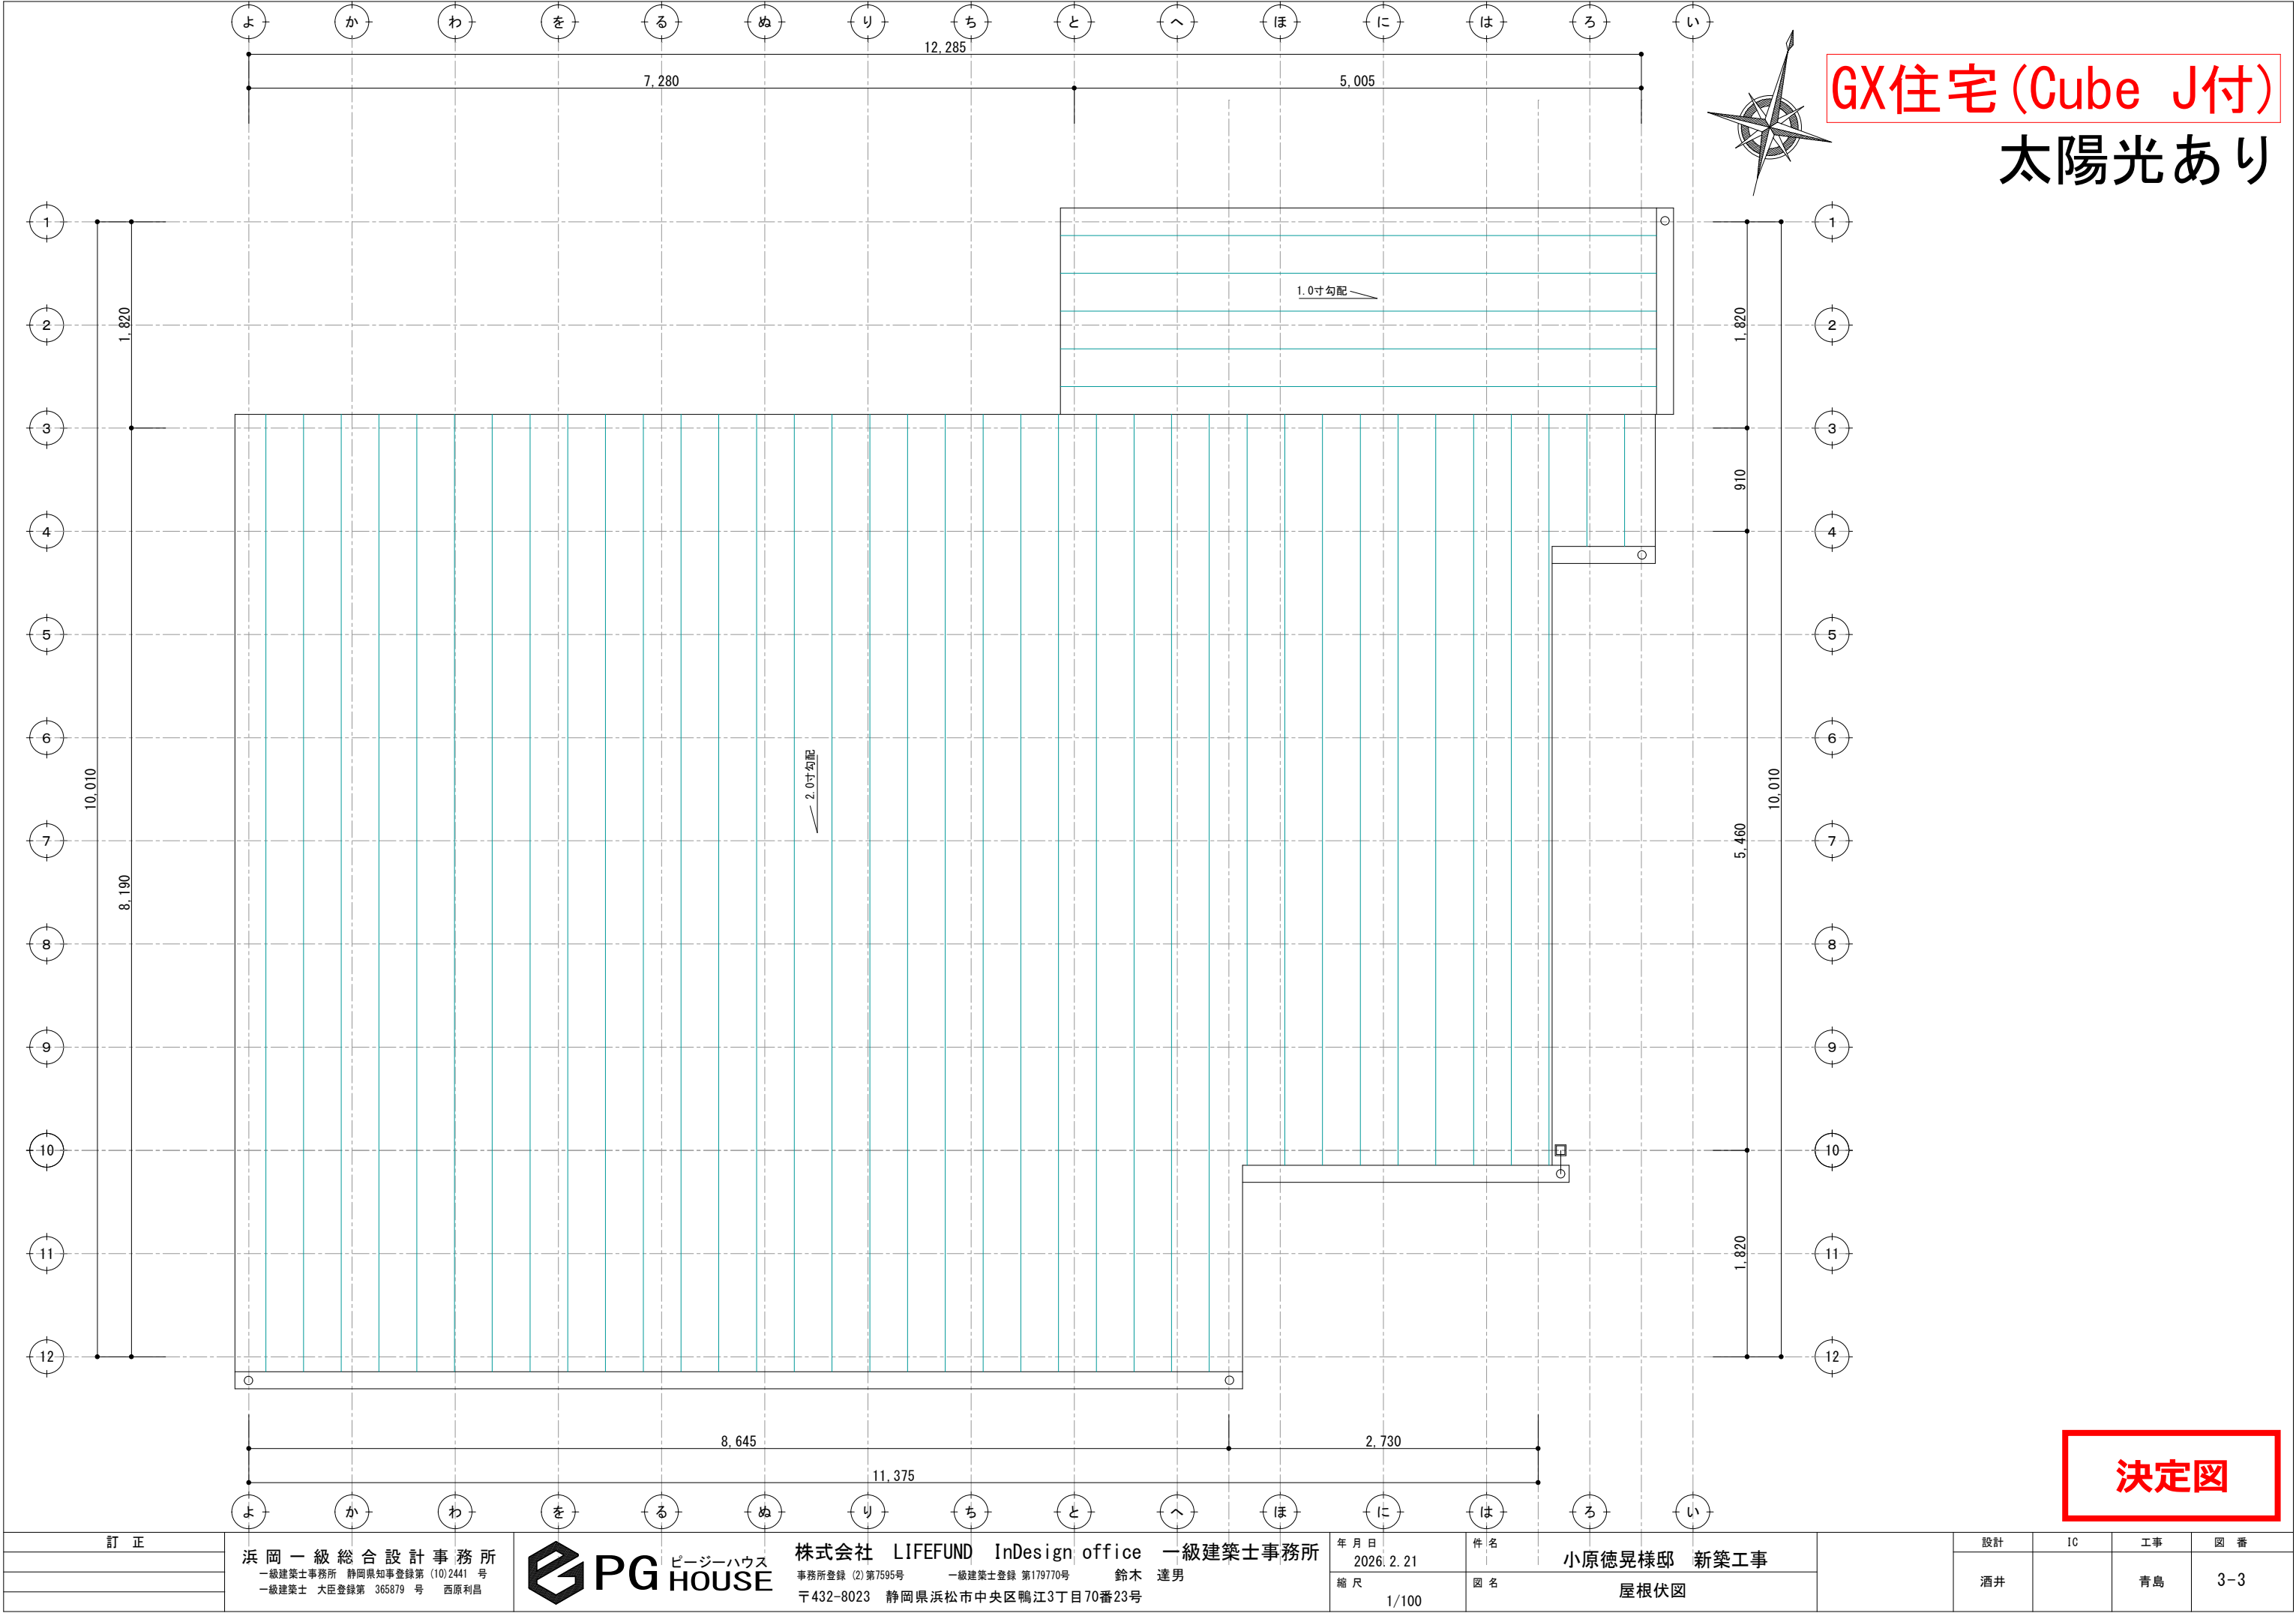




訂 正	浜 岡 一 級 総 合 設 計 事 務 所 一級建築士事務所 静岡県知事登録第 (10)2441 号 一級建築士 大臣登録第 365879 号 西原利昌		株式会社 LIFEFUND InDesign office 一級建築士事務所 事務所登録 (2) 第7595号 一級建築士登録 第179770号 鈴木 達男 〒432-8023 静岡県浜松市中央区鴨江3丁目70番23号	年月日	件 名	設計	IC	工事	図 番
				2026. 2. 21	小原徳晃様邸 新築工事				
				縮 尺	図 名				
				1/100	屋根伏図	酒井		青島	3-3

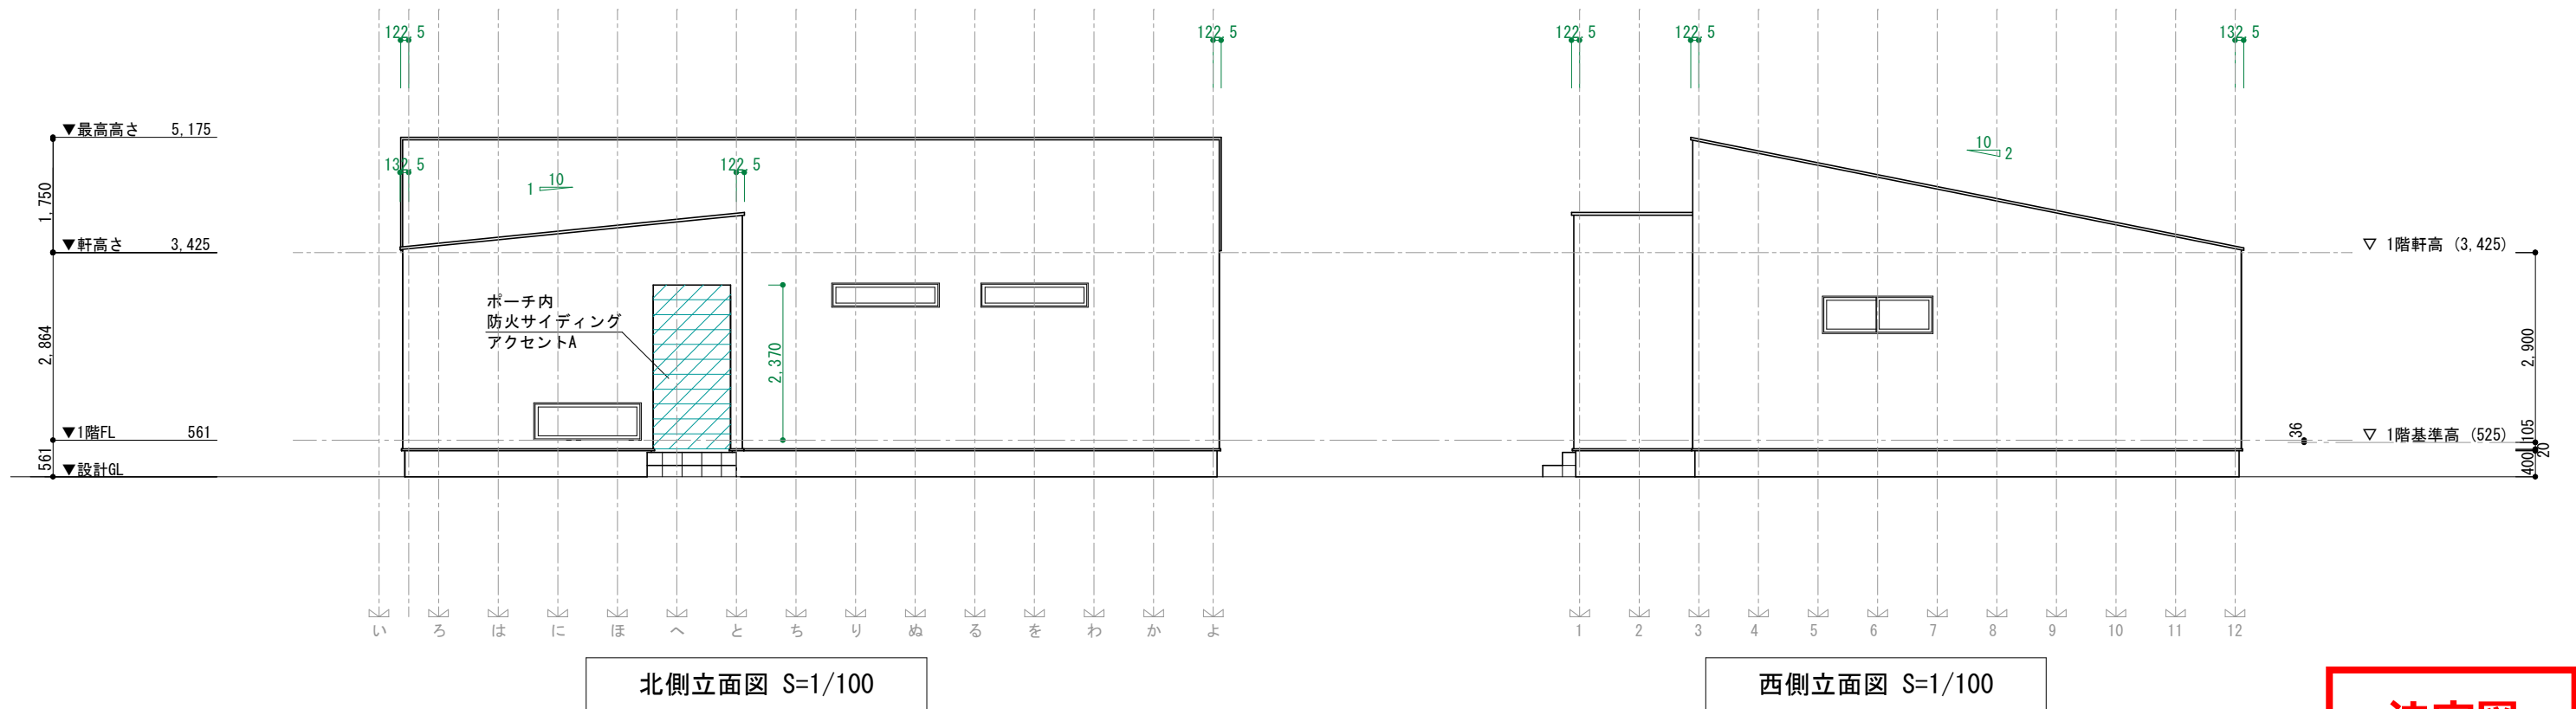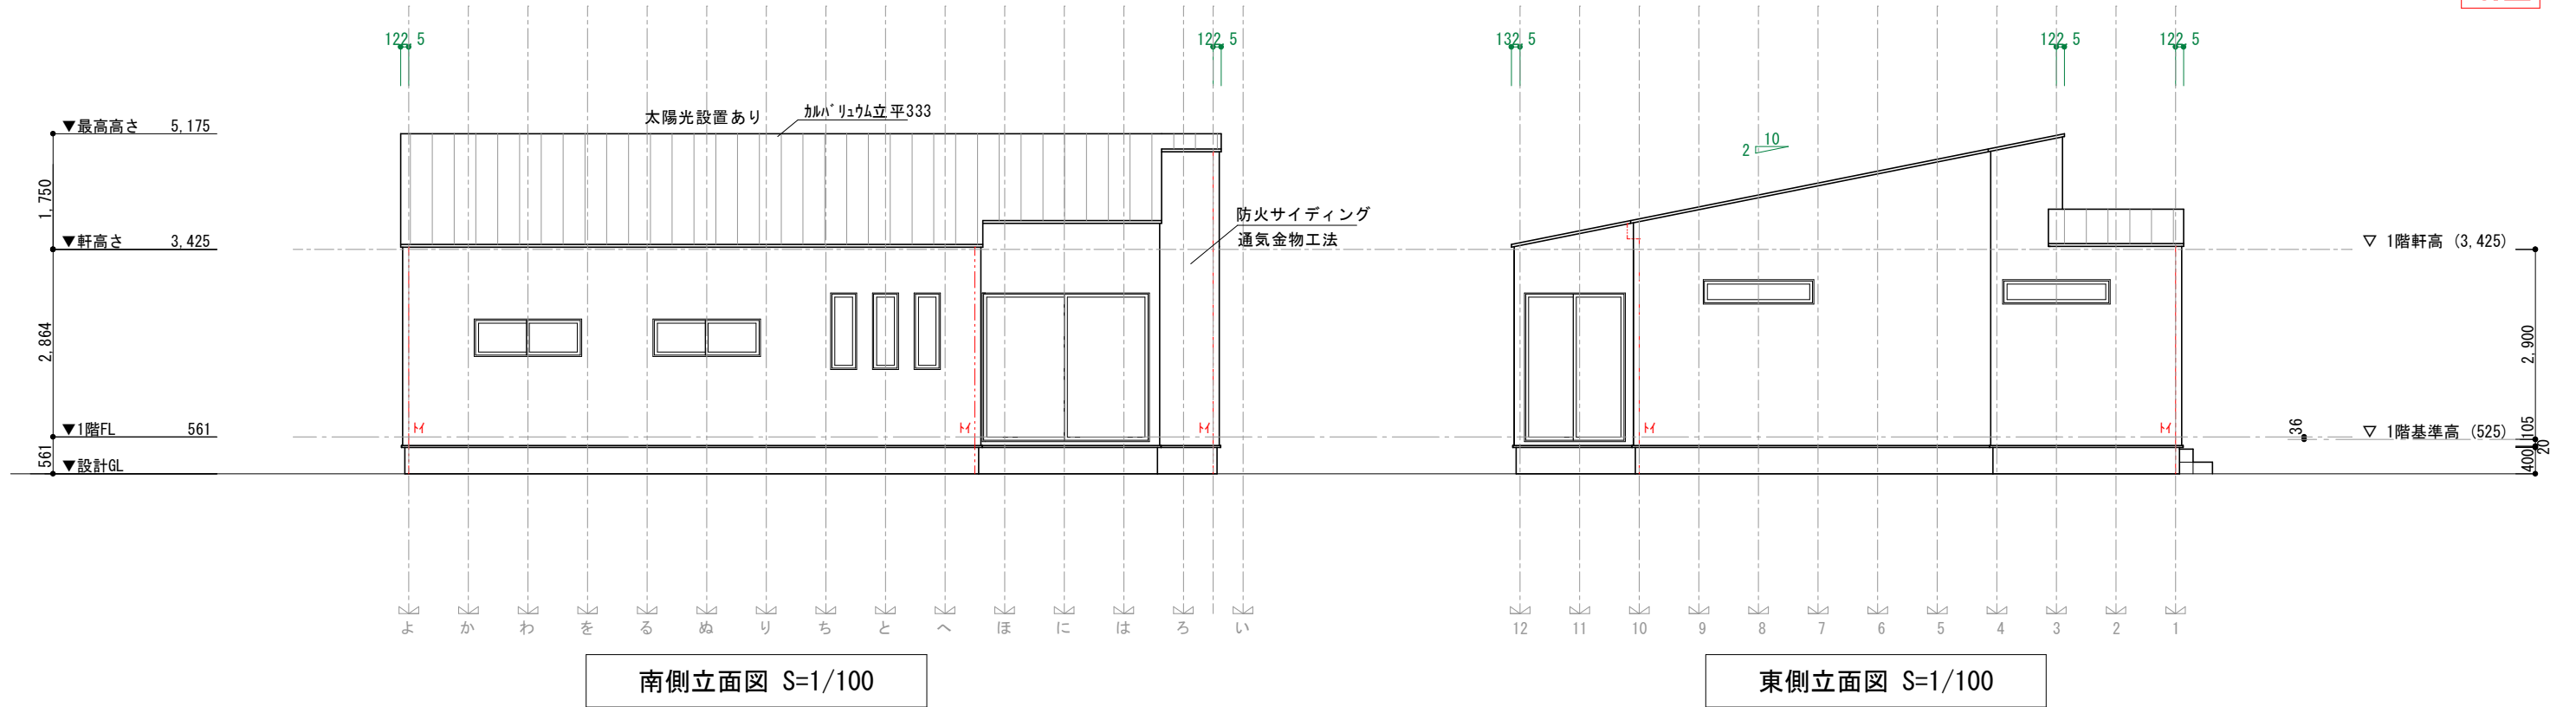

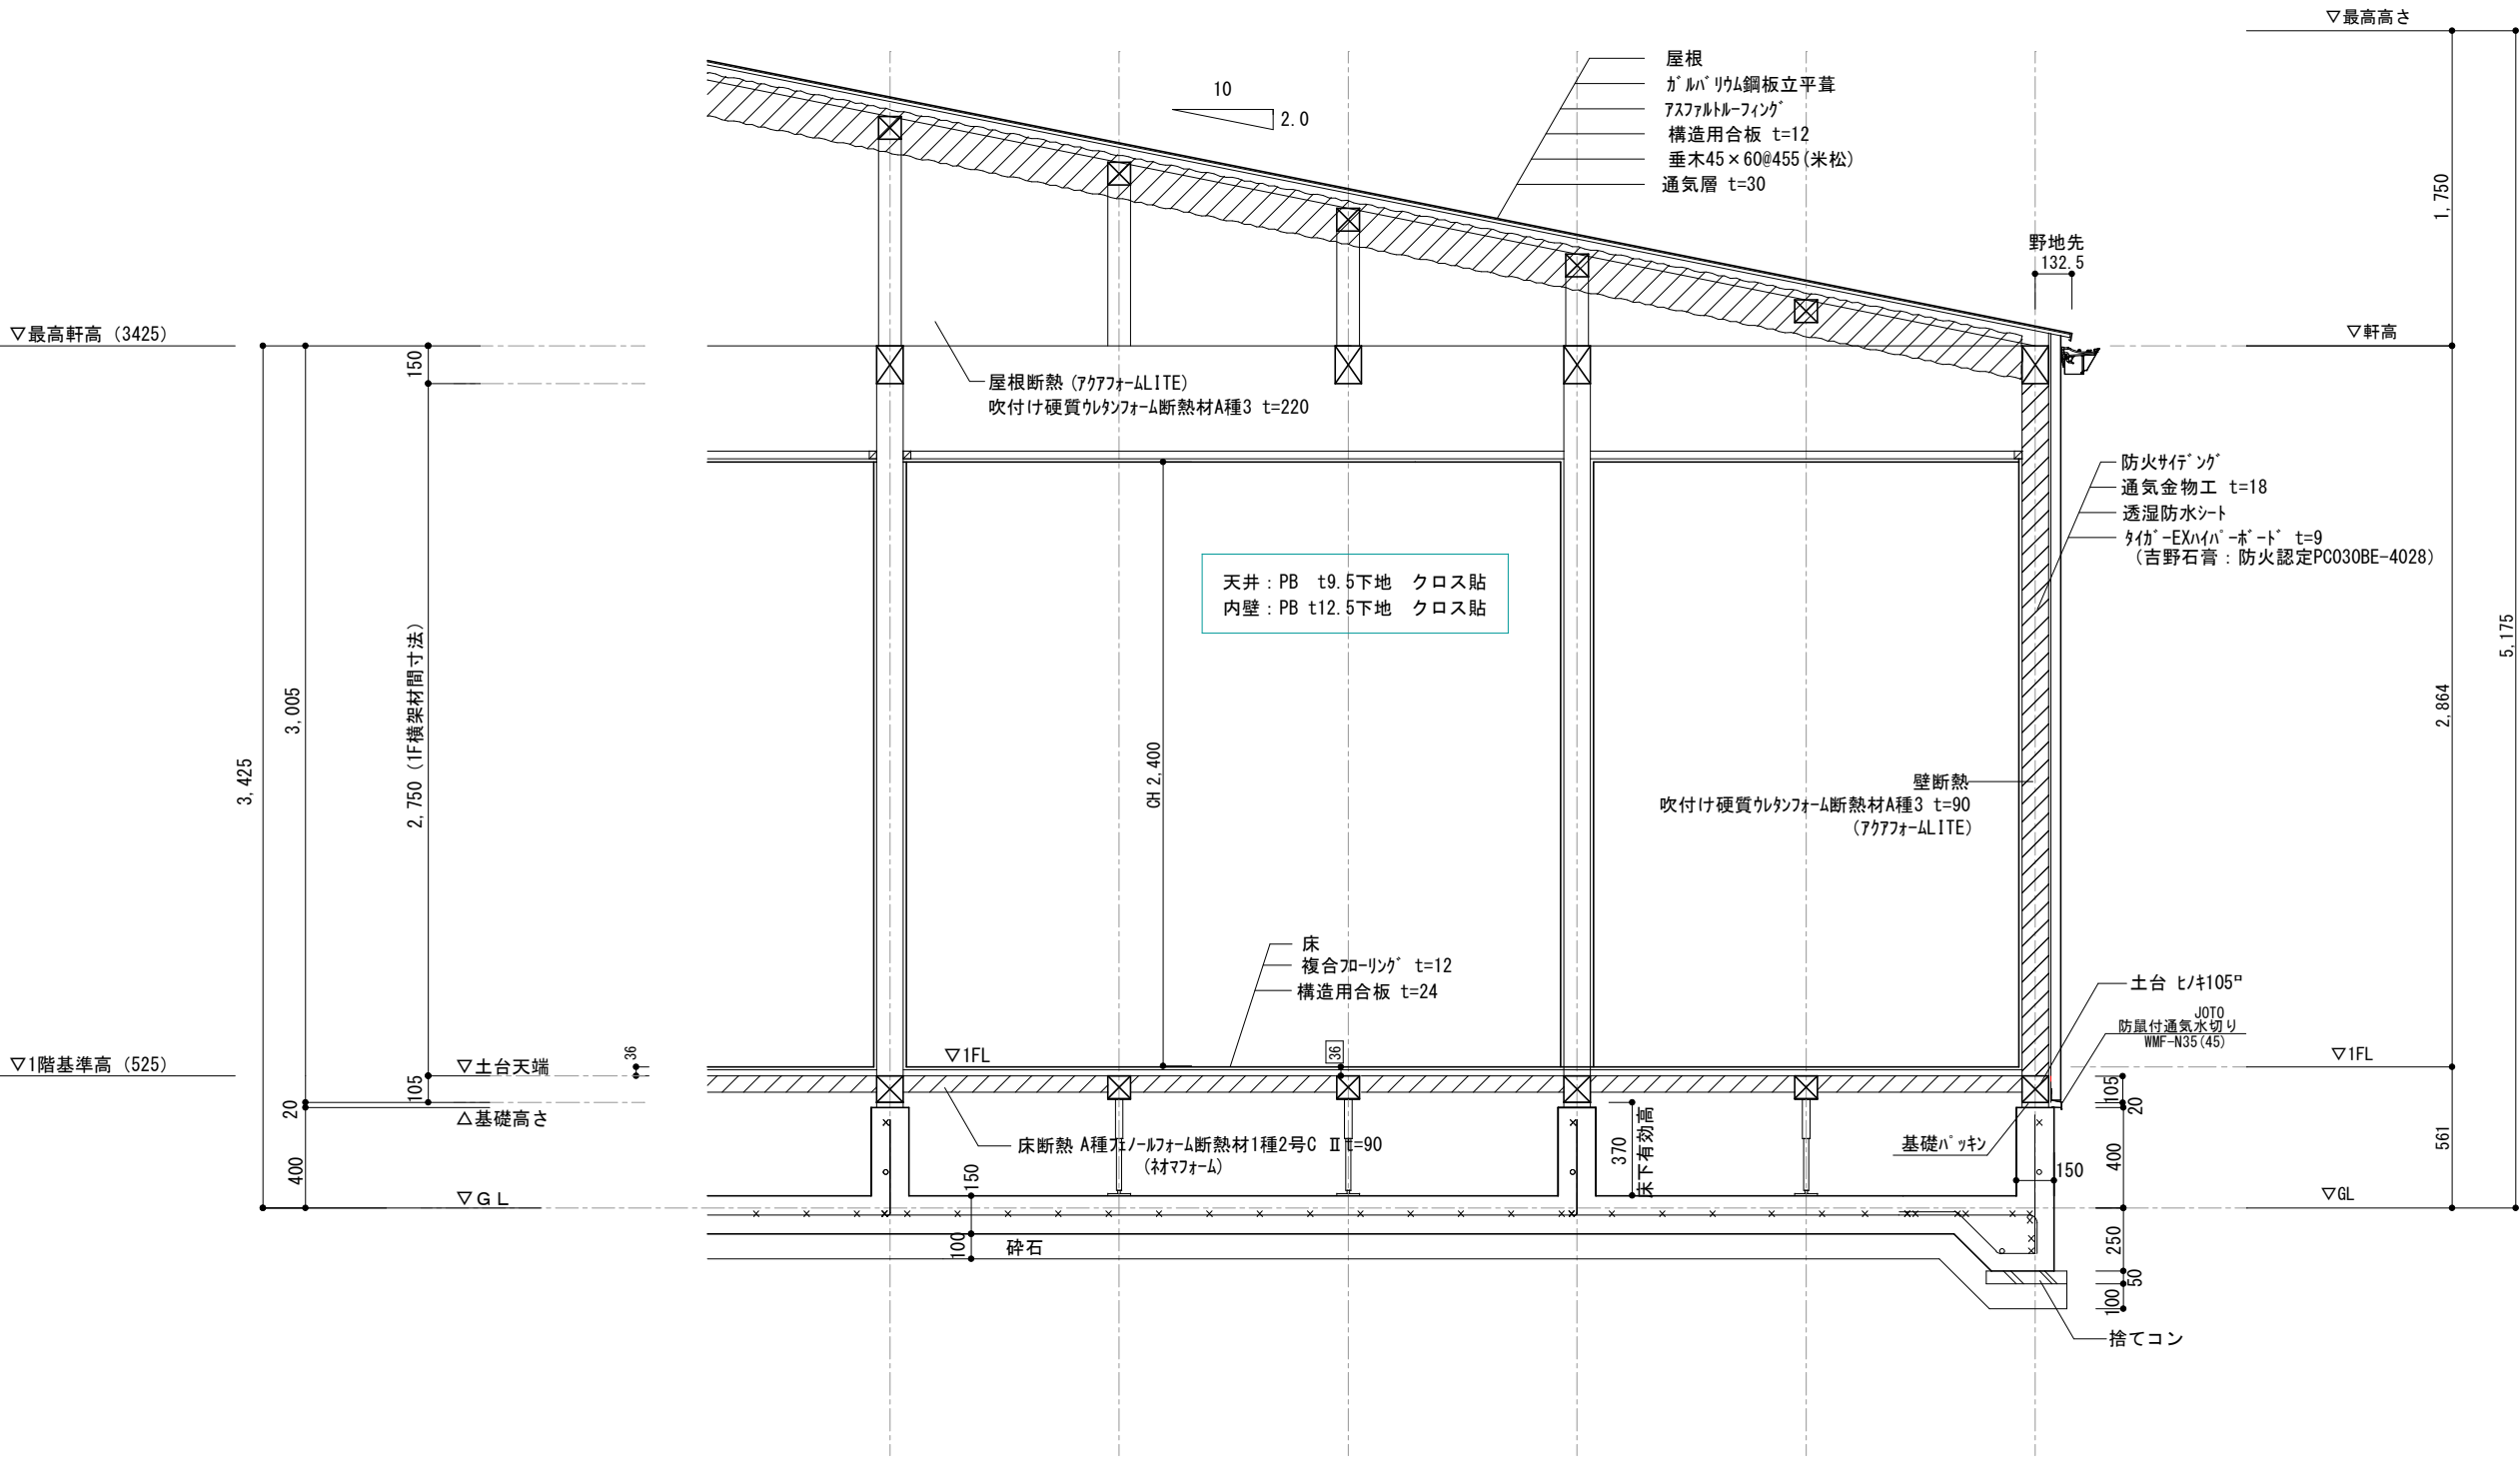


決定図

訂 正	浜 岡 一 級 総 合 設 計 事 務 所 一級建築士事務所 静岡県知事登録第 (10)2441 号 一級建築士 大臣登録第 365879 号 西原利昌		株式会社 LIFEFUND InDesign office 一級建築士事務所 事務所登録 (2) 第7595号 一級建築士登録 第179770号 鈴木 達男 〒432-8023 静岡県浜松市中央区鴨江3丁目70番23号	年 月 日	件 名		設計	IC	工事	図 番
				2026. 2. 21	小原徳晃様 邸新築工事					
				縮 尺	図 名					
				1/30	矩計図		酒井		青島	5

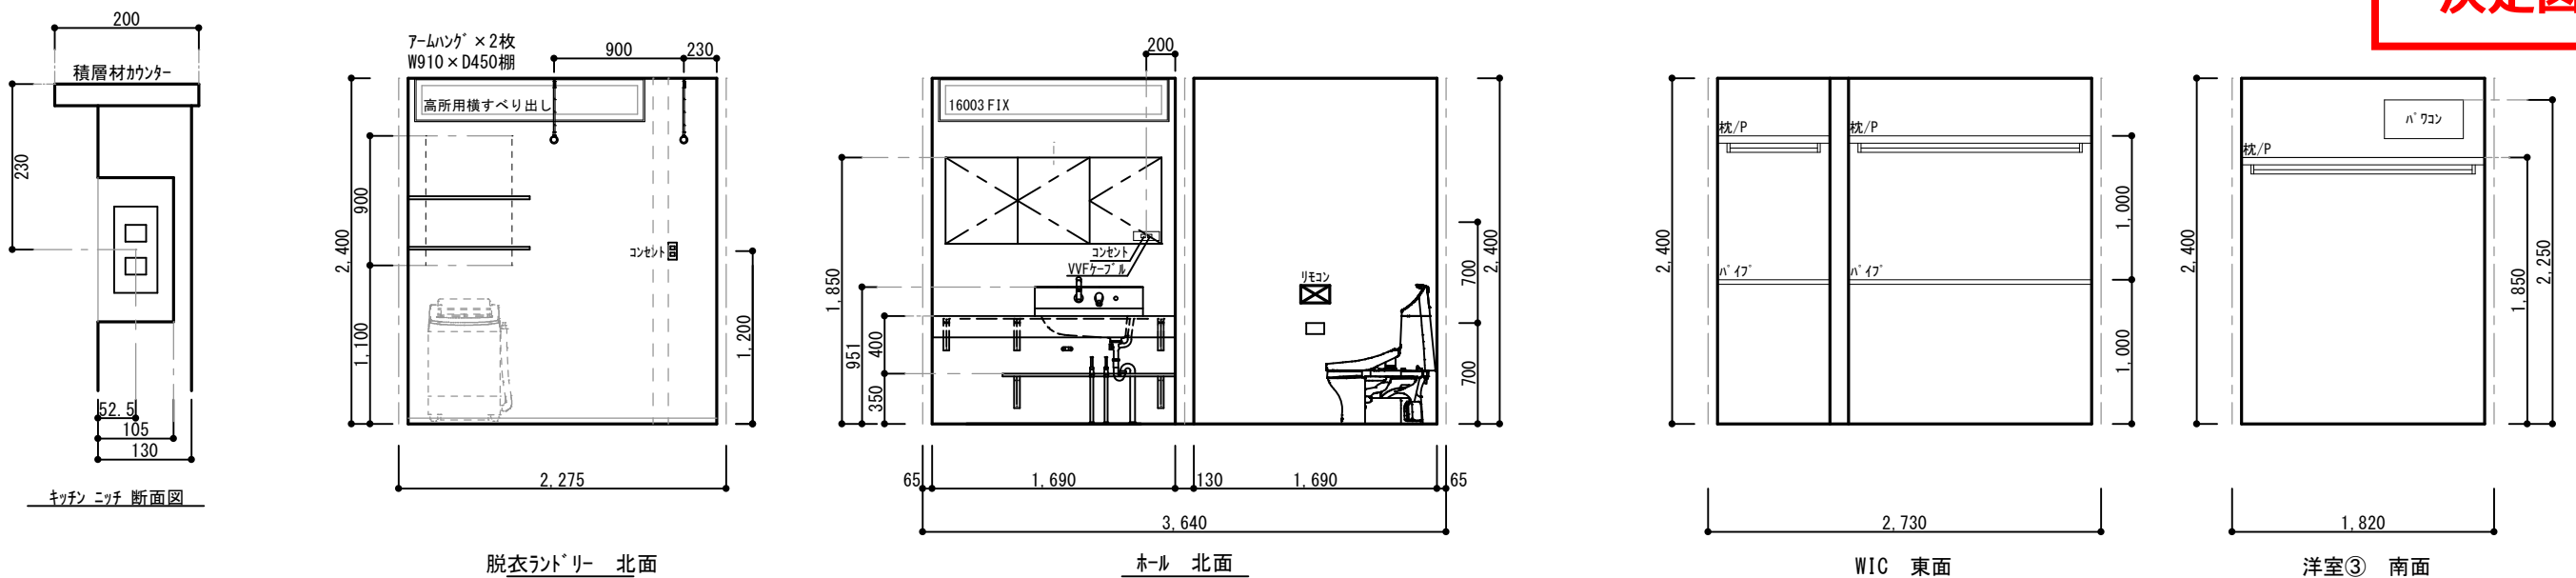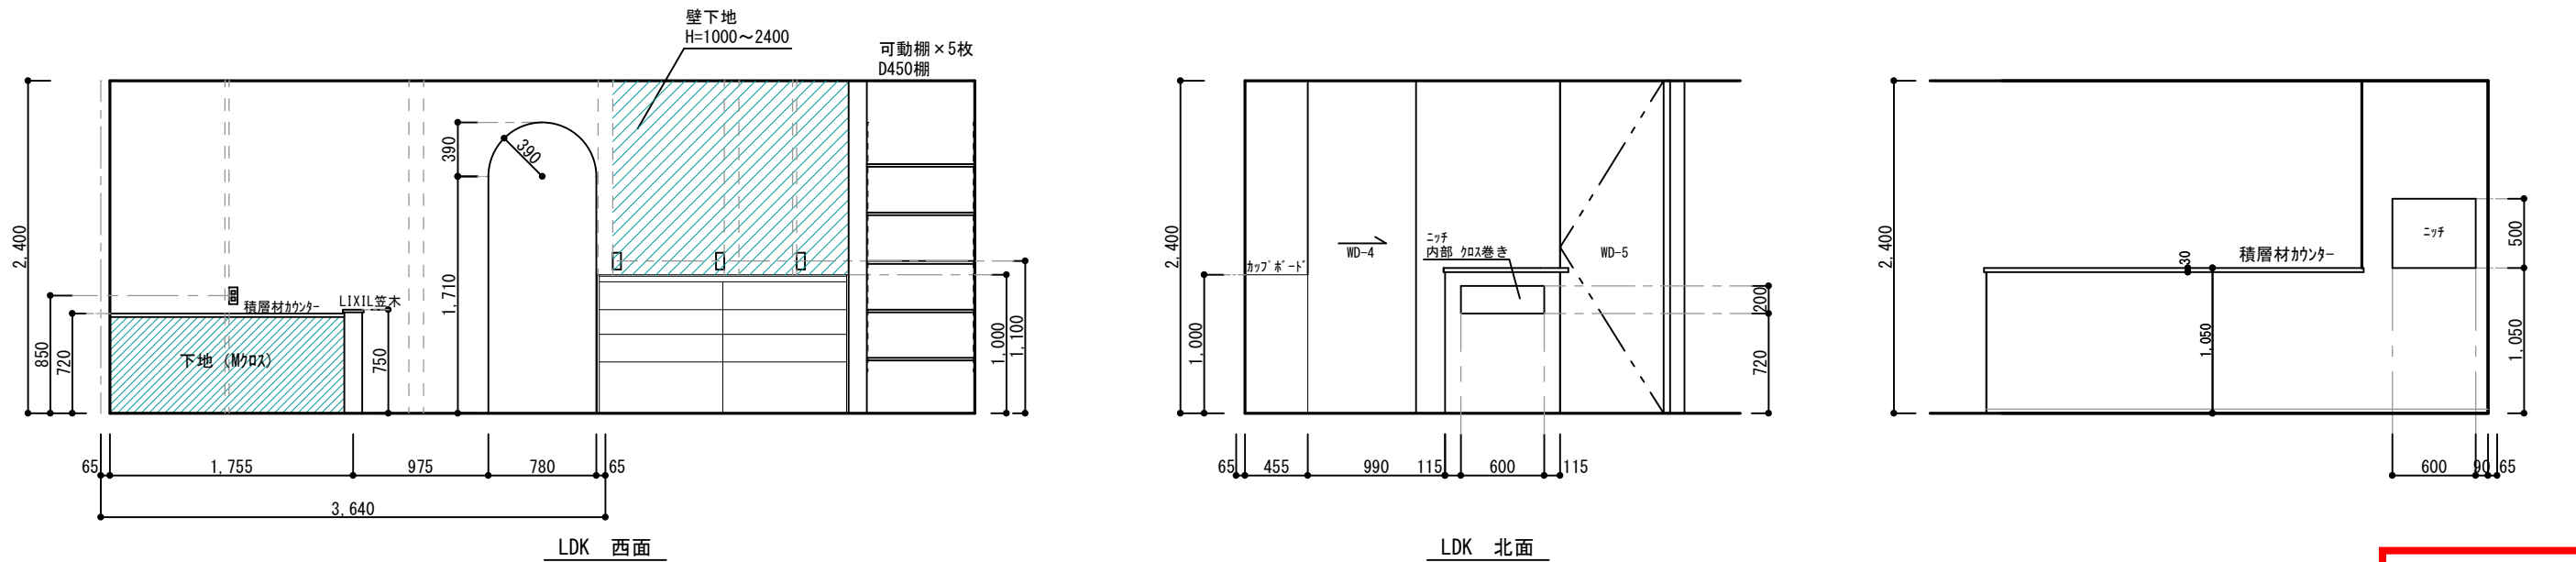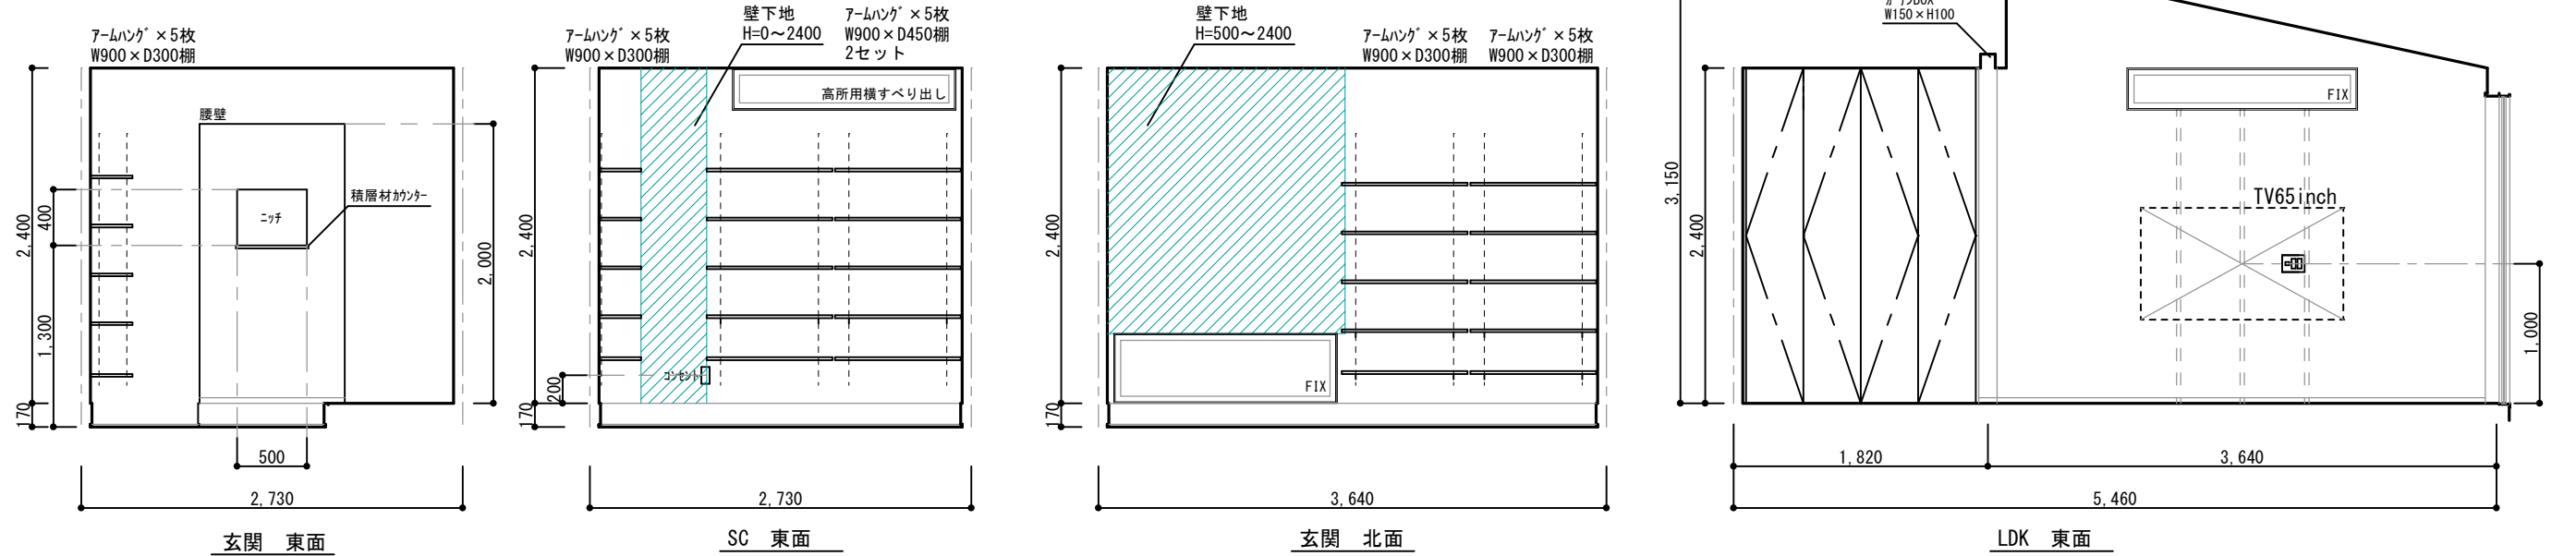

決定図

訂正	浜岡一級総合設計事務所 一級建築士事務所 静岡県知事登録第 (10)2441 号 一級建築士 大田登録第 365879 号 西原利昌	LIFEFUND PG HOUSE	株式会社 LIFEFUND InDesign office 一級建築士事務所 事務所登録 (2) 第7595号 一級建築士登録 第179770号 鈴木 達男 〒432-8023 静岡県浜松市中央区鴨江3丁目70番23号	年月日 2026.2.21	件名 小原徳晃様 邸新築工事	図名 展開図-1	設計 酒井	IC 青島	工事 青島	図番 6-1
				縮尺 1/50						

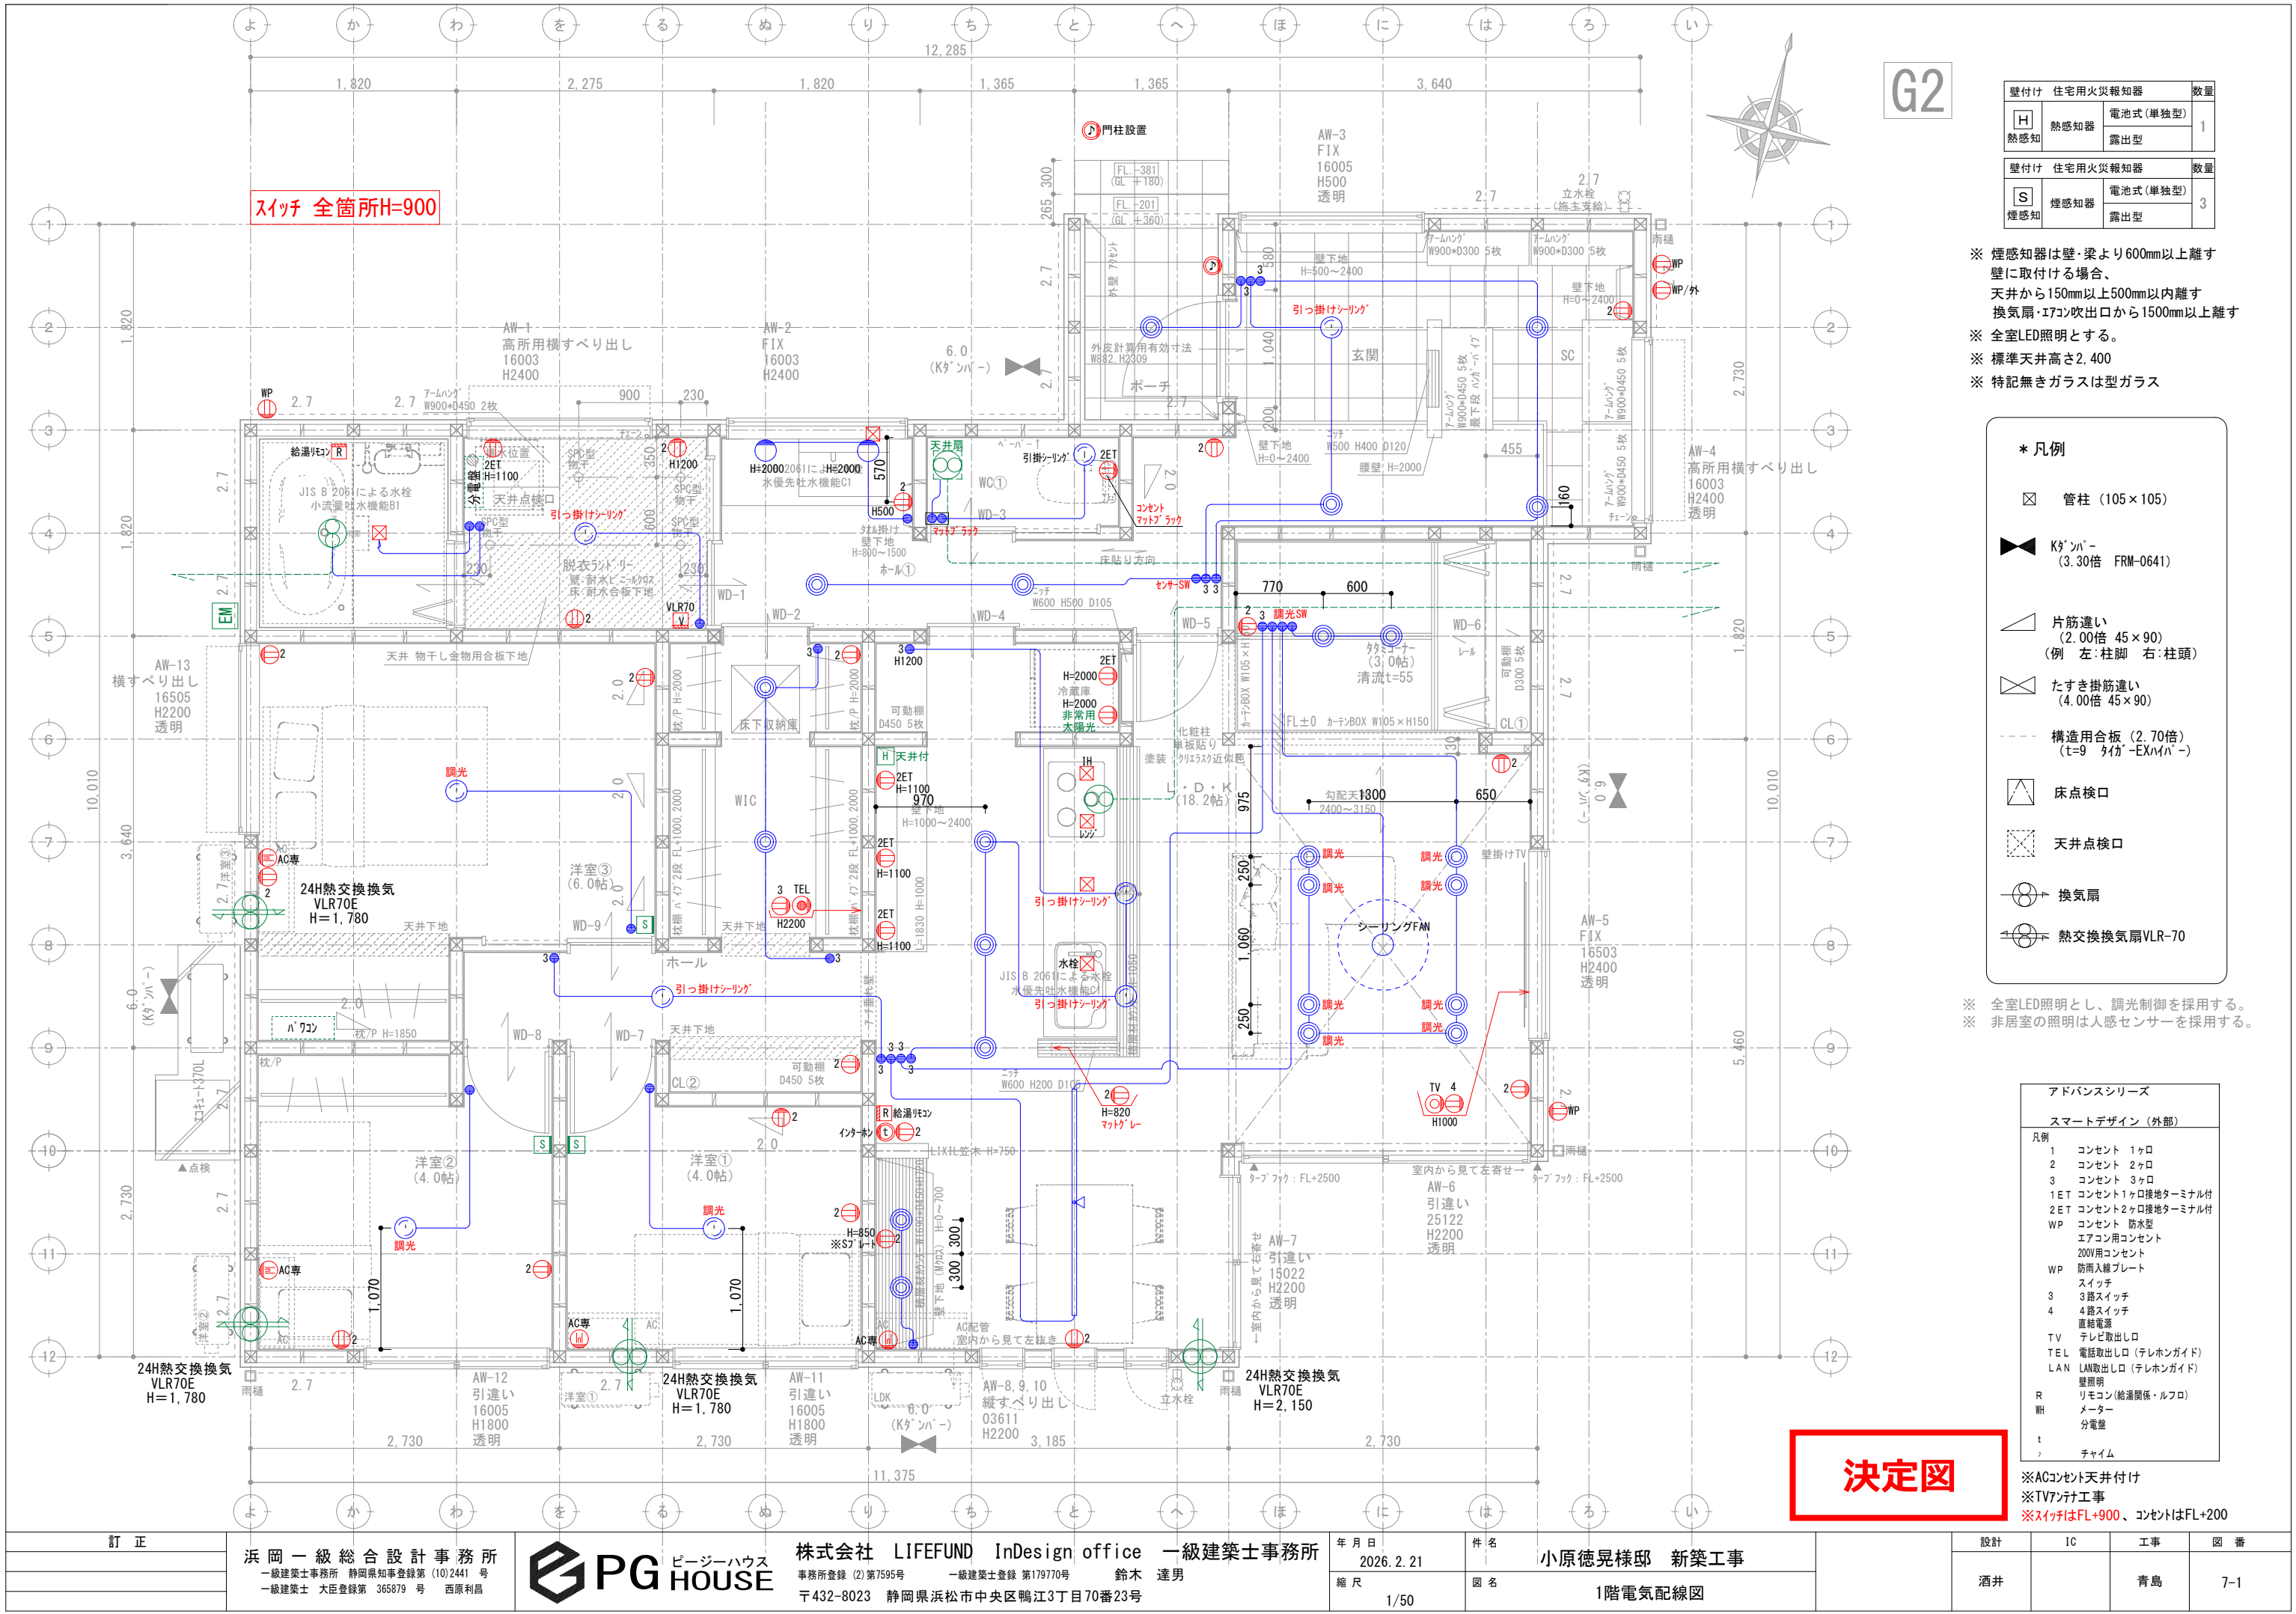

G2

壁付け 住宅用火災報知器			数量
H	熱感知器	電池式(単独型)	1
	熱感知	露出型	
壁付け 住宅用火災報知器			数量
S	煙感知器	電池式(単独型)	3
	煙感知	露出型	

- ※ 煙感知器は壁・梁より600mm以上離す
壁に取付ける場合、
天井から150mm以上500mm以内離す
換気扇・エアコン吹出口から1500mm以上離す
- ※ 全室LED照明とする。
- ※ 標準天井高さ2,400
- ※ 特記無きガラスは型ガラス

* 凡例


- 管柱 (105×105)
- K's'ンパ- (3.30倍 FRM-0641)
- 片筋違い (2.00倍 45×90)
(例 左:柱脚 右:柱頭)
- たすき掛筋違い (4.00倍 45×90)
- 構造用合板 (2.70倍)
(t=9 9'付 -EX'n' -)
- 床点検口
- 天井点検口
- 換気扇
- 熱交換換気扇VLR-70

- ※ 全室LED照明とし、調光制御を採用する。
- ※ 非居室の照明は人感センサーを採用する。

アドバンスシリーズ	
スマートデザイン (外部)	
凡例	
1	コンセント 1ヶ所
2	コンセント 2ヶ所
3	コンセント 3ヶ所
1ET	コンセント1ヶ所接地ターミナル付
2ET	コンセント2ヶ所接地ターミナル付
WP	コンセント 防水型
	エアコン用コンセント
WP	200V用コンセント
WP	防雨入線プレート
スイッチ	
3	3路スイッチ
4	4路スイッチ
	直結電源
TV	テレビ取出口
TEL	電話取出口 (テレホンガイド)
LAN	LAN取出口 (テレホンガイド)
	壁照明
R	リモコン(給湯関係・ルフロ)
WH	メーター
t	分電盤
	チャイム

- ※ACコンセント天井付け
- ※TVアンテナ工事
- ※スイッチはFL+900、コンセントはFL+200

決定図

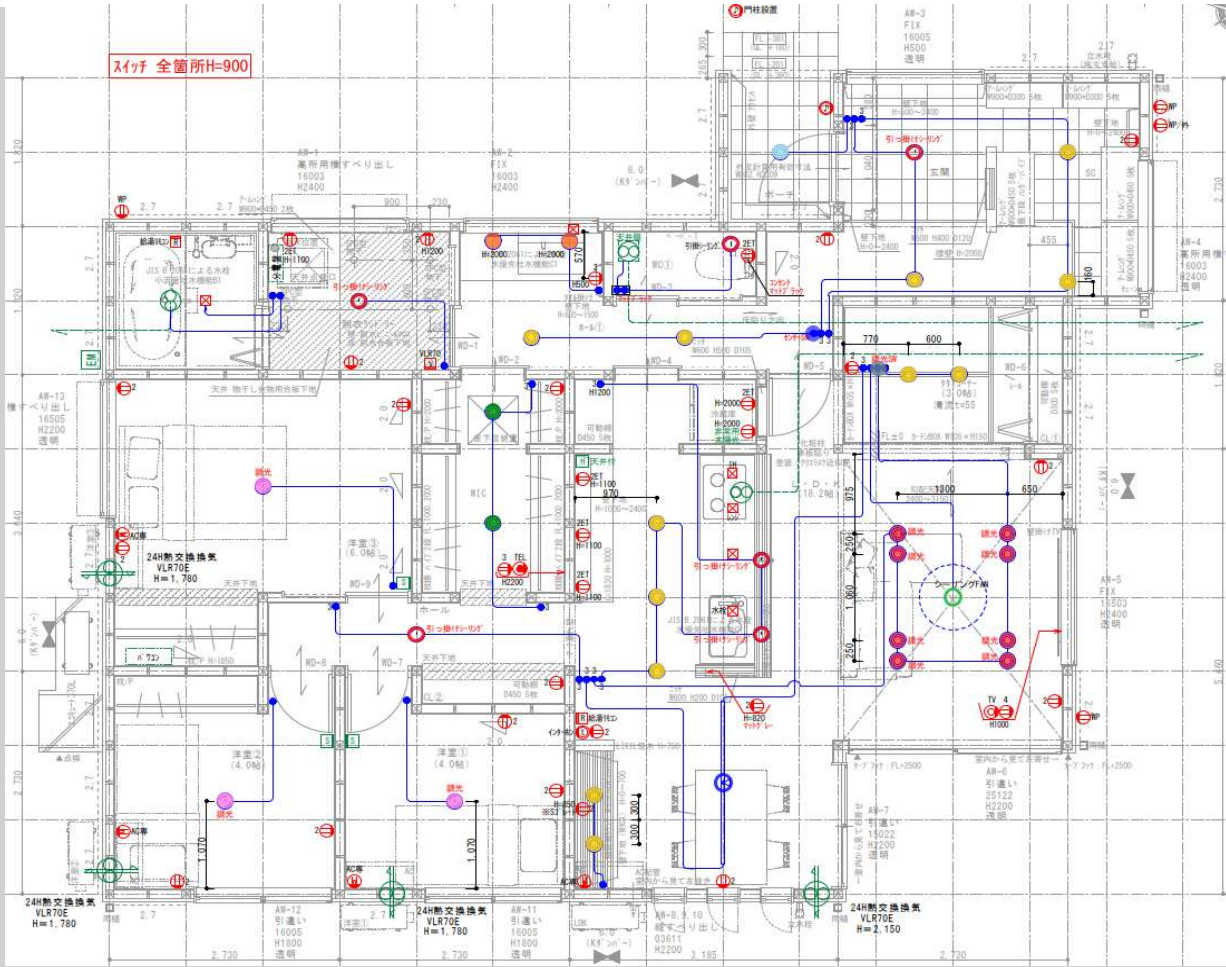

1階

ドアホン：VL-SE31XL(Panasonic)



内部SW：アドバンス

マットホワイト/マットブラック/マットグレー



外部：スマートデザインシリーズ
ブラック



エコユートリモコン



LDK

○ ×1

シーリングファン

24時間換気 VLR-70



LDK

○ ×1

ダクトレール

DP_00292K



ダクトレール2m用
DP-00292 K
¥10,800(税抜)
●アルミ型材 黒アルマイト
●巾33 ダクト長2000 全長2103 高19mm
●2P 15A 125V
●フィードインボックス・エンドキャップ1個付

施主
支給品

ポーチ灯

○ ×1

センサー付きダクトレール

DDL_6259YB

基本照明ダクトレール

○ ×20

DDL_6132YW

脱衣ランドリ、WC①、玄関、キッチン

○ ×6

引っ掛けシーリング

洋室①②③

○ ×3

シーリングライト

DCL_42121

LDK

● ×8

調光ダクトレール

DDL_6032YBG

WIC

○ ×2

センサー付きダクトレール

DDL_6259YW

ホール

○ ×2

ブラケット

DBK_41544Y

ホール

○ ×1

センサーSW

WTA_14119W

LDK

○ ×1

調光SW

WTA_57583WK



高気密SB形 | 人感センサー
運動マルチタイプ
DDL-6259 YB
電球色 / 2700K Ra93(クラス2)
415 lm 7.7 W 53.8 lm/W
¥21,800(税抜) (LED内蔵)
LED 7.7W 白熱灯60W相当
●銅板 黒塗装
●アルミダイカスト 黒塗装
●アクリル 乳白(マット)
●径φ116 埋込穴φ100
●埋込深75mm 0.5kg
●14VA
●点灯照度調節機能付(暗・明切)
●点灯保持時間(1分)
●調光器併用不可
【運動器具について】
LED調光タイプ60VAまで
LED非調光タイプ不可 電球色不可
白熱灯60Wまで



COBタイプ | 高気密SB形
DDL-6132 YW
電球色 / 2700K Ra93(クラス2)
440 lm 4.6 W 95.6 lm/W
¥3,600(税抜) (LED内蔵)
LED 4.6W 白熱灯60W相当
●銅板 白塗装
●アクリル 乳白(マット)
●径φ116 埋込穴φ100 埋込深70mm 0.3kg
●8VA
●拡散バネル付
●AC100V
●光束維持時間60,000時間
●取付可能天井厚5~25mm
●調光器併用不可



タイマー付リモコンブルレス | 調色調光タイプ
DCL-42121
電球色 / 6500K~電球色 / 2700K Ra93
LED 27.1W 3699 lm 27.1 W 136.4 lm/W
¥22,000(税抜) (LED内蔵)
●再生アクリル 乳白(マット)
●径φ110 埋込深138mm 1.4kg
●ブルレススイッチ付(全灯・半灯・点灯・常夜灯)
●点灯前の調色調光状態
●調色機能付(6500K~2700K) ●調光機能付(5%~100%)
●常夜灯6段階調光 ●AC100V ●光束維持時間40,000時間
●調光器併用不可 ●シーンコントローラーは使用できません
※定電圧電源、消費電力、固有エネルギー消費効率等は
屋白色での値です。



COBタイプ | 高気密SB形
DDL-6032 YBG
電球色 / 2700K Ra93(クラス2)
370 lm 5.8 W 63.7 lm/W
¥4,600(税抜) (LED内蔵)
LED 5.8W 白熱灯60W相当
●銅板 黒塗装
●アクリル 乳白(マット)
●径φ116 埋込穴φ100 埋込深71mm 0.3kg
●7VA
●拡散バネル付
●AC100V
●調光可能(1%~100%)
●調光にLED専用調光器(別売)をご使用ください。
●光束維持時間60,000時間
●取付可能天井厚5~25mm



高気密SB形 | 人感センサー
運動マルチタイプ
DDL-6259 YW
電球色 / 2700K Ra93(クラス2)
510 lm 7.7 W 66.2 lm/W
¥21,800(税抜) (LED内蔵)
LED 7.7W 白熱灯60W相当
●銅板 白塗装
●アルミダイカスト 白塗装
●アクリル 乳白(マット)
●径φ116 埋込穴φ100
●埋込深75mm 0.5kg
●14VA
●点灯照度調節機能付(暗・明切)
●点灯保持時間(1分)
●調光器併用不可
【運動器具について】
LED調光タイプ60VAまで
LED非調光タイプ不可 電球色不可
白熱灯60Wまで



高気密SB形 | 人感センサー
運動マルチタイプ
DBK-41544 Y
電球色 / 2700K・Ra83
定電圧 消費電力 固有エネルギー消費効率
119lm 4.6W 25.8lm/W
¥10,800-(税抜) (LED内蔵)
LED 4.6W 白熱灯60W相当
●銅板 白塗装
●径 120 出36mm 0.5kg
●8VA
●AC100V
●光束維持時間40,000時間
●調光器併用不可
【カバリー化標準式】



3線 / 4線式
WTA14119W
【壁取付】熱線センサ付自動スイッチ(親器)
(検知後連続動作時間 約10秒~30分可変形)
(明るさセンサー・手動スイッチ付)(マットホワイト)
3A 100V AC
プレート別売



WTA57583WK
希望小売価格 11,900円(税抜)
※掲載の価格には消費税は含まれていません。
【LED埋込逆位相調光スイッチC(ほたるスイッチC)】
(適合LED専用3.2A)(ロータリー式)
(下限照度設定機能付)(マットホワイト)
プレート別売
WTA7101WK
希望小売価格 320円(税抜)
※掲載の価格には消費税は含まれていません。

決定図


PG House

小原徳晃 様邸新築工事

Lighting Plan

2026.2.21

(図面 7-3)

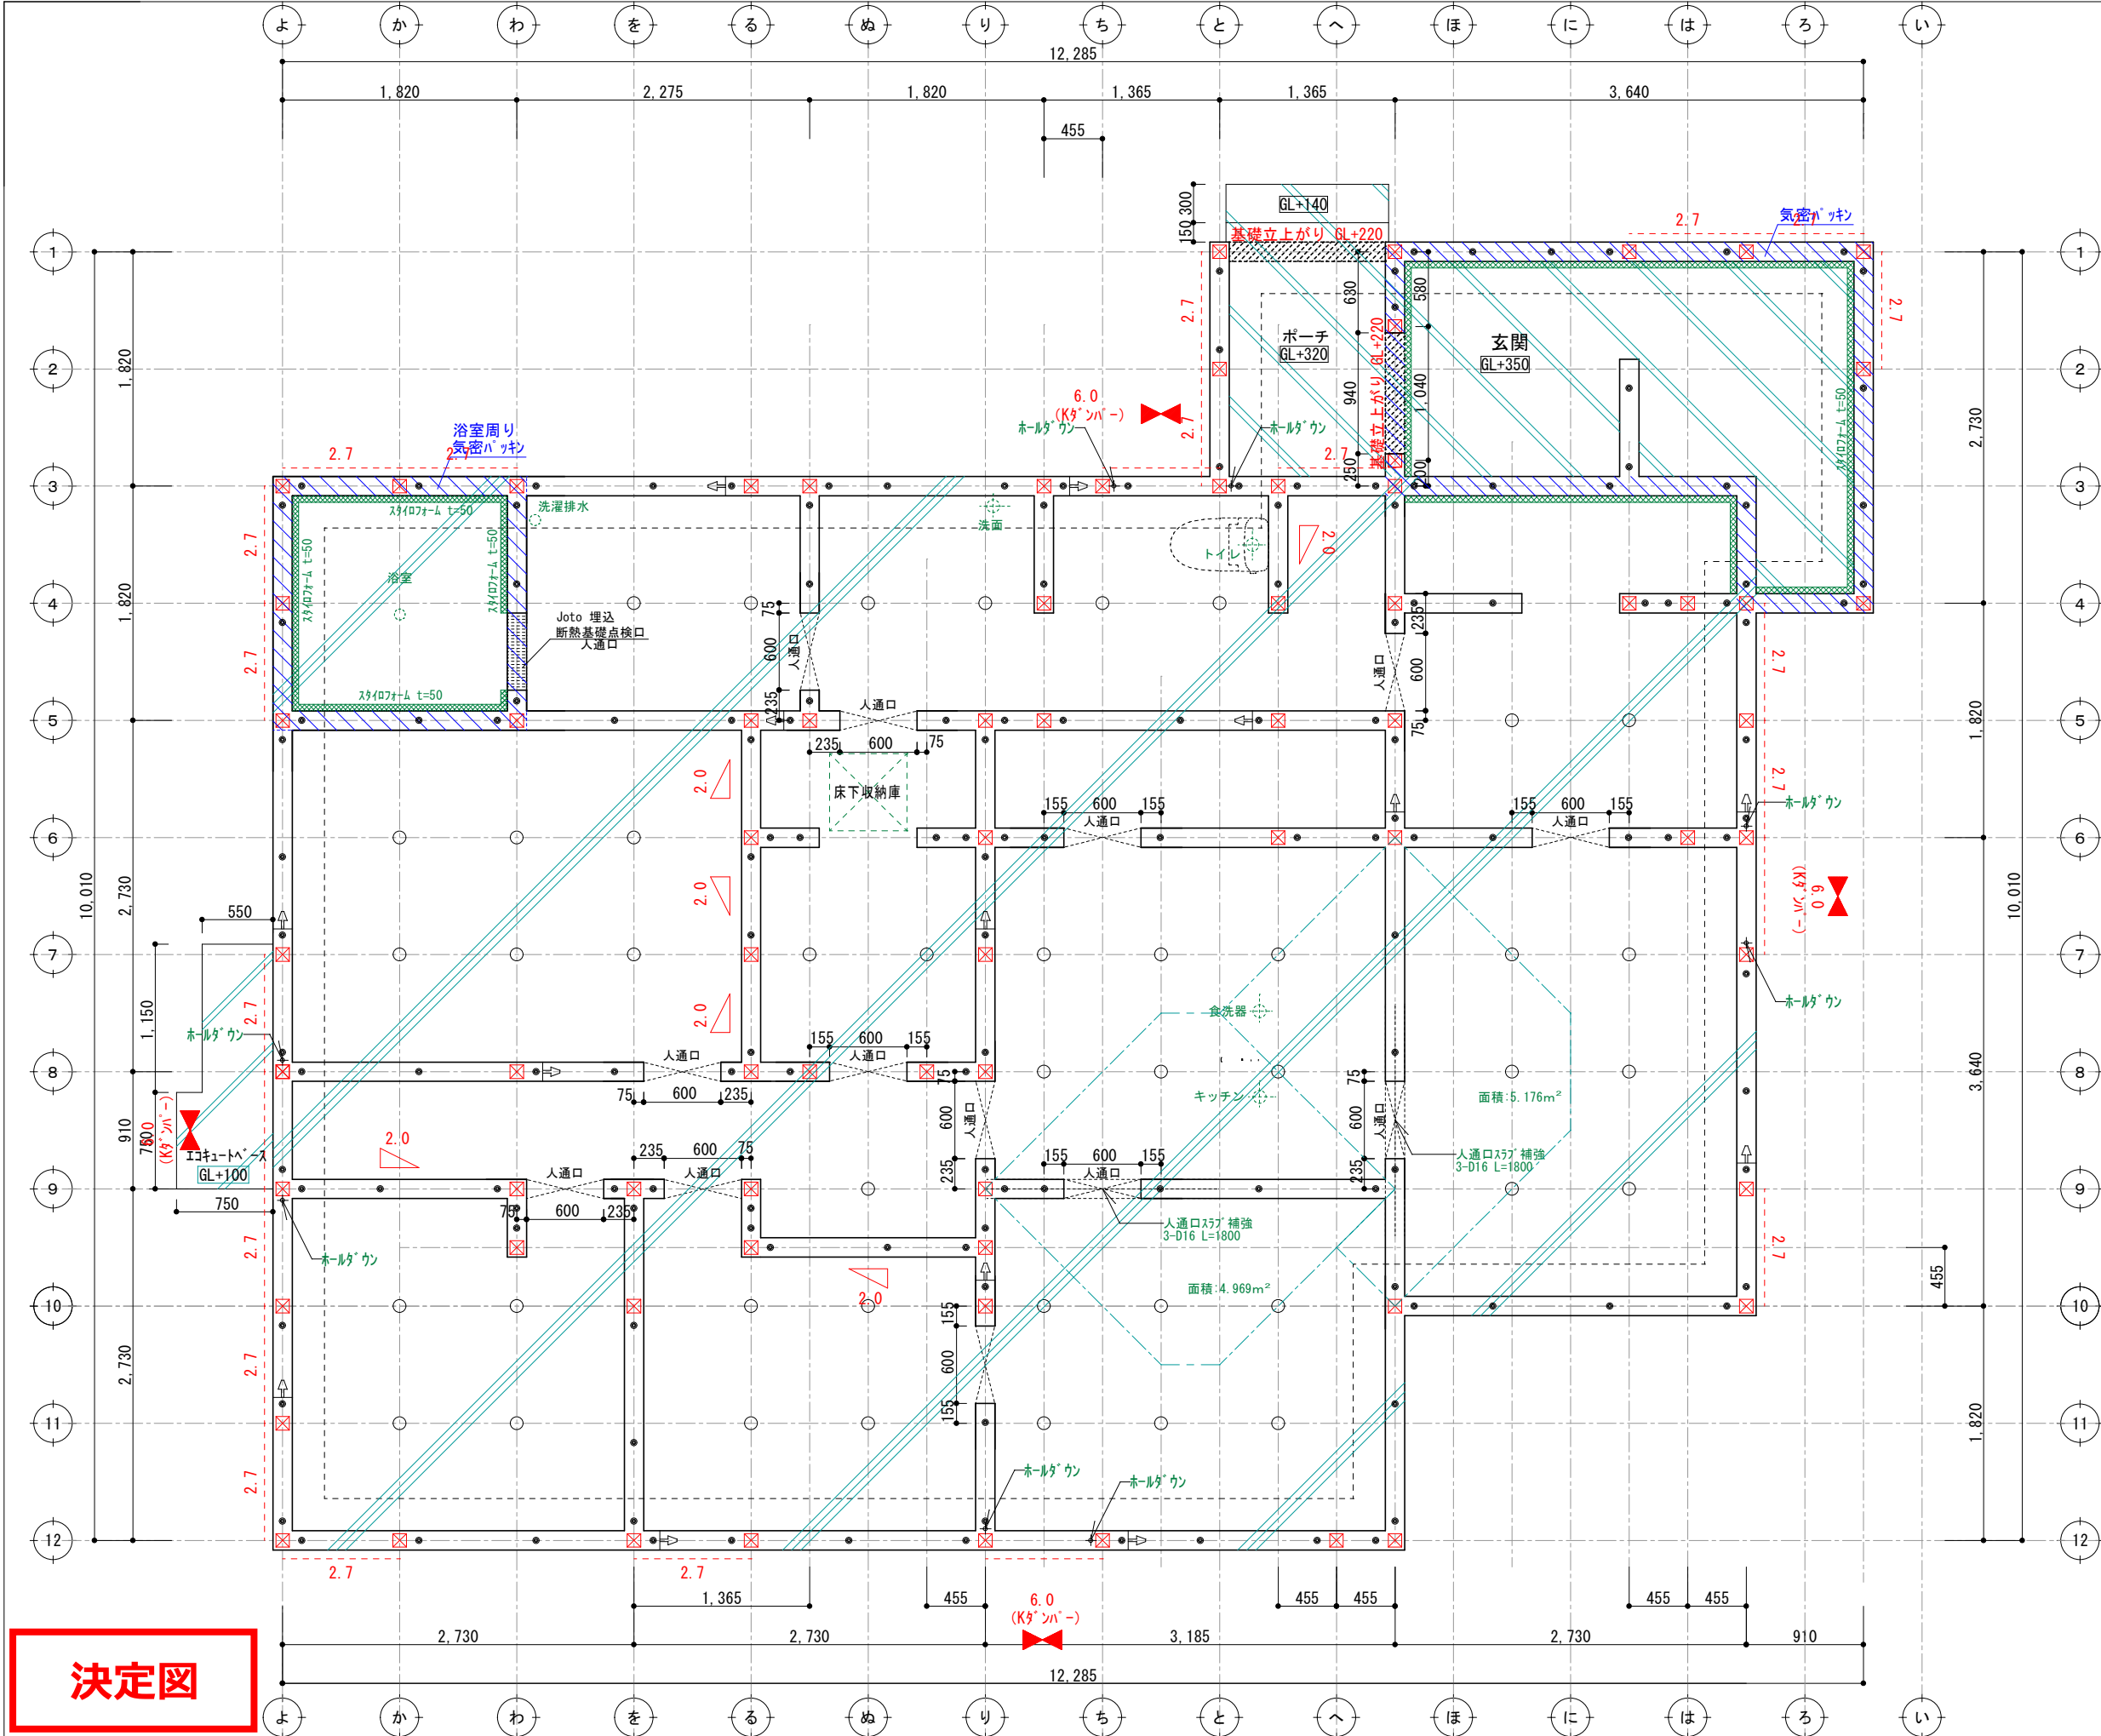


構造体ベースコンクリート t=150

後打ち土間コン

アンカーボルトの配置
土台切れの箇所より150mm
土台の継手及び仕口の端部より150mm
耐力壁の端部、筋交いの脚部より150mm
1.82m以下の間隔
250mm以上埋込み
基礎天端より120mm


筋かい凡例
柱脚 柱頭 片筋かい
たすき掛け筋かい
構造用パネル

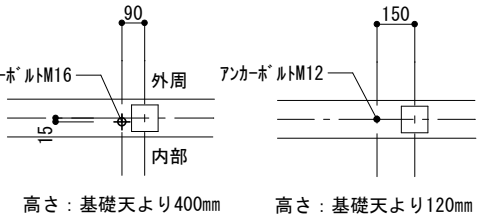

凡例
通し柱 (105*105) 管柱 (105*105)
● アンカーボルトM12 L=400
+ ホールダウンアンカーM16 L=800
柱芯より90mm 280mm以上埋め込み
(カナリフリストアンカーボルトM16)
⊕ 鋼製束
土台ジョイント
ベースコンクリート (t=150)
後打ちコンクリート

基礎伏図について特記なき場合に限り下記による。
1. コンクリート: 呼び強度 21N/mm²
2. 鉄筋: SD295A
3. 設計地耐力: fe=20kN/m²
地耐力計測後、不足の場合は相当の改良を行い、満たすものとする。
4. 基礎の位置は、芯振分けとする。
5. 玄関・S/C・UB周囲の基礎天端は気密パッキン施工 (網掛け部) とし、その他の基礎天端は基礎パッキン施工とする。
6. 設備配管の屋内への取り入れは基礎立上り部のスリーブによる。

決定図

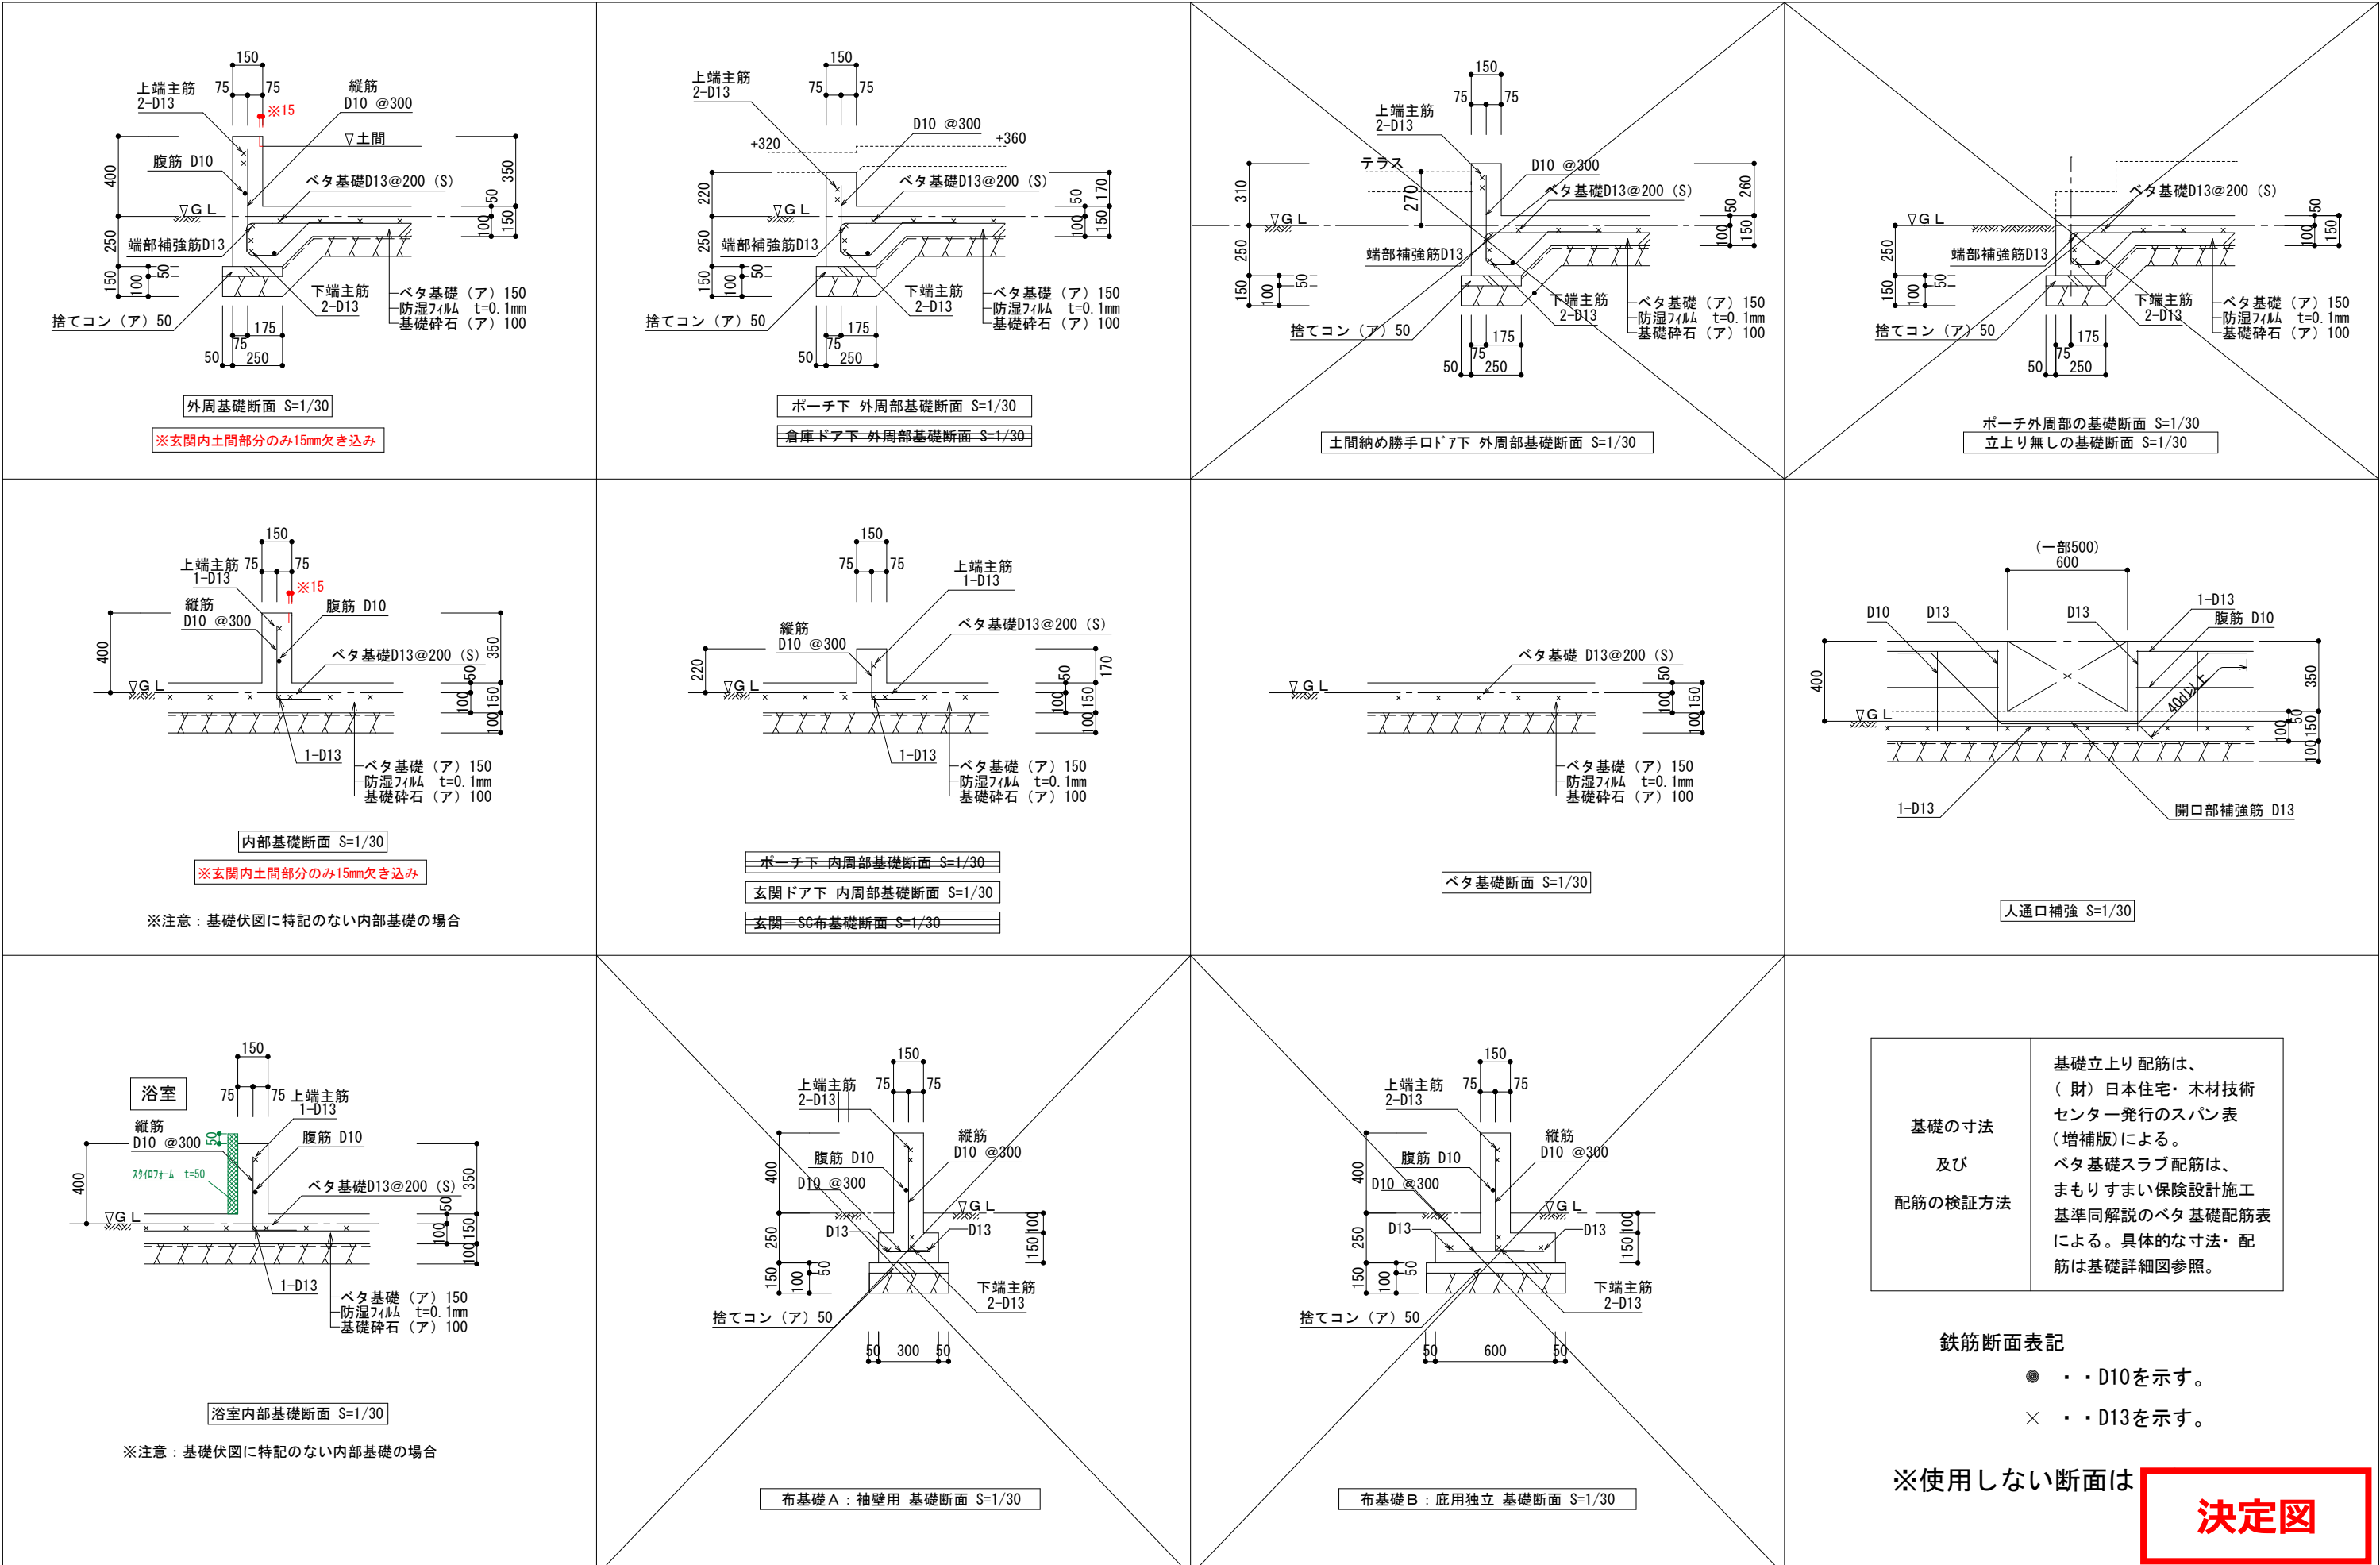

基礎の寸法
及び
配筋の検証方法


基礎立上り配筋は、
(財)日本住宅・木材技術
センター発行のスパン表
(増補版)による。
ベタ基礎スラブ配筋は、
まもりすまい保険設計施工
基準同解説のベタ基礎配筋表
による。具体的な寸法・配
筋は基礎詳細図参照。

鉄筋断面表記

●・・・D10を示す。
×・・・D13を示す。

※使用しない断面は

決定図

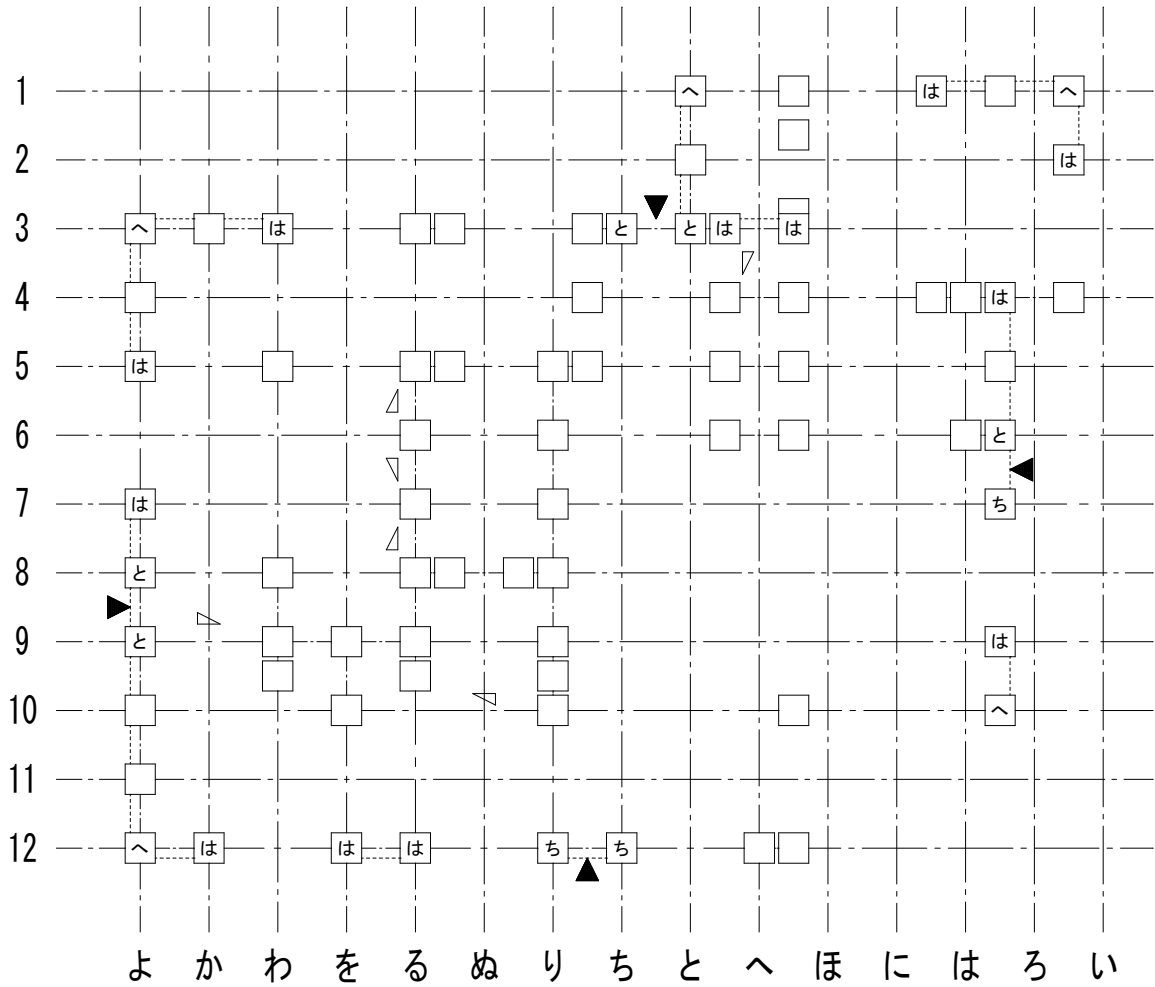

1 階柱壁伏図

接合部凡例				*接合部凡例はユーザ設定されたものです。	
記号	仕様（カナイ金物）		N	倍率	
SBCP	スリムビルドコーナー75, チビクリCK (化粧柱の場合)		0.00	1.00	
SBCP	スリムビルドコーナー75, チビクリCK (化粧柱の場合)		0.65	1.00	
SBCP	は	スリムビルドコーナー75	1.00	1.00	
ARCG	に	アレントコーナー合板用	1.40	2.20	
ARCG	ほ	アレントコーナー合板用	1.60	2.20	
ARCG	へ	アレントコーナー合板用	1.80	2.20	
HD15	と	ブレイブホールダウン B-HD15	2.80	3.60	
HD20	ち	ブレイブホールダウン B-HD20	3.70	4.70	
HD25	り	ブレイブホールダウン B-HD25	4.70	4.80	
HD30	ぬ	ブレイブホールダウン B-HD30	5.60	7.20	
J1	る	腰掛け蟻若しくは大入れ蟻掛け+羽子板*ルト、短冊金物		1.90	梁継手・仕口用
J2	を	腰掛け蟻若しくは大入れ蟻掛け+羽子板*ルト、短冊金物×2		3.00	梁継手・仕口用

※表示なき金物は「は」とする。

接合部凡例				*接合部凡例はユーザ設定されたものです。	
記号	仕様（タナカ金物）		N	倍率	
FCP	フックコーナー, チビクリCK (化粧柱の場合)		0.00	1.00	
FCP	フックコーナー, チビクリCK (化粧柱の場合)		0.65	1.00	
FCP	は	フックコーナー	1.00	1.00	
CCP	に	シナコーナー	1.40	2.20	
CCP	ほ	シナコーナー	1.60	2.20	
CCP	へ	シナコーナー	1.80	2.20	
HD15	と	ビス止めホールダウンU HD15	2.80	3.60	
HD20	ち	ビス止めホールダウンU HD20	3.70	4.70	
HD25	り	ビス止めホールダウンU HD25	4.70	4.80	
HD30	ぬ	ビス止めホールダウンU HD15×2 (HD35)	5.60	7.20	
J1	る	腰掛け蟻若しくは大入れ蟻掛け+羽子板*ルト、短冊金物		1.90	梁継手・仕口用
J2	を	腰掛け蟻若しくは大入れ蟻掛け+羽子板*ルト、短冊金物×2		3.00	梁継手・仕口用


※表示なき金物は「は」とする。

筋かいの種類に応じた筋かいの端部の接合部の仕様		
	筋かいの種類	接合部の仕様（構造方法）
イ	鉄筋φ9	柱又は横架材を貫通し、三角座金を介してナット締め、又は鋼板添え板を用い鋼板を柱及び横架材にCN90, 8本平打ち
ロ	筋かい:15×90	柱・横架材を欠き込み、柱・横架材双方に対してN65, 5本平打ち
ハ	筋かい:30×90	鋼板添え板t=1.6mmを筋かいに対してボルトφ12及びCN65, 3本平打ち、柱に対してCN65, 3本平打ち、横架材に対してCN65, 4本平打ち。筋かいプレートBP同等品
ニ	筋かい:45×90	鋼板添え板t=2.3mmを筋かいに対してボルトφ12及びスクリュー釘φ4.5L50, 7本平打ち、柱及び横架材に対してスクリュー釘φ4.5L50, 5本平打ち。筋かいプレートBP-2同等品
ホ	筋かい:90×90	柱又は横架材にボルトφ12mmを用いて一面剪断接合

胴差と通し柱の接合部の仕様		
	胴差と通し柱の条件	仕口
T1	通し柱の片側に胴差が来る場合	胴差を柱にかたぎ大入れ短ほぞ差しの上、羽子板ボルト、かね折り金物又は同等以上の仕口
T2	通し柱の両側に胴差が来る場合	胴差を柱にかたぎ大入れ短ほぞ差しの上、短冊金物又は、同等以上の仕口で胴差相互を緊結
T3	通し柱と胴差の接合部の近くに90×90以上の筋かいが来る場合(通し柱が建物の出隅にあるか、筋かい壁が外壁と直交して接する場合)	胴差を通し柱に、15KN用引き寄せ金物を水平に用いて緊結

決定図

アクセントクロス指示書

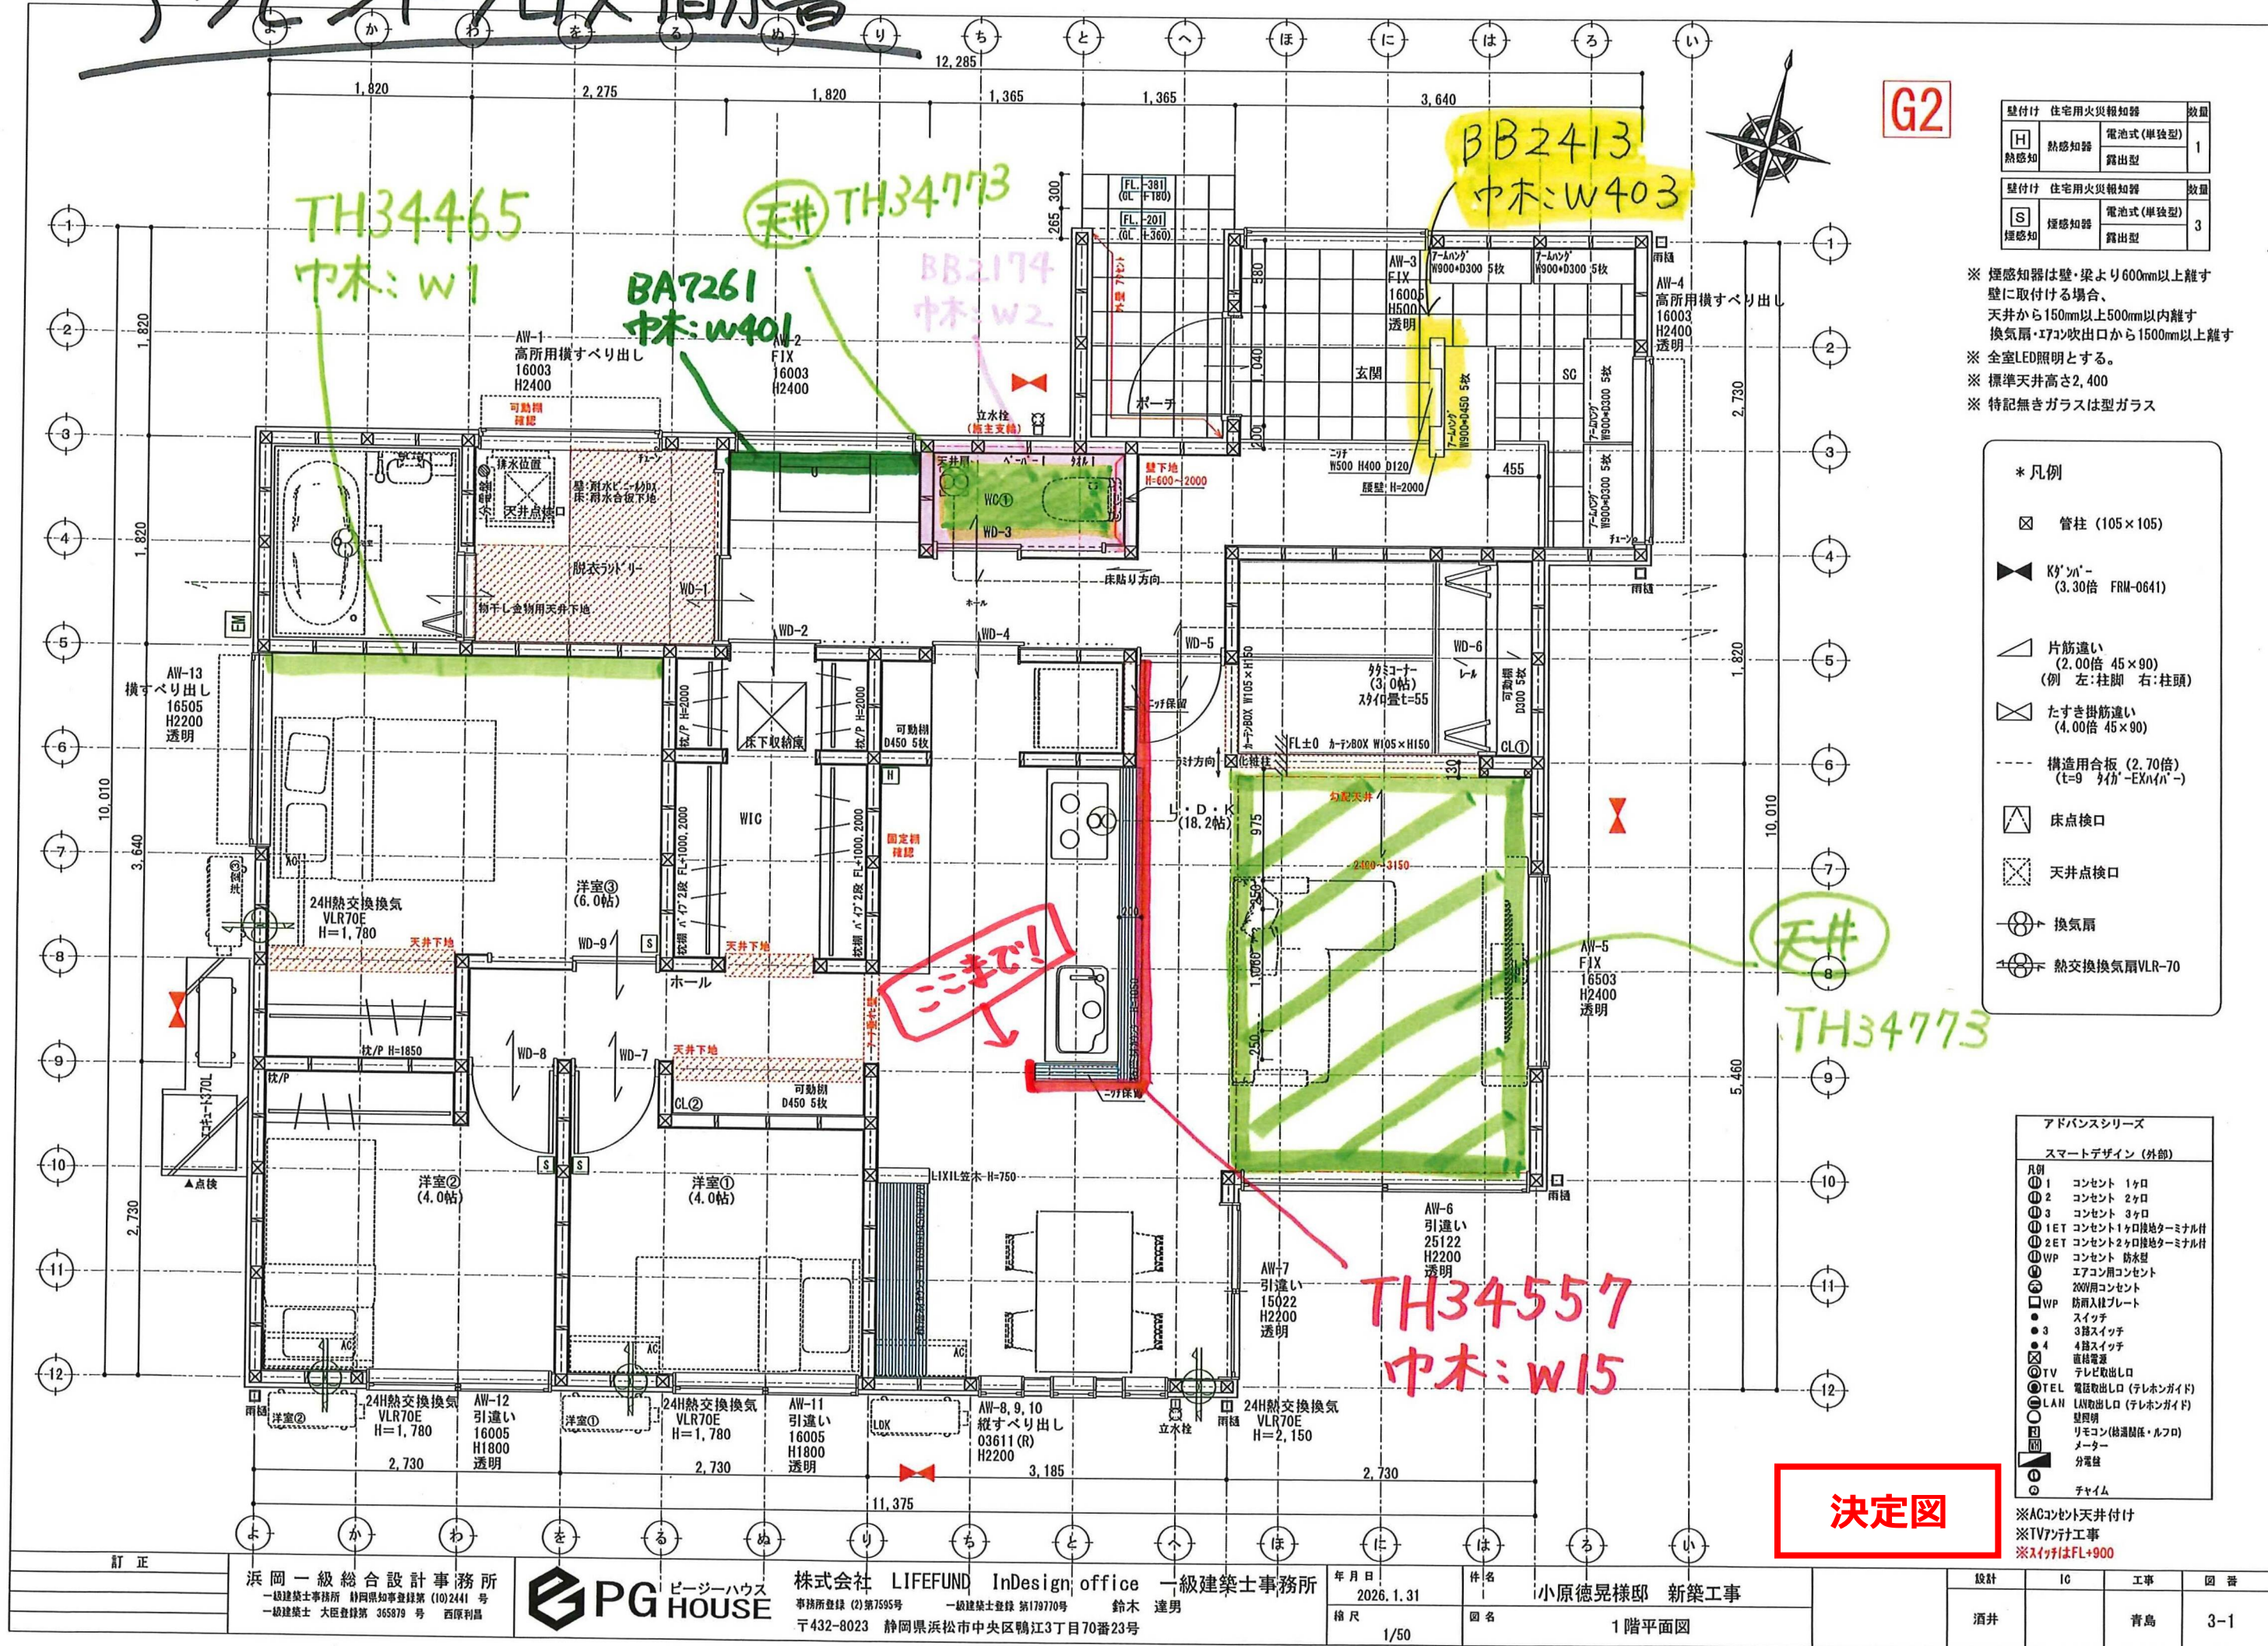

決定図