
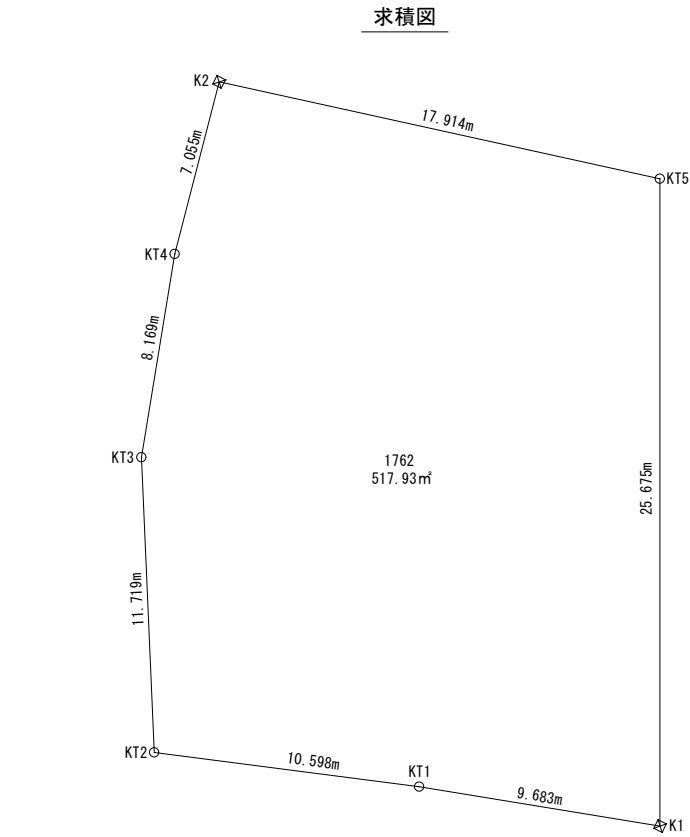


浜松市浜名区新原地内

G2

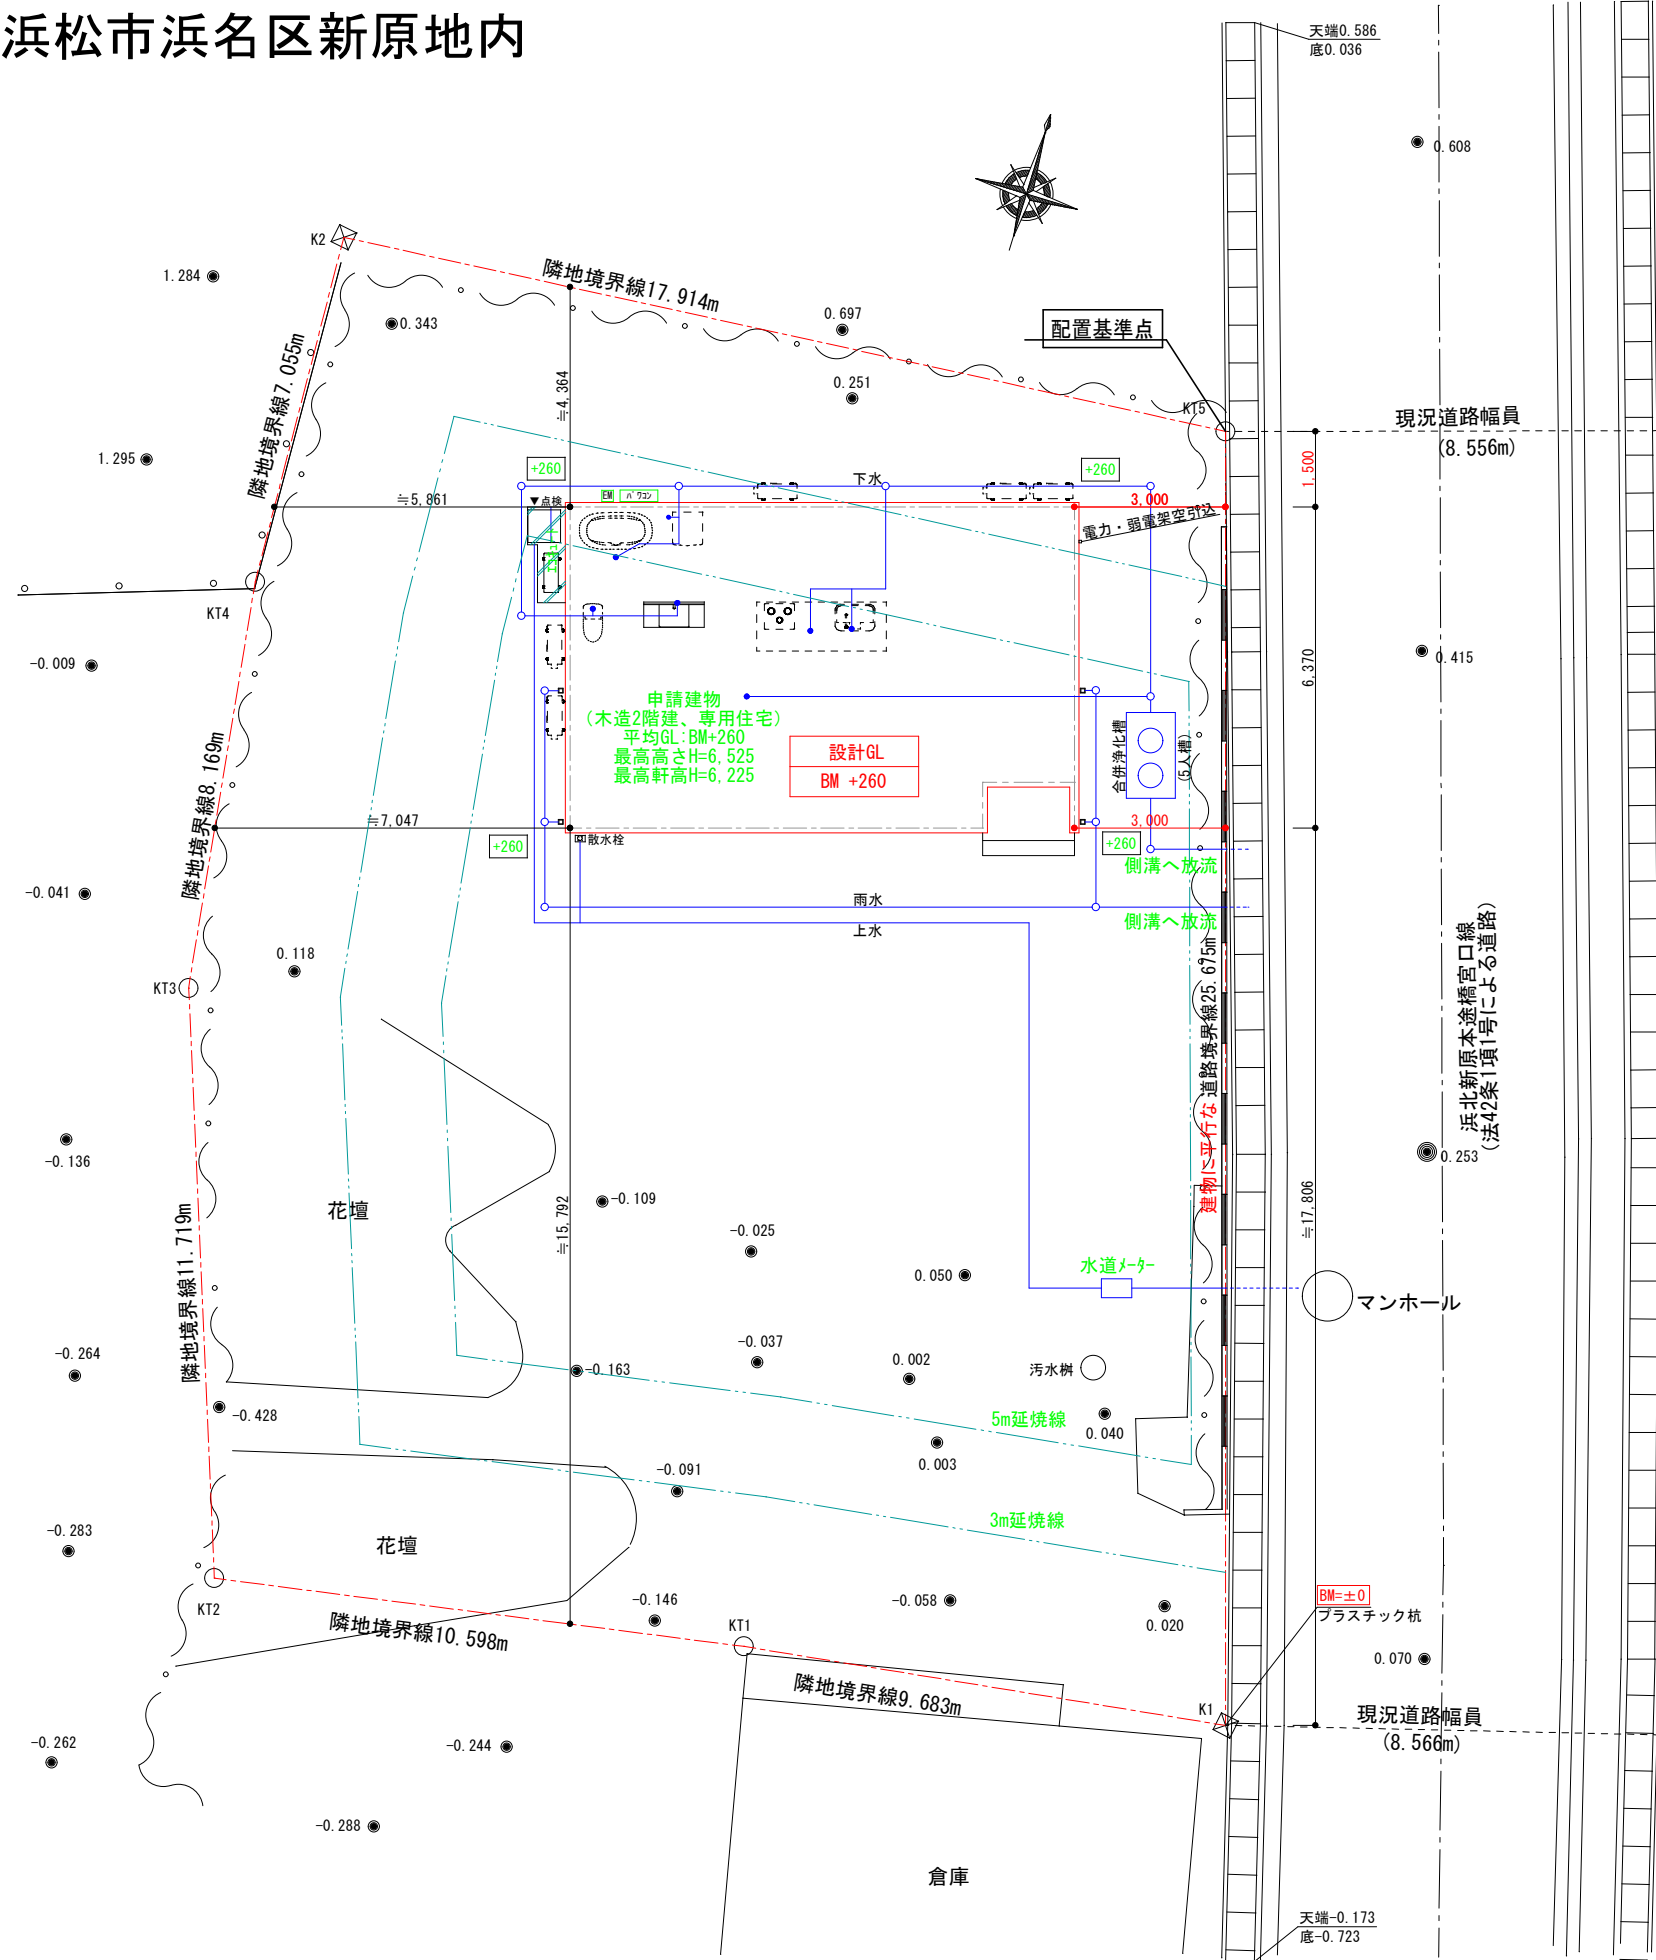

求積表				
地番	1 1762			
NO	X _n	Y _n	Y _{n+1} - Y _{n-1}	X _n × (Y _{n+1} - Y _{n-1})
K1	-4.780	6.839	25.828	-123.457840
KT1	-14.018	9.744	6.429	-90.121722
KT2	-24.013	13.268	-6.699	160.863087
KT3	-29.744	3.045	-18.017	535.897648
KT4	-32.191	-4.749	-14.686	472.757026
K2	-33.701	-11.641	-11.335	382.000835
KT5	-16.346	-16.084	18.480	-302.074080
合計			1035.864954	
合計面積			517.9324770	
地積			517.93	

トータル面積表 (㎡)	
敷地面積	517.93
建築面積	63.76
床面積 1階	62.11
2階	36.43
延床面積	98.54
建築率	(63.76/517.93) × 100
容積率	(98.54/517.93) × 100

道路斜線制限については、明らかに適合する。
隣地斜線制限については、明らかに適合する。
平均地盤面について
申請建物の周囲の平均地盤面高さをBM+260とする。
盛土規制法の許可対象となる工事なし。

決定図