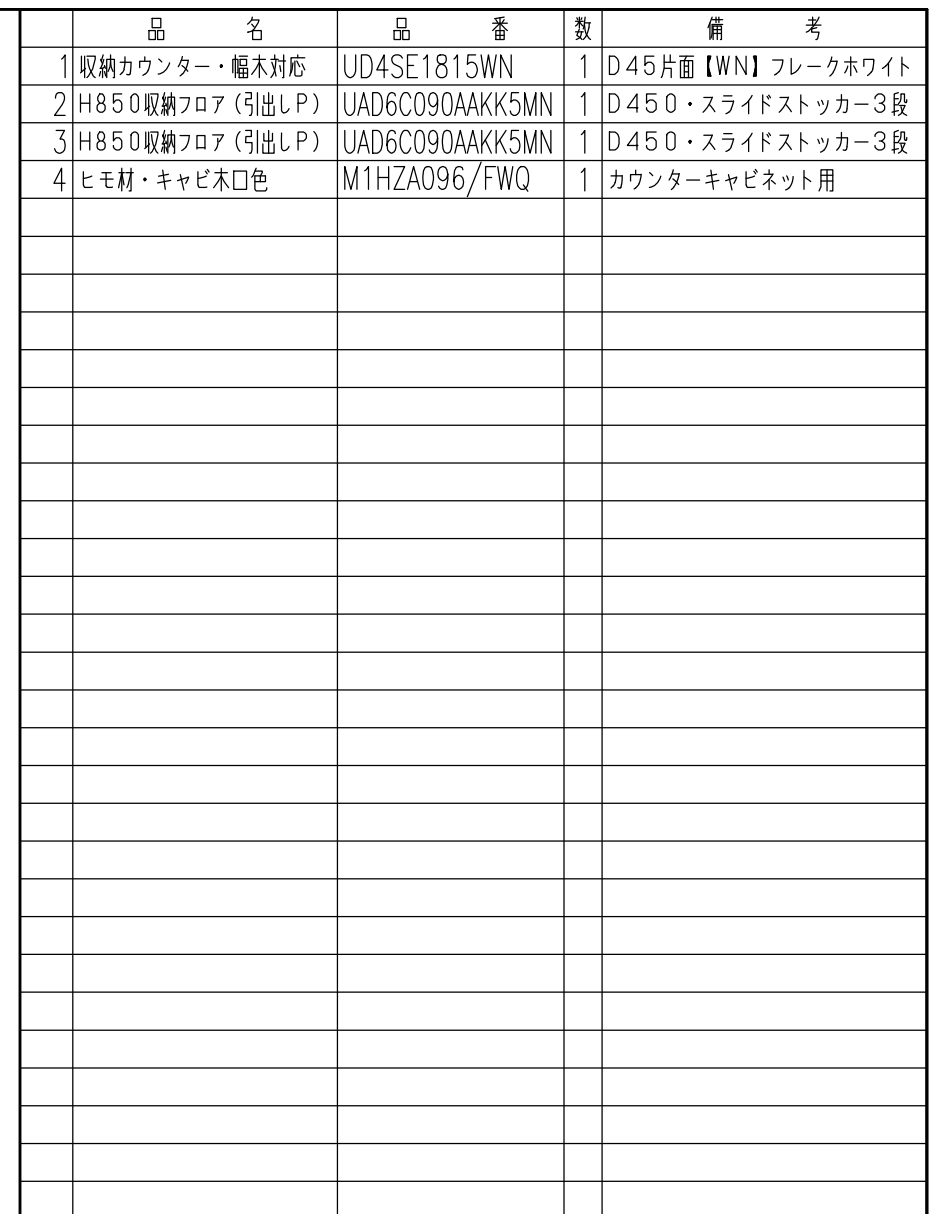
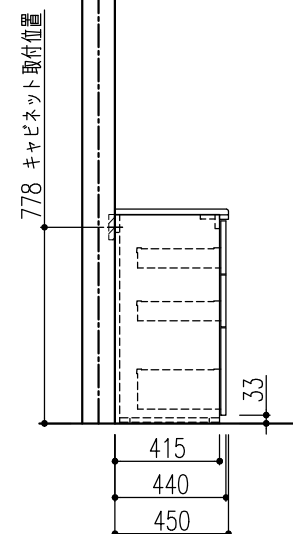




特記事項 扉色 KK5:ブラックスタック 取手 [M]スリム取手(ブラック)	物件名	平松久美江 様邸	案件No.	図面名	担当	図面	図番 : 株式会社 LIXIL
			A2512DDD0EZSWS	レイアウト図	葉野 友仁		
	仕様	ES21	見積No.	縮尺	日付		
			M25129577942-009-3	1/30	2026.02.16		

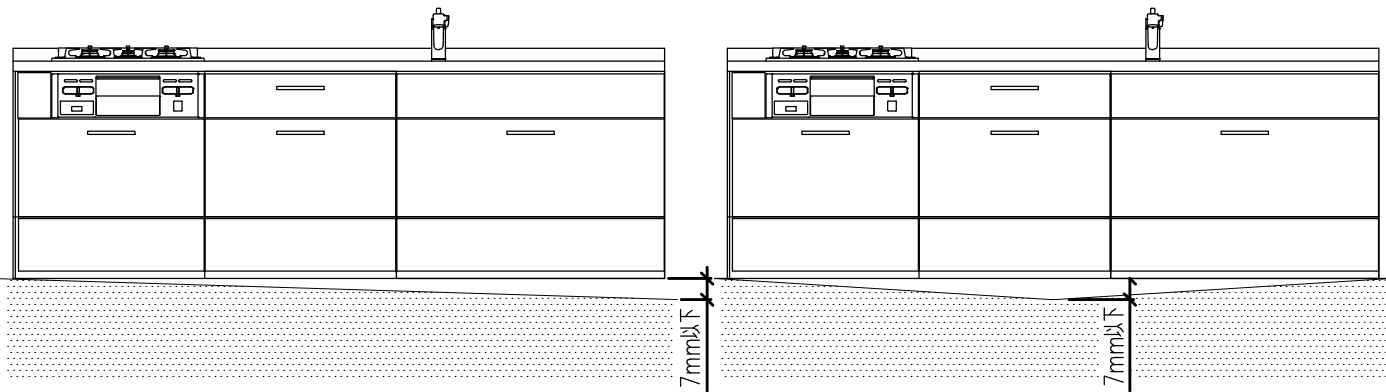


【ご注意】

- 記載のキャビネット寸法は扉前面までの呼び寸法です。キャビネット本体の寸法・扉厚み等は商品ガイドの巻末資料をご確認ください。
- 記載のワークトップ、カウンター、エンドパネル、サイドパネルの寸法は呼び寸法です。詳細寸法は商品ガイドの巻末資料をご確認ください。
- 取付・設置に際し、各製品の取付・設置説明書や図面の機能図を必ずお読み下さい。

特記事項 扉色 KK5:ブラックスタック 取手 [M]スリム取手 (ブラック)	物件名	平松久美江 様邸	案件No.	図面名	担当	図面	図番 : 株式会社 LIXIL
			A2512DD00EZSWS	納まり図	栗野 友仁		
	仕様	ES21	見積No.	縮尺	日付		
			M25129577942-009-3	1/30	2026.02.16		

■ 床の不陸に関して

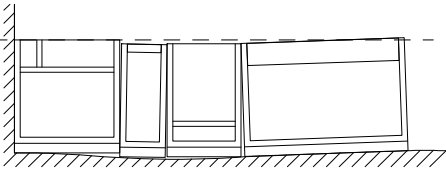


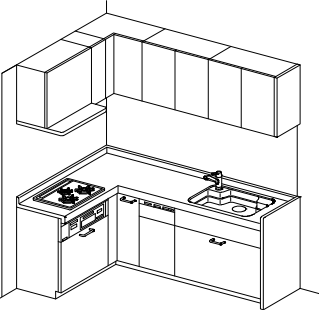
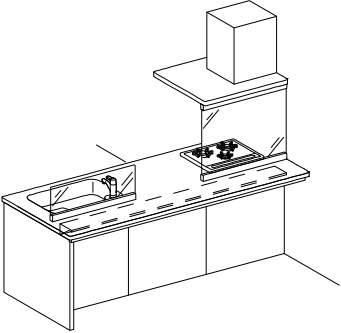
床の不陸は、7 m m 以下に抑えるようにしてください。不陸が大きい場合は、現場責任者に床の修正を依頼してください。
※キャビネット取付時には不陸調整スペーサー等で水平になるように設置してください。

特記事項 扉色 KK5:ブラックスタック 取手 [M]スリム取手（ブラック）	物件名	平松久美江 様邸	案件No.	図面名	担当	図面	図番
			A2512DDD0EZSWS	機能図	栗野 友仁		株式会社 LIXIL
			見積No.	縮尺	日付		
			M25129577942-009-3		2026.02.16		
仕 様	ES 2 1						

■ キッチン取付者さま向け 動画コンテンツ ■

商品取付けの注意点を2次元コードでご視聴いただけます。
取付日より前に、是非ご確認ください。

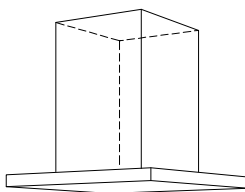
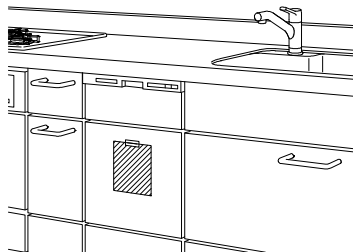
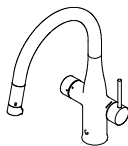
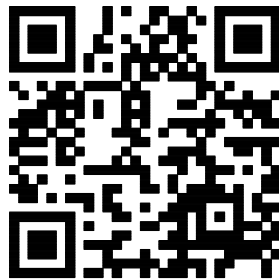
荷扱い・搬入	カウンター開梱搬入「養生ツール」	不陸の確認と調整	マグネットキッチンパネル
荷扱い・搬入	カウンター開梱搬入 「養生ツール」のご紹介		マグネット キッチンパネル 「取付・設置」ポイント
作成日：2024年10月01日	作成日：2024年10月01日 改定日：2025年12月11日	作成日：2024年02月07日	作成日：2024年03月06日

人造大理石カウンターL型キッチン	センターキッチン（ペニンシュラ型）		
			
作成日：2024年02月07日	作成日：2024年02月07日		

	特記事項 扉色 KK5:ブラックスタック 取手 [M]スリム取手（ブラック）	物件名	平松久美江 様邸	案件No.	図面名	担当	図面	図番	
		仕様	E S 2 1	A2512DDD0EZSWS	機能図	栗野 友仁		株式会社 LIXIL	
				見積No.	縮尺	日付			
				M25129577942-009-3		2026.02.16			

■ キッチン取付者さま向け 動画コンテンツ ■

商品取付けの注意点を2次元コードでご視聴いただけます。
取付日より前に、是非ご確認ください。

センターフード型レンジフード (天吊りフード)  作成日：2024年06月03日 		I H加熱機器関連 I H加熱機器 仕切り板 作成日：2024年02月07日 		食器洗い乾燥機  作成日：2024年02月07日 		ミネラル浄水栓 Greentap  作成日：2024年06月03日 			
	特記事項 扉色 KK5:ブラックスタック 取手 [M]スリム取手 (ブラック)	物件名 仕様	平松久美江 様邸		案件No.	図面名	担当	図面	図番
					A2512DDD0EZSWS	機能図	栗野 友仁		
			ES21		見積No.	縮尺	日付		
					M25129577942-009-3		2026.02.16		

株式会社 LIXIL