




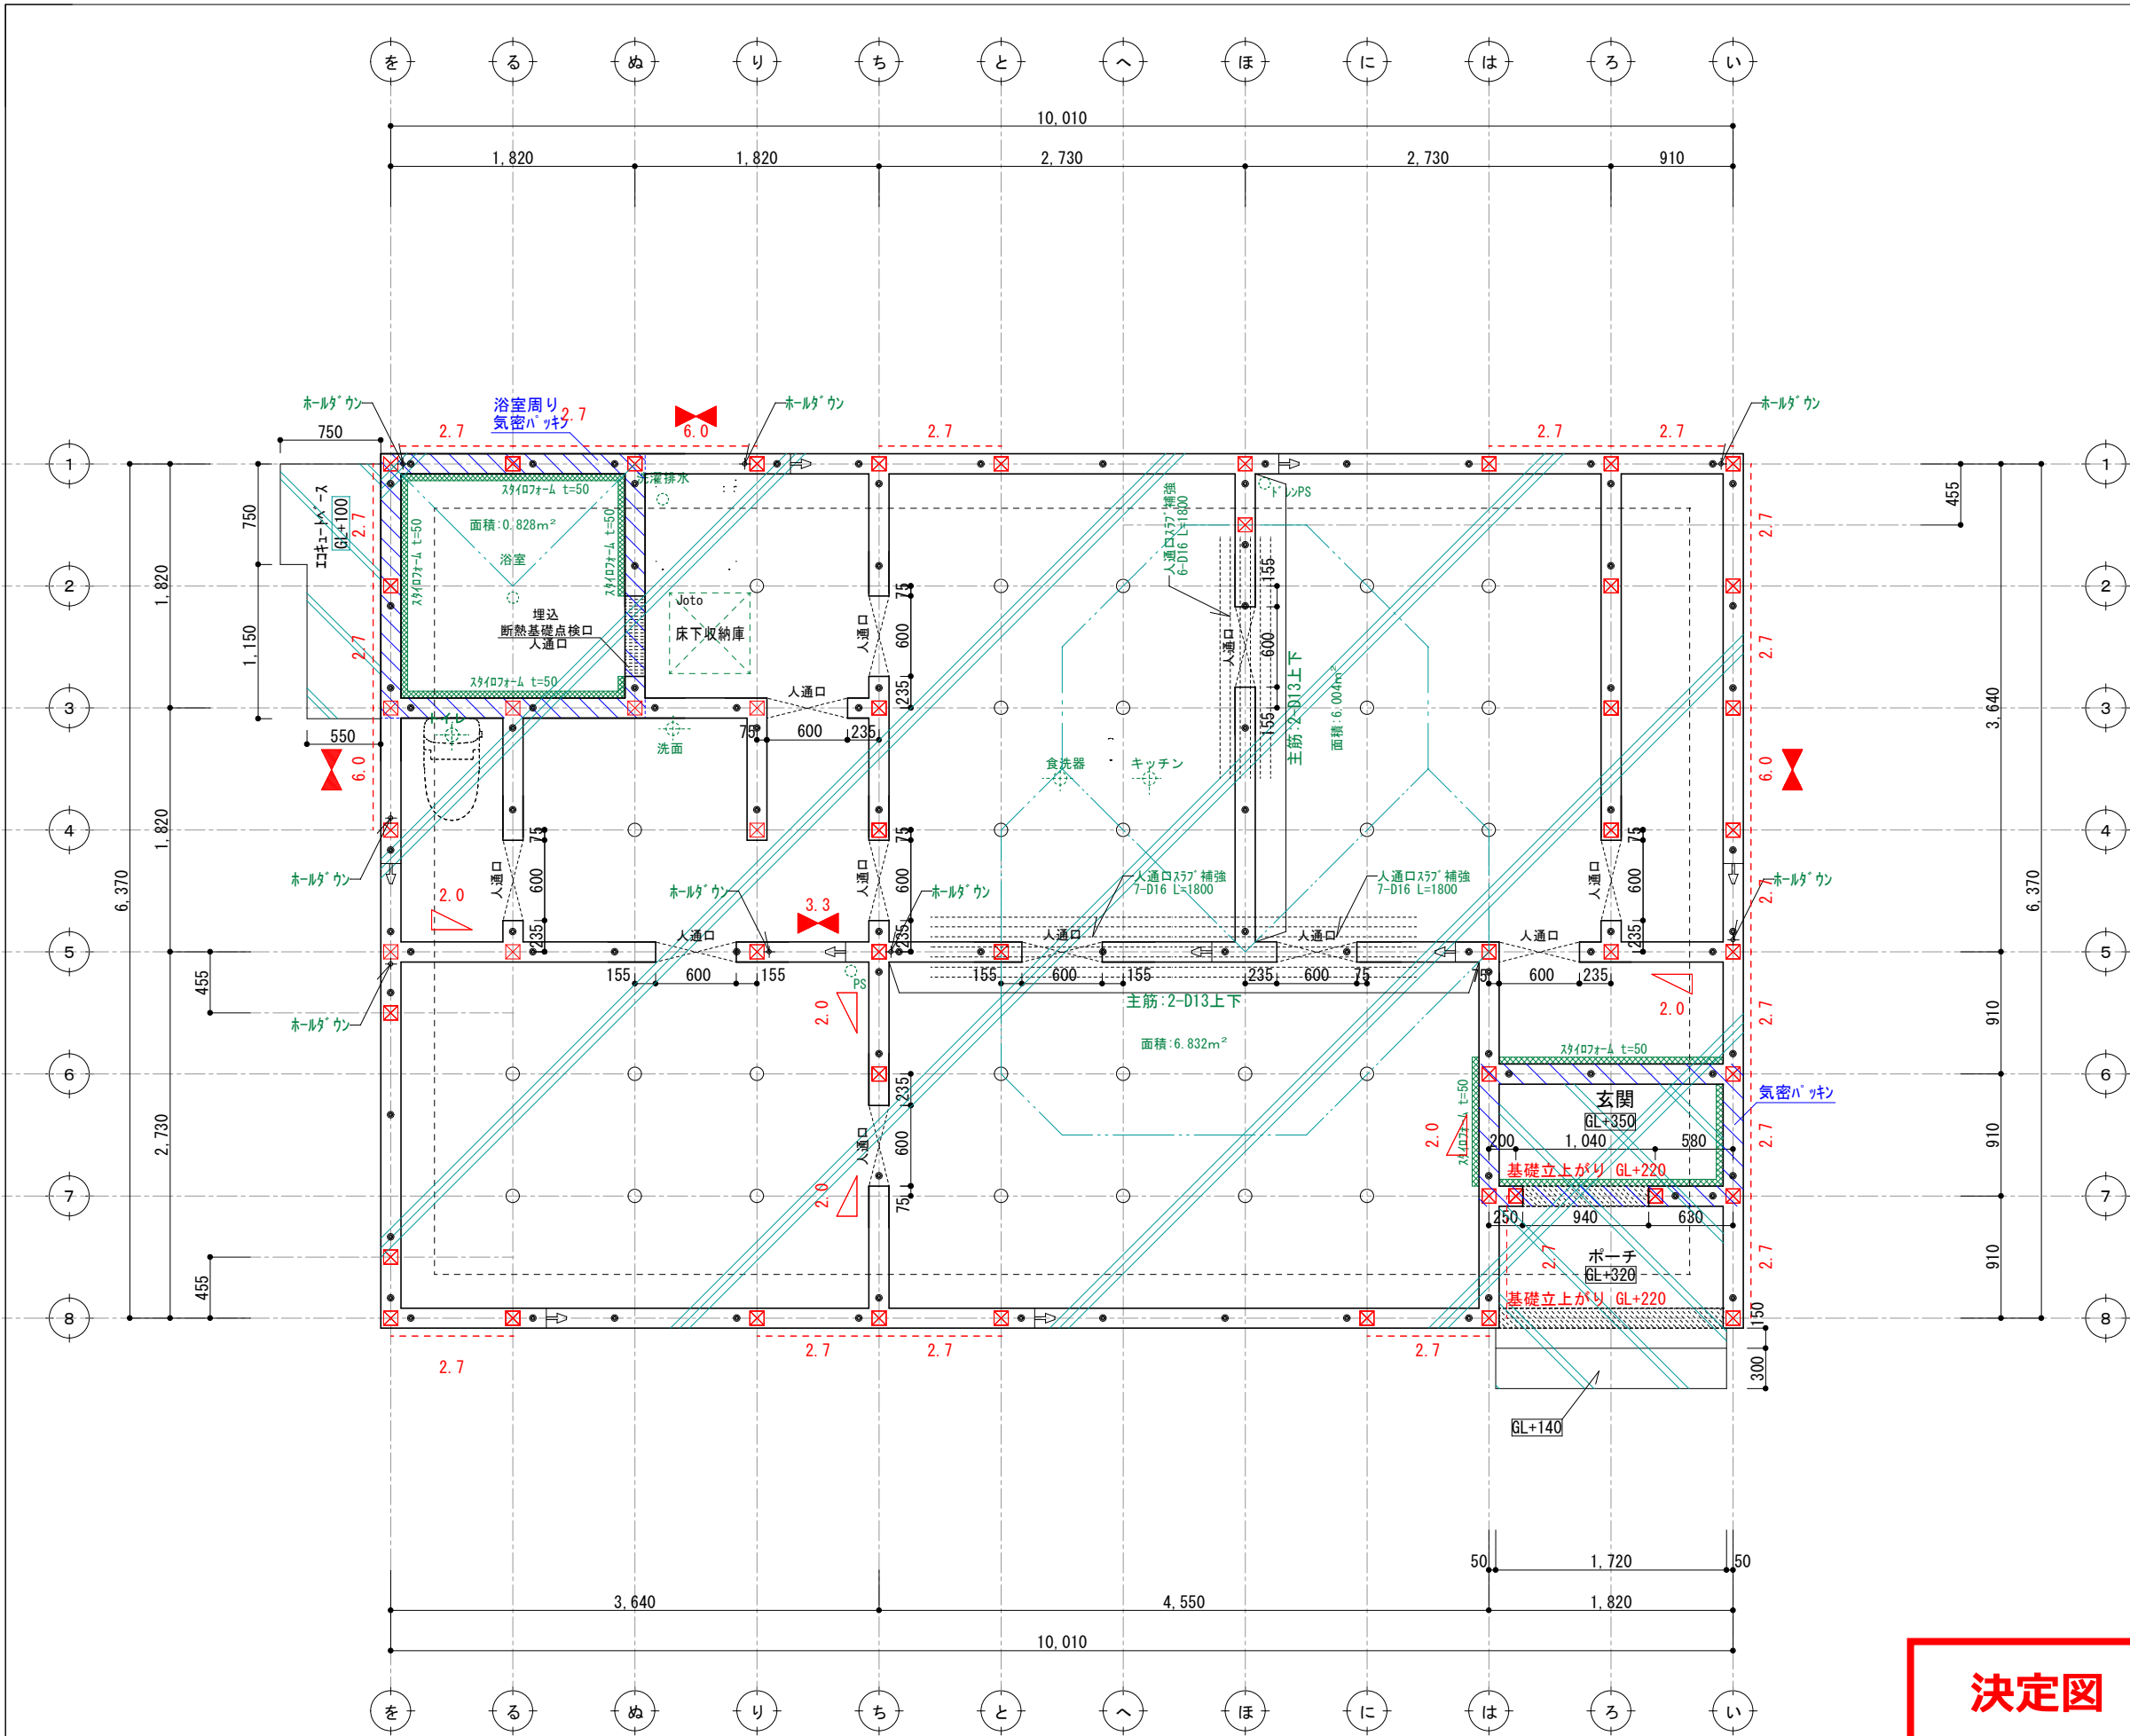

構造体ベースコンクリート t=150

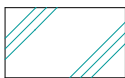

後打ち土間コン

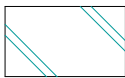


アンカーボルトの配置

- 土台切れの箇所より150mm
- 土台の継手及び仕口の端部より150mm
- 耐力壁の端部、筋交いの脚部より150mm
- 1.82m以下の間隔
- 250mm以上埋込み
- 基礎天端より120mm

筋かい凡例

- 柱脚 柱頭 片筋かい
- たすき掛け筋かい
- 構造用パネル

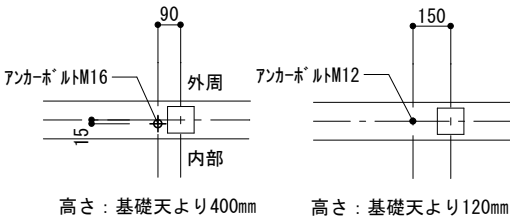

ホールダウンアンカーボルト配置

アンカーボルト配置

凡例

- 通し柱 (105*105) 管柱 (105*105)
- アンカーボルトM12 L=400
- + ホールダウンアンカーM16 L=800
- 柱芯より90mm 280mm以上埋め込み (カナイフリストアンカーボルトM16)
- ⊕ 鋼製束
- 土台ジョイント
- ▨ ベースコンクリート (t=150)
- ▨ 後打ちコンクリート

基礎伏図について特記なき場合に限り下記による。

- コンクリート：呼び強度 21N/mm²
- 鉄筋：SD295A
- 設計地耐力：fe=20kN/m²
地耐力計測後、不足の場合は相当の改良を行い、満たすものとする。
- 基礎の位置は、芯振分けとする。
- 玄関・S/C・UB周囲の基礎天端は気密パッキン施工 (網掛け部) とし、その他の基礎天端は基礎パッキン施工とする。
- 設備配管の屋内への取り入れは基礎立上り部のスリーブによる。

決定図

訂正	浜岡一級総合設計事務所	LIFEFUND	株式会社 LIFEFUND InDesign office	一級建築士事務所	年月日	件名	設計	IC	工事	図番
	一級建築士事務所 静岡県知事登録第 (10)2441 号	PG HOUSE	事務所登録 (2)第7595号	一級建築士登録 第179770号 鈴木 達男	2026. 2. 15	平松久美江様 邸新築工事				
	一級建築士 大臣登録第 365879 号 西原利昌		〒432-8023 静岡県浜松市中央区鶴江3丁目70番23号	鈴木 達男	縮尺	図名				
					1/50	基礎伏図	酒井		青島	B-1