

G2



壁付け 住宅用火災報知器		数量
[H] 熱感知	電池式(単独型)	1
	露出型	
壁付け 住宅用火災報知器		数量
[S] 煙感知	電池式(単独型)	
	露出型	

- ※ 煙感知器は壁・梁より600mm以上離す
壁に取付ける場合、
天井から150mm以上500mm以内離す
換気扇・エアコン吹出口から1500mm以上離す
- ※ 全室LED照明とする。
- ※ 標準天井高さ2,400
- ※ 特記無きガラスは型ガラス

* 凡例

☒ 管柱 (105×105)

☒ K'ンパ-
(3.30倍 FRM-0641)

△ 片筋違い
(2.00倍 45×90)
(例 左:柱脚 右:柱頭)

☒ たすき掛筋違い
(4.00倍 45×90)

--- 構造用合板 (2.70倍)
(t=9 9分 -EXN(ハ-))

☒ 床点検口

☒ 天井点検口

☒ 換気扇

☒ 熱交換換気扇VLR-70

アドバンスシリーズ

スマートデザイン (外部)

凡例		
①	コンセント	1ヶ所
②	コンセント	2ヶ所
③	コンセント	3ヶ所
①ET	コンセント1ヶ所接地ターミナル付	
②ET	コンセント2ヶ所接地ターミナル付	
①WP	コンセント 防水型	
②	エアコン用コンセント	
③	200V用コンセント	
①WP	防雨入線プレート	
●	スイッチ	
●3	3路スイッチ	
●4	4路スイッチ	
☒	直結電源	
☒TV	テレビ取出口	
☒TEL	電話取出口 (テレホンガイド)	
☒LAN	LAN取出口 (テレホンガイド)	
☒	壁照明	
☒	リモコン (給湯関係・ルフロ)	
☒	メーター	
☒	分電盤	
☒	チャイム	

- ※ACコンセント天井付け
- ※TVアンテナ工事
- ※スイッチはFL+1100、コンセントはFL+200

決定図



訂正

浜岡一級総合設計事務所
一級建築士事務所 静岡県知事登録第 (10)2441 号
一級建築士 大臣登録第 365879 号 西原利昌




株式会社 LIFEFUND InDesign office 一級建築士事務所
事務所登録 (2) 第7595号 一級建築士登録 第179770号 鈴木 達男
〒432-8023 静岡県浜松市中央区鶴江3丁目70番23号

年月日
2026.1.11
縮尺
1/50

件名
平松久美江様邸 新築工事
図名
1階平面図

設計	IC	工事	図番
酒井		青島	3-1

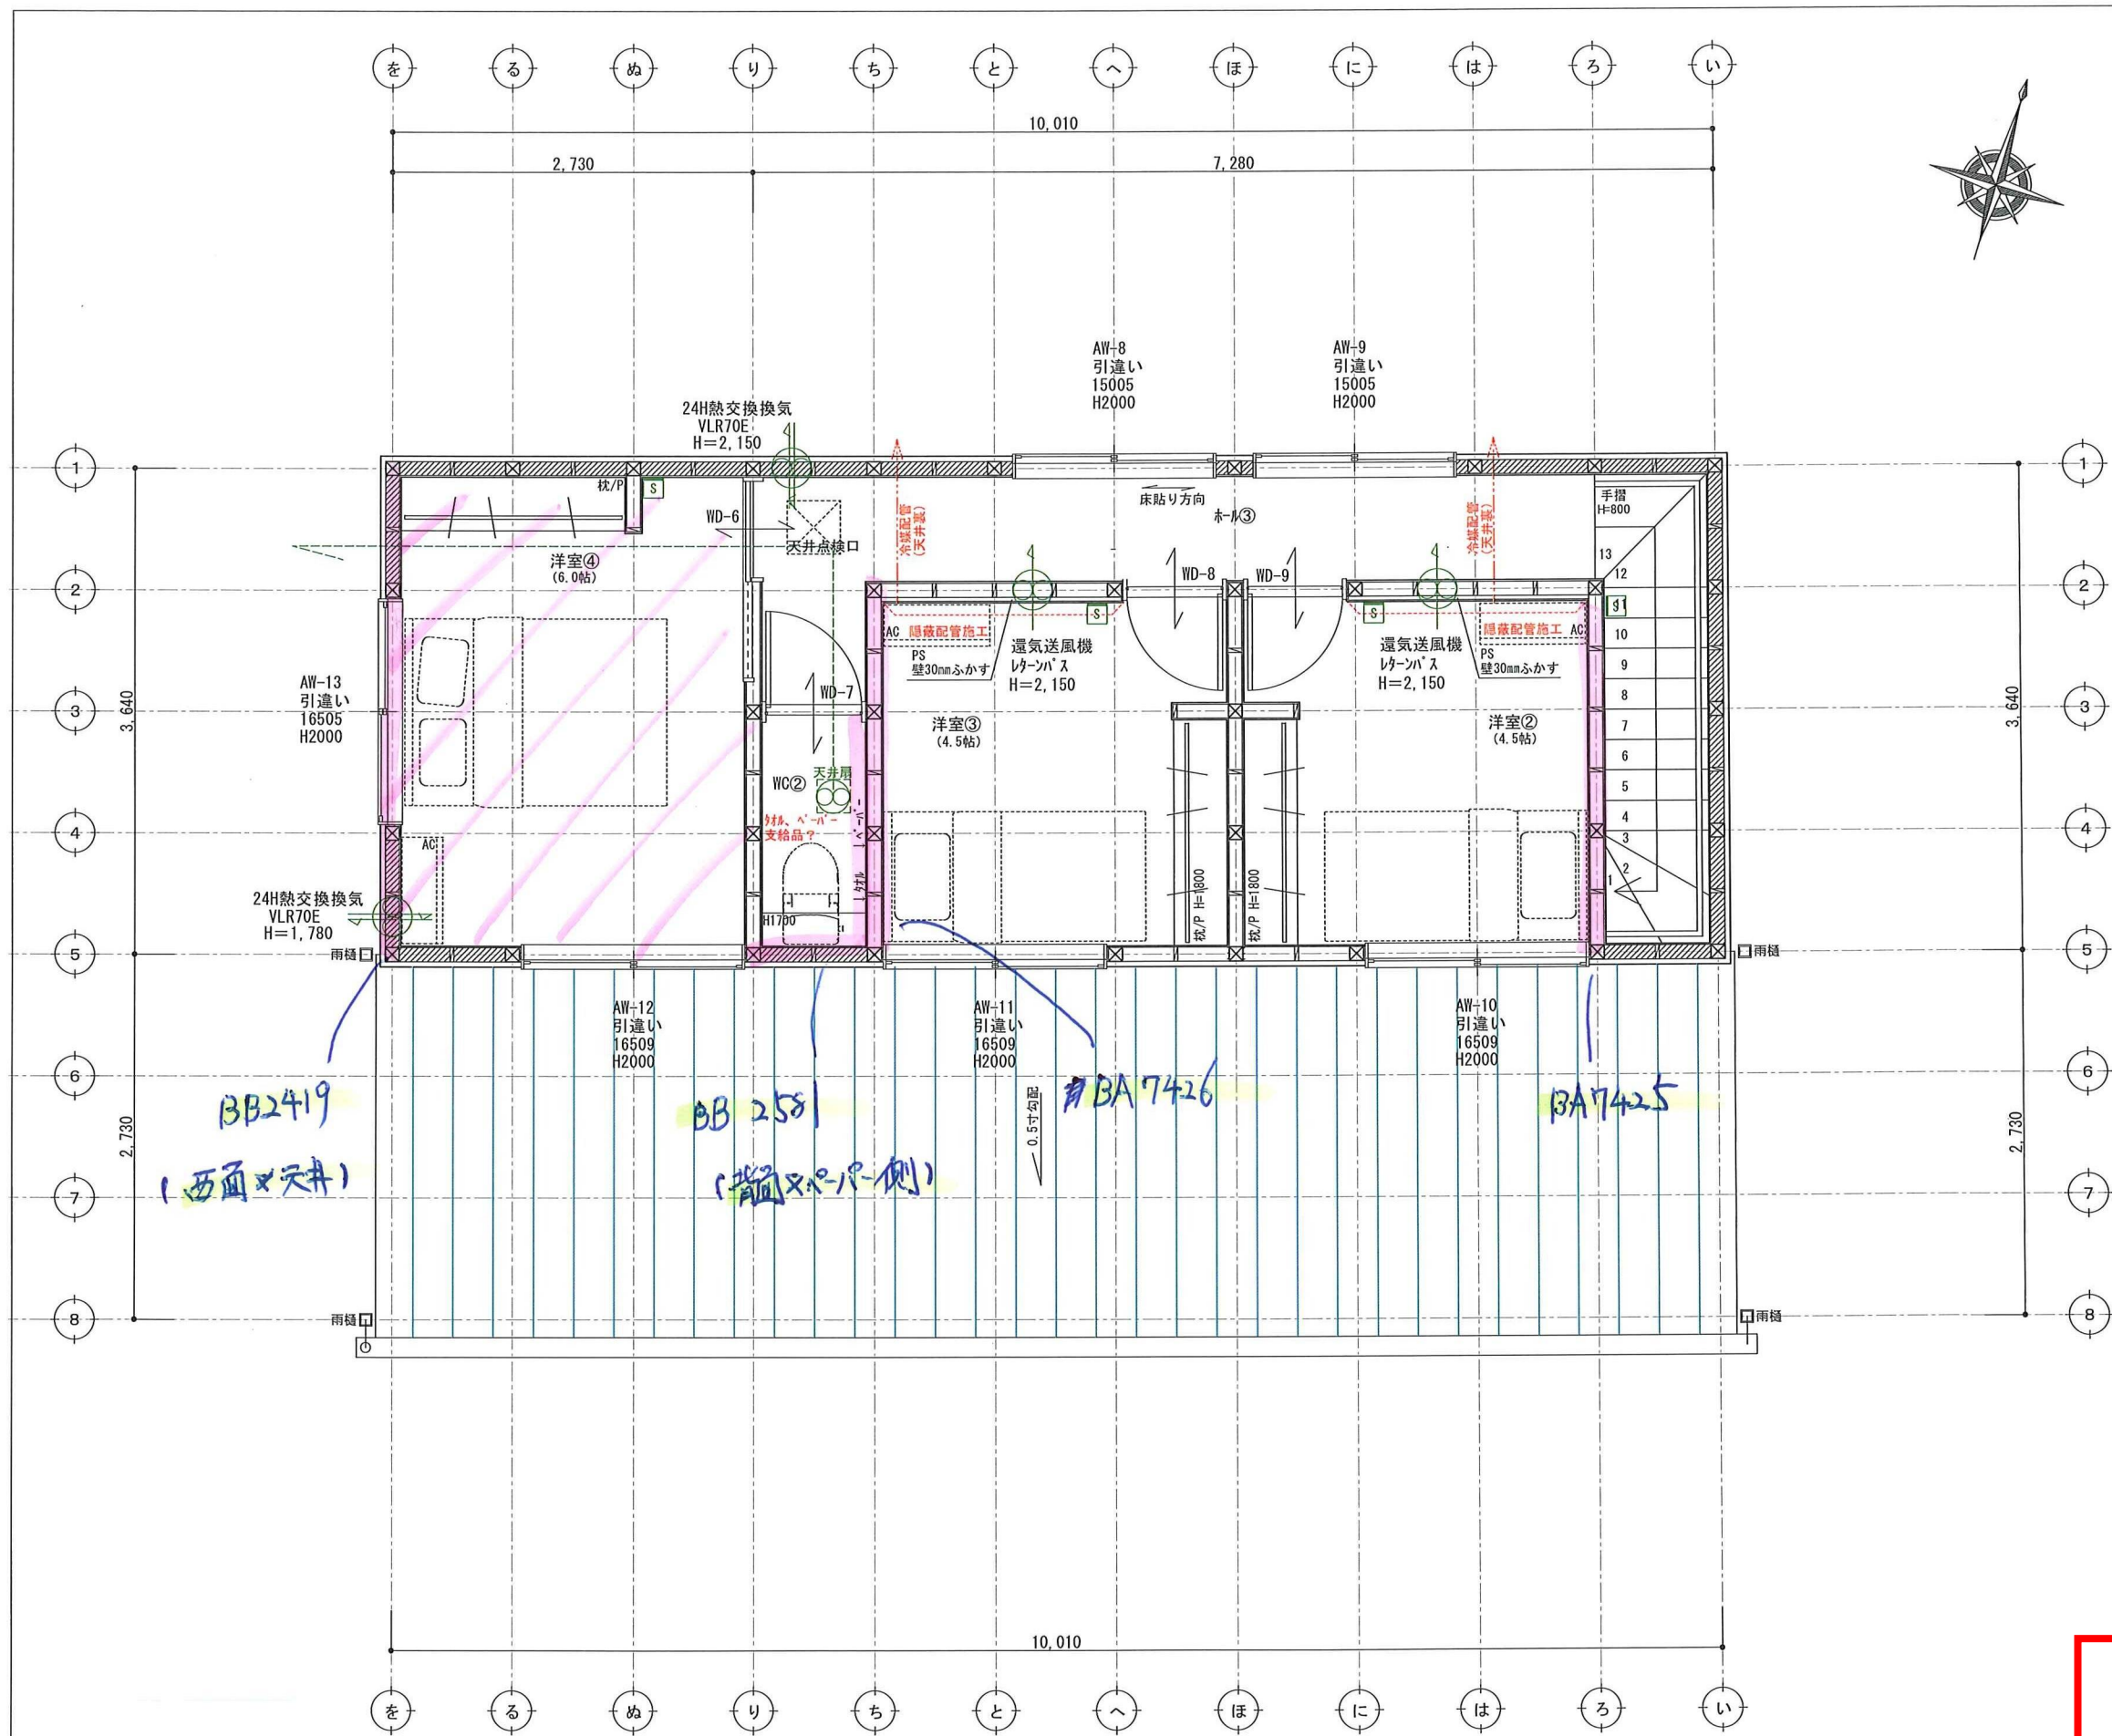

G2

壁付 住宅用火災報知器			数量
[H] 熱感知	熱感知器	電池式(単独型)	
		露出型	
壁付 住宅用火災報知器			数量
[S] 煙感知	煙感知器	電池式(単独型)	4
		露出型	

- ※ 煙感知器は壁・梁より600mm以上離す
壁に取付ける場合、
天井から150mm以上500mm以内離す
換気扇・エアコン吹出口から1500mm以上離す
- ※ 全室LED照明とする。
- ※ 標準天井高さ2,400
- ※ 特記無きガラスは型ガラス

* 凡例

- ☒ 管柱 (105×105)
- ◀▶ K'f'ha (3.30倍 FRM-0641)
- △ 片筋違い (2.00倍 45×90)
(例 左:柱脚 右:柱頭)
- ⊠ たすき掛筋違い (4.00倍 45×90)
- 構造用合板 (2.70倍)
(t=9 タカ EXN(ハ))
- ◻ 床点検口
- ⊠ 天井点検口
- ⊕ 換気扇
- ⊕ 熱交換換気扇VLR-70

アドバンスシリーズ	
スマートデザイン (外部)	
凡例	
①	コンセント 1ヶ所
②	コンセント 2ヶ所
③	コンセント 3ヶ所
①ET	コンセント1ヶ所接地ターミナル付
②ET	コンセント2ヶ所接地ターミナル付
①WP	コンセント 防水型
②WP	エアコン用コンセント
③WP	200V用コンセント
④WP	防雨入替プレート
●	スイッチ
●3	3路スイッチ
●4	4路スイッチ
⊠	直結電源
⊕	テレビ取出口
⊕TEL	電話取出口 (テレホンガイド)
⊕LAN	LAN取出口 (テレホンガイド)
⊕	壁照明
⊕	リモコン (給湯関係・ルフロ)
⊕	メーター
⊕	分電盤
⊕	チャイム

- ※ACコンセント天井付け
- ※TVアンテナ工事
- ※スイッチはFL+1100、コンセントはFL+200

決定図

訂正	浜岡一級総合設計事務所 一級建築士事務所 静岡県知事登録第 (10)2441 号 一級建築士 大臣登録第 365879 号 西原利昌	PG HOUSE ピージーハウス	株式会社 LIFEFUND InDesign office 一級建築士事務所 事務所登録 (2)第7595号 一級建築士登録 第179770号 鈴木 達男 〒432-8023 静岡県浜松市中央区鶴江3丁目70番23号	年月日 2025. 12. 21 縮尺 1/50	件名 平松久美江様邸 新築工事 図名 2階平面図	設計 IC 工事 青島 図番 3-2
----	--	---------------------	--	-----------------------------------	-----------------------------------	-----------------------------------