

■ 仕 様				■ HEAT20 G2	
断熱工事		■ 床:カネライトフォーム t90		■ 土間床等の外周:スタイロフォームAT t50	
		■ 壁:アクアフォームLITE吹付 t90		■ 天井:アクファフォームLITE吹付 t220	
床下換気		■ 基礎パッキン JOTO (玄関・UB周り:気密基礎パッキン)			
防虫防蟻		■ 土壌処理・木部 ガントナーMC			
■ 外 部 仕 上 表				■ 22条地域	
部位		仕上・仕様・メーカー		色番・品番	
屋根		■ ガルバリウム鋼板(t0.35)UK立平 ニスクカラーPro GH 軒先通気金物 日本住環境株式会社【REV-15】		GHK01 Sブラック	
パラペット笠木		■ なし			
破風・鼻隠		■ なし			
雨樋	(軒樋)	■ Panasonic サーフeskエアFS-I型		ブラック	
	(縦樋)	■ Panasonic S30角樋		ブラック	
軒天	屋根軒	■ なし			
	ポーチ軒	■ ニチハ軒天5 木目調 910×1820×5		ライト	
	バルコニー軒	■ なし			
オーバーハング水切り		■ ガルバリウム鋼板 ※外壁合わせ JOTO:HF-A3550		ブラック	
外壁	通気金物(15mm)	■メイン	Kmewエクセレージ・シマンフラット	光セラ	ソイル チタン マルーンブラック
	※下地面材:タイガーEXハイパー	■アクセントA	なし		
	防火認定 PC030BE-4028	■アクセントB	なし		
玄関ポーチ		■ 床 玄関に同じ			
基礎		■ 立上り巾木: モルタル刷毛引き			
基礎水切り金物		■ JOTO鋼板製 防鼠材付き水切り JOTO:WMF-N35		ブラック	
バルコニー	床・内壁	■ なし		-	
	笠木	■ なし			
外部建具		■ LIXIL EW(アルゴンガス高遮熱仕様LowEトリプルガラス クリア) ・SD、TSは、メーカー設定によるが、オペレーターハンドル優先とする ・オペレーター付サッシの場合は固定網戸とする ・グレモンハンドル式サッシの場合は可動網戸とする		外観 ブラック 内観 シャドーオークforDesign ※樹脂パッキン・網戸付	
シャッター		■ なし			
軒天通気金物					
玄関扉		■ LIXIL ジエスタ2 K2仕様 LIXILファミロック タグキー×5 (電池式)		ドア型: M17 型 ドア色: ラスティックオーク ハンドル: S型ハンドル 色 ブラック	
外部物干し金物		■			
換気フード	■ 局所換気扇(トイレ 浴室 キッチンフード) 防火ダンパー無		外気フード: ブラック		
	■ ダクトレス熱交換換気システム (日本スティーベル株式会社) VLR-70E 防火ダンパー無		外気フード: B ブラック 室内パネル マッドグレー		

■ 構 造 概 要					
基礎	■ RCベタ基礎コンクリート				
通し柱・管柱	■ 構造用集成材 105×105		間柱	■ 集成材	
土台	■ 桧 105×105	大引き	■ 桧 90*90	筋交い	■ 構造用製材 火打梁 ■ 鋼製火打(当社基準により米松あり)
桁・梁	■ 構造用製材及び集成材		制震装置	■ Kダンパー (株)アイ・エム・エー	
■ 設 備 装 着 品					
住宅設備	部位	メーカー	商品名 ※ 詳細は見積り、プレゼン参照	見積りNo.	(日付)
	キッチン	LIXIL	■ ES	見積り番号 : M25129577942-010-2	(日付) 2026.02.16
	バックカウンタ ※オプション	LIXIL	■ ES L1800(W900スライドストッカー×2)	見積り番号 : M25129577942-010-3	(日付) 2026.02.16
	浴室	LIXIL	■ AX1616 PGハウス標準仕様	見積り番号 : M25129577942-010-1	(日付) 2026.02.16
	1Fトイレ	LIXIL	■ ベーシアシャワートイレ 白 ● タオル掛け: なし(支給品取付) タンク手洗 無し ● 紙巻き器: CF-AA64H/WA(2連)	見積り番号 : M25129577942-010-5	(日付) 2026.02.16
	2Fトイレ	LIXIL	■ ベーシアシャワートイレ 白 ● タオル掛け: KF-AA70D(リング) タンク手洗 無し ● 紙巻き器: CF-AA64H/WA(2連)	見積り番号 : M25129577942-010-6	(日付) 2026.02.16
	洗面台	LIXIL	■ EV W1200(D500タイプ) その他 トールキャビネット450(標準タイプ) ● タオル掛け: KF-AA71D(バー)	見積り番号 : M25129577942-010-4	(日付) 2026.02.16
給排水設備	給湯器	■ エコキュート460L Panasonic Sシリーズ スタンダードモデル 追い焚きフルオート※在庫限り			
	排水	■ 合併浄化槽 5人槽 ポンプアップ無			
	外水栓	■ 1 カ所 (平面図参照)	■ 外部立栓柱: 散水栓ボックス MS-21ユニット【前澤化成工業】		
	外部ガーデンパン	■ 無し			
	その他	■ 洗濯機用単水栓: 緊急止水弁付 ■ 洗濯機用排水: トラップ金物(標準) ■ 排水さや管(長期優良住宅仕様)			
ガス配管設備	■ なし (配置図・平面図参照) ■ガス使用器具				
電気設備	インターホン	■ パナソニック VL-SE31XL			
	TVアンテナ	■ UHF + BS・110度CS／CSアンテナ [2K・4K・8K対応] ■ブラック ※電波状況によりホワイトになる可能性あり			
	エアコン	■ 設置場所: 洋室②、洋室③			
	ソーラー	■ あり(Qセルズ) 12 枚 5.28 KW Re.RISE-G3 440 (1722×1134×30)			
	※標準搭載	※メーカーのモデルチェンジ等で後継品に変更される可能性あり ■ 屋外パワコン エネルギーマネジメントシステム Cube J			
その他					
決定図					

決定図

	浜 岡 一 級 総 合 設 計 事 務 所 一級建築士事務所 静岡県知事登録第 (10)2441 号 一級建築士 大臣登録第 365879 号 西原利昌	 PG HOUSE	株式会社 LIFEFUND InDesign office 一級建築士事務所 事務所登録 (2)第7595号 一級建築士登録 第179770号 鈴木 達男 〒432-8023 静岡県浜松市中央区鴨江3丁目70番23号	年 月 日 2026.2.15		件名 平松久美江 様邸 新築工事			設計	IC	工務	図 番	
				縮尺		図面 仕上表 1			酒井		青島	1-1	

内 部 仕 上 表 （壁下地:石膏ボード12.5mm/天井下地:9.5mm）※脱衣室:床合板特類 下地									
階		床	巾木	壁	品番	廻 縁	天 井	品番	特記事項
1F	ポーチ	LIXILパセオ300/PSO-FN 2							
	玄関	LIXILパセオ300/PSO-FN 2	ライン巾木(W)	ビニルクロス	SLP-385	突付	ビニルクロス	SLP-385	
	ホール①	フロアタイルt2.3 サンゲツIS-2071	ライン巾木(W)	ビニルクロス	SLP-385	突付	ビニルクロス	SLP-385	
	LDK	フロアタイルt2.3 サンゲツIS-2071	ライン巾木(W)	ビニルクロス	SLP-385	突付	ビニルクロス	SLP-385	アクセントクロスあり
	ホール②	フロアタイルt2.3 サンゲツIS-2071	ライン巾木(W)	ビニルクロス	SLP-385	突付	ビニルクロス	SLP-385	
	脱衣ランドリー	フロアタイルt2.3 サンゲツIS-2071	ライン巾木(W)	ビニルクロス	SLP-385	突付	ビニルクロス	SLP-385	
	WC①	フロアタイルt2.3 サンゲツIS-2071	H40ソフト巾木W97	ビニルクロス	SLP-385	突付	ビニルクロス	SLP-385	
	洋室①	イタ銘木フロアーラスティックt12 ウォールナット3P	H40ソフト巾木W97	ビニルクロス	SLP-385	突付	ビニルクロス	SLP-385	
2F	ホール③	イタ銘木フロアーラスティックt12 ウォールナット3P	ライン巾木(W)	ビニルクロス	SLP-385	突付	ビニルクロス	SLP-385	
	洋室②	イタ銘木フロアーラスティックt12 ウォールナット3P	ライン巾木(W)	ビニルクロス	SLP-385	突付	ビニルクロス	SLP-385	アクセントクロスあり
	洋室③	イタ銘木フロアーラスティックt12 ウォールナット3P	ライン巾木(W)	ビニルクロス	SLP-385	突付	ビニルクロス	SLP-385	アクセントクロスあり
	洋室④	イタ銘木フロアーラスティックt12 ウォールナット3P	ライン巾木(W)	ビニルクロス	SLP-385	突付	ビニルクロス	SLP-385	アクセントクロスあり
	WC②	フロアタイルt2.3 サンゲツIS-2071	ライン巾木(W)	ビニルクロス	SLP-385	突付	ビニルクロス	SLP-385	
物入・収納・CL etc		※接続する部屋と同仕様とする							



上 框 ※	■ LIXILラシッサS 上框のみ30×150 色: クリエダーク
階 段	■ LIXIL KA 階段 ササラ: プレシャスホワイト
KA階段で対応できない場合、オプション	段板: クリエダーク 蹴込板: プレシャスホワイト
ラウンド手摺: ブラック	手摺金物: ブラック
にてラシッサS階段	上段框: クリエダーク 長尺笠木156: LIXIL なし
窓 枠	■ LIXIL スマート10(玄関以外) 色 プレシャスホワイト ※浴室ドア枠 フクビ3方枠 [ホワイト]
キッチン笠木 カウンター	■ ゴム集成カウンター(オスモカラー) 色 707 ウォールナット 形状 L型(ジョイント加工) t=30
天井点検口	■ 天井アルミ点検口枠 450角 TAN45BW フクビ化学工業 ミルキーホワイト
床下収納庫	■ 高気密型床下点検口断熱型 SPF-R6060 城東テクノ 収納付 (脱衣室) ライトグレー(LG)
トイレ棚	■ 1,2階トイレ D250 アートランバー棚(ダークグレー)
室内物干し金物	■ 川口技研SPC型 1セット
LDK-カウンター	■ ゴム集成カウンター(オスモカラー) 色 707 ウォールナット t=25
下足入 プッシュタイプ	■ ラフィス 色 ブラック サイズ: W1600 D400※OP品 形状: プッシュタイプ

支給品	■ 無し
備考	※付框は(30×150)プレシャスホワイト

内 部 建 具 表								
LIXIL		建具色： ブラック		枠色 ： 扉同色		※その他、下記特記による		
ラフィス		把手 ： スクエアL (アイアンブラック) 丁番 固定枠(156) 外付戸当り ガイドピン床色合せ 引戸のみ上吊Wソフトモーション						
階	No	室名	形式	枠外W サイズ	デザイン	枠色	特記事項	
				枠外H サイズ	建具色	把手		
1	1	脱衣ランドリー	片開き戸	—	RAA	—	明り窓・表示錠	
	WD			2400		—		
	2	脱衣ランドリー	片引き戸	—	RAA		明り窓・表示錠	
	WD			2400				
	3	CL①	折れ戸	—	RAA	—	ノンレールタイプ	
	WD			1800		—		
	4	LDK	アウトセット片引	—	RAA	—		
	WD			2400		—		
	5	CL②	折れ戸	—	RAA	—		
	WD			2200		—		
	6	洋室①	片引き戸	—	RAA	—		
	WD			2400		—		
	7	WC①	片引き戸	—	RAA	—	明り窓・表示錠	
	WD			2400		—		
2	8	洋室④	片引き戸	—	RAA	—		
	WD			2400		—		
	9	WC②	片開き戸	—	RAA	—	明り窓・表示錠	
	WD			2400		—		
	10	洋室③	片開き戸	—	RAA	—		
	WD			2400		—		
	11	洋室②	片開き戸	—	RAA	—		
	WD			2400		—		
	決定図							

浜松市浜名区新原地内

G2

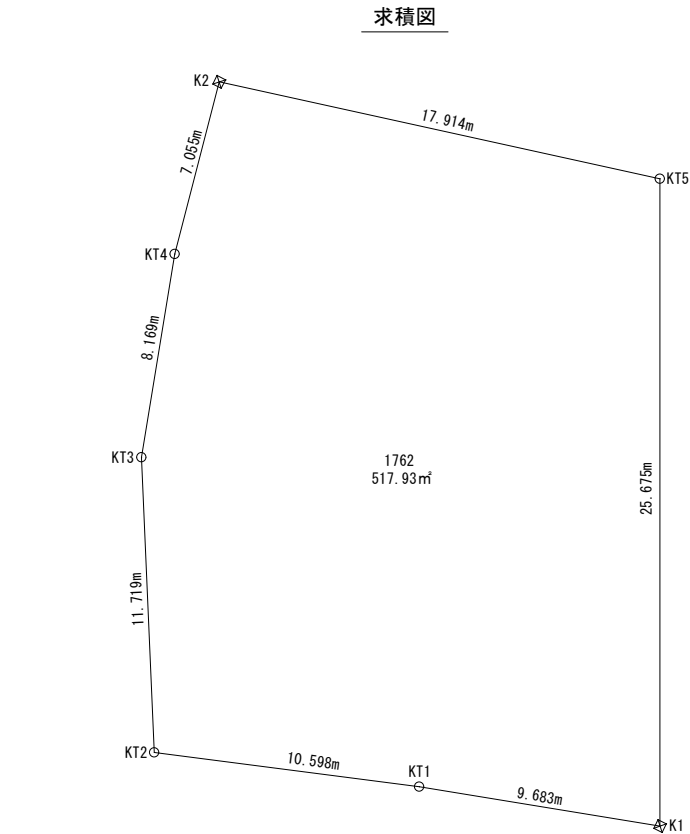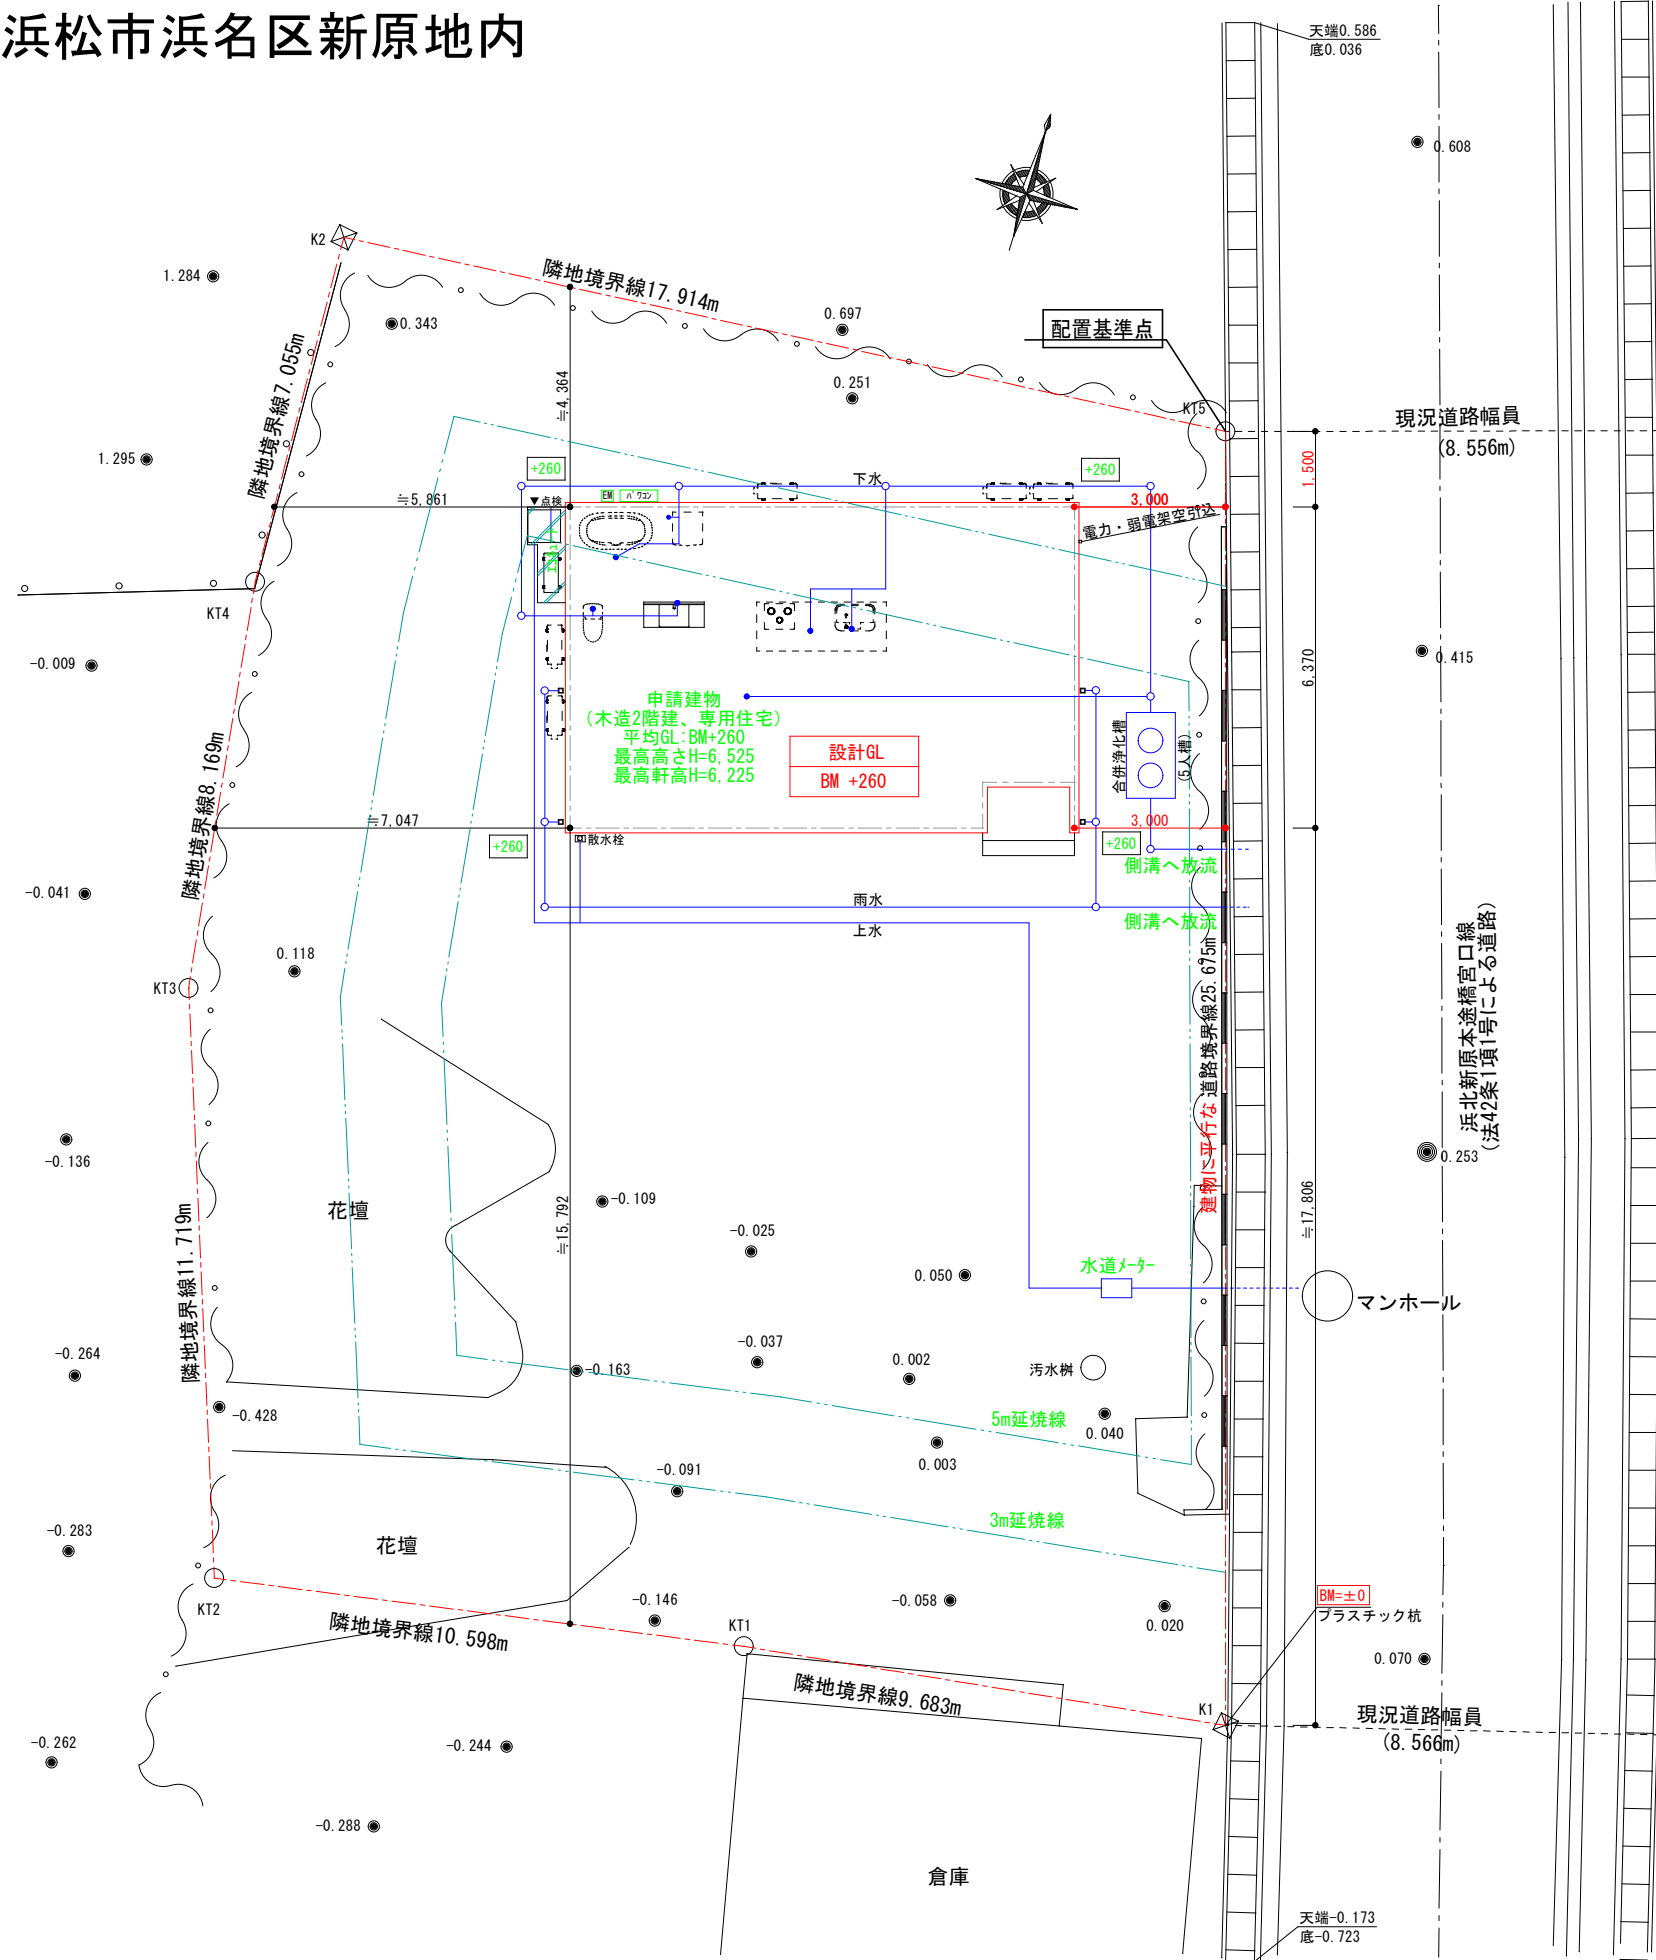


求積表

地 番	1 1762			
NO	X _n	Y _n	Y _{n+1} - Y _{n-1}	X _n × (Y _{n+1} - Y _{n-1})
K1	-4.780	6.839	25.828	-123.457840
KT1	-14.018	9.744	6.429	-90.121722
KT2	-24.013	13.268	-6.699	160.863087
KT3	-29.744	3.045	-18.017	535.897648
KT4	-32.191	-4.749	-14.686	472.757026
K2	-33.701	-11.641	-11.335	382.000835
KT5	-16.346	-16.084	18.480	-302.074080
合 計			1035.864954	
合 計 面 積			517.9324770	
地 積			517.93	

トータル面積表		(㎡)
敷地面積		517.93
建築面積		63.76
床面積 1階		62.11
2階		36.43
延床面積		98.54
建築率	(63.76/517.93) × 100	12.32%
容積率	(98.54/517.93) × 100	19.03%

道路斜線制限については、明らかに適合する。
隣地斜線制限については、明らかに適合する。
平均地盤面について
申請建物の周囲の平均地盤面高さをBM+260とする。
盛土規制法の許可対象となる工事なし。


決定図

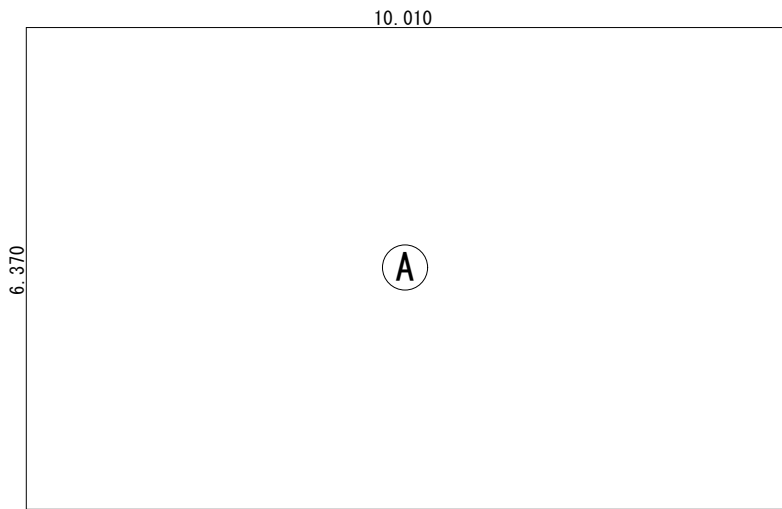

建築面積求積図 S=1/100

建築面積求積表


番号	計算式	(m)	面積 (㎡)
Ⓐ	10.010 × 6.370		63.7637
合計			63.7637 63.76 (19.2坪)

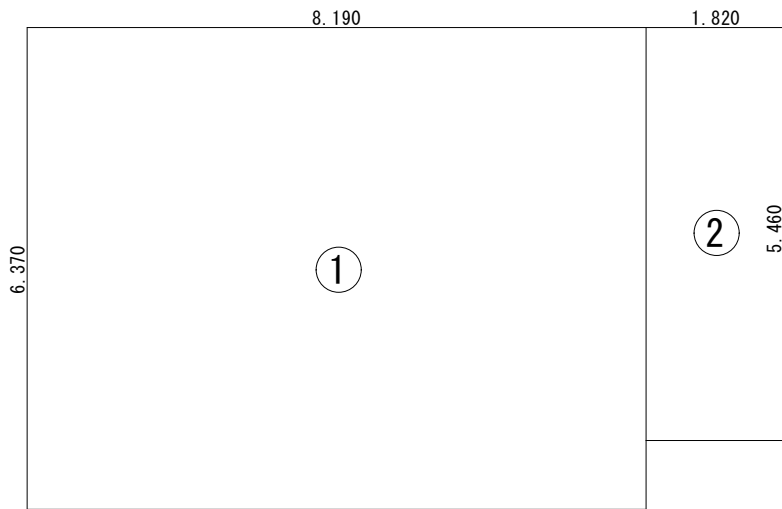

1階床面積図 S=1/100

1階床面積求積表

番号	計算式	(m)	面積 (㎡)
①	8.190 × 6.370		52.1703
②	1.820 × 5.460		9.9372
合計			62.1075 62.10 (18.7坪)

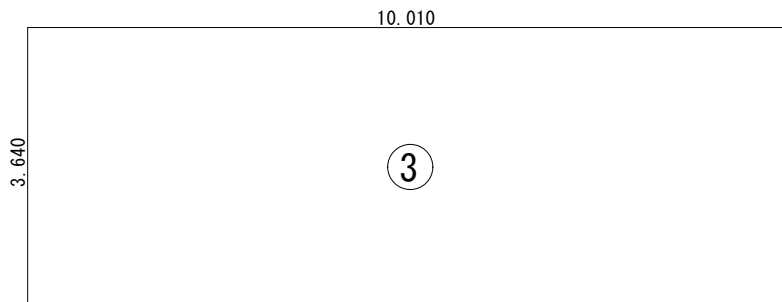

2階床面積図 S=1/100

2階床面積求積表


番号	計算式	(m)	面積 (㎡)
③	10.010 × 3.640		36.4346
合計			36.4346 36.43 (11.0坪)

延べ床面積表

	番号	(m)	面積 (㎡)
1階床面積	① ②		62.10
2階床面積	③		36.43
合計			98.54 (29.8坪)

決定図

G2

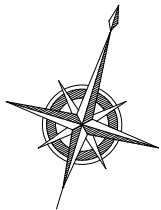

壁付け 住宅用火災報知器			数量
H	熱感知器	電池式(単独型)	
	熱感知器	露出型	
壁付け 住宅用火災報知器			数量
S	煙感知器	電池式(単独型)	4
	煙感知器	露出型	

- ※ 煙感知器は壁・梁より600mm以上離す
壁に取付ける場合、
天井から150mm以上500mm以内離す
換気扇・エアコン吹出口から1500mm以上離す
- ※ 全室LED照明とし、居室においては調光
制御、非居室においては人感センサーを
採用する。
- ※ 標準天井高さ2,400
- ※ 特記無きガラスは型ガラス


* 凡例

- ☒ 管柱 (105×105)
- ▶ Kダクト (3.30倍 FRM-0641)
- △ 片筋違い (2.00倍 45×90)
(例 左:柱脚 右:柱頭)
- ⊗ たすき掛筋違い (4.00倍 45×90)
- 構造用合板 (2.70倍)
(t=9 9材 EXハイバー)
- ◻ 床点検口
- ⊗ 天井点検口
- ⊗ 換気扇
- ⊗ 熱交換換気扇VLR-70



アドバンスシリーズ			
スマートデザイン (外部)			
凡例	1	コンセント	1ヶ所
2	コンセント	2ヶ所	
3	コンセント	3ヶ所	
1ET	コンセント1ヶ所接地ターミナル付		
2ET	コンセント2ヶ所接地ターミナル付		
WP	コンセント	防水型	
WP	エアコン用コンセント		
WP	200V用コンセント		
WP	防雨入線プレート		
●	スイッチ		
●	3路スイッチ		
●	4路スイッチ		
●	直結電源		
●	テレビ取出口		
●	TEL 電話取出口 (テレホンガイド)		
●	LAN LAN取出口 (テレホンガイド)		
●	壁照明		
●	リモコン (給湯関係・ルフロ)		
●	メーター		
●	分電盤		
●	チャイム		

- ※ACコンセント天井付け
- ※TVアンテナ工事
- ※スイッチはFL+1100、コンセントはFL+200

決定図

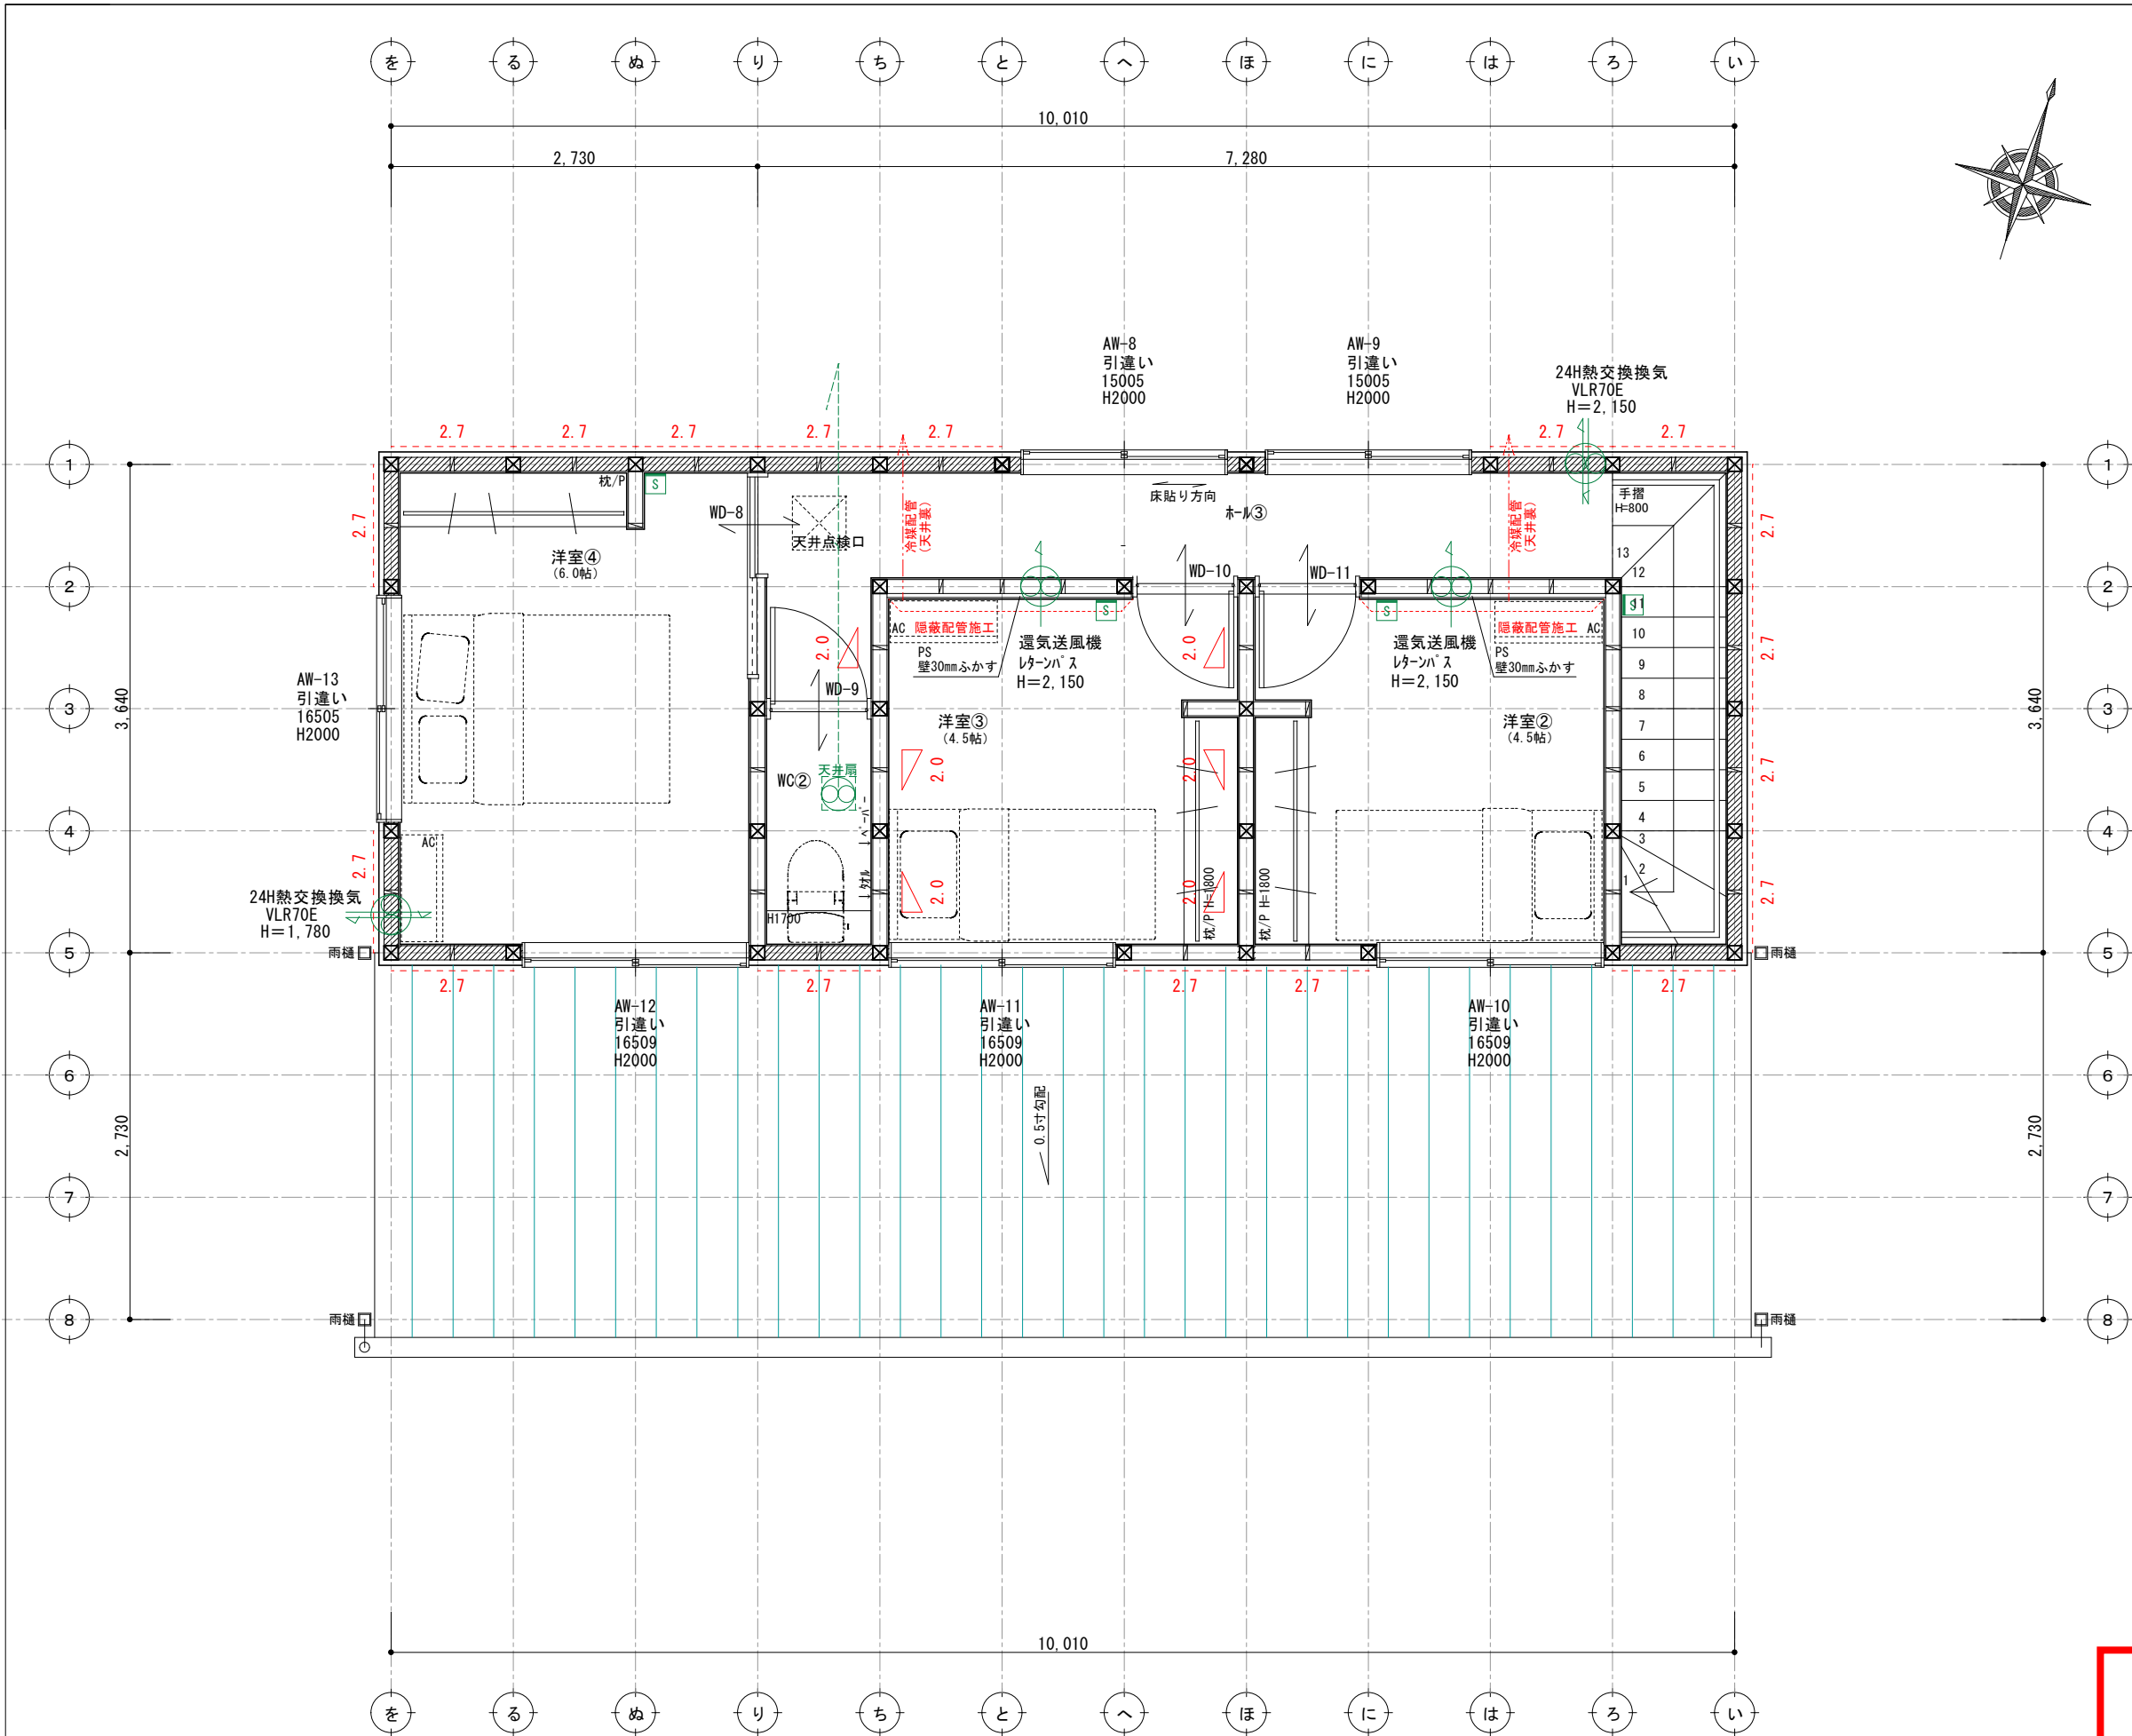



GX住宅 (Cube J付)
太陽光あり

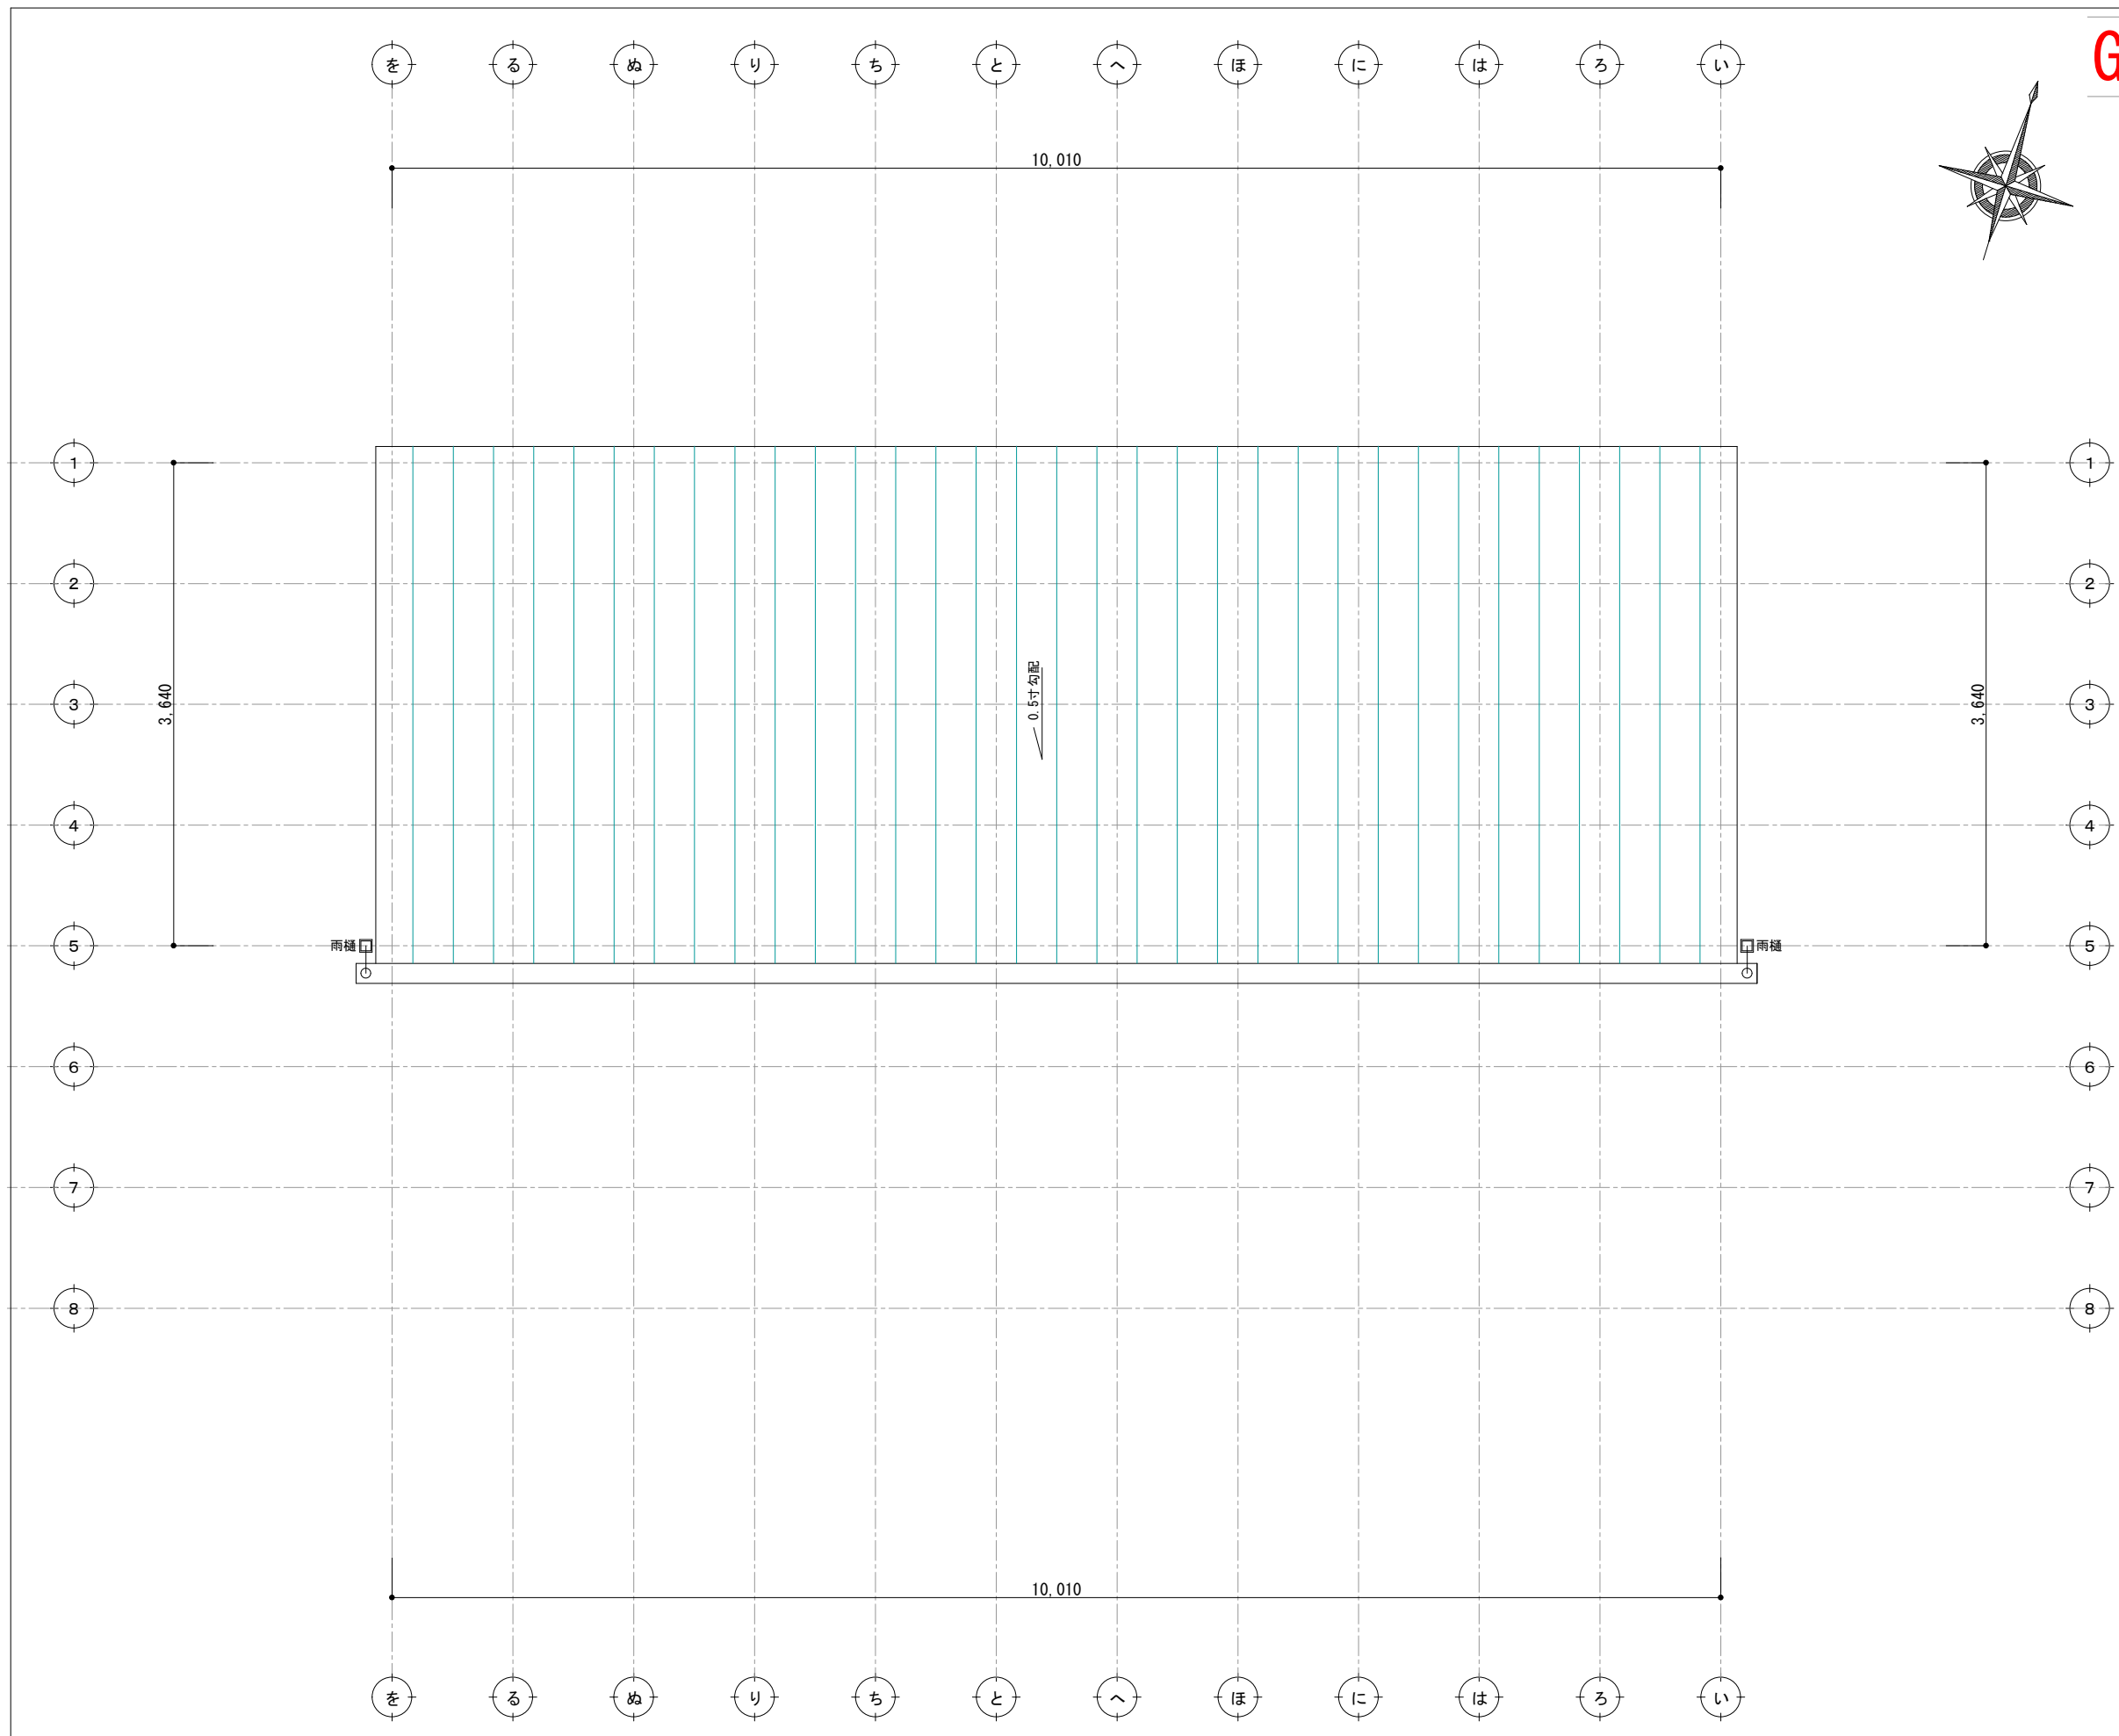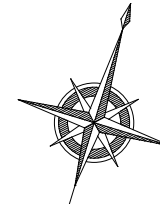

決定図


訂正	浜岡一級総合設計事務所 一級建築士事務所 静岡県知事登録第 (10)2441 号 一級建築士 大臣登録第 365879 号 西原利昌		株式会社 LIFEFUND InDesign office 一級建築士事務所 事務所登録 (2) 第7595号 一級建築士登録 第179770号 鈴木 達男 〒432-8023 静岡県浜松市中央区鴨江3丁目70番23号	年月日 2026. 2. 15	件名 平松久美江様邸 新築工事		設計	IC	工事	図番
				縮尺 1/100	図名 屋根伏図		酒井		青島	3-3

G2

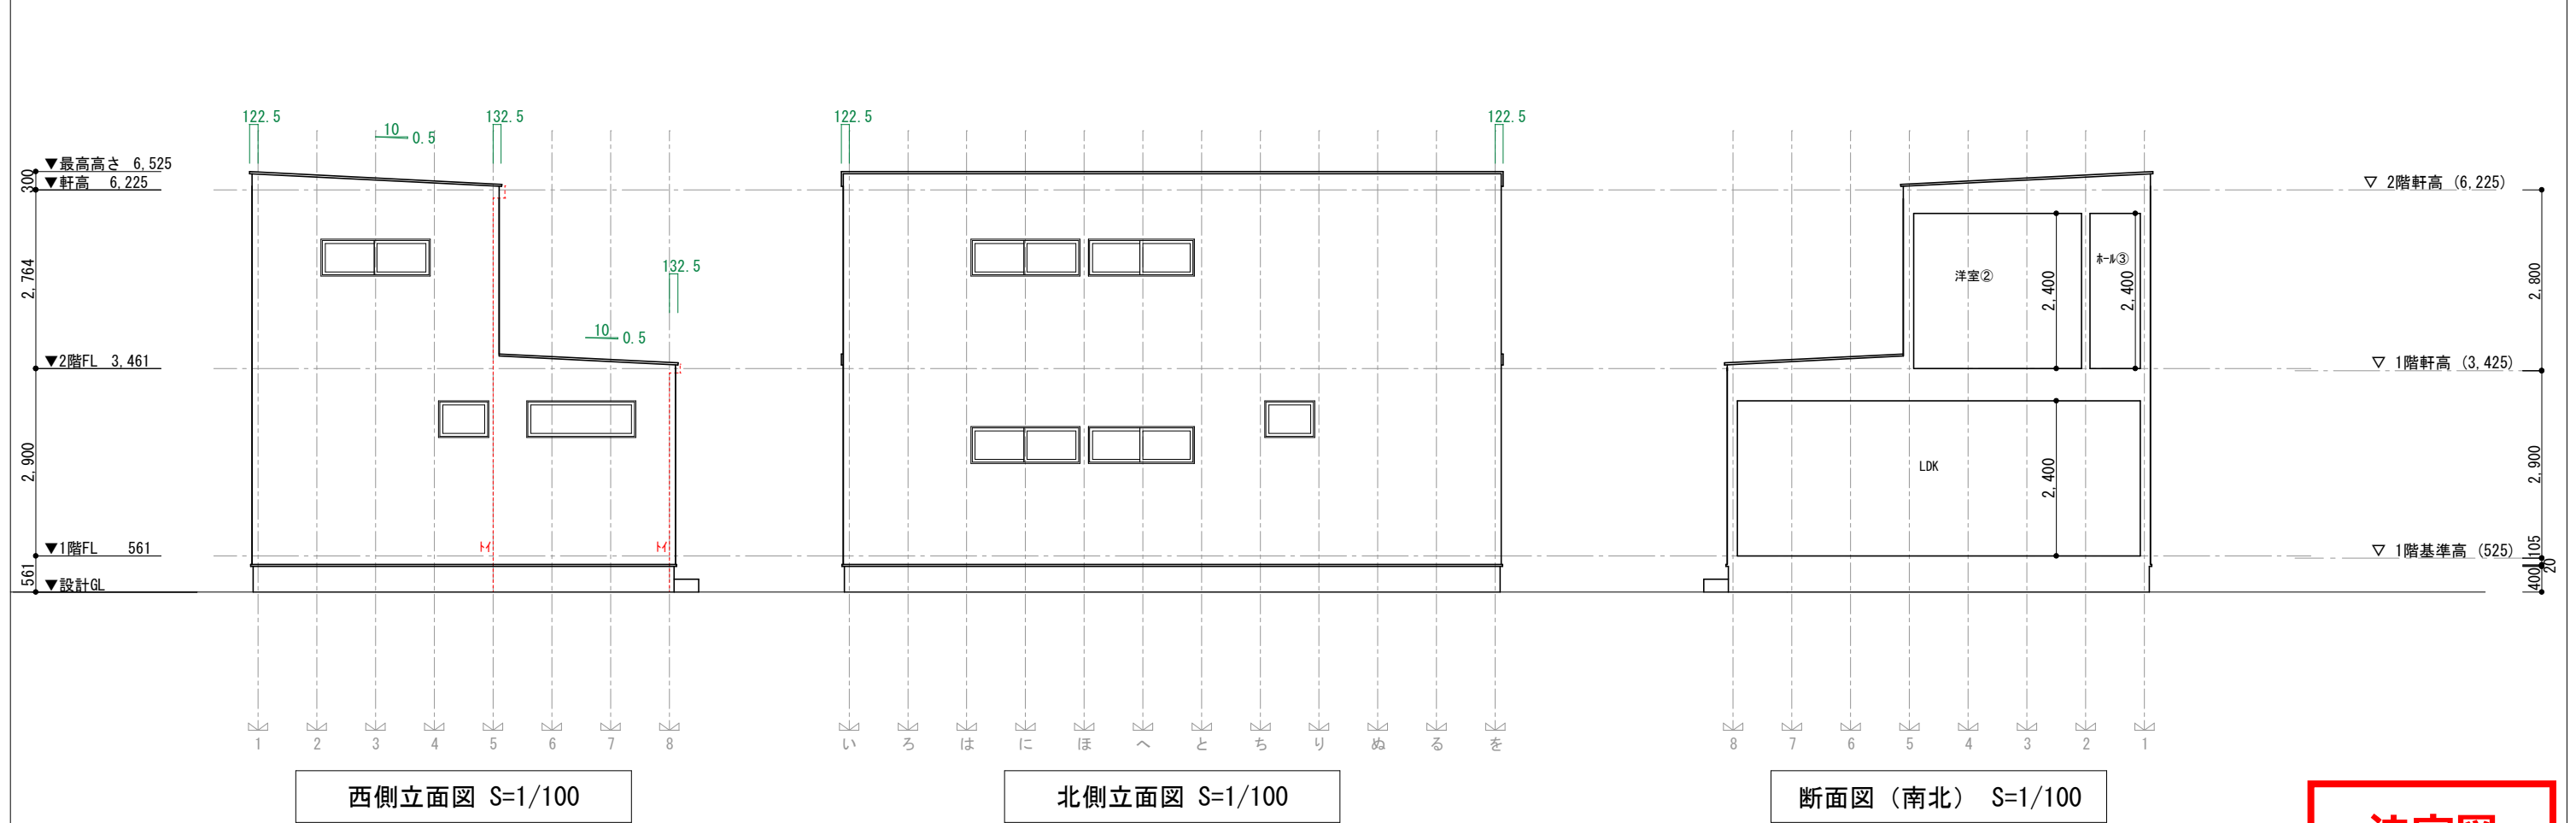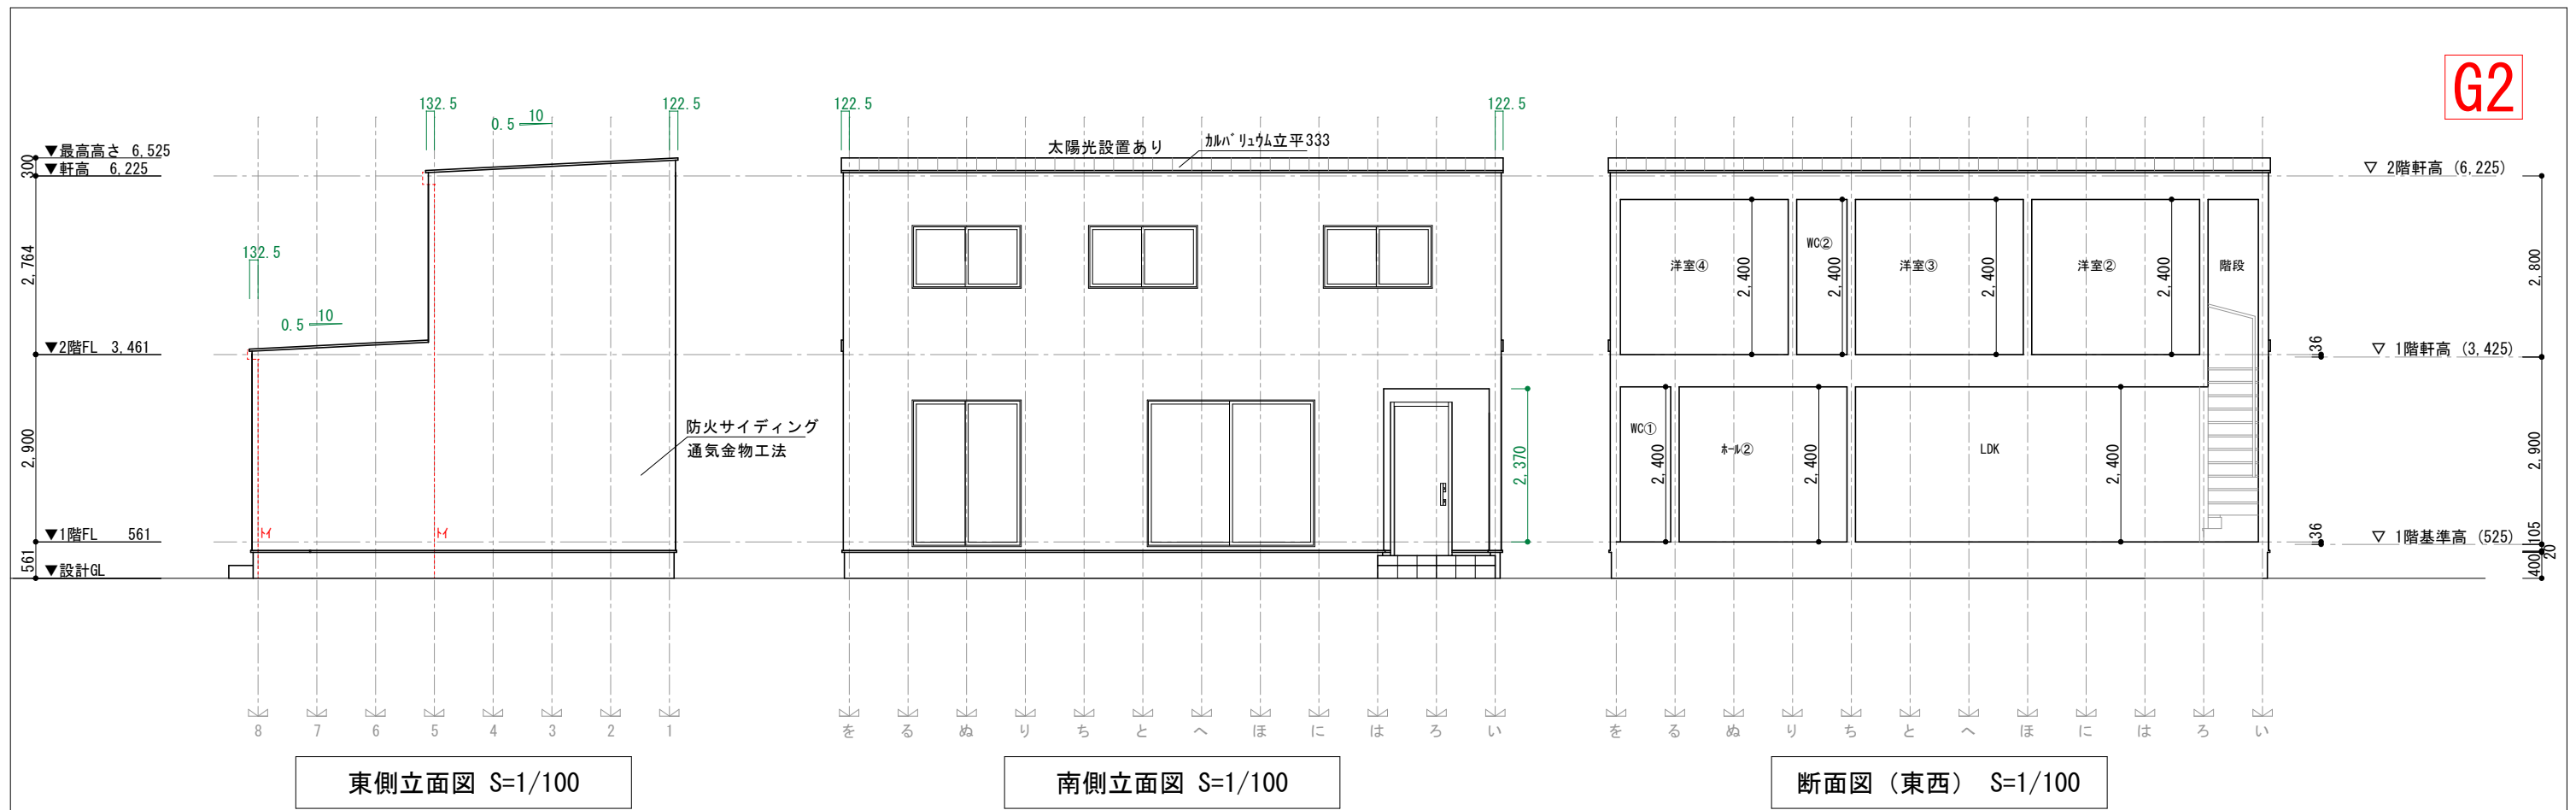

決定図


訂 正	浜 岡 一 級 総 合 設 計 事 務 所			株式会社 LIFEFUND InDesign office 一級建築士事務所	年 月 日	件 名		設計	IC	工事	図 番
	一級建築士事務所 静岡県知事登録第 (10)2441 号				2026.2.15	平松久美江様邸 新築工事					
	一級建築士 大臣登録第 365879 号 西原利昌				縮 尺	図 名					
		1/100			立面図						
		事務所登録 (2) 第7595号 一級建築士登録 第179770号 鈴木 達男 〒432-8023 静岡県浜松市中央区鴨江3丁目70番23号									

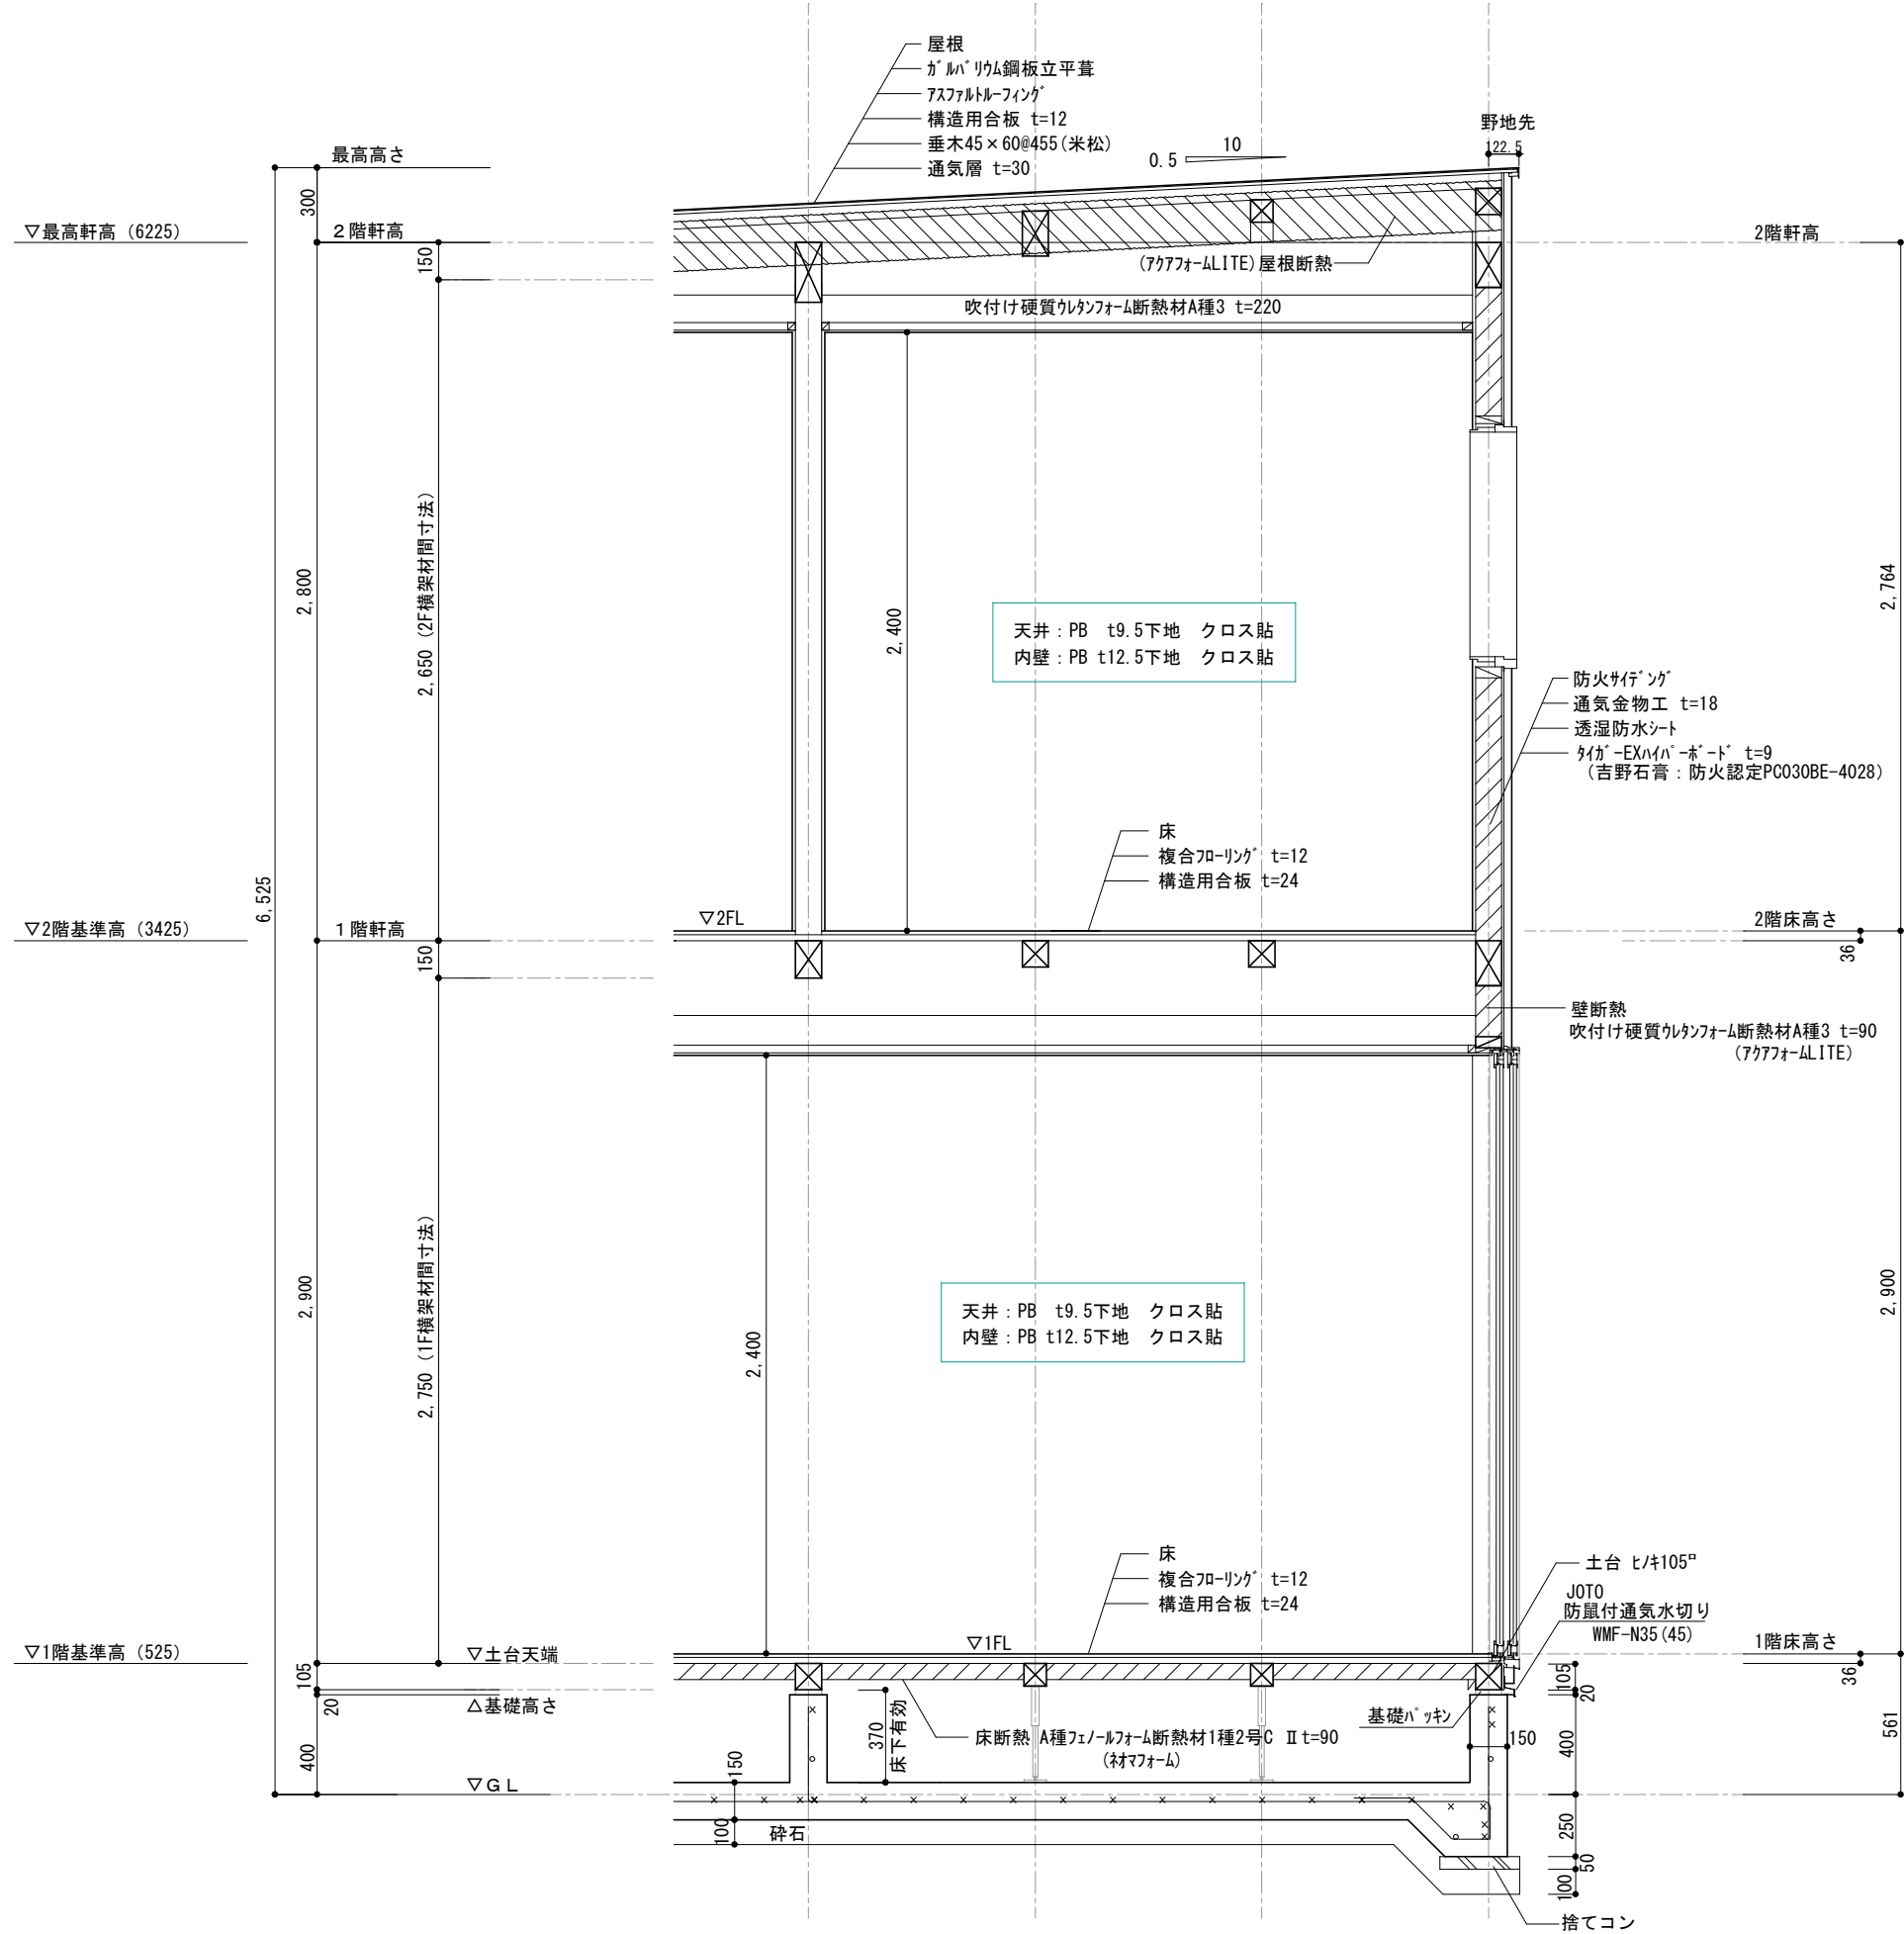


決定図

訂正	浜岡一級総合設計事務所 一級建築士事務所 静岡県知事登録第 (10)2441 号 一級建築士 大臣登録第 365879 号 西原利昌		株式会社 LIFEFUND InDesign office 一級建築士事務所 事務所登録 (2)第7595号 一級建築士登録 第179770号 鈴木 達男 〒432-8023 静岡県浜松市中央区鴨江3丁目70番23号	年月日 2026.2.15	件名 平松久美江様 邸新築工事		設計 10	工事	図番
				縮尺 1/30	図名 矩計図		酒井	青島	5


Λ

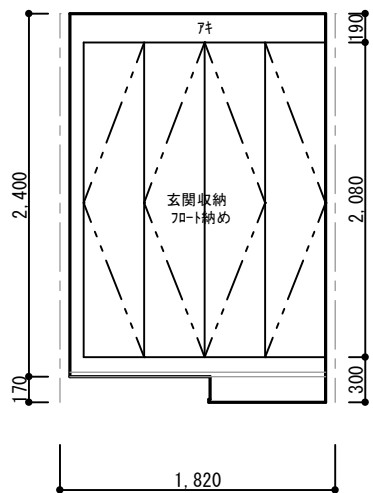


玄関 東面

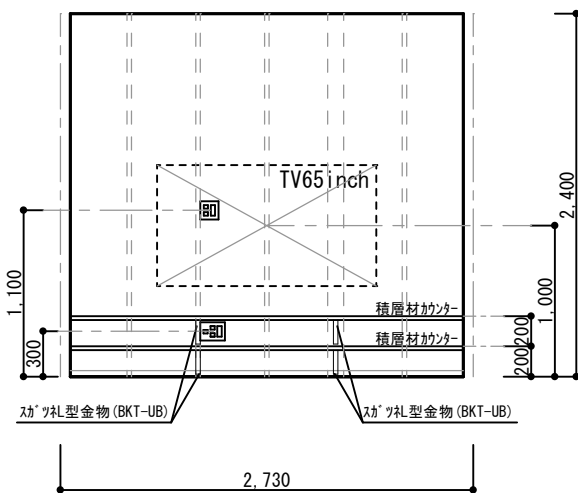


LDK 西面

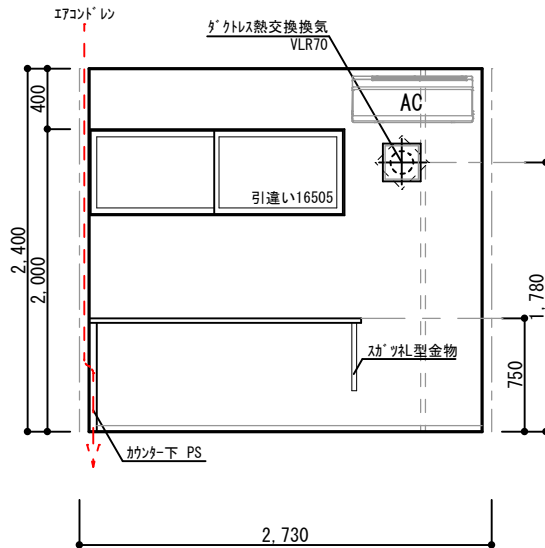


LDK 西面

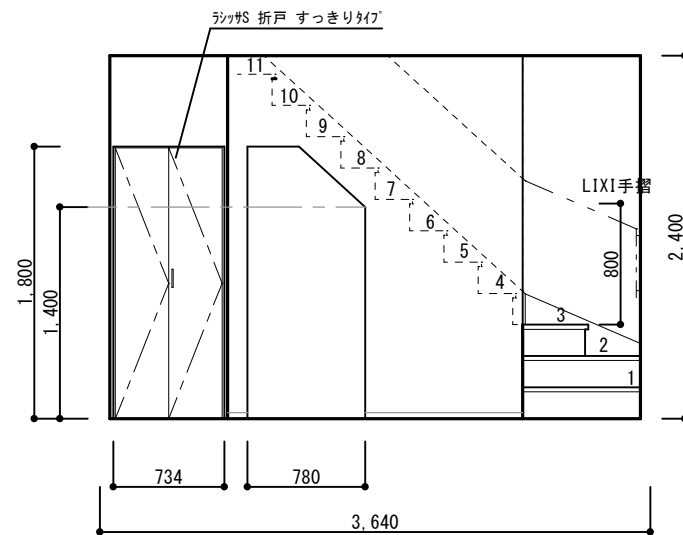


LDK 東面

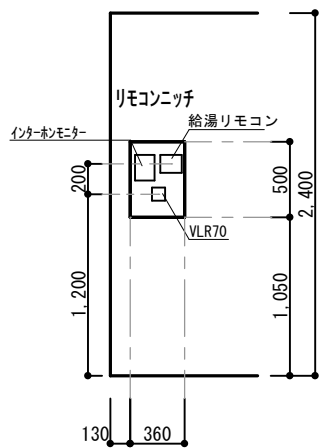

LDK 南面

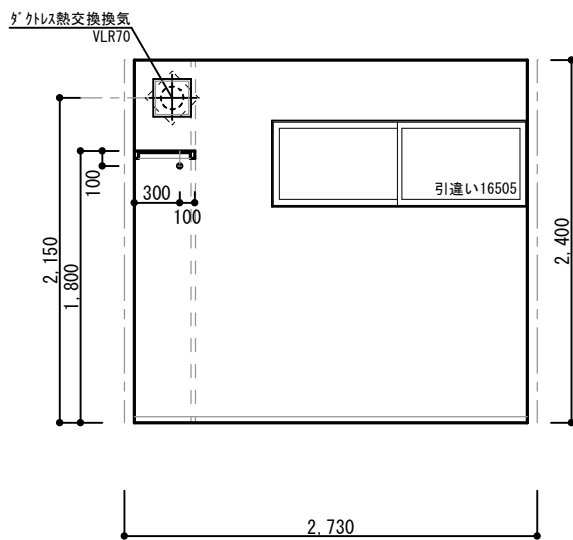

洋室③ 南面



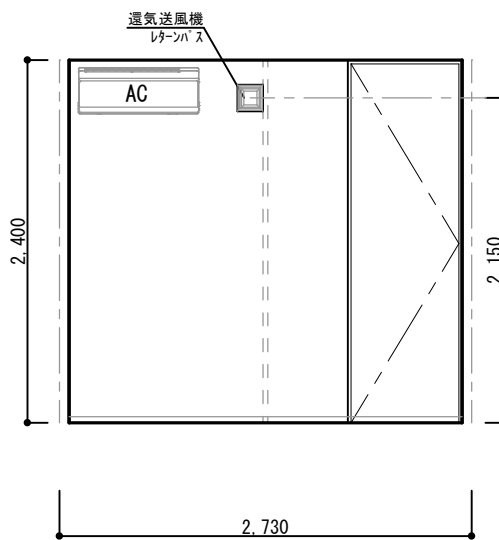


洋室③ 北面

決定図

訂正	浜岡一級総合設計事務所 一級建築士事務所 静岡県知事登録第 (10)2441 号 一級建築士 大臣登録第 365879 号 西原利昌	LIFEFUND PG HOUSE	株式会社 LIFEFUND InDesign office 一級建築士事務所 事務所登録 (2) 第7595号 一級建築士登録 第179770号 鈴木 達男 〒432-8023 静岡県浜松市中央区鴨江3丁目70番23号	年月日 2026.2.15 縮尺 1/50	件名 平松久美江様 新築工事 図名 展開図-1		設計 酒井	IC	工事 青島	図番 6-1
----	--	----------------------	---	--------------------------------	----------------------------------	--	----------	----	----------	-----------

G2

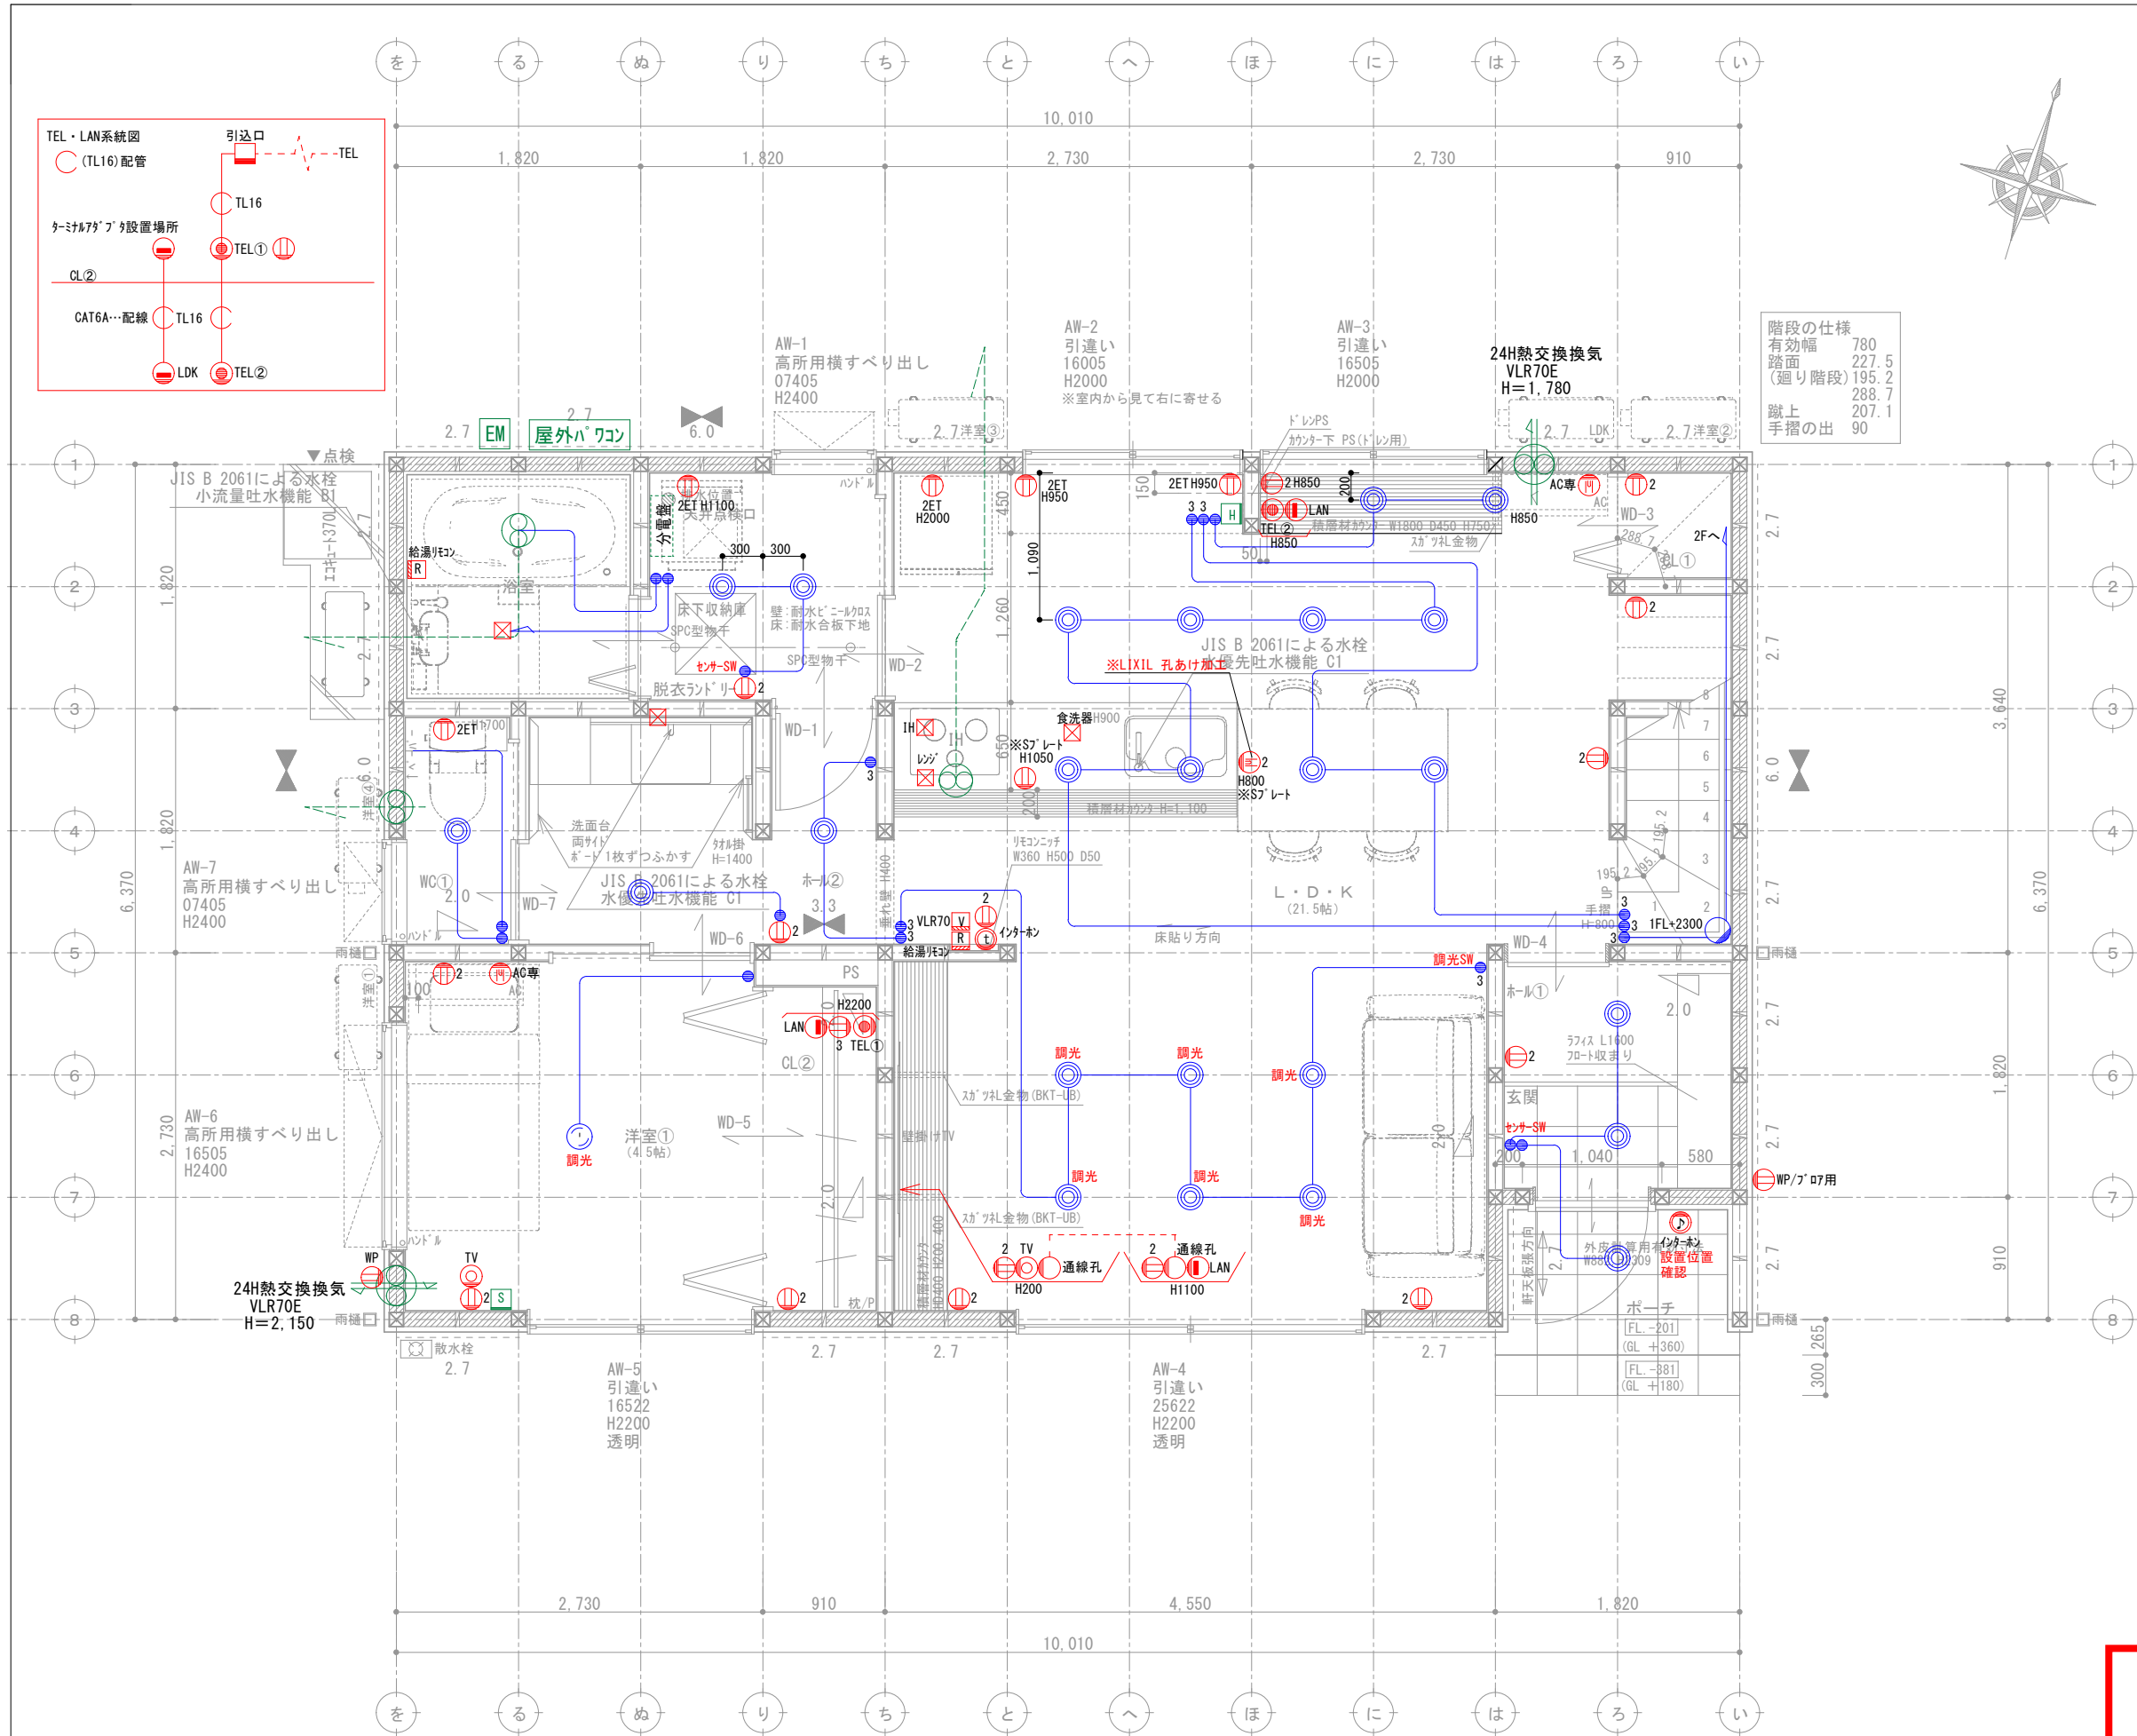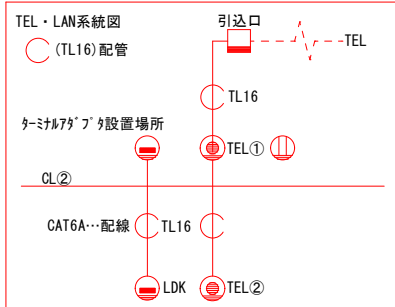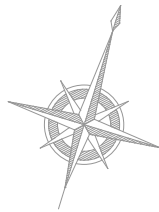

階段の仕様

有効幅	780
路面	227.5
(廻り階段)	195.2
蹴上	288.7
手摺の出	207.1
	90

壁付け	住宅用火災報知器	数量
H	熱感知器	電池式(単独型)
熱感知	露出型	1

壁付け	住宅用火災報知器	数量
S	煙感知器	電池式(単独型)
煙感知	露出型	1

- ※ 煙感知器は壁・梁より600mm以上離す
壁に取付ける場合、
天井から150mm以上500mm以内離す
換気扇・エアコン吹出口から1500mm以上離す
- ※ 全室LED照明とし、居室においては調光
制御、非居室においては人感センサーを
採用する。
- ※ 標準天井高さ2,400
- ※ 特記無きガラスは型ガラス

* 凡例

- 管柱 (105×105)
- K&P (3.30倍 FRM-0641)
- 片筋違い (2.00倍 45×90)
(例 左:柱脚 右:柱頭)
- たすき掛筋違い (4.00倍 45×90)
- 構造用合板 (2.70倍)
(t=9 9材 EXハイバ)
- 床点検口
- 天井点検口
- 換気扇
- 熱交換換気扇VLR-70


アドバンスシリーズ

スマートデザイン (外部)

凡例	1	コンセント	1ヶ所
	2	コンセント	2ヶ所
	3	コンセント	3ヶ所
	1ET	コンセント1ヶ所接地ターミナル付	
	2ET	コンセント2ヶ所接地ターミナル付	
	WP	コンセント 防水型	
		エアコン用コンセント	
		200V用コンセント	
	WP	防雨入線プレート	
		スイッチ	
	3	3路スイッチ	
	4	4路スイッチ	
		直結電源	
	TV	テレビ取出口	
	TEL	電話取出口 (テレホンガイド)	
	LAN	LAN取出口 (テレホンガイド)	
		壁照明	
	R	リモコン (給湯関係・ルフロ)	
	WH	メーター	
	t	分電盤	
		チャイム	

- ※ACコンセント天井付け
- ※TVアンテナ工事
- ※スイッチはFL+1100、コンセントはFL+200

決定図

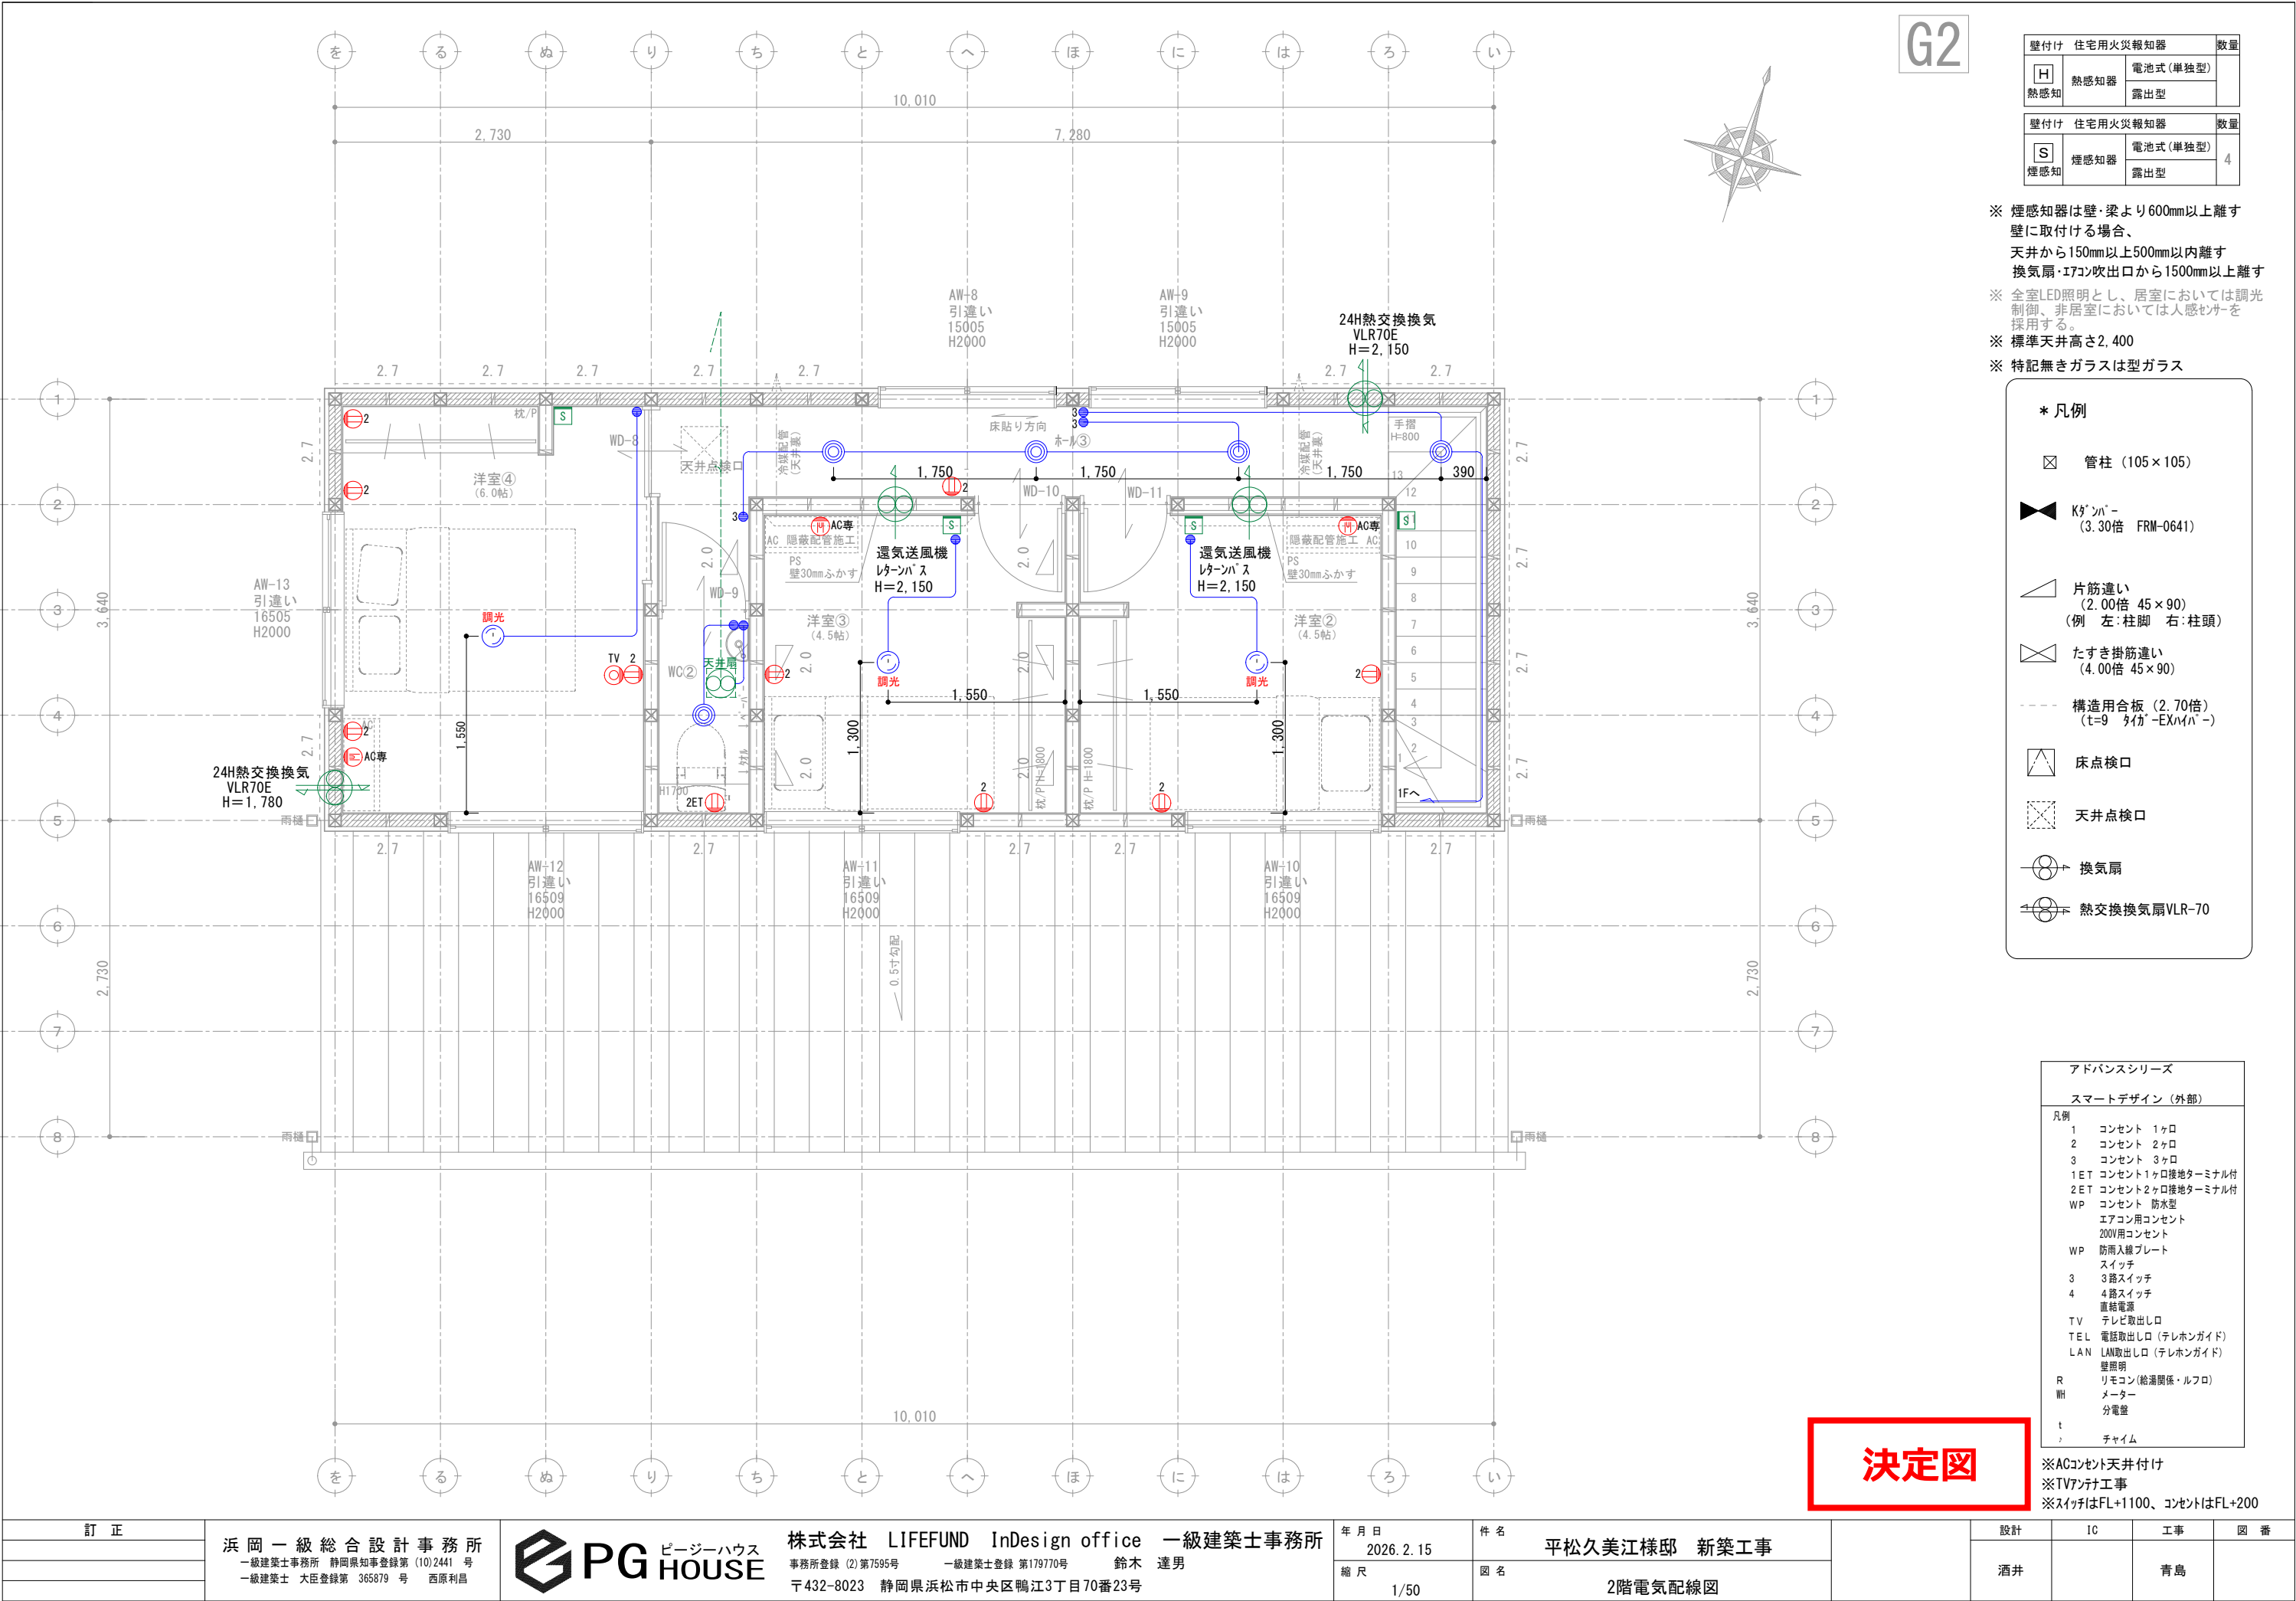

G2

壁付け 住宅用火災報知器			数量
H 熱感知	熱感知器	電池式(単独型)	
		露出型	
壁付け 住宅用火災報知器			数量
S 煙感知	煙感知器	電池式(単独型)	4
		露出型	

- ※ 煙感知器は壁・梁より600mm以上離す
壁に取付ける場合、
天井から150mm以上500mm以内離す
換気扇・エアコン吹出口から1500mm以上離す
- ※ 全室LED照明とし、居室においては調光
制御、非居室においては人感センサーを
採用する。
- ※ 標準天井高さ2,400
- ※ 特記無きガラスは型ガラス

* 凡例

管柱 (105×105)

Kタンパー (3.30倍 FRM-0641)

片筋違い (2.00倍 45×90)
(例 左:柱脚 右:柱頭)

たすき掛筋違い (4.00倍 45×90)

構造用合板 (2.70倍)
(t=9 3枚付 EXハイパー)

床点検口

天井点検口


換気扇

熱交換換気扇VLR-70

アドバンスシリーズ			
スマートデザイン (外部)			
凡例			
1	コンセント	1ヶ所	
2	コンセント	2ヶ所	
3	コンセント	3ヶ所	
1ET	コンセント1ヶ所接地ターミナル付		
2ET	コンセント2ヶ所接地ターミナル付		
WP	コンセント	防水型	
	エアコン用コンセント		
	200V用コンセント		
WP	防雨入線プレート		
	スイッチ		
3	3路スイッチ		
4	4路スイッチ		
	直結電源		
TV	テレビ取出口		
TEL	電話取出口 (テレホンガイド)		
LAN	LAN取出口 (テレホンガイド)		
	壁照明		
R	リモコン (給湯関係・ルフロ)		
WH	メーター		
	分電盤		
t	チャイム		

- ※ACコンセント天井付け
- ※TVアンテナ工事
- ※スイッチはFL+1100、コンセントはFL+200

決定図

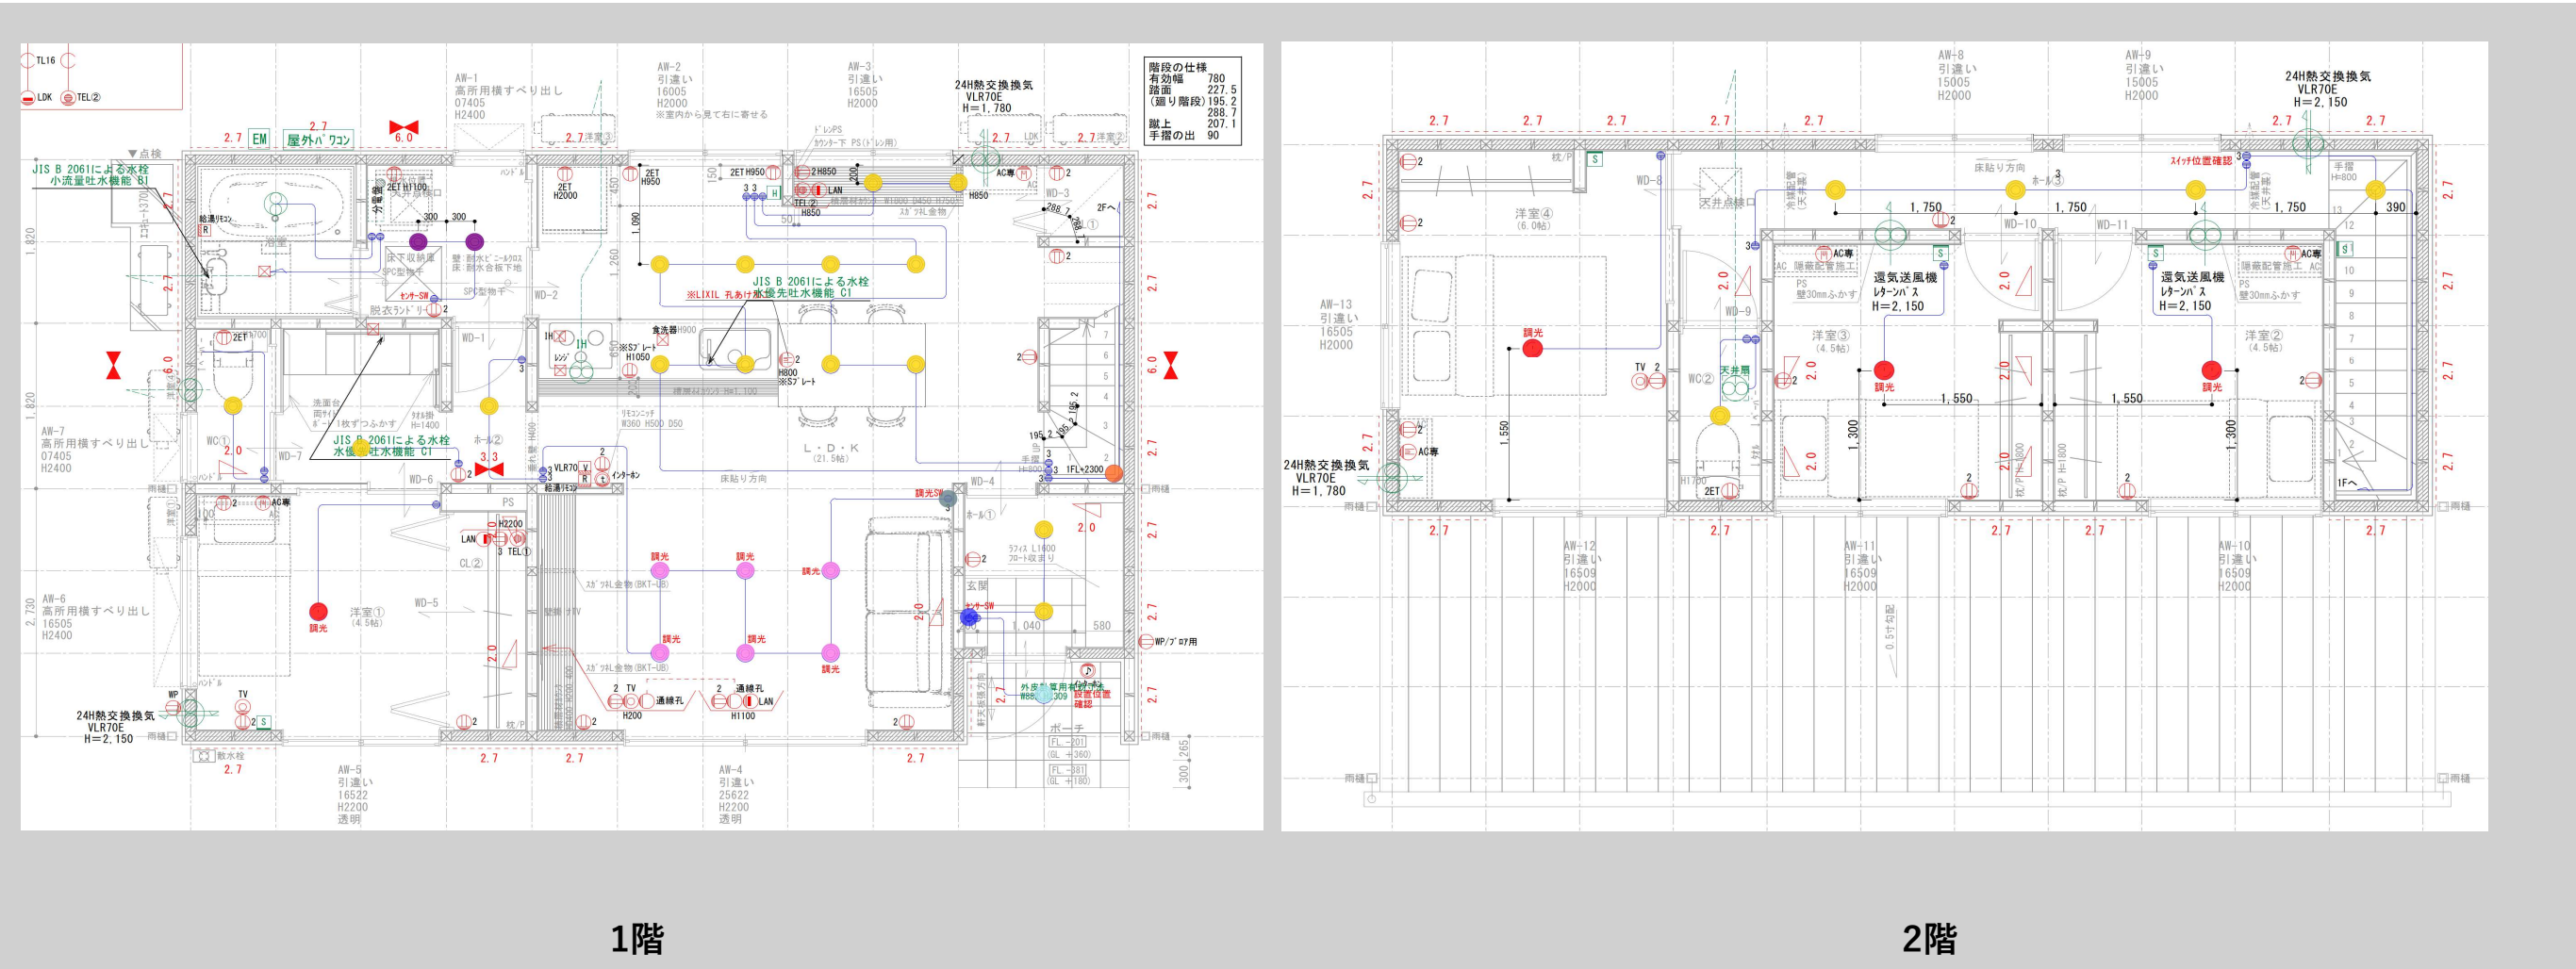

ドアホン：VL-SE31XL
(Panasonic)

内部SW：アドバンス
マットグレー

外部：スマートデザインシリーズ
ブラック

ポーチ灯
×1
センサー付きダウンドライ
DDL_6259YB

基本照明ダウンドライ
×20
DDL_6132YB

脱衣ランドリー
×2
ダウンドライ
DDL_6132AB

LDK
×6
調光ダウンドライ
DDL_6032YBG


洋室①②③④
×4
シーリングライト
DCL_42121

階段
×1
ブラケット
DBK_41131YE


玄関
×1
センサー-SW
WTA_14119H

LDK
×1
調光SW
WTA_57583HK

決定図

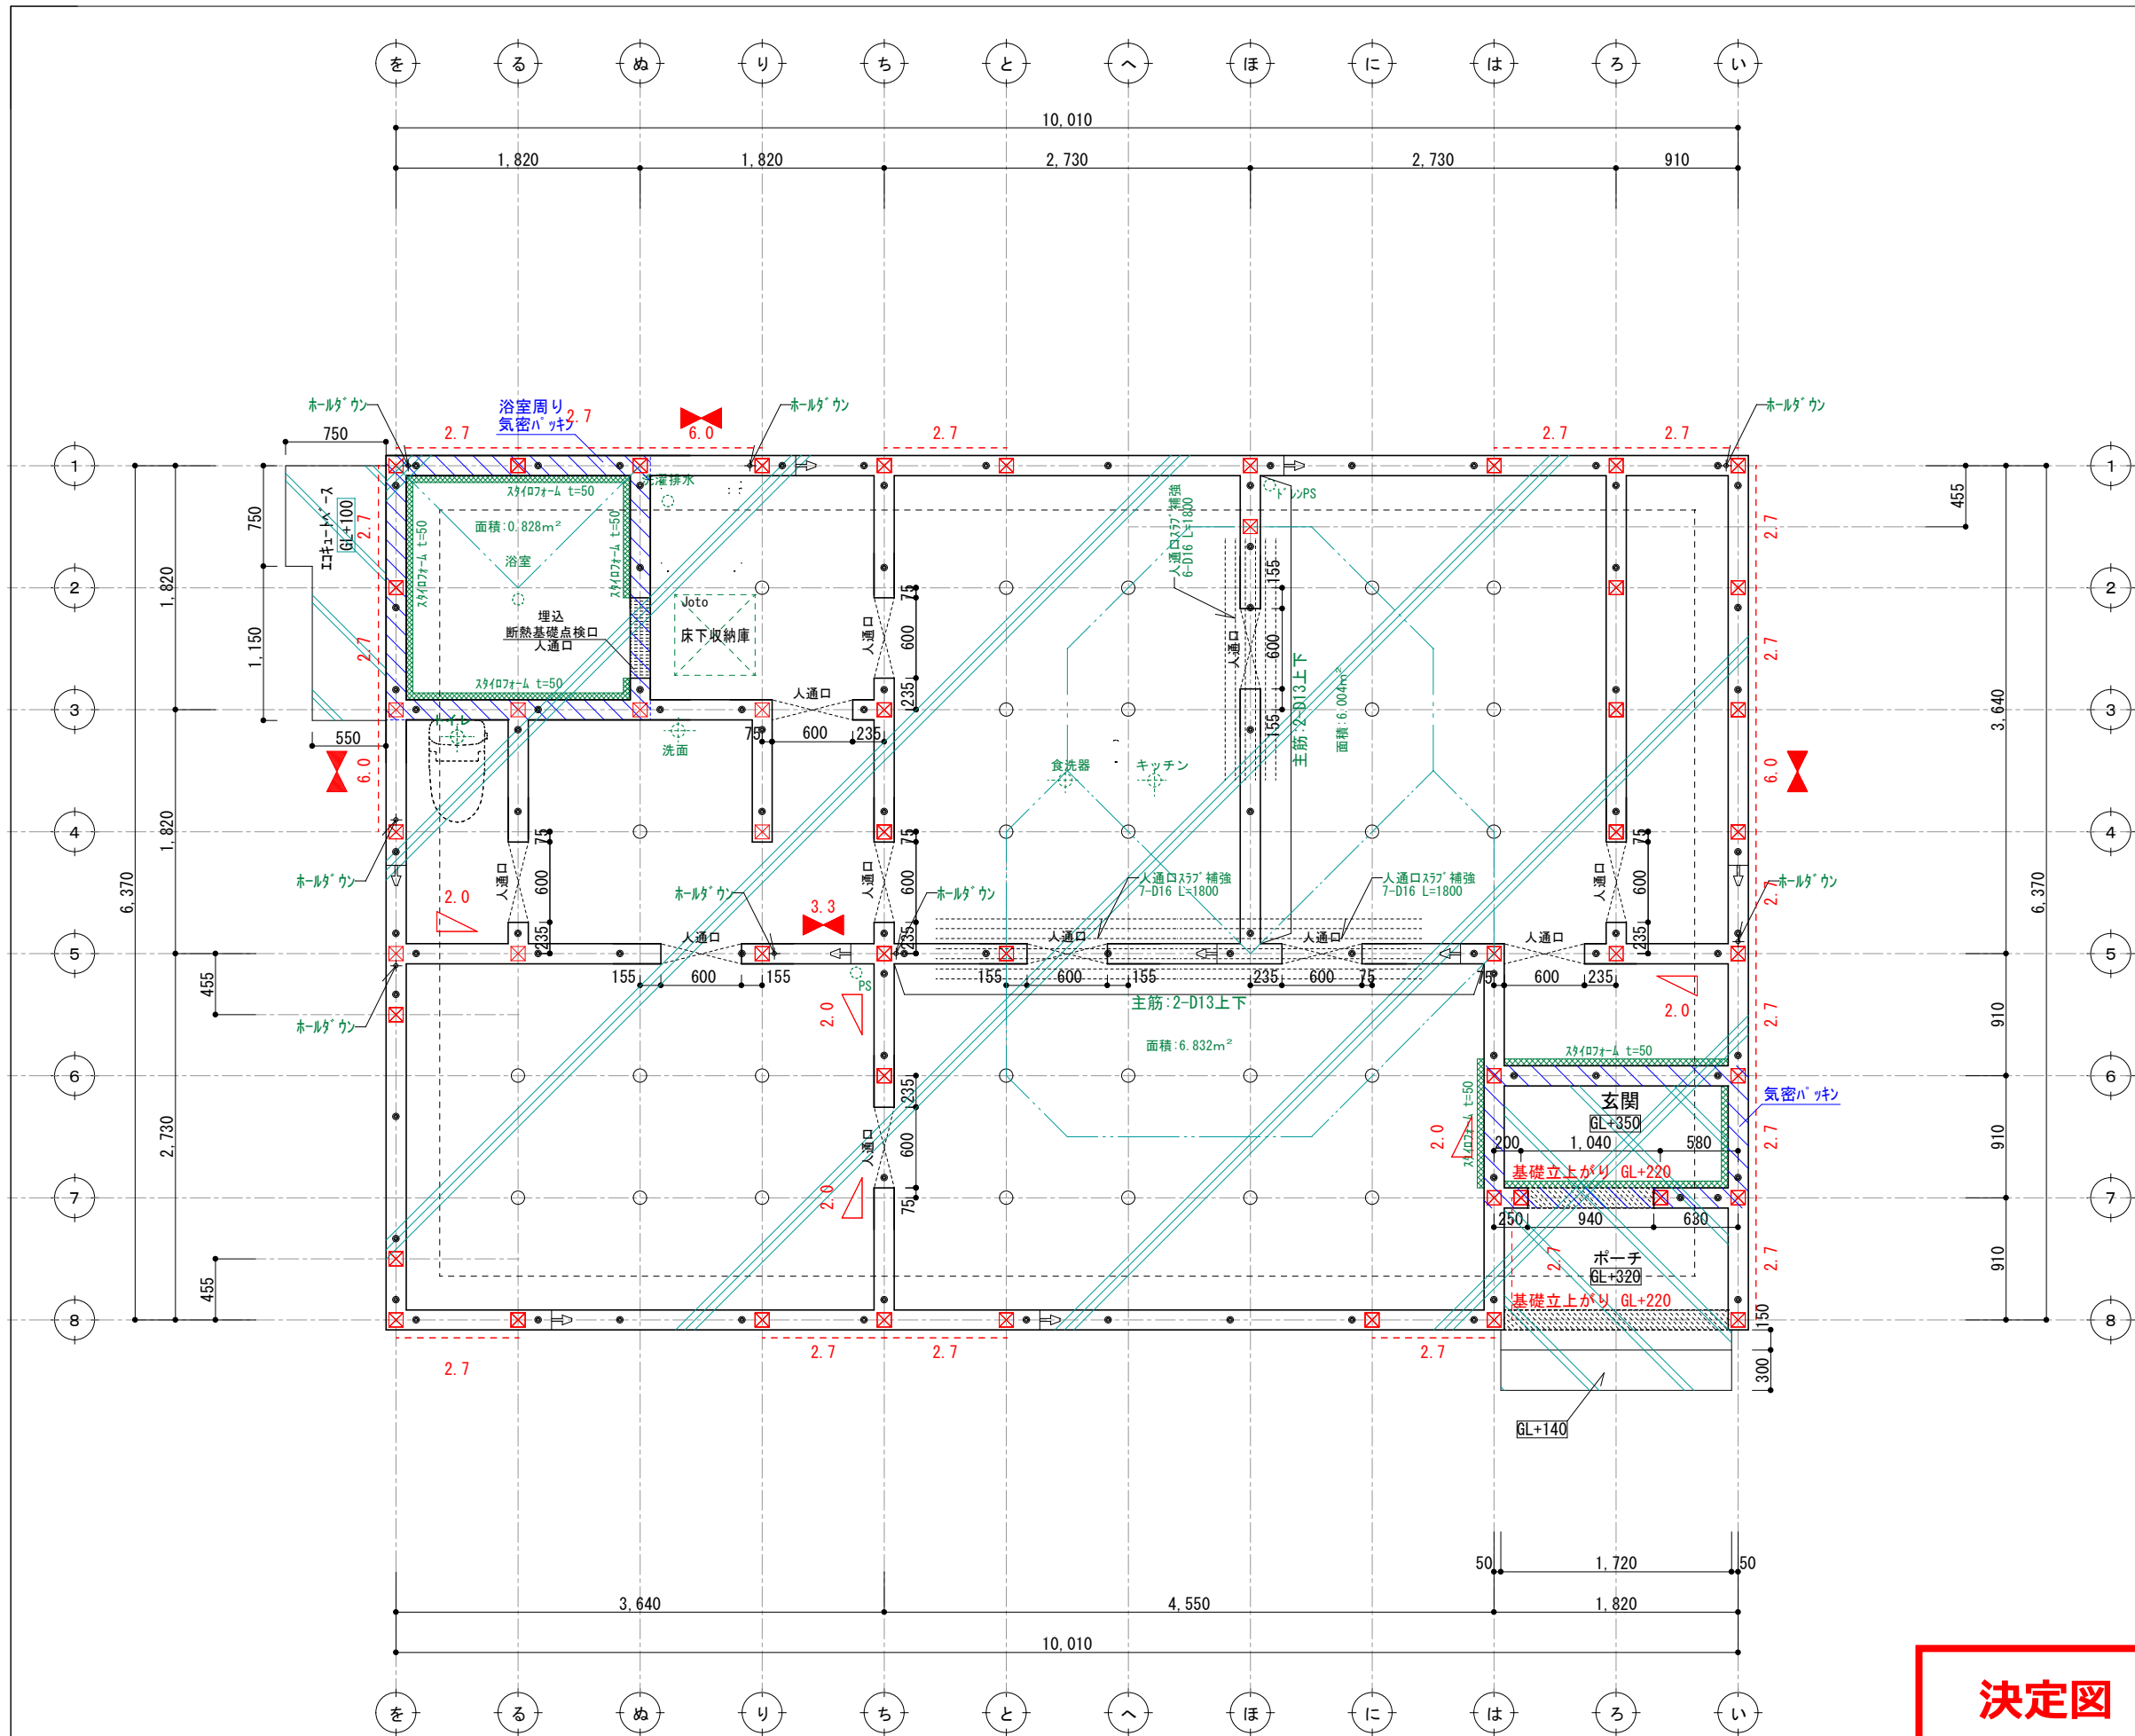

構造体ベースコンクリート t=150

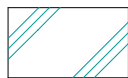

後打ち土間コン




アンカーボルトの配置

- 土台切れの箇所より150mm
- 土台の継手及び仕口の端部より150mm
- 耐力壁の端部、筋交いの脚部より150mm
- 1.82m以下の間隔
- 250mm以上埋込み
- 基礎天端より120mm

筋かい凡例

- 柱脚 柱頭 片筋かい
- たすき掛け筋かい
- 構造用パネル

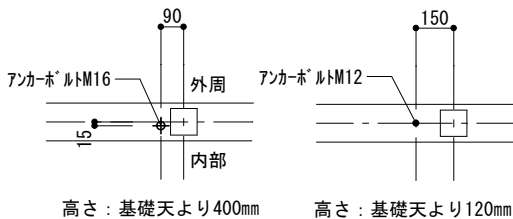

高さ：基礎天より400mm

高さ：基礎天より120mm

ホールダウン用アンカーボルト配置

アンカーボルト配置

凡例







- 通し柱 (105*105) 管柱 (105*105)
- アンカーボルトM12 L=400
- + ホールダウンアンカーM16 L=800
- 柱芯より90mm 280mm以上埋め込み (カナイフリストアンカーボルトM16)
- ⊕ 鋼製束
- 土台ジョイント
- ▨ ベースコンクリート (t=150)
- ▨ 後打ちコンクリート

基礎伏図について特記なき場合に限り下記による。

1. コンクリート：呼び強度 21N/mm²
2. 鉄筋：SD295A
3. 設計地耐力：fe=20kN/m²
地耐力計測後、不足の場合は相当の改良を行い、満たすものとする。
4. 基礎の位置は、芯振分けとする。
5. 玄関・S/C・UB周囲の基礎天端は気密パッキン施工 (網掛け部) とし、その他の基礎天端は基礎パッキン施工とする。
6. 設備配管の屋内への取り入れは基礎立上り部のスリーブによる。

決定図

訂正	浜岡一級総合設計事務所	LIFEFUND	株式会社 LIFEFUND InDesign office	一級建築士事務所	年月日	件名	設計	IC	工事	図番
	一級建築士事務所 静岡県知事登録第 (10)2441 号	PG HOUSE	事務所登録 (2)第7595号	一級建築士登録 第179770号 鈴木 達男	2026. 2. 15	平松久美江様 邸新築工事				
	一級建築士 大臣登録第 365879 号 西原利昌		〒432-8023 静岡県浜松市中央区鶴江3丁目70番23号		縮尺	図名				
					1/50	基礎伏図	酒井		青島	B-1

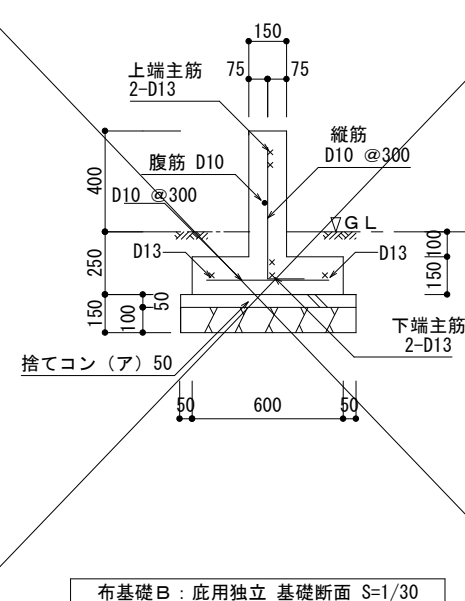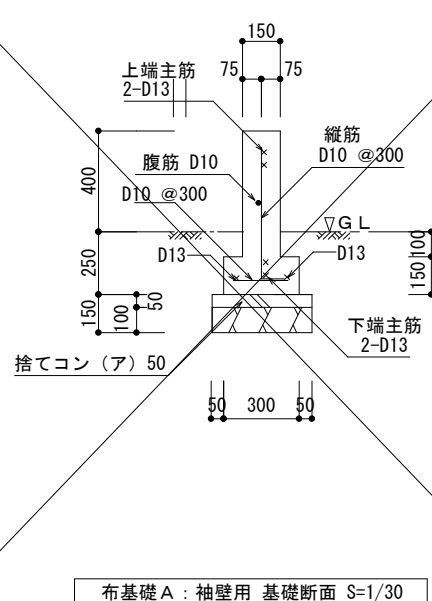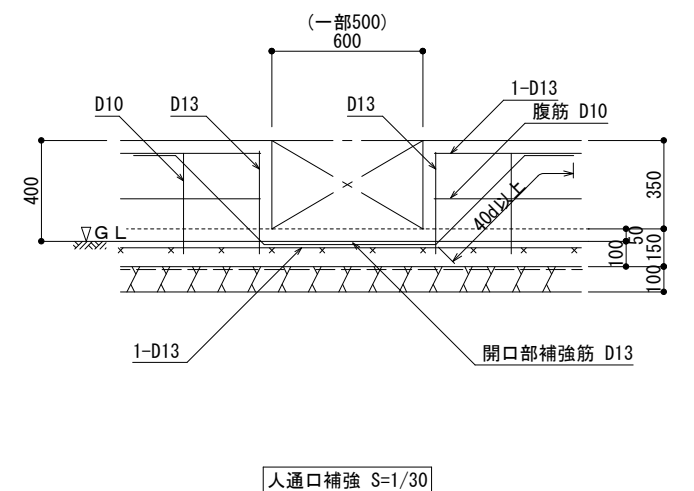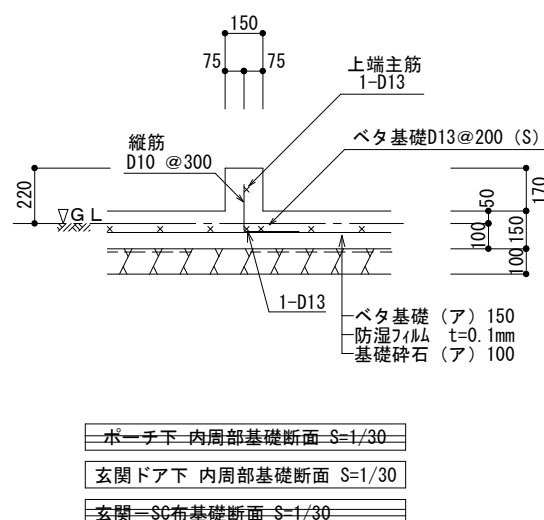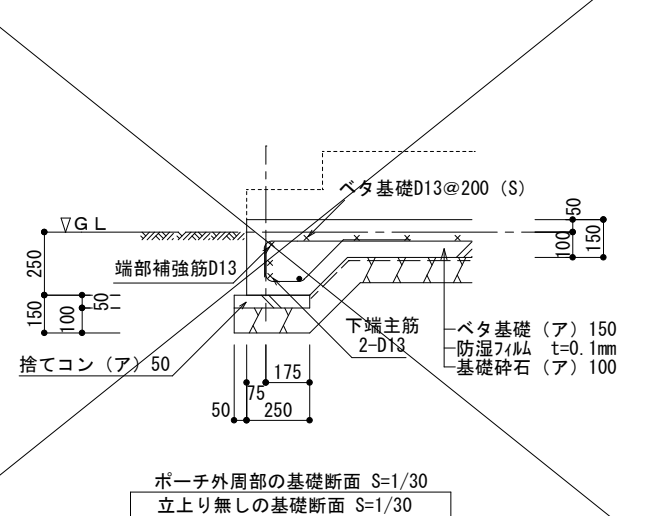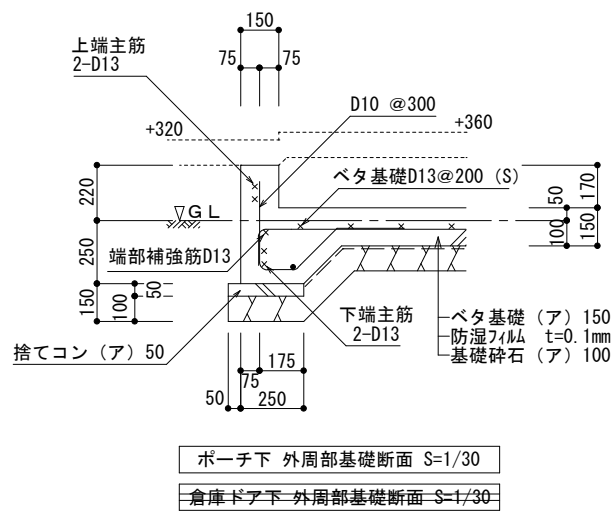


基礎の寸法 及び 配筋の検定方法	基礎立上り配筋は、 (財)日本住宅・木材技術 センター発行のスパン表 (増補版)による。 ベタ基礎スラブ配筋は、 まもりすまい保険設計施工 基準同解説のベタ基礎配筋表 による。具体的な寸法・配 筋は基礎詳細図参照。
---------------------------------------	--


- ・ D10を示す。
- × ・ D13を示す。

※使用しない断面は

決定図

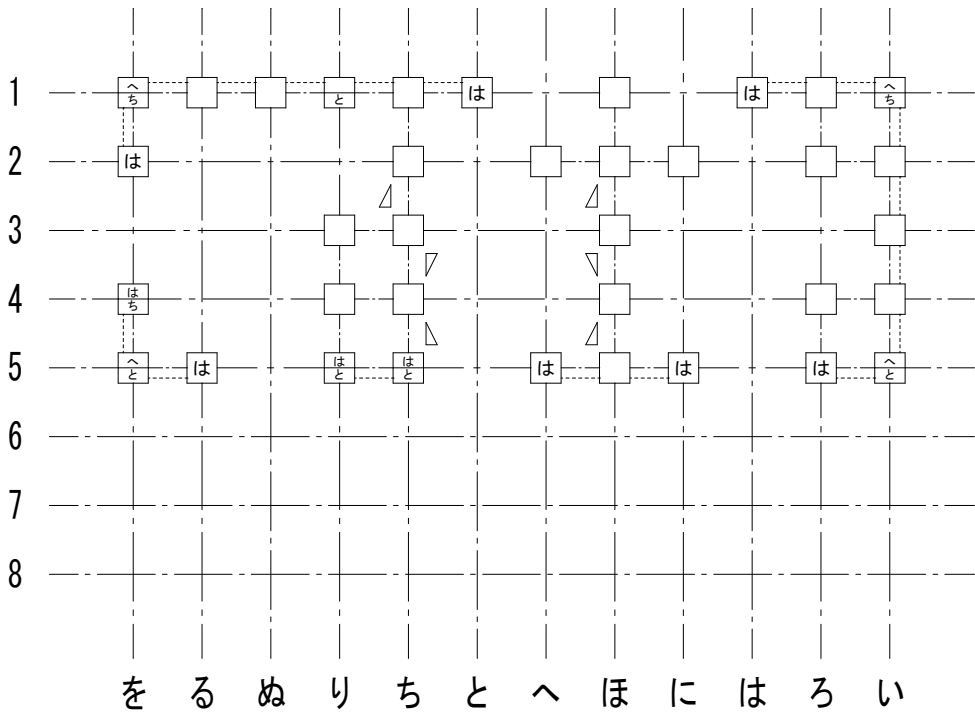

2階柱壁伏図

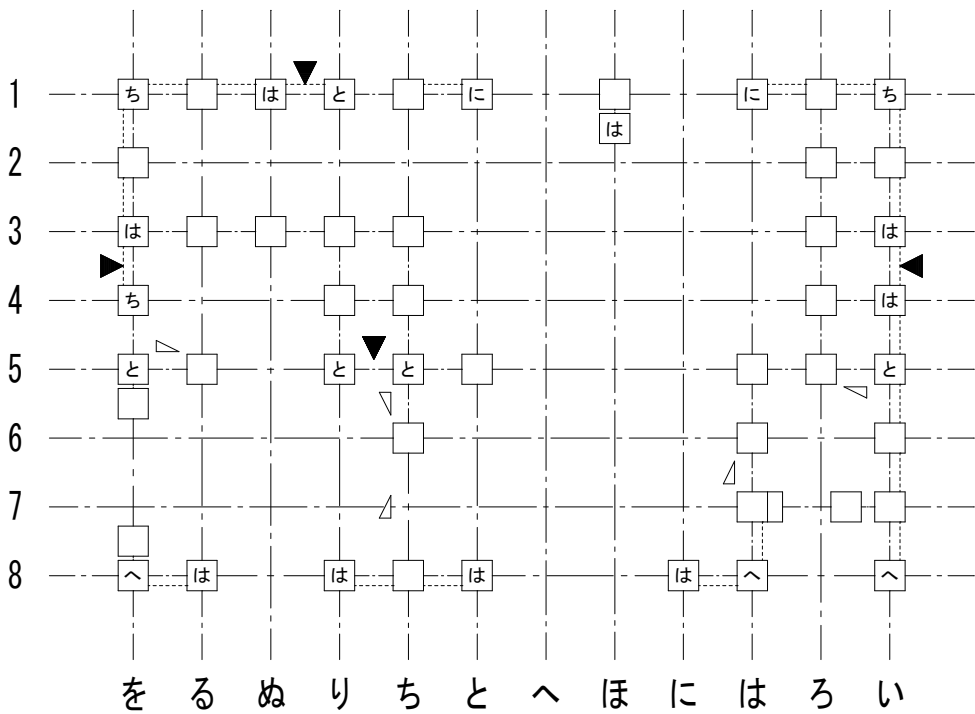

1階柱壁伏図

接合部凡例				*接合部凡例はユーザ設定されたものです。	
記号	仕様（カナイ金物）		N	倍率	
SBCP	スリムビルドコーナー75, チビクリCK(化粧柱の場合)		0.00	1.00	
SBCP	スリムビルドコーナー75, チビクリCK(化粧柱の場合)		0.65	1.00	
SBCP	は	スリムビルドコーナー75	1.00	1.00	
ARCG	に	アレントコーナー合板用	1.40	2.20	
ARCG	ほ	アレントコーナー合板用	1.60	2.20	
ARCG	へ	アレントコーナー合板用	1.80	2.20	
HD15	と	ブレイブホールダウン B-HD15	2.80	3.60	
HD20	ち	ブレイブホールダウン B-HD20	3.70	4.70	
HD25	り	ブレイブホールダウン B-HD25	4.70	4.80	
HD30	ぬ	ブレイブホールダウン B-HD30	5.60	7.20	
J1	る	腰掛け蟻若しくは大入れ蟻掛け+羽子板ボルト, 短冊金物		1.90	
J2	を	腰掛け蟻若しくは大入れ蟻掛け+羽子板ボルト, 短冊金物×2		3.00	

※表示なき金物は「は」とする。

梁継手・仕口用

梁継手・仕口用

接合部凡例				*接合部凡例はユーザ設定されたものです。	
記号	仕様（タナカ金物）		N	倍率	
FCP	フックコーナー, チビクリCK(化粧柱の場合)		0.00	1.00	
FCP	フックコーナー, チビクリCK(化粧柱の場合)		0.65	1.00	
FCP	は	フックコーナー	1.00	1.00	
CCP	に	シナコーナー	1.40	2.20	
CCP	ほ	シナコーナー	1.60	2.20	
CCP	へ	シナコーナー	1.80	2.20	
HD15	と	ビス止めホールダウンU HD15	2.80	3.60	
HD20	ち	ビス止めホールダウンU HD20	3.70	4.70	
HD25	り	ビス止めホールダウンU HD25	4.70	4.80	
HD30	ぬ	ビス止めホールダウンU HD15×2 (HD35)	5.60	7.20	
J1	る	腰掛け蟻若しくは大入れ蟻掛け+羽子板ボルト, 短冊金物		1.90	
J2	を	腰掛け蟻若しくは大入れ蟻掛け+羽子板ボルト, 短冊金物×2		3.00	

※表示なき金物は「は」とする。

梁継手・仕口用

梁継手・仕口用

筋かいの種類に応じた筋かいの端部の接合部の仕様		
	筋かいの種類	接合部の仕様（構造方法）
イ	鉄筋φ9	柱又は横架材を貫通し、三角座金を介してナット締め、又は鋼板添え板を用い鋼板を柱及び横架材にCN90, 8本平打ち
ロ	筋かい:15×90	柱・横架材を欠き込み、柱・横架材双方に対してN65, 5本平打ち
ハ	筋かい:30×90	鋼板添え板t=1.6mmを筋かいに対してボルトφ12及びCN65, 3本平打ち、柱に対してCN65, 3本平打ち、横架材に対してCN65, 4本平打ち。筋かいプレートBP同等品
ニ	筋かい:45×90	鋼板添え板t=2.3mmを筋かいに対してボルトφ12及びスクリュー釘φ4.5L50, 7本平打ち、柱及び横架材に対してスクリュー釘φ4.5L50, 5本平打ち。筋かいプレートBP-2同等品
ホ	筋かい:90×90	柱又は横架材にボルトφ12mmを用いて一面剪断接合

胴差と通し柱の接合部の仕様		
	胴差と通し柱の条件	仕口
T1	通し柱の片側に胴差が来る場合	胴差を柱にかたぎ大入れ短ほぞ差しの上、羽子板ボルト、かね折り金物又は同等以上の仕口
T2	通し柱の両側に胴差が来る場合	胴差を柱にかたぎ大入れ短ほぞ差しの上、短冊金物又は、同等以上の仕口で胴差相互を緊結
T3	通し柱と胴差の接合部の近くに90×90以上の筋かいが来る場合(通し柱が建物の出隅にあるか、筋かい壁が外壁と直交して接する場合)	胴差を通し柱に、15KN用引き寄せ金物を水平に用いて緊結

決定図

G2



壁付け 住宅用火災報知器			数量
[H] 熱感知	熱感知器	電池式(単独型)	1
		露出型	
壁付け 住宅用火災報知器			数量
[S] 煙感知	煙感知器	電池式(単独型)	1
		露出型	

- ※ 煙感知器は壁・梁より600mm以上離す
壁に取付ける場合、
天井から150mm以上500mm以内離す
換気扇・エアコン吹出口から1500mm以上離す
- ※ 全室LED照明とする。
- ※ 標準天井高さ2,400
- ※ 特記無きガラスは型ガラス

* 凡例


- ☒ 管柱 (105×105)
- ☒ K'ンパ- (3.30倍 FRM-0641)
- △ 片筋違い (2.00倍 45×90)
(例 左:柱脚 右:柱頭)
- ⊠ たすき掛筋違い (4.00倍 45×90)
- 構造用合板 (2.70倍)
(t=9 9分 -EXN(ハ-))
- ⊠ 床点検口
- ⊠ 天井点検口
- ⊕ 換気扇
- ⊕ 熱交換換気扇VLR-70

アドバンスシリーズ		
スマートデザイン (外部)		
凡例	①	コンセント 1ヶ所
②	コンセント 2ヶ所	
③	コンセント 3ヶ所	
④ET	コンセント1ヶ所接地ターミナル付	
⑤ET	コンセント2ヶ所接地ターミナル付	
⑥WP	コンセント 防水型	
⑦	エアコン用コンセント	
⑧	200V用コンセント	
⑨WP	防雨入線プレート	
⑩	スイッチ	
⑪	3路スイッチ	
⑫	4路スイッチ	
⑬	直結電源	
⑭TV	テレビ取出口	
⑮TEL	電話取出口 (テレホンガイド)	
⑯LAN	LAN取出口 (テレホンガイド)	
⑰	壁照明	
⑱	リモコン (給湯関係・ルフロ)	
⑲	メーター	
⑳	分電盤	
㉑	チャイム	

- ※ACコンセント天井付け
- ※TVアンテナ工事
- ※スイッチはFL+1100、コンセントはFL+200

決定図



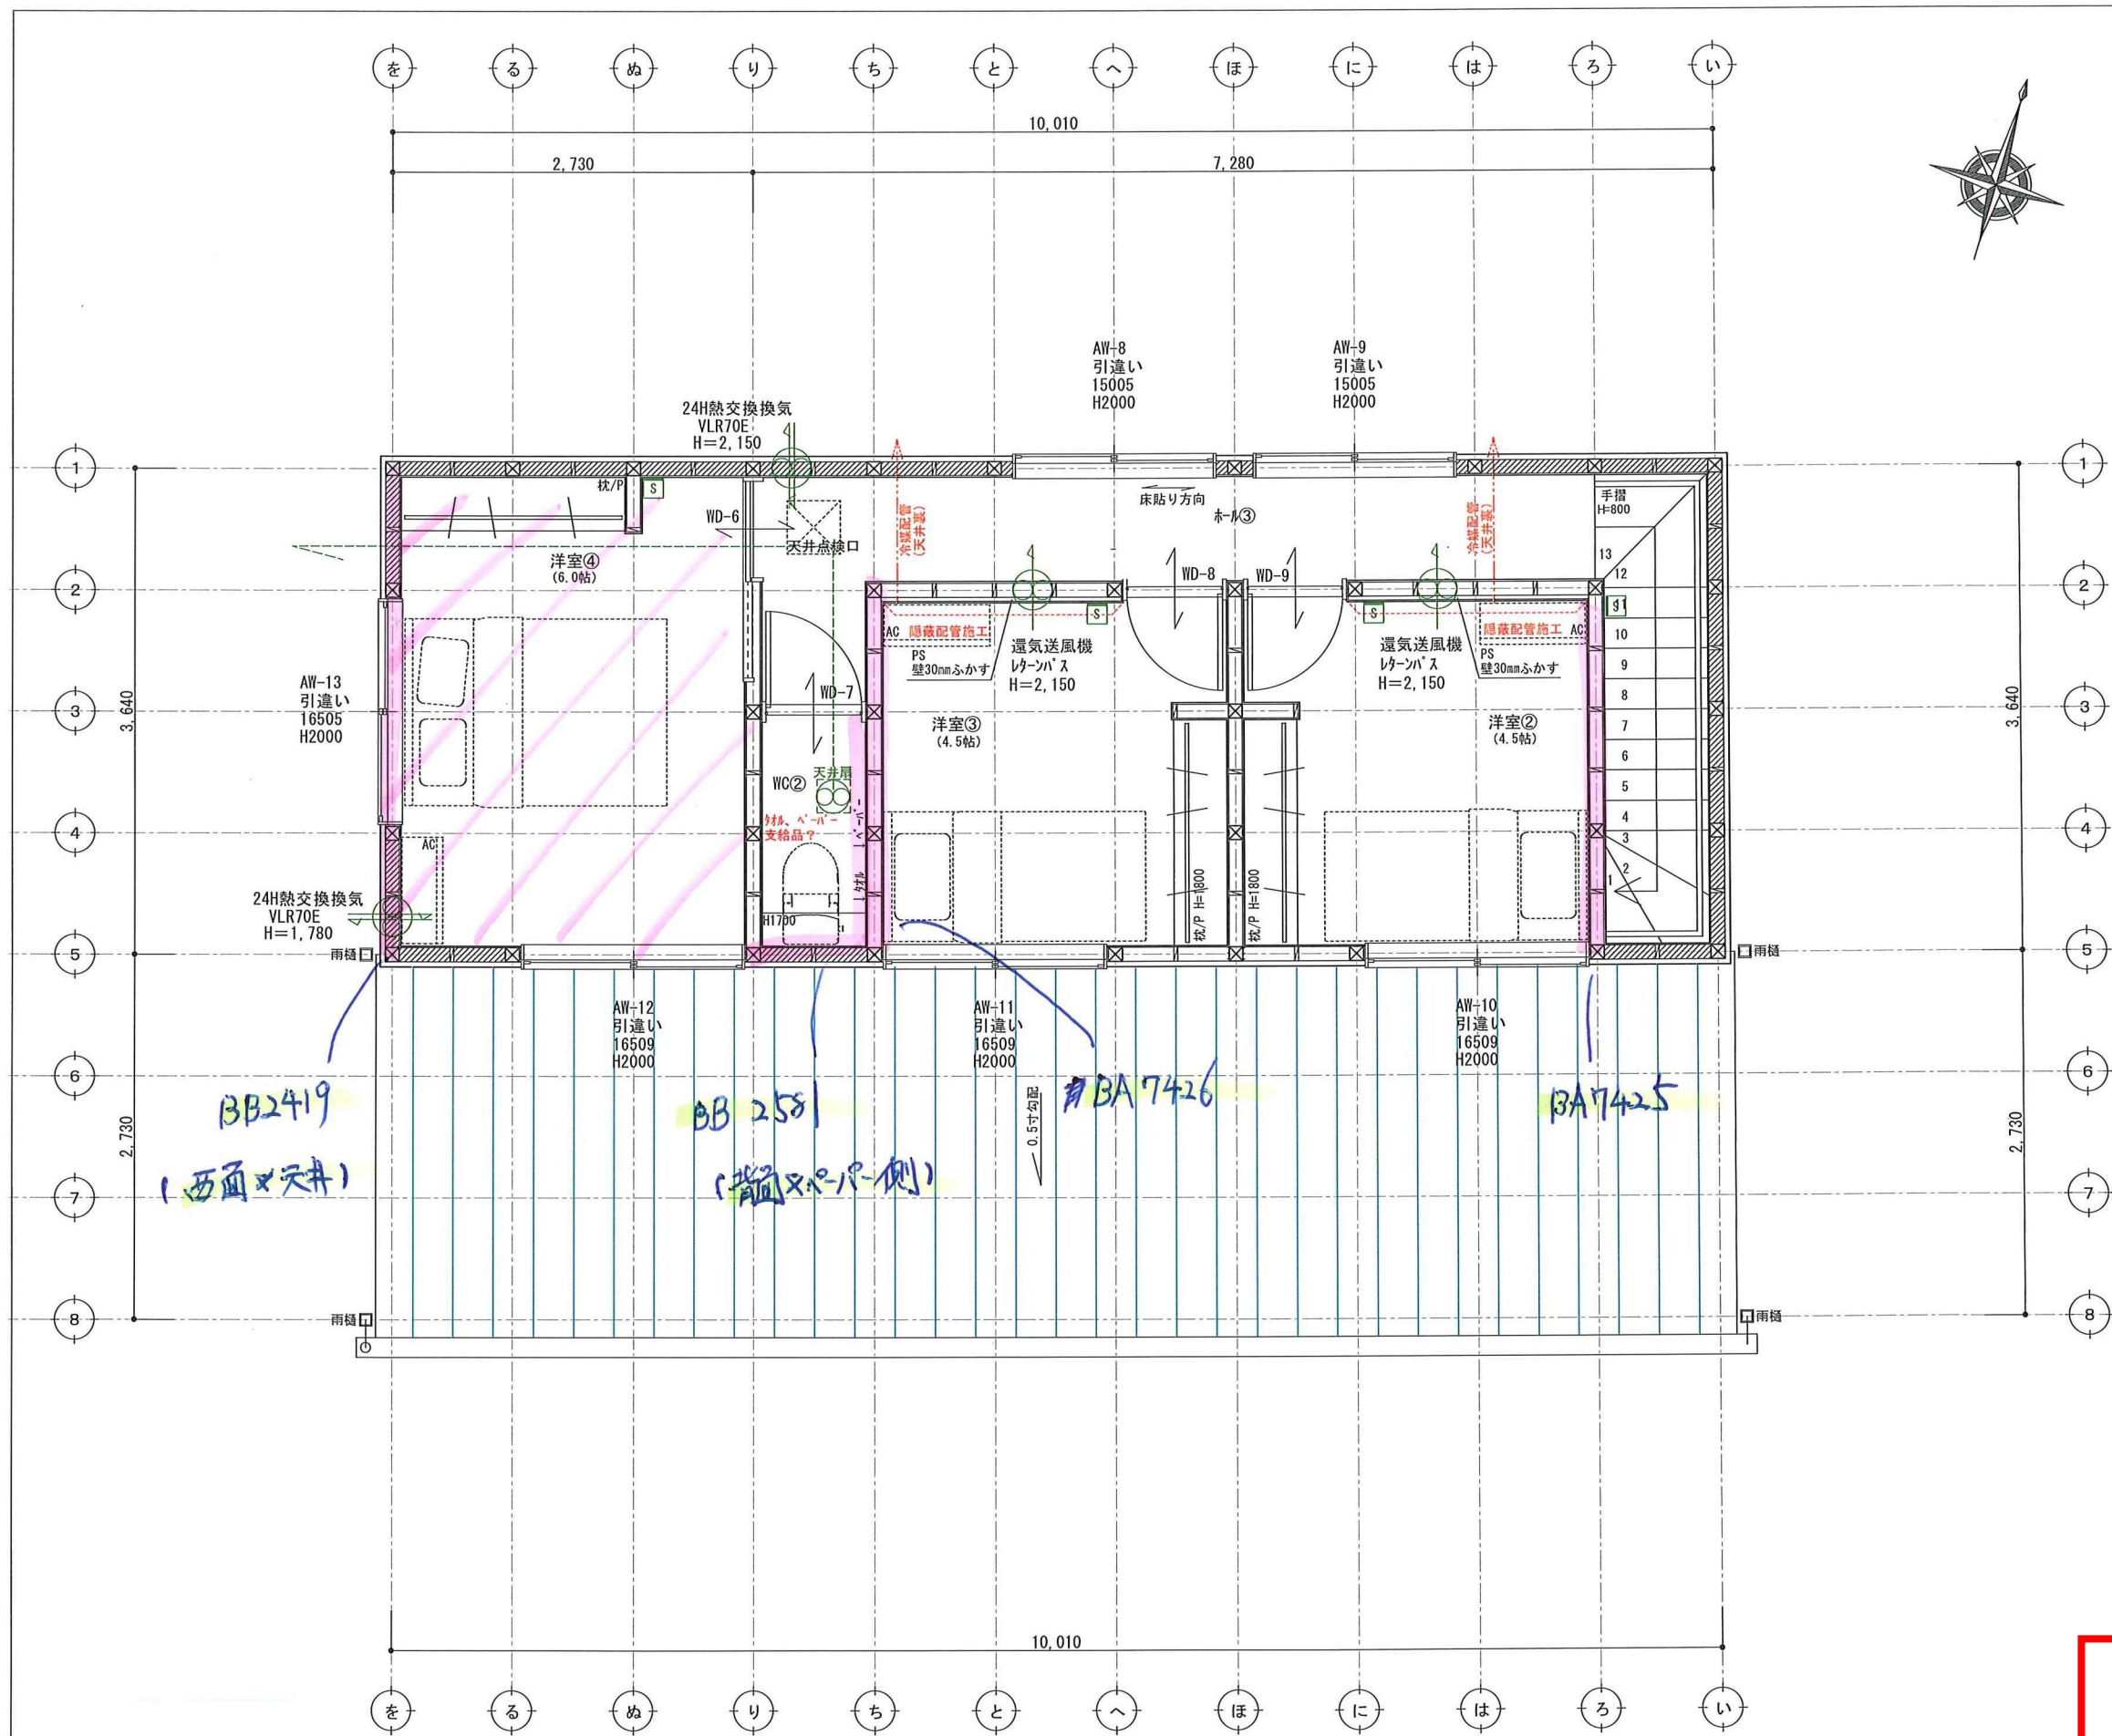

G2

壁付け 住宅用火災報知器			数量
H 熱感知	熱感知器	電池式(単独型)	
		露出型	
壁付け 住宅用火災報知器			数量
S 煙感知	煙感知器	電池式(単独型)	4
		露出型	

- ※ 煙感知器は壁・梁より600mm以上離す
壁に取付ける場合、
天井から150mm以上500mm以内離す
換気扇・エアコン吹出口から1500mm以上離す
- ※ 全室LED照明とする。
- ※ 標準天井高さ2,400
- ※ 特記無きガラスは型ガラス

* 凡例

- ☒ 管柱 (105×105)
- ◀▶ K9'ハ- (3.30倍 FRM-0641)
- △ 片筋違い (2.00倍 45×90)
(例 左:柱脚 右:柱頭)
- ⊠ たすき掛筋違い (4.00倍 45×90)
- 構造用合板 (2.70倍)
(t=9 タカ EXNハ-)
- ◻ 床点検口
- ◻ 天井点検口
- ⊕ 換気扇
- ⊕ 熱交換換気扇VLR-70

アドバンスシリーズ	
スマートデザイン (外部)	
凡例	
①	コンセント 1ヶ所
②	コンセント 2ヶ所
③	コンセント 3ヶ所
①ET	コンセント1ヶ所接地ターミナル付
②ET	コンセント2ヶ所接地ターミナル付
①WP	コンセント 防水型
②	エアコン用コンセント
③	200V用コンセント
①WP	防雨入替プレート
●	スイッチ
●	3路スイッチ
●	4路スイッチ
⊗	直結電源
⊗	テレビ取出口
⊗TEL	電話取出口 (テレホンガイド)
⊗LAN	LAN取出口 (テレホンガイド)
⊗	壁照明
⊗	リモコン (給湯関係・ルフロ)
⊗	メーター
⊗	分電盤
⊗	チャイム

- ※ACコンセント天井付け
- ※TVアンテナ工事
- ※スイッチはFL+1100、コンセントはFL+200

決定図