



浜松市中央区倉松地内

G2

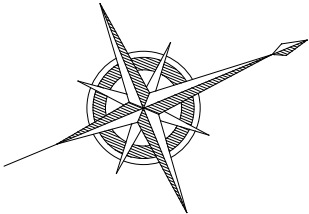


求積図

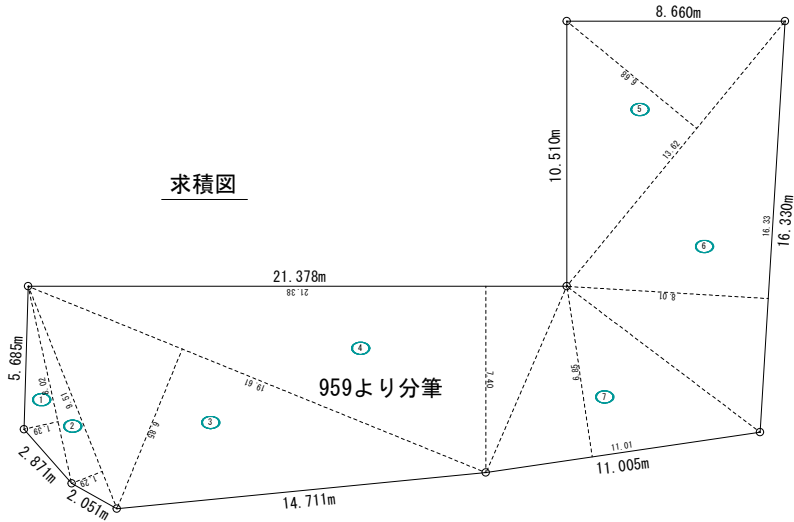

番号	底 辺	高 さ	倍 面 積	面 積
1	8.02	1.39	11.1478	5.57390
2	9.51	1.29	12.2679	6.13395
3	19.61	6.85	134.3285	67.16425
4	21.38	7.40	158.2120	79.10600
5	13.62	6.68	90.9816	45.49080
6	16.33	8.01	130.8033	65.40165
7	11.01	6.85	75.4185	37.70925
合 計				306.57980
敷 地 面 積				306.57 m ²

トータル面積表		(m ²)
敷地面積		306.57
建築面積		93.16
床面積	1階	86.12
	2階	11.59
延床面積		97.71
建蔽率	(93.16/306.57) × 100	30.39%
容積率	(97.71/306.57) × 100	31.88%

道路斜線制限については、明らかに適合する。
隣地斜線制限については、明らかに適合する。
平均地盤面について
申請建物の周囲の平均地盤面高さをBM+200とする。
盛土規制法の許可対象となる工事なし。

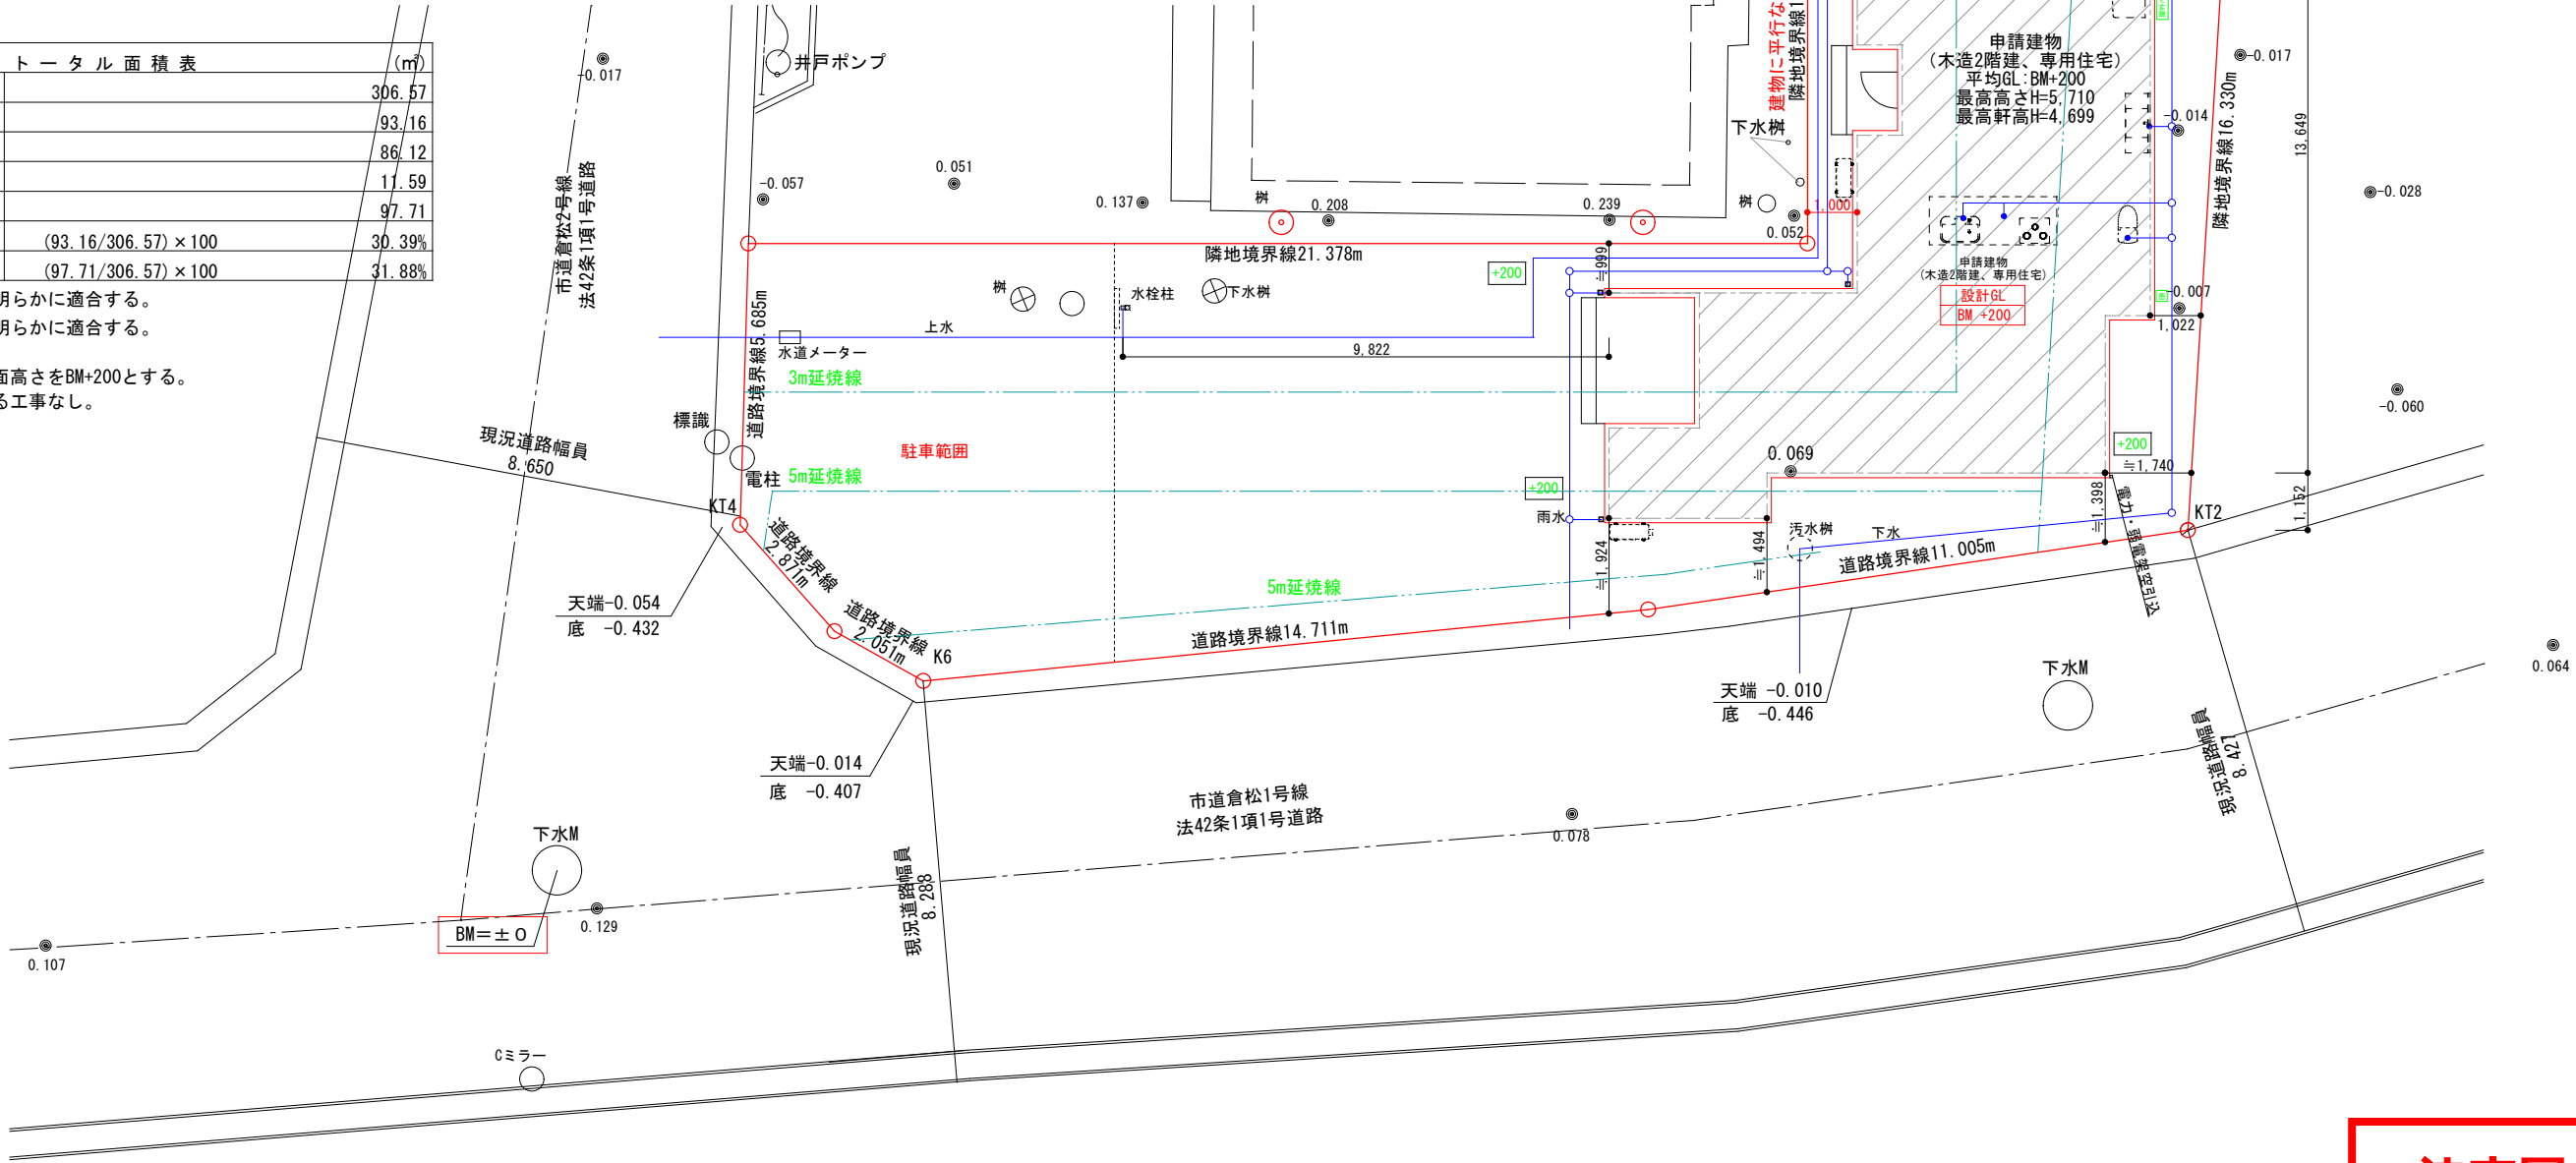

決定図