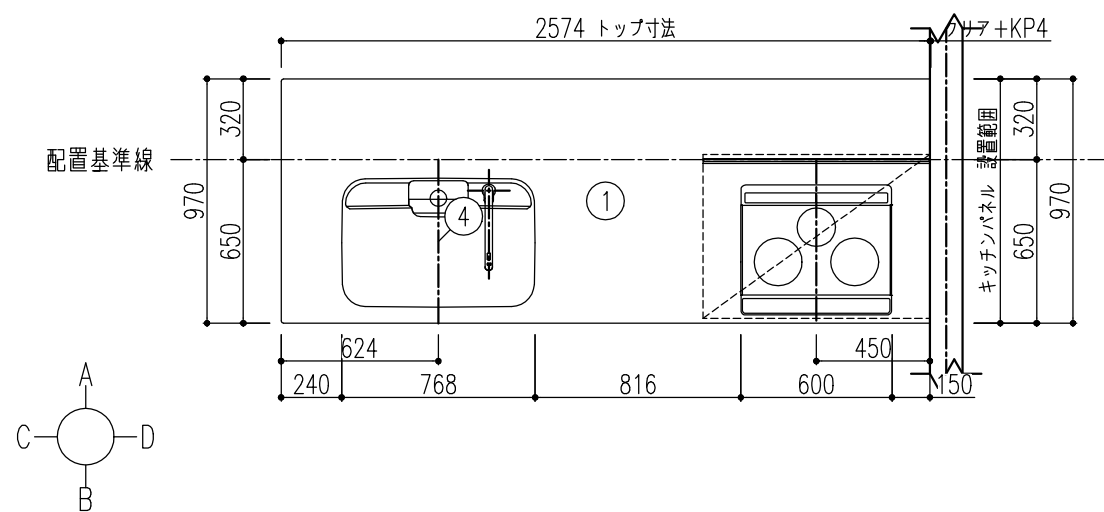



[illegible]

【 ご注意 】


- 記載のキャビネット寸法は扉前面での呼び寸法です。キャビネット本体の寸法・扉厚等は商品ガイドの巻末資料をご確認ください。
- 記載のワークトップ、カウンター、エンドパネル、サイドパネルの寸法は呼び寸法です。詳細寸法は商品ガイドの巻末資料をご確認ください。
- レンジフード電源プラグ仕様：3芯電源プラグ（アース工事が必要です。）

特記事項 扉色 KK3:ソリッドブラック 取手 [F]ミドルハンドル (ブラック) ワークトップカラー 【DW】ソルティホワイト	物件名	山村和孝 様邸	案件No.	図面名	担当	図面	図番 : 株式会社 LIXIL
			A2512DDD0FOLLU	レイアウト図	栗野 友仁		
	仕様	ES21	見積No.	縮尺	日付		
			M26019847625-009-2	1/30	2026.03.17		


A面

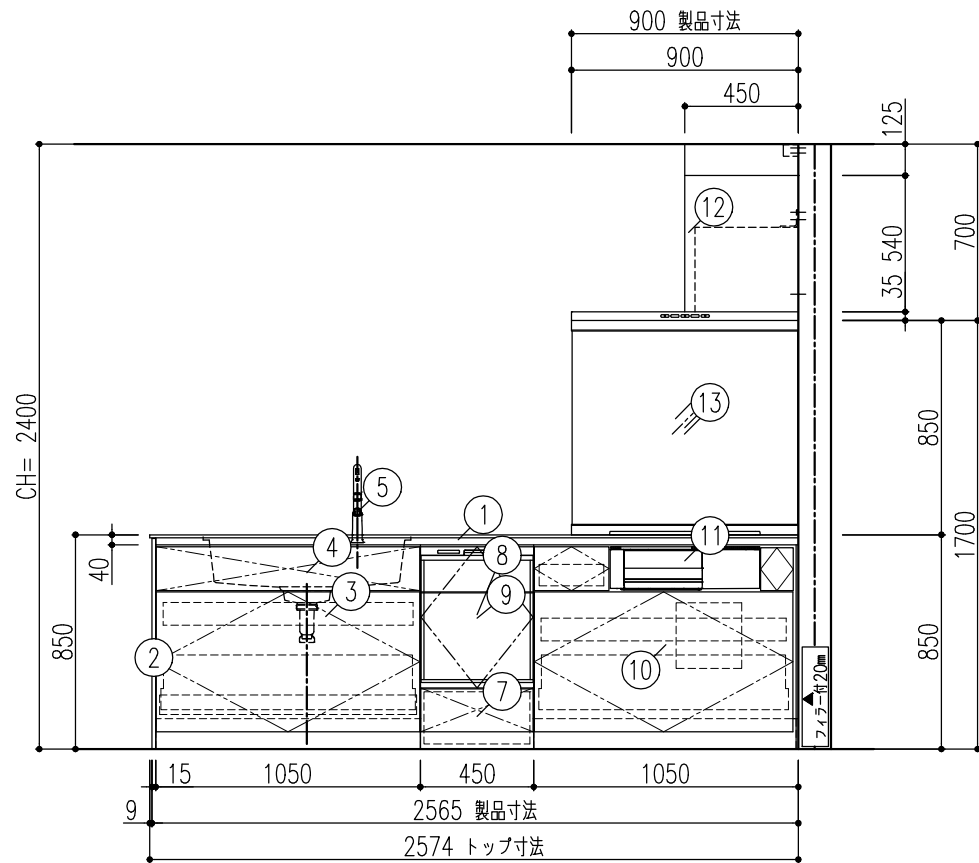


B面

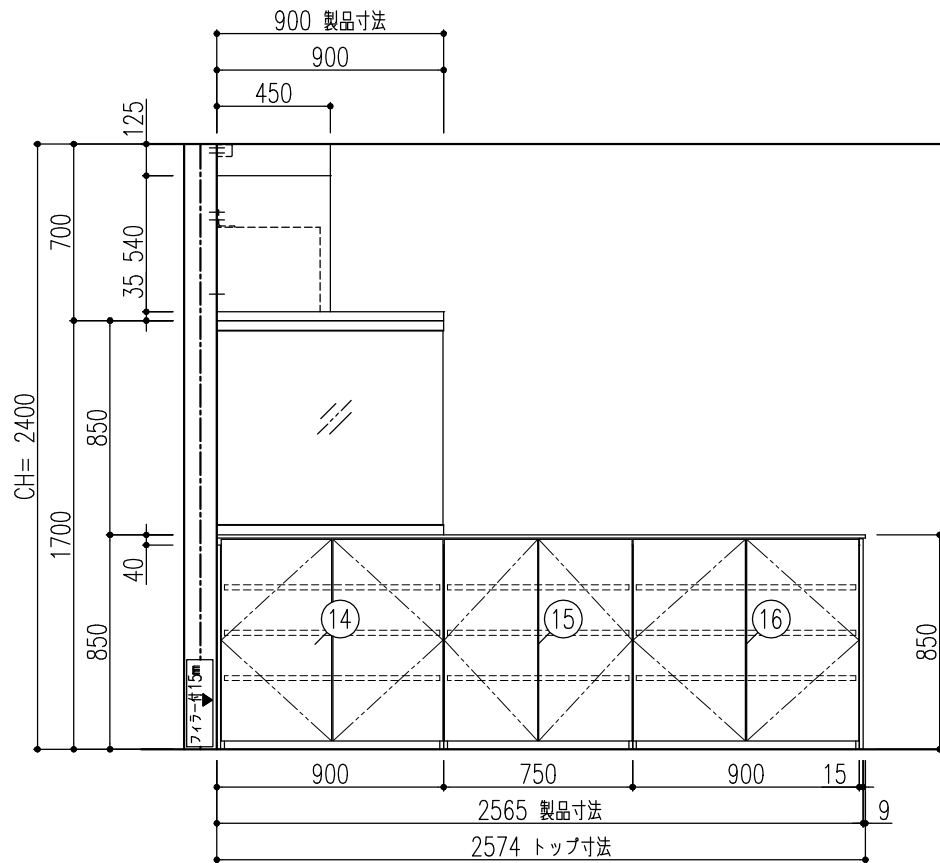


C面

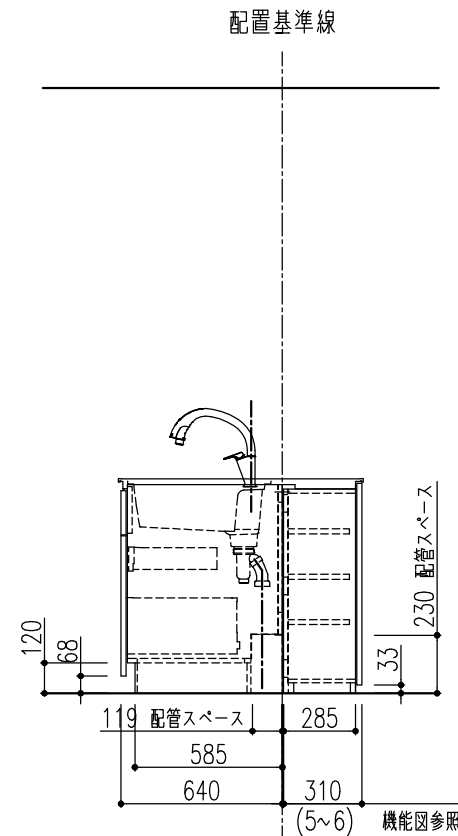

D面

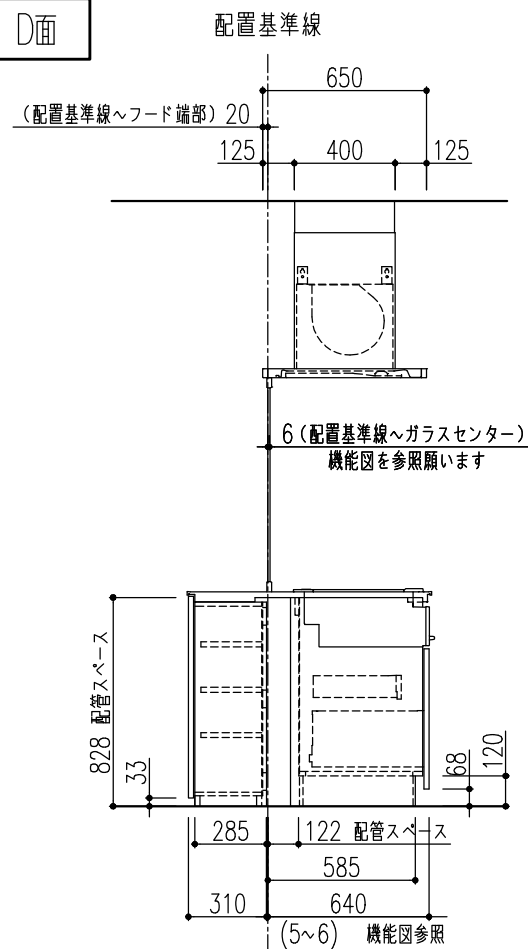

特記事項 扉色 KK3:ソリッドブラック 取手 [F]ミドルハンドル (ブラック) ワークトップカラー 【DW】ソルティホワイト	物件名 山村和孝 様邸	案件No.	図面名	担当	図面	図番
		A2512DDDOFOLLU	レイアウト図	栗野 友仁		株式会社 LIXIL
		見積No.	縮尺	日付		
		M26019847625-009-2	1/30	2026.03.17		
仕様 ES21						

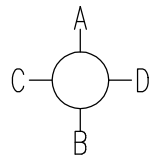

【ご注意】



- 記載のキャビネット寸法は扉前面での呼び寸法です。キャビネット本体の寸法・扉厚み等は商品ガイドの巻末資料をご確認ください。
- 記載のワークトップ、カウンター、エンドパネル、サイドパネルの寸法は呼び寸法です。詳細寸法は商品ガイドの巻末資料をご確認ください。
- 電気・ガス・給排水・換気等は法令・規定に従って有資格者が行ってください。
- 水道工事は排水配管工事となります。
- 取付・設置に際し、各製品の取付・設置説明書や図面の機能図を必ずお読み下さい。
- 内線規程上、各機器のプラグ仕様に問わず建築側には接地極付コンセントを推奨しています。
- レンジフード電源プラグ仕様：3芯電源プラグ（アース工事が必要です。）
- 食器洗い乾燥機配管は、給水接続か給湯接続かお客様に確認したうえで施工願います。
- 食洗機内配管の詳細については必ず別添の機能図をご確認ください。

A3 20260317NMZ5-01

A面

面

注1) 125V・15A 2極接地極付アースターミナル付コンセント 側板取付【専用】
 注2) 125V・15A 2極接地極付コンセント（側板取付）
 注3) 250V・30A 2極接地極付コンセント（コンセントベース固定）【専用】
 注4) レンジフード総高さ（600～900）の時 ダクトカバー範囲（25～325）

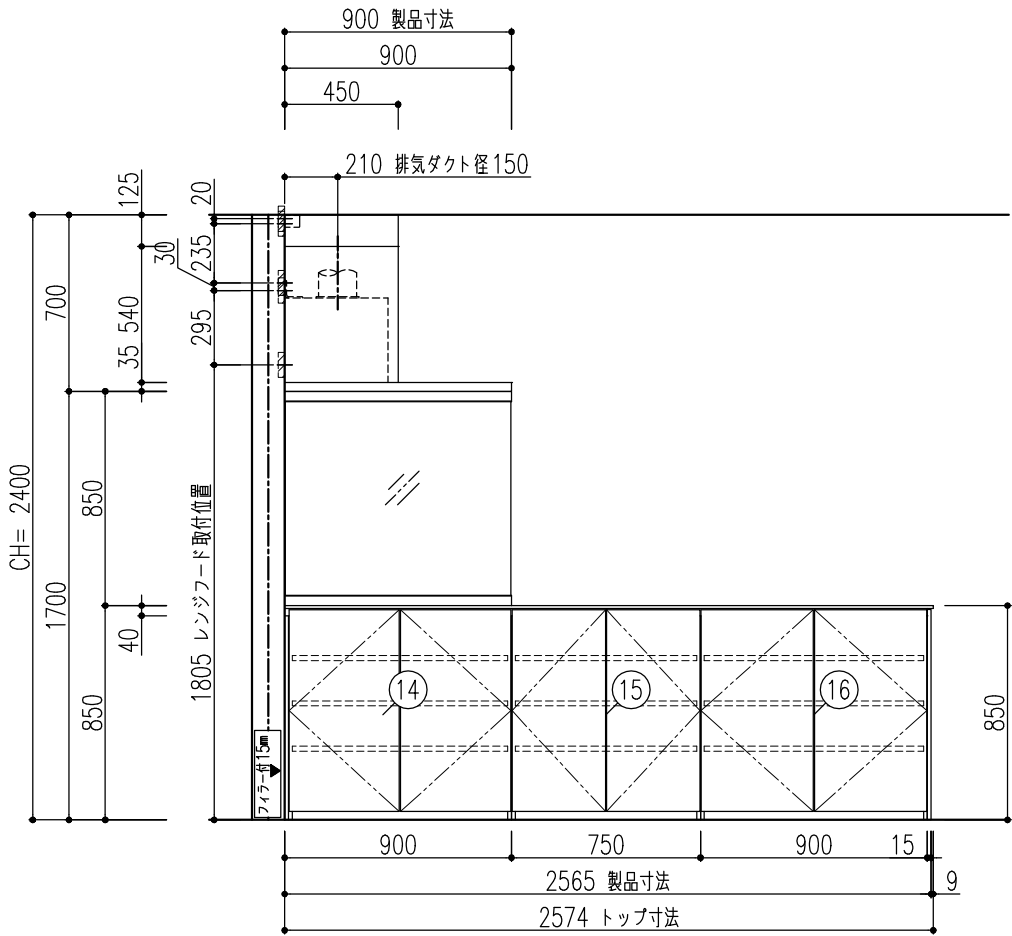
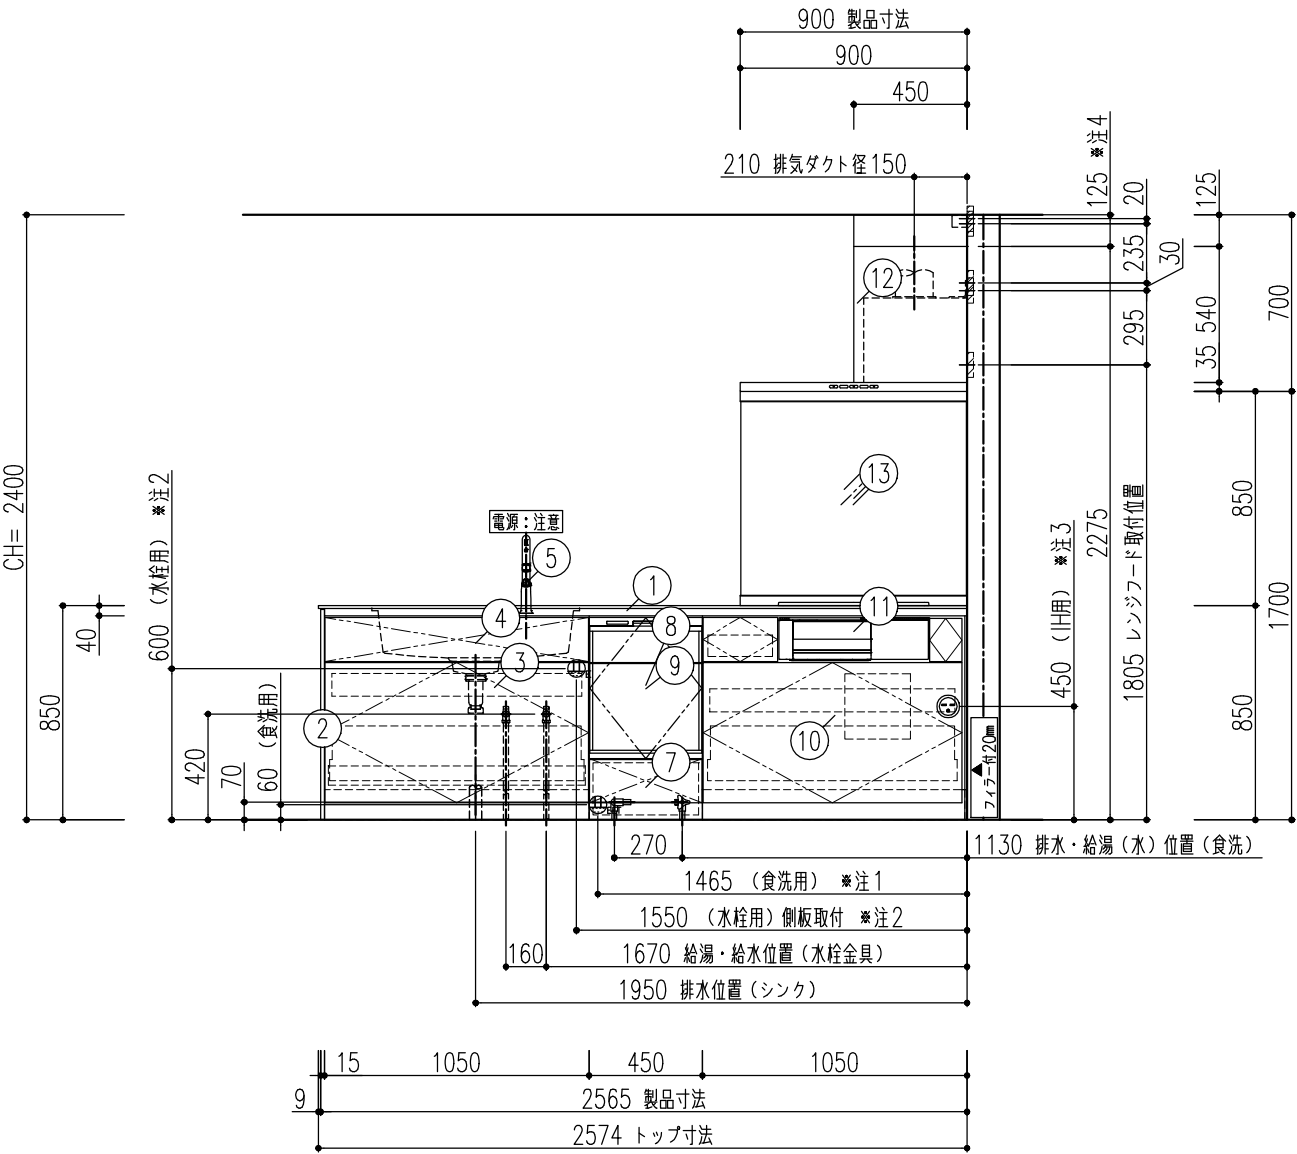


特記事項 屋色 KK3:ソリッドブラック 取手 [F]ミドルハンドル(ブラック) ワークトップカラー 【DW】ソルティホワイト	物件名	山村和孝 様邸	案件No.	図面名	担当	図面	図番 : 株式会社 LIXIL
	仕様	ES21	A2512DDD0FOLLU	納まり図	葉野 友仁		
			見積No.	縮尺	日付		
			M26019847625-009-2	1/30	2026.03.17		

C面


D面

注3) 250V・30A 2極接地極付コンセント（コンセントベース固定）【専用】
注5) 125V・15A 2極接地極付アースターミナル付コンセント 【専用】（フード用）

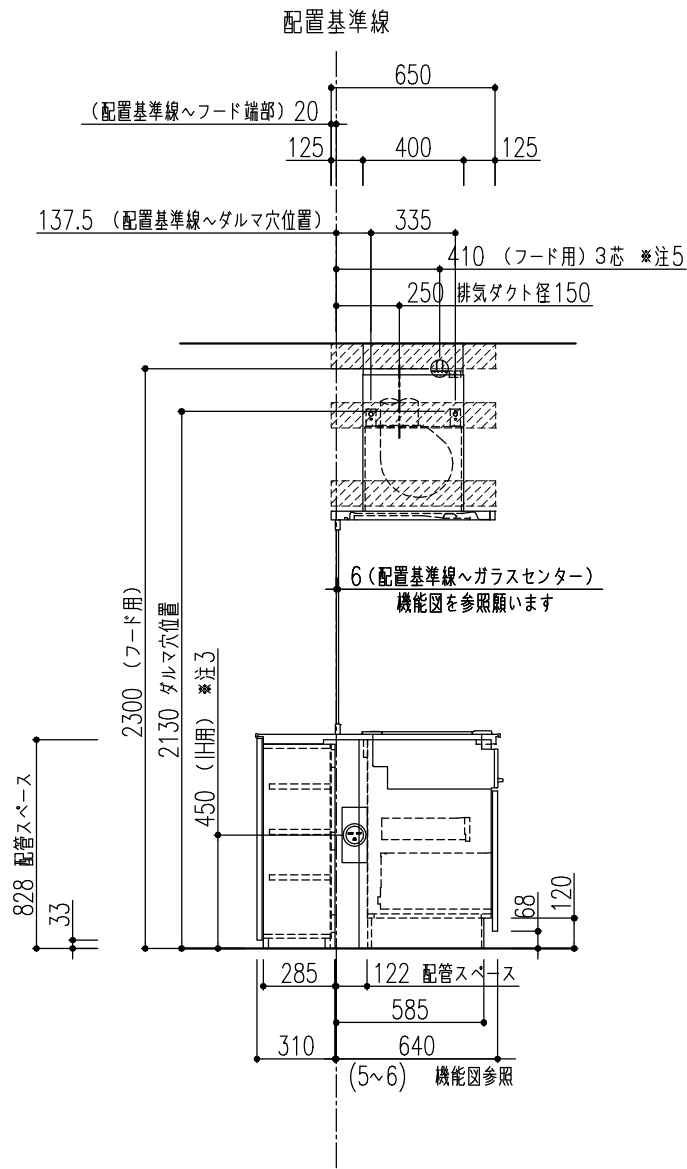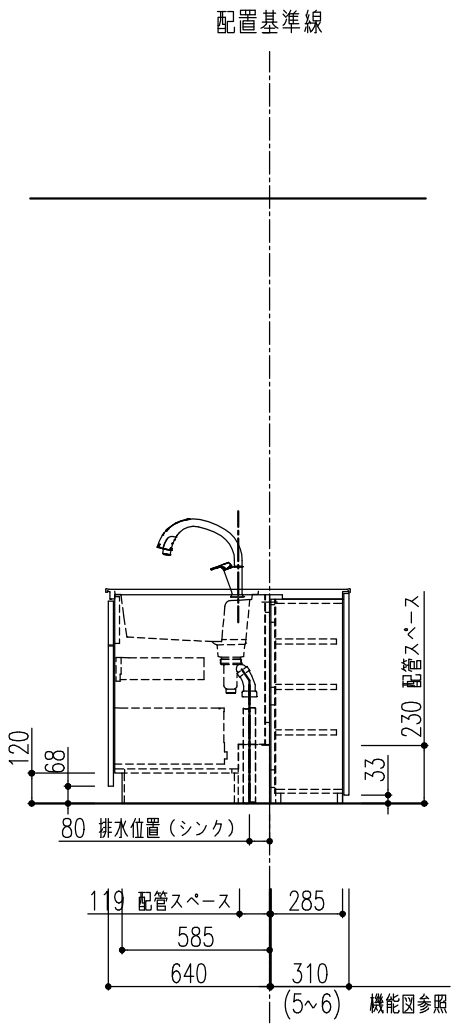

特記事項 扉色 KK3:ソリッドブラック 取手 [F]ミドルハンドル（ブラック） ワークトップカラー 【DW】ソルティホワイト	物件名	山村和孝 様邸	案件No.	図面名	担当	図面	図番
	仕様	ES21	A2512DDDOFOLLU	納まり図	栗野 友仁		株式会社 LIXIL
			見積No.	縮尺	日付		
			M26019847625-009-2	1/30	2026.03.17		




■ 床の不陸に関して

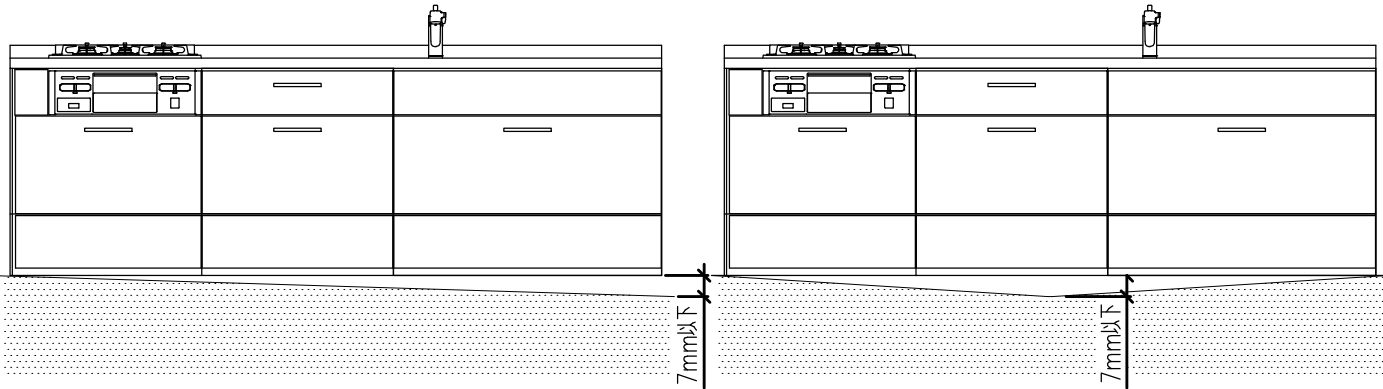

床の不陸は、7mm以下に抑えるようにしてください。不陸が大きい場合は、現場責任者に床の修正を依頼してください。
※キャビネット取付時には不陸調整スペーサー等で水平になるように設置してください。

■ 裏面キャビネット納まりについて

(キッチン側キャビネット背面) 配置基準▽

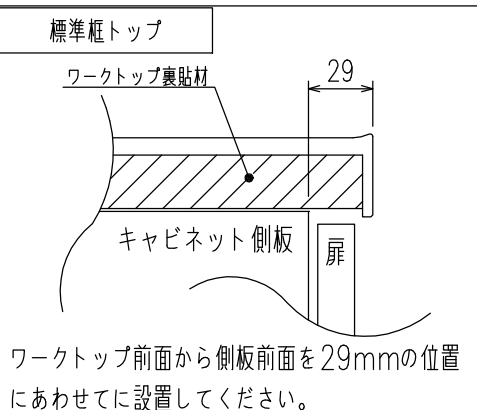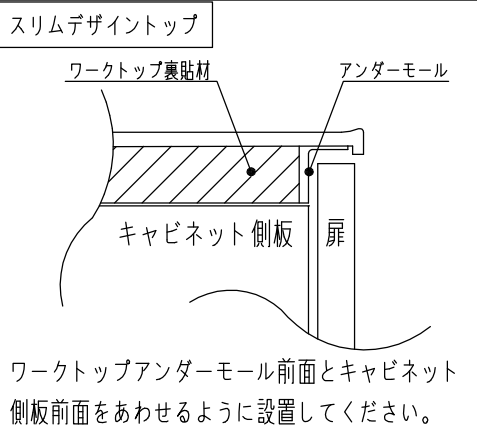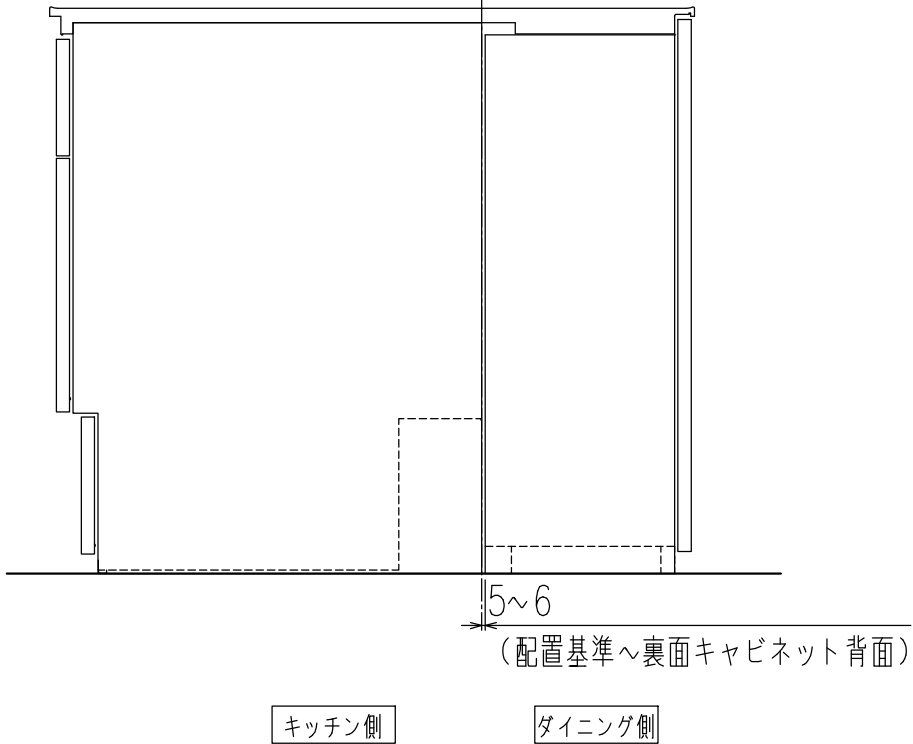


■ レンジフード取付注意事項（壁面取付時）


レンジフードを取付ける場合は下地の材が厚み30mm以上、幅100mm以上、ビス固定位置が材の端部から25mm以上であることを確認してください。
また、壁強度などの詳細は「レンジフード設置説明書」を必ず事前に確認してください。

取付位置については、取付設置図を確認してください。


参考図_CLS. SER. NST. ASR. ADR. RVJ. GSR. BFRS. TARシリーズ
(※RVJ. GSRシリーズの場合はレンジフードパネルの取付下地は不要です。)

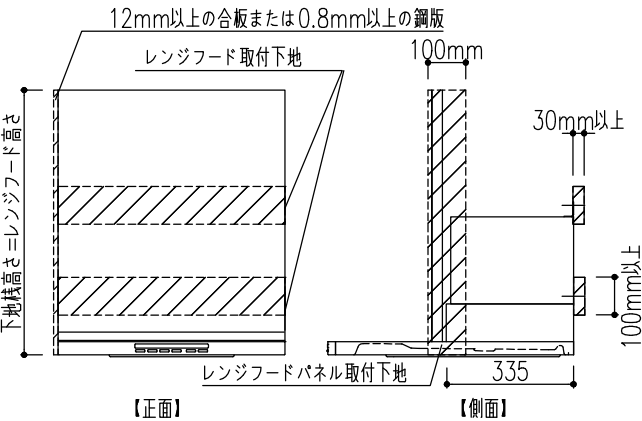

参考図_FED. HVR. NSDシリーズ（サイドマントルタイプ）

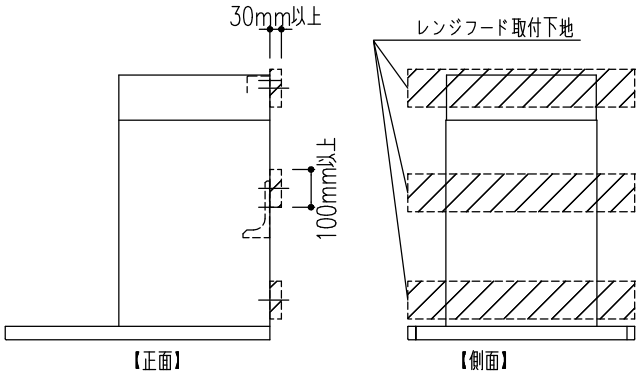

参考図_NBHシリーズ

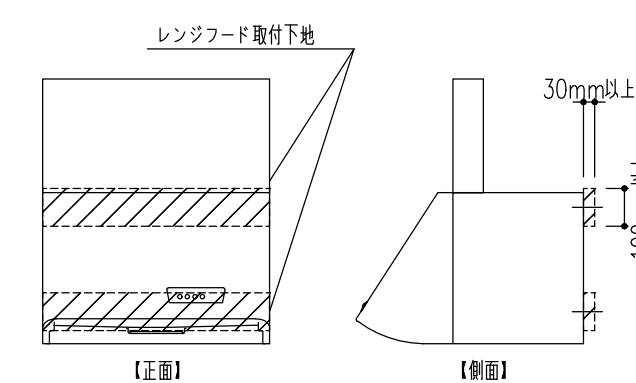

■ SMHVRフード

特性表

型名	定格電圧 (V)	定格周波数 (Hz)	消費電力 (W)	風量 (m³/h)	騒音 (dB)	製品質量 (Kg)	
SMHVR-93*	100	強	50	70	530	435	48
		中	50	28	370	—	39
		弱	50	11	220	—	28
		常時	50	7	155	—	22

電動機形式 8極DC ブラシレスモーター 絶縁抵抗 10MΩ以上 (500V時) 前電圧 AC100V 1分置 絶縁区分 E種
風量値はJIS C9603 4次元法による

静圧・風量 曲線 (静圧は静圧値)

静圧・風量 曲線 (静圧は静圧値)


付属品

品番	色調
SMHVR-93* S (R/L)	シルバー塗装
SMHVR-93* W (R/L)	ホワイト塗装

※付部詳細図 (S=1/2)

4. 製品名の末尾の () には材質/サイズによって記号が入る場合があります。
3. 電動シャッター (HDS150) (別売) を使用時は、中継ユニットを外して取り付けてください。
2. 赤外線連動型レンジフードです。単独でも使用できます。
1. 排気方向は側方 (L型) 外使用: 別売) と上方向です。


※ センターキッチンや対面キッチンユニットにキッチンパネルを奥行方向で分割かつガラスパネルがある場合は、継ぎ目位置がガラスパネルのセンターになるよう調整してください。

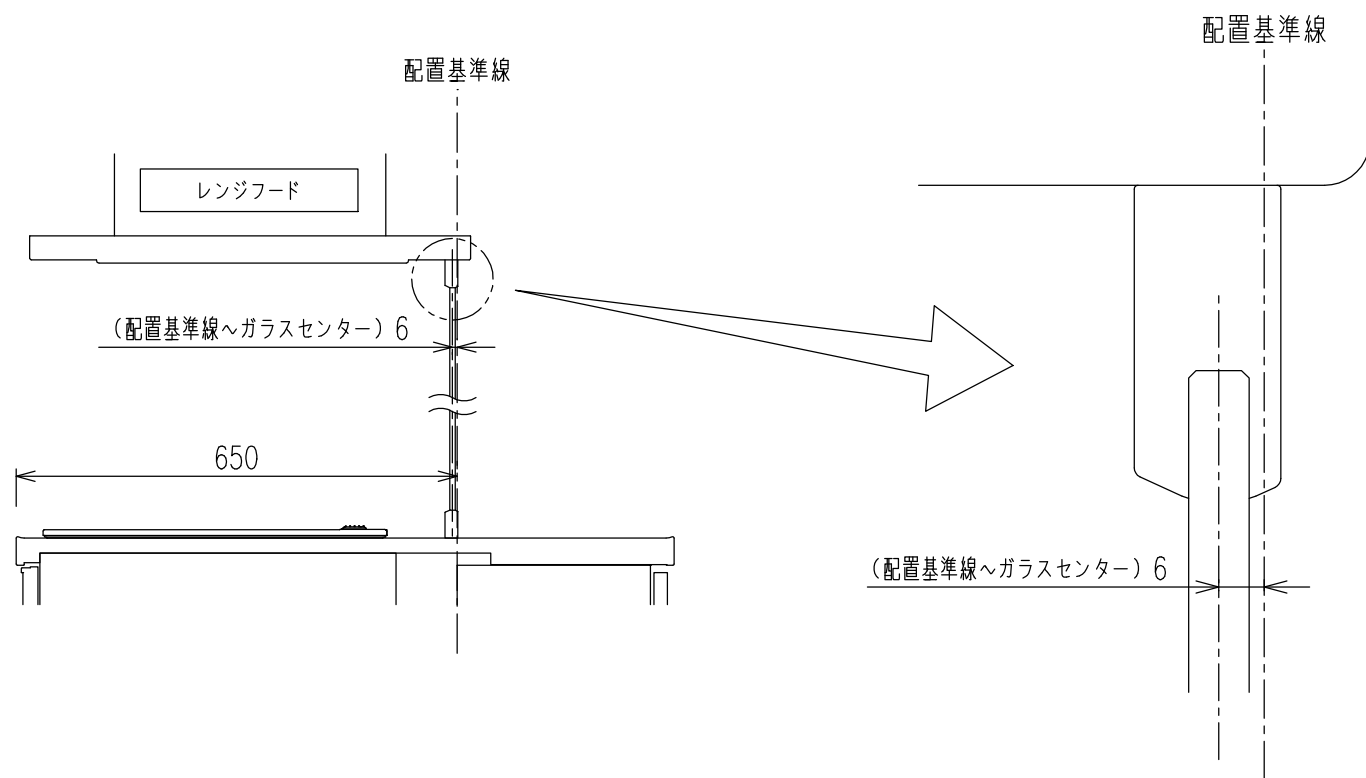

※コンセントや電源プラグが、引き出しおよびIHヒーター用仕切板（オプション）に接触しないように注意してください。


※木製キッチンの配管スペース付キャビネットは、キャビネット内にコンセントを取り付けるスペースがありませんので、別売のコンセントベース（W-SOCKET-B）などを使用して配管スペース内にコンセントを設置してください。

キッチン高さ	コンセント下端高さ	コンセントセンター高さ
800	355	400
850	405	450
900	455	500

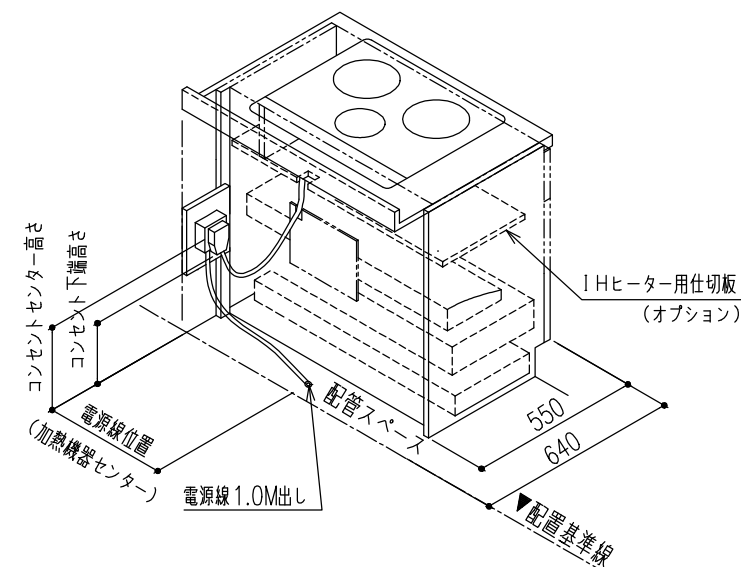

注意：引き出しおよびIHヒーター用仕切板（オプション）に接触しないように上記寸法を参照してください。

※イラスト表記の事前配管部材は現地手配

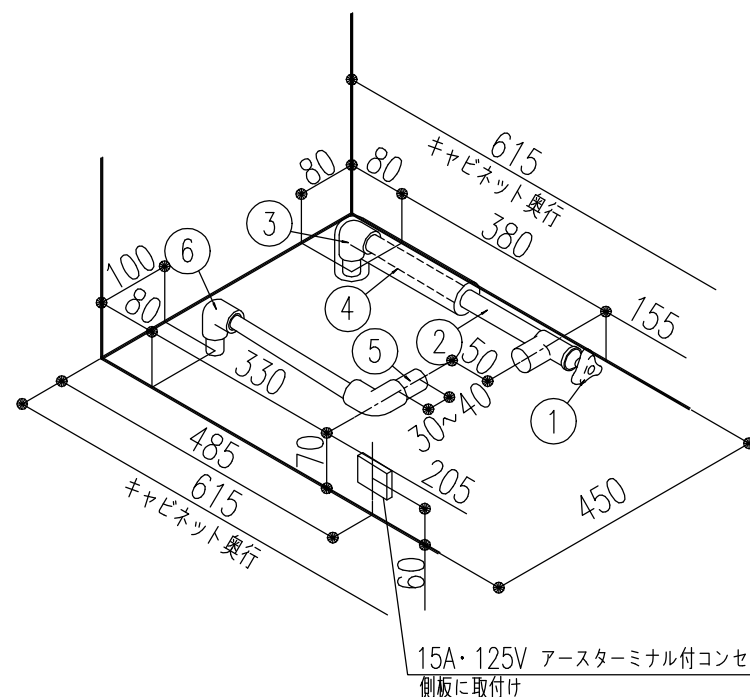

注意：配管立ち上げ位置は必ず本図の位置に立ち上げて下さい。

※給水接続か給湯接続かお客様に確認したうえで施工願います。

給水（給湯の場合は耐熱配管）

- ①アンゲル型止水栓（ハンドル式・固定ゴマタイプ）

※必ず固定コマタイプをご使用ください。

落としゴマタイプを使用すると、水栓内でコマが移動し、ゴトゴト音を生じる恐れがあります。

- ②硬質塩化ビニルライニング鋼管（相当品）
③RC1／2ソケット
④断熱材（Φ48）

排水（耐熱塩ビ使用のこと）


- ⑤排水パイプHT20
⑥HTエルボ

※配水管先端のエルボを上向きにしないでください。

キャビネットに当たるため、排水ホース折れの原因になります。


床立ち上げ配管

配管立ち上げ寸法は、止水栓芯までの高さを示しています。

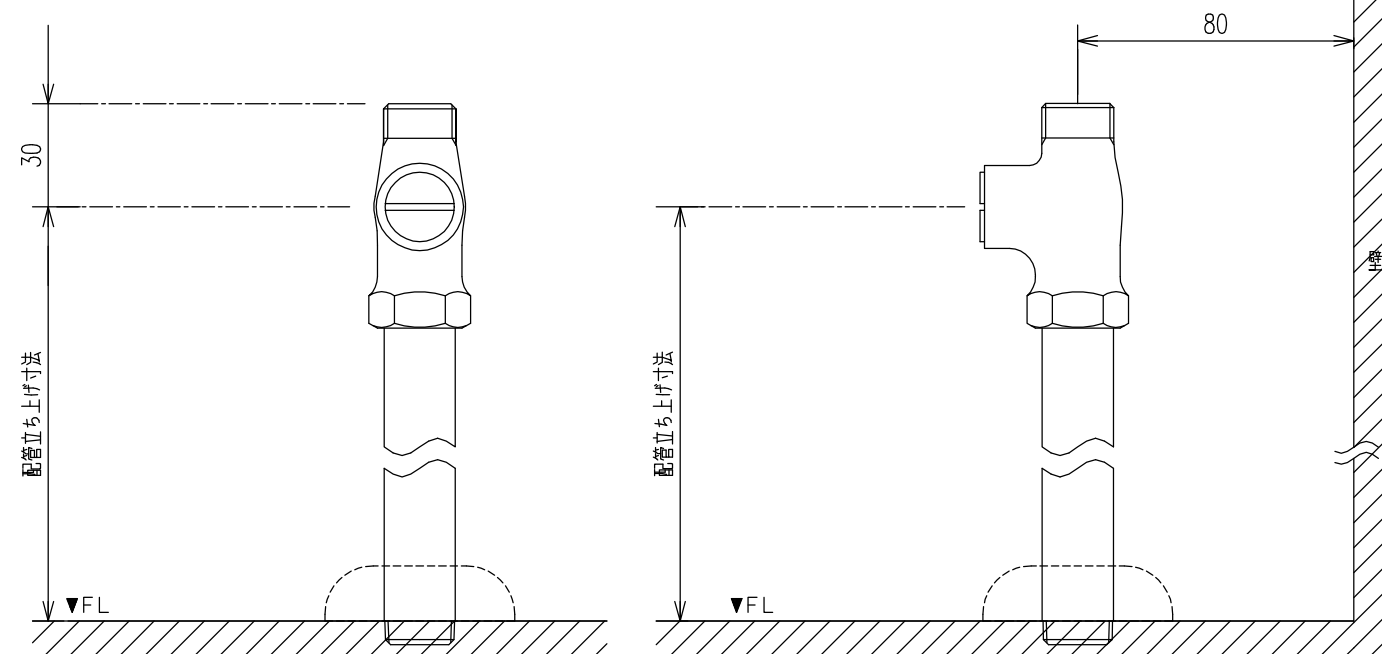

物件名	山村和孝 様邸	案件No.	図面名	担当	図面	図番 :
		A2512DDD0FOLLU	機能図	栗野 友仁		
仕様	ES21	見積No.	縮尺	日付		株式会社 LIXIL
		M26019847625-009-2		2026.03.17		

■ タッチレス水栓ナビッシュ 推奨電源位置図

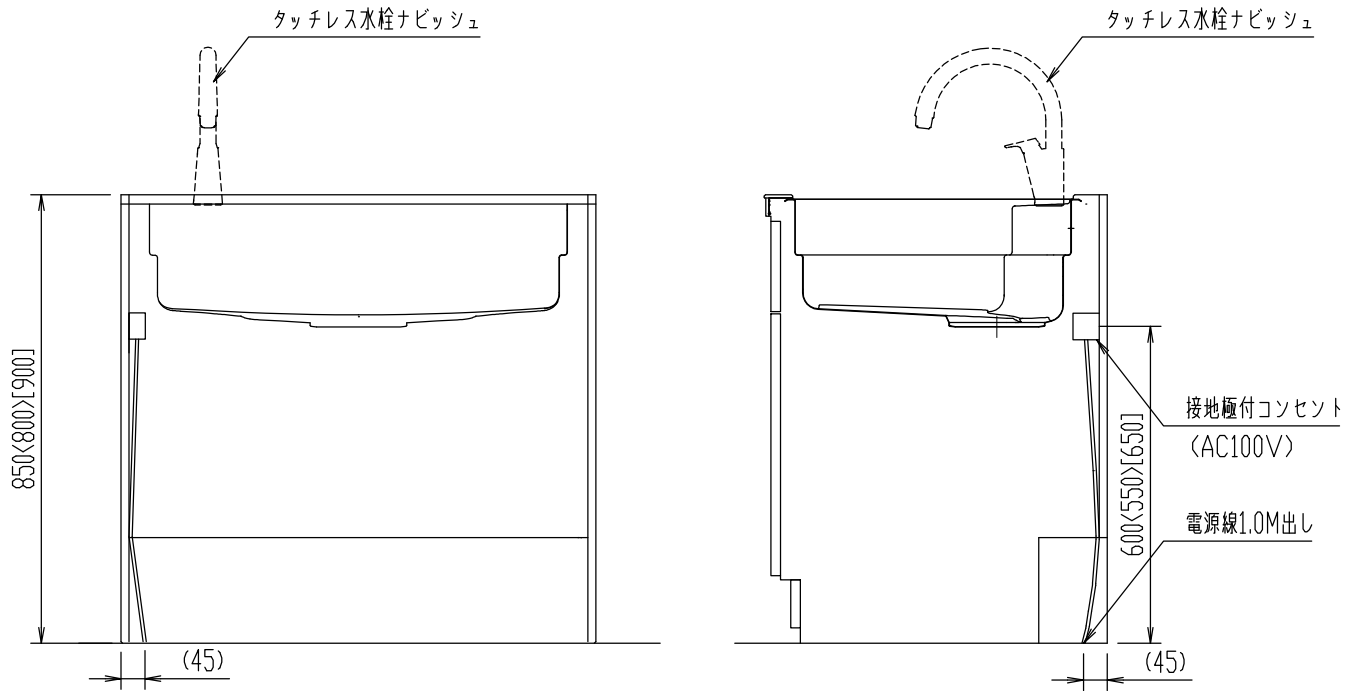

○水栓がシンク右側の場合、電源位置は左右対象の位置にしてください。
○水栓がシンク中央の場合、電源位置は左右どちらでも構いません。
○< >内寸法はワークトップ高さ80cmの場合、[]内寸法はワークトップ高さ90cmの場合。

特記事項 扉色 KK3:ソリッドブラック 取手 [F]ミドルハンドル（ブラック） ワークトップカラー 【DW】ソルティホワイト	物件名 山村和孝 様邸	案件No.	図面名	担当	図面	図番
		A2512DDD0FOLLU	機能図	栗野 友仁		株式会社 LIXIL
		見積No.	縮尺	日付		
		M26019847625-009-2		2026.03.17		
仕様	ES21					

■ キッチン取付者さま向け 動画コンテンツ ■
商品取付けの注意点を2次元コードでご視聴いただけます。
取付日より前に、是非ご確認ください。

1 ページ目

■ キッチン取付者さま向け 動画コンテンツ ■


商品取付けの注意点を2次元コードでご視聴いただけます。
取付日より前に、是非ご確認ください。


1 ページ目


■ キッチン取付者さま向け 動画コンテンツ ■


商品取付けの注意点を2次元コードでご視聴いただけます。
取付日より前に、是非ご確認ください。



1 ページ目


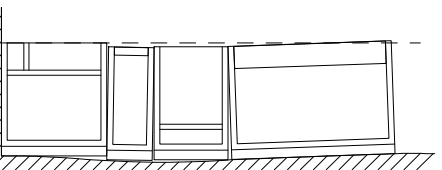
荷扱い・搬入 荷扱い・搬入  作成日：2024年10月01日	カウンター開梱搬入「養生ツール」 カウンター開梱搬入 「養生ツール」のご紹介  作成日：2024年10月01日 改定日：2025年12月11日	不陸の確認と調整   作成日：2024年02月07日	マグネットキッチンパネル マグネット キッチンパネル 「取付・設置」ポイント  作成日：2024年03月06日
--	---	--	---

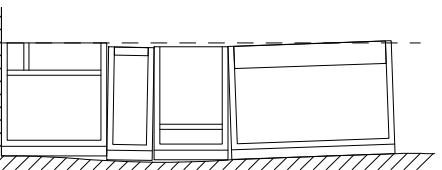
荷扱い・搬入 荷扱い・搬入  作成日：2024年10月01日	カウンター開梱搬入「養生ツール」 カウンター開梱搬入 「養生ツール」のご紹介  作成日：2024年10月01日 改定日：2025年12月11日	不陸の確認と調整   作成日：2024年02月07日	マグネットキッチンパネル マグネット キッチンパネル 「取付・設置」ポイント  作成日：2024年03月06日
--	---	--	---


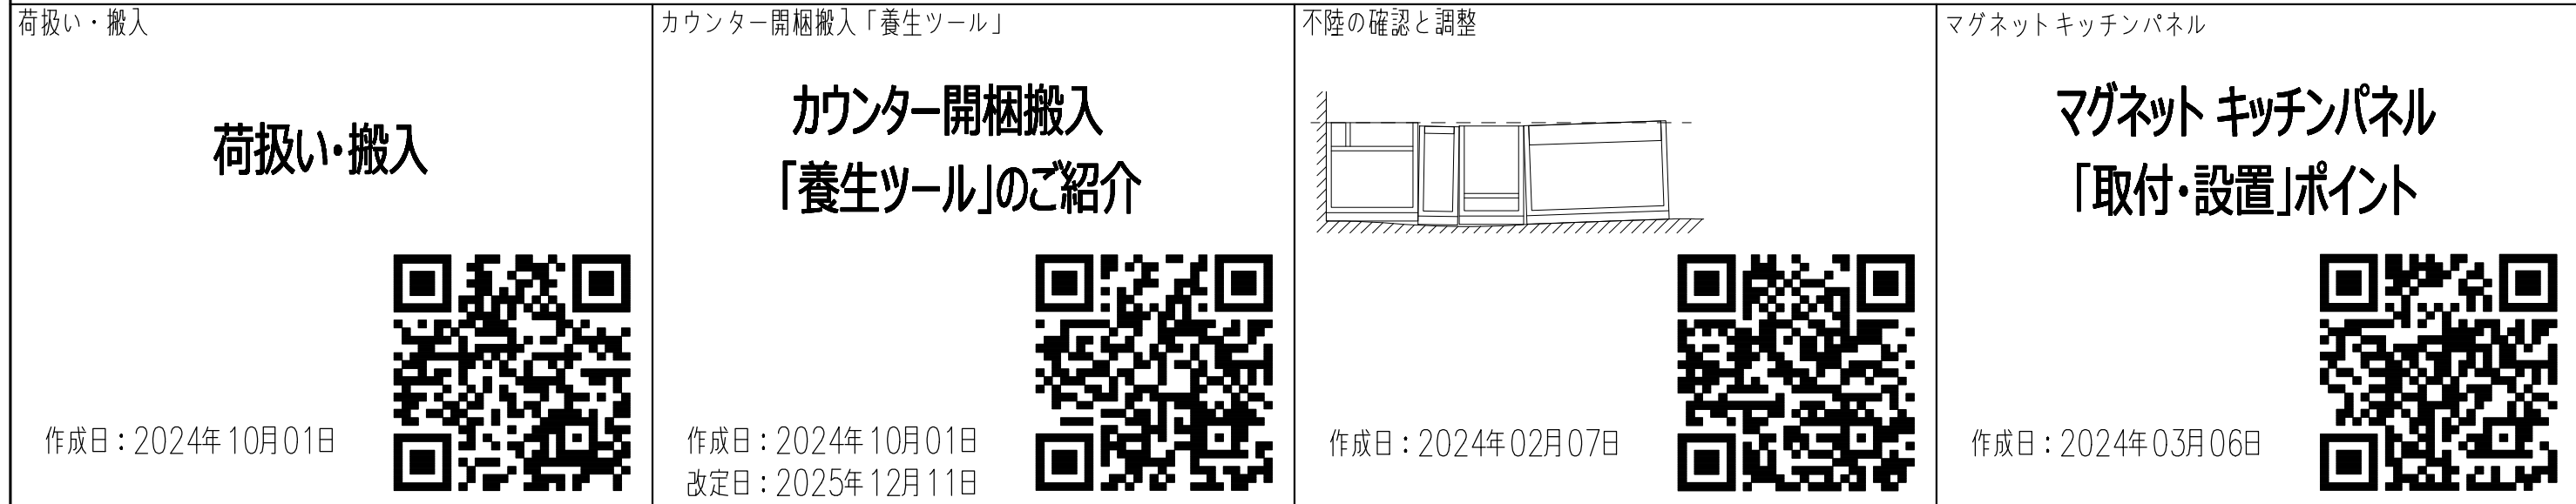



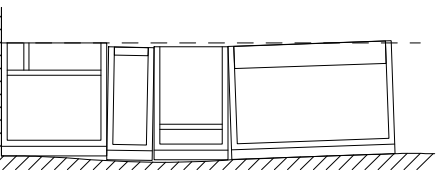
荷扱い・搬入 荷扱い・搬入  作成日：2024年10月01日	カウンター開梱搬入「養生ツール」 カウンター開梱搬入 「養生ツール」のご紹介  作成日：2024年10月01日 改定日：2025年12月11日	不陸の確認と調整   作成日：2024年02月07日	マグネットキッチンパネル マグネット キッチンパネル 「取付・設置」ポイント  作成日：2024年03月06日
--	---	--	---

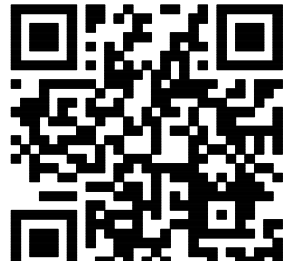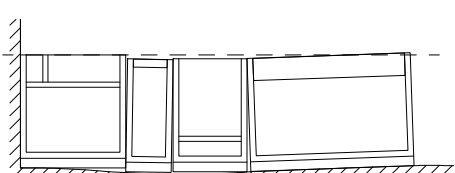カウンター開梱搬入「養生ツール」 カウンター開梱搬入 「養生ツール」のご紹介  作成日：2024年10月01日 改定日：2025年12月11日	不陸の確認と調整  作成日：2024年02月07日	マグネットキッチンパネル マグネット キッチンパネル 「取付・設置」ポイント  作成日：2024年03月06日
---	--	---

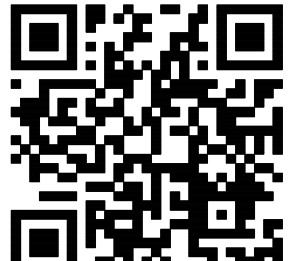
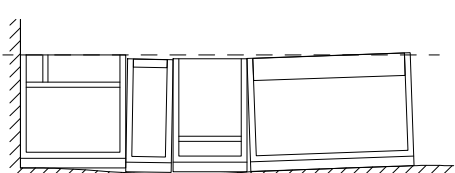
カウンター開梱搬入「養生ツール」 カウンター開梱搬入 「養生ツール」のご紹介  作成日：2024年10月01日 改定日：2025年12月11日	不陸の確認と調整  作成日：2024年02月07日	マグネットキッチンパネル マグネット キッチンパネル 「取付・設置」ポイント  作成日：2024年03月06日
---	--	---

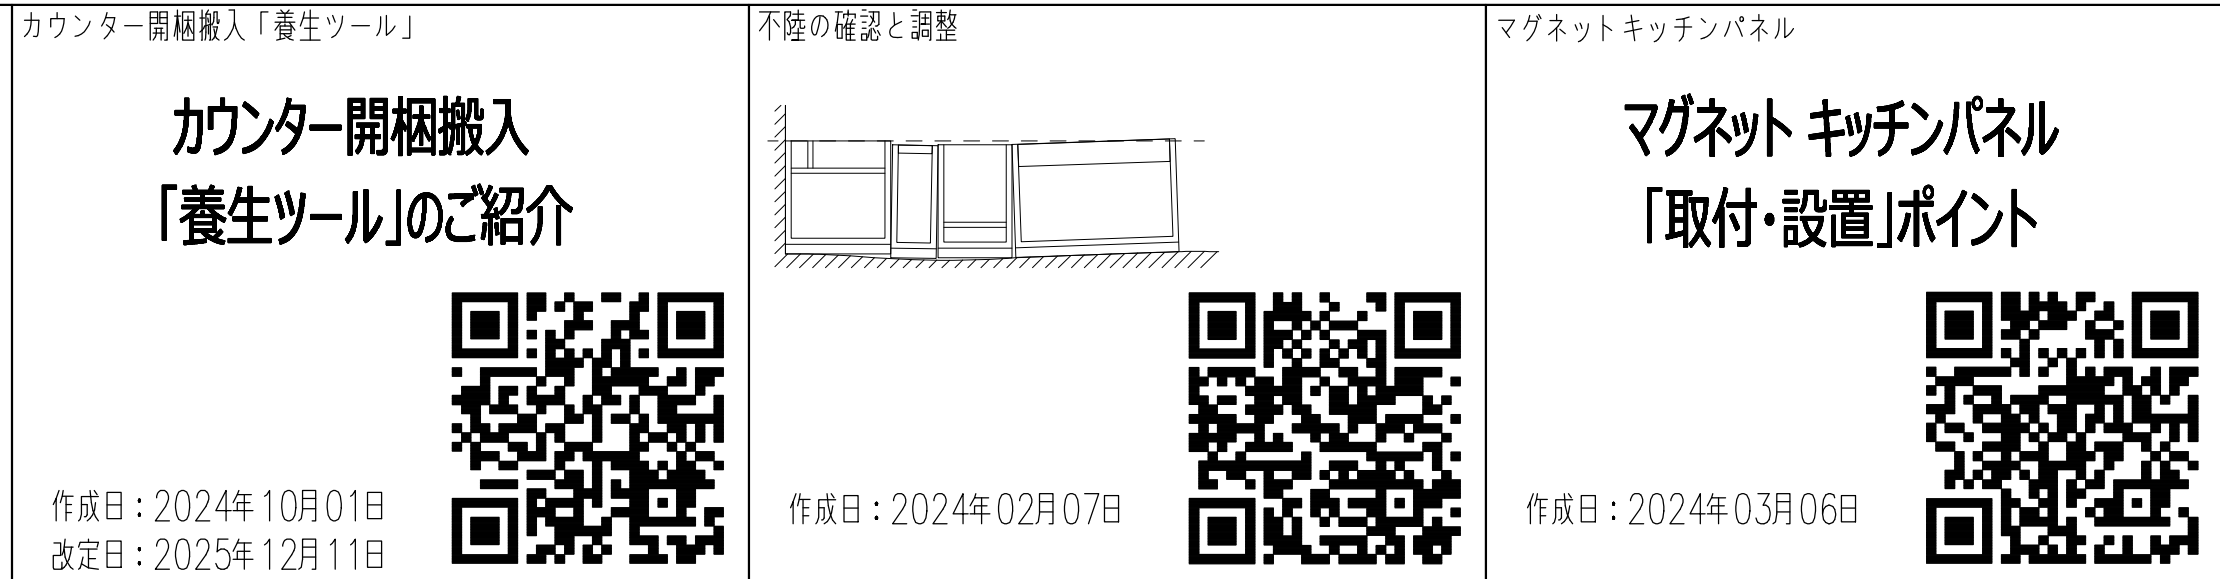

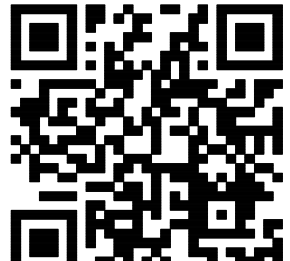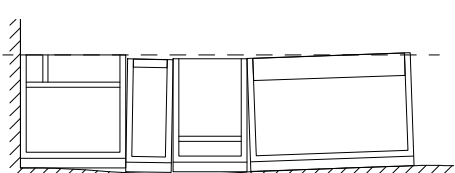カウンター開梱搬入「養生ツール」 カウンター開梱搬入 「養生ツール」のご紹介  作成日：2024年10月01日 改定日：2025年12月11日	不陸の確認と調整  作成日：2024年02月07日	マグネットキッチンパネル マグネット キッチンパネル 「取付・設置」ポイント  作成日：2024年03月06日
---	--	---

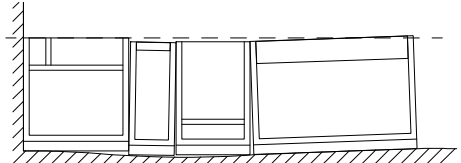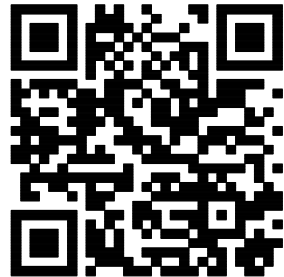不陸の確認と調整  作成日：2024年02月07日 	マグネットキッチンパネル マグネット キッチンパネル 「取付・設置」ポイント  作成日：2024年03月06日
--	---

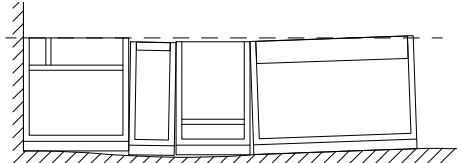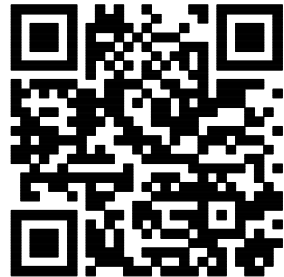

不陸の確認と調整  作成日：2024年02月07日 	マグネットキッチンパネル マグネット キッチンパネル 「取付・設置」ポイント  作成日：2024年03月06日
--	---

マグネット キッチンパネル

マグネット キッチンパネル 「取付・設置」ポイント



作成日：2024年03月06日

マグネット キッチンパネル

マグネット キッチンパネル 「取付・設置」ポイント



作成日：2024年03月06日






マグネット キッチンパネル



マグネット キッチンパネル 「取付・設置」ポイント





作成日：2024年03月06日

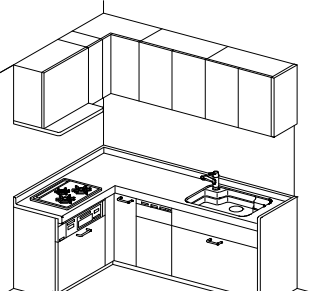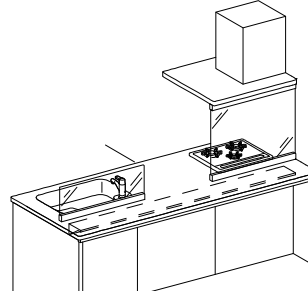人造大理石カウンターL型キッチン   作成日：2024年02月07日	センターキッチン（ペニンシュラ型）   作成日：2024年02月07日		
---	---	--	--

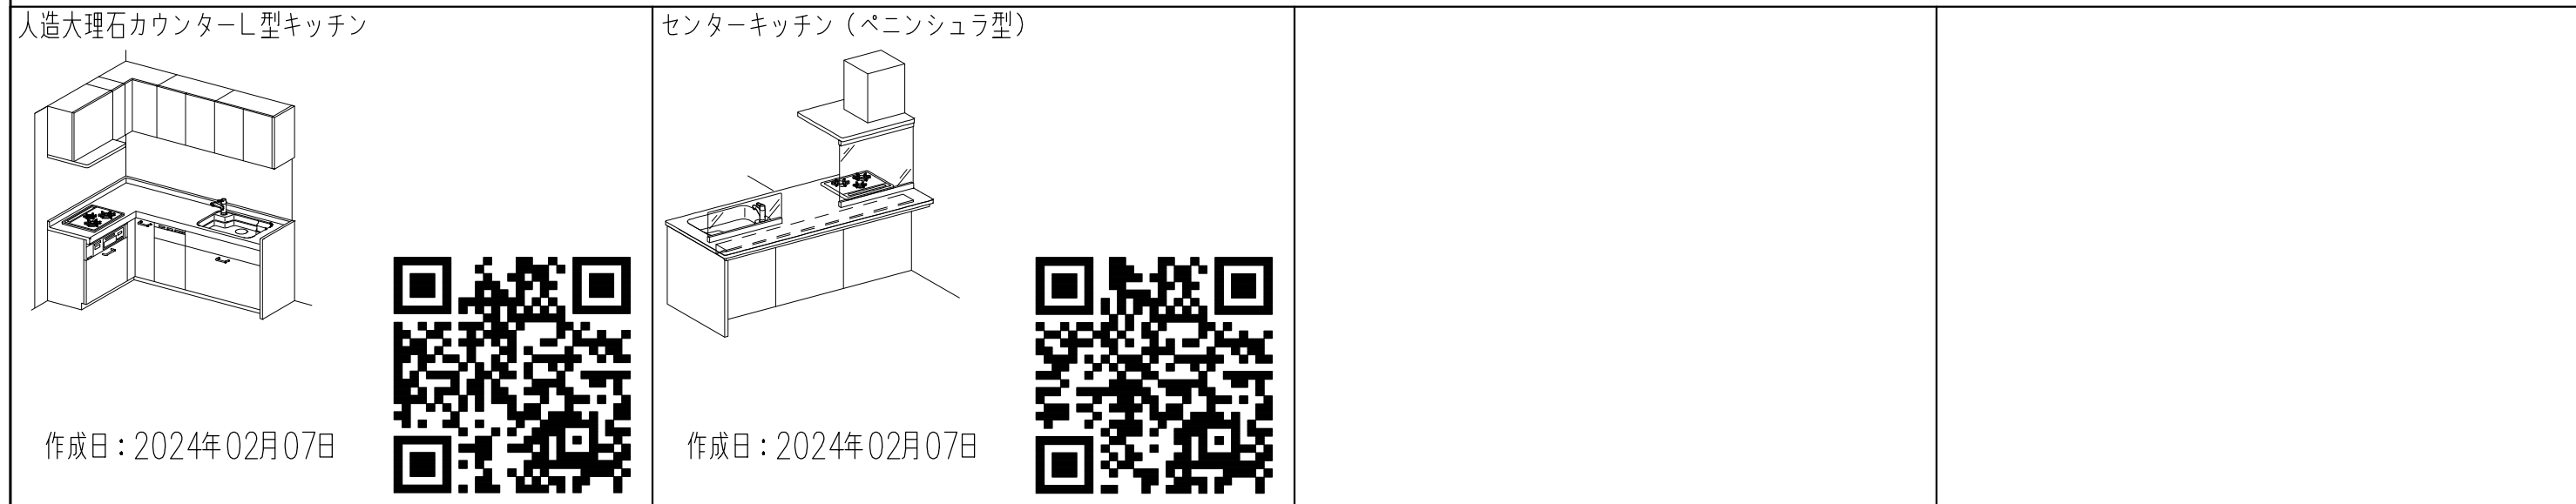


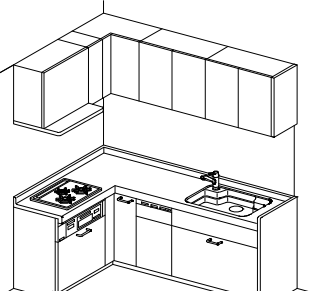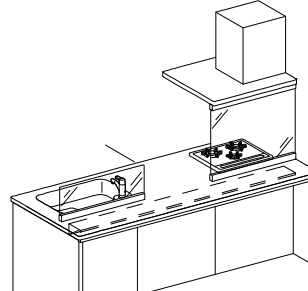人造大理石カウンターL型キッチン   作成日：2024年02月07日	センターキッチン（ペニンシュラ型）   作成日：2024年02月07日		
---	---	--	--

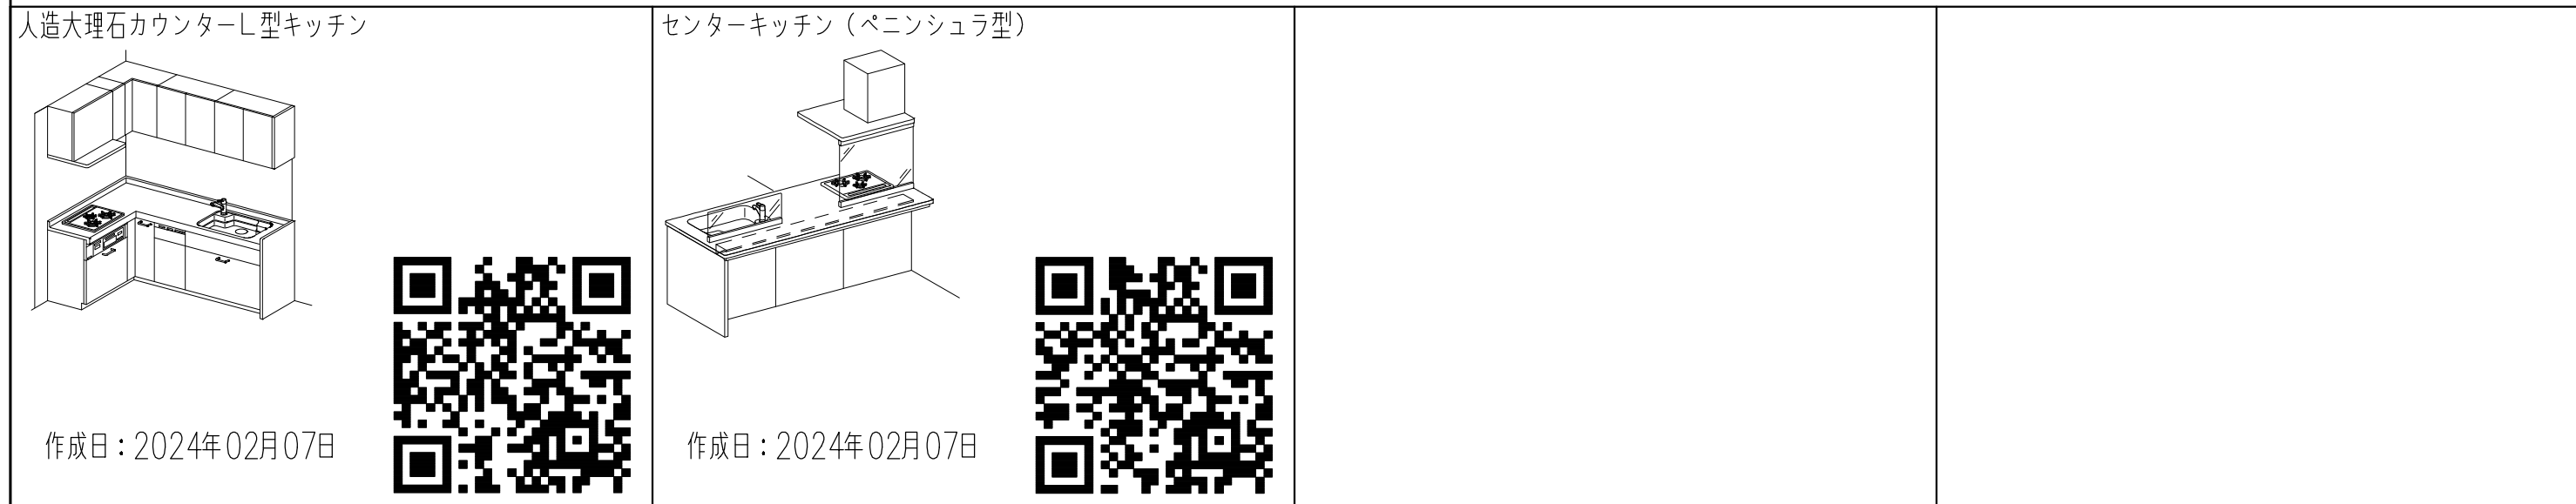

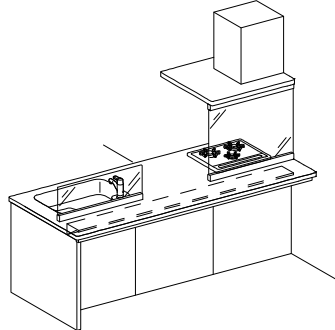センターキッチン（ペニンシュラ型）  作成日：2024年02月07日		
---	--	--

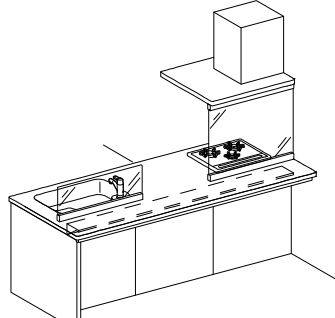






センターキッチン（ペニンシュラ型）  作成日：2024年02月07日		
---	--	--

		特記事項 扉色 KK3:ソリッドブラック 取手 [F]ミドルハンドル (ブラック) ワークトップカラー 【DW】ソルティホワイト	物件名 仕様	山村和孝 様邸 ES21		案件No.	図面名	担当	図面	図番
						A2512DDD0FOLLU	機能図	栗野 友仁		株式会社 LIXIL
						見積No.	縮尺	日付		
						M26019847625-009-2		2026.03.17		

■ キッチン取付者さま向け 動画コンテンツ ■

商品取付けの注意点を２次元コードでご視聴いただけます。
取付日より前に、是非ご確認ください。

2 ペー ジ

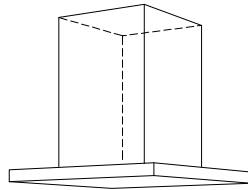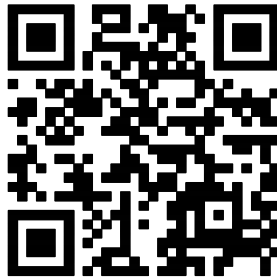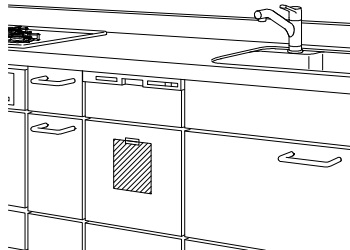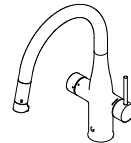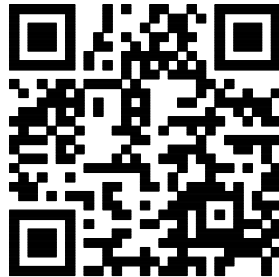センターフード型レンジフード (天吊りフード)  作成日：2024年06月03日 		I H加熱機器関連 I H加熱機器 仕切り板 作成日：2024年02月07日 		食器洗い乾燥機  作成日：2024年02月07日 		ミネラル浄水栓 Greentap  作成日：2024年06月03日 			

	特記事項 扉色 KK3:ソリッドブラック 取手 [F]ミドルハンドル (ブラック) ワークトップカラー 【DW】 ソルティホワイト	物件名	山村和孝 様邸	案件No.	図面名	担当	図面	図番 ：	
				A2512DDD0FOLLU	機能図	栗野 友仁			
				見積No.	縮尺	日付			
				M26019847625-009-2		2026.03.17			
		仕様	ES21					株式会社 LIXIL	