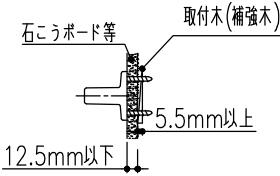
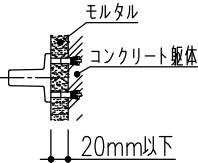
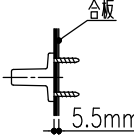
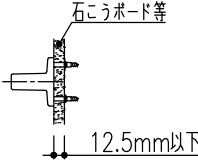
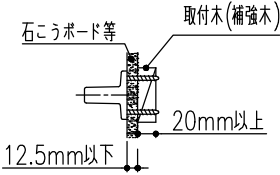
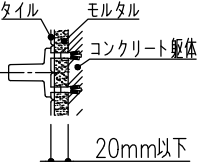
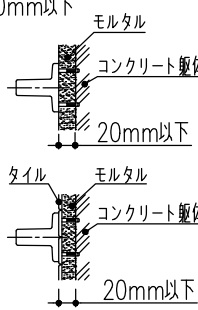
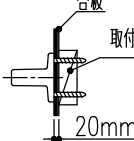
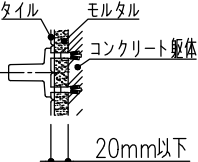
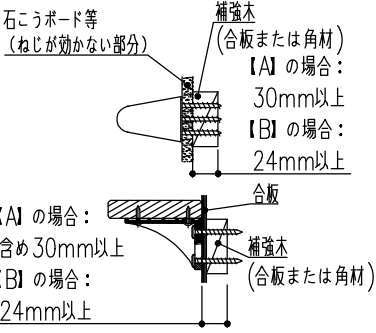
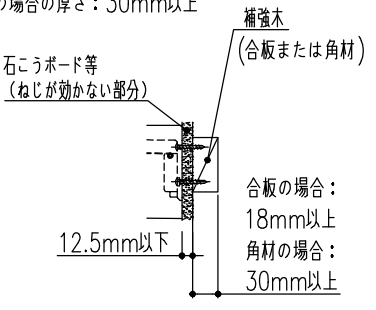
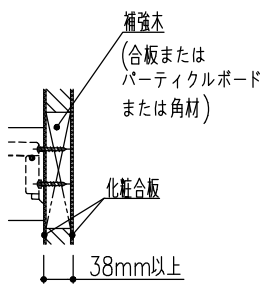
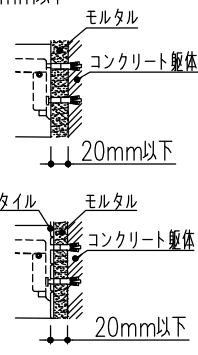



●アクセサリー 施工要領図

壁取付アクセサリーの落下事故防止のため、取付部材（木ねじ、AYボルト等）の固定強度（種類・数）については十分配慮を行っておりますが、壁面の構造についても配慮いただくことが不可欠です。

アクセサリー種類	乾式壁			湿式壁	
	木ねじ	木ねじ＋プラスチックプラグ	パーテーション壁	AYボルト	木ねじ＋プラスチックプラグ
紙巻器 化粧鏡 石けん入れ	ねじ込み深さ：5.5mm以上 	取付不可	取付不可	壁仕上材厚さ：20mm以下 	取付不可
化粧鏡		石こうボード壁厚：9.5mm以上 12.5mm以下 			
紙巻器 石けん入れ	ねじ込み深さ：20mm以上 	取付不可		壁仕上材厚さ：20mm以下 	壁仕上材厚さ：20mm以下 
フック タオル掛 化粧棚 紙巻器 タオルリング 化粧鏡 スベアペーパーホルダー サニタリーボックス	ねじ込み深さ：20mm以上 	取付不可		壁仕上材厚さ：20mm以下 	取付不可
【A】 アクセサリーパー 棚手すり (NKF-2W系・3W系・6W系) 紙巻器 タオル棚 手すり 照明付鏡 【B】 カウンター(NKF-70系・80系) 棚手すり(NKF-20系・30系)	ねじ込み深さ：【A】補強木(合板または角材)30mm以上 【B】構造用合板24mm以上※2枚合わせ可 				
棚付二連紙巻器 横2連ストック付紙巻器 横4連ストック付紙巻器	合板の場合の厚さ：18mm以上 角材の場合の厚さ：30mm以上 		パーテーション (化粧合板＋補強木)の厚さ：38mm以上 	壁仕上材厚さ：20mm以下 	


	特記事項	物件名	山村和孝 様邸	案件No.	図面名	担当	図面	図番	株式会社 LIXIL	
				A2512DDDOFOLLU	機能図	栗野 友仁				
			仕様	ベーシアハーモ Jタイプ/ECO5 床排水 一般地・水抜方式・流動方式兼用	見積No.	縮尺	日付			
					M26019847625-009-5		2026.03.17			

●ベーシアハーモJタイプ取付最小スペース

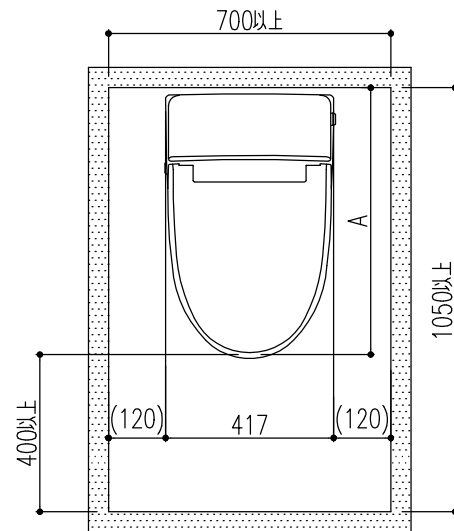


- ※ 最少スペースはA寸法(前出寸法)+400となり、便器排水方向や既設配管により、異なります。
- ※ 上図の空間寸法は、衣服の着脱などの行為に必要な最低寸法です。手すりや紙巻器などの機器を併設する場合は、必要に応じて広い空間が必要になります。
- ※ 便器に向かって左右共に120mm以上の空間を確保してください。

●ベ－シアハーモJタイプ便フタ開時寸法

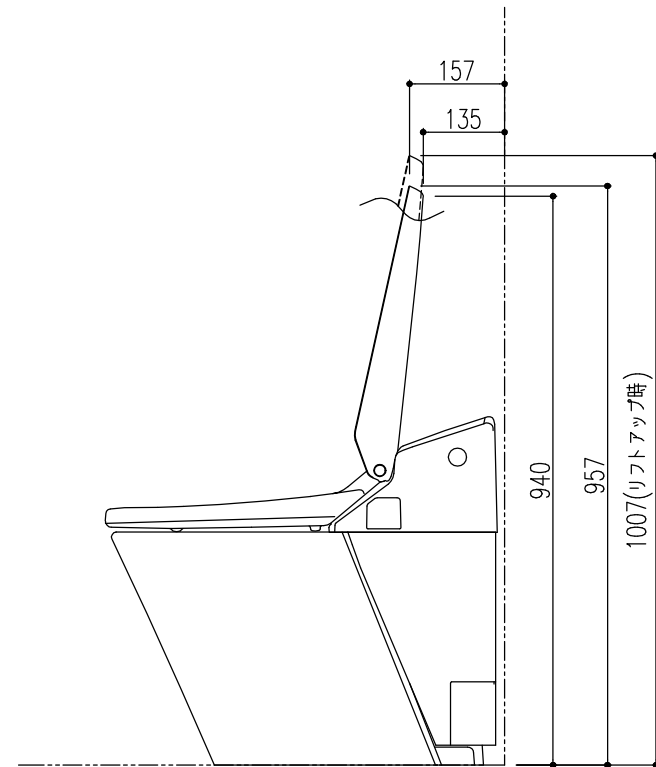

- ※上図は代表商品のイメージ図です。
※防振シートを組み合わせる場合は、全体が5mm高くなります。

●便器床設置面寸法・固定穴寸法

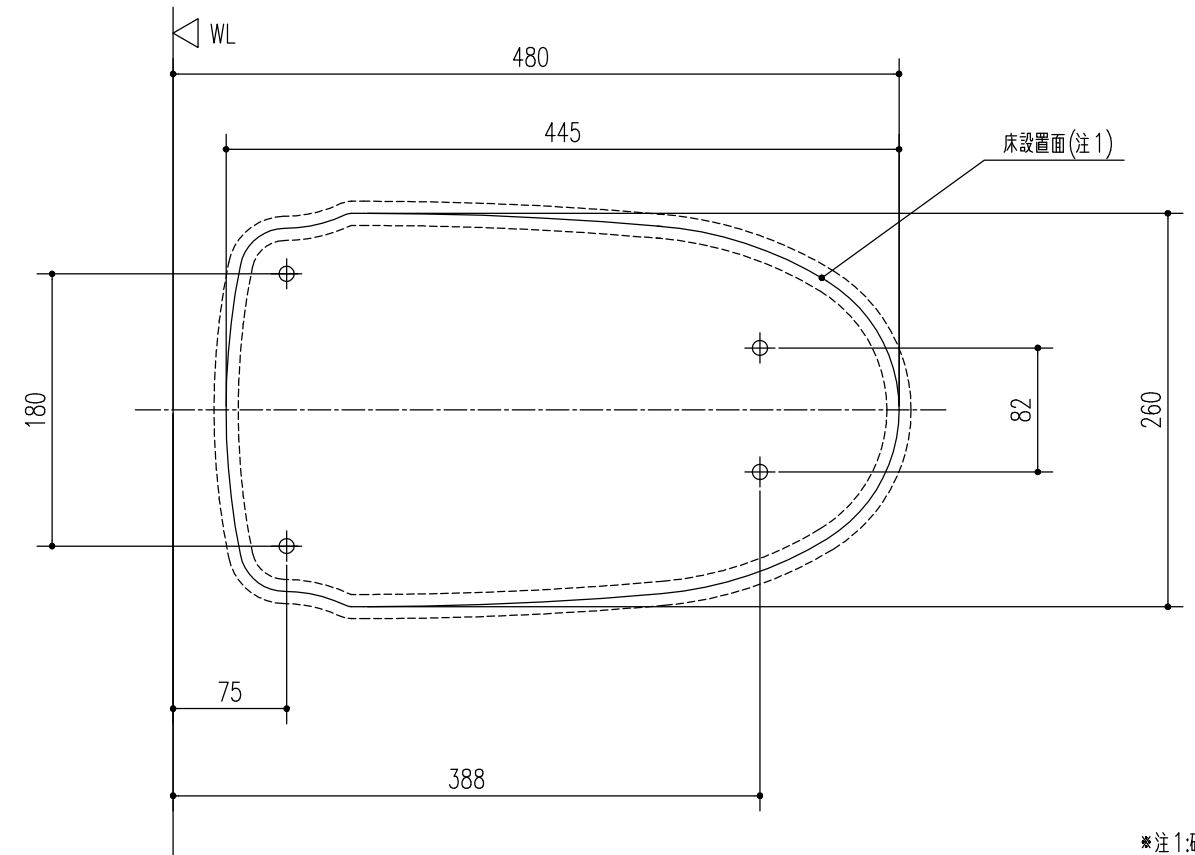


※注1:破線は±5%許容差範囲

●給排水の位置決めと取出し


給水管、排水管を取り出します。

- ※ 右給水の場合は、排水管を中心に左右反対の位置に給水管を取り出してください。
- ※ 右給水の場合は、給水ホース(322-1135-62)を別途手配してください。

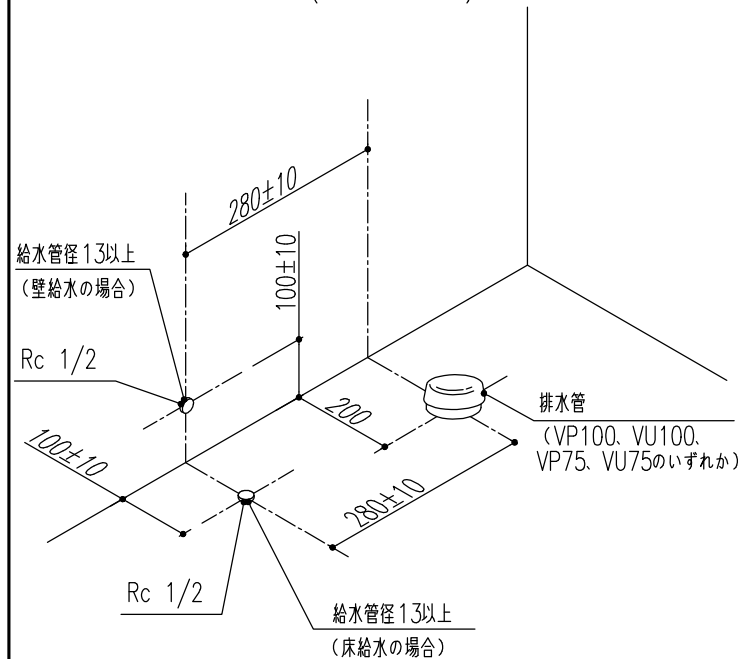



●排水塩ビ管の接続

- * 排水芯200のみの対応です。
- * 接続は、塩ビ接着剤にて確実に行なって下さい。
- * 接続(接着)位置及び立ち上げ高さは、配管サイズにより異なります。

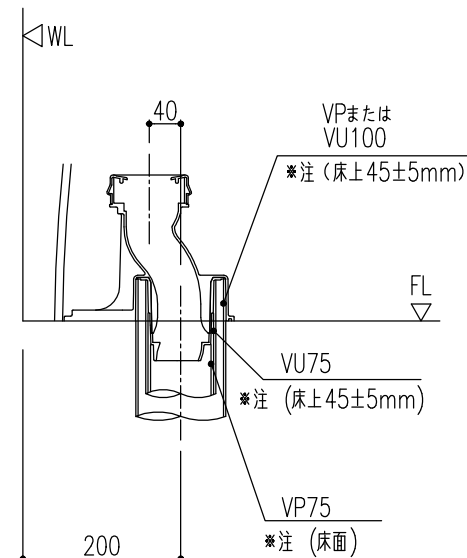


*注…防振シートを組み合わせる場合は5mm高くしてください。

物件名	山村和孝 様邸	案件No.	図面名	担当	図面	図番 :
		A2512DDD0FOLLU	機能図	栗野 友仁		
仕様	ベーシアハーモJタイプ/EC05 床排水 一般地・水抜方式・流動方式兼用	見積No.	縮尺	日付		株式会社 LIXIL
		M26019847625-009-5		2026.03.17		

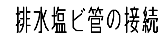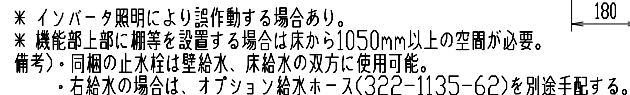

- * 排水芯200のみの対応です。
- * 接続は、塩ビ接着剤にて確実に行なって下さい。
- * 接続（接着）位置及び立ち上げ高さは、配管サイズにより異なります。

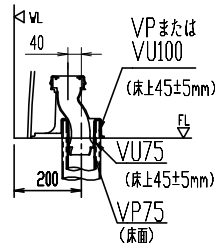

YBC-J22S

洋風ダイレクトバルブ防露便器(シャワートイレ)

節水

洗淨水量：大5L、小3.8L

[illegible]

- ※ 製品両側面に120mm以上、背面に15mm以上の空間確保。
※ 設置前に水压判定治具(CWA-234)で、水压の確認を行ってください。

- ※ 静水压0.15MPa、流動圧0.05MPa(瞬間流量13L/min)以上が必要。
 - ※ 最高水压0.75MPa以下(静水压)。※ 給水管径φ13以上。
 - ※ D種接地工事必要。アース・シールド接地極付コネクタを使用のこと。
 - ※ 一般地用、寒冷地用水板式、寒冷地用流動式を兼用。※ 凍結防止には器具への通電が必要。
- 【寒冷地用水板式の場合】トイレ内使用限界：0℃以上(室内暖房)、器具の水抜き。
- 【寒冷地用流動式の場合】トイレ内使用限界：0℃以上(室内暖房)、流動水量40L/h。

縮尺	製図	大塚	検図	松本	備考	
1:20	図番	GS-CJ22S-100013A/31338				
日付						
2026.01.18	株式会社 LIXIL					

陶器寸法許容差はJIS A5207に準ずる。壁取付商品には、補強木による壁補強が必要です。詳しくは、商品別「壁補強」一覧を参照ください。

