


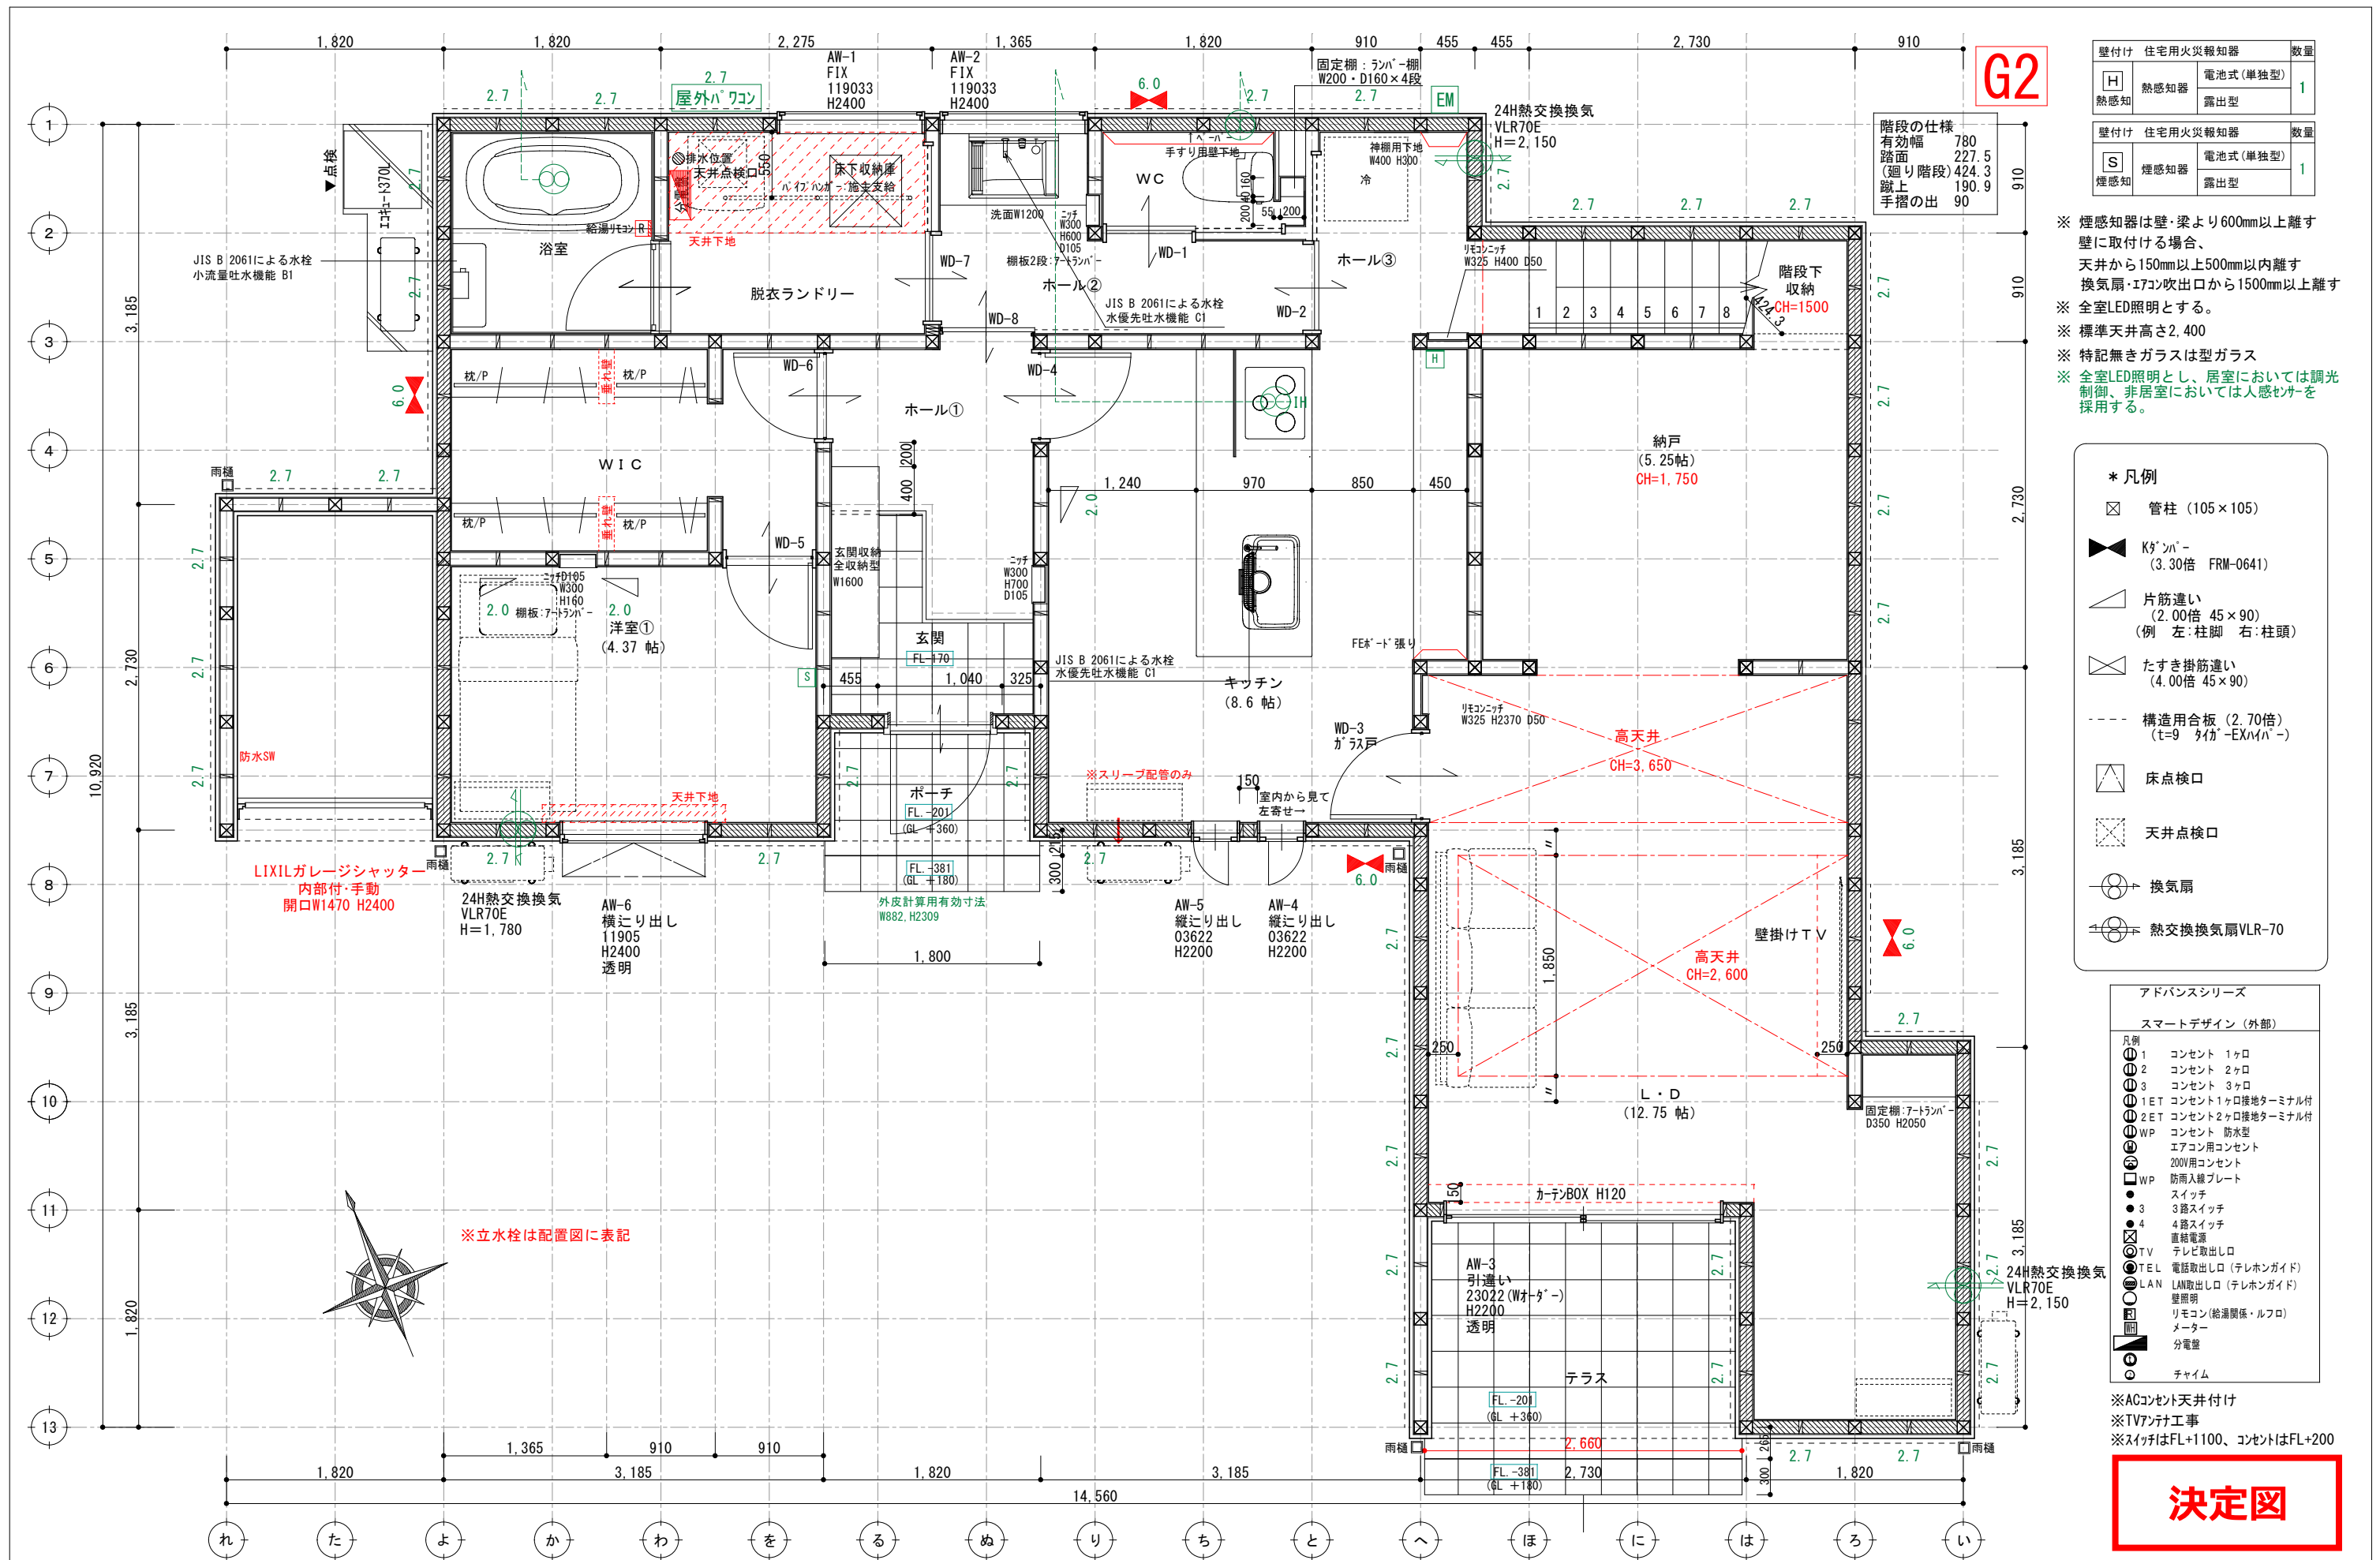

壁付け 住宅用火災報知器			数量
H	熱感知器	電池式(単独型)	1
	熱感知	露出型	
壁付け 住宅用火災報知器			数量
S	煙感知器	電池式(単独型)	1
	煙感知	露出型	

※ 煙感知器は壁・梁より600mm以上離す
壁に取付ける場合、
天井から150mm以上500mm以内離す
換気扇・エアコン吹出口から1500mm以上離す
※ 全室LED照明とする。
※ 標準天井高さ2,400
※ 特記無きガラスは型ガラス
※ 全室LED照明とし、居室においては調光
制御、非居室においては人感センサー
を採用する。

- * 凡例**
- 管柱 (105×105)
 - K*ンバー (3.30倍 FRM-0641)
 - 片筋違い (2.00倍 45×90)
(例 左:柱脚 右:柱頭)
 - たすき掛筋違い (4.00倍 45×90)
 - 構造用合板 (2.70倍)
(t=9 タイパ-EXハイパ-)
 - 床点検口
 - 天井点検口
 - 換気扇
 - 熱交換換気扇VLR-70

アドバンスシリーズ	
スマートデザイン (外部)	
凡例	
1	コンセント 1ヶ所
2	コンセント 2ヶ所
3	コンセント 3ヶ所
1ET	コンセント1ヶ所接地ターミナル付
2ET	コンセント2ヶ所接地ターミナル付
WP	コンセント 防水型
WP	エアコン用コンセント
WP	200V用コンセント
WP	防雨入線プレート
WP	スイッチ
3	3路スイッチ
4	4路スイッチ
TV	直結電源
TEL	テレビ取出口
TEL	電話取出口 (テレビガイド)
LAN	LAN取出口 (テレビガイド)
TEL	壁照明
TEL	リモコン (給湯関係・ルフロ)
TEL	メーター
TEL	分電盤
TEL	チャイム

※ACコンセント天井付け
※TVアンテナ工事
※スイッチはFL+1100、コンセントはFL+200

決定図