

G2

壁付け 住宅用火災報知器			数量
熱感知	H	電池式(単独型)	
		露出型	
壁付け 住宅用火災報知器			数量
煙感知	S	電池式(単独型)	4
		露出型	

- ※ 煙感知器は壁・梁より600mm以上離す
壁に取付ける場合、
天井から150mm以上500mm以内離す
換気扇・エアコン吹出口から1500mm以上離す
- ※ 全室LED照明とする。
- ※ 標準天井高さ2,400
- ※ 特記無きガラスは型ガラス
- ※ 全室LED照明とし、居室においては調光制御、非居室においては人感センサーを採用する。

* 凡例

- 管柱 (105 × 105)
- K&Pバー (3.30倍 FRM-0641)
- 片筋違い (2.00倍 45 × 90)
(例 左: 柱脚 右: 柱頭)
- たすき掛筋違い (4.00倍 45 × 90)
- 構造用合板 (2.70倍)
(t=9 タイガ EXNバー)
- 床点検口
- 天井点検口
- 換気扇
- 熱交換換気扇VLR-70


アドバンスシリーズ

スマートデザイン (外部)

- 凡例
- 1 コンセント 1ヶ所
- 2 コンセント 2ヶ所
- 3 コンセント 3ヶ所
- 1ET コンセント1ヶ所接地ターミナル付
- 2ET コンセント2ヶ所接地ターミナル付
- WP コンセント 防水型
- エアコン用コンセント
- 200V用コンセント
- WP 防雨入線プレート
- スイッチ
- 3 3路スイッチ
- 4 4路スイッチ
- 直結電源
- TEL テレビ取出口
- TEL 電話取出口 (テレホンガイド)
- LAN LAN取出口 (テレホンガイド)
- 壁照明
- リモコン (給湯関係・ルフロ)
- メーター
- 分電盤
- チャイム

- ※ACコンセント天井付け
- ※TVアンテナ工事
- ※スイッチはFL+1100、コンセントはFL+200

決定図

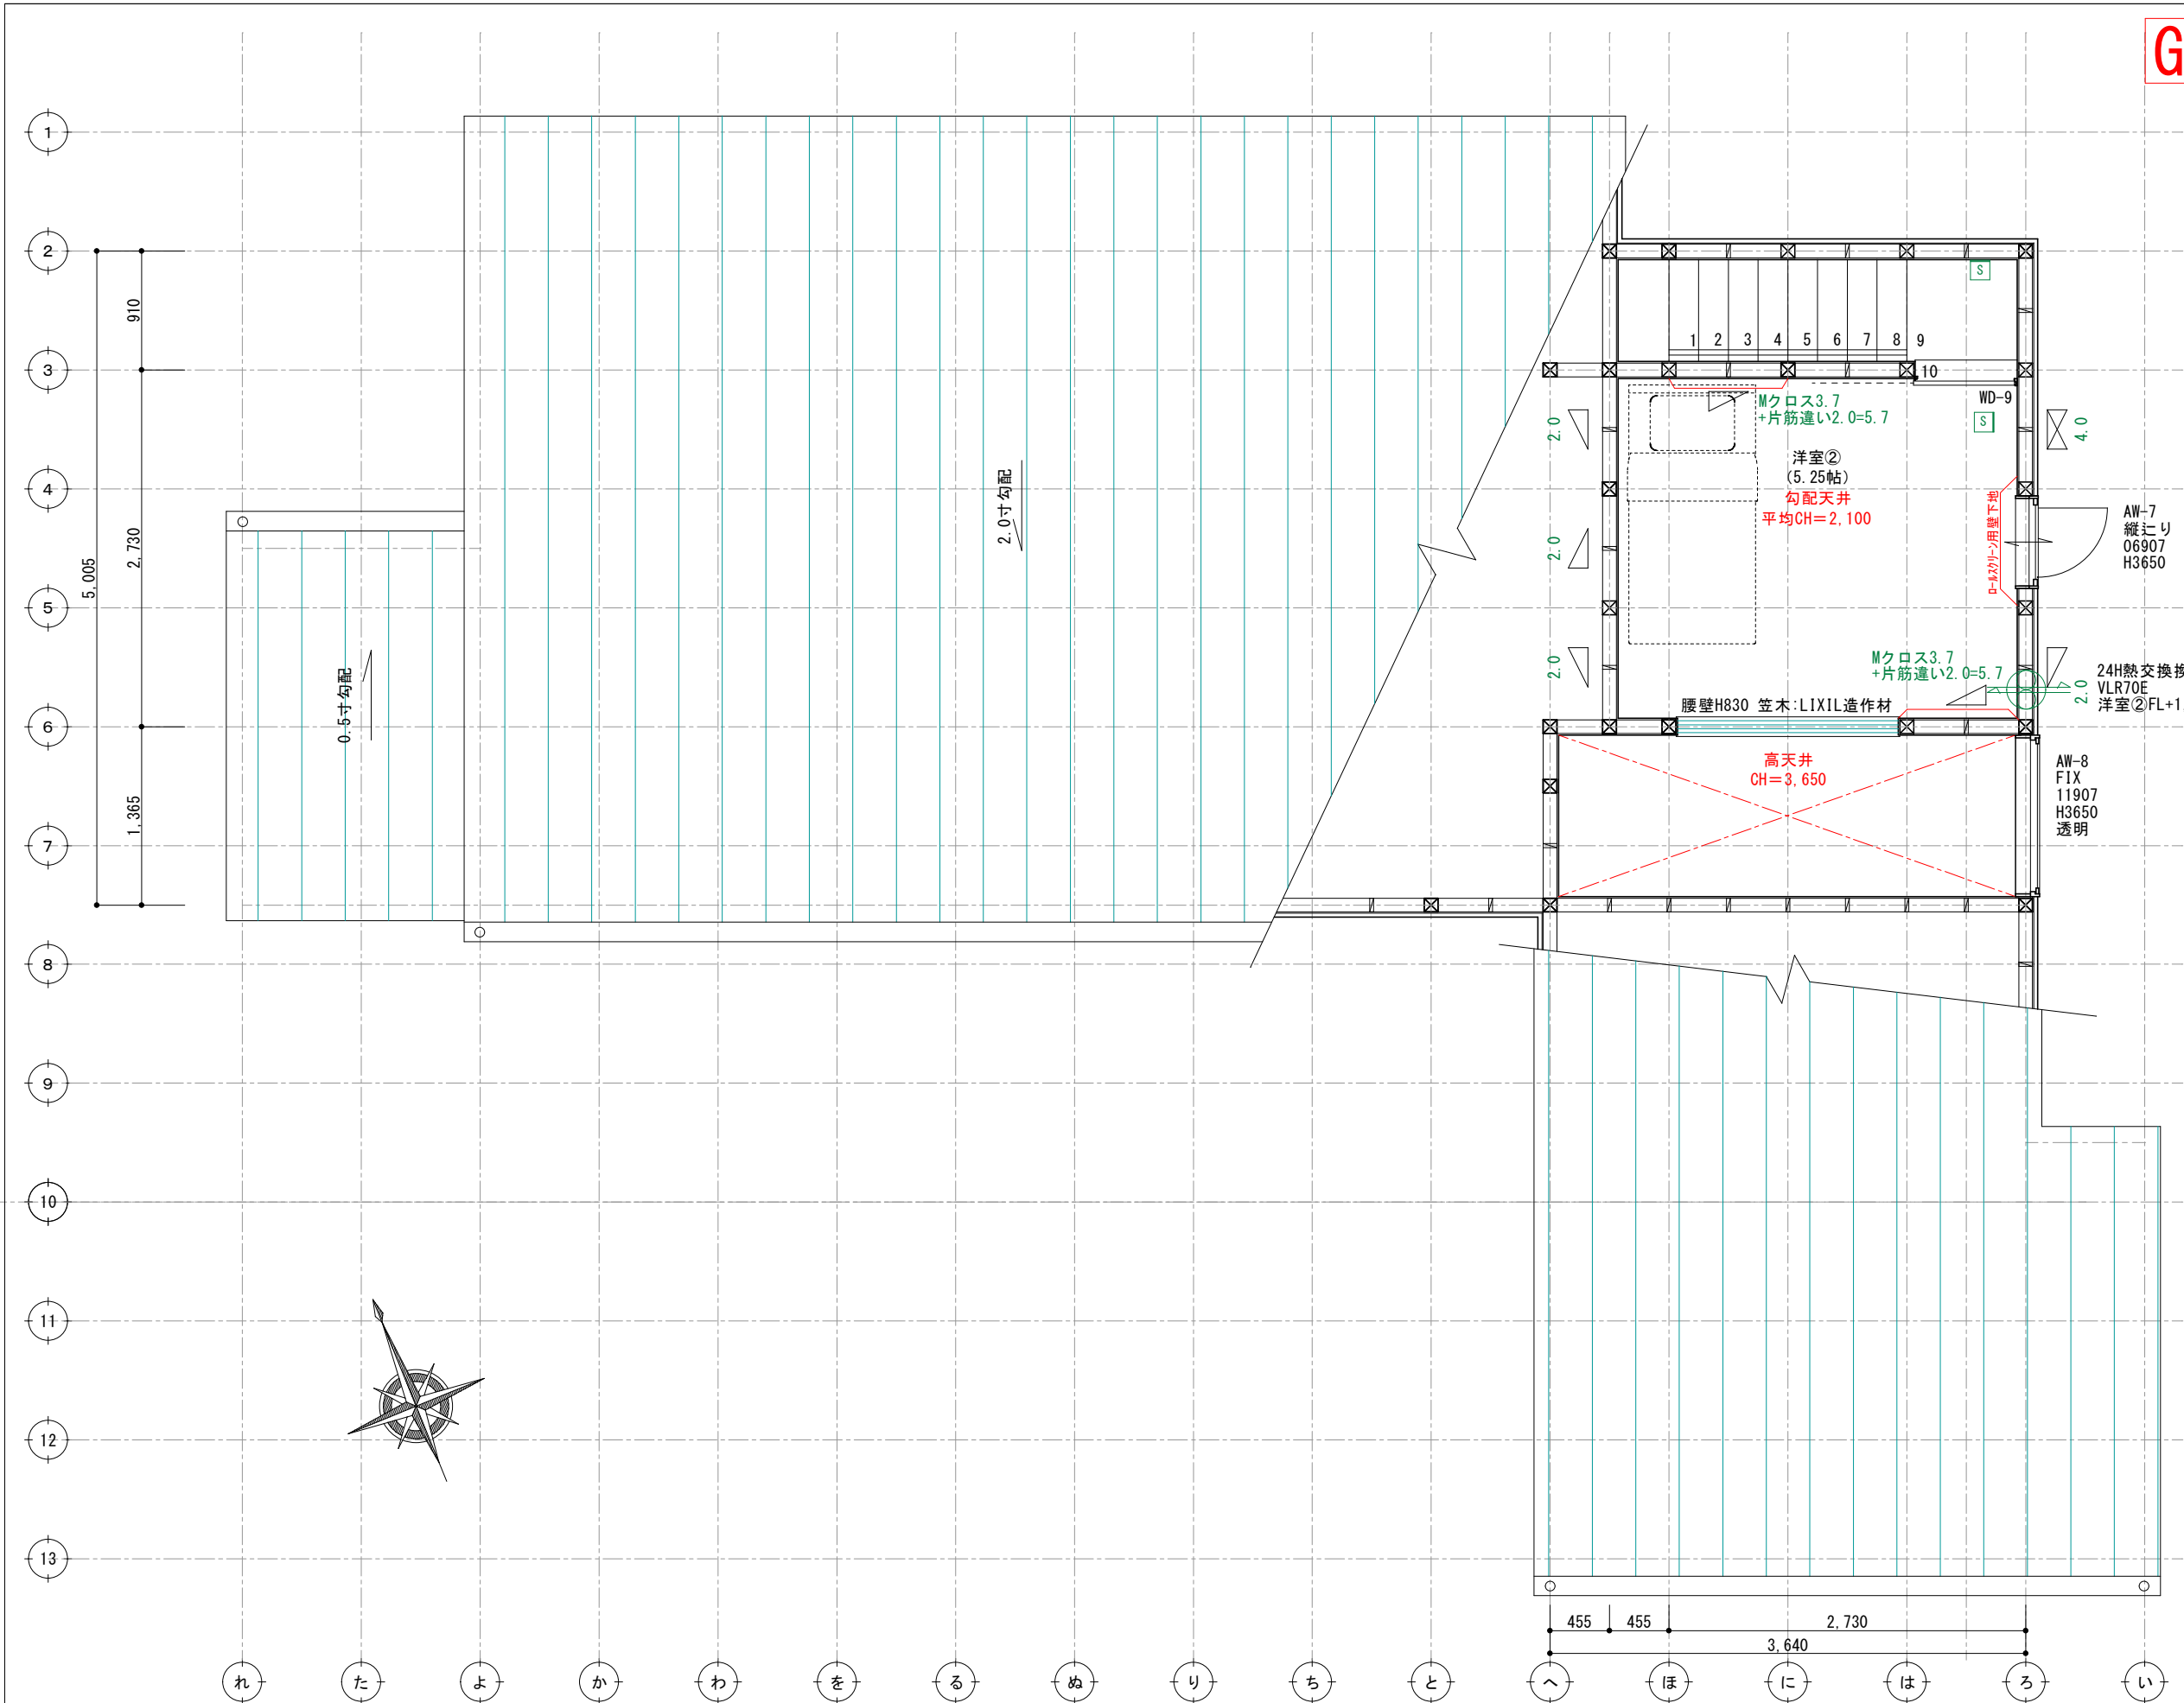

訂正	浜岡 一級総合設計事務所 一級建築士事務所 静岡県知事登録第 (10)2441 号 一級建築士 大臣登録第 365879 号 西原利昌	 PG HOUSE	株式会社 LIFEFUND InDesign office 一級建築士事務所 事務所登録 (2)第7595号 一級建築士登録 第179770号 鈴木 達男 〒432-8023 静岡県浜松市中央区鴨江3丁目70番23号	年月日 2026.3.15	件名 山村和孝様邸 新築工事	設計 IC 工事 図番	角谷	青島	3-2
				縮尺 1/50	図名 2階平面図				