


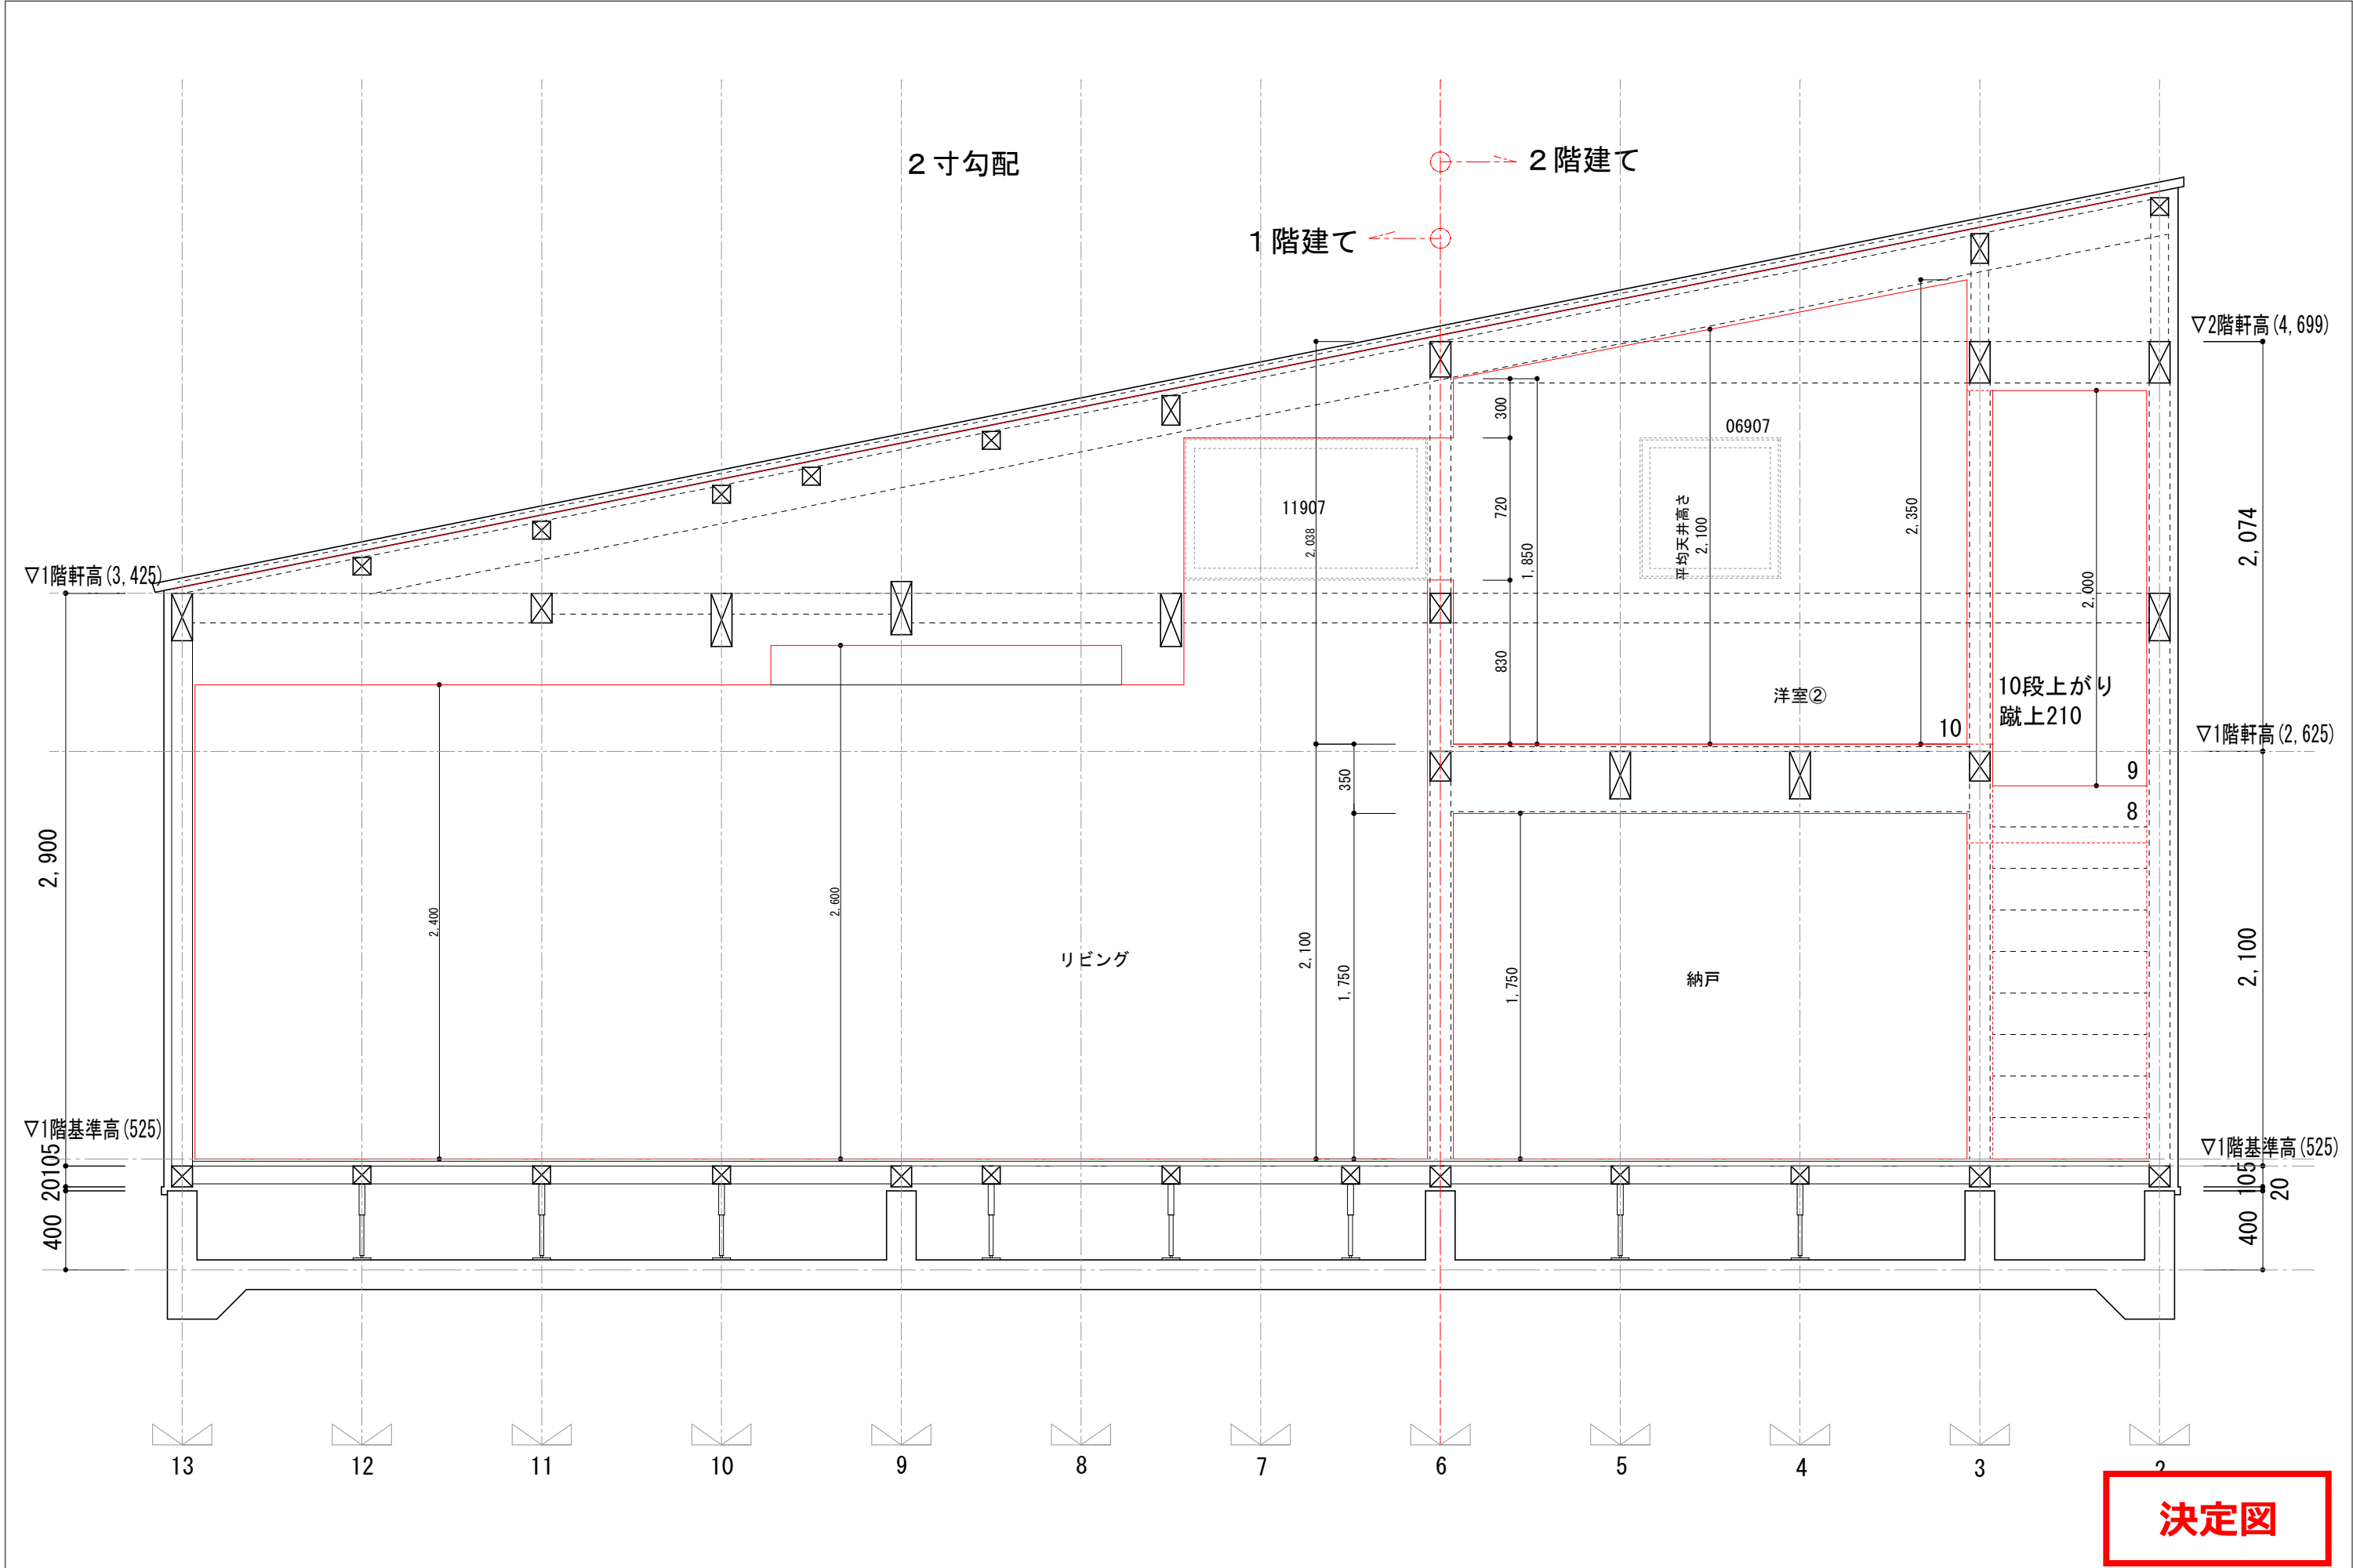

訂正	浜岡一級総合設計事務所 一級建築士事務所 静岡県知事登録第(10)2441号 一級建築士 大臣登録第 365879号 西原利昌		株式会社 LIFEFUND InDesign office 一級建築士事務所 事務所登録(2)第7595号 一級建築士登録 第179770号 鈴木 達男 〒432-8023 静岡県浜松市中央区鴨江3丁目70番23号	年月日 2026.03.15	件名 山村和孝様邸 新築工事	設計 IC 工事 図番	角谷	青島	5-2
				縮尺 1/30	図名 ロフト断面図				