


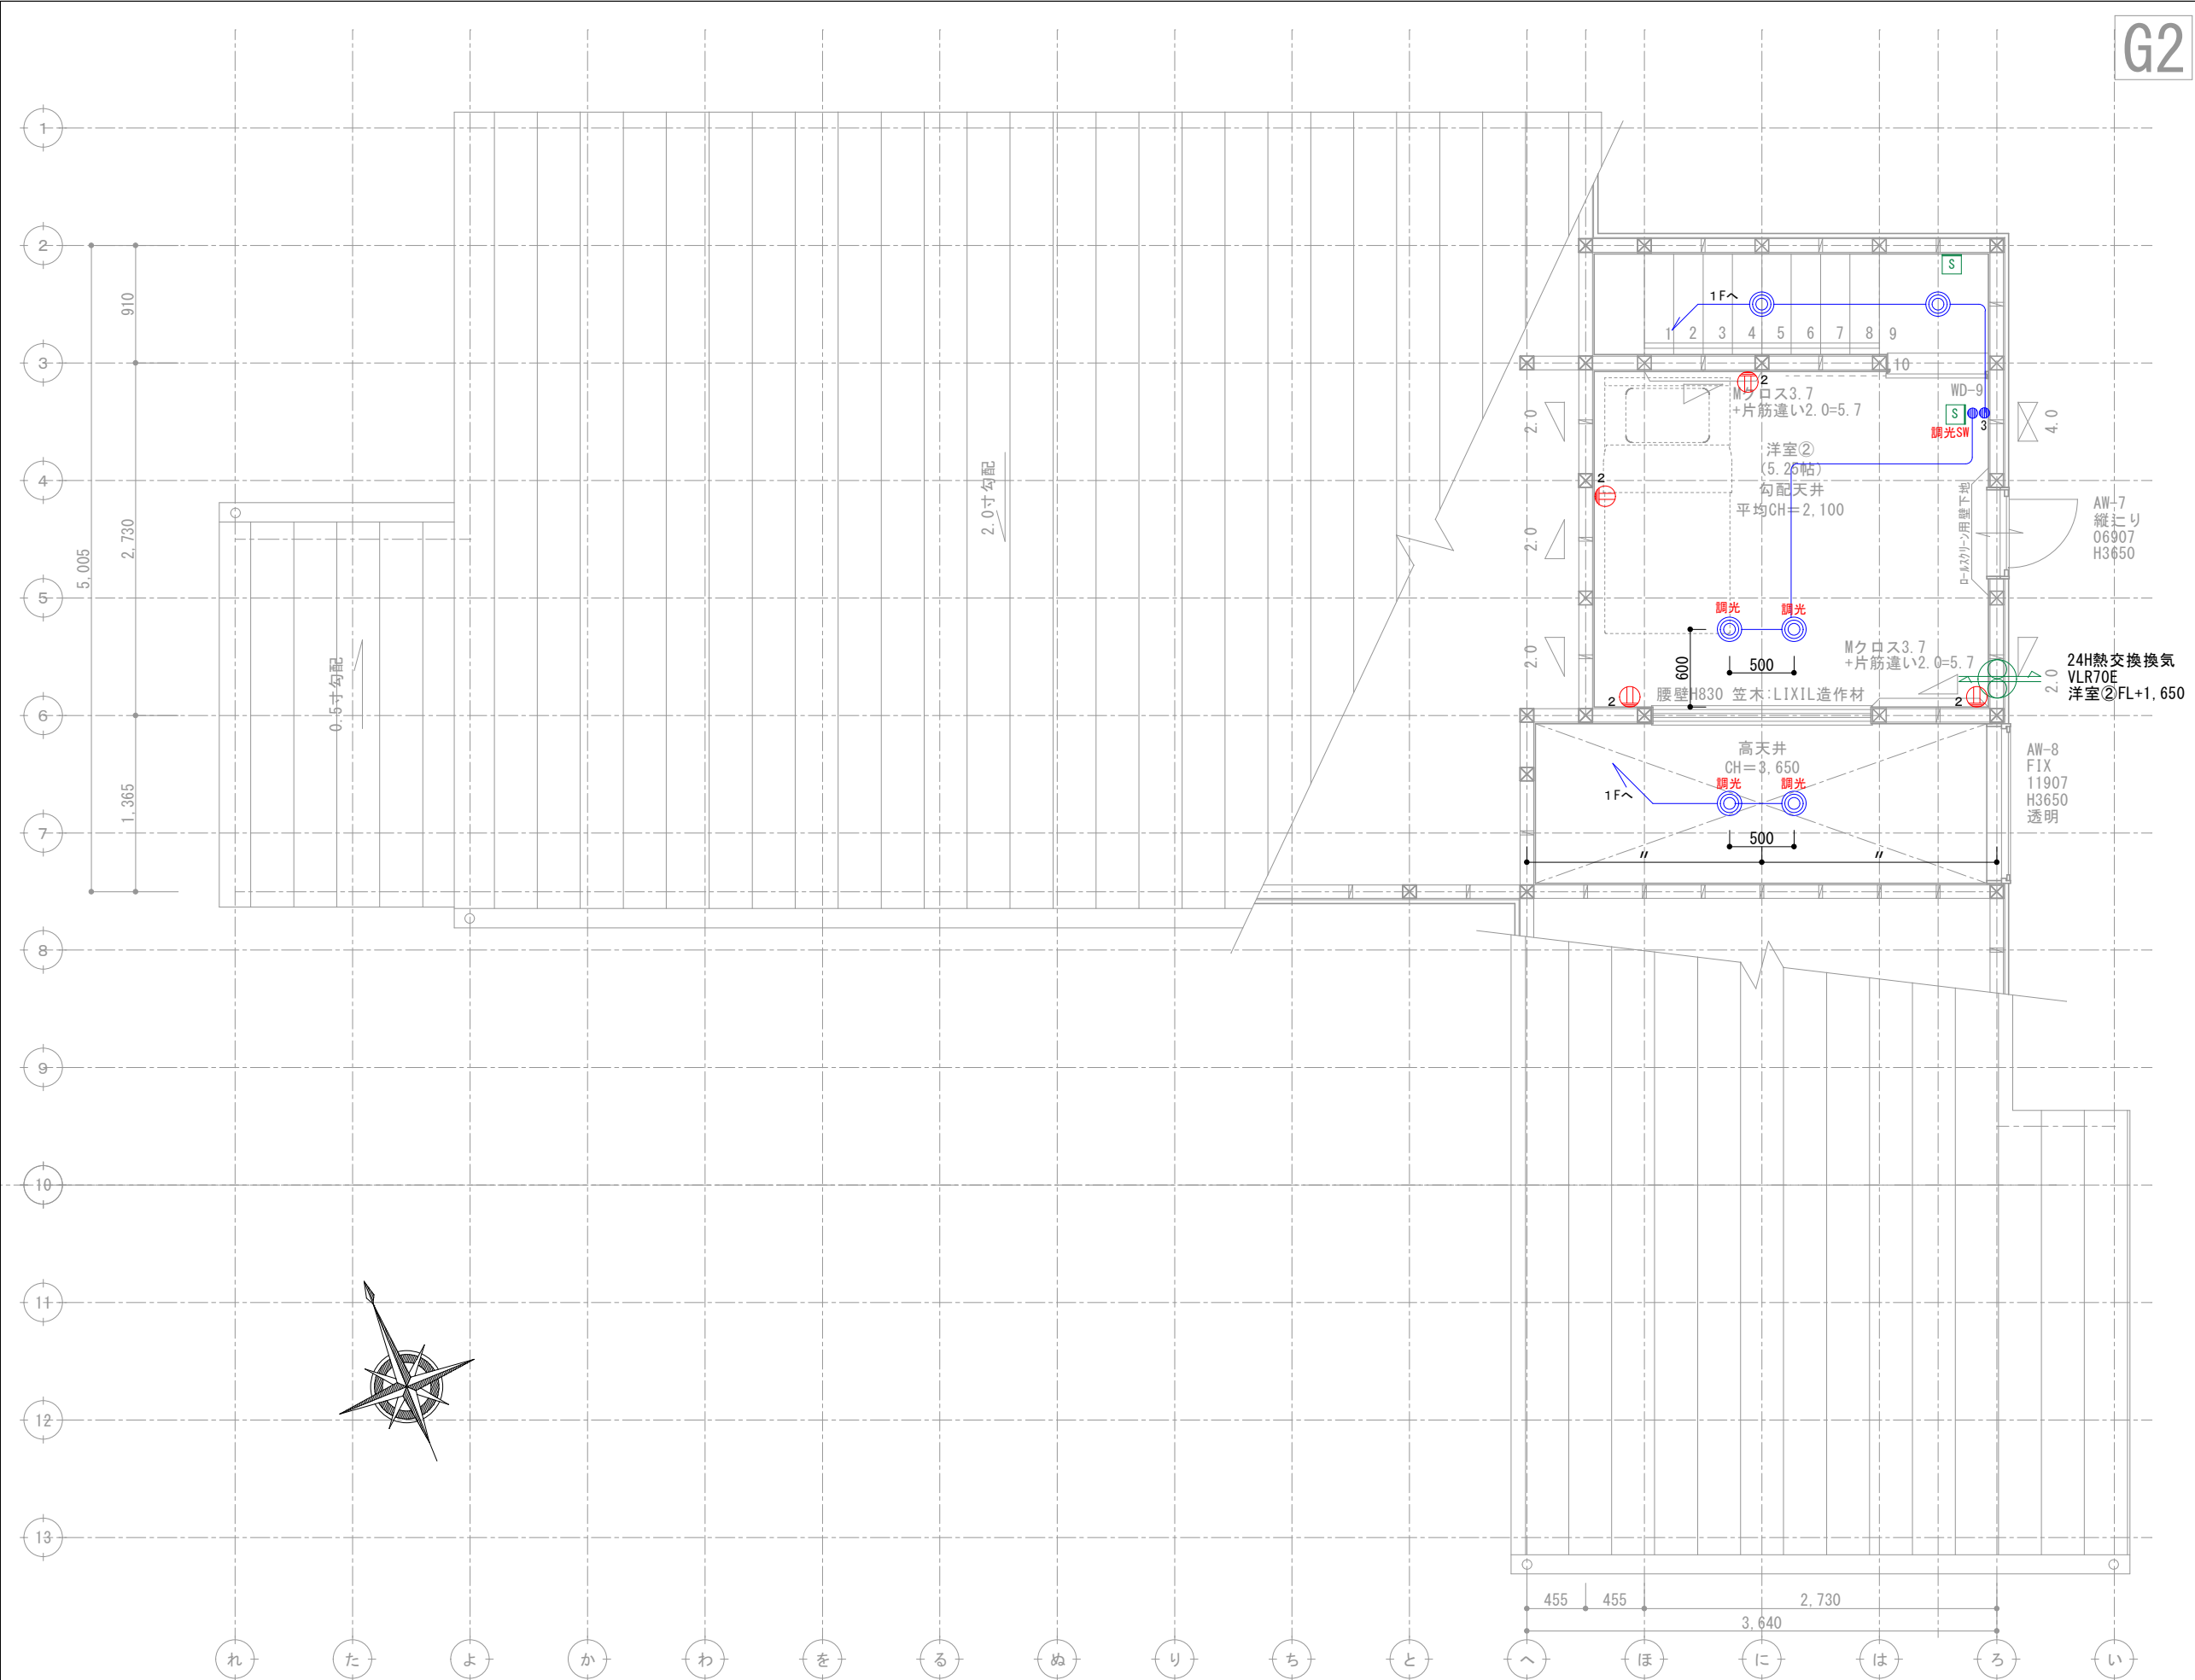

G2

壁付け 住宅用火災報知器			数量
H	熱感知器	電池式(単独型)	
		露出型	
壁付け 住宅用火災報知器			数量
S	煙感知器	電池式(単独型)	4
		露出型	

- ※ 煙感知器は壁・梁より600mm以上離す
壁に取付ける場合、
天井から150mm以上500mm以内離す
換気扇・エアコン吹出口から1500mm以上離す
- ※ 全室LED照明とする。
- ※ 標準天井高さ2,400
- ※ 特記無きガラスは型ガラス
- ※ 全室LED照明とし、居室においては調光
制御、非居室においては人感センサーを
採用する。

* 凡例

- ☒ 管柱 (105×105)
- ≡ K&Tンバ - (3.30倍 FRM-0641)
- △ 片筋違い (2.00倍 45×90)
(例 左:柱脚 右:柱頭)
- ⊗ たすき掛筋違い (4.00倍 45×90)
- 構造用合板 (2.70倍)
(t=9 タイガ-EXハイバ-)
- ▲ 床点検口
- ⊠ 天井点検口
- ⊕ 換気扇
- ⊕ 熱交換換気扇VLR-70

アドバンスシリーズ		
スマートデザイン (外部)		
凡例		
①	コンセント	1ヶロ
②	コンセント	2ヶロ
③	コンセント	3ヶロ
①ET	コンセント1ヶロ接地ターミナル付	
②ET	コンセント2ヶロ接地ターミナル付	
WP	コンセント	防水型
⊕	エアコン用コンセント	
⊕	200V用コンセント	
WP	防雨入線プレート	
スイッチ	スイッチ	
●	3路スイッチ	
●	4路スイッチ	
⊗	直結電源	
⊕TV	テレビ取出口	
TEL	電話取出口 (テレホンガイド)	
LAN	LAN取出口 (テレホンガイド)	
⊕	壁照明	
⊕	リモコン (給湯関係・ルフロ)	
⊕	メーター	
⊕	分電盤	
⊕	チャイム	

- ※ACコンセント天井付け
- ※TVアンテナ工事
- ※スイッチはFL+1100、コンセントはFL+200

決定図

訂正	浜岡 一級総合設計事務所 一級建築士事務所 静岡県知事登録第 (10)2441 号 一級建築士 大臣登録第 365879 号 西原利昌	 PG HOUSE	株式会社 LIFEFUND InDesign office 一級建築士事務所 事務所登録 (2)第7595号 一級建築士登録 第179770号 鈴木 達男 〒432-8023 静岡県浜松市中央区鴨江3丁目70番23号	年月日 2026.3.15	件名 山村和孝様邸 新築工事	設計 IC 工事 青島	図番 7-2
				縮尺 1/50	図名 2階電気配線図		