



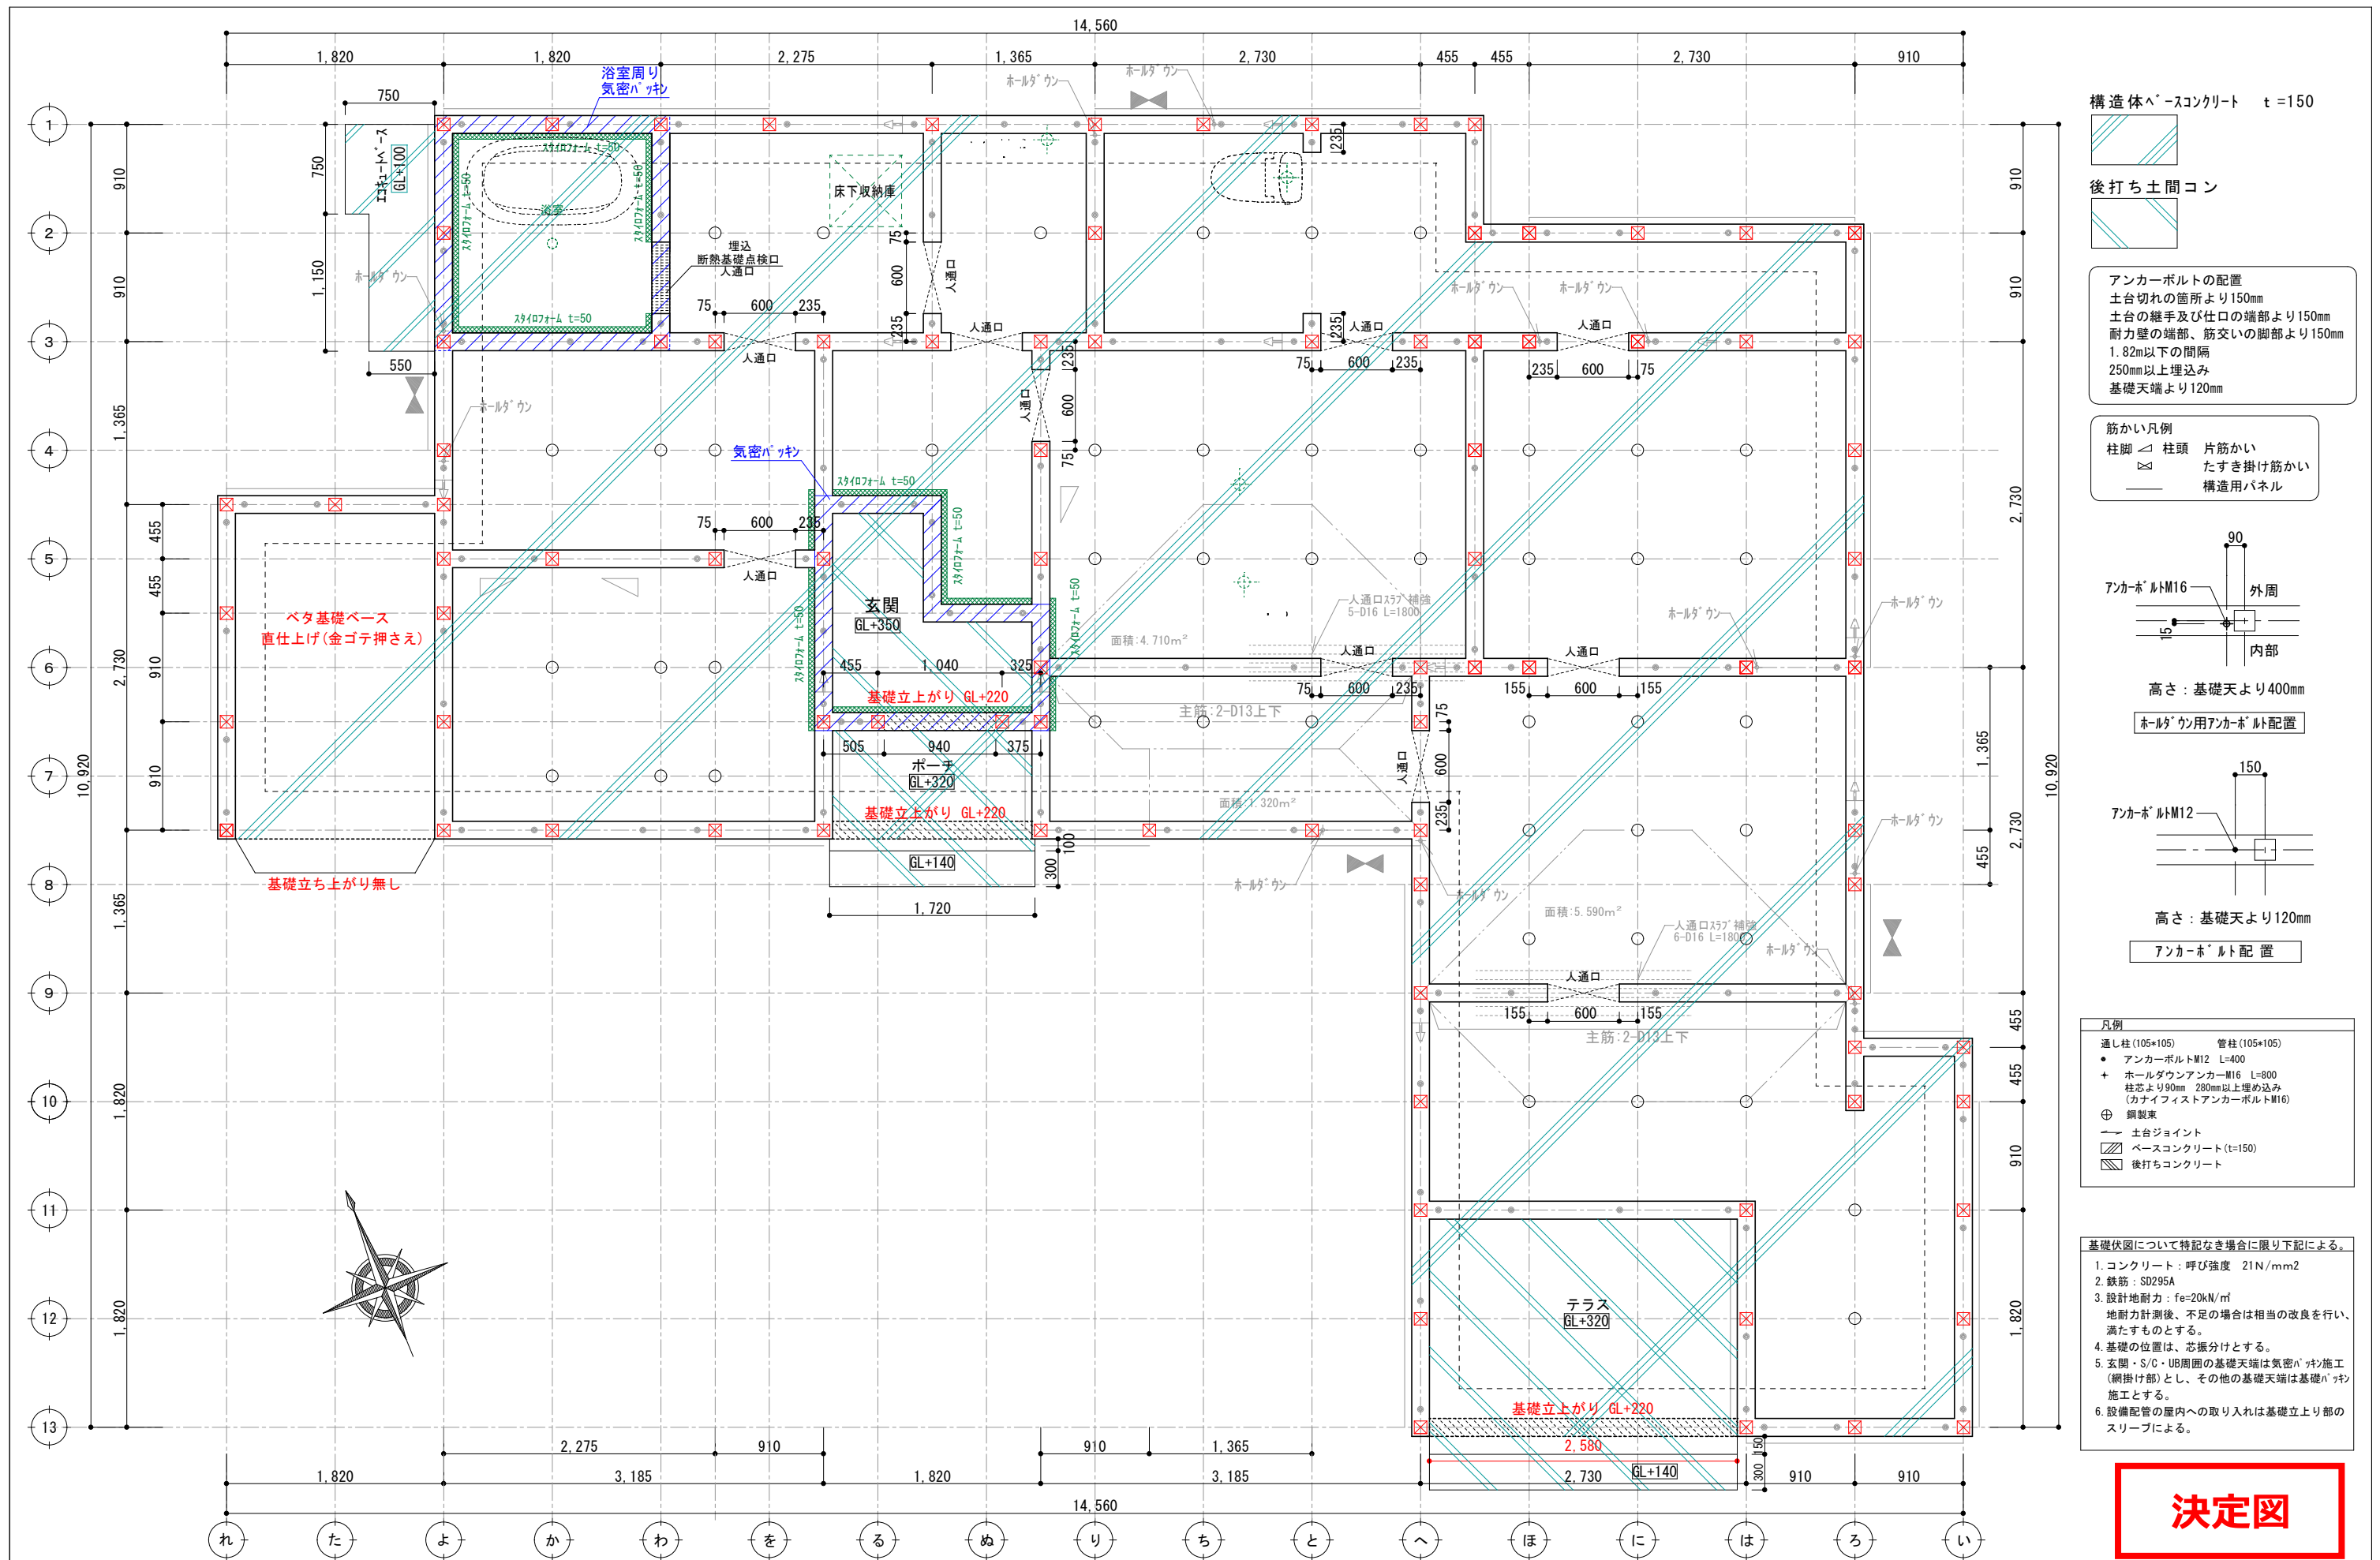


構造体ベ-スコンクリート t=150

後打ち土間コン

アンカーボルトの配置
土台切れの箇所より150mm
土台の継手及び仕口の端部より150mm
耐力壁の端部、筋交いの脚部より150mm
1.82m以下の間隔
250mm以上埋込み
基礎天端より120mm

筋かい凡例
柱脚 柱頭 片筋かい 片筋かい
たすき掛け筋かい
構造用パネル

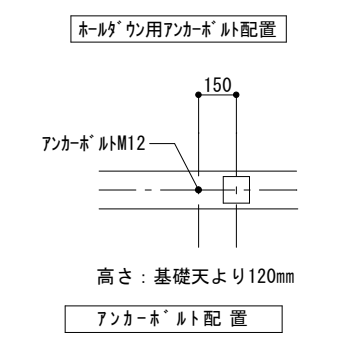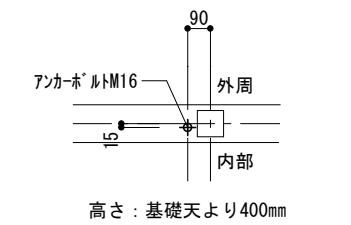

凡例
通し柱 (105*105) 管柱 (105*105)
アンカーボルトM12 L=400
ホルダウンアンカーM16 L=800
柱芯より90mm 280mm以上埋め込み
(カナイフリストアンカーボルトM16)
鋼製束
土台ジョイント
ベースコンクリート (t=150)
後打ちコンクリート

基礎伏図について特記なき場合に限り下記による。
1. コンクリート: 呼び強度 21N/mm²
2. 鉄筋: SD295A
3. 設計地耐力: fe=20kN/m²
地耐力計測後、不足の場合は相当の改良を行い、満たすものとする。
4. 基礎の位置は、芯振分けとする。
5. 玄関・S/C・UB周囲の基礎天端は気密パッキン施工 (網掛け部) とし、その他の基礎天端は基礎パッキン施工とする。
6. 設備配管の屋内への取り入れは基礎立上り部のスリーブによる。

決定図

訂正	浜岡一級総合設計事務所 一級建築士事務所 静岡県知事登録第 (10)2441 号 一級建築士 大臣登録第 365879 号 西原利昌	LIFEFUND PG HOUSE	株式会社 LIFEFUND InDesign office 一級建築士事務所 事務所登録 (2) 第7595号 一級建築士登録 第179770号 鈴木 達男 〒432-8023 静岡県浜松市中央区鴨江3丁目70番23号	年月日 2026. 3. 15	件名 山村和孝様邸 新築工事	設計 IC 工事 図番 B-1
				縮尺 1/50	図名 基礎伏図	