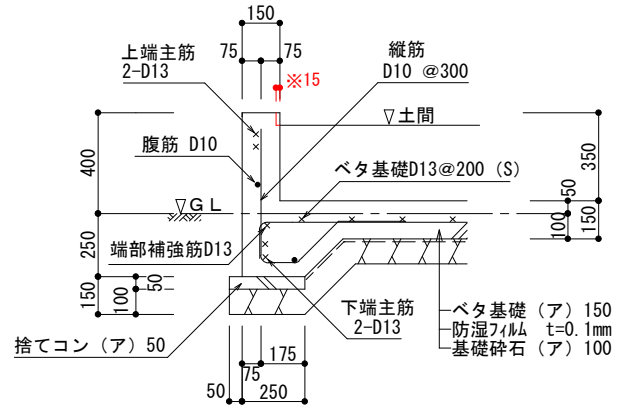
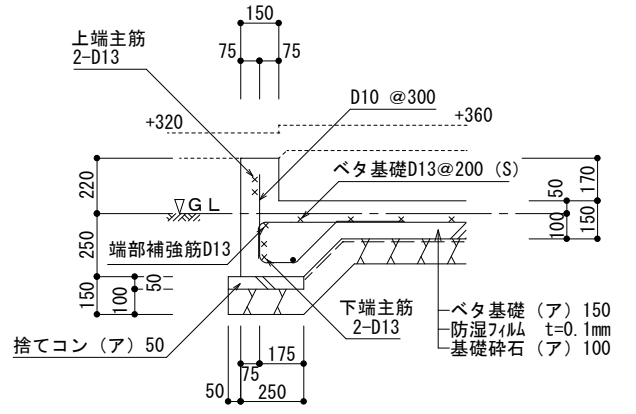
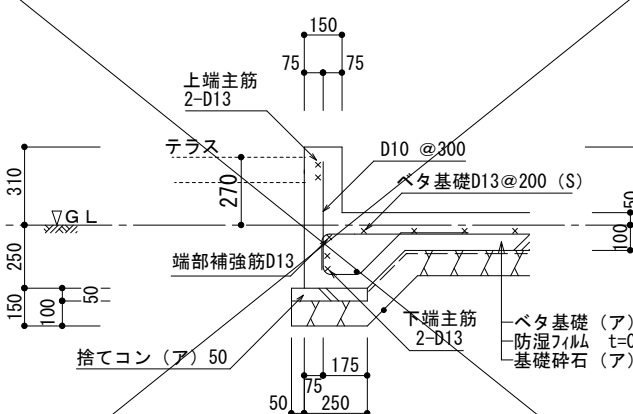
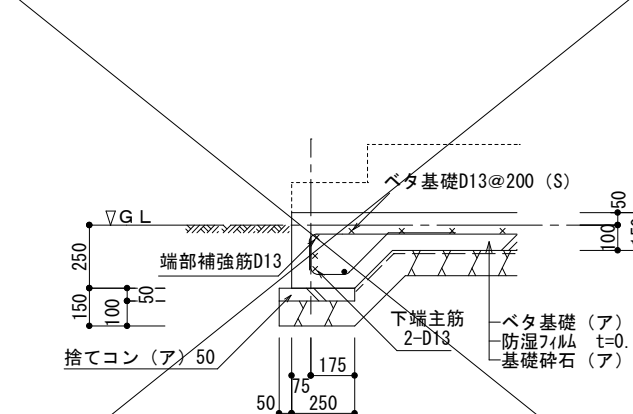
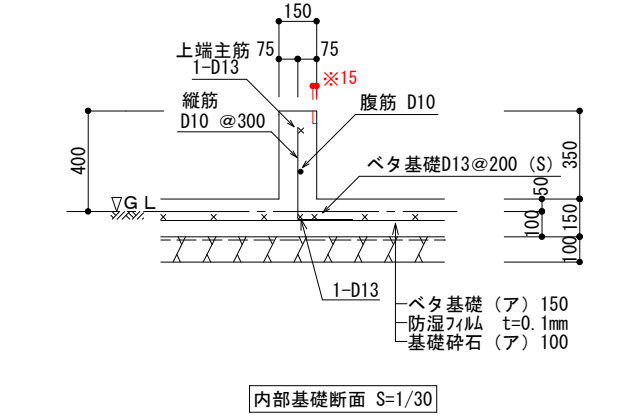
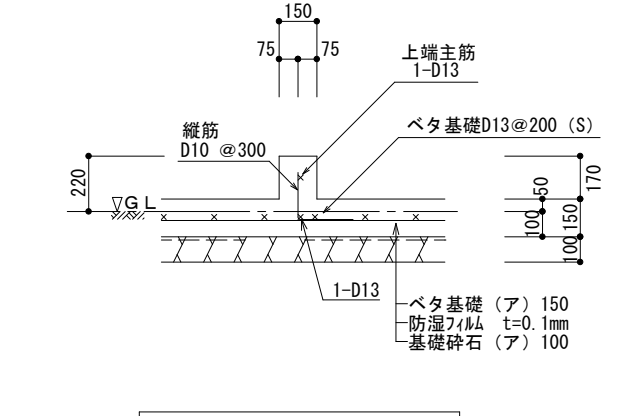
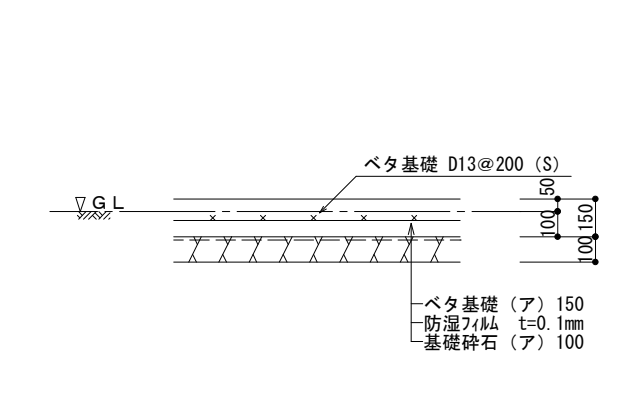
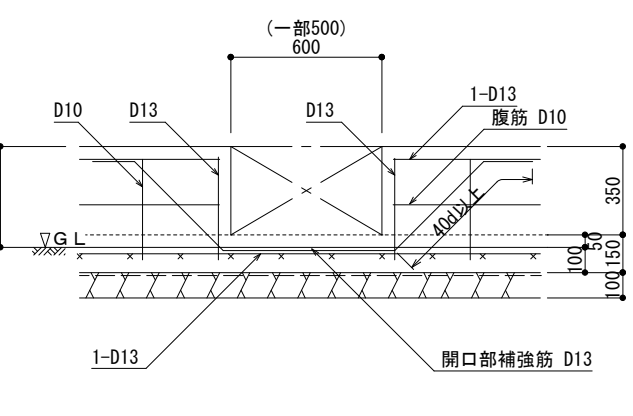
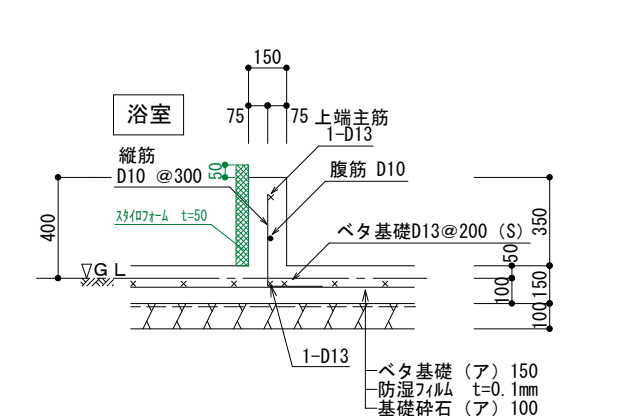
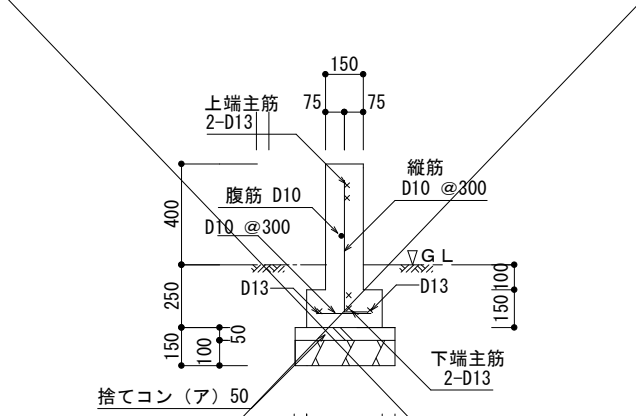
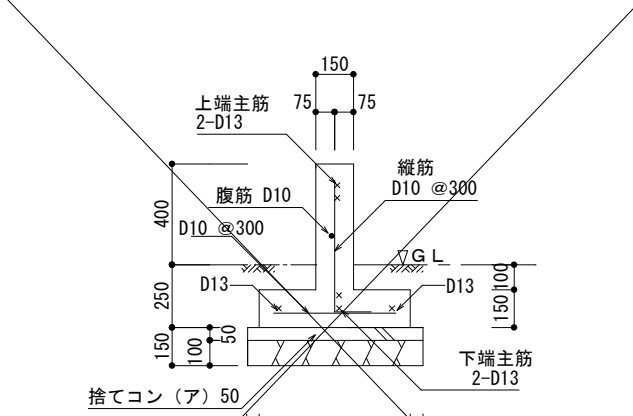


|   |   |   |   |                                  |                                    |          |     |          |           |
|---|---|---|---|----------------------------------|------------------------------------|----------|-----|----------|-----------|
|  <p>外周基礎断面 S=1/30</p> <p>※玄関内土間部分のみ15mm欠き込み</p>                               |  <p>ポーチ下 外周部基礎断面 S=1/30</p> <p>倉庫ドア下 外周部基礎断面 S=1/30</p>                           |  <p>土間納め勝手口ドア下 外周部基礎断面 S=1/30</p> |  <p>ポーチ外周部の基礎断面 S=1/30</p> <p>立上り無しの基礎断面 S=1/30</p>   |                                  |                                    |          |     |          |           |
|  <p>内部基礎断面 S=1/30</p> <p>※玄関内土間部分のみ15mm欠き込み</p> <p>※注意：基礎伏図に特記のない内部基礎の場合</p> |  <p>ポーチ下 内周部基礎断面 S=1/30</p> <p>玄関ドア下 内周部基礎断面 S=1/30</p> <p>玄関＝SC布基礎断面 S=1/30</p> |  <p>ベタ基礎断面 S=1/30</p>            |  <p>人通口補強 S=1/30</p>   |                                  |                                    |          |     |          |           |
|  <p>浴室内部基礎断面 S=1/30</p> <p>※注意：基礎伏図に特記のない内部基礎の場合</p>                        |  <p>布基礎A：袖壁用 基礎断面 S=1/30</p>                                                    |  <p>布基礎B：応用独立 基礎断面 S=1/30</p>   | <div><div>基礎の寸法<br/>及び<br/>配筋の検証方法</div><div>基礎立上り配筋は、<br/>(財)日本住宅・木材技術<br/>センター発行のスパン表<br/>(増補版)による。<br/>ベタ基礎スラブ配筋は、<br/>まもりすまい保険設計施工<br/>基準同解説のベタ基礎配筋表<br/>による。具体的な寸法・配<br/>筋は基礎詳細図参照。</div></div> <div>鉄筋断面表記</div> <div>● ・ ・ D10を示す。<br/>× ・ ・ D13を示す。</div> <div>※使用しない断面は×を記入。</div> <div>決定図</div> |                                  |                                    |          |     |          |           |
| 訂正   | 浜岡一級総合設計事務所<br>一級建築士事務所 静岡県知事登録第 (10)2441 号<br>一級建築士 大臣登録第 365879 号 西原利昌                                                                                            | PG HOUSE   | 株式会社 LIFEFUND InDesign office 一級建築士事務所<br>事務所登録 (2) 第7595号 一級建築士登録 第179770号 鈴木 達男<br>〒432-8023 静岡県浜松市中央区鴨江3丁目70番23号   | 年月日<br>2026. 3. 15<br>縮尺<br>1/30 | 件名<br>山村和孝様邸 新築工事<br>図名<br>基礎断面リスト | 設計<br>角谷 | I C | 工務<br>青島 | 図番<br>B-2 |