


クロス指示書

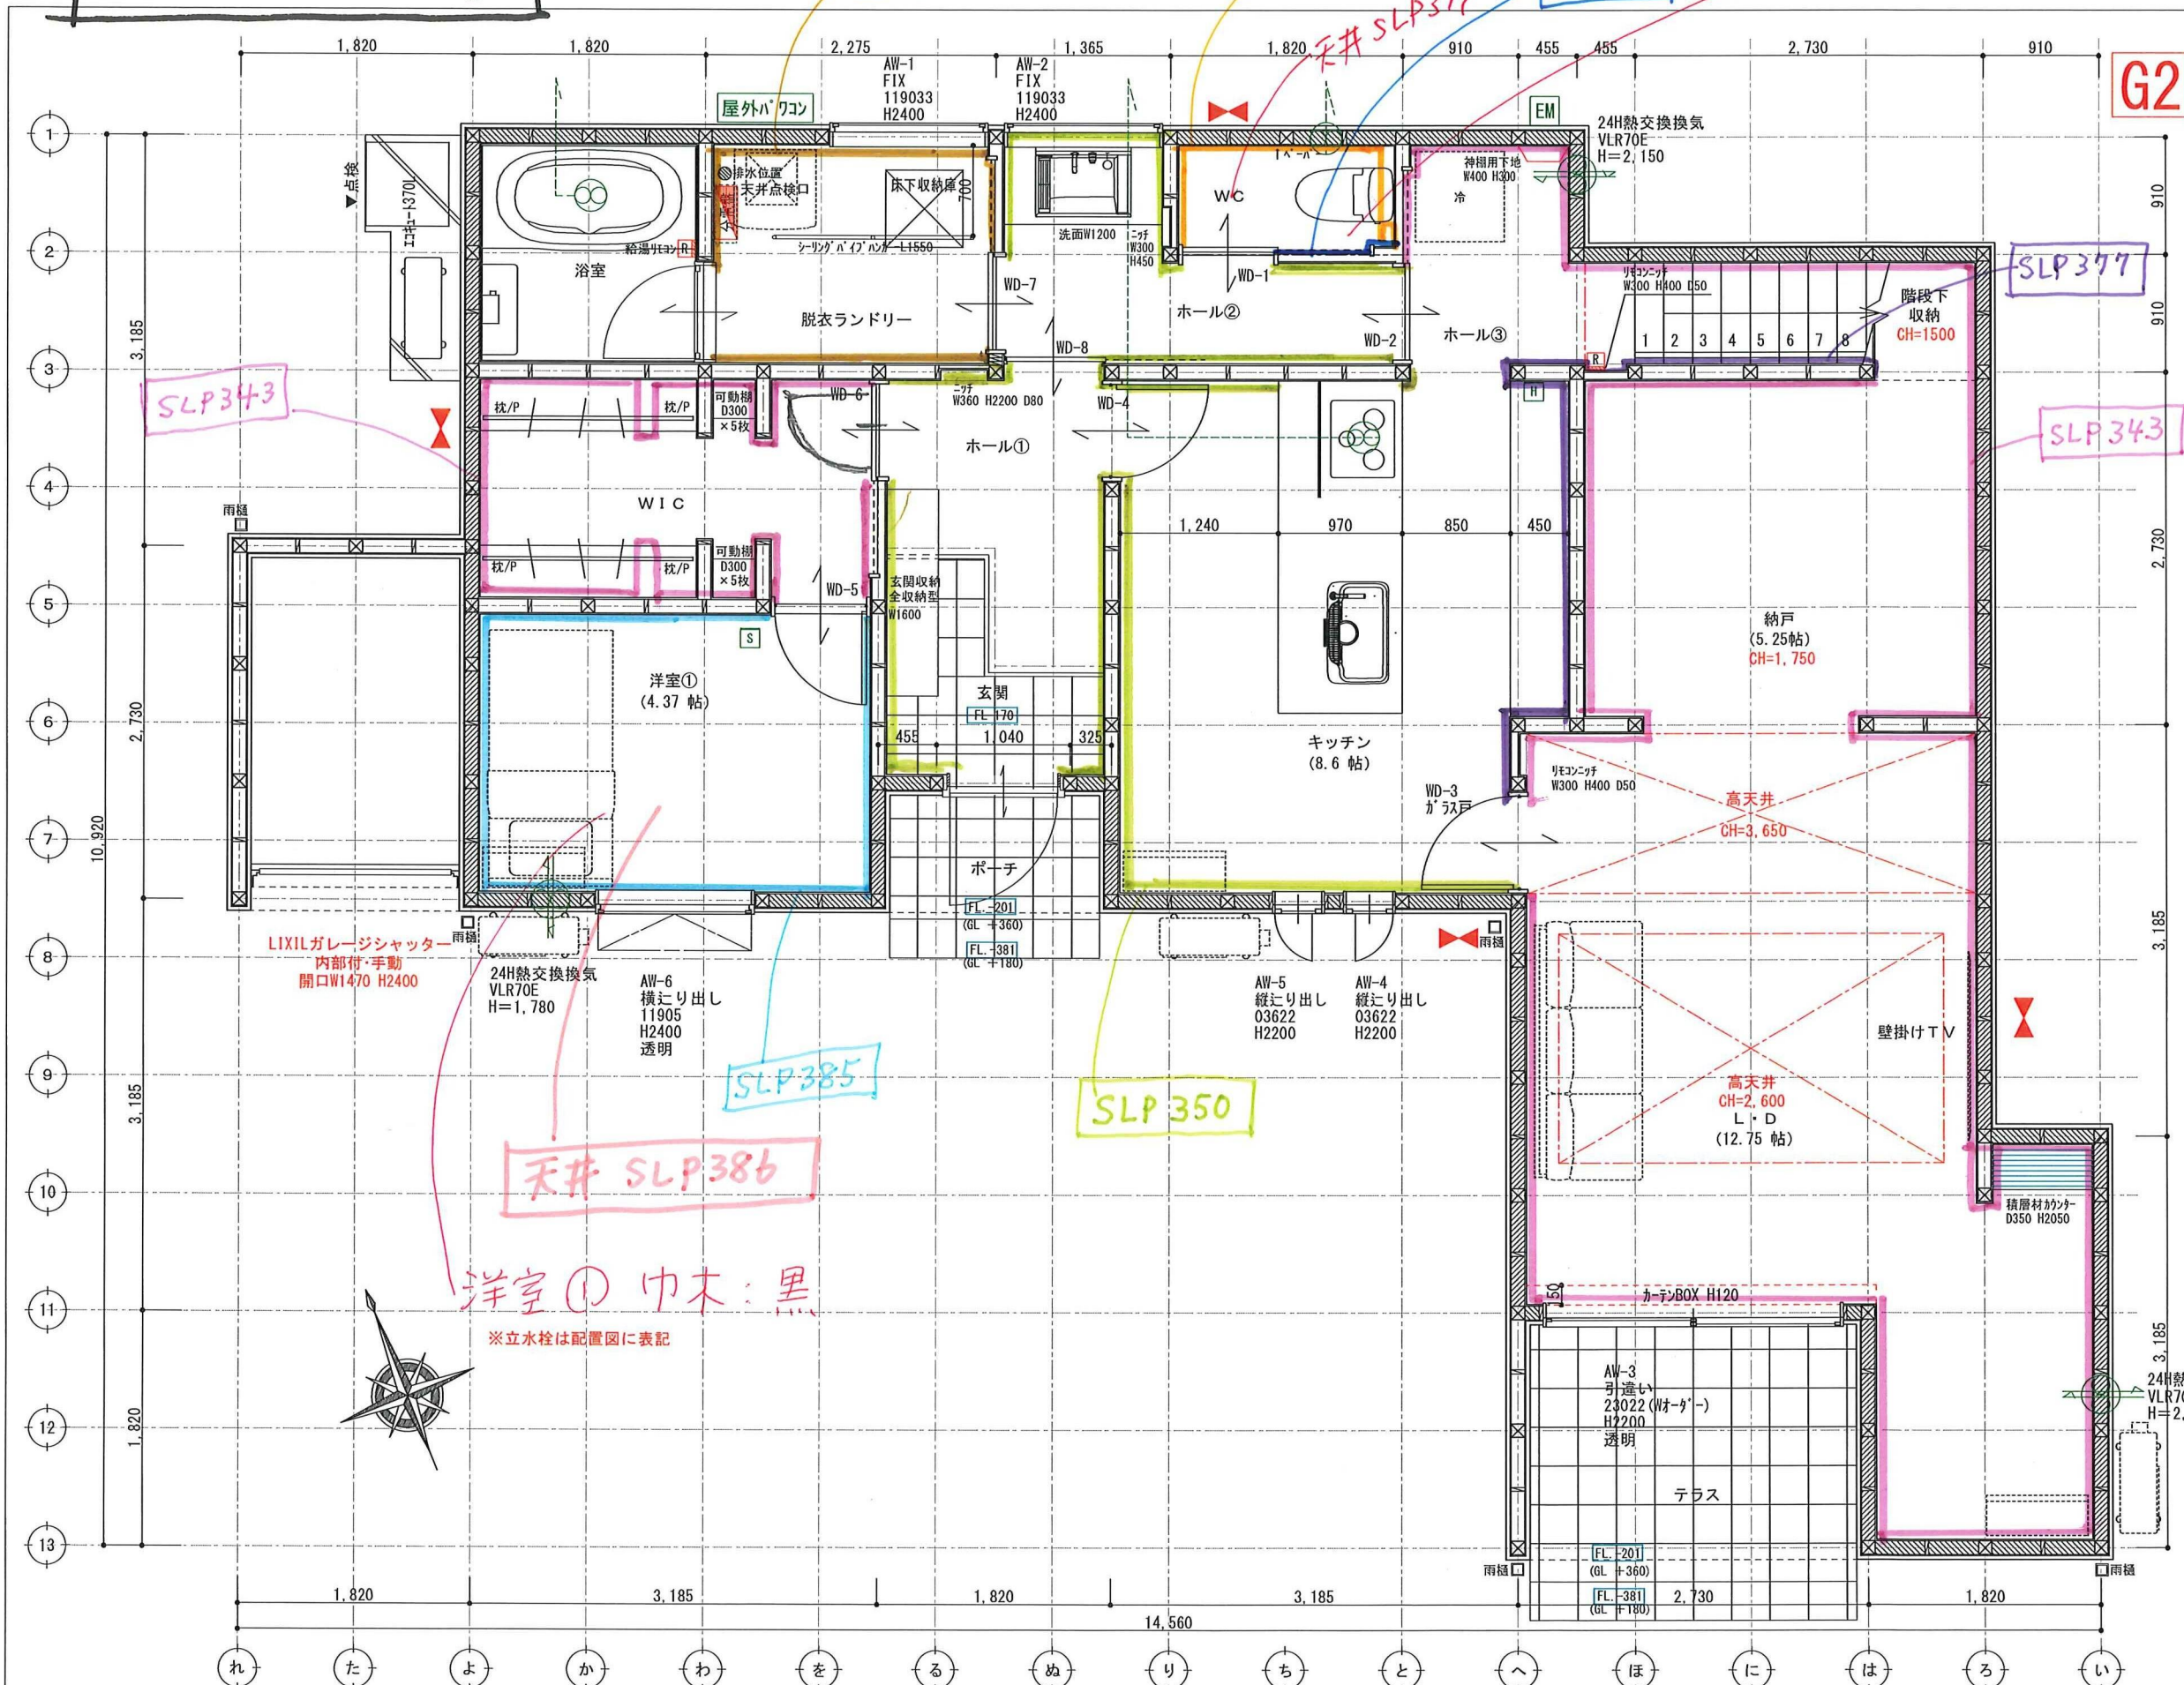

壁付け	住宅用火災報知器	数量
[H]	熱感知器	電池式(単独型) 1
[S]	煙感知器	電池式(単独型) 1

※ 煙感知器は壁・梁より600mm以上離す
壁に取付ける場合、
天井から150mm以上500mm以内離す
換気扇・エアコン吹出口から1500mm以上離す
※ 全室LED照明とする。
※ 標準天井高さ2,400
※ 特記無きガラスは型ガラス


* 凡例

- ☒ 管柱 (105×105)
- ◀▶ K' ユニバーサル (3.30倍 FRM-0641)
- △ 片筋違い (2.00倍 45×90)
(例 左:柱脚 右:柱頭)
- ⊠ たすき掛筋違い (4.00倍 45×90)
- 構造用合板 (2.70倍)
(t=9 タイガ EXN41A)
- △ 床点検口
- ⊠ 天井点検口
- ⊕ 換気扇
- ⊕ 熱交換換気扇VLR-70

アドバンスシリーズ	
スマートデザイン (外部)	
凡例	
①	コンセント 1ヶ所
②	コンセント 2ヶ所
③	コンセント 3ヶ所
①ET	コンセント1ヶ所接地ターミナル付
②ET	コンセント2ヶ所接地ターミナル付
WP	コンセント 防水型
WP	エアコン用コンセント
WP	200V用コンセント
WP	防雨入接プレート
●	スイッチ
●	3路スイッチ
●	4路スイッチ
⊕	直結電源
TV	テレビ取出口
TEL	電話取出口 (テレホンガイド)
LAN	LAN取出口 (テレホンガイド)
リモコン	リモコン (給湯・風呂・エアコン)
メーカー	メーカー

決定図

※天井高はFL+1100、コンクリートはFL+200

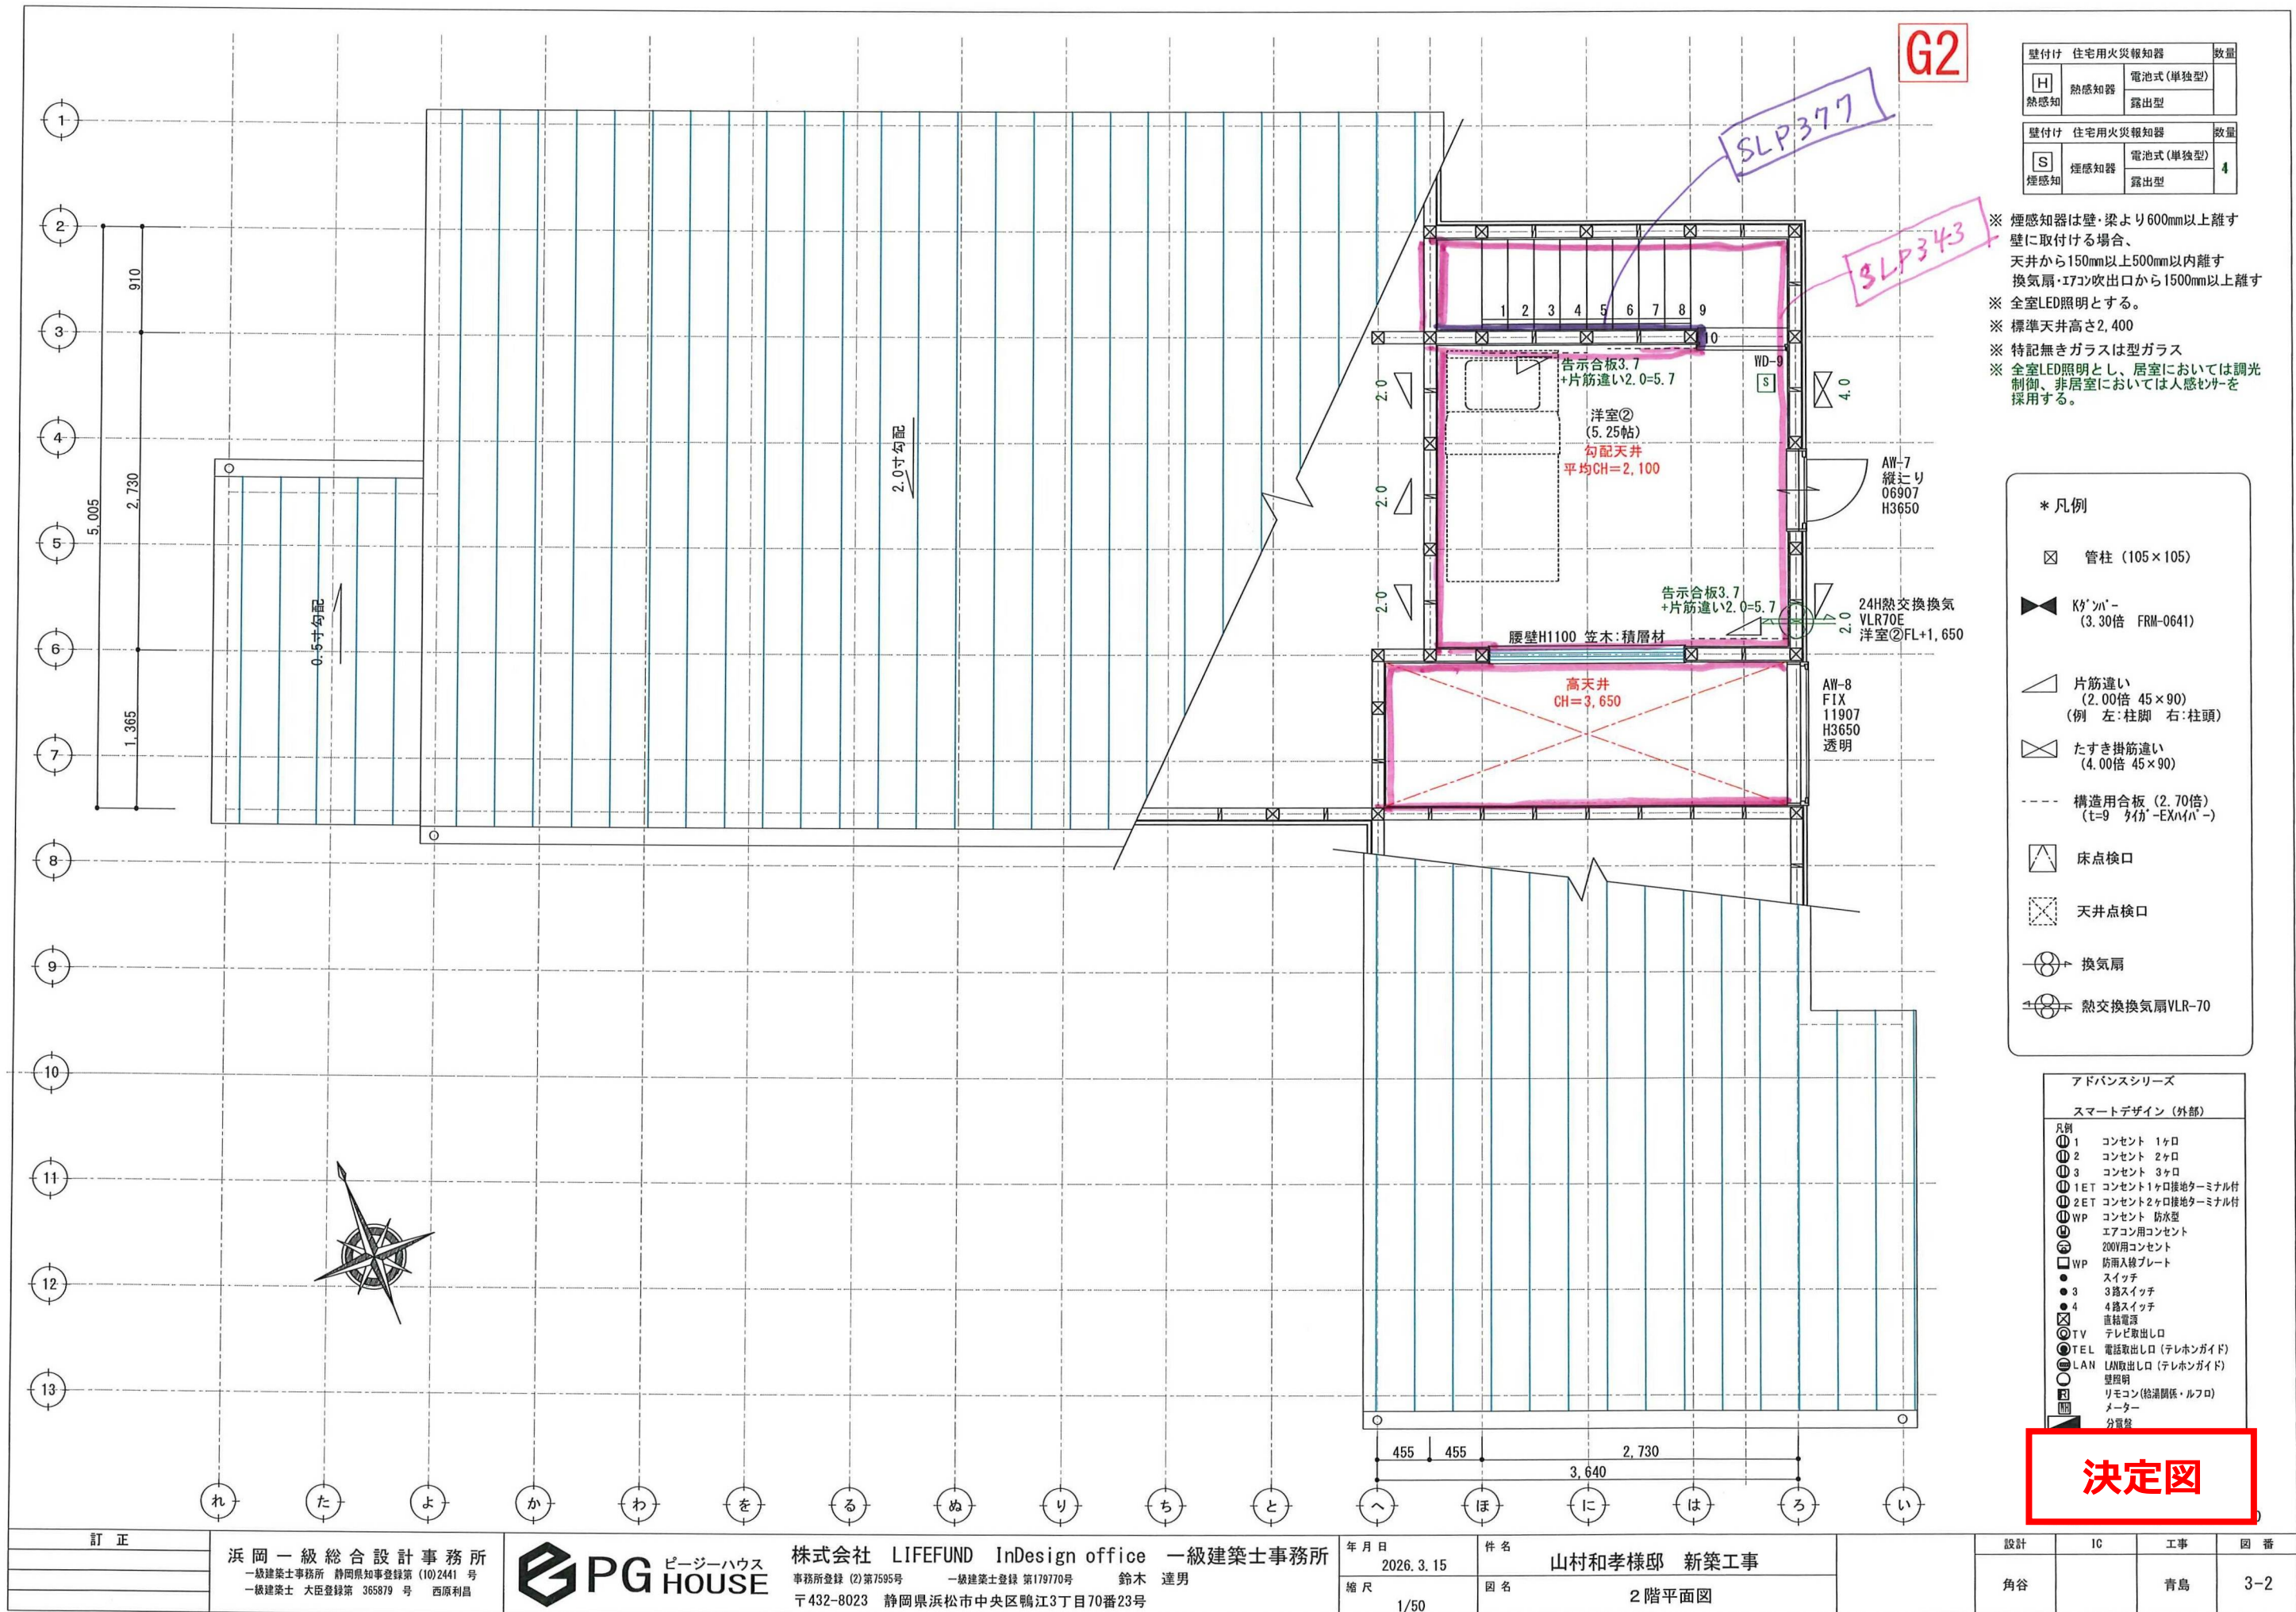

G2

SLP377

SLP343

壁付け	住宅用火災報知器	数量
H	熱感知器	電池式(単独型)
熱感知	露出型	
壁付け	住宅用火災報知器	数量
S	煙感知器	電池式(単独型)
煙感知	露出型	4

- ※ 煙感知器は壁・梁より600mm以上離す壁に取付ける場合、天井から150mm以上500mm以内離す換気扇・エアコン吹出口から1500mm以上離す
- ※ 全室LED照明とする。
- ※ 標準天井高さ2,400
- ※ 特記無きガラスは型ガラス
- ※ 全室LED照明とし、居室においては調光制御、非居室においては人感センサーを採用する。

* 凡例

- ☒ 管柱 (105×105)
- ◀▶ K'ンパ' (3.30倍 FRM-0641)
- △ 片筋違い (2.00倍 45×90) (例 左:柱脚 右:柱頭)
- ⊠ たすき掛筋違い (4.00倍 45×90)
- 構造用合板 (2.70倍) (t=9 タイプ-EXM/A/-)
- △ 床点検口
- ⊠ 天井点検口
- ⊙ 換気扇
- ⊕ 熱交換換気扇VLR-70

アドバンスシリーズ

スマートデザイン (外部)

- 凡例
- ① コンセント 1ヶ所
- ② コンセント 2ヶ所
- ③ コンセント 3ヶ所
- 1ET コンセント1ヶ所接地ターミナル付
- 2ET コンセント2ヶ所接地ターミナル付
- WP コンセント 防水型
- エアコン用コンセント
- 200V用コンセント
- WP 防雨入線プレート
- スイッチ
- 3路スイッチ
- 4路スイッチ
- 直結電源
- TV テレビ取出口
- TEL 電話取出口 (テレホンガイド)
- LAN LAN取出口 (テレホンガイド)
- 壁照明
- リモコン (給湯関係・ルフロ)
- メーター
- 分電盤

決定図