


■ 仕 様			■ HEAT20	G2
断熱工事	■ 床:ネオフォーム t90 ■ 土間床等の外周:スタイロフォームAT t50 ■ 壁:アクアフォームLITE吹付 t90 ■ 天井:アクファフォームLITE吹付 t220			
床下換気	■ 基礎パッキン JOTO (玄関・UB周り:気密基礎パッキン)			
防虫防蟻	■ 土壌処理・木部 ガントナーMC			
■ 外 部 仕 上 表			■ 22条地域	
部位		仕上・仕様・メーカー		色番・品番
屋根		■ ガルバリウム鋼板(t0.35)UK立平 ニスクカラーPro GH 軒先通気金物 日本住環境株式会社【REV-15】		GHK01 Sブラック
パラペット笠木		■ なし		
破風・鼻隠		■ なし		
雨樋	(軒樋)	■ Panasonic サーフেসケアFS-I型		ブラック
	(竖樋)	■ Panasonic S30角樋		ブラック
	屋根軒	■ なし		
	ポーチ軒	■ 神島化学 t= 6mm 軒天ボード エンボス		Wチャコールブラック
	バルコニー軒	■ なし		
オーバーハング水切り		■ ガルバリウム鋼板 ※外壁合わせ JOTO:HF-A3550		ブラック
外壁	通気金物(15mm)	■メイン	Kmewエクセレージ・シマンフラット	光セラ
	※下地面材:タイガーEXハイパー	■バイクガレージ壁仕上げ 外壁同仕上げ(サイディング)		
	防火認定 PC030BE-4028	■アクセントB	なし	
玄関ポーチ		■ 床 玄関タイルに同じ		
基礎		■ 立上り巾木: モルタル刷毛引き		-
基礎水切り金物		■ JOTO鋼板製 防鼠材付き水切り JOTO:WMF-N35		ブラック
バルコニー	床・内壁	■ なし		-
	笠木	■ なし		
外部建具		■ LIXIL EW(アルゴンガス高遮熱仕様LowEトリプルガラス クリア) ・SD、TSは、メーカー設定による。 ・オペレーター付サッシの場合は固定網戸とする ・グレモンハンドル式サッシの場合は可動網戸とする		外観 ブラック 内観 シェド・オークforDesign ※樹脂パッキン・網戸付
シャッター		■ 手動シャッター LIXILガレージシャッター内部付		ブラック
軒天通気金物		■ なし		
玄関扉		■ LIXIL ジェスタ2 K2仕様 LIXILファミロック タグキー×3 (電池式)		ドア型: M17 型 ドア色: マッド ブラック ハンドル: S型ハンドル 色: ブラック
外部物干し金物		■ なし		
換気フード	■ 局所換気扇(トイレ 浴室 キッチンフード) 防火ダンパー無		外気フード:	ブラック
	■ ダクトレス熱交換換気システム (日本スティーベル株式会社) VLR-70E		外気フード:	B ブラック
	防火ダンパー無		室内パネル	マッドブラック

■ 構 造 概 要					
基礎	■ RCベタ基礎コンクリート				
通し柱・管柱	■ 構造用集成材 105×105		間柱	■ 集成材	
土台	■ 桧 105×105	大引き	■ 桧 90*90	筋交い	■ 構造用製材 火打梁 ■ 鋼製火打(当社基準により米松あり)
桁・梁	■ 構造用製材及び集成材		制震装置	■ Kダンパー (株)アイ・エム・エー	
■ 設 備 装 着 品					
住宅設備	部位	メーカー	商品名 ※ 詳細は見積り、プレゼン参照	見積りNo.	(日付)
	キッチン	LIXIL	■ ES ペニンシュラ	見積り番号 : M26019847625-008-2	2026.03.04
	バックカウンタ ※オプション	LIXIL	■ ES W2565	見積り番号 : M26019847625-008-3	2026.03.04
	浴室	LIXIL	■ AX1616 PGハウス標準仕様	見積り番号 : M26019847625-008-1	2026.03.04
	1Fトイレ	LIXIL	■ ベーシアシャワートイレ 白 ● タオル掛け: 無し タンク手洗 無し ● 紙巻き器: FKF-AE34W/MBK	見積り番号 : M26019847625-008-7	2026.03.04
	洗面台	LIXIL	■ カスタムパニティW1200(ボウルW750) ※2026モデル ミラーキャビネット スクエアミラー-W1200 ● タオル掛け: 無し	見積り番号 : M26019847625-008-5	2026.03.04
給排水設備	給湯器	■ エコキュート370L Panasonic Sシリーズ スタンダードモデル 追い焚きフルオート			
	排水	■ 下水			
	外水栓	■ 1 カ所 (配置図参照) ■ 外部立栓柱: PVC製 水栓柱12型【前澤化成工業】			
	外部ガーデンパン	■ 無し			
	その他	■ 洗濯機用単水栓: 緊急止水弁付 ■ 洗濯機用排水: トラップ金物(標準) ■ 排水さや管(長期優良住宅仕様)			
ガス配管設備	■ なし ■ガス使用器具				
電気設備	インターホン	■ パナソニック ブラックモデルVL-SWD505KFK			
	TVアンテナ	■ UHF + BS・110度CS／CSアンテナ [2K・4K・8K対応] ■ブラック ※電波状況によりホワイトになる可能性あり			
	エアコン	■ 設置場所:			
	ソーラー ※標準搭載	■ あり(Qセルズ) 12 枚 5.28 KW Re.RISE-G3 440 (1722×1134×30) ※メーカーのモデルチェンジ等で後継品に変更される可能性あり ■ 屋外パワコン エネルギーマネジメントシステム Cube J			
	その他				


	浜 岡 一 級 総 合 設 計 事 務 所 一級建築士事務所 静岡県知事登録第 (10)2441 号 一級建築士 大臣登録第 365879 号 西原利昌	 株式会社 LIFEFUND InDesign office 一級建築士事務所 事務所登録 (2) 第7595号 一級建築士登録 第179770号 鈴木 達男 〒432-8023 静岡県浜松市中央区鴨江3丁目70番23号	年 月 日 2026.3.15	件名 山村和孝 様邸 新築工事	設計 IC 工務 図 番 角谷 青島 1-1
			縮尺	図面 仕上表 1	

浜松市中央区倉松地内

G2

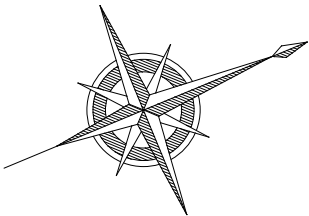


求積図

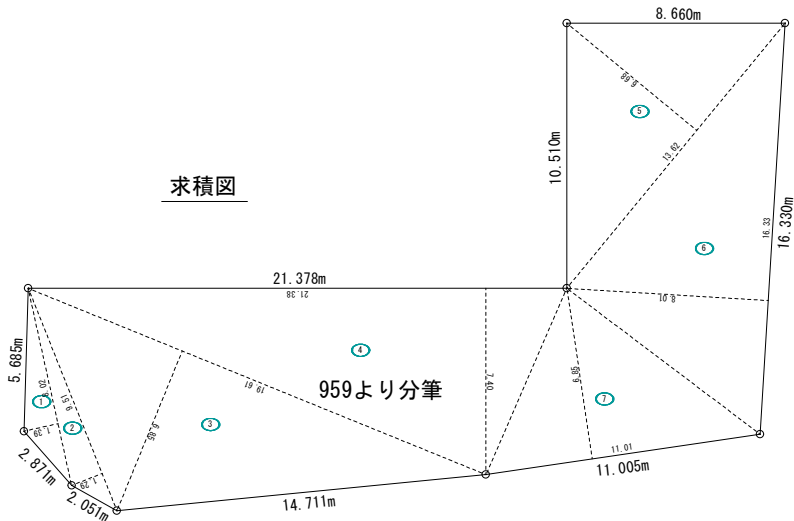


番号	底 辺	高 さ	倍 面 積	面 積
1	8.02	1.39	11.1478	5.57390
2	9.51	1.29	12.2679	6.13395
3	19.61	6.85	134.3285	67.16425
4	21.38	7.40	158.2120	79.10600
5	13.62	6.68	90.9816	45.49080
6	16.33	8.01	130.8033	65.40165
7	11.01	6.85	75.4185	37.70925
合 計				306.57980
敷 地 面 積				306.57 m²

トータル面積表		(㎡)
敷地面積		306.57
建築面積		93.16
床面積	1階	86.12
	2階	11.59
延床面積		97.71
建蔽率	(93.16/306.57) × 100	30.39%
容積率	(97.71/306.57) × 100	31.88%


道路斜線制限については、明らかに適合する。
隣地斜線制限については、明らかに適合する。
平均地盤面について
申請建物の周囲の平均地盤面高さをBM+200とする。
盛土規制法の許可対象となる工事なし。

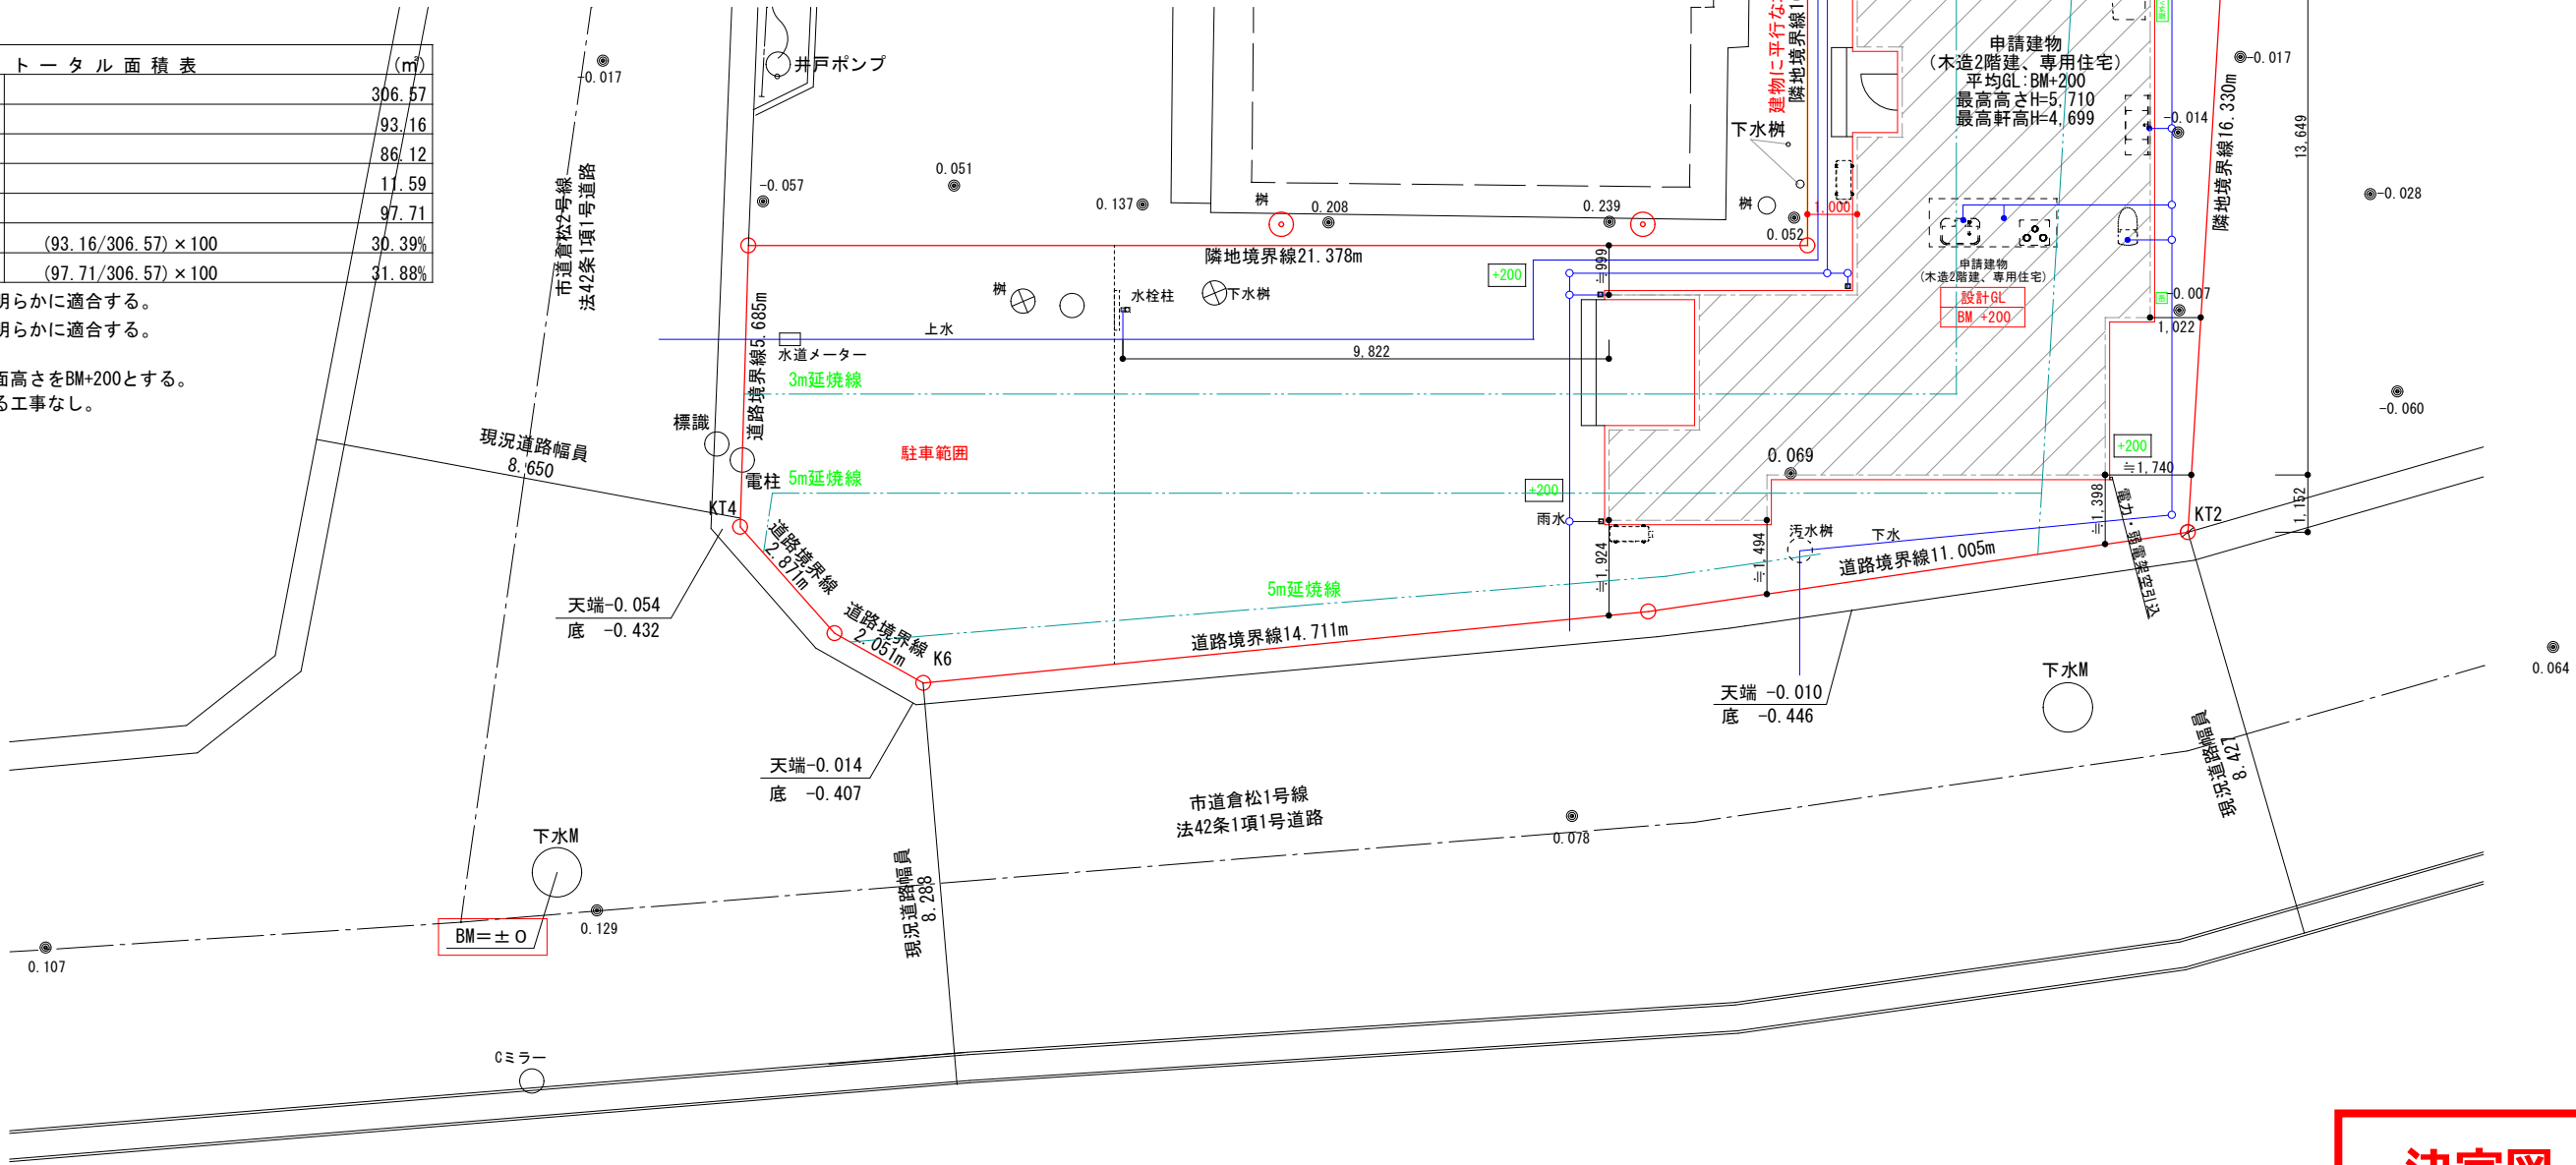


決定図

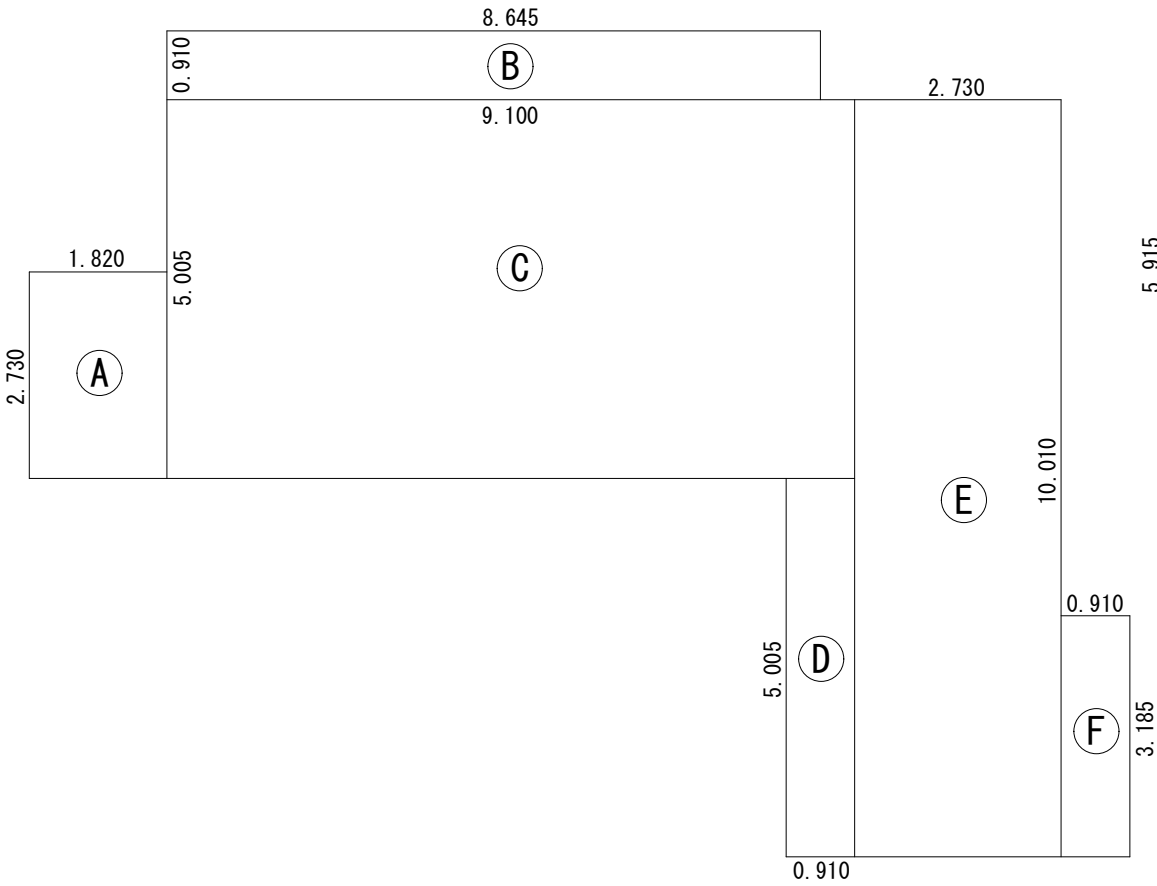

建築面積求積図 S=1/100

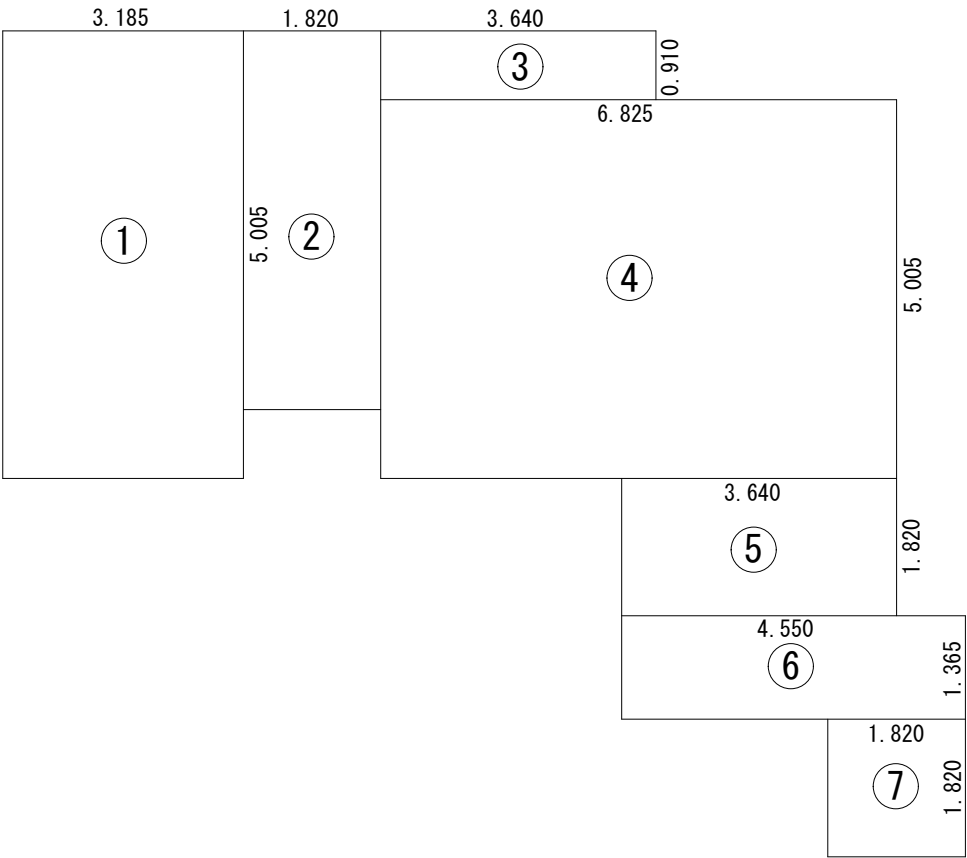

1階床面積図 S=1/100

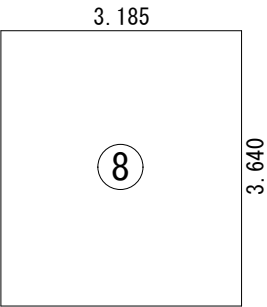

2階床面積図 S=1/100

建築面積求積表

番号	計算式 (m)	面積 (㎡)
Ⓐ	1.820 × 2.730	4.9686
Ⓑ	8.645 × 0.910	7.8670
Ⓒ	9.100 × 5.005	45.5455
Ⓓ	0.910 × 5.005	4.5546
Ⓔ	2.730 × 10.010	27.3273
Ⓕ	0.910 × 3.185	2.8983
合計		93.1613
		93.16 (28.1坪)

1階床面積求積表

番号	計算式 (m)	面積 (㎡)
①	3.185 × 5.915	18.8392
②	1.820 × 5.005	9.1091
③	3.640 × 0.910	3.3124
④	6.825 × 5.005	34.1591
⑤	3.640 × 1.820	6.6248
⑥	4.550 × 1.365	6.2107
⑦	1.820 × 1.820	3.3124
合計		81.5678
		81.56 (24.6坪)


2階床面積求積表

番号	計算式 (m)	面積 (㎡)
⑧	3.185 × 3.640	11.5934
合計		11.5934
		11.59 (3.5坪)

延べ床面積表

	番号 (m)	面積 (㎡)
1階床面積	①②③④⑤⑥⑦	81.56
2階床面積	⑧	11.59
合計		93.15
		(28.1坪)

決定図

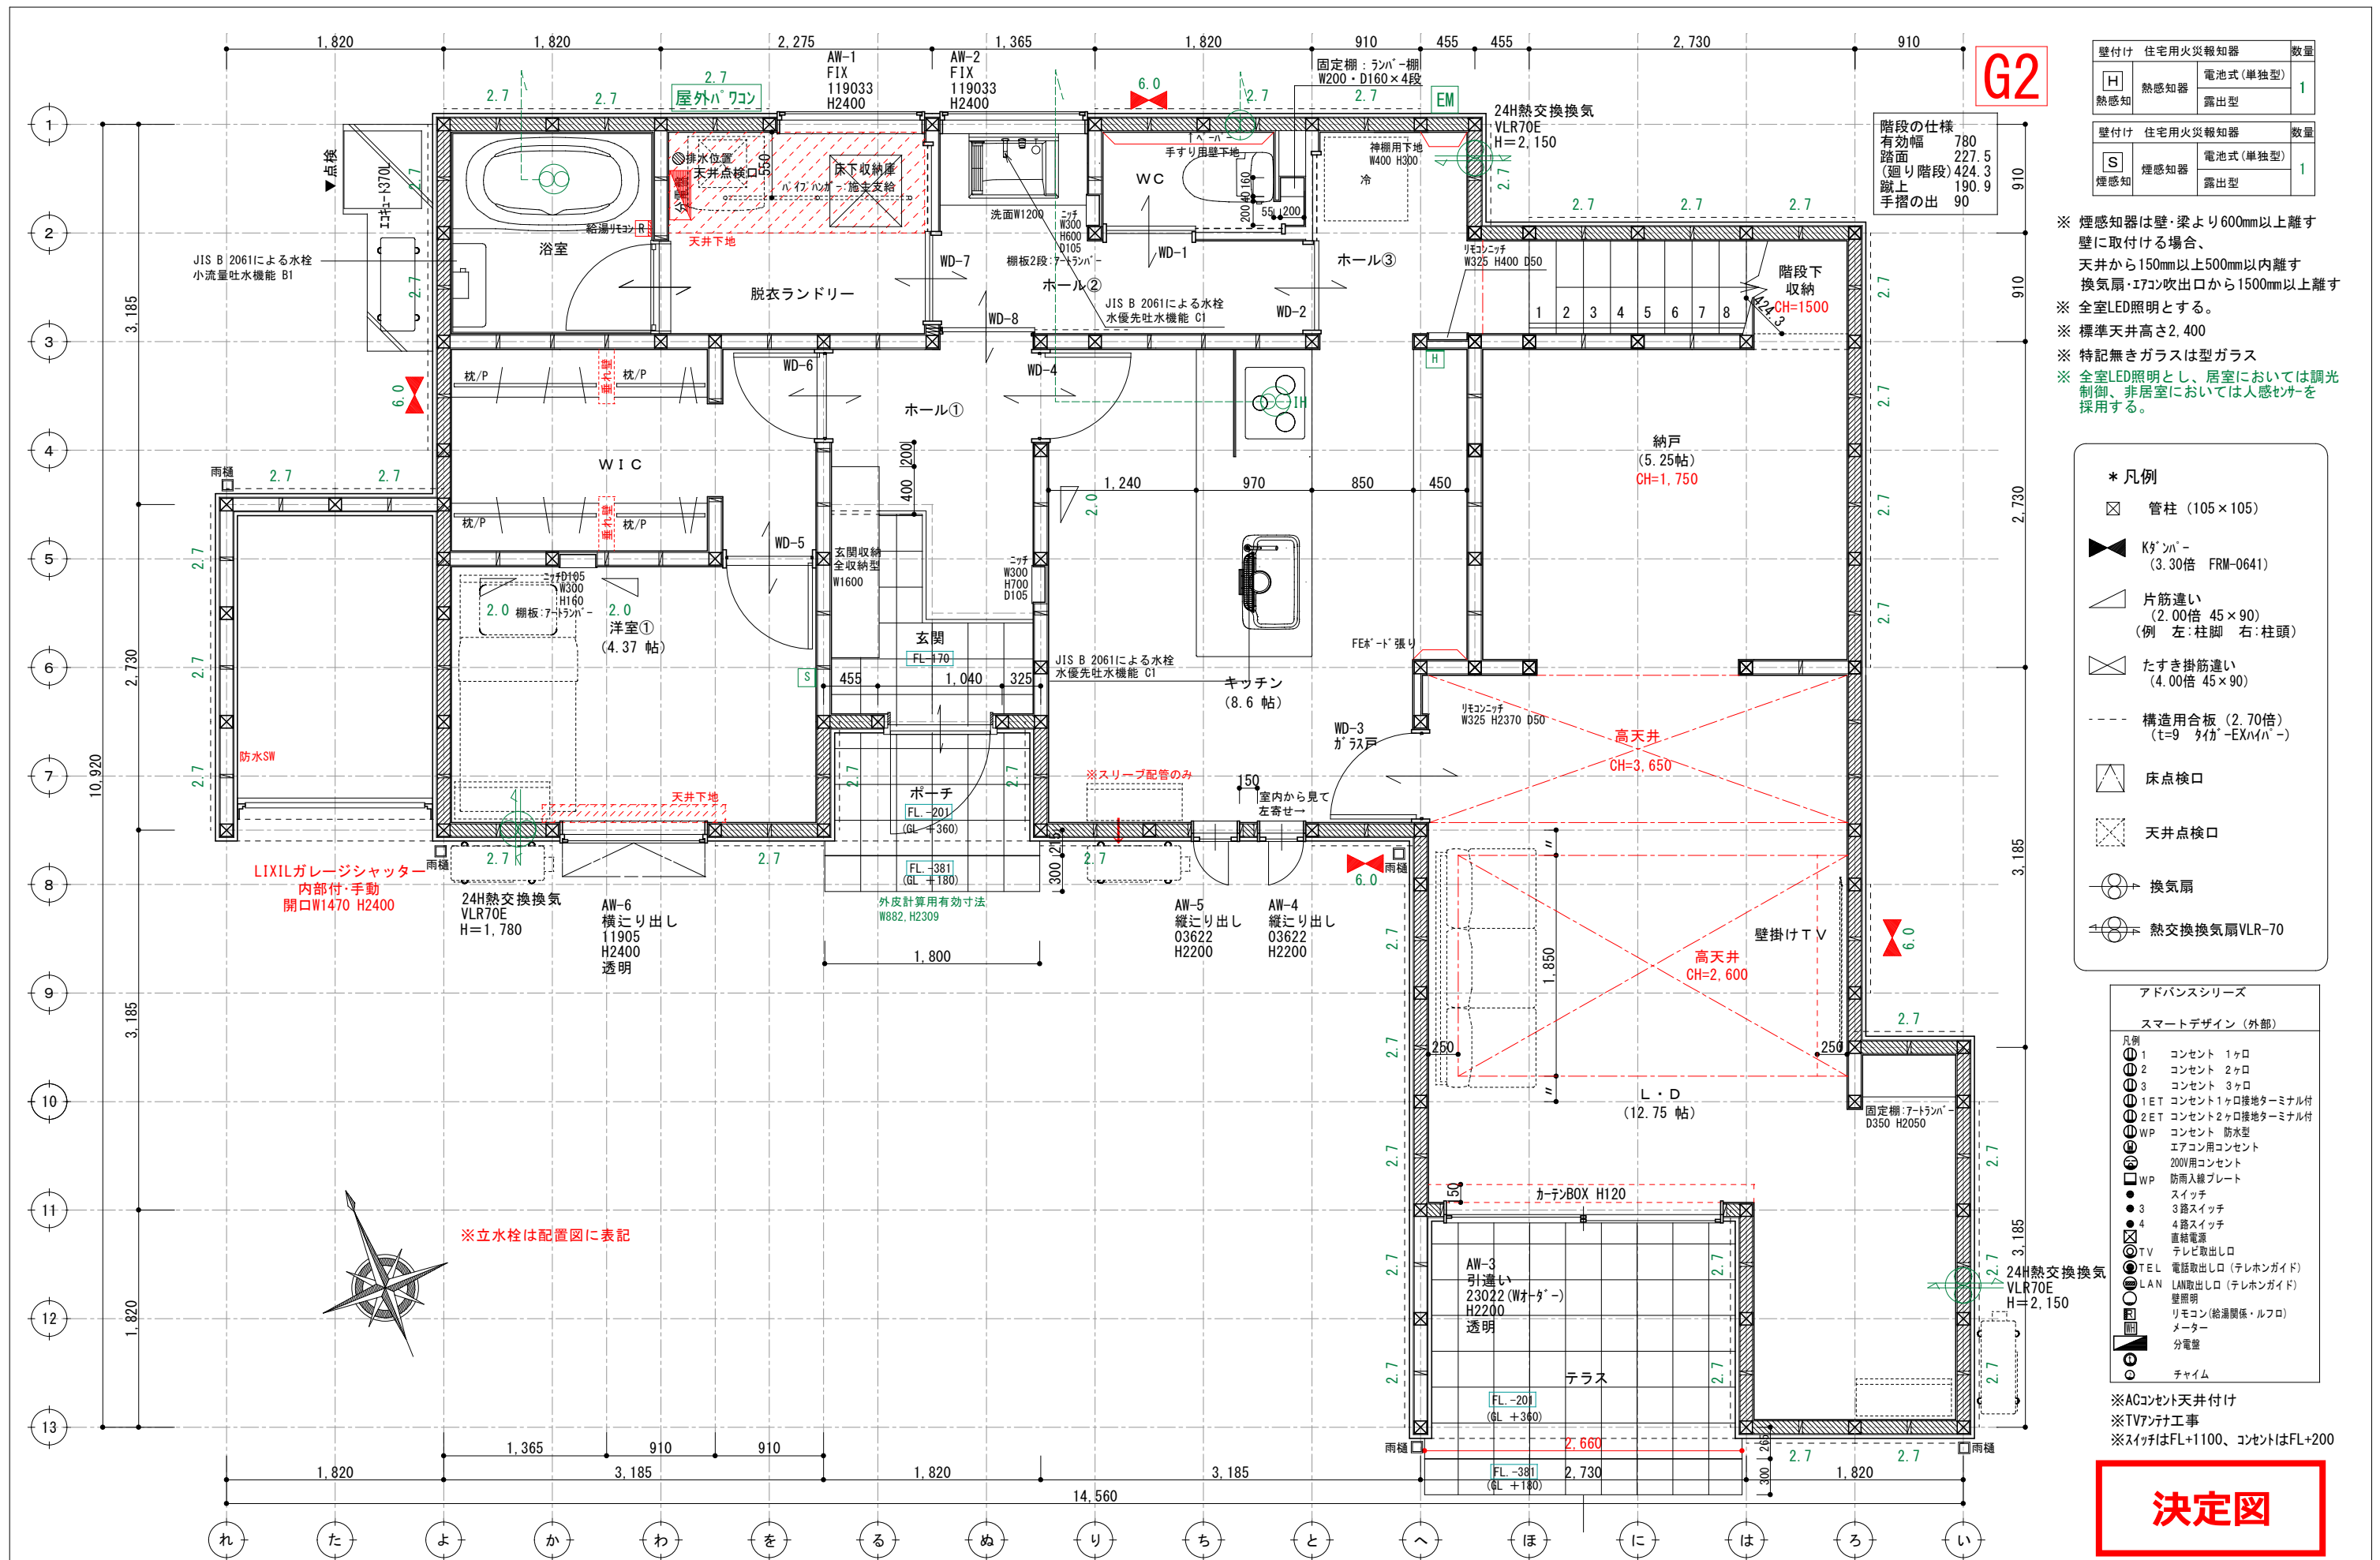

壁付け 住宅用火災報知器			数量
H	熱感知器	電池式(単独型)	1
	熱感知器	露出型	
壁付け 住宅用火災報知器			数量
S	煙感知器	電池式(単独型)	1
	煙感知器	露出型	

※ 煙感知器は壁・梁より600mm以上離す
壁に取付ける場合、
天井から150mm以上500mm以内離す
換気扇・エアコン吹出口から1500mm以上離す
※ 全室LED照明とする。
※ 標準天井高さ2,400
※ 特記無きガラスは型ガラス
※ 全室LED照明とし、居室においては調光
制御、非居室においては人感センサー
を採用する。

- * 凡例**
- 管柱 (105×105)
 - K*ンバー (3.30倍 FRM-0641)
 - 片筋違い (2.00倍 45×90)
(例 左:柱脚 右:柱頭)
 - たすき掛筋違い (4.00倍 45×90)
 - 構造用合板 (2.70倍)
(t=9 タイパ-EXハイパ-)
 - 床点検口
 - 天井点検口
 - 換気扇
 - 熱交換換気扇VLR-70

アドバンスシリーズ	
スマートデザイン (外部)	
凡例	
1	コンセント 1ヶ所
2	コンセント 2ヶ所
3	コンセント 3ヶ所
1ET	コンセント1ヶ所接地ターミナル付
2ET	コンセント2ヶ所接地ターミナル付
WP	コンセント 防水型
WP	エアコン用コンセント
WP	200V用コンセント
WP	防雨入線プレート
WP	スイッチ
3	3路スイッチ
4	4路スイッチ
●	直結電源
TV	テレビ取出口
TEL	電話取出口 (テレホンガイド)
LAN	LAN取出口 (テレホンガイド)
●	壁照明
●	リモコン (給湯関係・ルフロ)
●	メーター
●	分電盤
●	チャイム

※ACコンセント天井付け
※TVアンテナ工事
※スイッチはFL+1100、コンセントはFL+200

決定図

G2

壁付け 住宅用火災報知器			数量
熱感知	H	電池式(単独型)	
		露出型	
壁付け 住宅用火災報知器			数量
煙感知	S	電池式(単独型)	4
		露出型	

- ※ 煙感知器は壁・梁より600mm以上離す
壁に取付ける場合、
天井から150mm以上500mm以内離す
換気扇・エアコン吹出口から1500mm以上離す
- ※ 全室LED照明とする。
- ※ 標準天井高さ2,400
- ※ 特記無きガラスは型ガラス
- ※ 全室LED照明とし、居室においては調光制御、非居室においては人感センサーを採用する。

* 凡例

- ☒ 管柱 (105 × 105)
- ≡ K&Pバ - (3.30倍 FRM-0641)
- △ 片筋違い (2.00倍 45 × 90)
(例 左:柱脚 右:柱頭)
- ⊗ たすき掛筋違い (4.00倍 45 × 90)
- 構造用合板 (2.70倍)
(t=9 タイガ EXNバ -)
- ▤ 床点検口
- ▥ 天井点検口
- ⊕ 換気扇
- ⊕ 熱交換換気扇VLR-70


アドバンスシリーズ

スマートデザイン (外部)


- 凡例
- ① コンセント 1ヶロ
- ② コンセント 2ヶロ
- ③ コンセント 3ヶロ
- ①ET コンセント1ヶロ接地ターミナル付
- ②ET コンセント2ヶロ接地ターミナル付
- WP コンセント 防水型
- ⊕ エアコン用コンセント
- ⊕ 200V用コンセント
- WP 防雨入線プレート
- スイッチ
- 3 3路スイッチ
- 4 4路スイッチ
- ⊕ 直結電源
- ⊕ TV テレビ取出口
- TEL 電話取出口 (テレホンガイド)
- LAN LAN取出口 (テレホンガイド)
- ⊕ 壁照明
- ⊕ リモコン (給湯関係・ルフロ)
- ⊕ メーター
- ⊕ 分電盤
- チャイム

- ※ACコンセント天井付け
- ※TVアンテナ工事
- ※スイッチはFL+1100、コンセントはFL+200

決定図

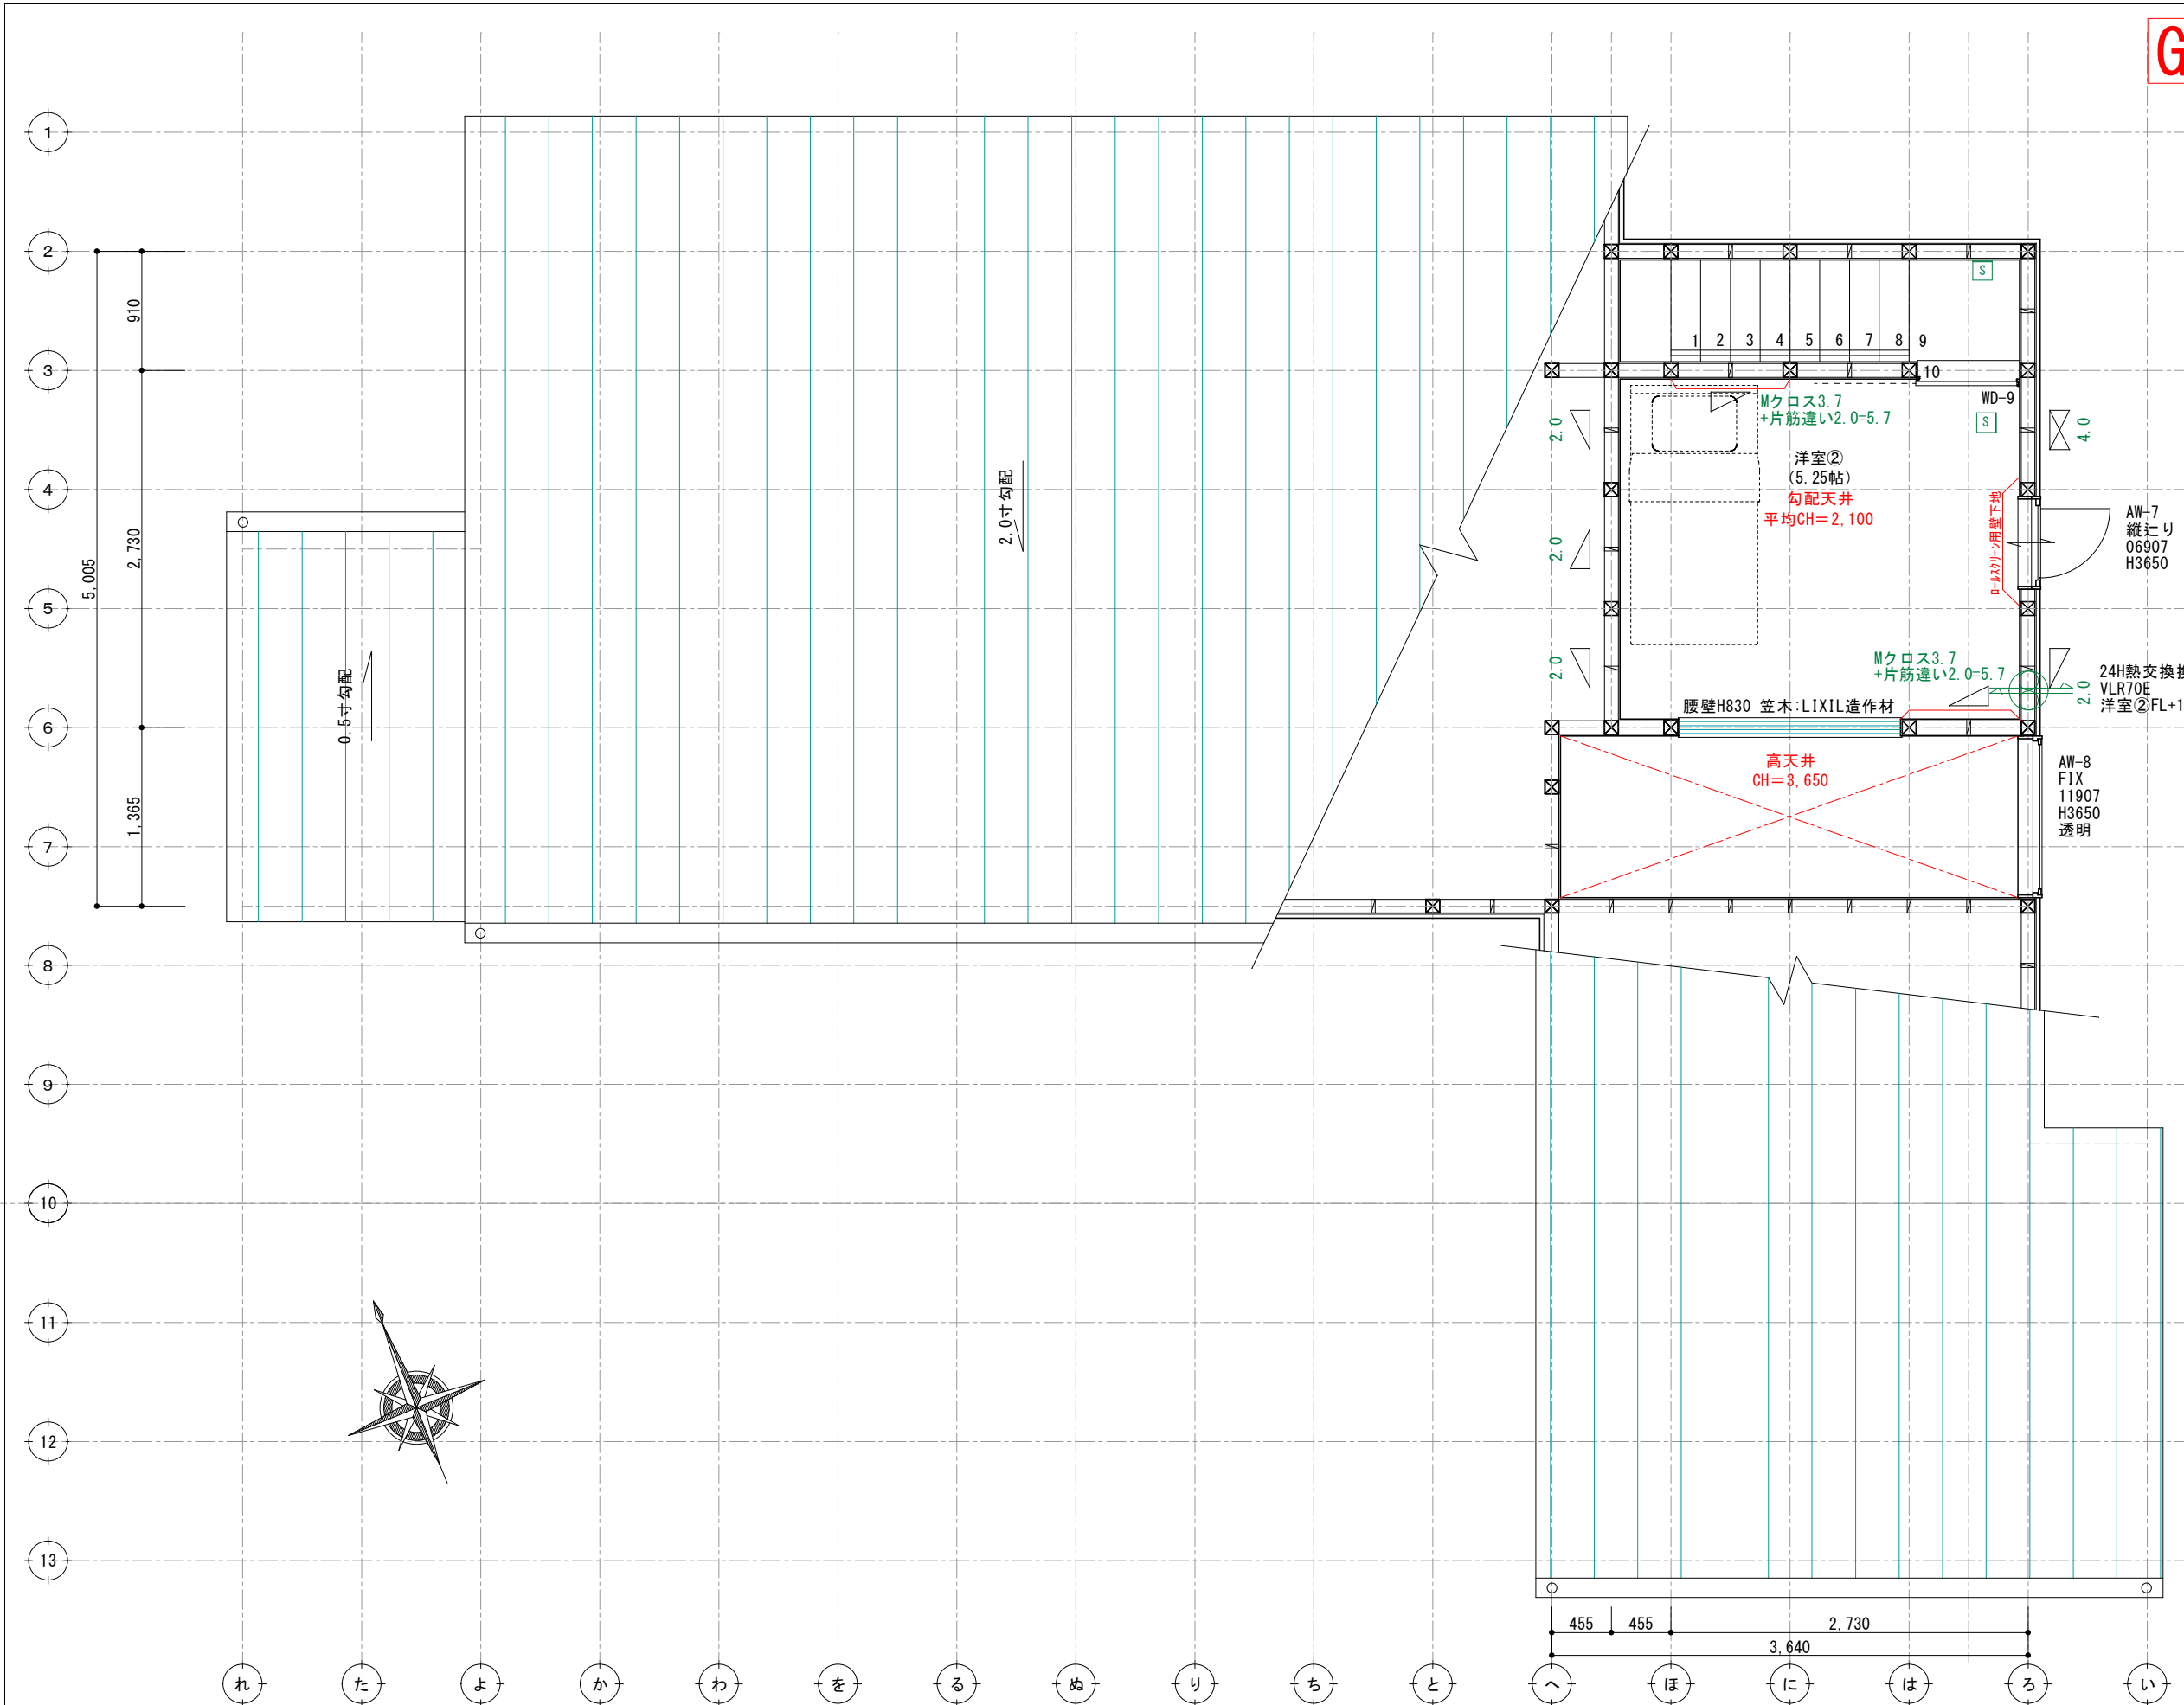


訂正	浜岡 一級総合設計事務所 一級建築士事務所 静岡県知事登録第 (10)2441 号 一級建築士 大臣登録第 365879 号 西原利昌	 ピージーハウス	株式会社 LIFEFUND InDesign office 一級建築士事務所 事務所登録 (2)第7595号 一級建築士登録 第179770号 鈴木 達男 〒432-8023 静岡県浜松市中央区鴨江3丁目70番23号	年月日 2026.3.15	件名 山村和孝様邸 新築工事	設計 IC 工事 図番	角谷	青島	3-2
				縮尺 1/50	図名 2階平面図				

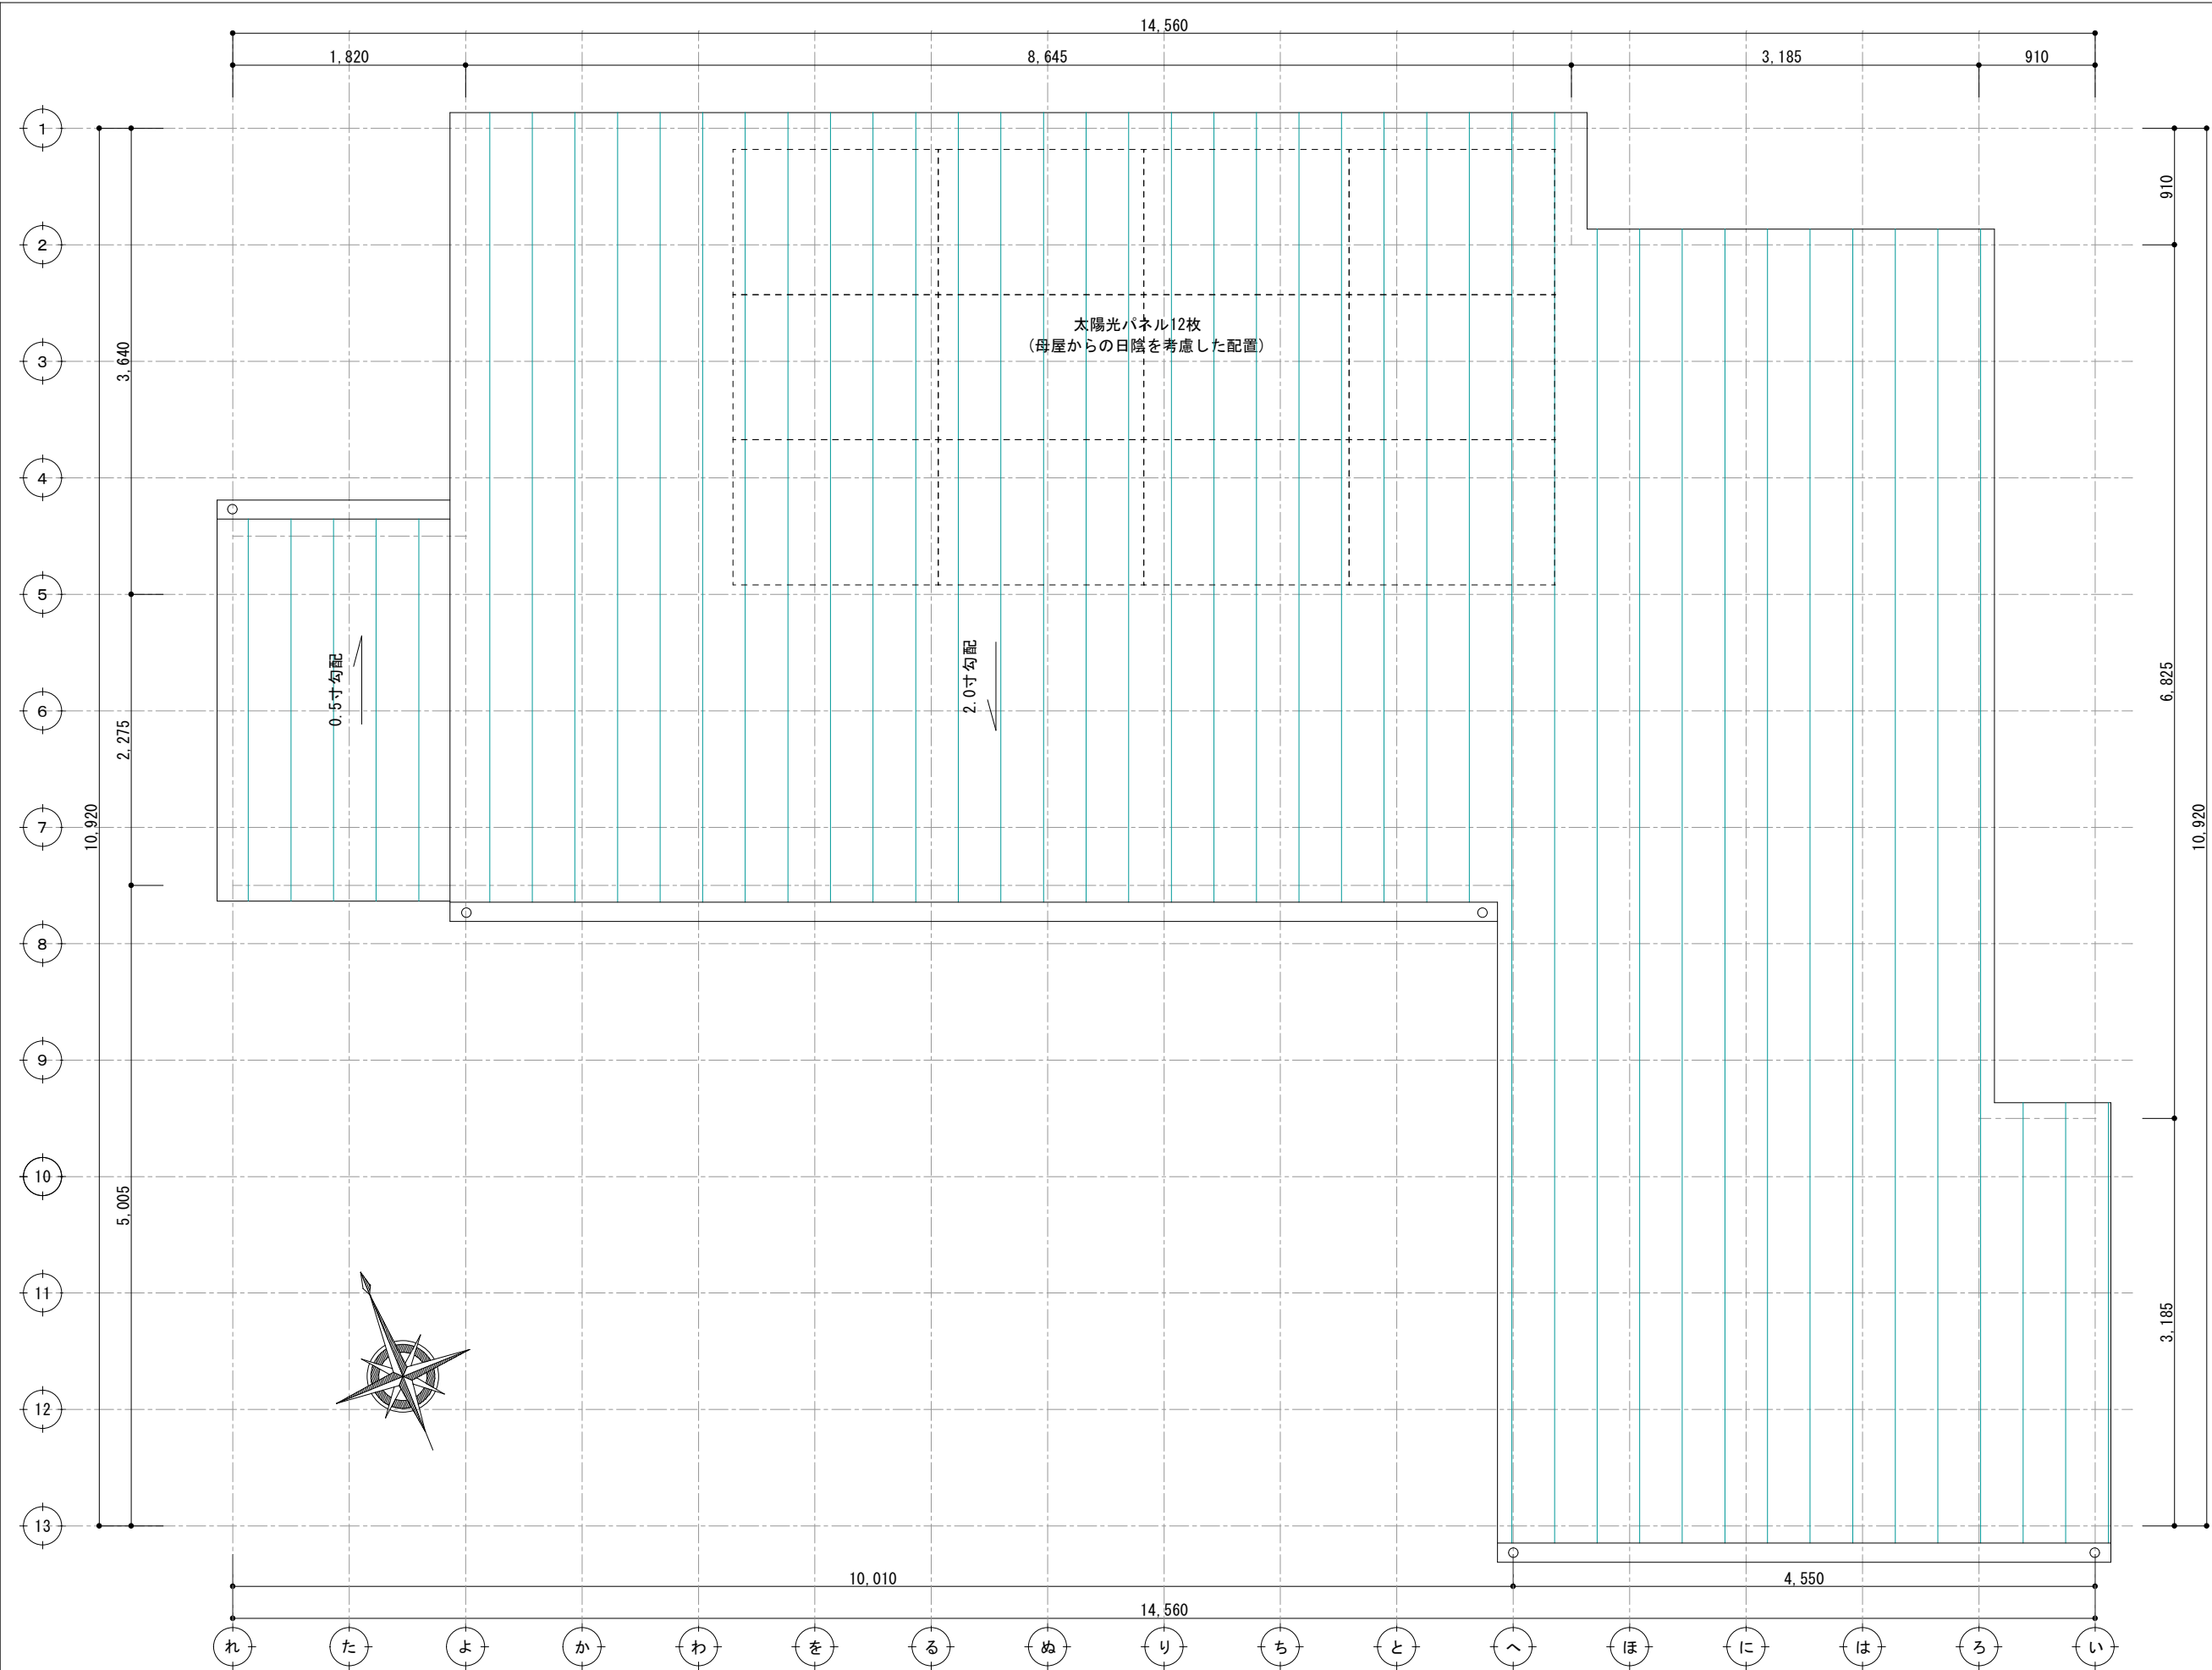

GX住宅
(Cube J付)
太陽光あり


決定図

訂正	浜岡一級総合設計事務所 一級建築士事務所 静岡県知事登録第 (10)2441 号 一級建築士 大臣登録第 365879 号 西原利昌	 ピージーハウス	株式会社 LIFEFUND InDesign office 一級建築士事務所 事務所登録 (2) 第7595号 一級建築士登録 第179770号 鈴木 達男 〒432-8023 静岡県浜松市中央区鴨江3丁目70番23号	年月日	件名	設計	IC	工事	図番
				2026. 3. 15	山村和孝様邸 新築工事				
				縮尺	図名				
				1/100	屋根伏図	角谷		青島	3-3

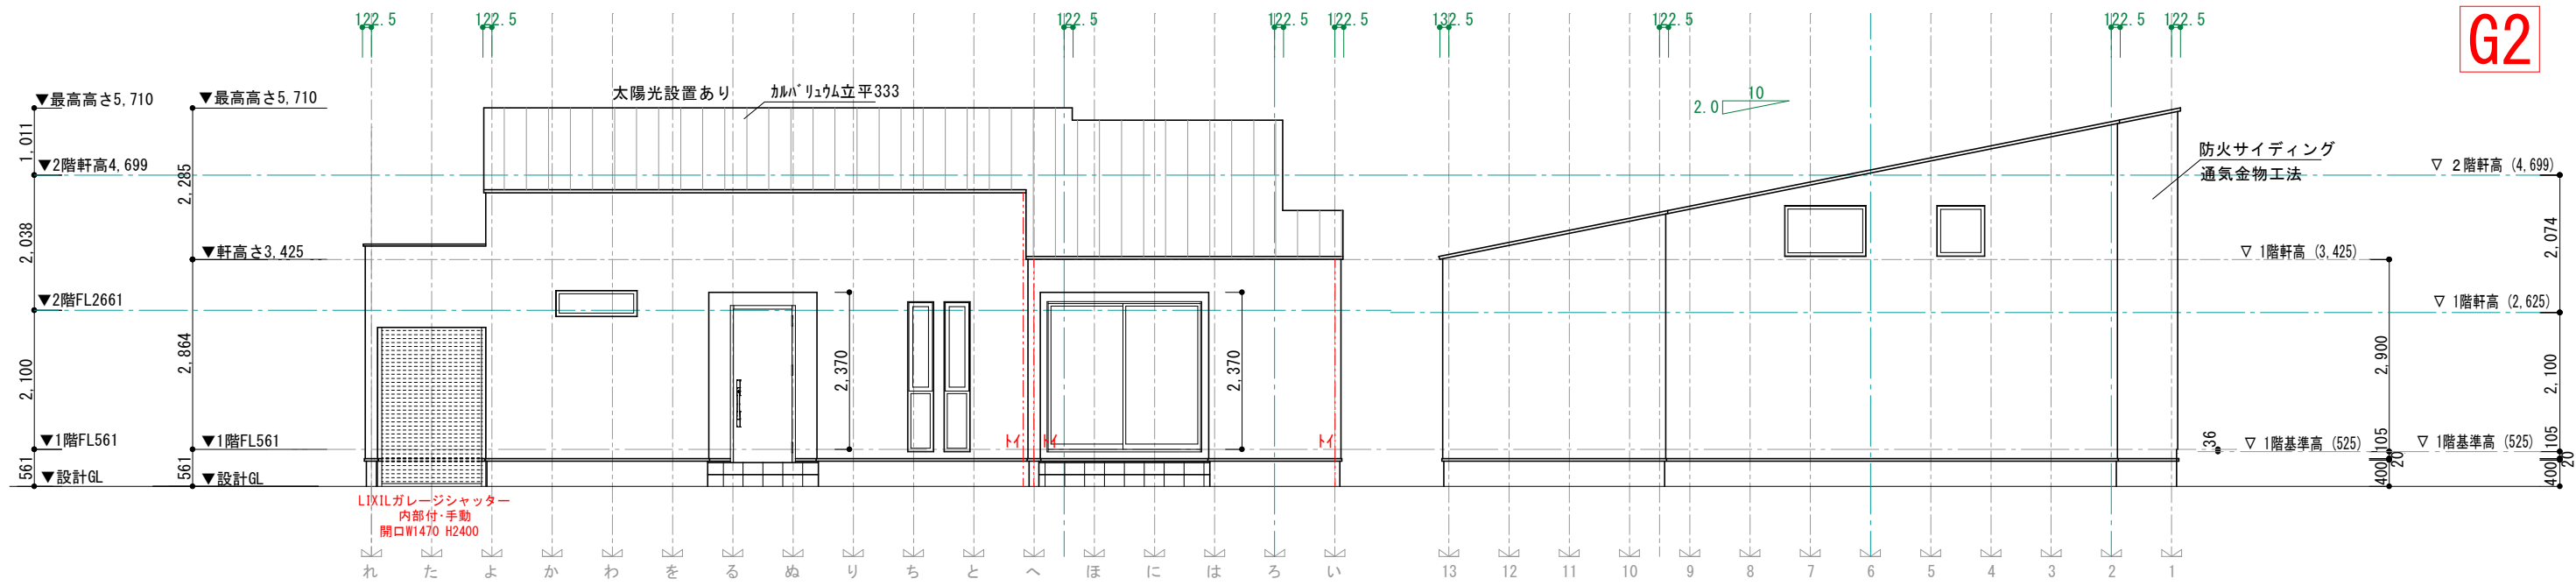

南側立面図 S=1/100

東側立面図 S=1/100

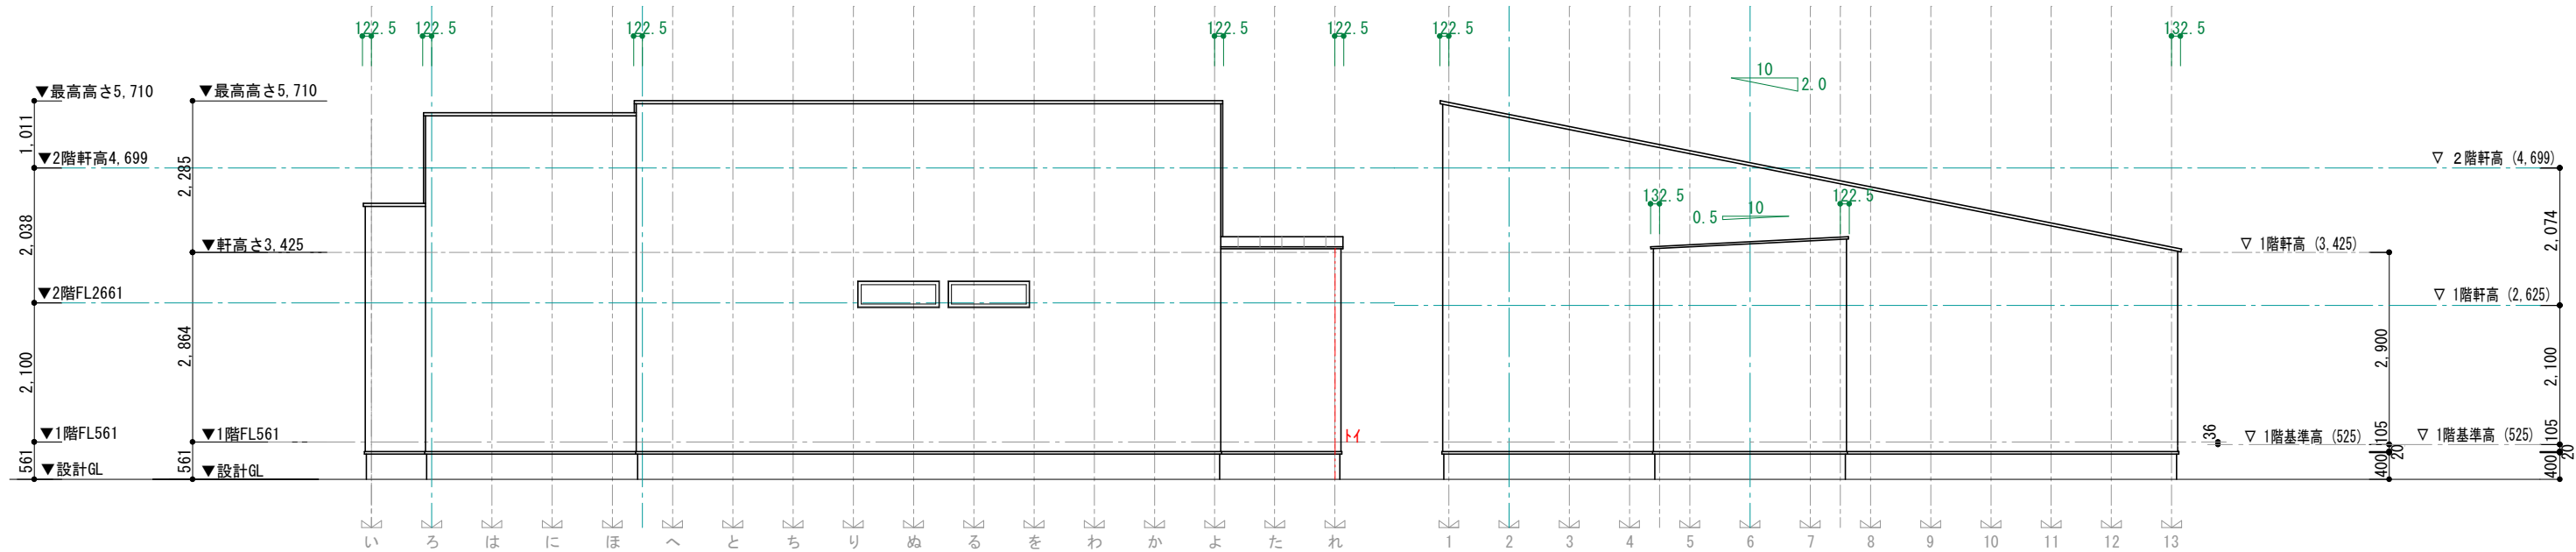


北側立面図 S=1/100

西側立面図 S=1/100


決定図

訂正	浜岡一級総合設計事務所 一級建築士事務所 静岡県知事登録第 (10)2441 号 一級建築士 大臣登録第 365879 号 西原利昌		株式会社 LIFEFUND InDesign office 一級建築士事務所 事務所登録 (2) 第7595号 一級建築士登録 第179770号 鈴木 達男 〒432-8023 静岡県浜松市中央区鴨江3丁目70番23号	年月日 2026.3.15	件名 山村和孝様邸 新築工事		設計	IC	工事	図番
				縮尺 1/100	図名 立面図		角谷		青島	4-1

G2

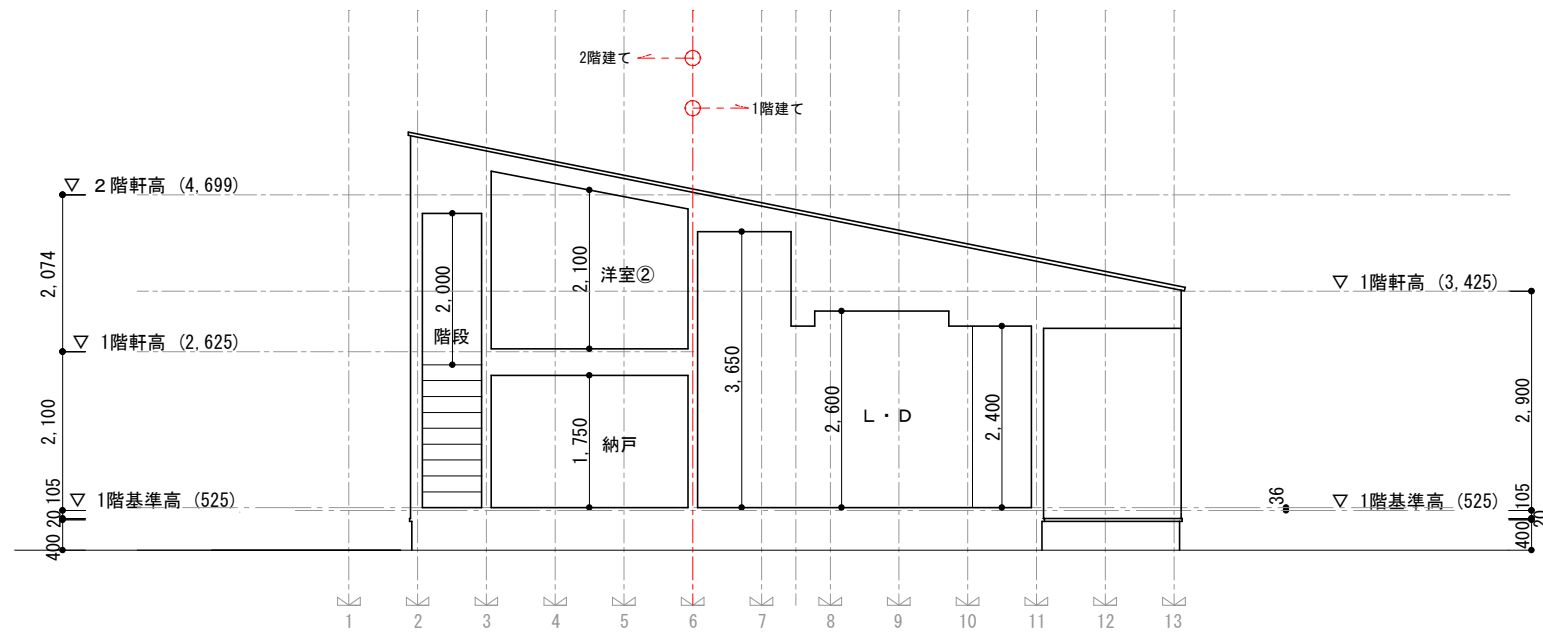


断面図(南北) S=1/100

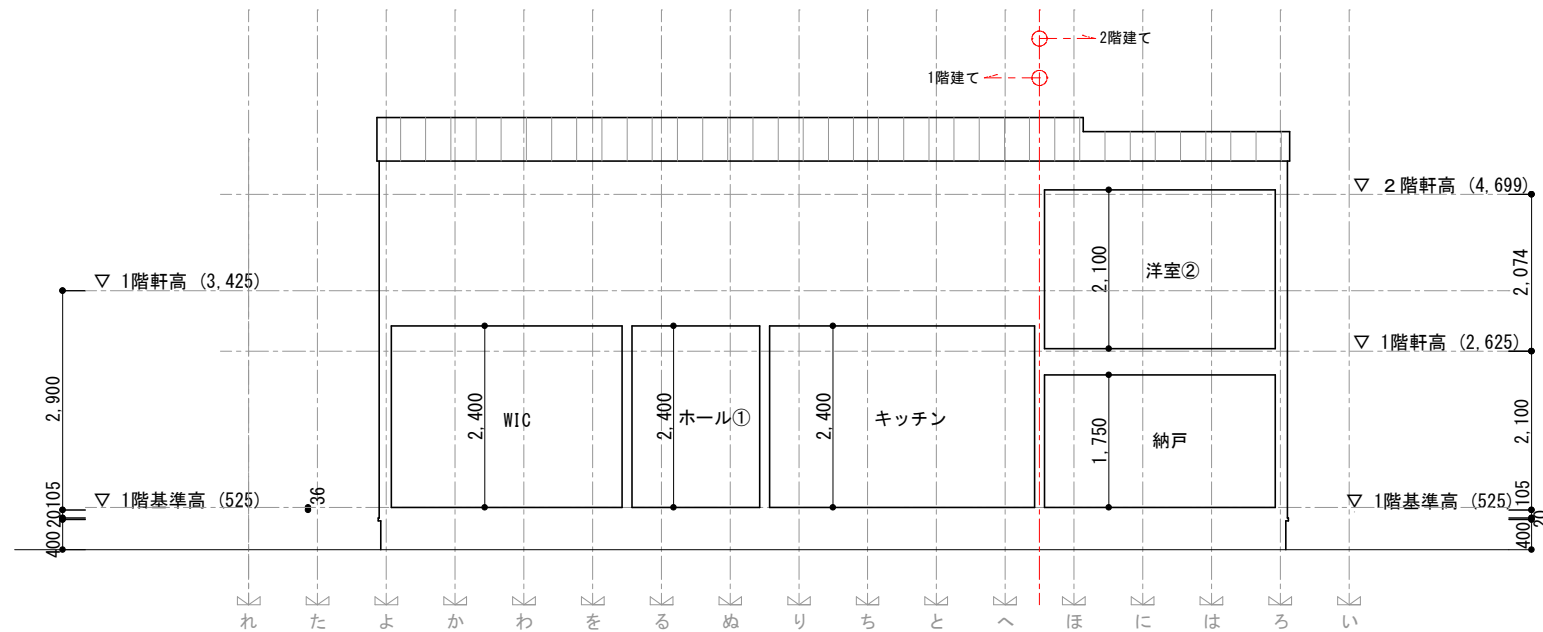



断面図(東西) S=1/100

決定図

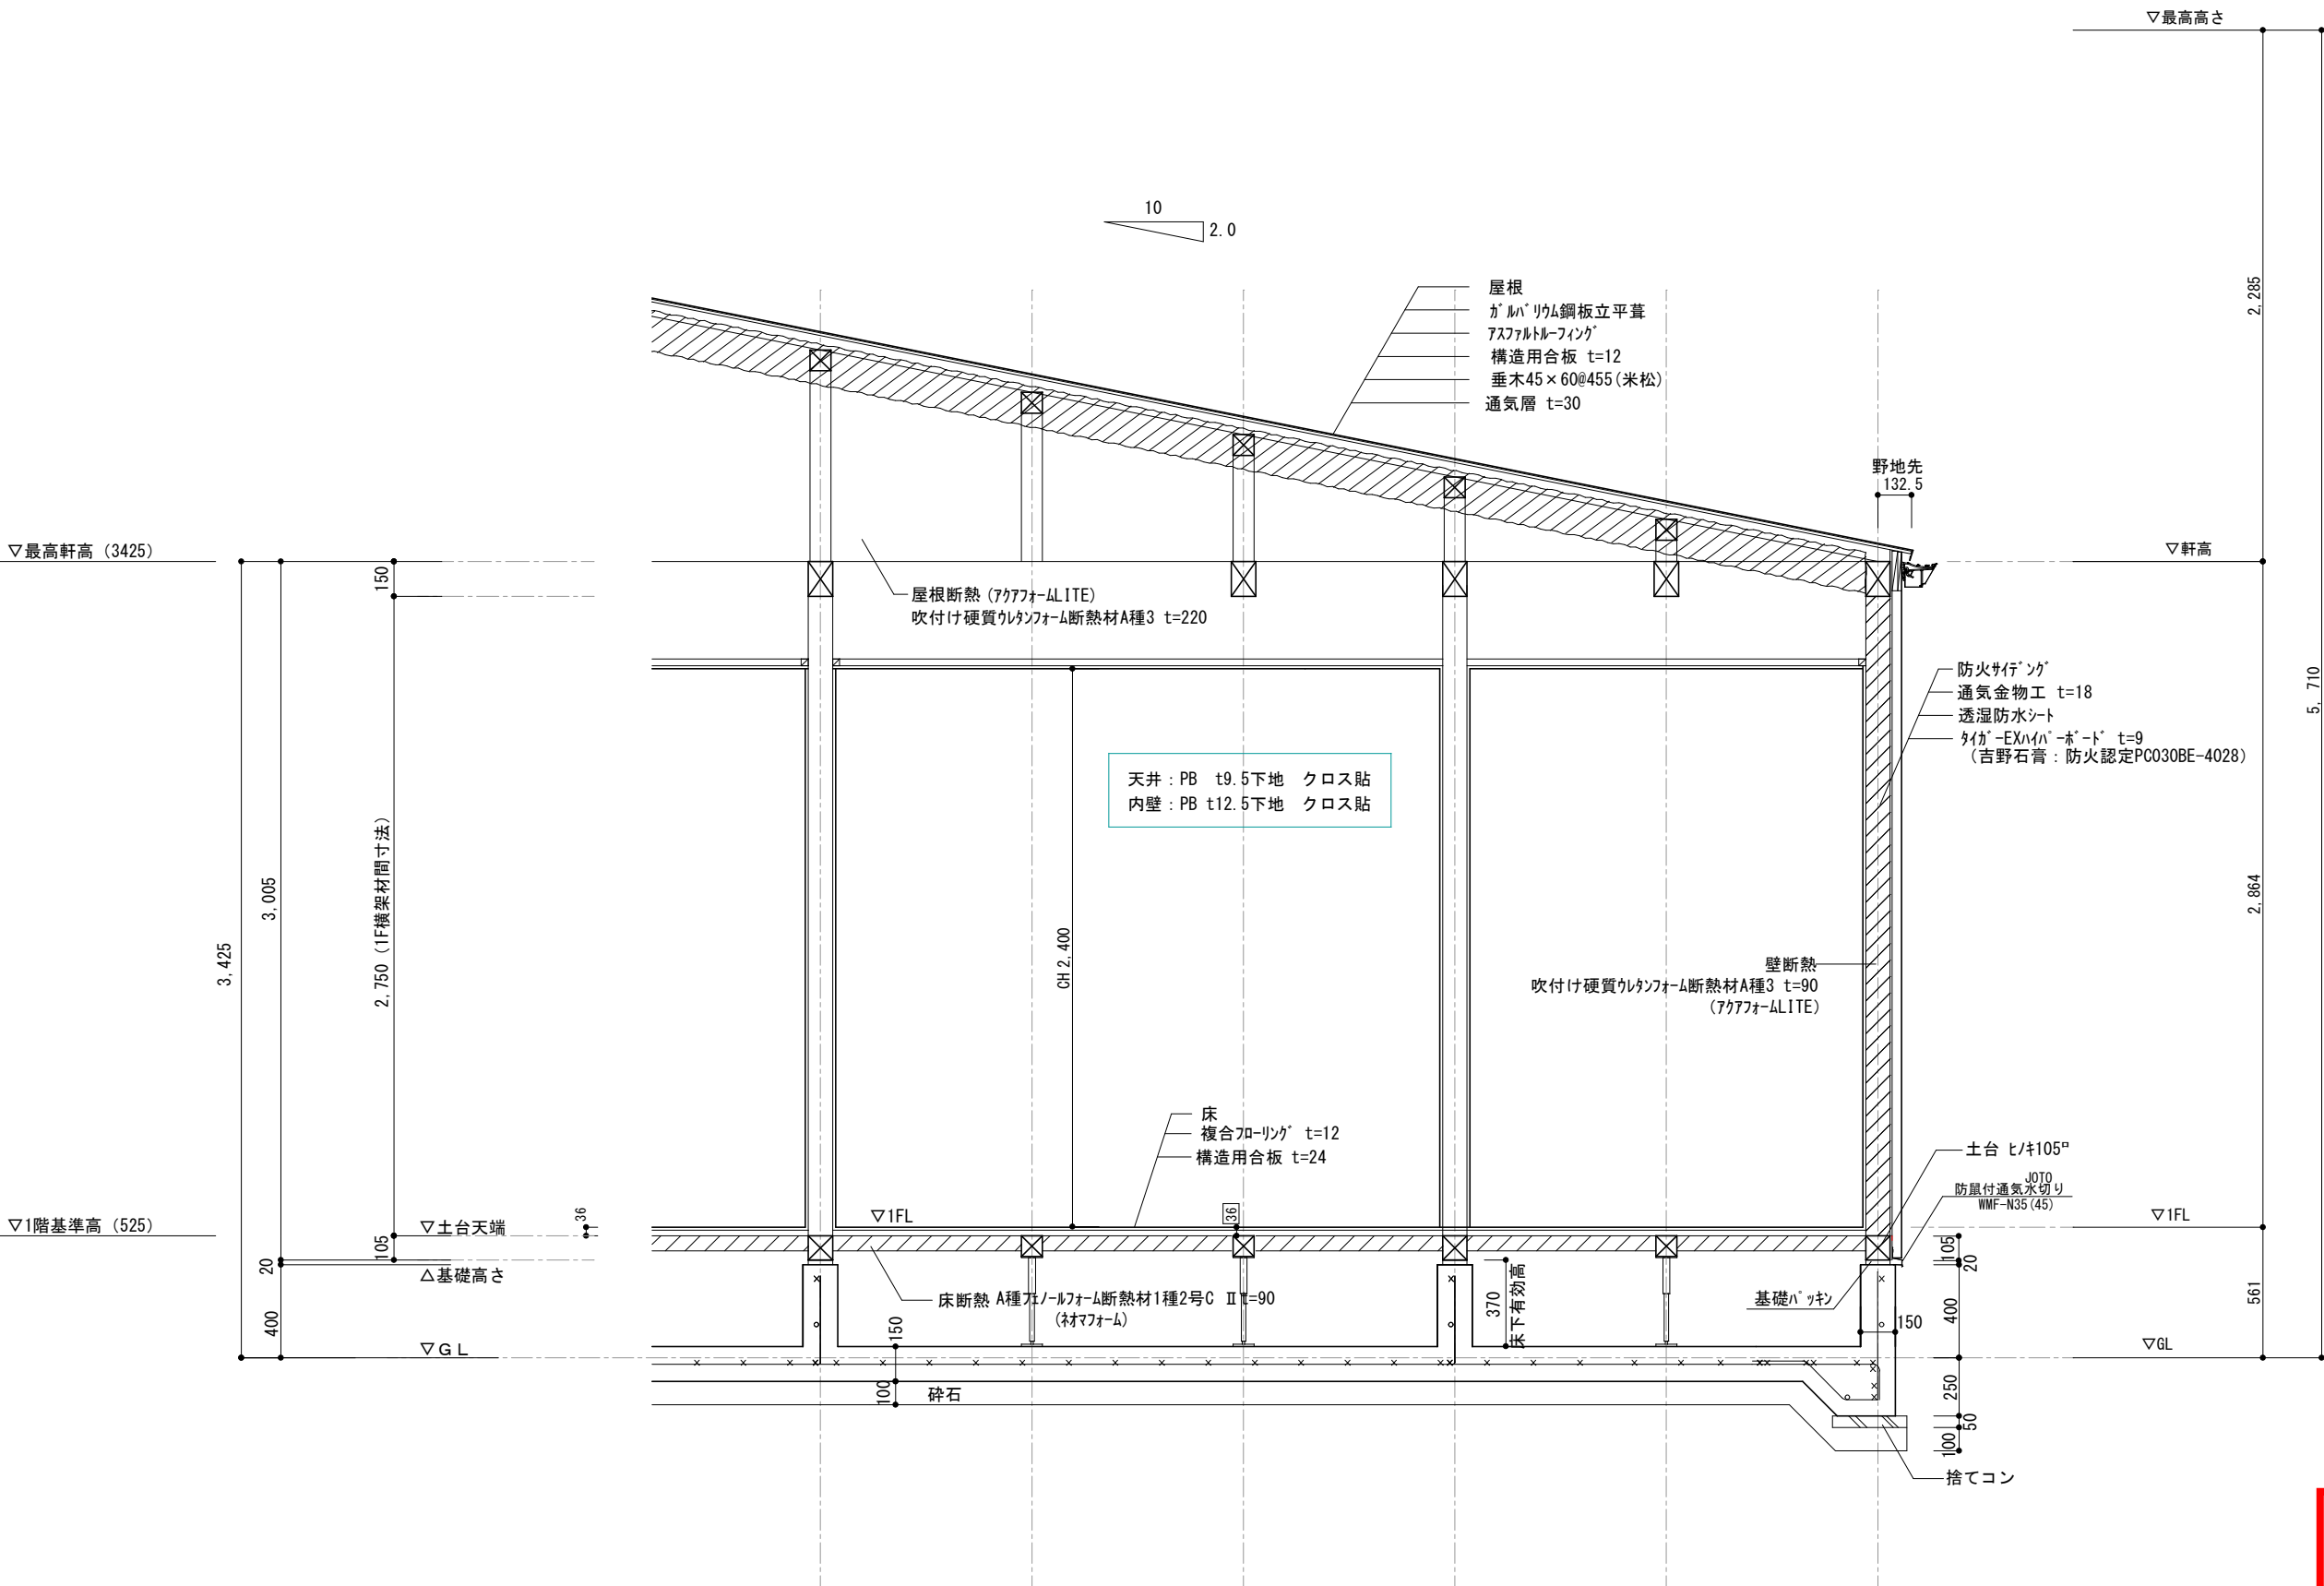



決定図

訂正	浜岡一級総合設計事務所 一級建築士事務所 静岡県知事登録第 (10)2441 号 一級建築士 大臣登録第 365879 号 西原利昌	 ピージーハウス	株式会社 LIFEFUND InDesign office 一級建築士事務所 事務所登録 (2) 第7595号 一級建築士登録 第179770号 鈴木 達男 〒432-8023 静岡県浜松市中央区鴨江3丁目70番23号	年月日 2026.03.15	件名 山村和孝様邸 新築工事	設計 角谷	IC	工事 青島	図番 5-1
				縮尺 1/30	図名 矩計図				

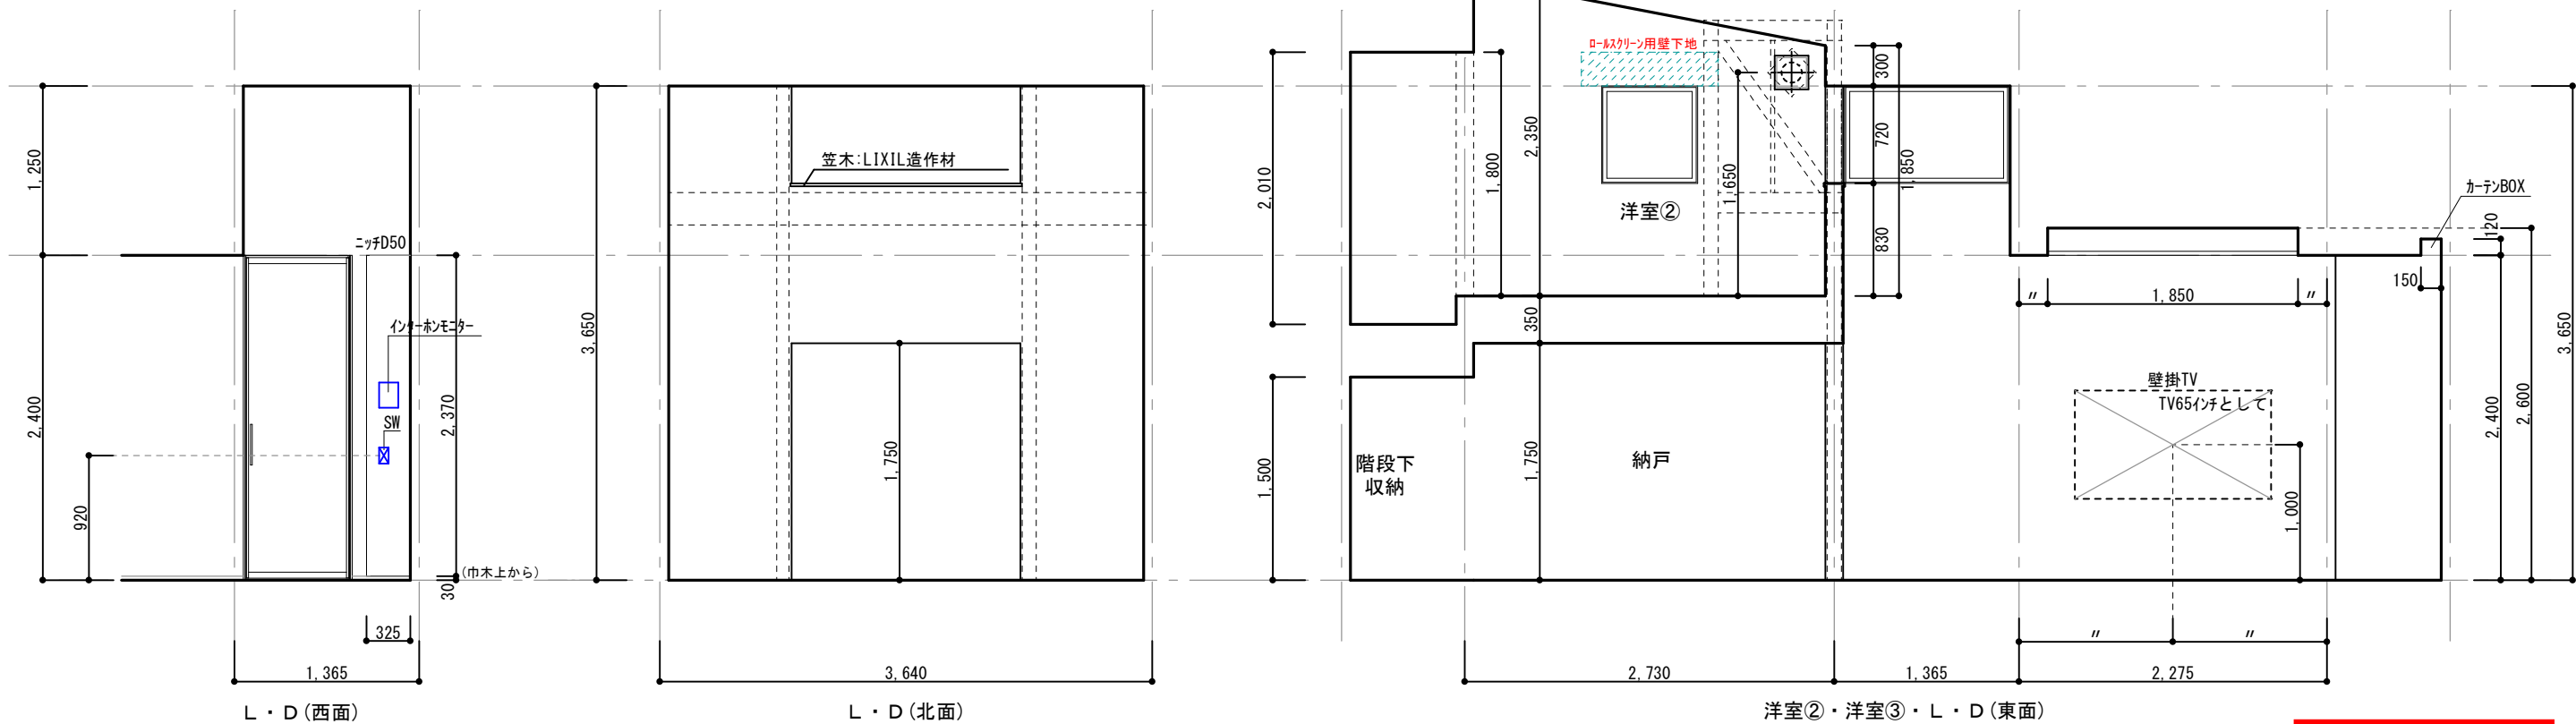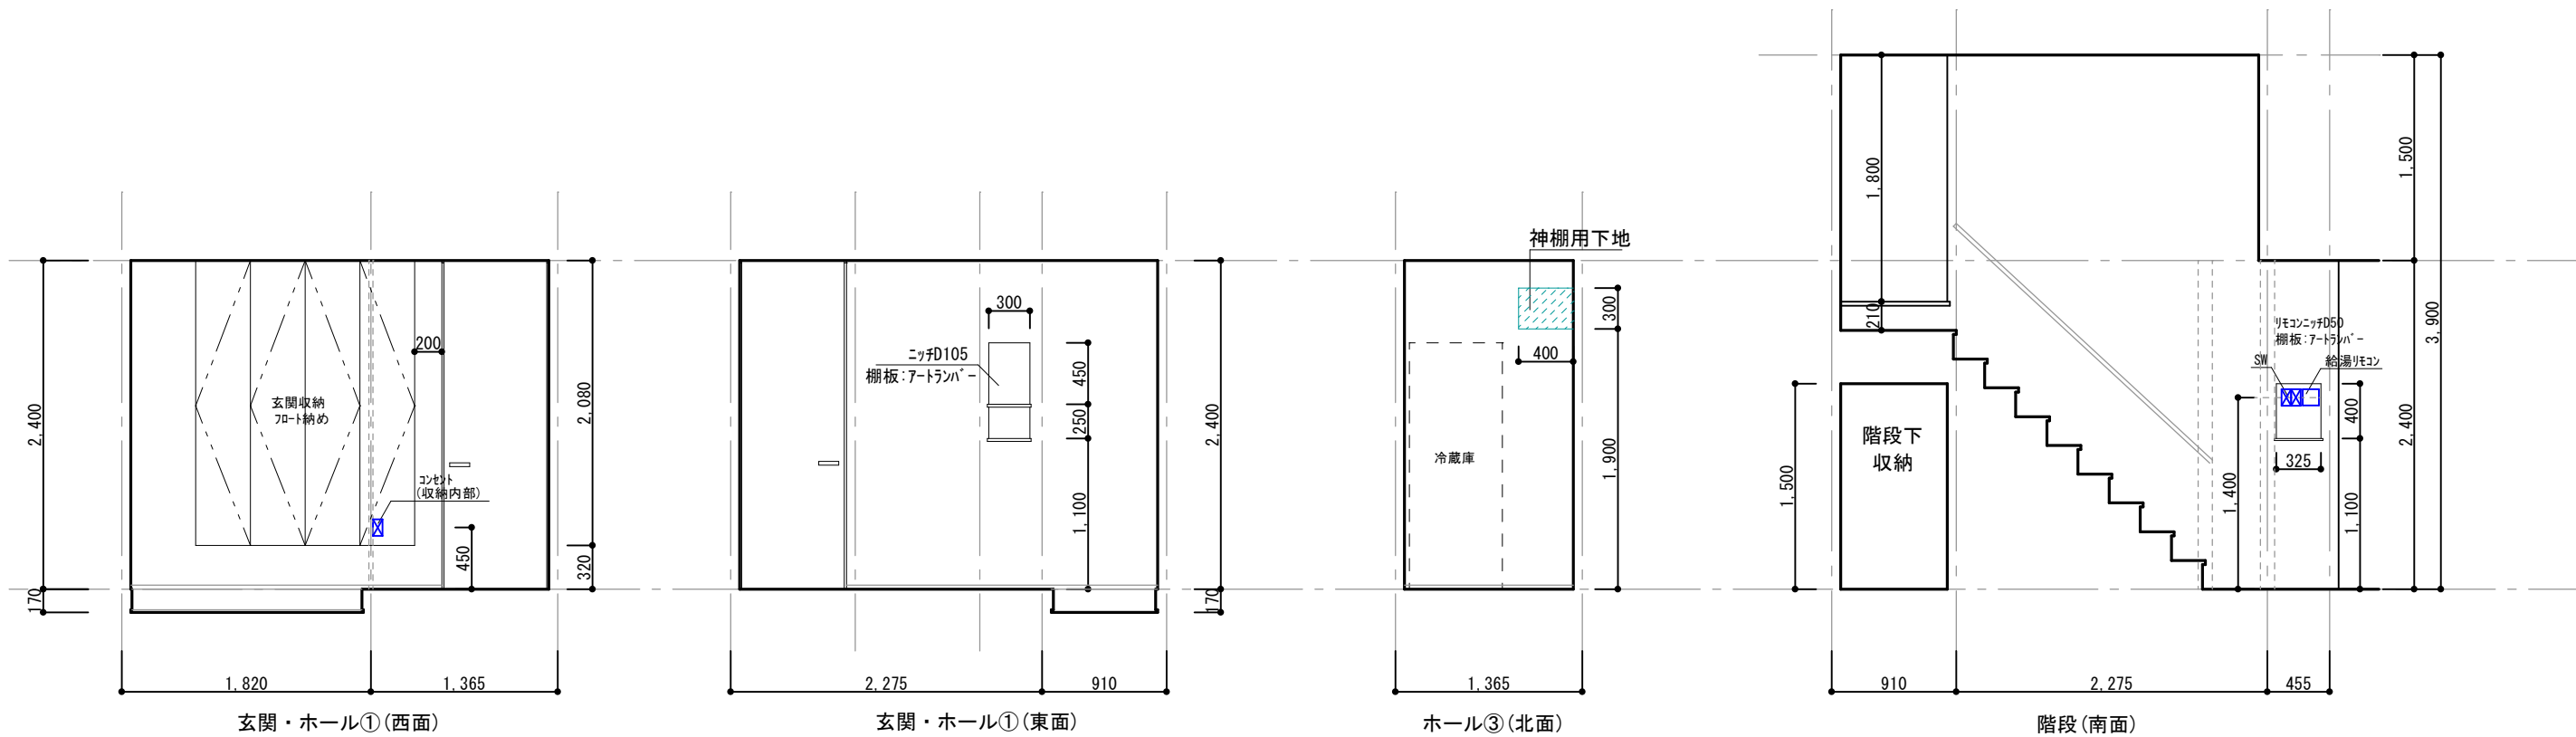

決定図

訂 正	浜 岡 一 級 総 合 設 計 事 務 所 一級建築士事務所 静岡県知事登録第 (10)2441 号 一級建築士 大臣登録第 365879 号 西原利昌	LIFEFUND PG HOUSE	株式会社 LIFEFUND InDesign office 一級建築士事務所 事務所登録 (2) 第7595号 一級建築士登録 第179770号 鈴木 達男 〒432-8023 静岡県浜松市中央区鴨江3丁目70番23号	年 月 日	件 名		設計	IC	工事	図 番
				2026. 3. 15	山村和孝様邸 新築工事		角谷		青島	6-1
				縮 尺	図 名					
				1/50	展開図-1					

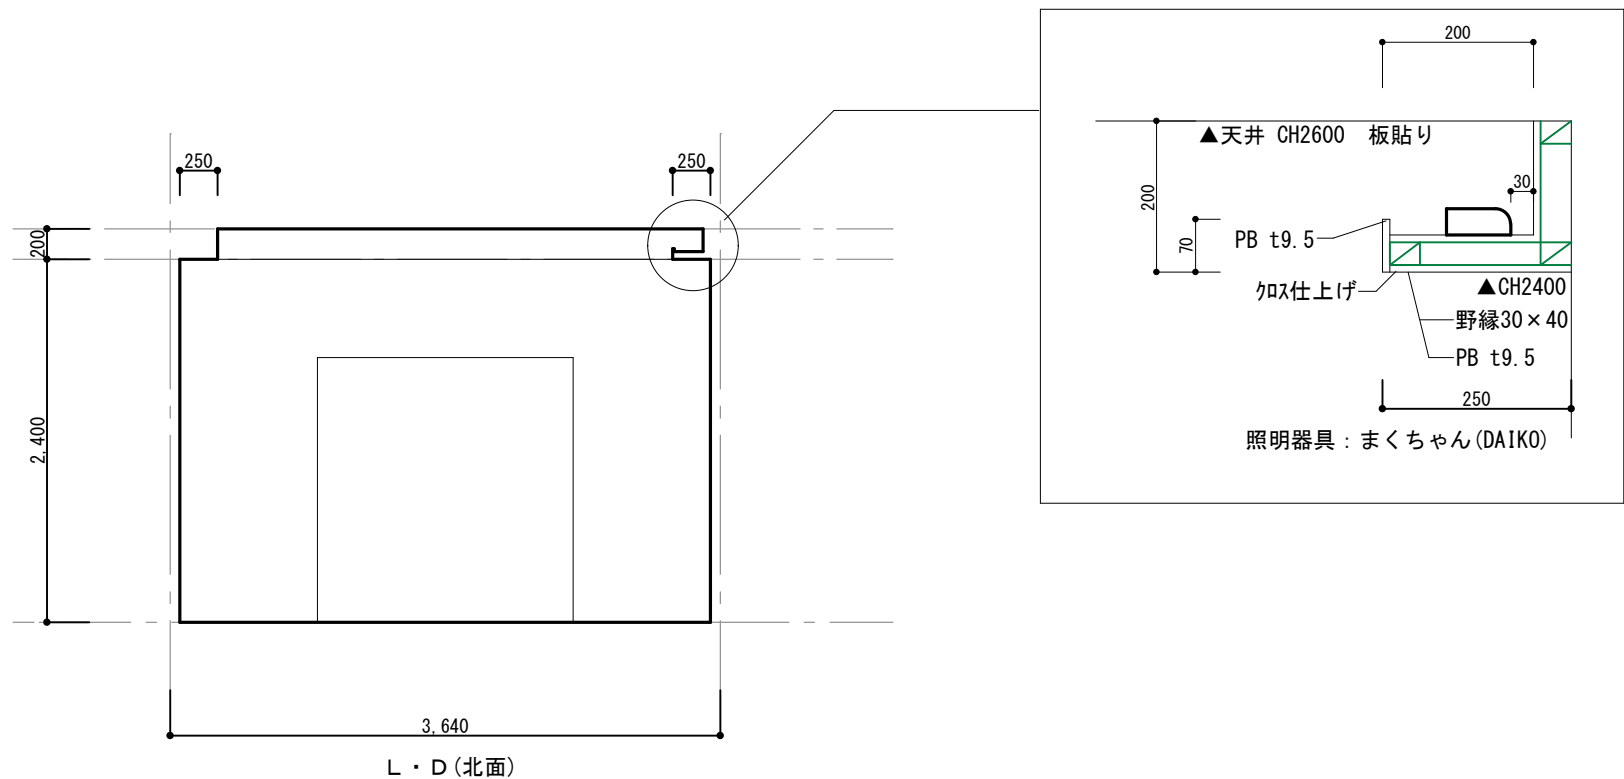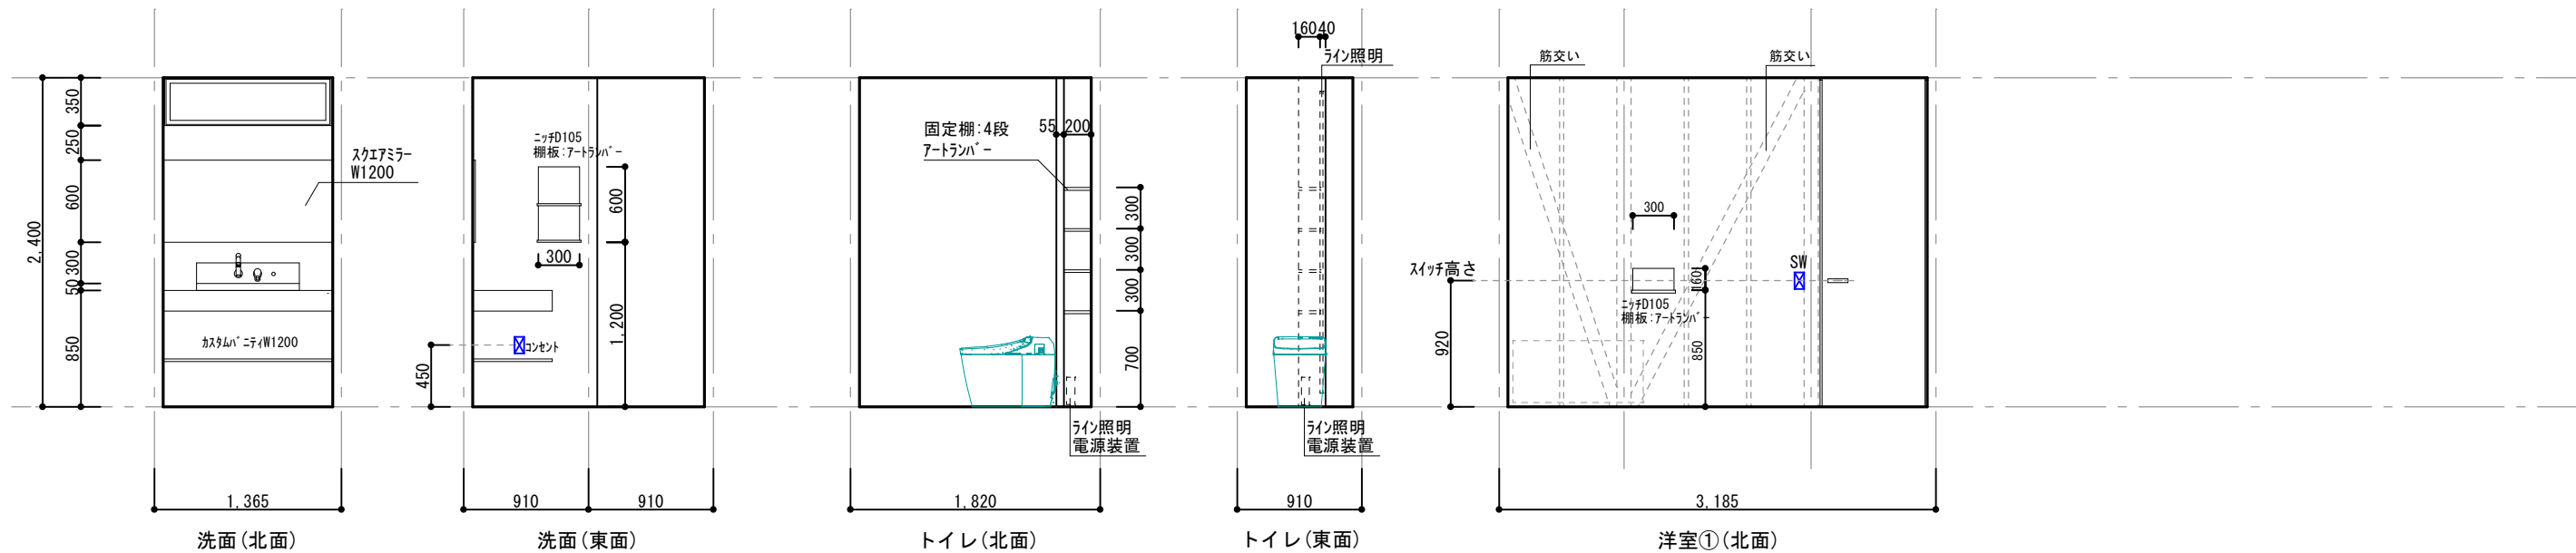

決定図

訂 正	浜 岡 一 級 総 合 設 計 事 務 所 一級建築士事務所 静岡県知事登録第 (10)2441 号 一級建築士 大臣登録第 365879 号 西原利昌	LIFEFUND PG HOUSE	株式会社 LIFEFUND InDesign office 一級建築士事務所 事務所登録 (2) 第7595号 一級建築士登録 第179770号 鈴木 達男 〒432-8023 静岡県浜松市中央区鴨江3丁目70番23号	年 月 日 2026. 3. 15	件 名 山村和孝様邸 新築工事		設計	IC	工事	図 番
				縮 尺 1/50	図 名 展開図-2		角谷		青島	6-2

G2

壁付付		住宅用火災報知器	数量
H 熱感知	熱感知器	電池式(单独型)	
		露出型	
壁付付		住宅用火災報知器	数量
S 煙感知	煙感知器	電池式(单独型)	4
		露出型	

- ※ 煙感知器は壁・梁より600mm以上離す
壁に取付ける場合、
天井から150mm以上500mm以内離す
換気扇・エアコン吹出口から1500mm以上離す
- ※ 全室LED照明とする。
- ※ 標準天井高さ2,400
- ※ 特記無きガラスは型ガラス
- ※ 全室LED照明とし、居室においては調光
制御、非居室においては人感センサーを
採用する。


* 凡例

- ☒ 管柱 (105×105)
- ◀▶ K&Tパイプ (3.30倍 FRM-0641)
- ◀▶ 片筋違い (2.00倍 45×90)
(例 左:柱脚 右:柱頭)
- ◀▶ たすき掛筋違い (4.00倍 45×90)
- 構造用合板 (2.70倍)
(t=9 タイガ EXNパイプ)
- ◀▶ 床点検口
- ◀▶ 天井点検口
- ⊕ 換気扇
- ⊕ 熱交換換気扇VLR-70


アドバンスシリーズ		
スマートデザイン (外部)		
凡例		
①	コンセント	1ヶ所
②	コンセント	2ヶ所
③	コンセント	3ヶ所
①ET	コンセント1ヶ所接地ターミナル付	
②ET	コンセント2ヶ所接地ターミナル付	
WP	コンセント	防水型
⊕	エアコン用コンセント	
⊕	200V用コンセント	
WP	防雨入線プレート	
スイッチ		
●	3	3路スイッチ
●	4	4路スイッチ
⊕	直結電源	
⊕	テレビ取出口	
TEL	電話取出口 (テレホンガイド)	
LAN	LAN取出口 (テレホンガイド)	
⊕	壁照明	
⊕	リモコン (給湯関係・ルフロ)	
⊕	メーター	
⊕	分電盤	
⊕	チャイム	

- ※ACコンセント天井付け
- ※TVアンテナ工事
- ※スイッチはFL+1100、コンセントはFL+200

決定図

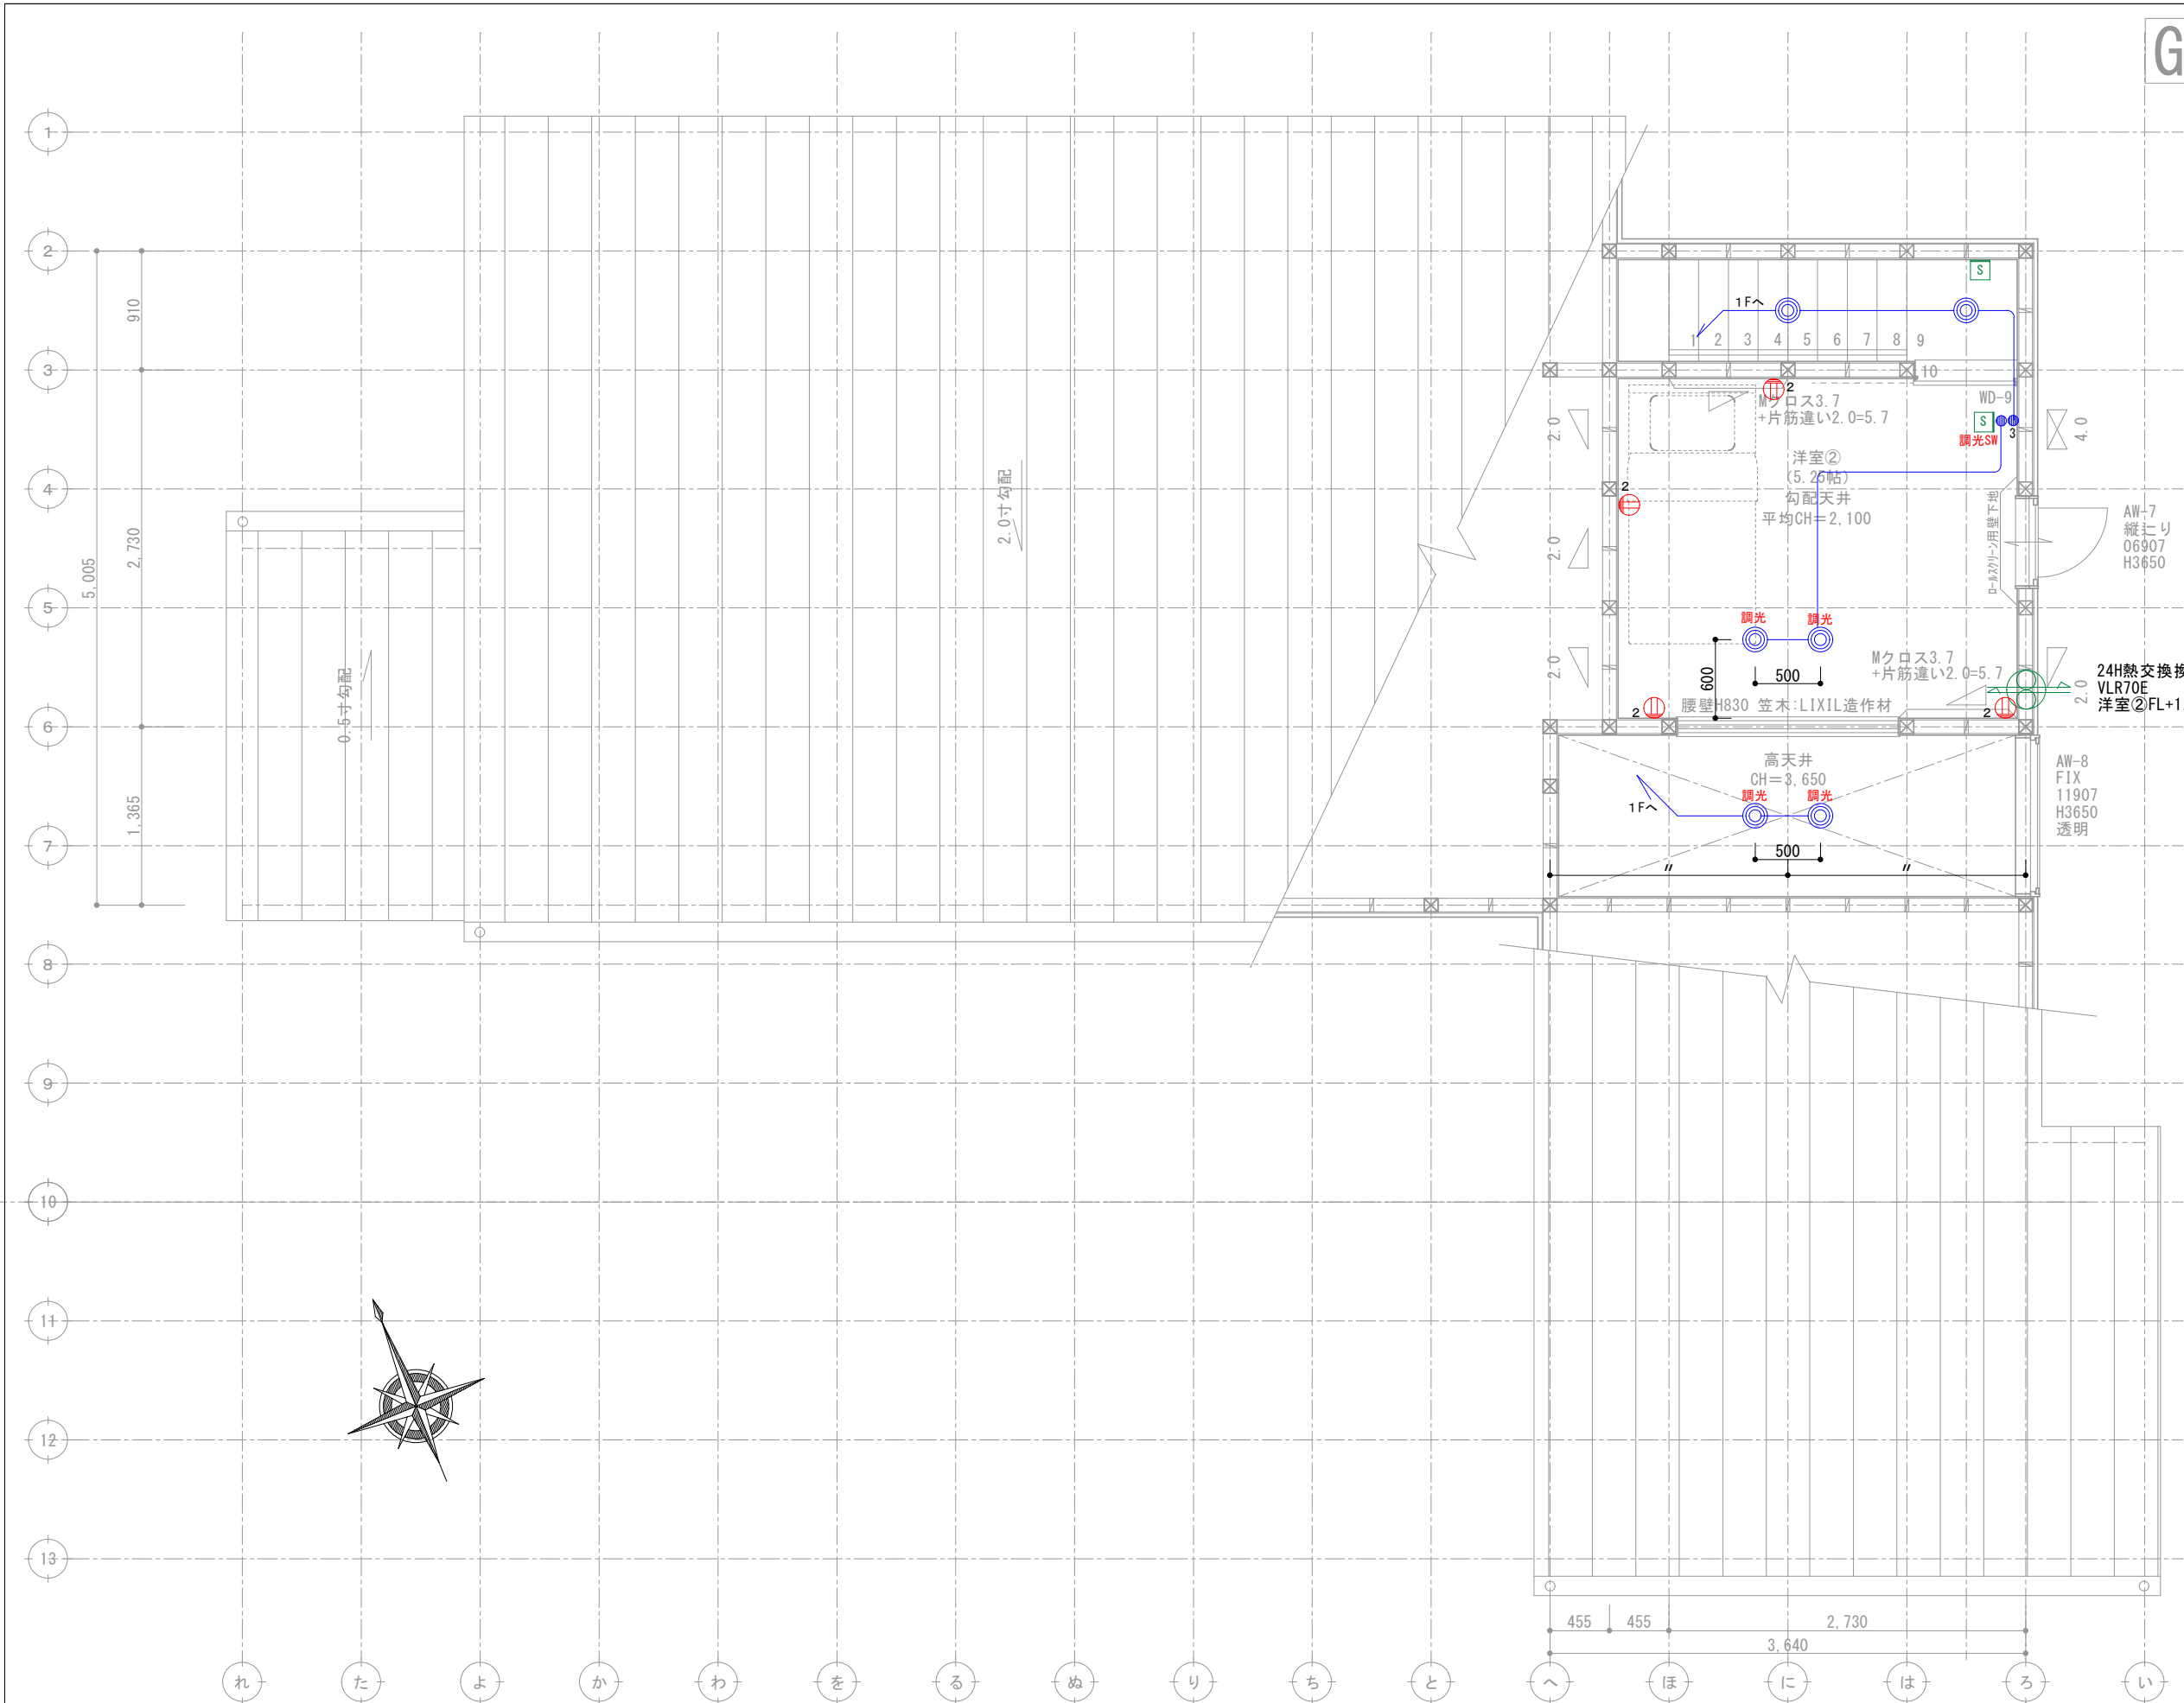

訂 正	浜 岡 一 級 総 合 設 計 事 務 所 一級建築士事務所 静岡県知事登録第 (10)2441 号 一級建築士 大臣登録第 365879 号 西原利昌		株式会社 LIFEFUND InDesign office 一級建築士事務所 事務所登録 (2)第7595号 一級建築士登録 第179770号 鈴木 達男 〒432-8023 静岡県浜松市中央区鴨江3丁目70番23号	年 月 日	件 名		設計	IC	工事	図 番
				2026. 3. 15	山村和孝様邸 新築工事					
				縮 尺	図 名					
				1/50	2階電気配線図		角谷		青島	7-2

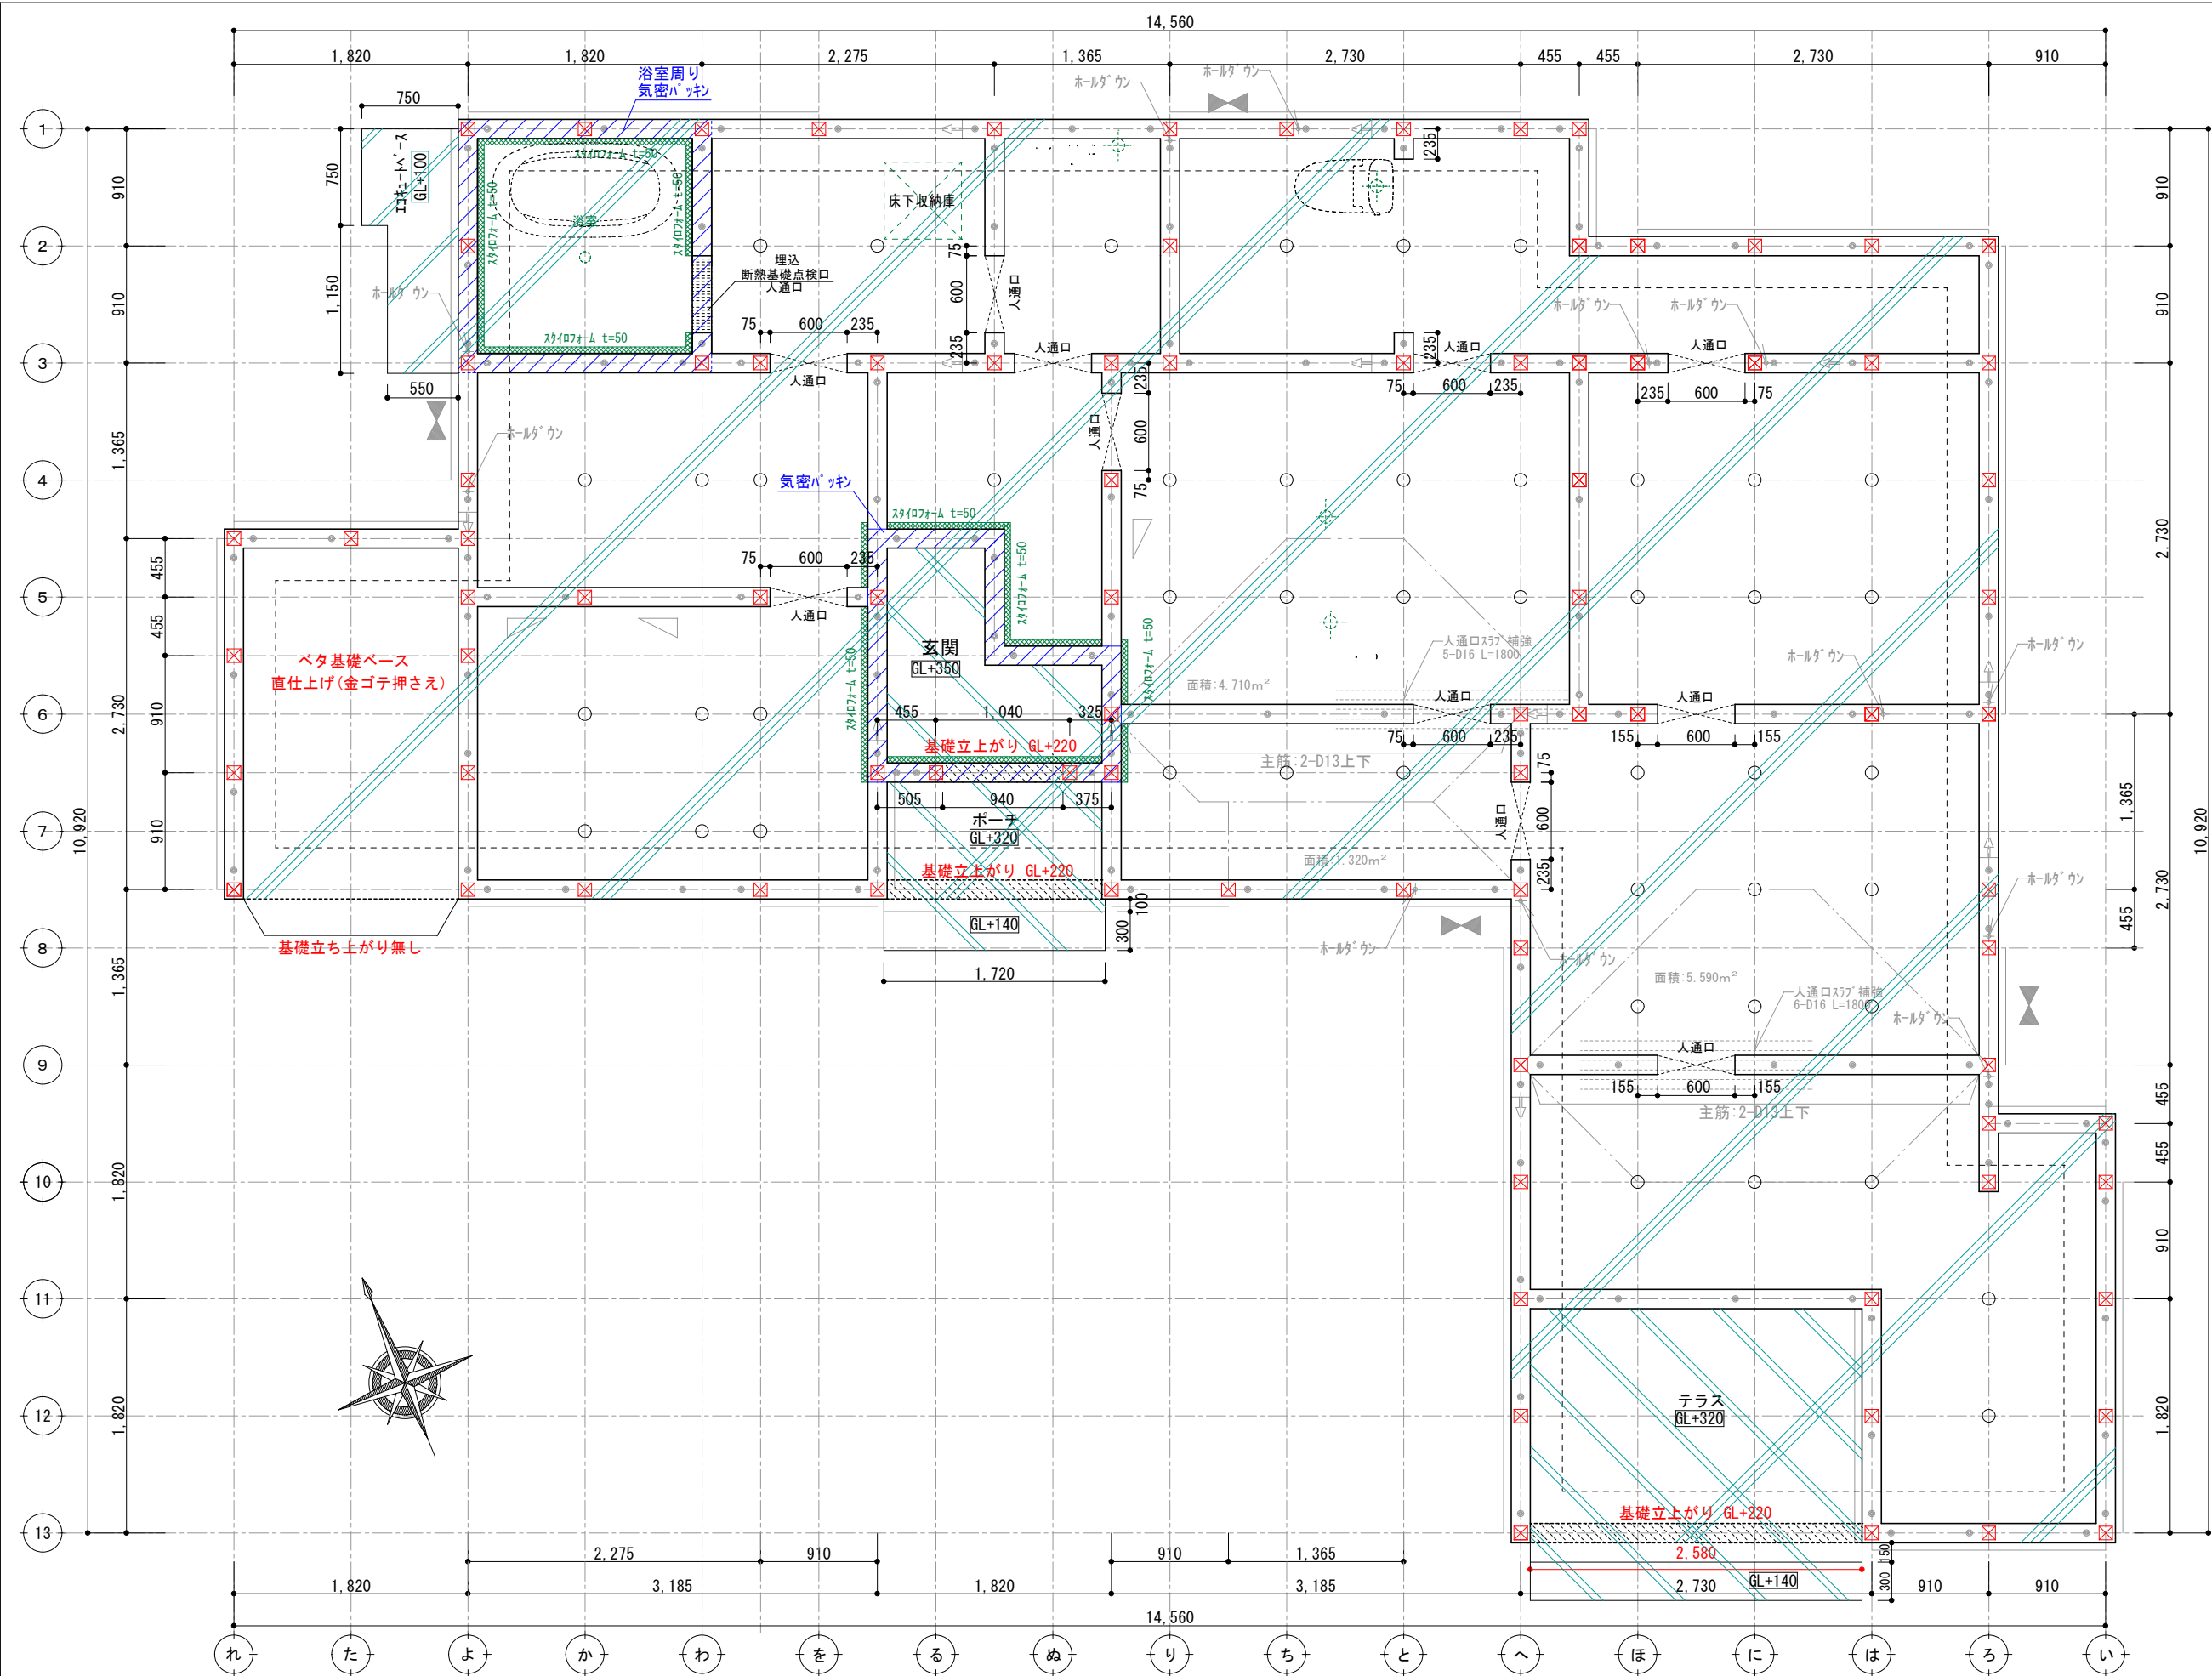

構造体ベ-スコンクリート t=150

後打ち土間コン

アンカーボルトの配置
土台切れの箇所より150mm
土台の継手及び仕口の端部より150mm
耐力壁の端部、筋交いの脚部より150mm
1.82m以下の間隔
250mm以上埋込み
基礎天端より120mm

筋かい凡例
柱脚 柱頭 片筋かい 片筋かい
たすき掛け筋かい
構造用パネル









アンカーボルトM16 外周 内部
高さ：基礎天より400mm
ホルダウアンカーボルト配置

アンカーボルトM12
高さ：基礎天より120mm
アンカーボルト配置

凡例
通し柱 (105*105) 管柱 (105*105)
アンカーボルトM12 L=400
ホルダウアンカーボルトM16 L=800
柱芯より90mm 280mm以上埋め込み
(カナイフリストアンカーボルトM16)
鋼製束
土台ジョイント
ベースコンクリート (t=150)
後打ちコンクリート

基礎伏図について特記なき場合に限り下記による。
1. コンクリート：呼び強度 21N/mm2
2. 鉄筋：SD295A
3. 設計地耐力：fe=20kN/m2
地耐力計測後、不足の場合は相当の改良を行い、満たすものとする。
4. 基礎の位置は、芯振分けとする。
5. 玄関・S/C・UB周囲の基礎天端は気密パッキン施工 (網掛け部) とし、その他の基礎天端は基礎パッキン施工とする。
6. 設備配管の屋内への取り入れは基礎立上り部のスリーブによる。

決定図

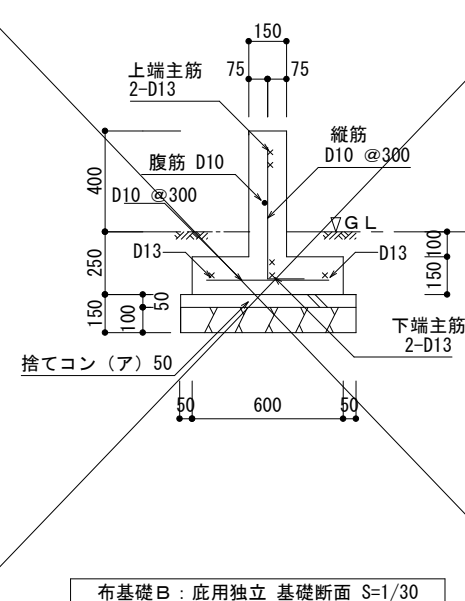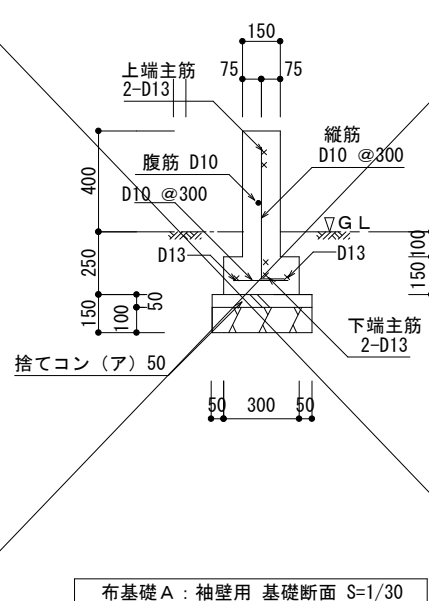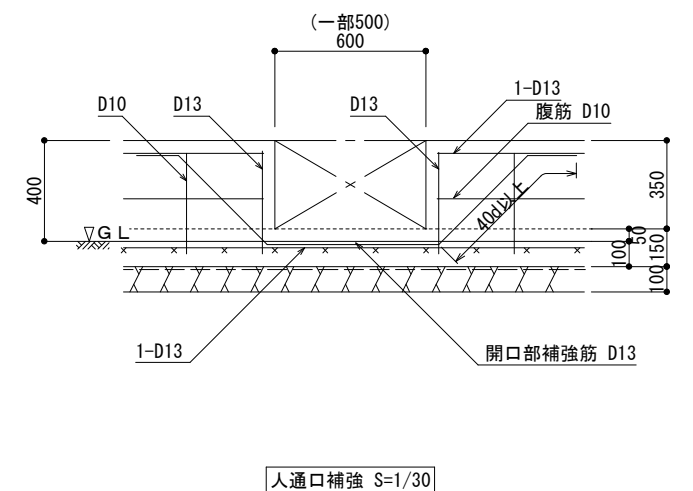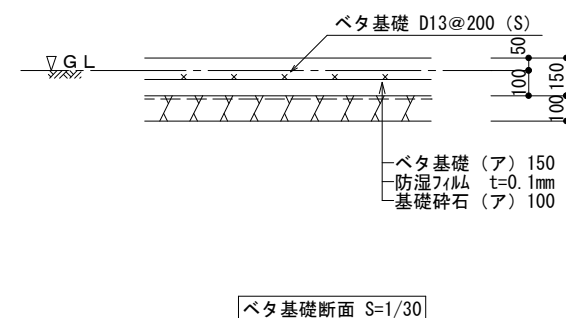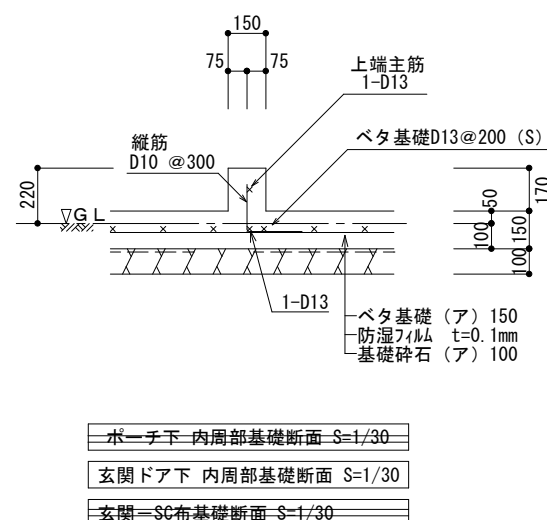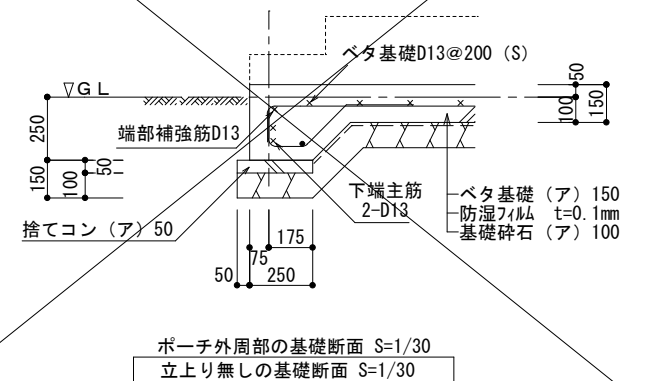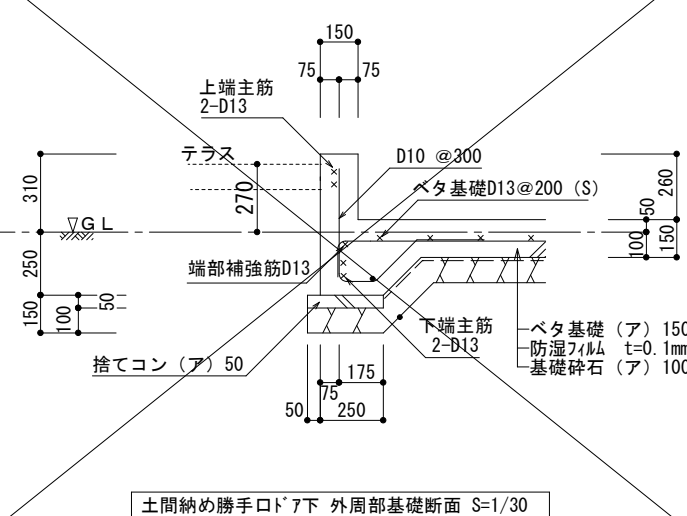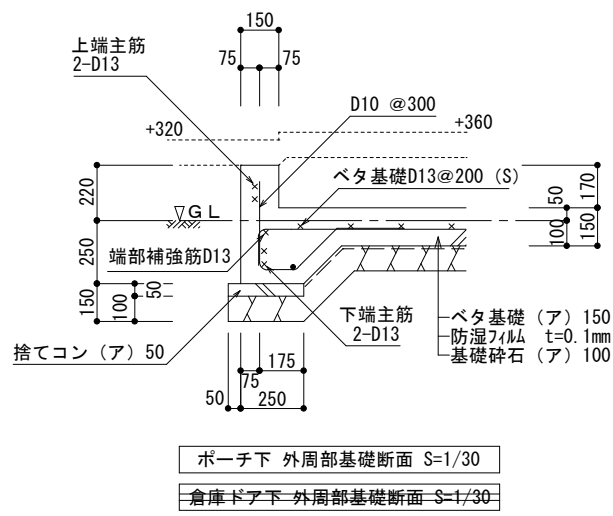


基礎の寸法 及び 配筋の検証方法	基礎立上り 配筋は、 (財) 日本住宅・ 木材技術 センター発行のスパン表 (増補版) による。 ベタ基礎スラブ配筋は、 まもりすまい保険設計施工 基準 同解説のベタ基礎配筋表 による。具体的な寸法・ 配 筋は基礎詳細図参照。
---------------------------------	--

鉄筋断面表記


- ・ D10を示す。
- × ・ D13を示す。

※使用しない断面は×を記入。

決定図

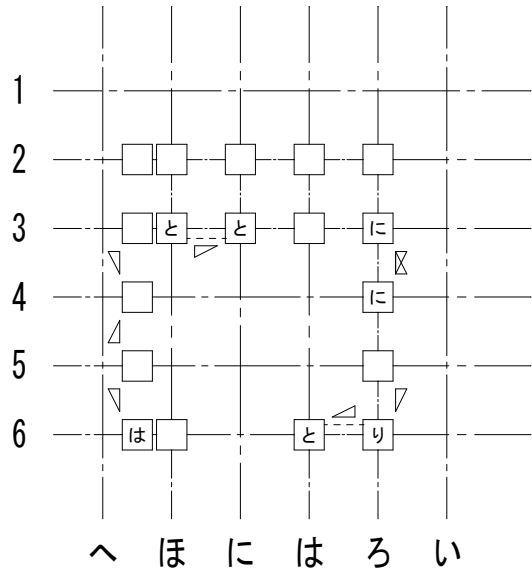

2階柱壁伏図

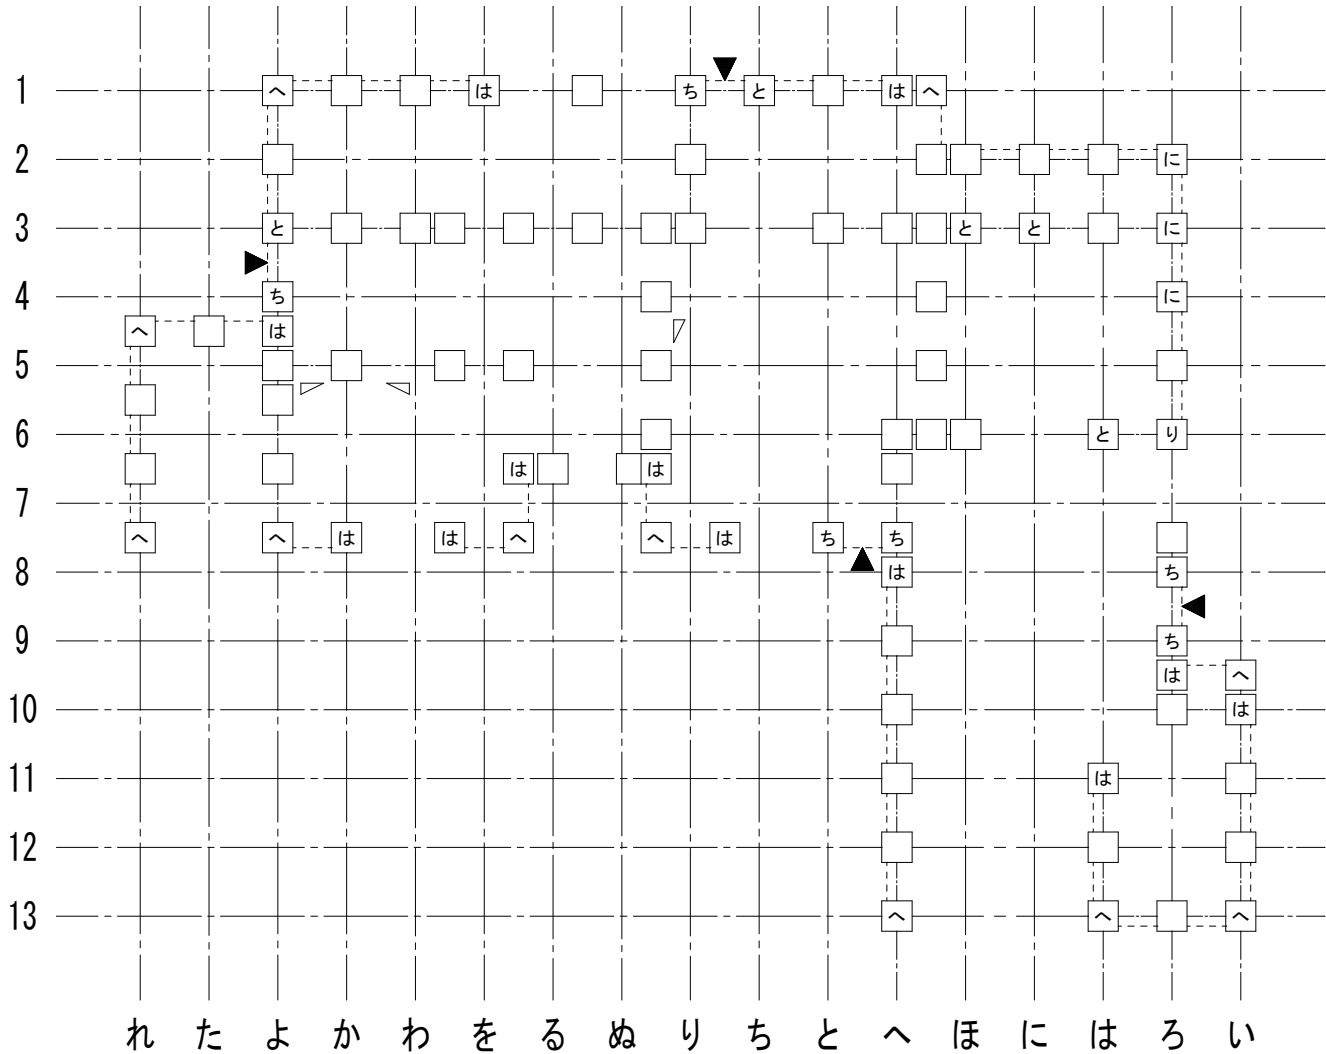

1階柱壁伏図

接合部凡例

*接合部凡例はユーザ設定されたものです。

記号	仕様（カナイ金物）	N	倍率
SBCP	スリムビルドコーナー75, チビクリCK (化粧柱の場合)	0.00	1.00
SBCP	スリムビルドコーナー75, チビクリCK (化粧柱の場合)	0.65	1.00
SBCP	は スリムビルドコーナー75	1.00	1.00
ARCG	に アレントコーナー合板用	1.40	2.20
ARCG	ほ アレントコーナー合板用	1.60	2.20
ARCG	へ アレントコーナー合板用	1.80	2.20
HD15	と ブレイブホールダウン B-HD15	2.80	3.60
HD20	ち ブレイブホールダウン B-HD20	3.70	4.70
HD25	り ブレイブホールダウン B-HD25	4.70	4.80
HD30	ぬ ブレイブホールダウン B-HD30	5.60	7.20
J1	る 腰掛け蟻若しくは大入れ蟻掛け+羽子板*ルト、短冊金物		1.90
J2	を 腰掛け蟻若しくは大入れ蟻掛け+羽子板*ルト、短冊金物×2		3.00

※表示なき金物は「は」とする。

接合部凡例

*接合部凡例はユーザ設定されたものです。

記号	仕様（タナカ金物）	N	倍率
FCP	フックコーナー, チビクリCK (化粧柱の場合)	0.00	1.00
FCP	フックコーナー, チビクリCK (化粧柱の場合)	0.65	1.00
FCP	は フックコーナー	1.00	1.00
CCP	に シナコーナー	1.40	2.20
CCP	ほ シナコーナー	1.60	2.20
CCP	へ シナコーナー	1.80	2.20
HD15	と ビス止めホールダウンU HD15	2.80	3.60
HD20	ち ビス止めホールダウンU HD20	3.70	4.70
HD25	り ビス止めホールダウンU HD25	4.70	4.80
HD30	ぬ ビス止めホールダウンU HD15×2 (HD35)	5.60	7.20
J1	る 腰掛け蟻若しくは大入れ蟻掛け+羽子板*ルト、短冊金物		1.90
J2	を 腰掛け蟻若しくは大入れ蟻掛け+羽子板*ルト、短冊金物×2		3.00

※表示なき金物は「は」とする。

筋かいの種類に応じた筋かいの端部の接合部の仕様		
	筋かいの種類	接合部の仕様（構造方法）
イ	鉄筋φ9	柱又は横架材を貫通し、三角座金を介してナット締め、又は鋼板添え板を用い鋼板を柱及び横架材にCN90, 8本平打ち
ロ	筋かい:15×90	柱・横架材を欠き込み、柱・横架材双方に対してN65, 5本平打ち
ハ	筋かい:30×90	鋼板添え板t=1.6mmを筋かいに対してボルトφ12及びCN65, 3本平打ち、柱に対してCN65, 3本平打ち、横架材に対してCN65, 4本平打ち。筋かいプレートBP同等品
ニ	筋かい:45×90	鋼板添え板t=2.3mmを筋かいに対してボルトφ12及びスクリュー釘φ4.5L50, 7本平打ち、柱及び横架材に対してスクリュー釘φ4.5L50, 5本平打ち。筋かいプレートBP-2同等品
ホ	筋かい:90×90	柱又は横架材にボルトφ12mmを用いて一面剪断接合

胴差と通し柱の接合部の仕様		
	胴差と通し柱の条件	仕口
T1	通し柱の片側に胴差が来る場合	胴差を柱にかたぎ大入れ短ほぞ差しの上、羽子板ボルト、かね折り金物又は同等以上の仕口
T2	通し柱の両側に胴差が来る場合	胴差を柱にかたぎ大入れ短ほぞ差しの上、短冊金物又は、同等以上の仕口で胴差相互を緊結
T3	通し柱と胴差の接合部の近くに90×90以上の筋かいが来る場合（通し柱が建物の出隅にあるか、筋かい壁が外壁と直交して接する場合）	胴差を通し柱に、15KN用引き寄せ金物を水平に用いて緊結

決定図