
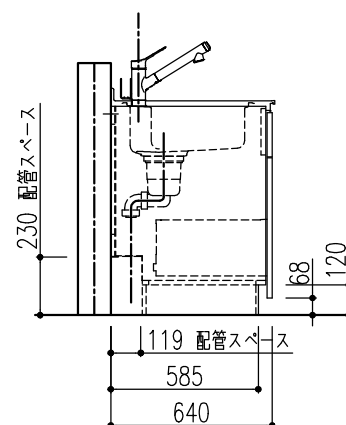
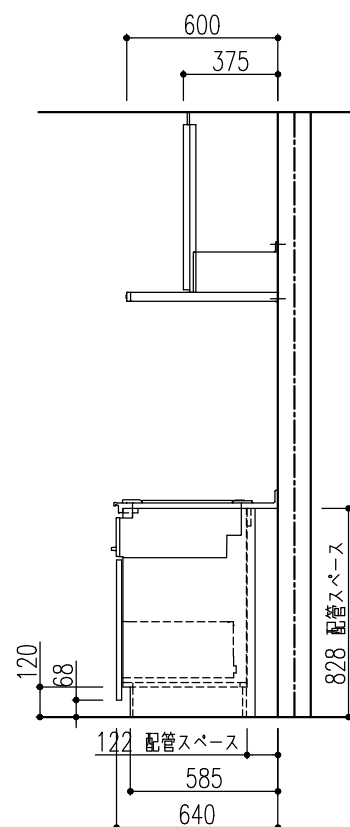
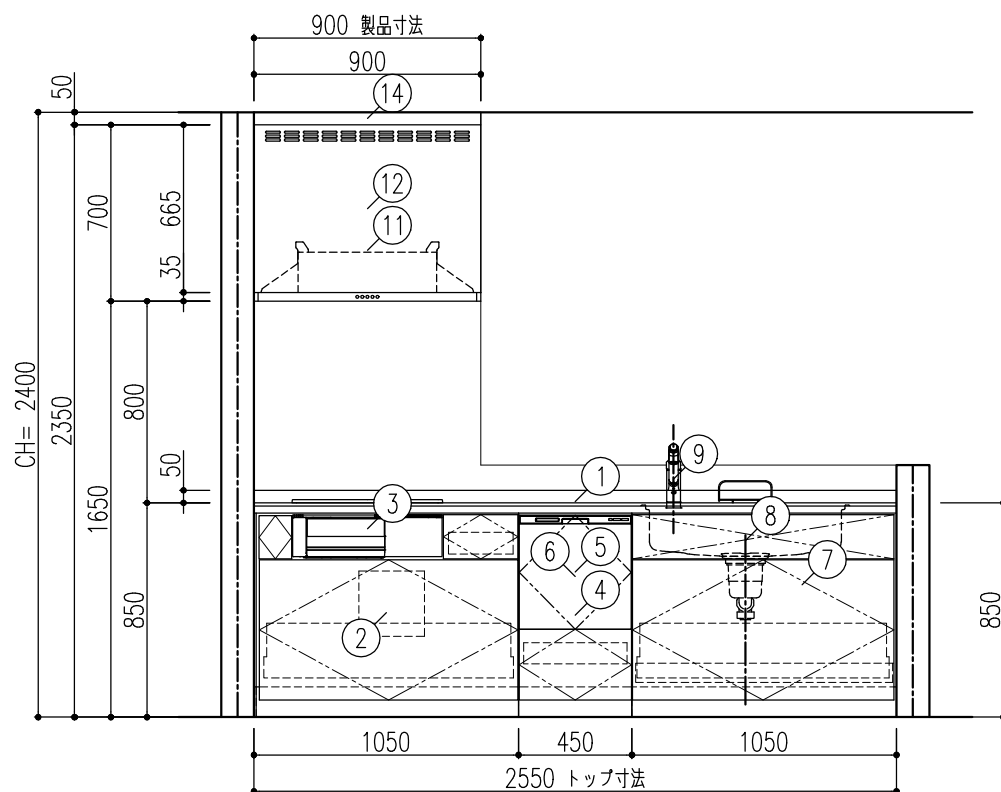
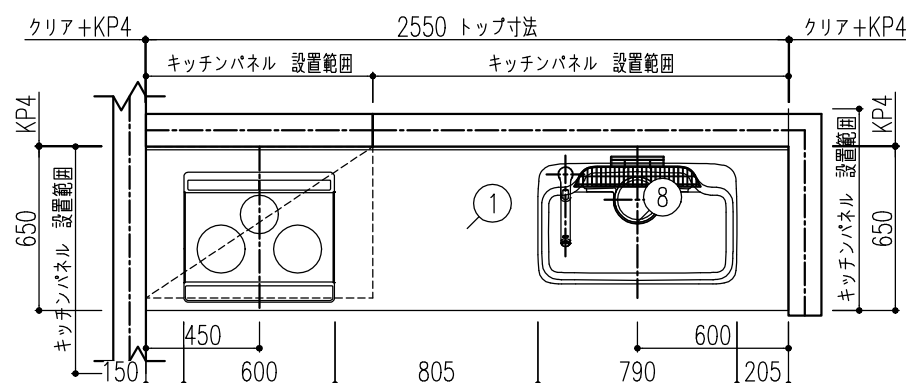
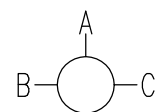


[illegible]

【ご注意】

- 壁面仕上材（キッチンパネル・タイルなど）の貼付下端位置が変わります。〔機能図参照〕
- 記載のキャビネット寸法は扉前面までの呼び寸法です。キャビネット本体の寸法・扉厚み等は商品ガイドの巻末資料をご確認ください。
- 記載のワークトップ、カウンター、エンドパネル、サイドパネルの寸法は呼び寸法です。詳細寸法は商品ガイドの巻末資料をご確認ください。
- レンジフード電源プラグ仕様：3芯電源プラグ（アース工事が必要です。）

特記事項 扉色 VK5:グレージュスタッコ 取手 【M】スリム取手（ブラック） ワークトップカラー 【DW】ソルティホワイト	物件名	前嶋実香 様邸	案件No.	図面名	担当	図面	図番 : 株式会社 LIXIL
			A2506DDD0EP4LC	レイアウト図	栗野 友仁		
	仕様	ES21	見積No.	縮尺	日付		
			M25067956064-003-2	1/30	2025.07.25		

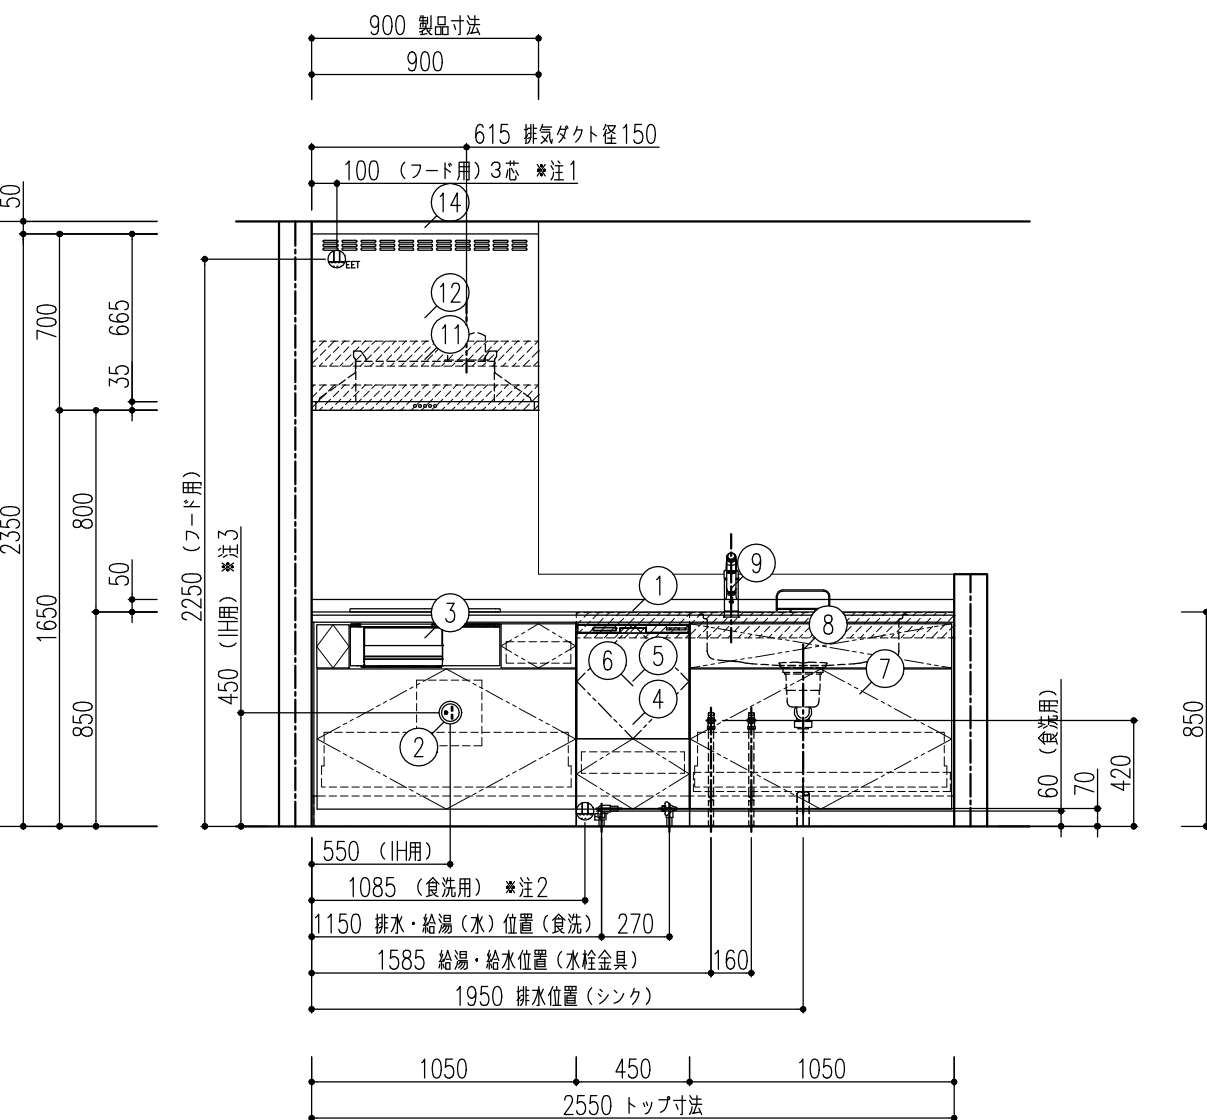

注1) 125V・15A 2極接地極付アースターミナル付コンセント 【専用】 (フード用)

注2) 125V・15A 2極接地極付アースターミナル付コンセント 側板取付【専用】


注3) 250V・30A 2極接地極付コンセント 【専用】

【 ご注意 】


- 壁面仕上材(キッチンパネル・タイルなど)の貼付下端位置が変わります。 [機能図参照]
- 記載のキャビネット寸法は扉前面での呼び寸法です。キャビネット本体の寸法・扉厚等は商品ガイドの巻末資料をご確認ください。
- 記載のワークトップ、カウンター、エンドパネル、サイドパネルの寸法は呼び寸法です。詳細寸法は商品ガイドの巻末資料をご確認ください。
- 電気・ガス・給排水・換気等は法令・規定に従って有資格者が行ってください。
- 水道工事は排水配管工事となります。
- 取付・設置に際し、各製品の取付・設置説明書や図面の機能図を必ずお読み下さい。
- 内線規程上、各機器のプラグ仕様に関わらず建築側には接地極付コンセントを推奨しています。
- 壁付けでレンジフード上天井フィルターを設置する場合は、横壁に下地が必要となります。下地位置は、機能図を参照願います。
- レンジフード電源プラグ仕様：3芯電源プラグ(アース工事が必要です。)
- 食器洗い乾燥機配管は、給水接続か給湯接続かお客様に確認したうえで施工願います。
- 食洗機内配管の詳細については必ず別添の機能図をご確認ください。

A3 20250725NB1H-0

B面

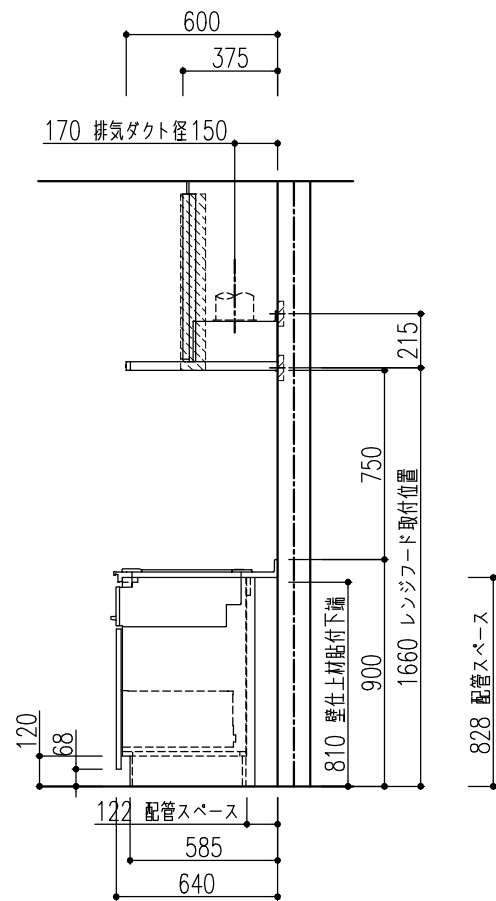

C面

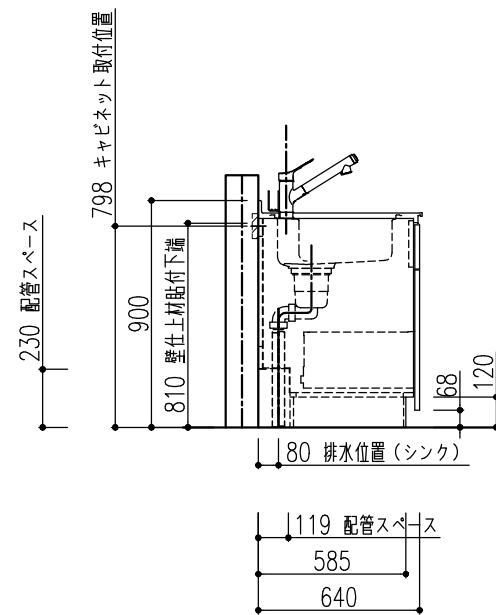

特記事項 扉色 VK5:グレージュスタック 取手 [M]スリム取手 (ブラック) ワークトップカラー 【DW】 ソルティホワイト	物件名	前嶋実香 様邸	案件No.	図面名	担当	図面	図番
			A2506DDD0EP4LC	納まり図	栗野 友仁		株式会社 LIXIL
	仕様	ES21	見積No.	縮尺	日付		
			M25067956064-003-2	1/30	2025.07.25		

■壁面仕上材（キッチンパネル、タイルなど）取付注意事項〔貼付下端位置〕

●キッチンパネルの貼付下端位置

キッチンパネルの貼付下端位置にご注意ください。

キッチンパネル

壁

810mm

(キッチンパネル貼付下端位置)

ワークトップ高さ：850mm以外の場合は、
下表を参照してください。

ワークトップ高さ	キッチンパネル貼付下端位置
900	860
875	835
825	785
800	760

●上表はキッチンパネルの場合です。ステンレスパネルの場合は、キッチンパネルの「取付・設置説明書」を参照してください。

《ワークトップ高さ：850mmの場合》

■壁面仕上材（キッチンパネル）取付注意事項〔貼付向き〕

●キッチンパネルの貼付向き

キッチンパネルの貼付向きにご注意ください。

【単位：mm】

レンジフード

ウォールキャビ（開き扉）

クイックポケット
クイックパレット

850

700

880

620

850

横貼

縦貼

フロアキャビ

(ウォールキャビ高さ)

(レンジフード高さ)

(壁面寸法)

(クイックポケット・パレット用キャビ高さ)

(ワークトップ高さ)

(ワークトップ高)

《バックガード：なし、ワークトップ高さ：850mm、ウォールキャビ高さ：700mmの場合》

《キッチンパネル 貼付方向》

総高さ：2350mmの場合

キッチンパネル貼付方向	ウォールキャビ		
	開き扉	クイックポケット クイックパレット	
	H700	H600 H500	H700 (620) H600 (520)
横	縦	縦	横

【ご注意】
リシェル以外のクイックパレットは、キャビネットの背板高さがショート（－80mm）しておりませんので、『開き扉』のキッチンパネル貼付方向に合せてください。

■床の不陸に関して

7mm以下

7mm以下

床の不陸は、7mm以下に抑えるようにしてください。不陸が大きい場合は、現場責任者に床の修正を依頼してください。
※キャビネット取付時には不陸調整スペーサー等で水平になるように設置してください。

■レンジフード取付注意事項（壁面取付時）

レンジフードを取付ける場合は下地の材が厚み30mm以上、幅100mm以上、ビス固定位置が材の端部から25mm以上であることを確認してください。
また、壁強度などの詳細は「レンジフード設置説明書」を必ず事前に確認してください。

取付位置については、取付設置図を確認してください。

参考図_CLS. SER. NST. ASR. ADR. RVJ. GSR. BFRS. TARシリーズ
（※RVJ. GSRシリーズの場合はレンジフードパネルの取付下地は不要です。）

12mm以上の合板または0.8mm以上の鋼板

レンジフード取付下地

100mm

30mm以上

100mm以上

335

レンジフードパネル取付下地

【正面】

【側面】

参考図_FED. HVR. NSDシリーズ（サイドマントルタイプ）

30mm以上

100mm以上

レンジフード取付下地

【正面】

【側面】

参考図_NBHシリーズ

レンジフード取付下地

30mm以上

100mm以上

【正面】

【側面】

特記事項

扉色 VK5:グレージュスタコ

取手 [M]スリム取手（ブラック）

ワークトップカラー 【DW】ソルティホワイト

物件名

仕様

前嶋実香 様邸

ES21

案件No.

A2506DDD0EP4LC

見積No.

M25067956064-003-2

図面名

機能図

縮尺

図番

担当

栗野 友仁

日付

2025.07.25

図番

：


株式会社 LIXIL

A3


20250725NB1H-01

■天井フィラーの取付（レンジフード上部）

レンジフード横に壁がくるレイアウト時は、横壁にも取付桎が必要になります。

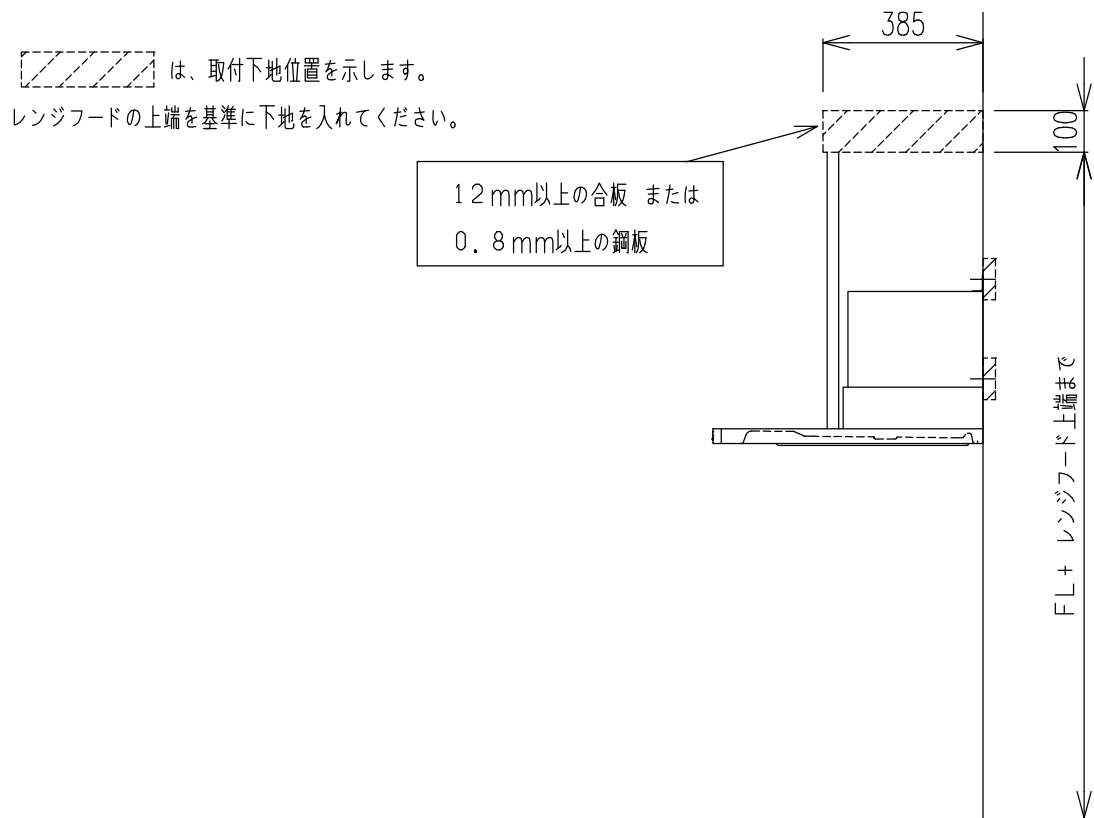

■ ASRフード

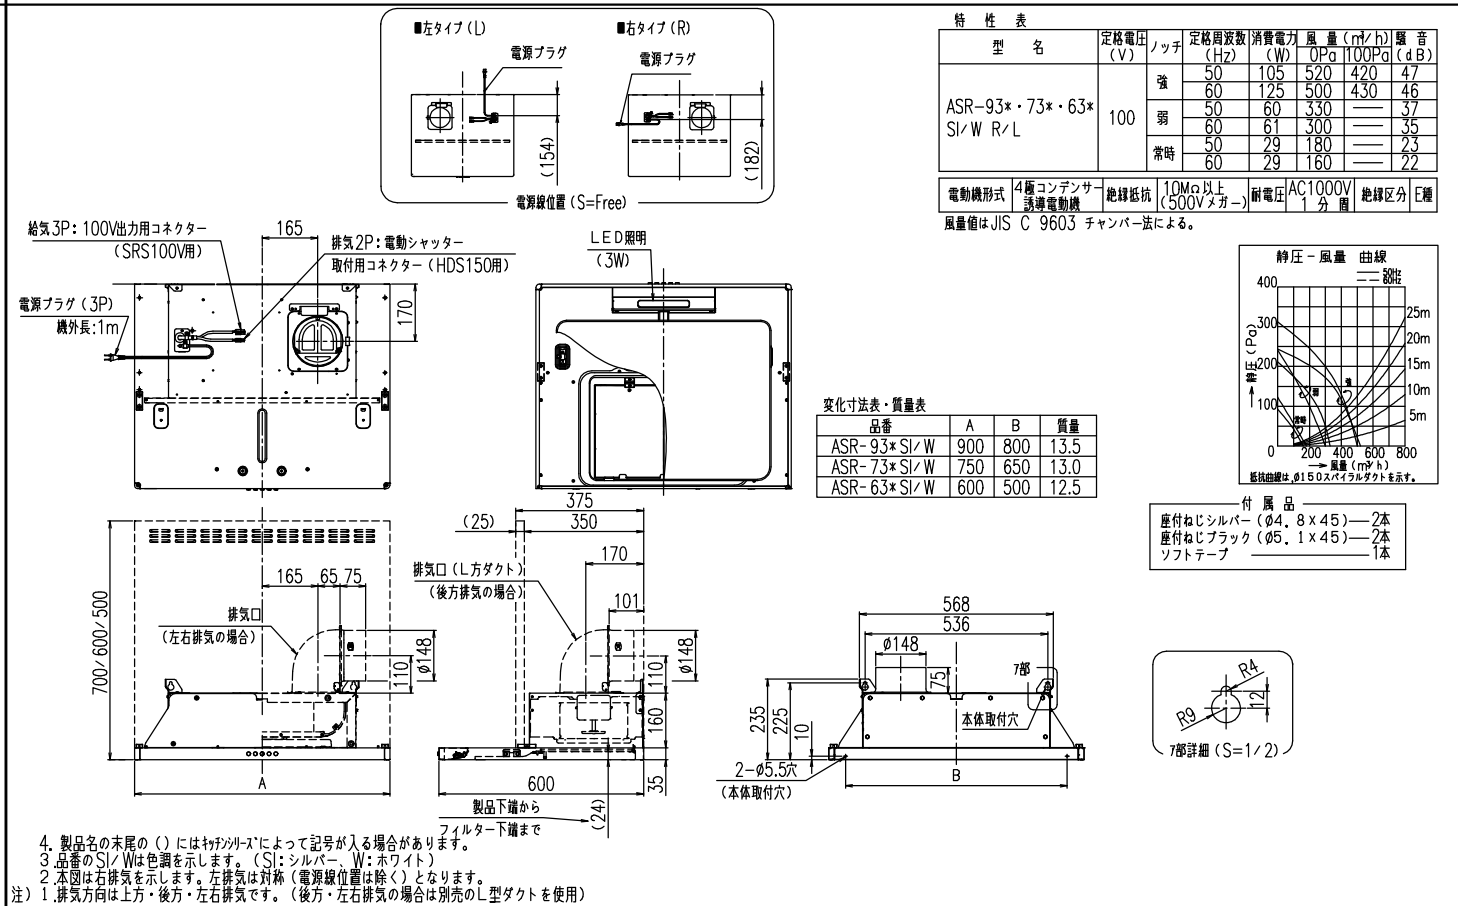


■ IHヒーター用コンセント推奨位置図 / 壁付設置の場合

※コンセントや電源プラグが、引き出しおよびIHヒーター用仕切板（オプション）に接触しないように注意してください。

※木製キャビネットの配管スペース付キャビネットを使用する場合は点検口裏の配管スペース内にコンセントを設置してください。


キッチン高さ	電源線高さ
800	400
850	450
900	500

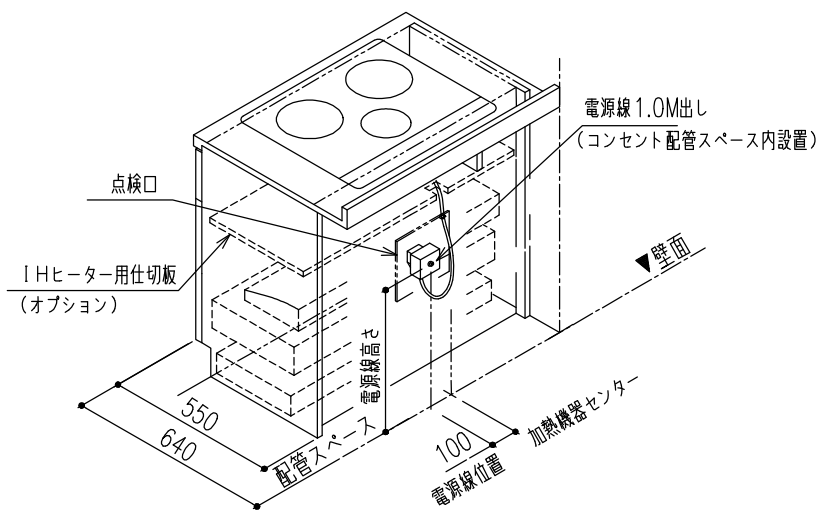

注意：引き出しおよびIHヒーター用仕切板（オプション）に接触しないように上記寸法を参照してください。

■食器洗い乾燥機内配管図 床立上げ配管例

※イラスト表記の事前配管部材は現地手配

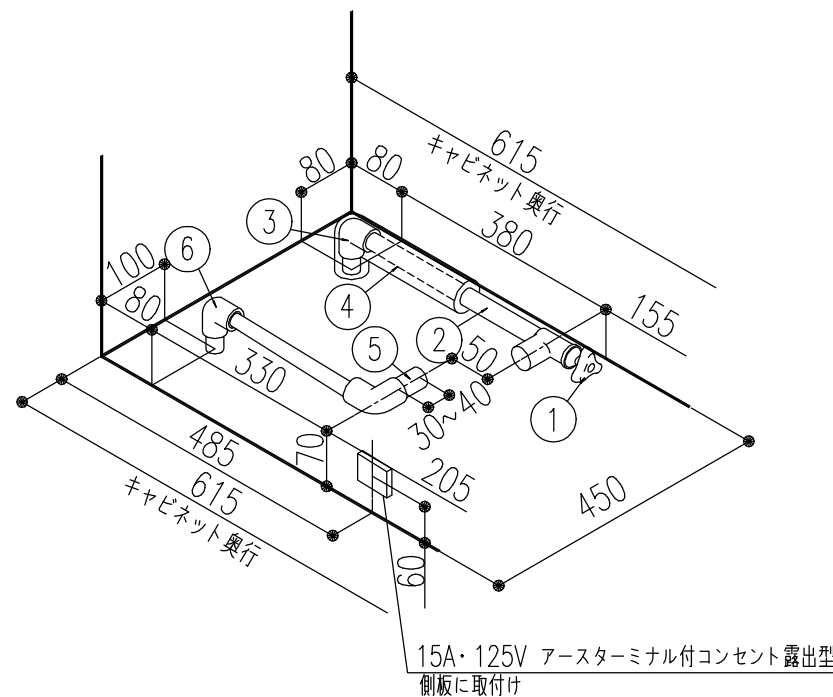

注意：配管立ち上げ位置は必ず本図の位置に立ち上げて下さい。

※給水接続か給湯接続かお客様に確認したうえで施工願います。

給水（給湯の場合は耐熱配管）

- ①アンクル型止水栓（ハンドル式・固定ゴマタイプ）

※必ず固定ゴムタイプをご使用ください。

落としゴマタイプを使用すると、水栓内でコマが移動し、ゴトゴト音を生じる恐れがあります。

- ②硬質塩化ビニルライニング鋼管（相当品）

排水（耐熱塩ビ使用のこと）

- ⑤排水パイプHT 20
- ⑥HTエルボ

※配水管先端のエルボを上向きにしないでください。


キャビネットに当たるため、排水ホース折れの原因になります。

特記事項 扉色 VK5:グレイジュスタッコ 取手 [M]スリム取手 (ブラック) ワークトップカラー 【DW】ソルティホワイト	物件名	前嶋実香 様邸	案件No.	図面名	担当	図面	図番 : 株式会社 LIXIL
			A2506DDD0EP4LC	機能図	栗野 友仁		
	仕様	ES21	見積No.	縮尺	日付		
			M25067956064-003-2		2025.07.25		

■ 止水栓図（床立上げ）

床立上げ配管

配管立ち上げ寸法は、止水栓芯までの高さを示しています。

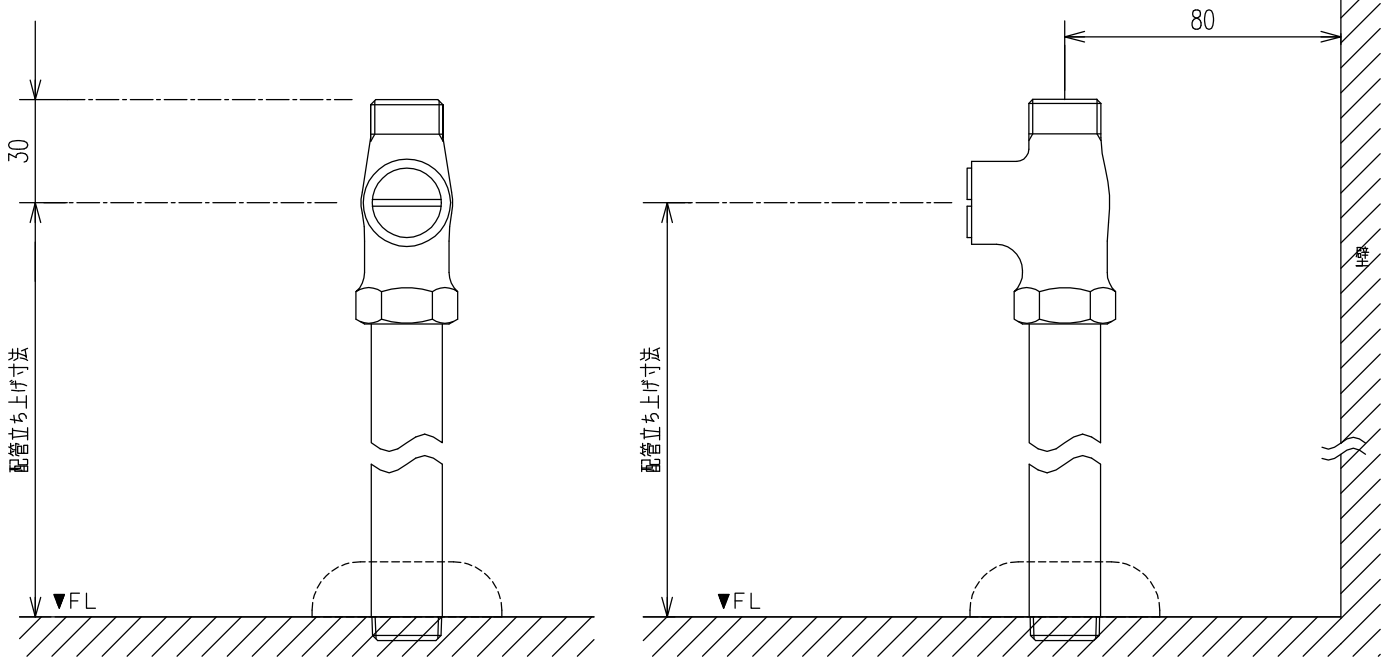

	特記事項 扉色 VK5:グレージュスタック 取手 [M]スリム取手（ブラック） ワークトップカラー 【DW】 ソルティホワイト	物件名 仕様	前嶋実香 様邸 ES 2 1	案件No.	図面名	担当	図面	図番
				A2506DDD0EP4LC	機能図	栗野 友仁		株式会社 LIXIL
				見積No.	縮尺	日付		
				M25067956064-003-2		2025.07.25		

■ キッチン取付者さま向け 動画コンテンツ ■


商品取付けの注意点を2次元コードでご視聴いただけます。

取付日より前に、是非ご確認ください。



1 ページ目

1 $\wedge^0$ — ジ

荷扱い・搬入

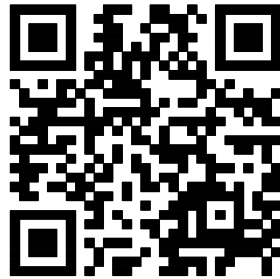

カウンター開梱搬入 「養生ツール」のご紹介

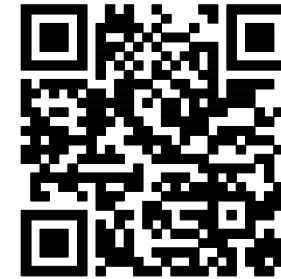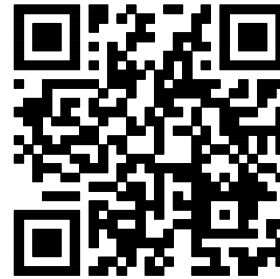


マグネット キッチンパネル 「取付・設置」ポイント




作成日：2024年03月06日

A line drawing of a kitchen unit. It features a corner cabinet configuration. On the left side, there is a built-in electric stove with four burners. To the right of the stove is a kitchen sink with a single faucet. Above the countertop, there are upper cabinets. Below the countertop, there are lower cabinets with drawers and doors. The drawing is a simple line art illustration without shading.

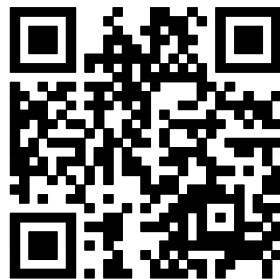

A line drawing of a kitchen unit. On the left is a sink with a single-lever water tap. To the right of the sink is a cooktop with four burners. Above the cooktop is a glass splashback and a square range hood. Below the countertop are three cabinet doors. A line points from the text 'Hot water tap' to the hot water tap on the right side of the sink.





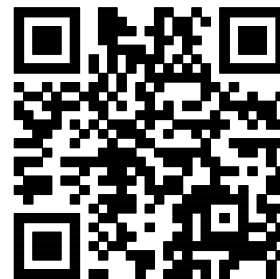


作成日：2024年02月07日

A3 20250725NB1H-0

■ キッチン取付者さま向け 動画コンテンツ ■

商品取付けの注意点を2次元コードでご視聴いただけます。
取付日より前に、是非ご確認ください。

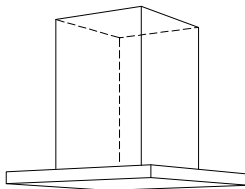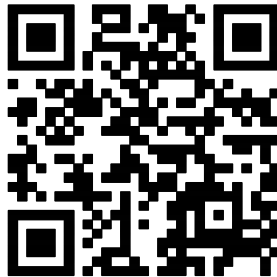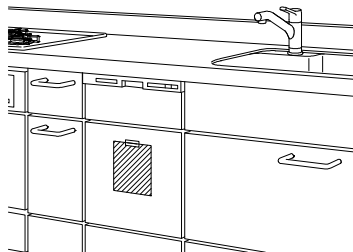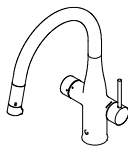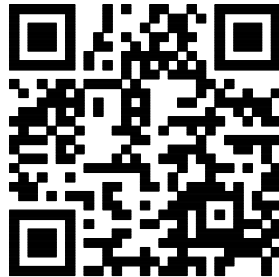センターフード型レンジフード (天吊りフード)  作成日：2024年06月03日 		IH加熱機器関連 IH加熱機器 仕切り板 作成日：2024年02月07日 		食器洗い乾燥機  作成日：2024年02月07日 		ミネラル浄水栓 Greentap  作成日：2024年06月03日 				
	特記事項 扉色 VK5:グレージュスタック 取手 [M]スリム取手 (ブラック) ワークトップカラー 【DW】ソルティホワイト	物件名	前嶋実香 様邸		案件No.		図面名	担当	図面	図番
					A2506DDD0EP4LC		機能図	栗野 友仁		株式会社 LIXIL
					見積No.		縮尺	日付		
					M25067956064-003-2			2025.07.25		
仕様		ES21								