

G2

壁付け 住宅用火災報知器			数量
H	熱感知器	電池式(単独型)	3
	露出型		
壁付け 住宅用火災報知器			数量
S	煙感知器	電池式(単独型)	1
	露出型		

- ※ 煙感知器は壁・梁より600mm以上離す
壁に取付ける場合、
天井から150mm以上500mm以内離す
換気扇・エアコン吹出口から1500mm以上離す
- ※ 全室LED照明とし、居室においては調光
制御、非居室においては人感センサーを
採用する。
- ※ 標準天井高さ2,400
- ※ 特記無きガラスは型ガラス


* 凡例

- 管柱 (105×105)
- ▲ Kダクト
(3.30倍 FRM-0641)
- △ 片筋違い
(2.00倍 45×90)
(例 左:柱脚 右:柱頭)
- △ たすき掛筋違い
(4.00倍 45×90)
- 構造用合板 (2.70倍)
(t=9 9材 EXハイパー)
- △ 床点検口
- △ 天井点検口
- 換気扇
- 熱交換換気扇VLR-70

アドバンスシリーズ		
スマートデザイン (外部)		
凡例	1	コンセント 1ヶ所
①	2	コンセント 2ヶ所
②	3	コンセント 3ヶ所
①ET	1	コンセント1ヶ所接地ターミナル付
②ET	2	コンセント2ヶ所接地ターミナル付
WP		コンセント 防水型
②		エアコン用コンセント
②		200V用コンセント
WP		防雨入線プレート
●		スイッチ
●	3	3路スイッチ
●	4	4路スイッチ
●		直結電源
●		テレビ取出口
●TEL		電話取出口 (テレホンガイド)
●LAN		LAN取出口 (テレホンガイド)
●		壁照明
●		リモコン (給湯関係・ルフロ)
●		メーター
●		分電盤
●		チャイム

- ※ACコンセント天井付け
- ※TVアンテナ工事
- ※スイッチはFL+1100、コンセントはFL+200

決定図

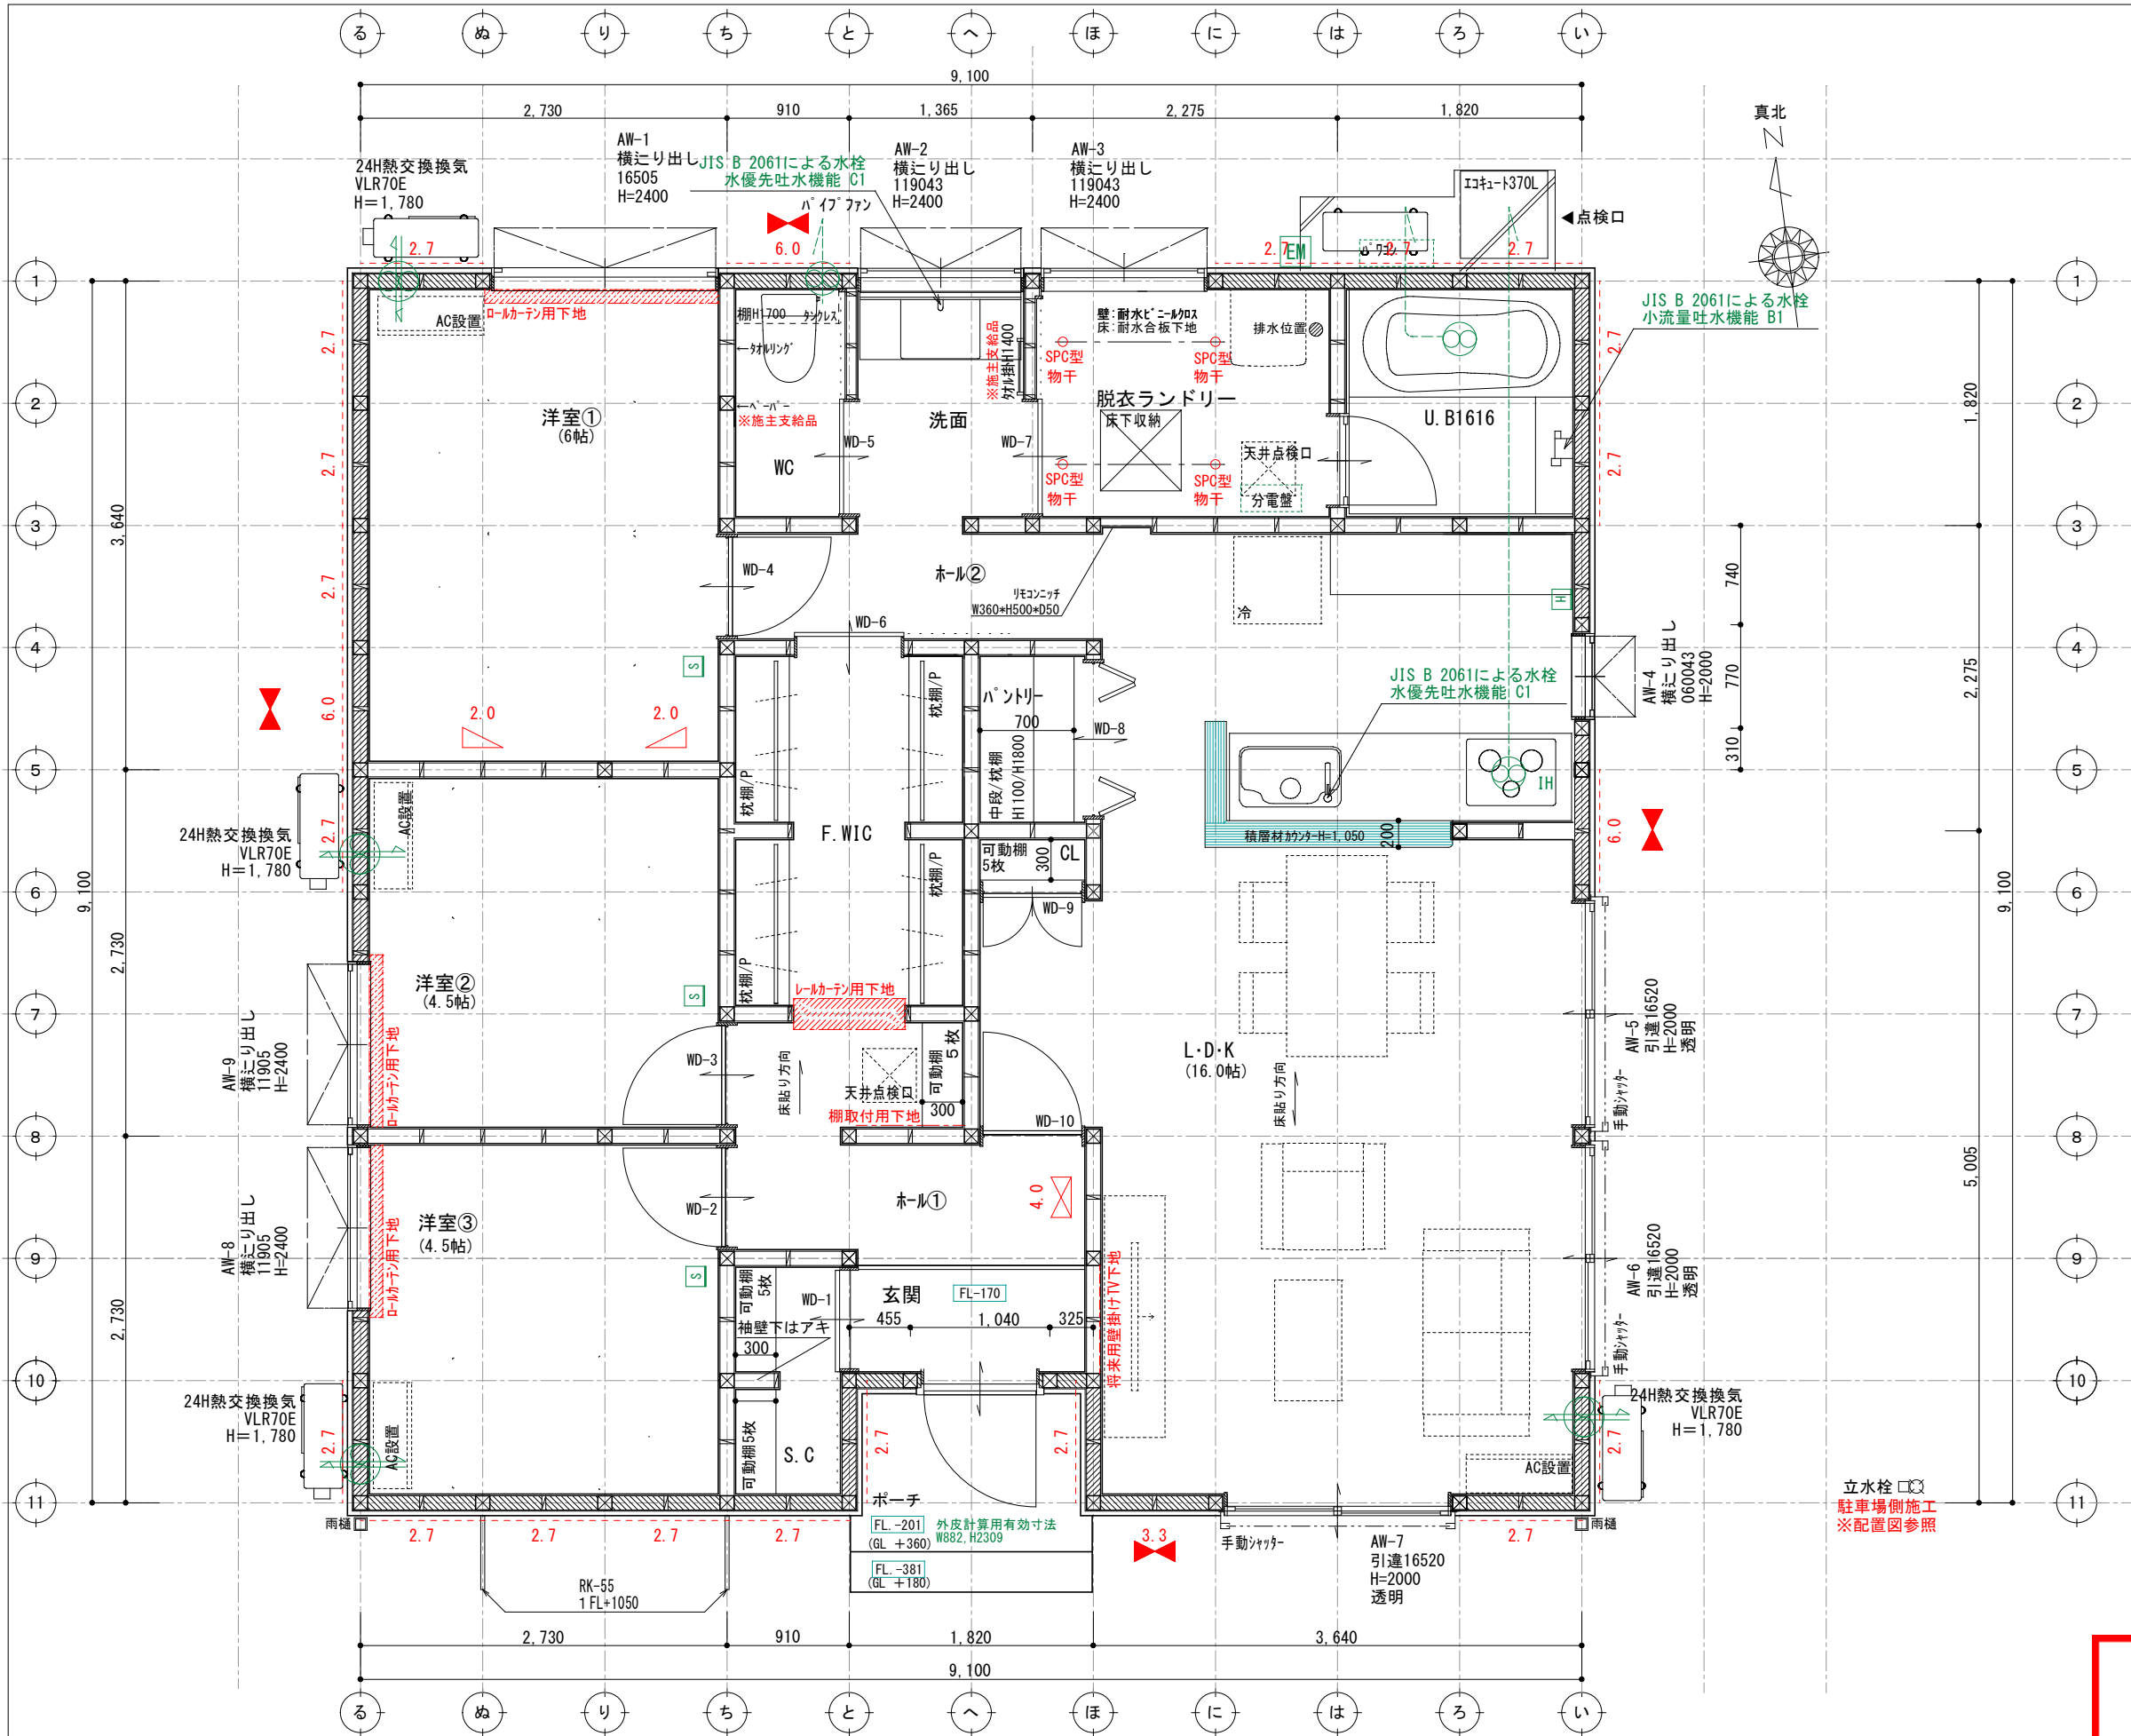

立水栓
駐車場側施工
※配置図参照