



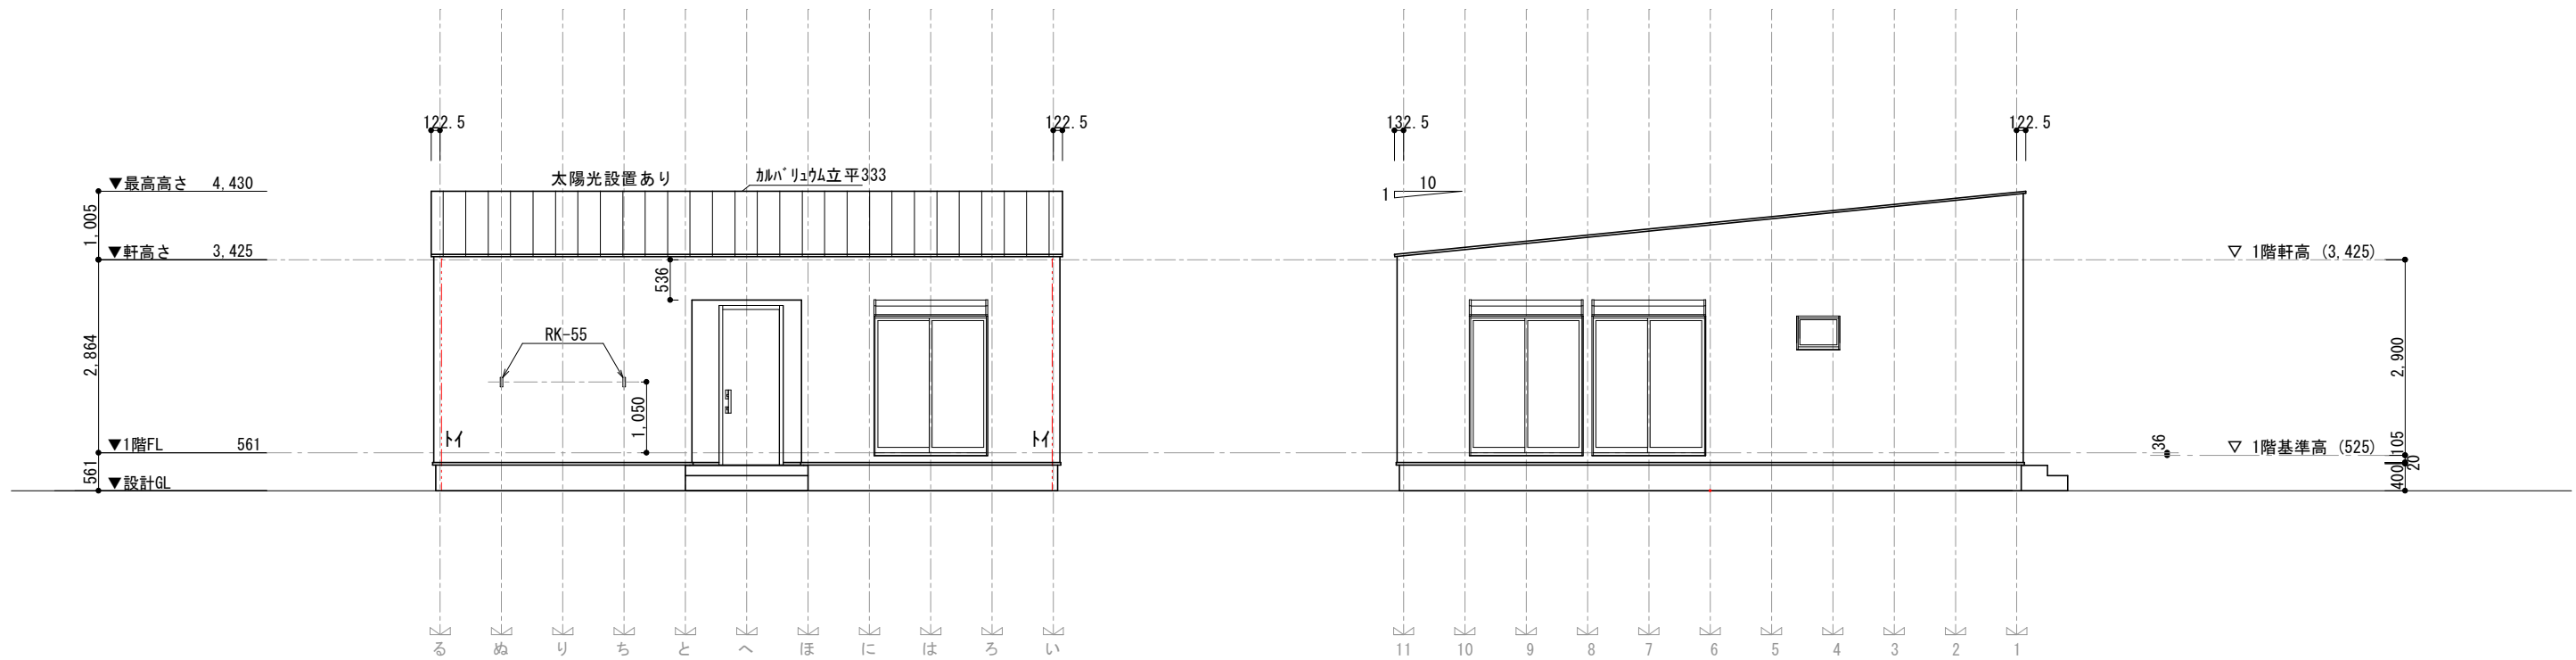

南側立面図 S=1/100

東側立面図 S=1/100

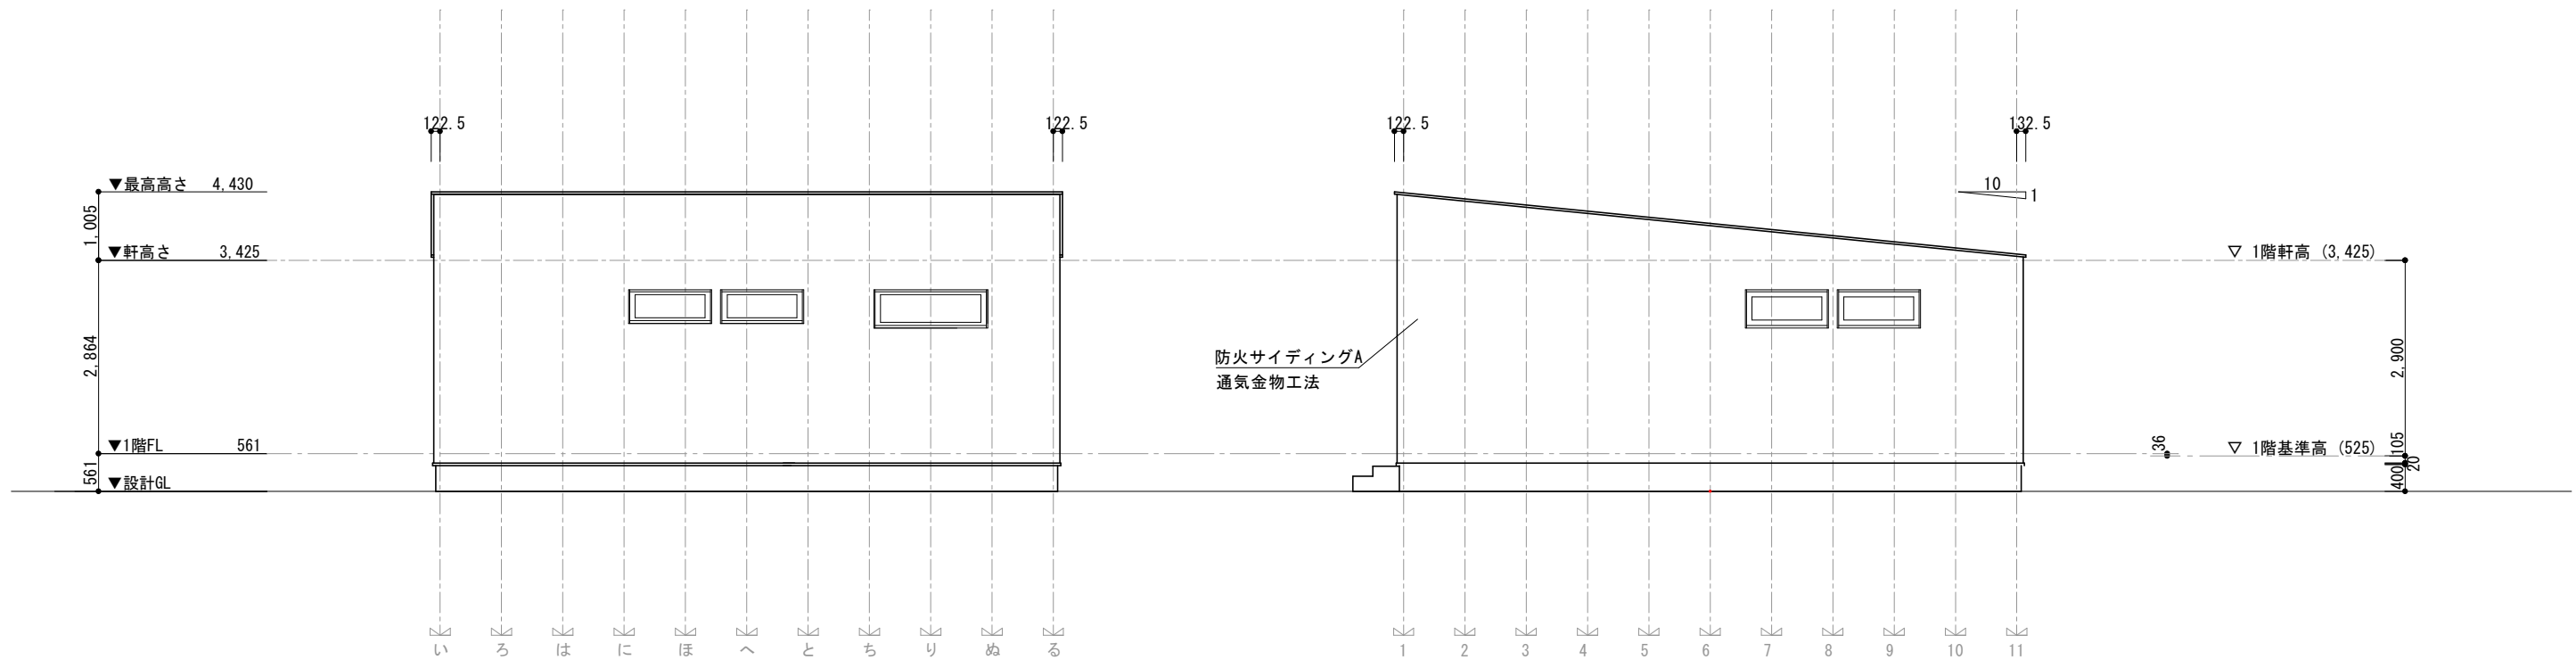

北側立面図 S=1/100

西側立面図 S=1/100

決定図

訂正	浜岡一級総合設計事務所 一級建築士事務所 静岡県知事登録第 (10)2441 号 一級建築士 大臣登録第 365879 号 西原利昌		株式会社 LIFEFUND InDesign office 一級建築士事務所 事務所登録 (2) 第7595号 一級建築士登録 第179770号 鈴木 達男 〒432-8023 静岡県浜松市中央区鴨江3丁目70番23号	年月日	件名		設計	IC	工事	図番
				2025.9.9	前嶋実香様邸 新築工事		酒井		青島	4
				縮尺	図名					