

■ 仕 様			■ HEAT20 G2		
断熱工事		■ 床:カネライトフォーム t90 ■ 土間床等の外周:スタイロフォームAT t50 ■ 壁:アクアフォームLITE吹付 t90 ■ 天井:アクファフォームLITE吹付 t220			
床下換気		■ 基礎パッキン JOTO (玄関・UB周り:気密基礎パッキン)			
防虫防蟻		■ 土壌処理・木部 ガントナーMC			
■ 外 部 仕 上 表			■ 22条地域		
部位		仕上・仕様・メーカー		色番・品番	
屋根		■ ガルバリウム鋼板(t0.35)UK立平 ニスクカラーPro GH 軒先通気金物 日本住環境株式会社【REV-15】		GHK01 Sブラック	
パラペット笠木		■ なし			
破風・鼻隠		■ なし			
雨樋	(軒樋)	■ Panasonic サーフeskエアFS-I型		ブラック	
	(縦樋)	■ Panasonic S30角樋		ブラック	
軒天	屋根軒	■			
	ポーチ軒	■ 神島化学 t= 6mm 軒天ボード エンボス		Wファインステン	
	バルコニー軒	■			
オーバーハング水切り		■ ガルバリウム鋼板 ※外壁合わせ JOTO:HF-A3550		ブラック	
外壁	通気金物(15mm)	■メイン	ニチハ エモンkセラード16 Vシリーズ リーガストーン調V	ランダMGブラック	
	※下地面材:タイガーEXハイパー	■アクセントA	なし		
	防火認定 PC030BE-4028	■アクセントB	なし		
玄関ポーチ		■ 床 玄関に同じ		-	
基礎		■ 立上り巾木: モルタル刷毛引き		-	
基礎水切り金物		■ JOTO鋼板製 防鼠材付き水切り JOTO:WMF-N35		ブラック	
バルコニー	床・内壁	■ なし		-	
	笠木	■ なし			
外部建具		■ LIXIL EW(アルゴンガス高遮熱仕様LowEトリプルガラス クリア) ・SD、TSは、メーカー設定によるが、オペレーターハンドル優先とする ・オペレーター付サッシの場合は固定網戸とする ・グレモンハンドル式サッシの場合は可動網戸とする		外観 ブラック 内観 ホワイト ※樹脂パッキン・網戸付	
シャッター		■ LDK 掃き出しサッシ 3か所 手動			
軒天通気金物					
玄関扉		■ LIXIL ジエスタ2 K2仕様 LIXILファミロック タグキー×3 (電池式)		ドア型: M17 型 ドア色: チーク浮造 ハンドル: S型ハンドル 色 ブラック	
外部物干し金物		■ 川口技研RK型-55 外壁付			
換気フード	■ 局所換気扇(トイレ 浴室 キッチンフード) 防火ダンパー無		外気フード: ブラック		
	■ ダクトレス熱交換換気システム (日本スティーベル株式会社) VLR-70E 防火ダンパー無		外気フード: B ブラック 室内パネル ホワイト		

■ 構 造 概 要					
基礎	■ RCベタ基礎コンクリート				
通し柱・管柱	■ 構造用集成材 105×105		間柱	■ 集成材	
土台	■ 桧 105×105	大引き	■ 桧 90*90	筋交い	■ 構造用製材 火打梁 ■ 鋼製火打(当社基準により米松あり)
桁・梁	■ 構造用製材及び集成材			制震装置	■ Kダンパー (株)アイ・エム・エー
■ 設 備 装 着 品					
住宅設備	部位	メーカー	商品名 ※ 詳細は見積り、プレゼン参照	見積りNo.	(日付)
	キッチン	LIXIL	■ ES I型 扉 グレージュスタック 天板 ソルティホワイト キッチンパネル: フレッシュホワイト 標準食洗器 標準IH, レンジフード (ブラック) スリム取手: ブラック	見積り番号 : M25067956064-004-2 (日付) 2025.7.28	
	バックカウンタ ※オプション	LIXIL	■ ES L1800(W900スライドストッカー×2)	見積り番号 : M25067956064-004-3 (日付) 2025.7.28	
	浴室	LIXIL	■ AX1616 PGハウス標準仕様 アクセント壁: モルティオダーク 浴槽:モナミ ホワイト 床: グレー マグネットシェフ: ホワイト	見積り番号 : M25067956064-004-1 (日付) 2025.7.28	
	1Fトイレ	LIXIL	■ ベーシアシャワートイレ 白 ● タオル掛け: KF-AA70D(リング) タンク手洗 無し ● 紙巻き器: なし(支給品取付)	見積り番号 : M25067956064-004-5 (日付) 2025.7.28	
	洗面台	LIXIL	■ EV W1200(D500タイプ) 扉:ディーブグレー [引出しタイプ シングルハンドシャワー スタンダードLED三面鏡 その他 ● タオル掛け: なし(支給品取付)	見積り番号 : M25067956064-004-4 (日付) 2025.7.28	
給排水設備	給湯器	■ エコキュート370L Panasonic Sシリーズ スタンダードモデル 追い焚きフルオート			
	排水	■ 下水			
	外水栓	■ 1 カ所 (平面図参照)		■ 外部立栓柱: PVC製 水栓柱12型【前澤化成工業】	
	外部ガーデンパン	■ 無し			
	その他	■ 洗濯機用単水栓: 緊急止水弁付 ■ 洗濯機用排水: トラップ金物(標準) ■ 排水さや管(長期優良住宅仕様)			
ガス配管設備		■ なし (配置図・平面図参照)			
電気設備	インターホン	■ パナソニック VL-SE31XL			
	TVアンテナ	■ UHF + BS・110度CS／CSアンテナ [2K・4K・8K対応] ■ ブラック ※電波状況によりホワイトになる可能性あり			
	エアコン	■ 設置場所:			
	ソーラー	■ あり(Qセルズ) 12 枚 5.28 KW Re.RISE-G3 440 (1722×1134×30)			
	※標準搭載	※メーカーのモデルチェンジ等で後継品に変更される可能性あり ■ 屋外パワコン エネルギーマネジメントシステム Cube J			
その他					
決定図					

決定図

	浜 岡 一 級 総 合 設 計 事 務 所 一級建築士事務所 静岡県知事登録第 (10)2441 号 一級建築士 大臣登録第 365879 号 西原利昌	 株式会社 LIFEFUND InDesign office 一級建築士事務所 事務所登録 (2)第7595号 一級建築士登録 第179770号 鈴木 達男 〒432-8023 静岡県浜松市中央区鴨江3丁目70番23号	年 月 日	2025.9.9	件名	前嶋実香 様邸 新築工事		設計	IC	工務	図 番
			縮尺		図面	仕上表 1		酒井		青島	1-1

トータル面積表		(㎡)
敷地面積		283.82
建築面積		82.81
床面積 1階		81.15
延床面積		81.15
建蔽率	$(82.81/283.82) \times 100$	29.18%
容積率	$(81.15/283.82) \times 100$	28.60%

道路斜線制限については、明らかに適合する。
隣地斜線制限については、明らかに適合する。
平均地盤面について
申請建物の周囲の平均地盤面高さをBM+1000とする。
盛土規制法の許可対象となる工事なし。


浜松市浜名区引佐町金指地内

求積表				
地番	1557-17			
NO	X _n	Y _n	Y _{n+1} - Y _{n-1}	X _n ・ (Y _{n+1} - Y _{n-1})
315	104.138	70.333	5.449	567.447962
314	103.609	76.511	19.262	1995.716558
313	101.552	89.595	15.506	1574.665312
312	111.814	92.017	3.675	410.916450
320	115.283	93.270	-13.945	-1607.621435
319	117.239	78.072	-16.550	-1940.305450
318	117.291	76.720	-1.955	-229.303905
321	117.343	76.117	-5.219	-612.413117
322	117.745	71.501	-5.055	-595.200975
316	112.638	71.062	-1.168	-131.561184
合計				-567.659784
合計面積				283.8298920
地積				283.82 m ²


※この図面は、現地の杭・構造物及び周辺建物を簡易測量し、
法務局備付地積測量図の成果を座標変換し、重ねたものです。

決定図

訂正	浜岡一級総合設計事務所	LIFEFUND	株式会社 LIFEFUND InDesign office	一級建築士事務所	年月日	件名	前嶋実香様 邸新築工事		設計	IC	工事	図番
	一級建築士事務所 静岡県知事登録第 (10)2441 号	PG HOUSE	事務所登録 (2) 第7595号 一級建築士登録 第179770号 鈴木 達男		2025.9.9				酒井		青島	2-1
	一級建築士 大臣登録第 365879 号 西原利昌		〒432-8023 静岡県浜松市中央区鶴江3丁目70番23号		縮尺	図名						

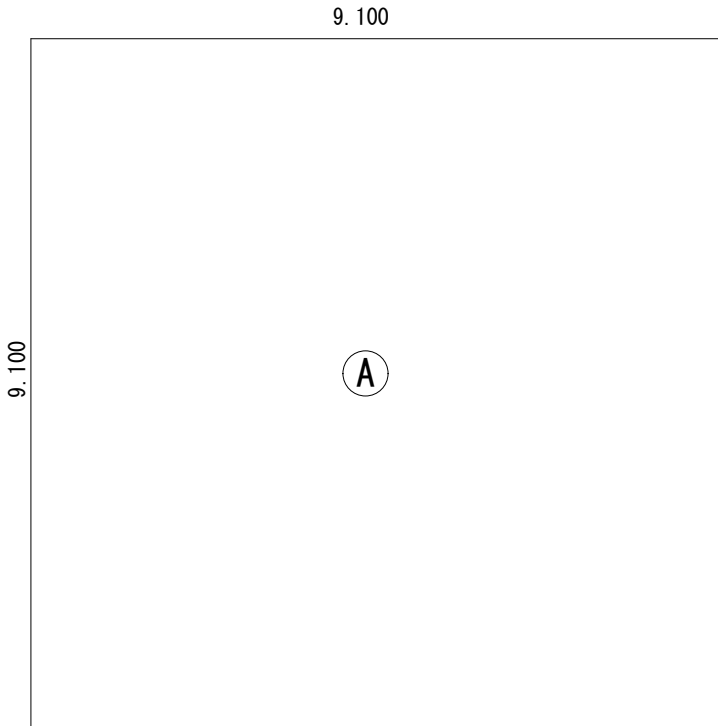

建築面積求積図 S=1/100

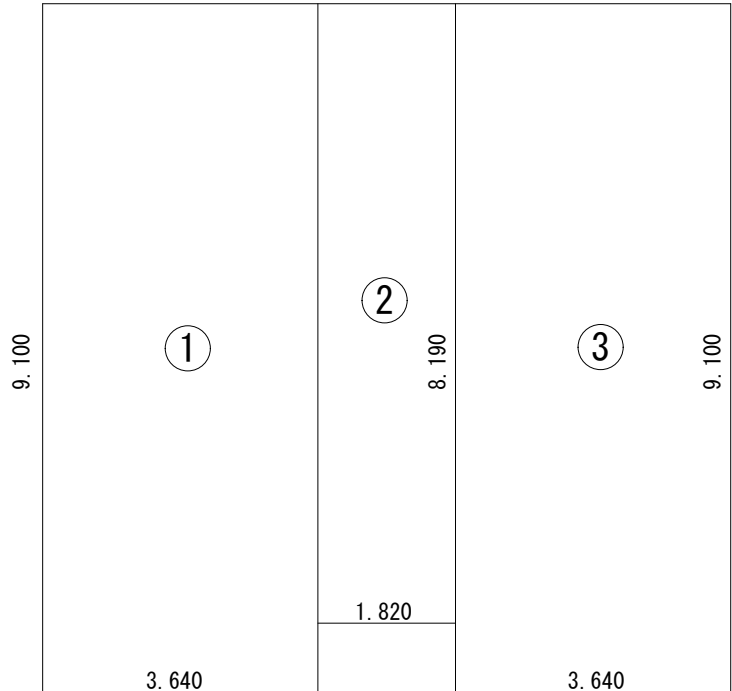

1階床面積図 S=1/100

建築面積求積表

番号	計算式	(m)	面積 (㎡)
Ⓐ	9.100×9.100		82.81
合計			82.81 82.81 (25.0坪)

1階床面積求積表

番号	計算式	(m)	面積 (㎡)
①	9.100×3.640		33.124
②	8.190×1.820		14.9058
③	9.100×3.640		33.124
合計			81.1538 81.15 (24.5坪)

延べ床面積表

	番号	(m)	面積 (㎡)
1階床面積	①②③		81.15
2階床面積			
合計			81.15 (24.5坪)

決定図

G2

壁付け 住宅用火災報知器			数量
H	熱感知器	電池式(単独型)	3
	露出型		
壁付け 住宅用火災報知器			数量
S	煙感知器	電池式(単独型)	1
	露出型		

- ※ 煙感知器は壁・梁より600mm以上離す
壁に取付ける場合、
天井から150mm以上500mm以内離す
換気扇・エアコン吹出口から1500mm以上離す
- ※ 全室LED照明とし、居室においては調光
制御、非居室においては人感センサーを
採用する。
- ※ 標準天井高さ2,400
- ※ 特記無きガラスは型ガラス


* 凡例

- 管柱 (105×105)
- Kタンパー
(3.30倍 FRM-0641)
- 片筋違い
(2.00倍 45×90)
(例 左:柱脚 右:柱頭)
- たすき掛筋違い
(4.00倍 45×90)
- 構造用合板 (2.70倍)
(t=9 9材 EXハイパー)
- 床点検口
- 天井点検口
- 換気扇
- 熱交換換気扇VLR-70

アドバンスシリーズ		
スマートデザイン (外部)		
凡例	1	コンセント 1ヶ所
2	コンセント 2ヶ所	
3	コンセント 3ヶ所	
1ET	コンセント1ヶ所接地ターミナル付	
2ET	コンセント2ヶ所接地ターミナル付	
WP	コンセント 防水型	
WP	エアコン用コンセント	
WP	200V用コンセント	
WP	防雨入線プレート	
WP	スイッチ	
3	3路スイッチ	
4	4路スイッチ	
直結電源		
TV	テレビ取出口	
TEL	電話取出口 (テレホンガイド)	
LAN	LAN取出口 (テレホンガイド)	
壁照明		
リモコン (給湯関係・ルフロ)		
メーター		
分電盤		
チャイム		

- ※ACコンセント天井付け
- ※TVアンテナ工事
- ※スイッチはFL+1100、コンセントはFL+200

決定図

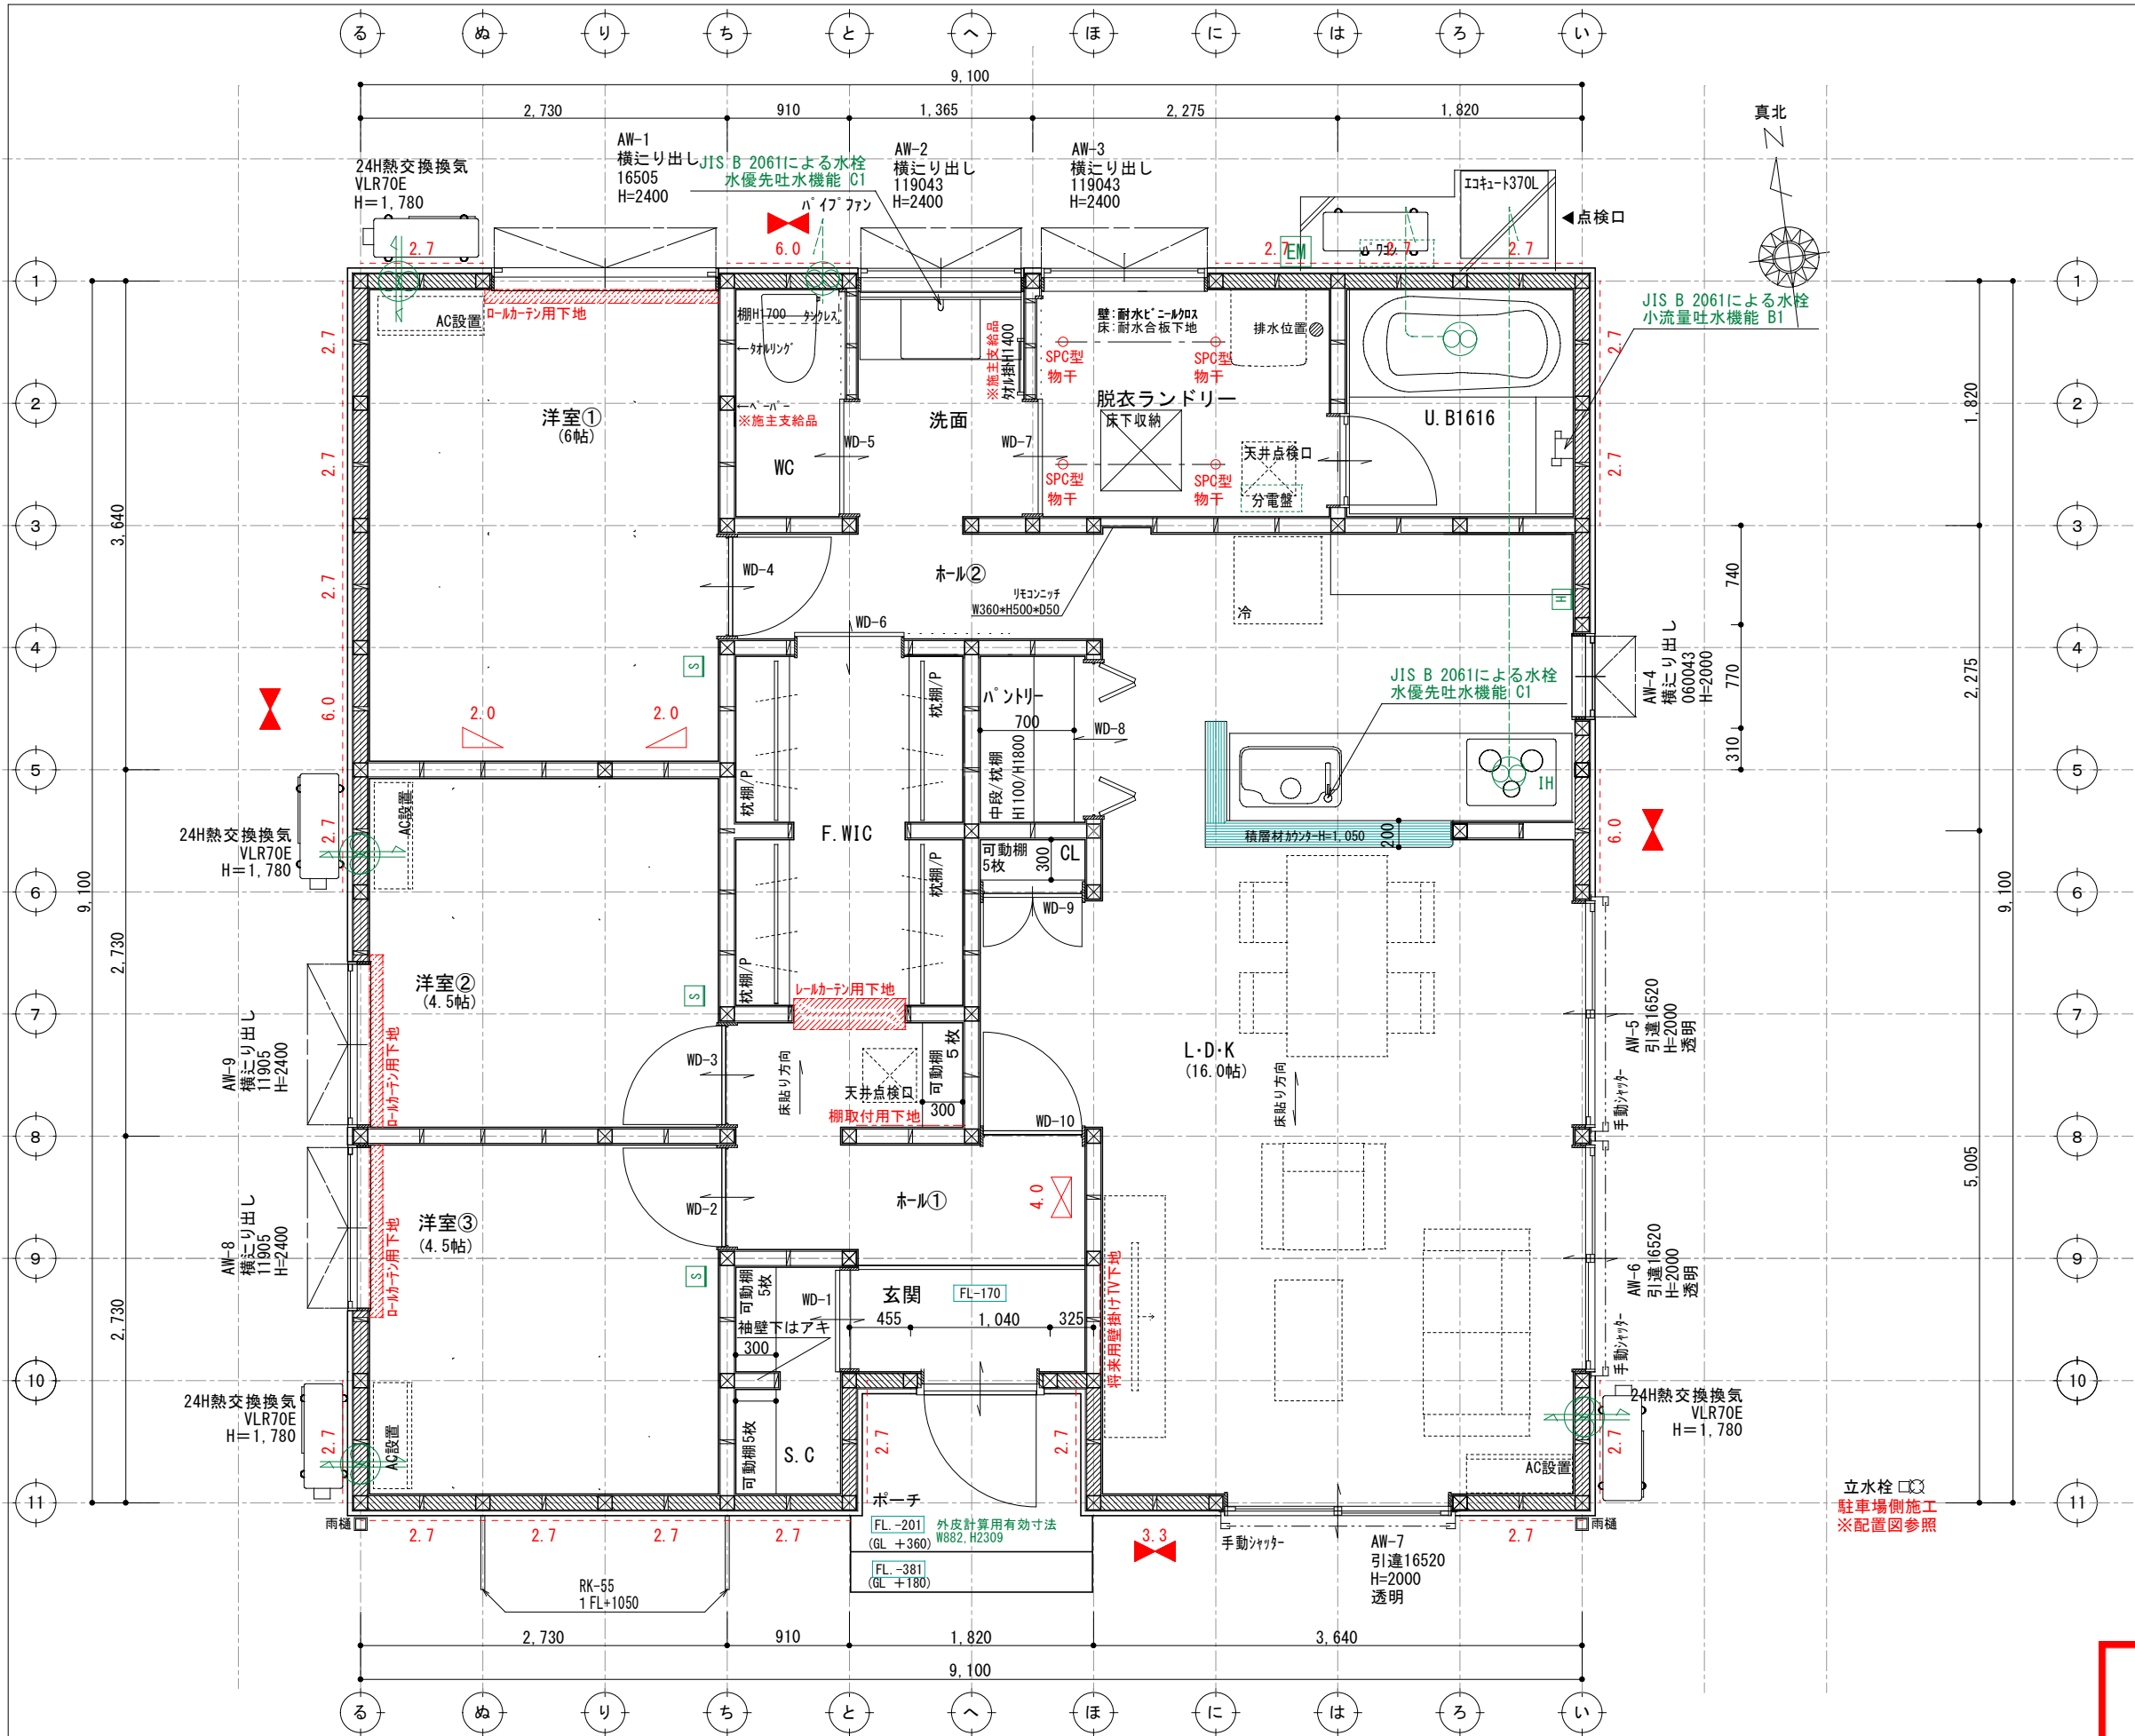

立水栓
駐車場側施工
※配置図参照

訂正

浜岡一級総合設計事務所
一級建築士事務所 静岡県知事登録第 (10)2441 号
一級建築士 大臣登録第 365879 号 西原利昌

PG HOUSE
ピージーハウス

株式会社 LIFEFUND InDesign office 一級建築士事務所
事務所登録 (2) 第7595号 一級建築士登録 第179770号 鈴木 達男
〒432-8023 静岡県浜松市中央区鴨江3丁目70番23号


年月日
2025. 9. 9
縮尺
1/50

件名
前嶋実香様邸 新築工事
図名
1階平面図

設計	IC	工事	図番
酒井		青島	3-1

GX住宅 (Cube J付)


太陽光あり

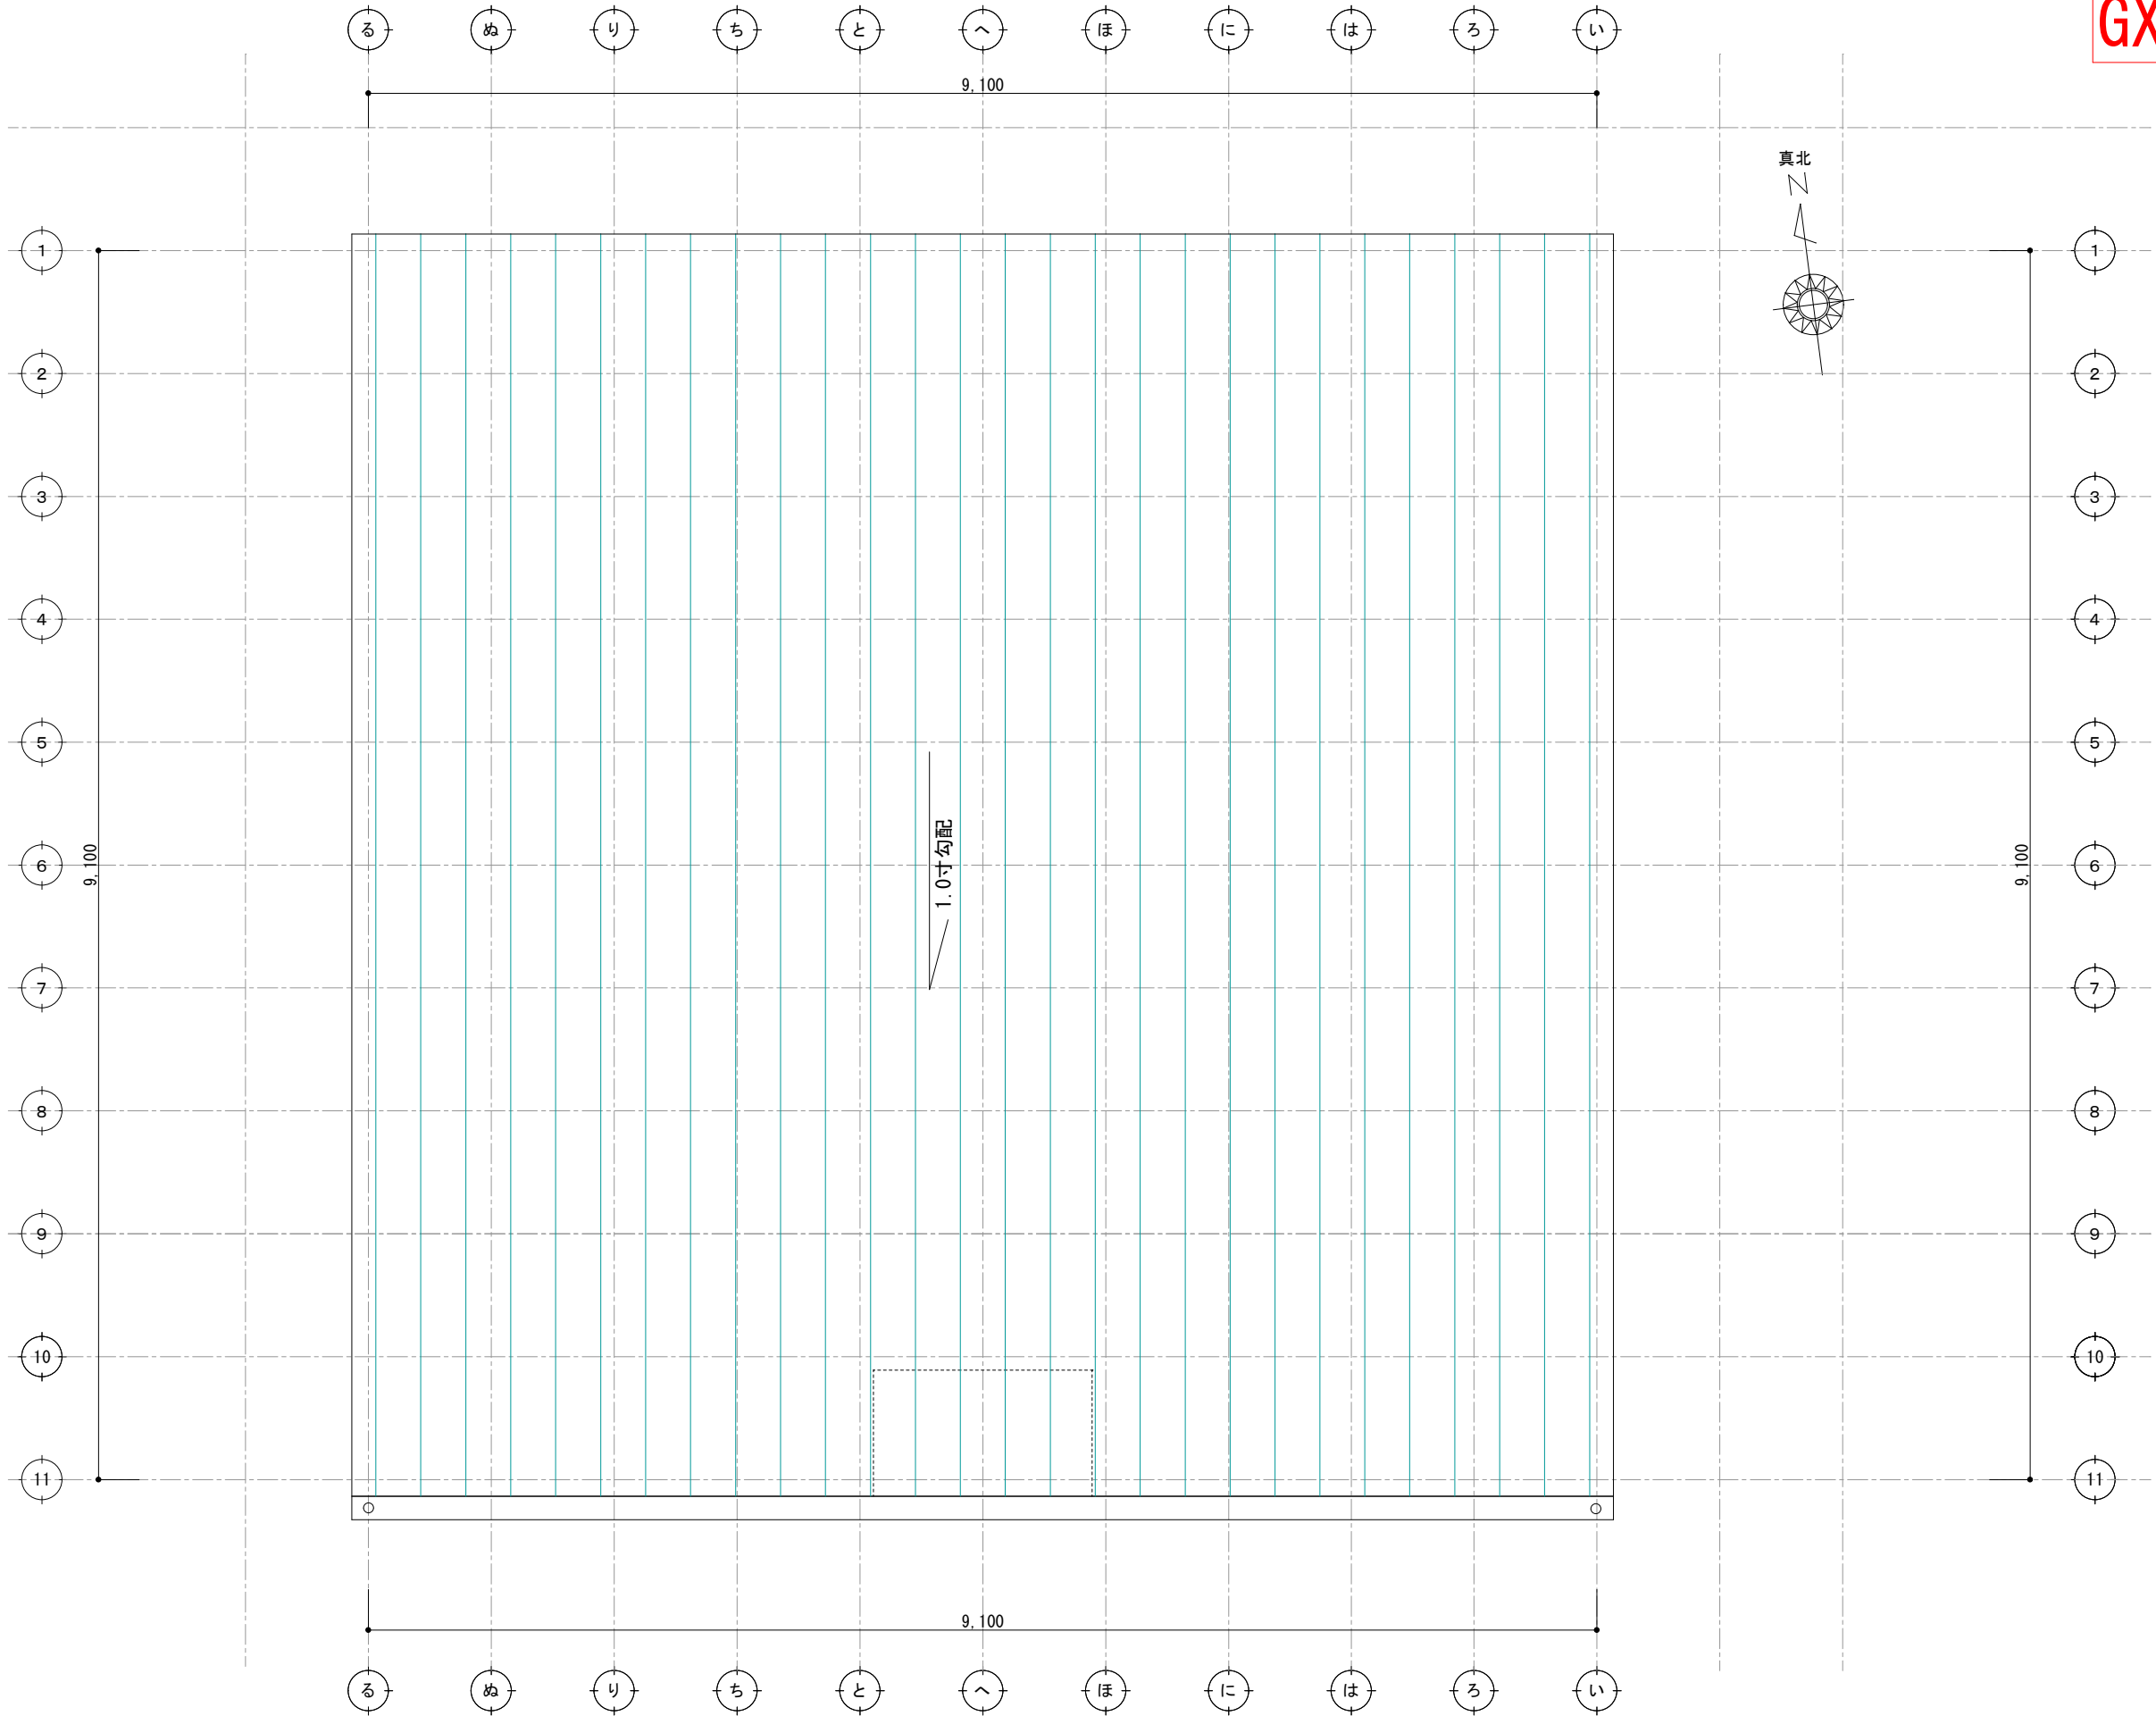

決定図


訂正	浜岡一級総合設計事務所 一級建築士事務所 静岡県知事登録第 (10)2441 号 一級建築士 大臣登録第 365879 号 西原利昌	 PG HOUSE	株式会社 LIFEFUND InDesign office 一級建築士事務所 事務所登録 (2) 第7595号 一級建築士登録 第179770号 鈴木 達男 〒432-8023 静岡県浜松市中央区鴨江3丁目70番23号	年月日 2025. 9. 9 縮尺 1/100	件名 前嶋実香様邸 新築工事 図名 屋根伏図		設計	IC	工事	図番
							酒井		青島	3-3

G2

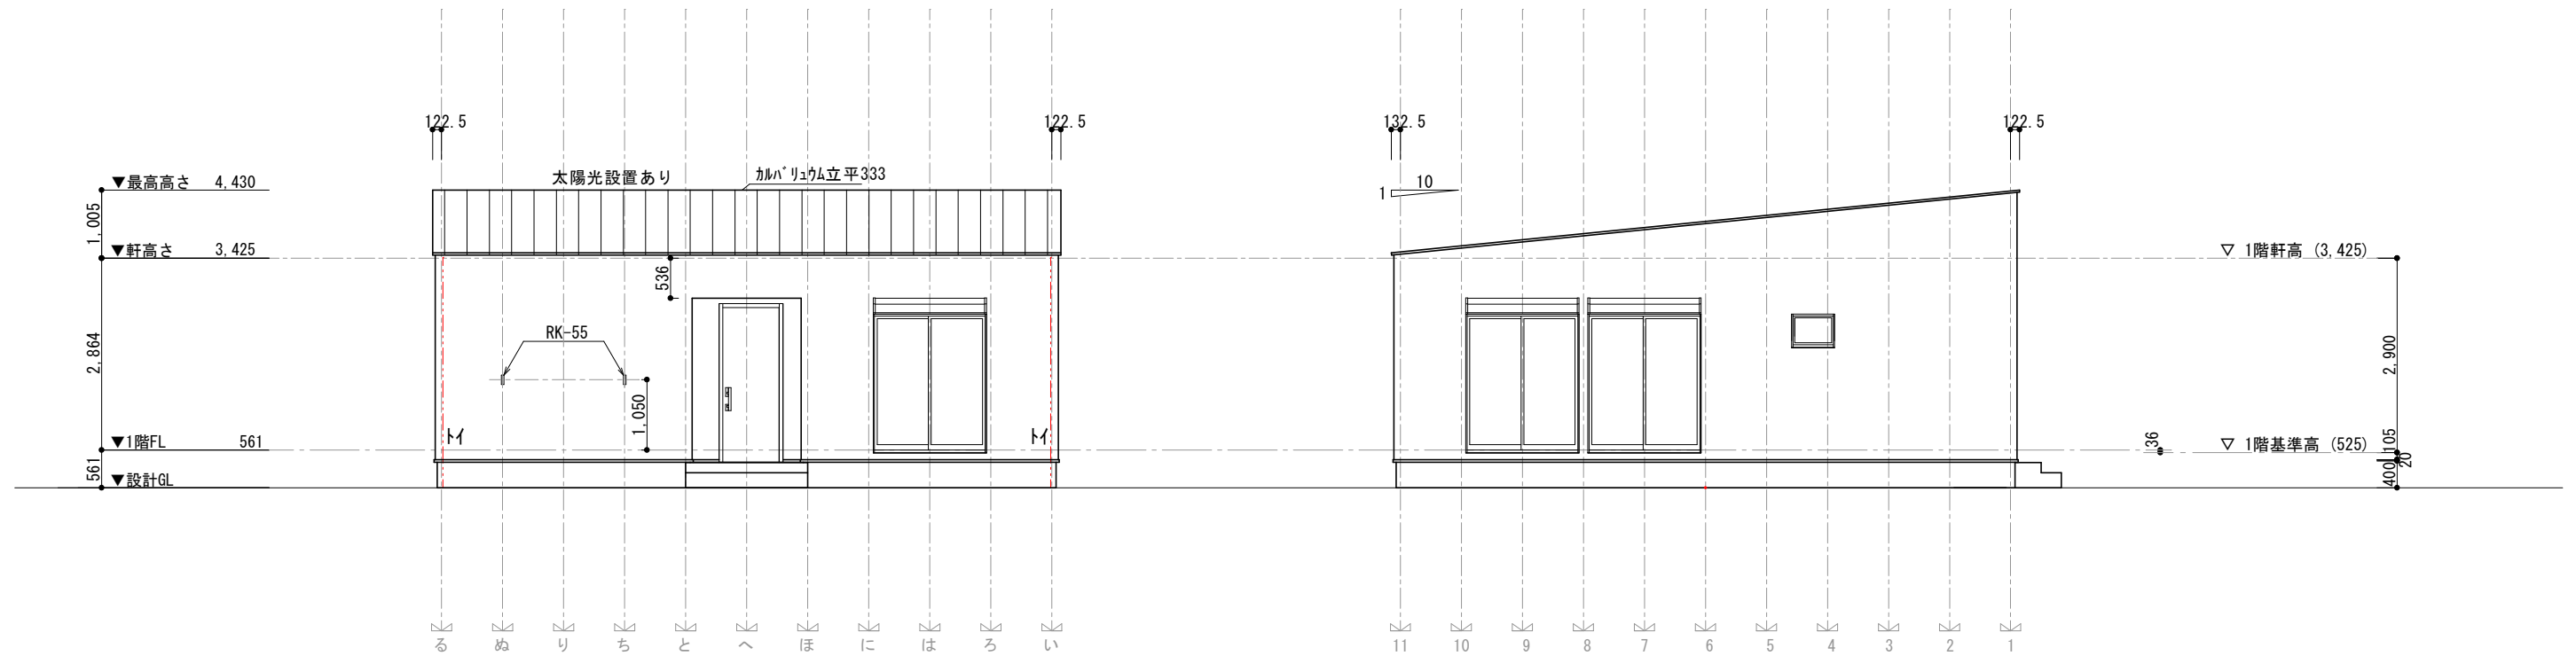

南側立面図 S=1/100

東側立面図 S=1/100

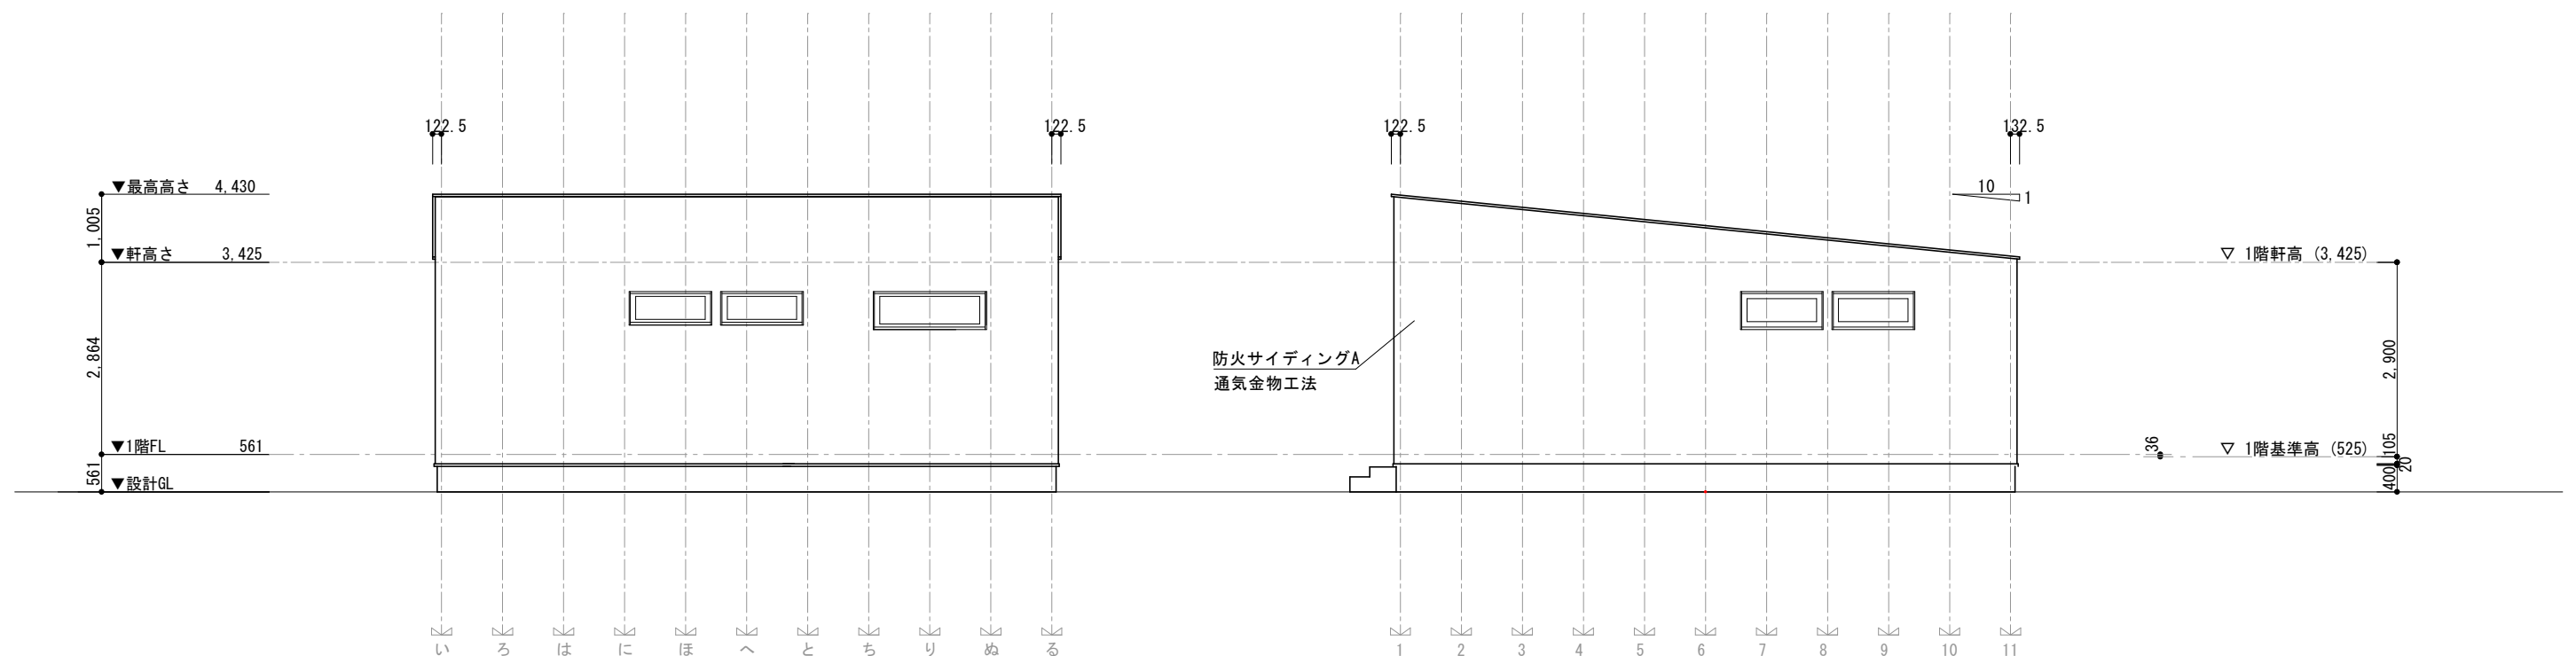


北側立面図 S=1/100

西側立面図 S=1/100







決定図

訂 正	浜 岡 一 級 総 合 設 計 事 務 所 一級建築士事務所 静岡県知事登録第 (10)2441 号 一級建築士 大臣登録第 365879 号 西原利昌	 PG HOUSE ビージーハウス	株式会社 LIFEFUND InDesign office 一級建築士事務所 事務所登録 (2) 第7595号 一級建築士登録 第179770号 鈴木 達男 〒432-8023 静岡県浜松市中央区鴨江3丁目70番23号	年 月 日 2025. 9. 9 縮 尺 1/100	件 名 前嶋実香様邸 新築工事 図 名 立面図	設計 酒井	IC	工事 青島	図 番 4
-----	--	--	---	-------------------------------------	----------------------------------	----------	----	----------	----------

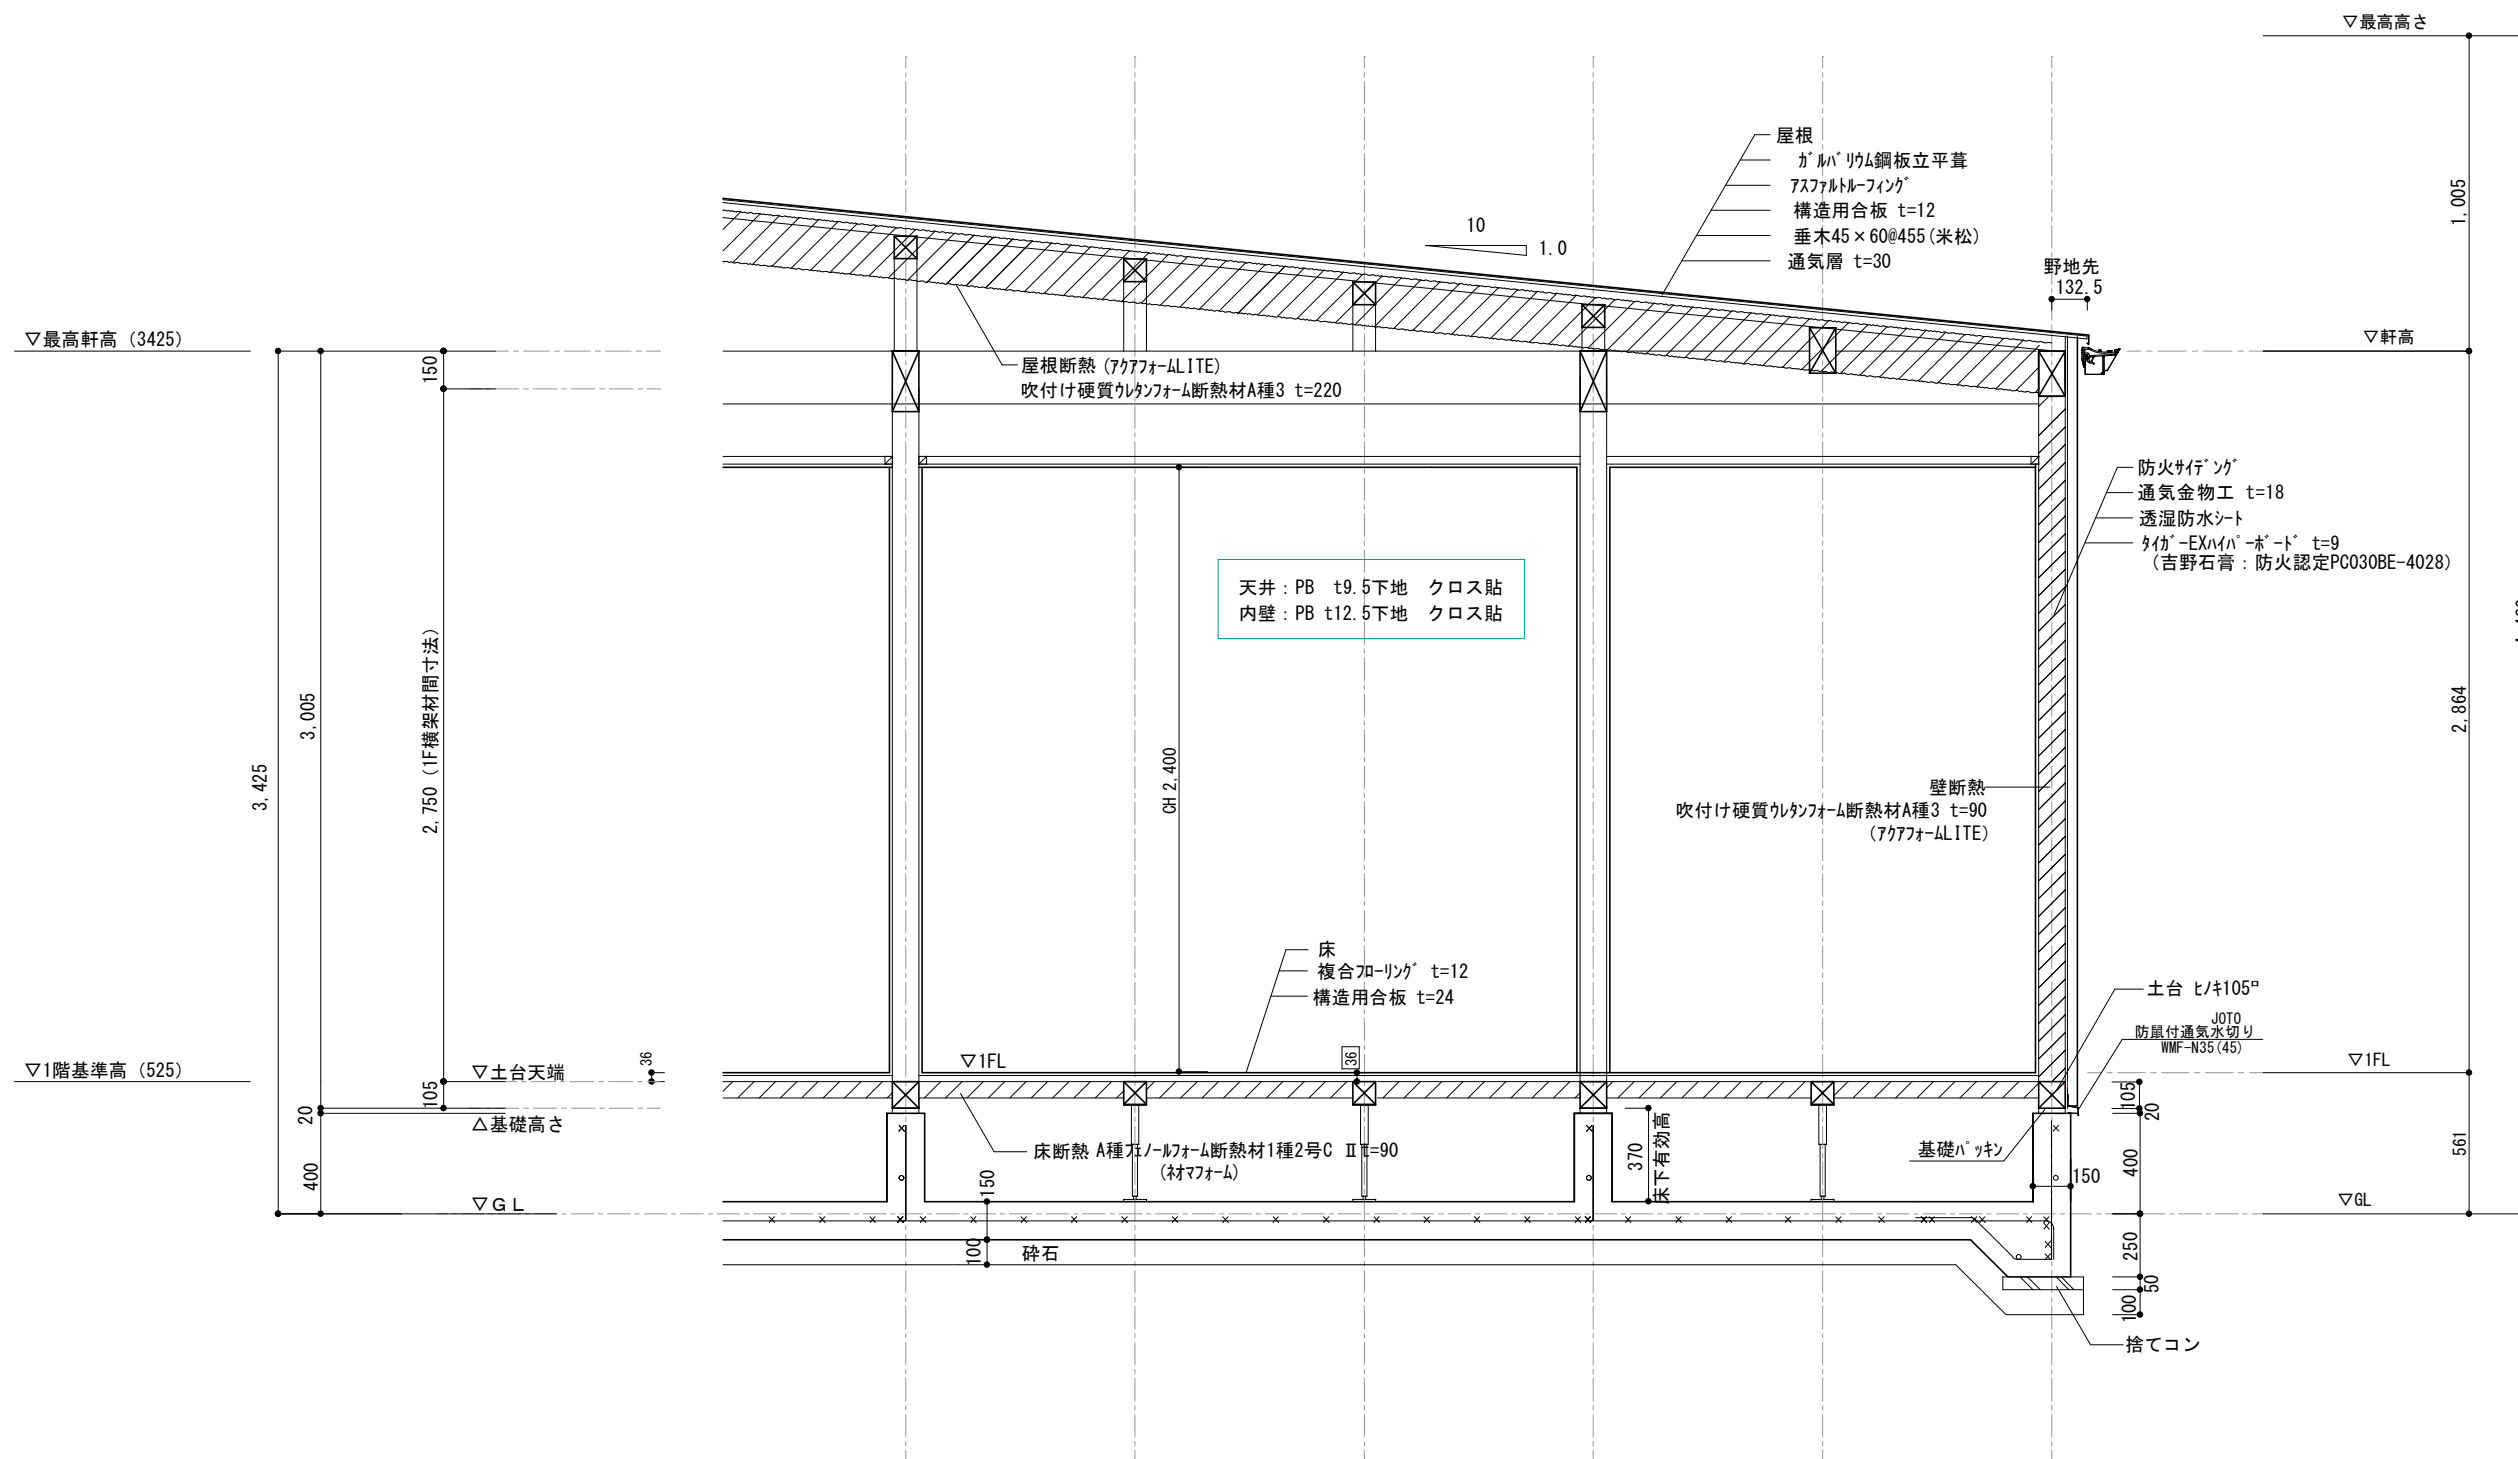


決定図

訂 正	浜 岡 一 級 総 合 設 計 事 務 所			株式会社 LIFEFUND InDesign office 一級建築士事務所		年 月 日	件 名		設計	IC	工事	図 番
	一級建築士事務所 静岡県知事登録第 (10)2441 号			事務所登録 (2)第7595号 一級建築士登録 第179770号 鈴木 達男		2025. 9. 9	前嶋実香様 邸新築工事		酒井	青島	5	
	一級建築士 大臣登録第 365879 号 西原利昌			〒432-8023 静岡県浜松市中央区鴨江3丁目70番23号		縮 尺	図 名					
				1/30	矩計図							

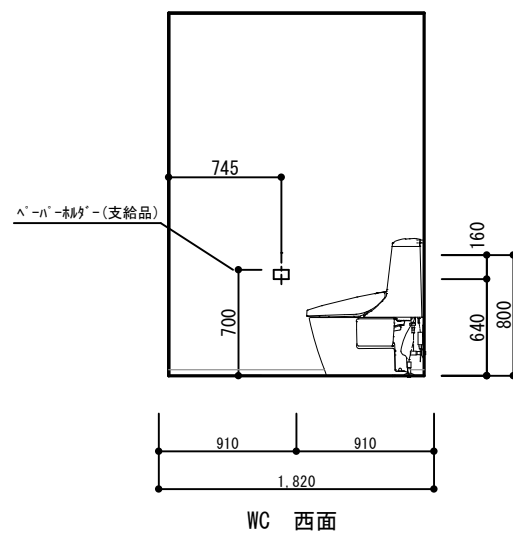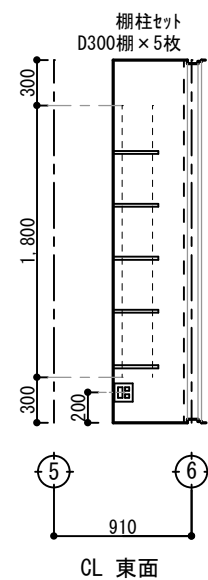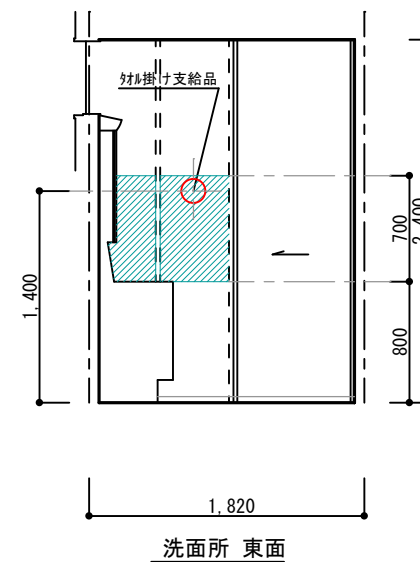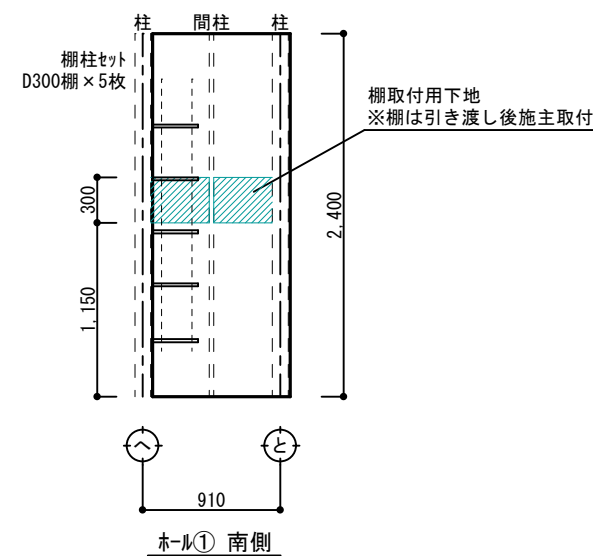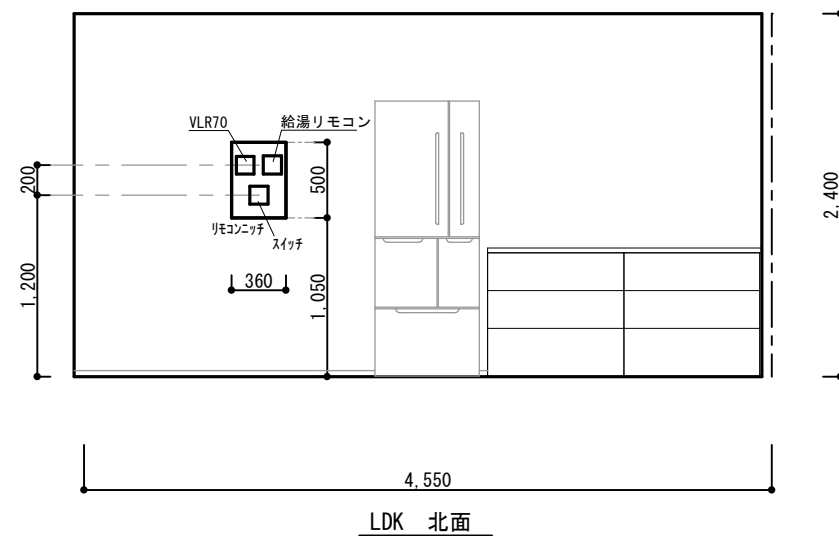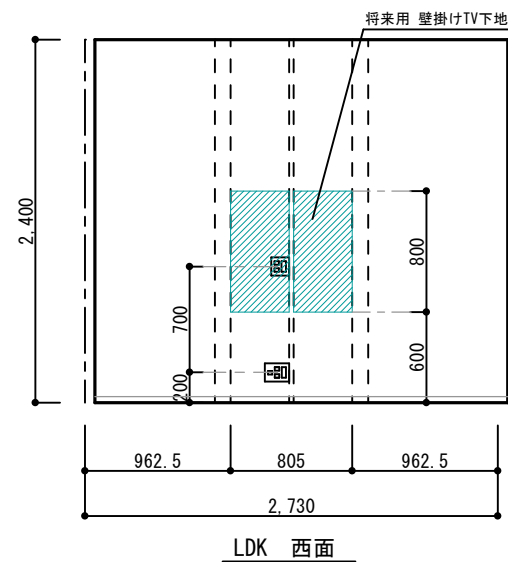

決定図

訂正	浜岡一級総合設計事務所 一級建築士事務所 静岡県知事登録第(10)2441号 一級建築士 大臣登録第365879号 西原利昌	LIFEFUND PG HOUSE	株式会社 LIFEFUND InDesign office 一級建築士事務所 事務所登録(2)第7595号 一級建築士登録第179770号 鈴木 達男 〒432-8023 静岡県浜松市中央区鴨江3丁目70番23号	年月日 2025.9.9	件名 前嶋実香様 新築工事		設計 酒井	IC	工事 青島	図番 6-1
				縮尺 1/50	図名 展開図-1					

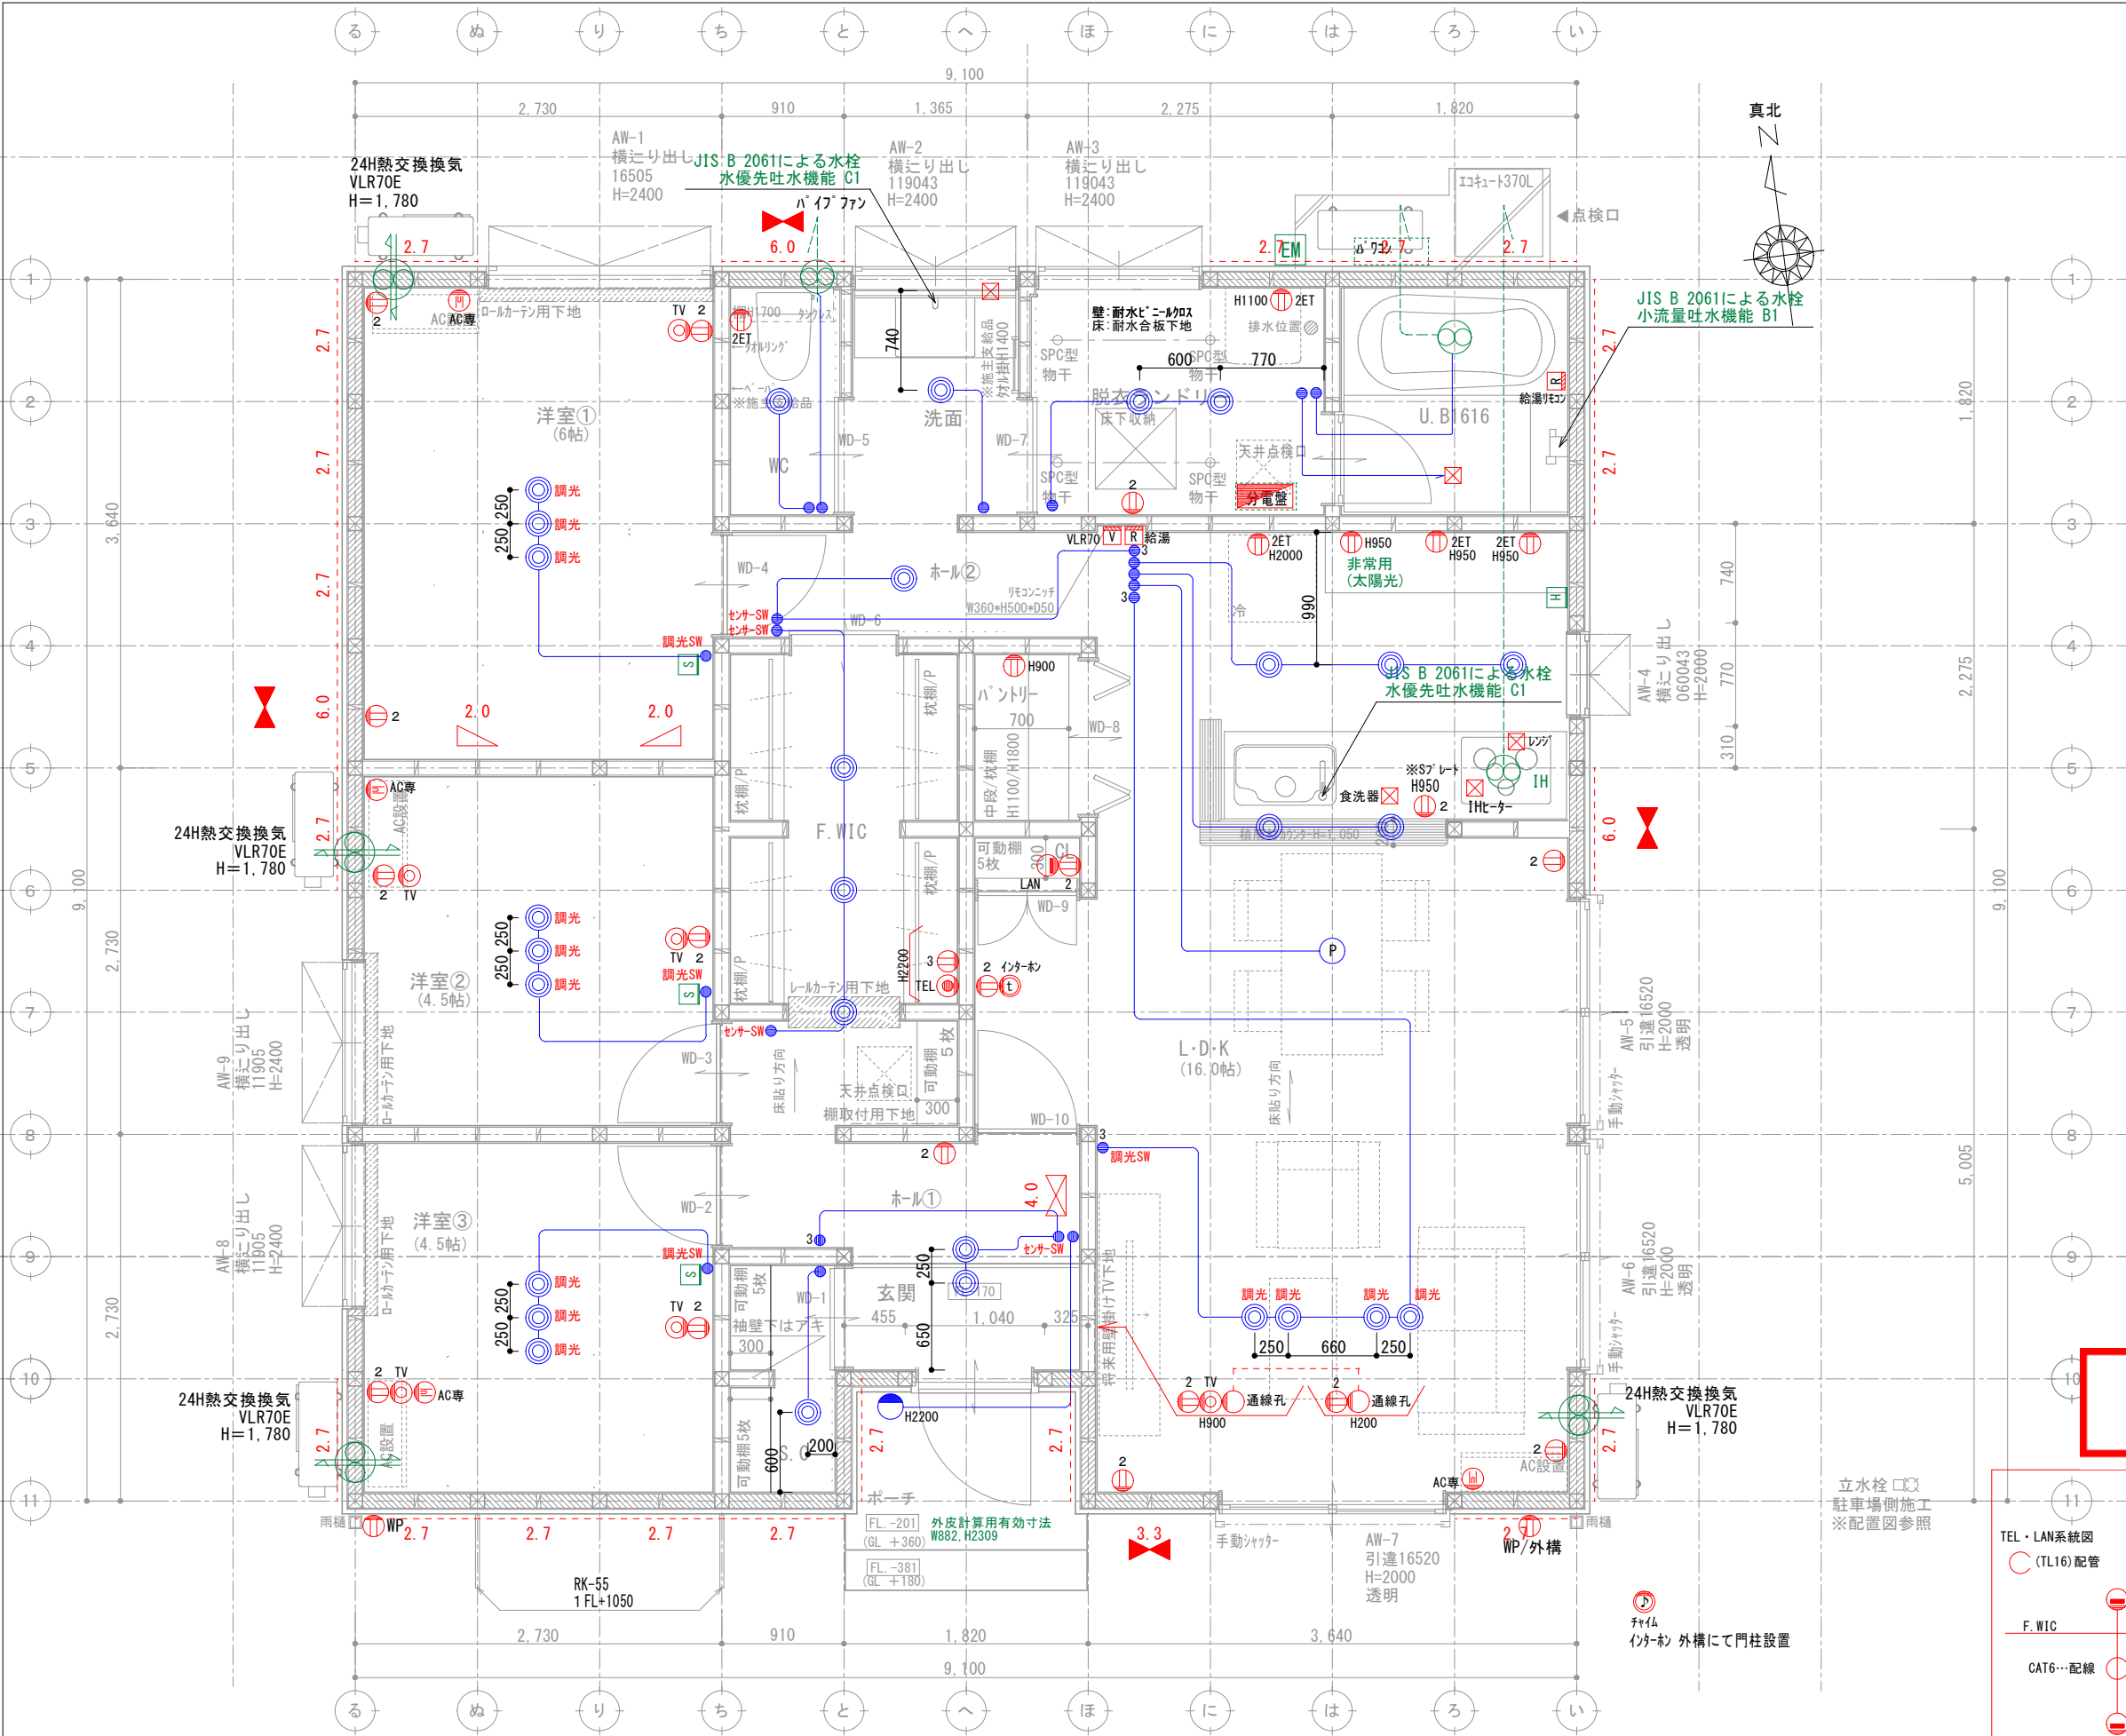

G2


壁付け 住宅用火災報知器			数量
H 熱感知	熱感知器	電池式(単独型)	3
		露出型	
壁付け 住宅用火災報知器			数量
S 煙感知	煙感知器	電池式(単独型)	1
		露出型	

※ 煙感知器は壁・梁より600mm以上離す
壁に取付ける場合、
天井から150mm以上500mm以内離す
換気扇・エアコン吹出口から1500mm以上離す
※ 全室LED照明とし、居室においては調光
制御、非居室においては人感センサー
を採用する。

*** 凡例**


- 管柱 (105×105)
- Kタンパー (3.30倍 FRM-0641)
- 片筋違い (2.00倍 45×90)
(例 左:柱脚 右:柱頭)
- たすき掛筋違い (4.00倍 45×90)
- 構造用合板 (2.70倍)
(t=9 9割 E-Xハイパー)
- 床点検口
- 天井点検口
- 換気扇
- 熱交換換気扇VLR-70

決定図

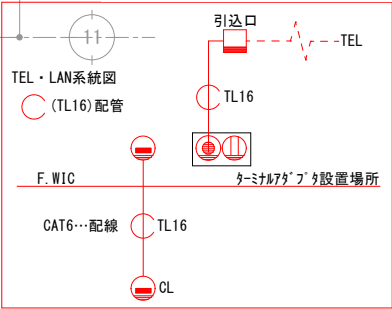

アドバンスシリーズ	
スマートデザイン (外部)	
凡例	
1	コンセント 1ヶロ
2	コンセント 2ヶロ
3	コンセント 3ヶロ
1ET	コンセント1ヶロ接地ターミナル付
2ET	コンセント2ヶロ接地ターミナル付
WP	コンセント 防水型
	エアコン用コンセント
	200V用コンセント
WP	防雨入線プレート
	スイッチ
3	3路スイッチ
4	4路スイッチ
	直結電源
TV	テレビ取出口
TEL	電話取出口 (テレホンガイド)
LAN	LAN取出口 (テレホンガイド)
	壁照明
R	リモコン(給湯関係・ルフロ)
WH	メーター
t	分電盤
チヤム	チヤム

※ACコンセント天井付け
※TVアンテナ工事
※スイッチはFL+1100、コンセントはFL+200

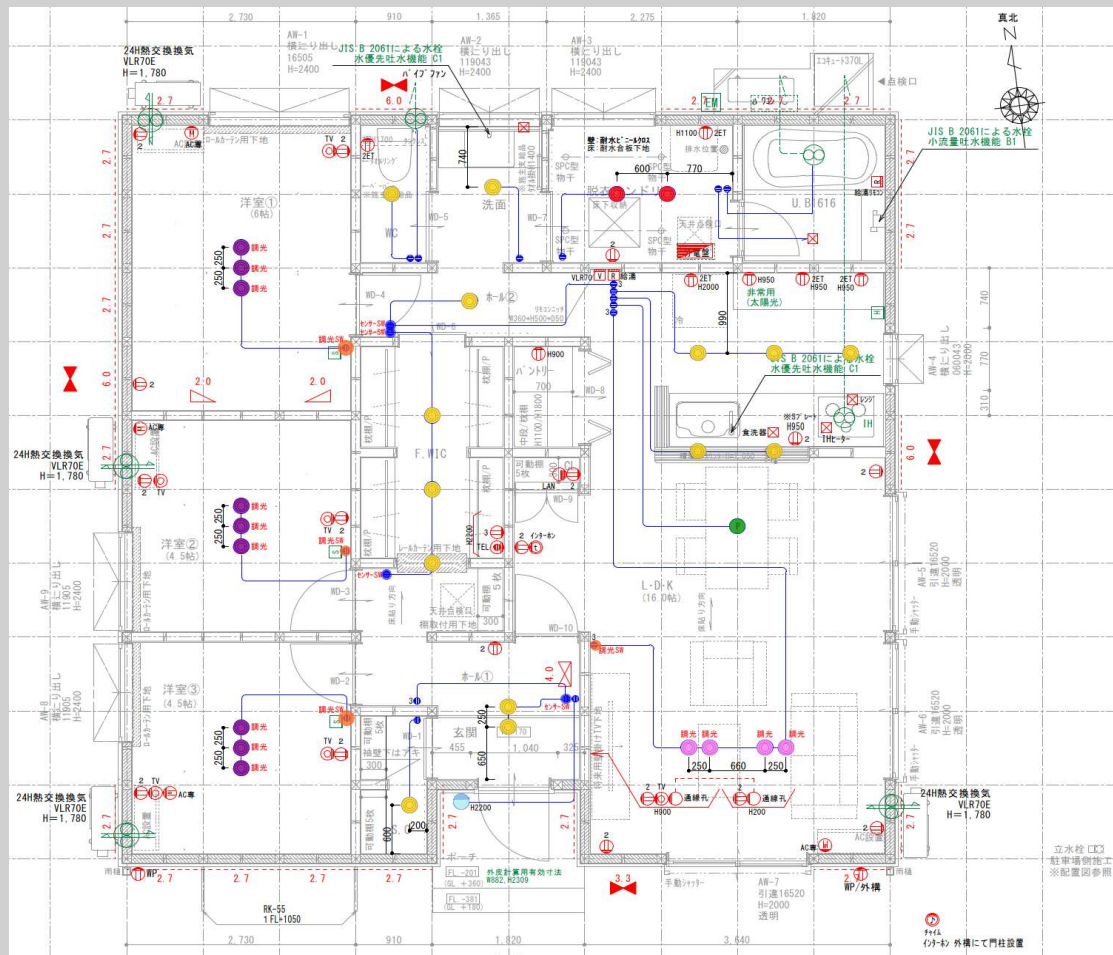

1階

ドアホン：VL-SE31XL
(Panasonic)



内部SW：アドバンス
マットホワイト



ポーチ灯

● × 1

外部灯

DWP_40294Y



DWP-40294 Y
電球色 / 2700K・Ra82
定格光束 消費電力 固有エネルギー消費効率
100lm 4.2W 23.8lm/W
¥12,000-(税抜) (ランプ付)
LED電球 4.2W(E17)
白熱灯60W相当
●アクリル 乳白
●プラスチック 黒
●径: 138 出85mm 0.4kg
●7VA
●AC100V
●光源寿命40,000時間
●調光器併用不可
カバーはめこみ式

基本照明ダウナイト

● × 14

DDL_6102YW



DDL-6102 YW
電球色 / 2700K・Ra83
定格光束 消費電力 固有エネルギー消費効率
440lm 4.6W 95.6lm/W
¥3,600-(税抜) (LED内蔵)
LED 4.6W
白熱灯60W相当
●鏡板 白塗装
●アクリル 乳白(マット)
●径φ116 埋込穴φ100 埋込深71mm 0.3kg
●8VA
●拡散/ネル付
●AC100V
●光源寿命60,000時間
●取付可能天井厚5~25mm
●調光器併用不可

洋室①②③

● × 9

調光ダウナイト

DDL_6002YWG



DDL-6002 YWG
電球色 / 2700K・Ra83
定格光束 消費電力 固有エネルギー消費効率
440lm 5.8W 75.8lm/W
¥4,600-(税抜) (LED内蔵)
LED 5.8W
白熱灯60W相当
●鏡板 白塗装
●アクリル 乳白(マット)
●径φ116 埋込穴φ100 埋込深71mm 0.3kg
●7VA
●拡散/ネル付
●AC100V
●調光可能(1%~100%)
●調光にはLED専用調光器(別売)をご使用ください。
●光源寿命60,000時間
●取付可能天井厚5~25mm

LDK

● × 4

調光ダウナイト

DDL_6004YWG



DDL-6004 YWG
電球色 / 2700K・Ra83
定格光束 消費電力 固有エネルギー消費効率
710lm 7.8W 91.0lm/W
¥7,000-(税抜) (LED内蔵)
LED 7.8W
白熱灯100W相当
●鏡板 白塗装
●アクリル 乳白(マット)
●径φ116 埋込穴φ100 埋込深71mm 0.3kg
●8VA
●拡散/ネル付
●AC100V
●調光可能(1%~100%)
●調光にはLED専用調光器(別売)をご使用ください。
●光源寿命60,000時間
●取付可能天井厚5~25mm

脱衣ランドリー

● × 2

ダウナイト

DDL_6102AW



DDL-6102 AW
電球色 / 3500K・Ra83
定格光束 消費電力 固有エネルギー消費効率
470lm 4.6W 102.1lm/W
¥3,600-(税抜) (LED内蔵)
LED 4.6W
白熱灯60W相当
●鏡板 白塗装
●アクリル 乳白(マット)
●径φ116 埋込穴φ100 埋込深70mm 0.3kg
●8VA
●拡散/ネル付
●AC100V
●光源寿命60,000時間
●取付可能天井厚5~25mm
●調光器併用不可

LDK

● × 1

ペンダントライト

DPN_39817GE



DPN-39817 GE
電球色 / 2700K・Ra83 / 昼白色 / 5000K・Ra83
定格光束 消費電力 固有エネルギー消費効率
530lm 8W 66.2lm/W
¥56,500-(税抜) (LED内蔵)
LED 8W
白熱灯100W相当
●鏡板 白塗装 ●アクリル 乳白(マット)
●径φ530 高248 全長700~1200mm 2.9kg
●14VA
●吊高で調節可能
●色温度切替機能付(2700K/5000K)
●調光可能(1%~100%)
●壁スイッチで色温度のみ切替可能
●AC100V
●調光にはLED専用調光器(別売)をご使用ください。
●光源寿命40,000時間
●シーンコントロールは使用できません。
引線シーリング取付式
特許登録済

LDK、洋室①②③

● × 4

調光SW

WTA_57583WK



WTA57583WK
希望小売価格 11,900円(税抜)
※掲載の価格には消費税は含まれていません。
[LED]埋込逆位相調光スイッチC(ほたるスイッチC)
(適合LED専用3.2A)(ロータリー式)
(下限照度設定機能付)(マットホワイト)
プレート別売
WTA7101WK
希望小売価格 320円(税抜)
※掲載の価格には消費税は含まれていません。

ホール①、ホール②

● × 3

センサーSW

WTA_14119W



WTA14119W
3線 / 4線式
壁取付 熱線センサ付自動スイッチ(鏡器)
(検知後連続動作時間 約10秒~30分可変形)
(明るさセンサ・手動スイッチ付)(マットホワイト)
3A 100V AC
プレート別売

外部：スマートデザインシリーズ
ブラック



決定図

PG House


前嶋実香様

邸新築工事

Lighting Plan

2025.9.9

(図面 7-3)

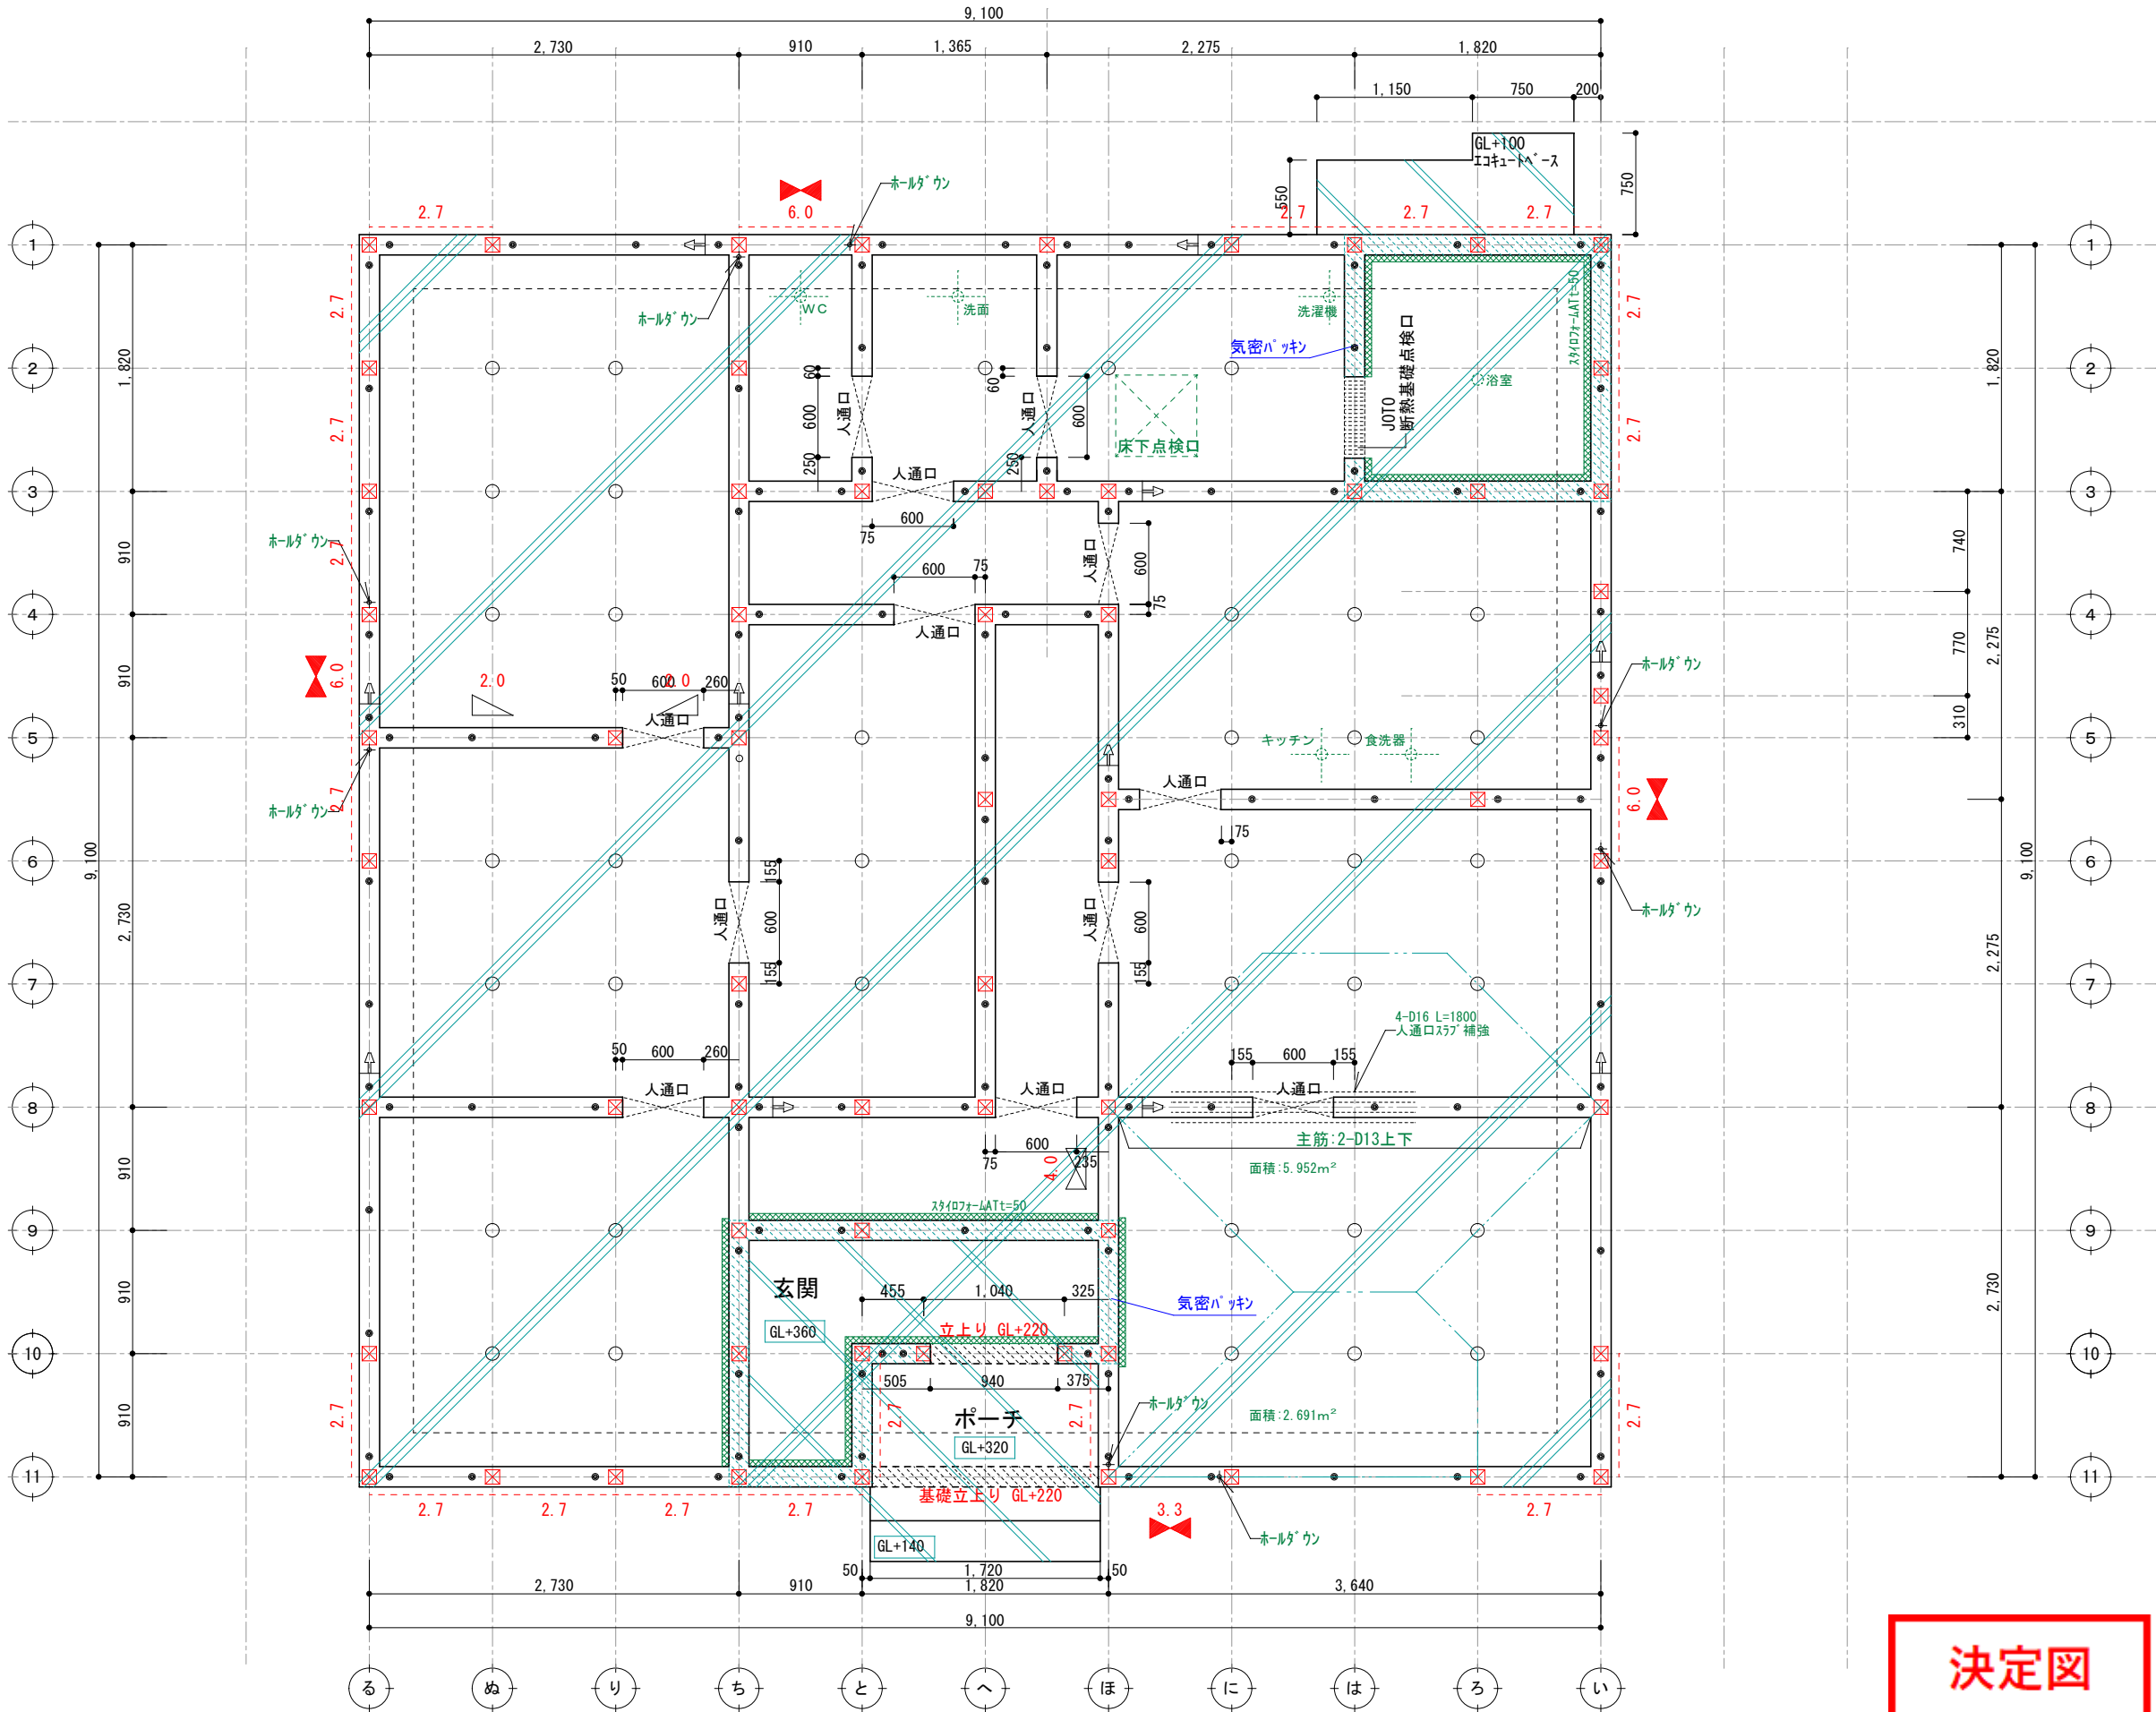


構造体ベースコンクリート t=150

後打ち土間コン

アンカーボルトの配置
土台切れの箇所より150mm
土台の継手及び仕口の端部より150mm
耐力壁の端部、筋交いの脚部より150mm
1.82m以下の間隔
250mm以上埋込み
基礎天端より120mm

筋かい凡例
柱脚 柱頭 片筋かい
たすき掛け筋かい
構造用パネル

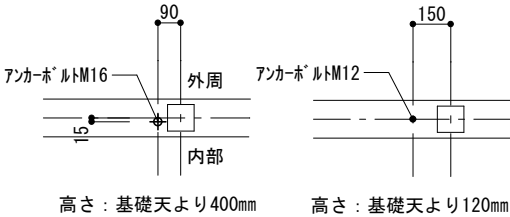

高さ：基礎天より400mm

高さ：基礎天より120mm









ホールダウン用アンカーボルト配置

アンカーボルト配置

凡例
通し柱 (105*105) 管柱 (105*105)
● アンカーボルトM12 L=400
+ ホールダウンアンカーM16 L=800
柱芯より90mm 280mm以上埋め込み
(カナリフィストアンカーボルトM16)
⊕ 鋼製束
→ 土台ジョイント
ベースコンクリート (t=150)
後打ちコンクリート

基礎伏図について特記なき場合に限り下記による。
1. コンクリート：呼び強度 21N/mm²
2. 鉄筋：SD295A
3. 設計地耐力：f_e=20kN/m²
地耐力計測後、不足の場合は相当の改良を行い、満たすものとする。
4. 基礎の位置は、芯振分けとする。
5. 玄関・S/C・UB周囲の基礎天端は気密パッキン施工（網掛け部）とし、その他の基礎天端は基礎パッキン施工とする。
6. 設備配管の屋内への取り入れは基礎立上り部のスリーブによる。

決定図

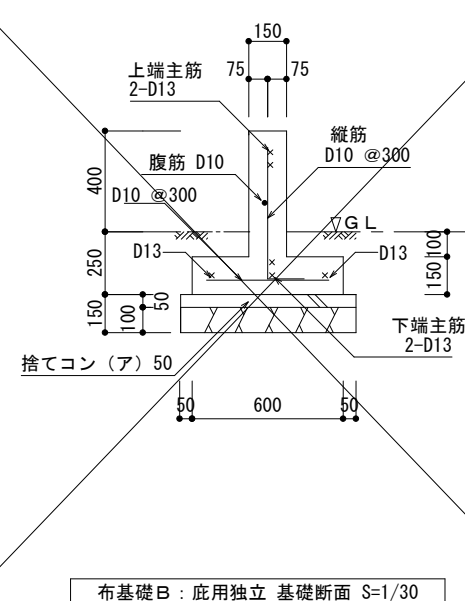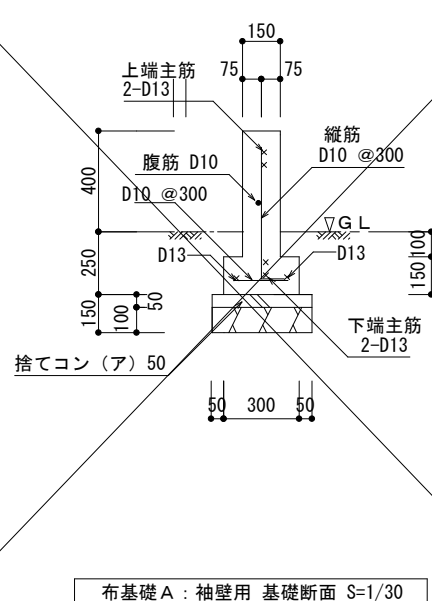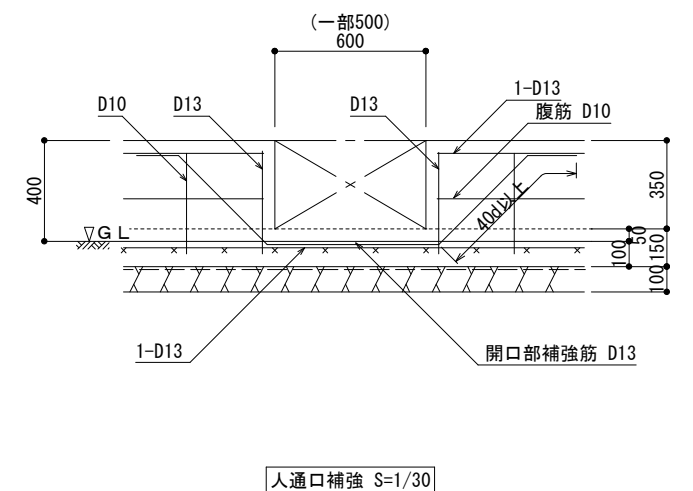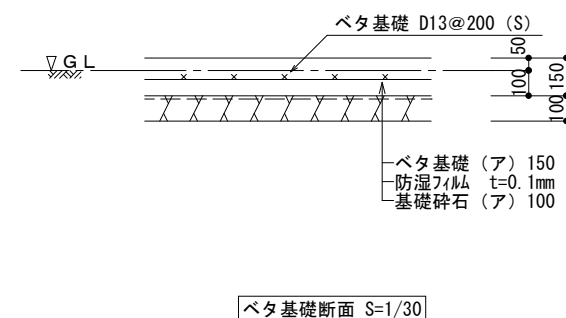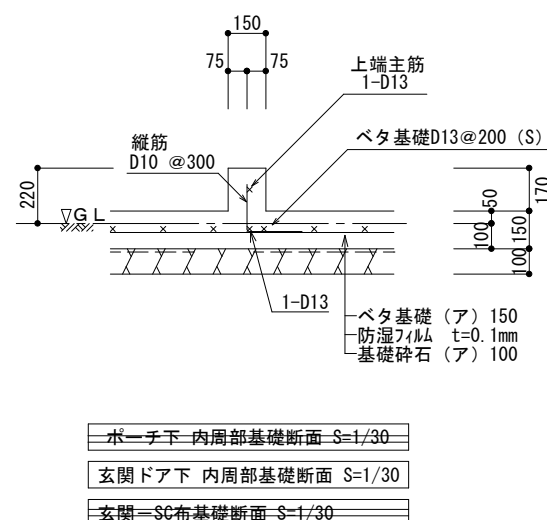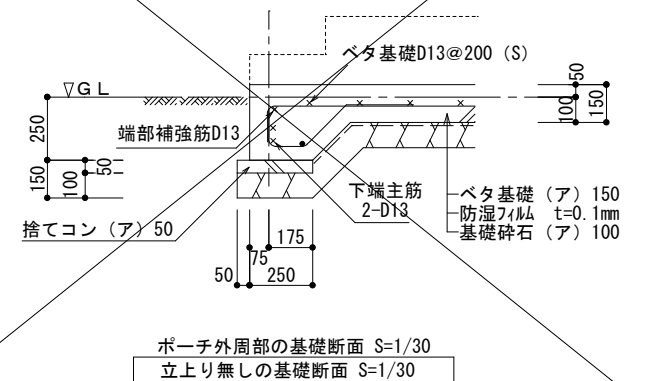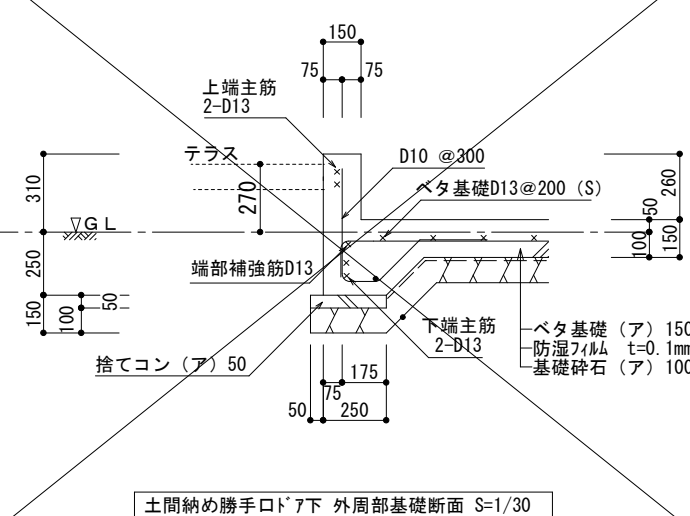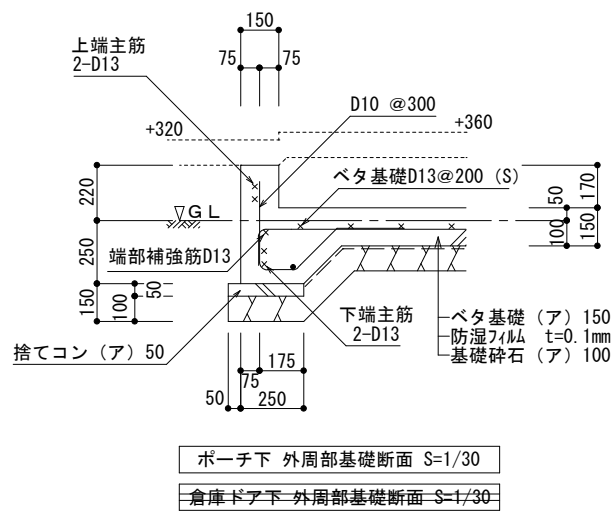

基礎の寸法 及び 配筋の検証方法	基礎立上り 配筋は、 (財) 日本住宅・ 木材技術 センター発行の スパン表 (増補版) による。 ベタ 基礎スラブ 配筋は、 まもりすまい保険設計施工 基準 同解説の ベタ 基礎配筋表 による。具体的な寸法・ 配 筋は基礎詳細図参照。
------------------------	--


鉄筋断面表記

・ D10を示す。

× ・ ・ D13を示す。

※使用しない断面は

決定図

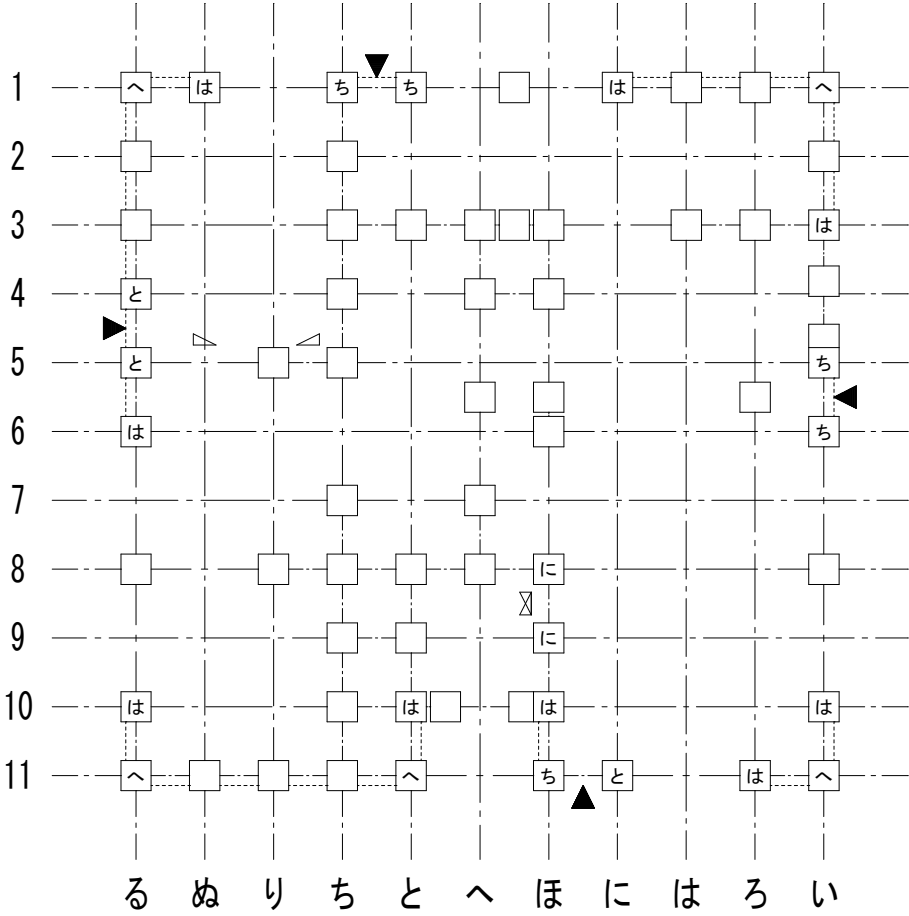

1 階柱壁伏図

接合部凡例				*接合部凡例はユーザ設定されたものです。	
記号	仕様（カナイ金物）		N	倍率	
SBCP	スリムビルドコーナー75, チビクリCK(化粧柱の場合)		0.00	1.00	
SBCP	スリムビルドコーナー75, チビクリCK(化粧柱の場合)		0.65	1.00	
SBCP	は	スリムビルドコーナー75	1.00	1.00	
ARCG	に	アレントコーナー合板用	1.40	2.20	
ARCG	ほ	アレントコーナー合板用	1.60	2.20	
ARCG	へ	アレントコーナー合板用	1.80	2.20	
HD15	と	ブレイブホールダウン B-HD15	2.80	3.60	
HD20	ち	ブレイブホールダウン B-HD20	3.70	4.70	
HD25	り	ブレイブホールダウン B-HD25	4.70	4.80	
HD30	ぬ	ブレイブホールダウン B-HD30	5.60	7.20	
J1	る	腰掛け蟻若しくは大入れ蟻掛け+羽子板ボルト、短冊金物		1.90	
J2	を	腰掛け蟻若しくは大入れ蟻掛け+羽子板ボルト、短冊金物×2		3.00	

※表示なき金物は「は」とする。

梁継手・仕口用

梁継手・仕口用

接合部凡例				*接合部凡例はユーザ設定されたものです。	
記号	仕様（タナカ金物）		N	倍率	
FCP	フックコーナー, チビクリCK(化粧柱の場合)		0.00	1.00	
FCP	フックコーナー, チビクリCK(化粧柱の場合)		0.65	1.00	
FCP	は	フックコーナー	1.00	1.00	
GCP	に	シナコーナー	1.40	2.20	
GCP	ほ	シナコーナー	1.60	2.20	
GCP	へ	シナコーナー	1.80	2.20	
HD15	と	ビス止めホールダウンU HD15	2.80	3.60	
HD20	ち	ビス止めホールダウンU HD20	3.70	4.70	
HD25	り	ビス止めホールダウンU HD25	4.70	4.80	
HD30	ぬ	ビス止めホールダウンU HD15×2 (HD35)	5.60	7.20	
J1	る	腰掛け蟻若しくは大入れ蟻掛け+羽子板ボルト、短冊金物		1.90	
J2	を	腰掛け蟻若しくは大入れ蟻掛け+羽子板ボルト、短冊金物×2		3.00	

※表示なき金物は「は」とする。

梁継手・仕口用

梁継手・仕口用

筋かいの種類に応じた筋かいの端部の接合部の仕様		
	筋かいの種類	接合部の仕様（構造方法）
イ	鉄筋φ9	柱又は横架材を貫通し、三角座金を介してナット締め、又は鋼板添え板を用い鋼板を柱及び横架材にCN90, 8本平打ち
ロ	筋かい:15×90	柱・横架材を欠き込み、柱・横架材双方に対してN65, 5本平打ち
ハ	筋かい:30×90	鋼板添え板t=1.6mmを筋かいに対してボルトφ12及びCN65, 3本平打ち、柱に対してCN65, 3本平打ち、横架材に対してCN65, 4本平打ち。筋かいプレートBP同等品
ニ	筋かい:45×90	鋼板添え板t=2.3mmを筋かいに対してボルトφ12及びスクリュー釘φ4.5L50, 7本平打ち、柱及び横架材に対してスクリュー釘φ4.5L50, 5本平打ち。筋かいプレートBP-2同等品
ホ	筋かい:90×90	柱又は横架材にボルトφ12mmを用いて一面剪断接合

胴差と通し柱の接合部の仕様		
	胴差と通し柱の条件	仕口
T1	通し柱の片側に胴差が来る場合	胴差を柱にかたぎ大入れ短ほぞ差しの上、羽子板ボルト、かね折り金物又は同等以上の仕口
T2	通し柱の両側に胴差が来る場合	胴差を柱にかたぎ大入れ短ほぞ差しの上、短冊金物又は、同等以上の仕口で胴差相互を緊結
T3	通し柱と胴差の接合部の近くに90×90以上の筋かいが来る場合(通し柱が建物の出隅にあるか、筋かい壁が外壁と直交して接する場合)	胴差を通し柱に、15KN用引き寄せ金物を水平に用いて緊結

決定図

① TH32013

アクセントクロス
指示書

G2

壁付け 住宅用火災報知器			数量
H	熱感知器	電池式(単独型)	3
		露出型	
壁付け 住宅用火災報知器			数量
S	煙感知器	電池式(単独型)	1
		露出型	

※ 煙感知器は壁・梁より600mm以上離す
壁に取付ける場合、
天井から150mm以上500mm以内離す
換気扇・エアコン吹出口から1500mm以上離す
※ 全室LED照明とする居室においては調光
制御・非露光型においては人感センサーを
採用する。
※ 特記無きガラスは型ガラス

* 凡例	
□	管柱 (105×105)
△	K's パー (3.30倍 FRM-0641)
△	片筋違い (2.00倍 45×90) (例 左:柱脚 右:柱頭)
△	たすき掛筋違い (4.00倍 45×90)
---	構造用合板 (2.70倍) (t=9 タイプ-EXハイパー)
△	床点検口
△	天井点検口
△	換気扇
△	熱交換換気扇VLR-70

② TH32008

ニットの内面も全て

決定図

アドバンスシリーズ	
スマートデザイン (外部)	
凡例	
①	コンセント 1ヶ所
②	コンセント 2ヶ所
③	コンセント 3ヶ所
①ET	コンセント1ヶ所接地ターミナル付
②ET	コンセント2ヶ所接地ターミナル付
WP	コンセント 防水型
②	エアコン用コンセント
②	200V用コンセント
WP	防雨入替プレート
スイッチ	
③	3路スイッチ
④	4路スイッチ
②	直結電源
TV	テレビ取出口
TEL	電話取出口 (テレホンガイド)
LAN	LAN取出口 (テレホンガイド)
照明	照明
リモコン	リモコン(給湯関係・ルフロ)
メーター	メーター
分電盤	分電盤
チャイム	チャイム

※ACコンセント天井付け
※TVアンテナ工事
※スイッチはFL+1100、コンセントはFL+200

