



●便器床設置面寸法・固定穴寸法

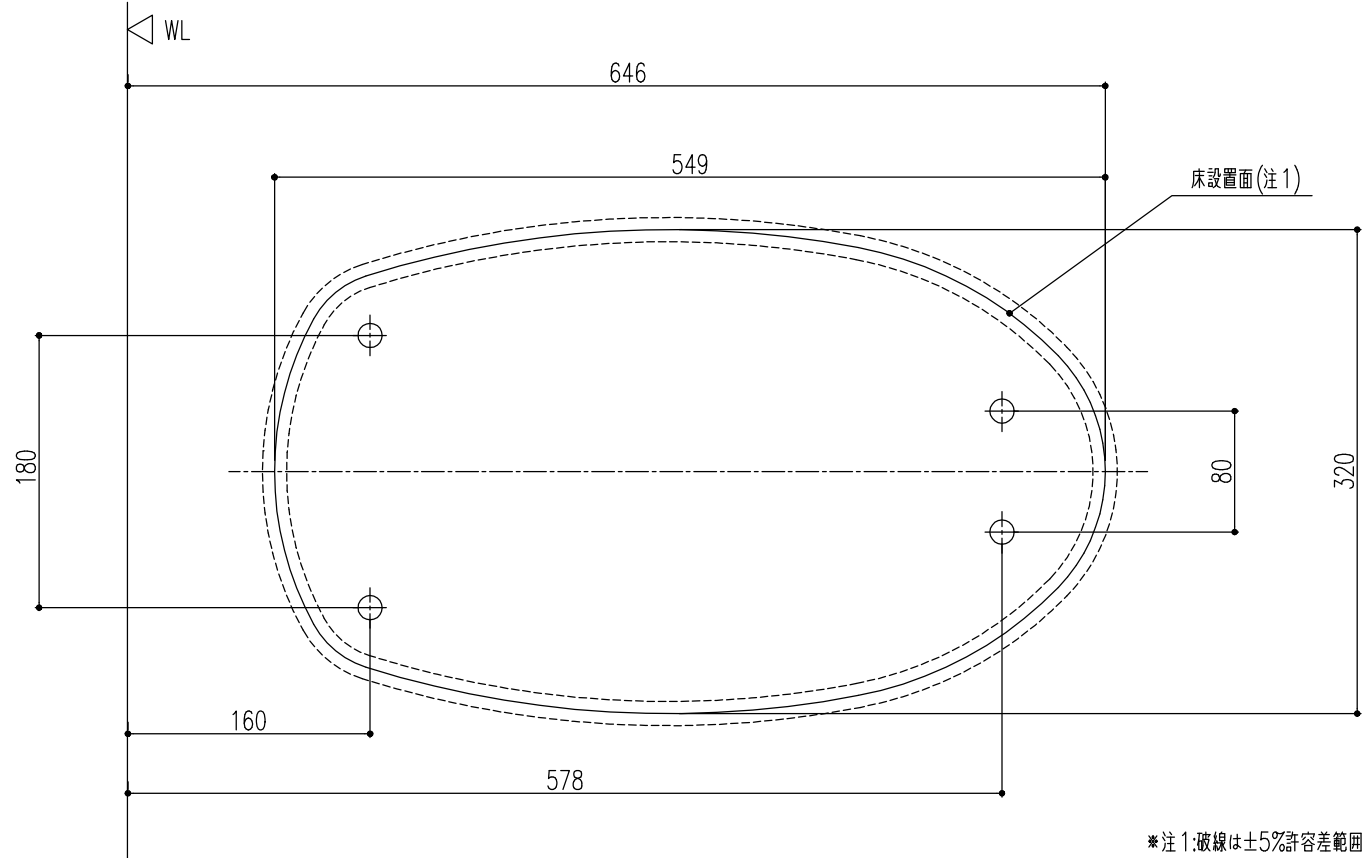

●給排水の位置決めと取出し

給水管、排水管を取り出します。

- ※ 給水管、排水管を施工寸法通りに取り出します。
誤って排水管を壁寄りに取り出した場合は、タンクと壁が干渉して
施工できない恐れがあります。

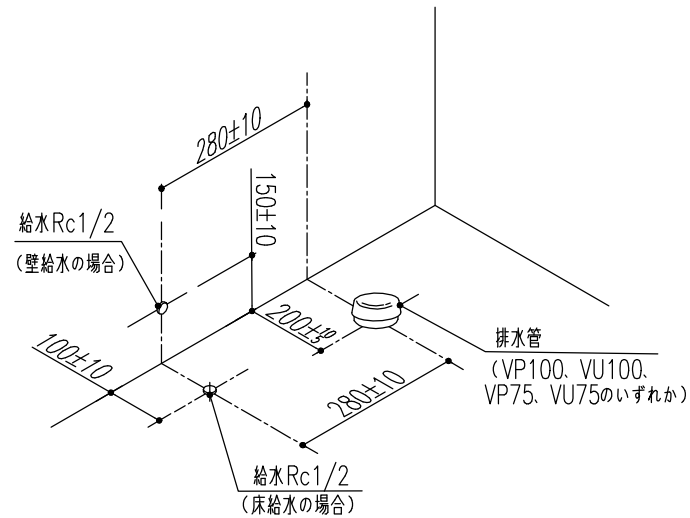


●排水塩ビ管の接続

- * 接続は、塩ビ接着剤にて確実に行なって下さい。
- * 排水管の立ち上げ高さは、必ず $60\pm 5\text{mm}$ の位置で切断してください。

施工方法詳細の動画を以下から読み取ることができます。


- ・ 通信料はおお客様のご負担となります。
- ・ お使いの環境・端末によっては、閲覧できない場合があります。
- ・ 実物と動画のデザインが異なる場合があります。
- ・ 動画内に表示される商品名と品番・デザインが異なる場合がありますが、施工手順に影響ありません。

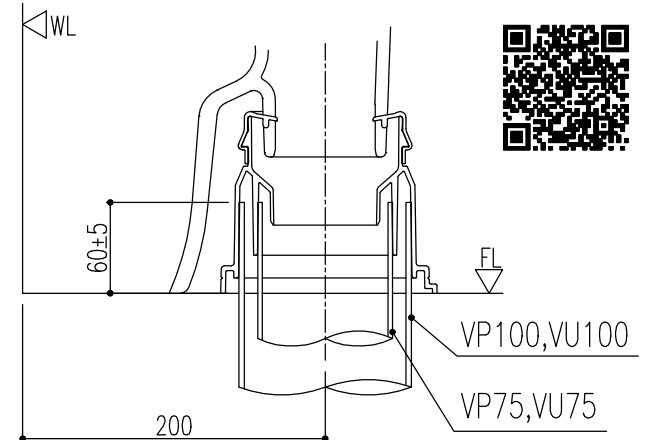

※注…立ち上げ寸法が60mm以下の場合は 既設配管に合った、
市販の60mm立ち上げ用部材(持ち出しニップル)を別途手配ください。
※注…防振シートを組み合わせる場合は5mm高くしてください。


●取付最小スペース

- ※ 最小スペースはA寸法(前出寸法)
+ 400となり、便器排水方向や既設
配管により、異なります。
A寸法は、床排水・床上排水(後抜き)
の場合760mm、床上排水(横抜き)
の場合860mmとなります。
ご確認ください。

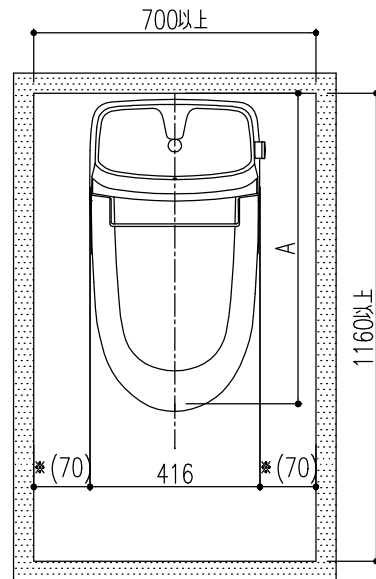


- ※ 右図の空間寸法は、衣服の着脱などの行為に必要な最低寸法です。
- 手すりや紙巻器などの機器を併設する場合は、必要に応じて広い空間が必要になります。
- ※ 便器に向かって左右共に70mm以上の空間を確保してください。

●便フタ開時寸法

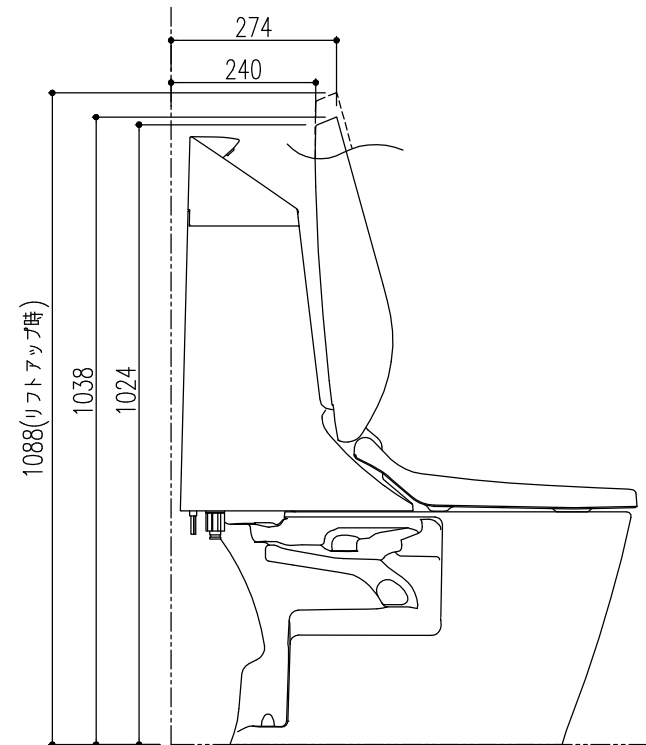


- ※ 上図は代表商品のイメージ図です。
※ 防振シートを組み合わせる場合は、全体が5mm高くなります。

●コフレルスリム(壁付)施工例

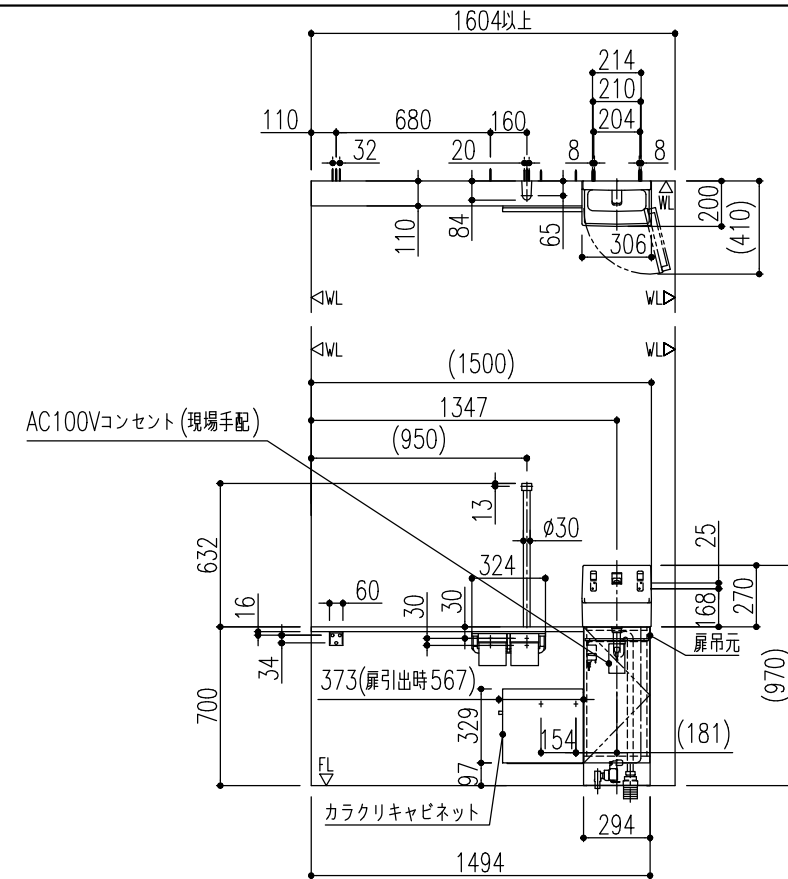

- * この図はR仕様、カウンター1500タイプです。
- * ()内は、参考寸法です。
- * この図は代表商品のイメージ図です。

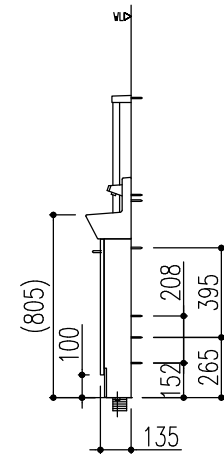

	特記事項	物件名	山本卓也 様邸	案件No.	図面名	担当	図面	図番 : 株式会社 LIXIL
				A2511DDD0EX5N5	機能図	栗野 友仁		
		仕様	ベーシアシャワートイレ／ECO5 床排水 一般地	見積No.	縮尺	日付		
				M25119172542-003-6		2026.01.05		

●コフレルスリム(壁付)給排水・コンセント位置		●補強木位置							
* 下図は1200サイズの場合を示し、 ()内寸法は、1500サイズの場合を示します。 【カウンター長さ注文サイズ対応】 * 下図は1000～1190の場合を示し、 ()内寸法は、1210～1490の場合を示します。 * 自動水栓の場合は下図を参照し、コンセントを設置してください。 * 温水自動水栓の場合は、D種接地工事が必要です。 アースターミナル付接地極付コンセントを使用してください。		* 下図は1200サイズの場合を示し、 ()内寸法は、1500サイズの場合を示します。 【カウンター長さ注文サイズ対応】 * 下図は1000～1190の場合を示し、 ()内寸法は、1210～1490の場合を示します。 * 取付強度を保つために、取付部に下地補強木 (厚さ30mm以上)を入れてください。							
	特記事項	物件名 仕様	山本卓也 様邸 ベーシアシャワートイレノEC05 床排水 一般地	案件No.	図面名	担当	図面	図番	
				A2511DDD0EX5N5	機能図	栗野 友仁		株式会社 LIXIL	
				見積No.	縮尺	日付			
				M25119172542-003-6		2026.01.05			