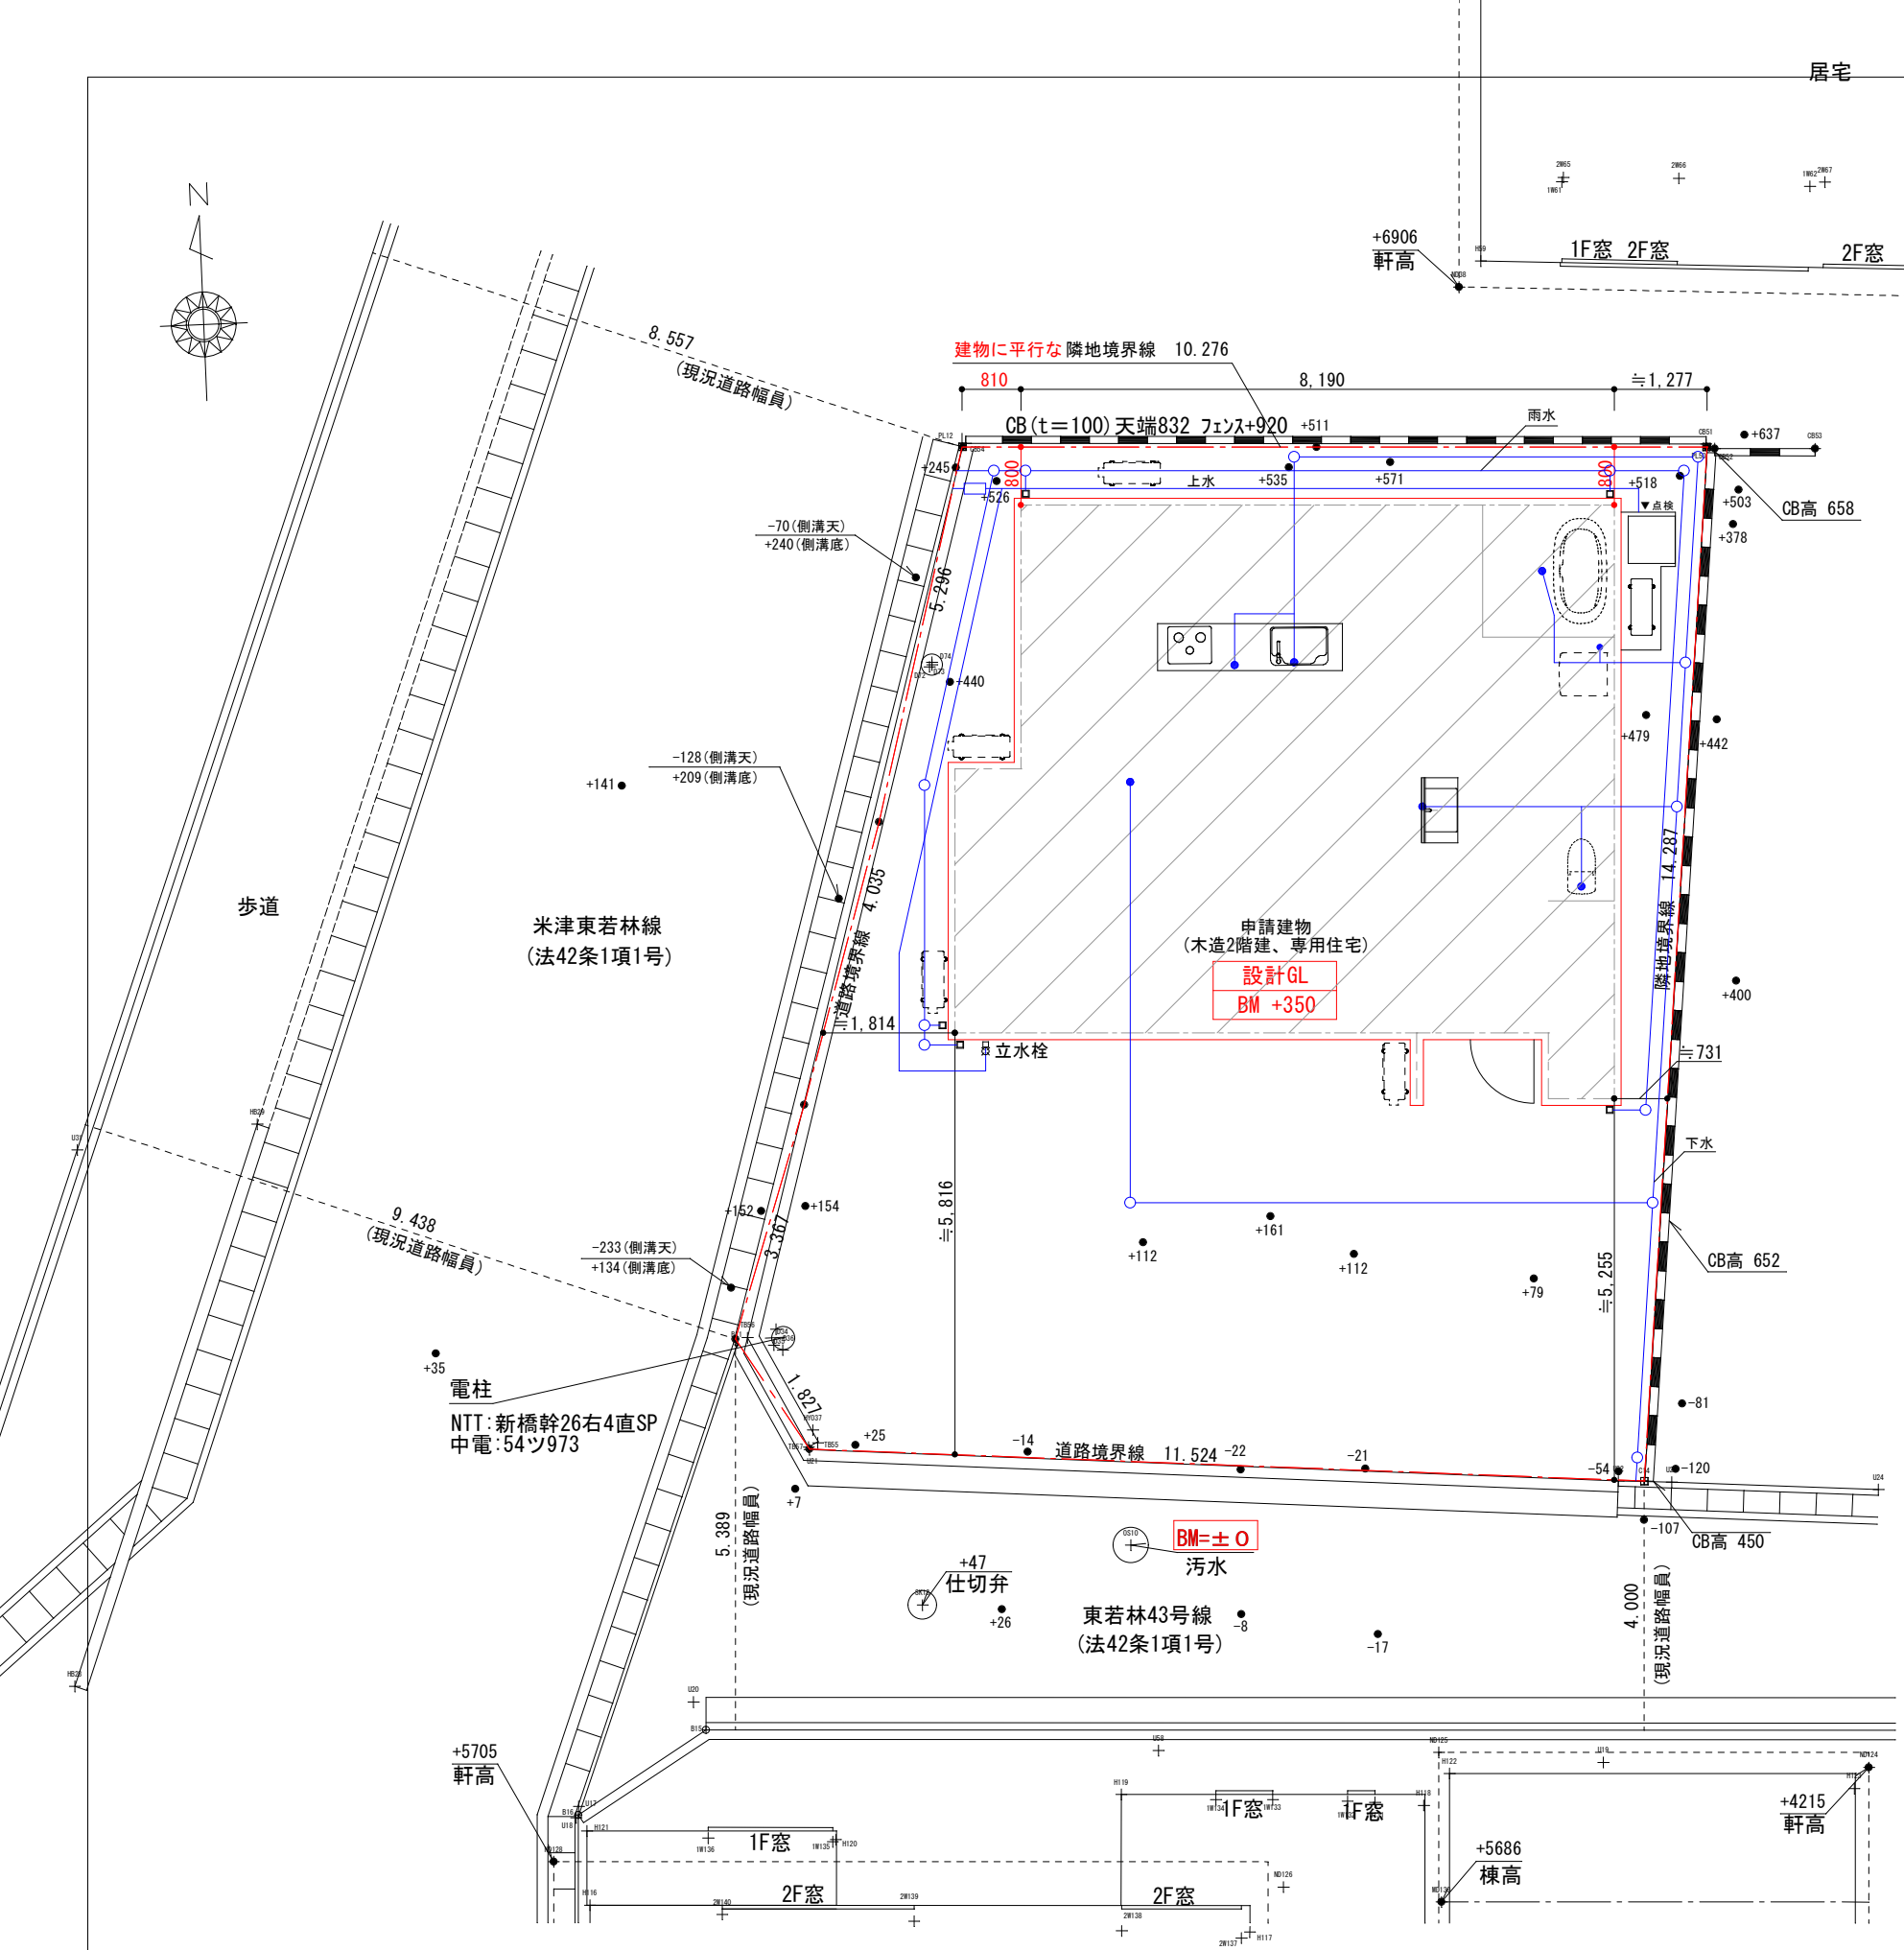


決定図

求積表

地番	1				
NO	X _n	Y _n	Y _{n+1} - Y _{n-1}	X _n × (Y _{n+1} - Y _{n-1})	
313	99.287	109.864	-12.011	-1192.536157	
312	100.956	109.121	0.750	75.717000	
311	103.974	110.614	3.180	330.637320	
310	107.640	112.301	3.709	399.236760	
309	112.536	114.323	12.144	1366.637184	
308	110.762	124.445	6.809	754.178458	
314	96.864	121.132	-14.581	-1412.373984	
合計				321.496581	
合計面積				160.7482905	
地積				160.74	m ²

※この図面は、現地の杭・構造物及び周辺建物を簡易測量し、
法務局備付地積測量図の成果を座標変換し、重ねたものです。
寸法及び面積の相違は座標変換及び数値の丸め方の相違によるものです。