



面

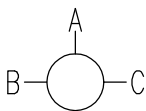


A面

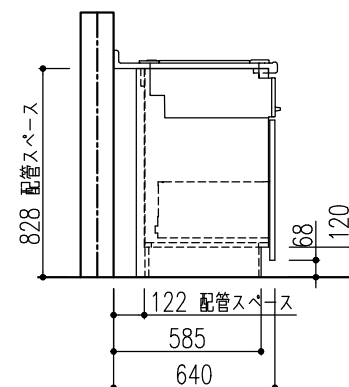

【 ご注意 】

- 壁面仕上材（キッチンパネル・タイルなど）の貼付下端位置が変わります。　〔機能図参照〕
- 記載のキャビネット寸法は扉前面までの呼び寸法です。キャビネット本体の寸法・扉厚み等は商品ガイドの巻末資料をご確認ください。
- 記載のワークトップ、カウンター、エンドパネル、サイドパネルの寸法は呼び寸法です。詳細寸法は商品ガイドの巻末資料をご確認ください。
- レンジフード電源プラグ仕様：3芯電源プラグ（アース工事が必要です。）

案件No.	図面名	担当	図面	図番：
11DDD0EX5N5	レイアウト図	栗野 友仁		株式会社 LIXIL
見積No.	縮尺	日付		
9172542-005-2	1/30	2026.02.19		

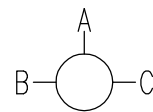

Technical drawing of a kitchen sink unit, showing top and side views with dimensions and numbered callouts.

Top View Dimensions:

- Overall width: 2550 (トップ寸法)
- Left section width: 1050
- Middle section width: 450
- Right section width: 1050
- Overall depth: 850
- Front panel depth: 420
- Top panel depth: 70
- Side panel depth: 60 (食洗用)

Side View Dimensions:

- Overall height: 2400 (CH)
- Bottom section height: 850
- Middle section height: 1700
- Top section height: 850
- Top panel height: 125
- Side panel height: 20
- Front panel height: 125

Internal Dimensions and Callouts:

- Callout 1: 1465 (食洗用) *注1
- Callout 2: 1585 給湯・給水位置 (水栓金具)
- Callout 3: 1950 排水位置 (シンク)
- Callout 4: 270
- Callout 5: 350 (IH用)
- Callout 6: 1130 排水・給湯 (水) 位置 (食洗)
- Callout 7: 2275
- Callout 8: 1805 レンジフード取付位置
- Callout 9: 450 (IH用) *注2
- Callout 10: 295
- Callout 11: 235
- Callout 12: 30
- Callout 13: 210 排気ダクト径150
- Callout 14: 900 製品寸法
- Callout 15: 450
- Callout 16: 125 *注3

Other Labels:

- ファイラ-付13mm
- ファイラ-付20mm

注1) 125V・15A 2極接地極付アースターミナル付コンセント側板取付【専用】
注2) 250V・30A 2極接地極付コンセント 【専用】
注3) レンジフード総高さ(600~900)の時 ダクトカバー範囲(25~325)

【ご注意】



- 壁面仕上材(キッチンパネル・タイルなど)の貼付下端位置が変わります。 [機能図参照]
- 記載のキャビネット寸法は扉前面での呼び寸法です。キャビネット本体の寸法・扉厚み等は商品ガイドの巻末資料をご確認ください。
- 記載のワークトップ、カウンター、エンドパネル、サイドパネルの寸法は呼び寸法です。詳細寸法は商品ガイドの巻末資料をご確認ください。
- 電気・ガス・給排水・換気等は法令・規定に従って有資格者が行ってください。
- 水道工事は排水配管工事となります。
- 取付・設置に際し、各製品の取付・設置説明書や図面の機能図を必ずお読み下さい。
- 内線規程上、各機器のプラグ仕様に関わらず建築側には接地極付コンセントを推奨しています。
- レンジフード電源プラグ仕様: 3芯電源プラグ(アース工事が必要です。)
- 食器洗い乾燥機配管は、給水接続か給湯接続かお客様に確認したうえで施工願います。
- 食洗機内配管の詳細については必ず別添の機能図をご確認ください。

特記事項 扉色 CK6:クリエラスク 取手 「M」スリム取手（ブラック） ワークトップカラー 【AA】スムースドットエンボス	物件名	山本卓矢 様邸	案件No.	図面名	担当	図面	図番 :
			A2511DD0EX5N5	納まり図	栗野 友仁		
	仕様	ES21	見積No.	縮尺	日付		株式会社 LIXIL
			M25119172542-005-2	1/30	2026.02.19		

B面

C面

注4) 125V・15A 2極接地極付アースターミナル付コンセント 【専用】（フード用）

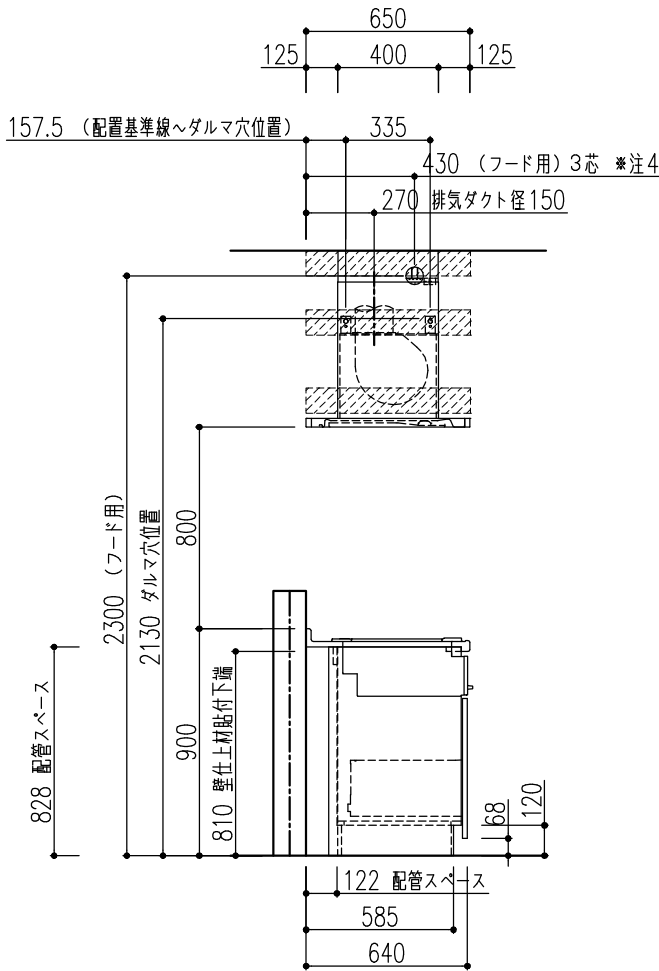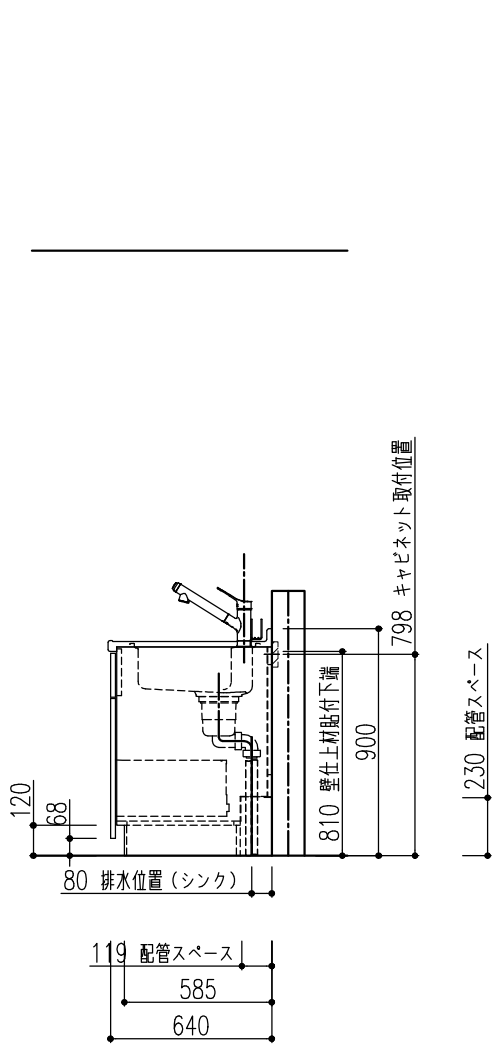

特記事項 扉色 CK6:クリエラスク 取手 [M]スリム取手 (ブラック) ワークトップカラー 【AA】 スムースドットエンボス	物件名	山本卓矢 様邸	案件No.	図面名	担当	図面	図番
	仕様	ES21	A2511DDD0EX5N5	納まり図	栗野 友仁		株式会社 LIXIL
			見積No.	縮尺	日付		
			M25119172542-005-2	1/30	2026.02.19		

■壁面仕上材（キッチンパネル、タイルなど）取付注意事項〔貼付下端位置〕

●キッチンパネルの貼付下端位置

キッチンパネルの貼付下端位置にご注意ください。

キッチンパネル

壁

810mm

(キッチンパネル貼付下端位置)

ワークトップ高さ：850mm以外の場合は、下表を参照してください。

ワークトップ高さ	キッチンパネル貼付下端位置
900	860
875	835
825	785
800	760

●上表はキッチンパネルの場合です。ステンレスパネルの場合は、キッチンパネルの「取付・設置説明書」を参照してください。

《ワークトップ高さ：850mmの場合》

■壁面仕上材（キッチンパネル）取付注意事項〔貼付向き〕

●キッチンパネルの貼付向き

キッチンパネルの貼付向きにご注意ください。

【単位：mm】

レンジフード

ウォールキャビ（開き扉）

クイックポケット
クイックパレット

850

700

880

620

850

700

880

620

850

700

880

620

850

700

880

620

横貼り

縦貼り

フロアキャビ

（ウォールキャビ・レンジフード高さ）

（クイックポケット・パレット用キャビ高さ）

（壁面寸法）

（ワークトップ高さ）

《バックガード：なし、ワークトップ高さ：850mm、ウォールキャビ高さ：700mmの場合》

《キッチンパネル 貼付方向》

総高さ：2350mmの場合

	ウォールキャビ		
	開き扉	クイックポケット クイックパレット	
	H700	H600 H500	H700 (620) H600 (520)
キッチンパネル貼付方向	横	縦	

【ご注意】
リシェル以外のクイックパレットは、キャビネットの背板高さがショート（－80mm）しておりませんので、『開き扉』のキッチンパネル貼付方向に合せてください。

■床の不陸に関して

7mm以下

7mm以下

床の不陸は、7mm以下に抑えるようにしてください。不陸が大きい場合は、現場責任者に床の修正を依頼してください。
※キャビネット取付時には不陸調整スペーサー等で水平になるように設置してください。

■レンジフード取付注意事項（壁面取付時）

レンジフードを取付ける場合は下地の材が厚み30mm以上、幅100mm以上、ビス固定位置が材の端部から25mm以上であることを確認してください。
また、壁強度などの詳細は「レンジフード設置説明書」を必ず事前に確認してください。

取付位置については、取付設置図を確認してください。

参考図_CLS. SER. NST. ASR. ADR. RVJ. GSR. BFRS. TARシリーズ
（※RVJ. GSRシリーズの場合はレンジフードパネルの取付下地は不要です。）

12mm以上の合板または0.8mm以上の鋼板

レンジフード取付下地

100mm

30mm以上

100mm以上

335

【正面】

【側面】

参考図_NBHシリーズ

レンジフード取付下地

30mm以上

100mm以上

【正面】


【側面】

特記事項 扉色 CK6:クリアスク 取手 [M]スリム取手（ブラック） ワークトップカラー 【AA】スムーズドットエンボス	物件名 仕様	山本卓矢 様邸 ES21	案件No.	図面名	担当	図面	図番
			A2511DDD0EX5N5	機能図	栗野 友仁		株式会社 LIXIL
			見積No.	縮尺	日付		
			M25119172542-005-2		2026.02.19		

A3

20260219MNP2-01

■ SMHVRフード

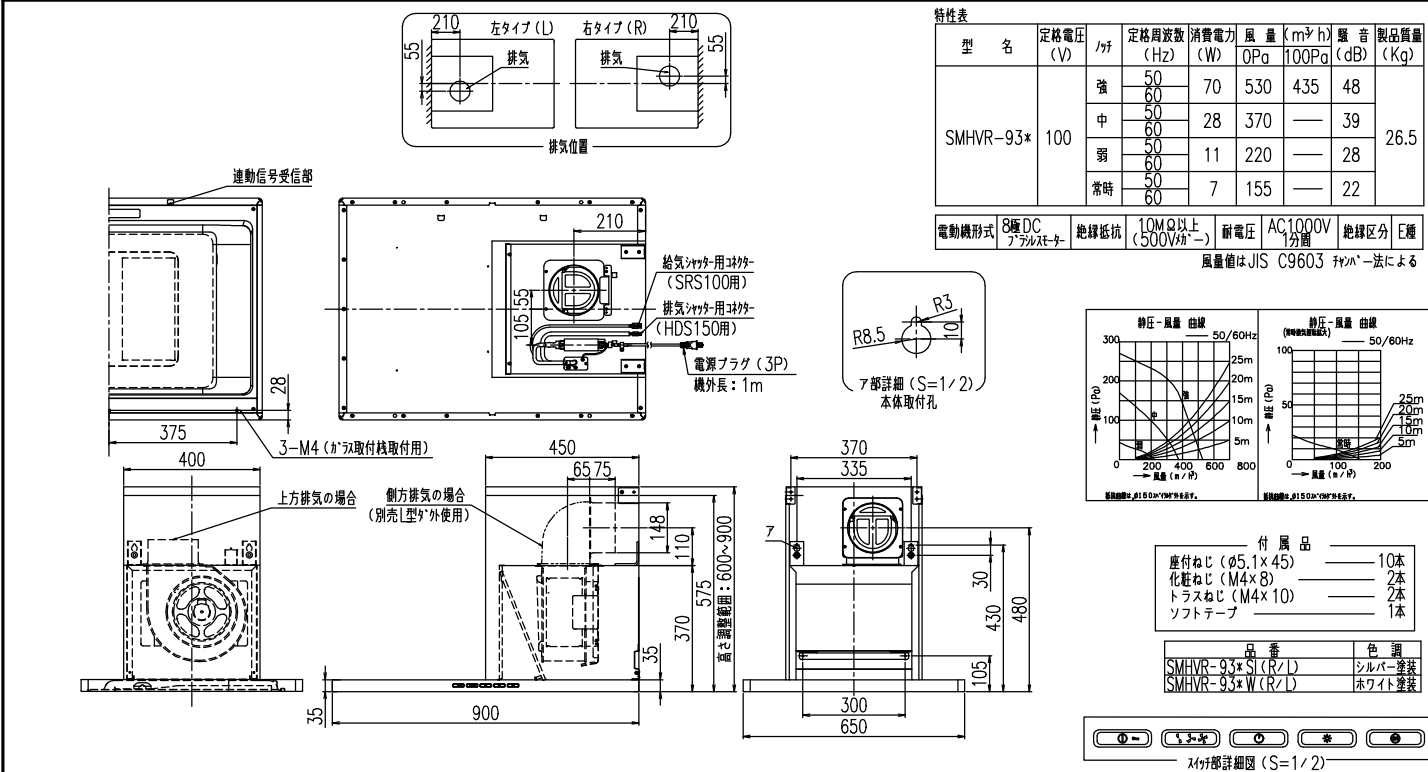


4. 製品名の末尾の()にはワザンシリーズによって記号が入る場合があります。
5. 電動シャッター(HDS150) (別売)を使用時は、中継コネクタを外して取り付けてください。
6. 赤外線連動型インフラ赤外線です。単独でも使用できます。
注) 1. 排気方向は側方(L型)外使用:別売)と上方です。

■ IHヒーター用コンセント推奨位置図 / 壁付設置の場合


※コンセントや電源プラグが、引き出しおよびIHヒーター用仕切板(オプション)に接触しないように注意してください。
※木製キャビネットの配管スペース付キャビネットを使用する場合は点検口裏の配管スペース内にコンセントを設置してください。

キッチン高さ	電源線高さ
800	400
850	450
900	500

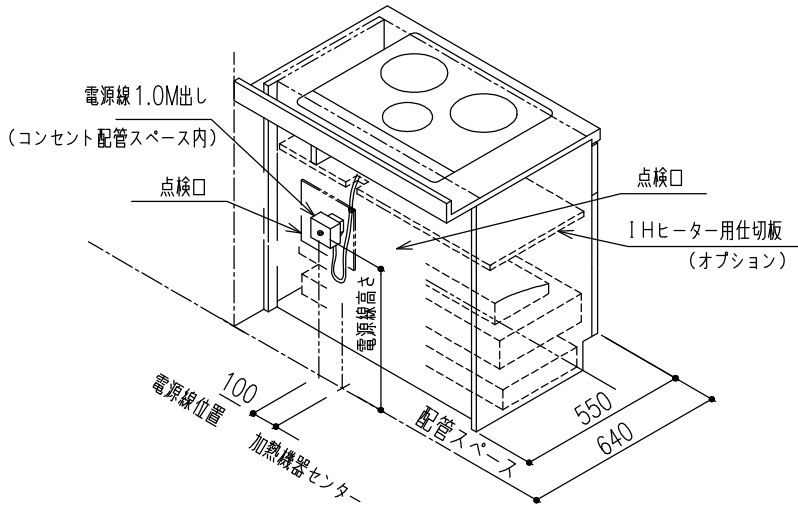

注意:引き出しおよびIHヒーター用仕切板(オプション)に接触しないように上記寸法を参照してください。

■ 食器洗い乾燥機内配管図 床立上げ配管例

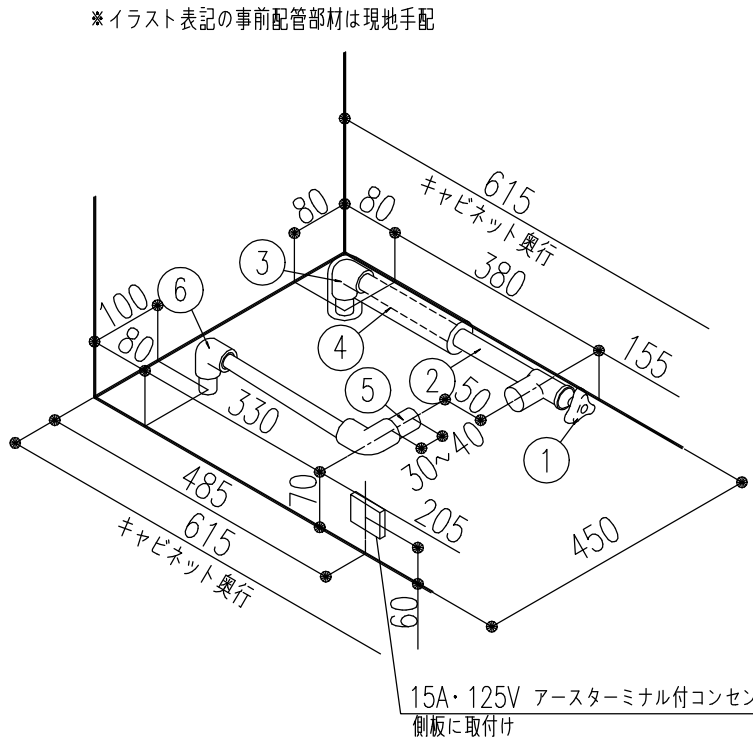

注意:配管立ち上げ位置は必ず本図の位置に立ち上げて下さい。

※給水接続か給湯接続かお客様に確認したうえで施工願います。

給水(給湯の場合は耐熱配管)

①アングル型止水栓(ハンドル式・固定ゴマタイプ)

※必ず固定ゴマタイプをご使用ください。

落としゴマタイプを使用すると、水栓内でコマが移動し、ゴトゴト音を生じる恐れがあります。

②硬質塩化ビニルライニング鋼管(相当品)

③RC1/2ソケット

④断熱材(Φ48)

排水(耐熱塩ビ使用のこと)

⑤排水パイプHT20

⑥HTエルボ


※配水管先端のエルボを上向きにしないでください。

キャビネットに当たるため、排水ホース折れの原因になります。

■ 止水栓図(床立上げ)

床立上げ配管

配管立ち上げ寸法は、止水栓芯までの高さを示しています。

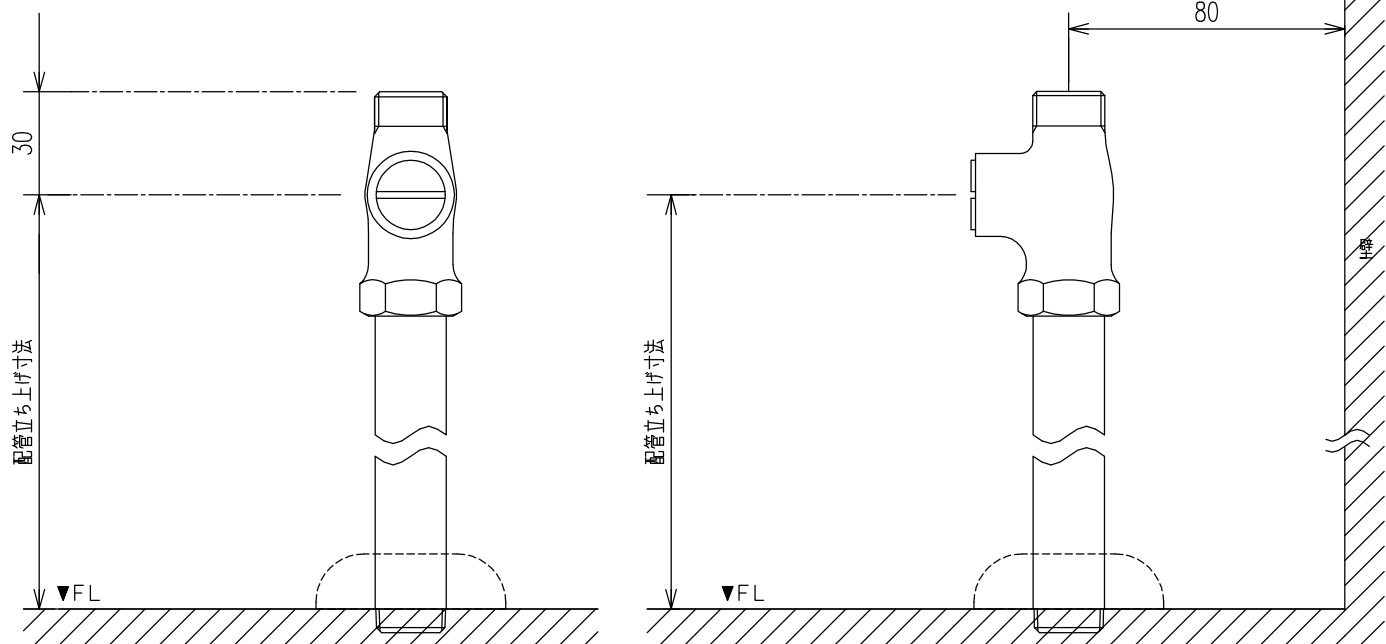

特記事項
扉色 CK6:クリエラスク
取手 [M]スリム取手(ブラック)
ワークトップカラー 【AA】スモースドットエンボス

物件名
仕様

山本卓矢 様邸

ES21

案件No.
A2511DDD0EX5N5
見積No.
M25119172542-005-2

図面名
機能図

担当
栗野 友仁

図面




図番

株式会社 LIXIL

■ キッチン取付者さま向け 動画コンテンツ ■
商品取付けの注意点を2次元コードでご視聴いただけます。
取付日より前に、是非ご確認ください。

1 ページ目




1 $\wedge^0$ — シ

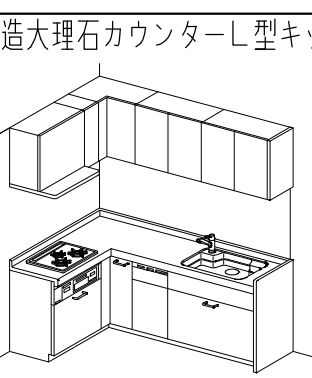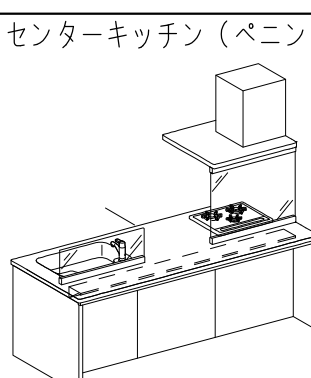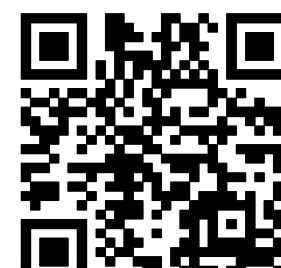人造大理石カウンターL型キッチン   作成日：2024年02月07日	センターキッチン（ペニンシュラ型）   作成日：2024年02月07日		
---	---	--	--

特記事項 扉色 CK6:クリエラスク 取手 [M]スリム取手 (ブラック) ワークトップカラー 【AA】 スムースドットエンボス		物件名	山本卓矢 様邸			案件No.		図面名		担当	図面	図番 : 株式会社 LIXIL
						A2511DDD0EX5N5		機能図		栗野 友仁		
		仕様	E S 2 1			見積No.		縮尺		日付		
						M25119172542-005-2				2026.02.19		

■ キッチン取付者さま向け 動画コンテンツ ■

商品取付けの注意点を2次元コードでご視聴いただけます。
取付日より前に、是非ご確認ください。

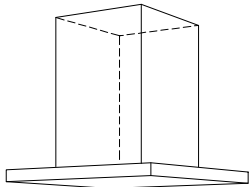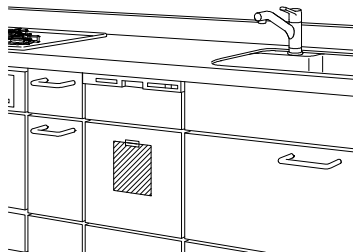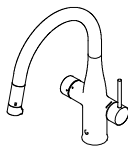センターフード型レンジフード (天吊りフード)  作成日：2024年06月03日 		I H加熱機器関連 I H加熱機器 仕切り板 作成日：2024年02月07日 		食器洗い乾燥機  作成日：2024年02月07日 		ミネラル浄水栓 Greentap  作成日：2024年06月03日 	
特記事項 扉色 CK6:クリアスク 取手 [M]スリム取手 (ブラック) ワークトップカラー 【AA】 スムースドットエンボス	物件名 山本卓矢 様邸 仕様 ES21	案件No. A2511DDD0EX5N5		図面名 機能図	担当 栗野 友仁	図面	図番 ： 株式会社 LIXIL
		見積No. M25119172542-005-2		縮尺	日付 2026.02.19		