


【 ご注意 】

- 記載のキャビネット寸法は扉前面までの呼び寸法です。キャビネット本体の寸法・扉厚み等は商品ガイドの巻末資料をご確認ください。
- 記載のワークトップ、カウンター、エンドパネル、サイドパネルの寸法は呼び寸法です。詳細寸法は商品ガイドの巻末資料をご確認ください。

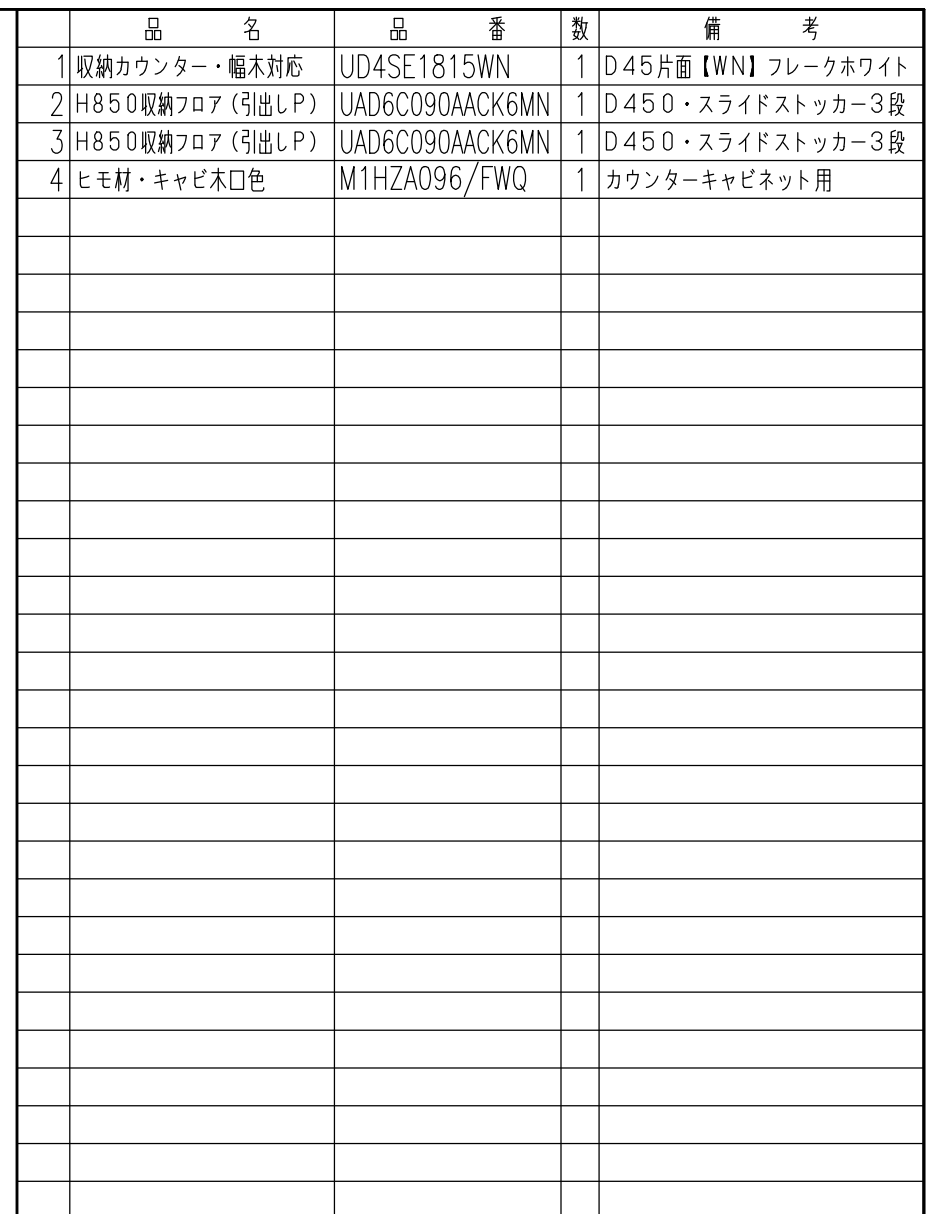


特記事項
扉色 CK6:クリエラスク
取手 [M]スリム取手(ブラック)

物件	山本卓矢 様邸
----	---------

仕様	ES21
----	------

案件No.	図面名	担当	図面	図番 : 株式会社 LIXIL
A2511DDDOEX5N5	納まり図	栗野 友仁		
見積No.	縮尺	日付		
M25119172542-005-3	1/30	2026.02.19		

■ 床の不陸に関して

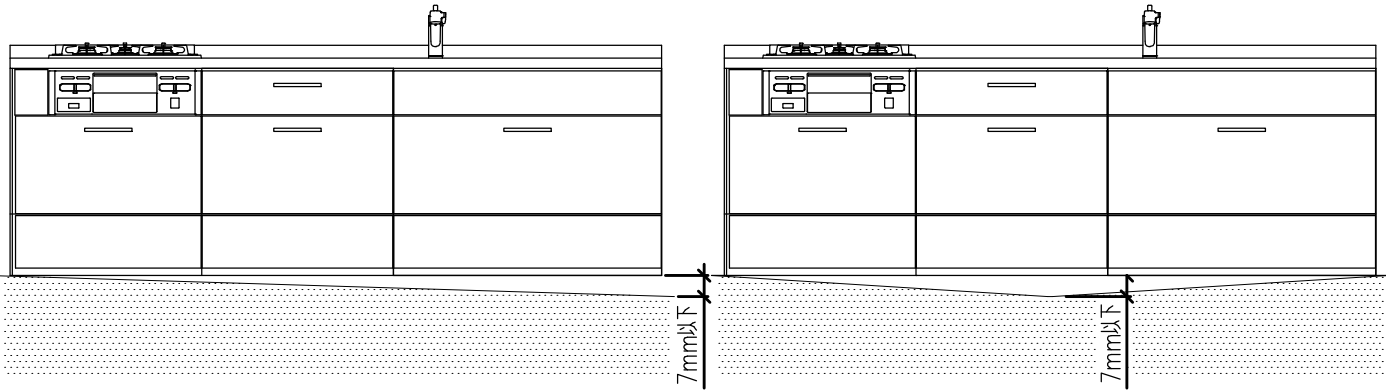

床の不陸は、7mm以下に抑えるようにしてください。不陸が大きい場合は、現場責任者に床の修正を依頼してください。
※キャビネット取付時には不陸調整スペーサー等で水平になるように設置してください。

特記事項 扉色 CK6:クリエラスク 取手 [M]スリム取手（ブラック）	物件名	山本卓矢 様邸	案件No.	図面名	担当	図面	図番
			A2511DDD0EX5N5	機能図	栗野 友仁		株式会社 LIXIL
	仕様	ES21	見積No.	縮尺	日付		
			M25119172542-005-3		2026.02.19		


■ キッチン取付者さま向け 動画コンテンツ ■

商品取付けの注意点を2次元コードでご視聴いただけます。

取付日より前に、是非ご確認ください。

荷扱い・搬入


荷扱い・搬入

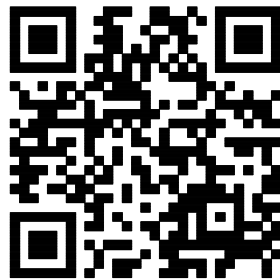

作成日：2024年10月01日



カウンター開梱搬入「養生ツール」

カウンター開梱搬入 「養生ツール」のご紹介

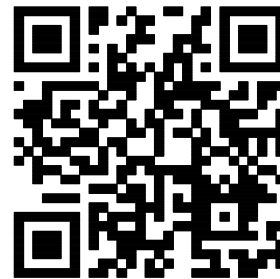

作成日：2024年10月01日
改定日：2025年12月11日

不陸の確認と調整

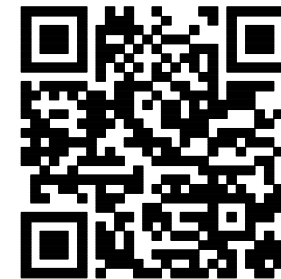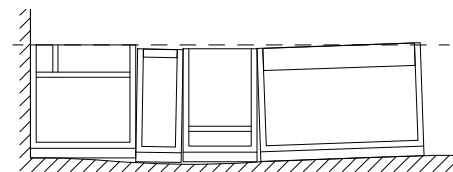

作成日：2024年02月07日



マグネットキッチンパネル

マグネット キッチンパネル 「取付・設置」ポイント





作成日：2024年03月06日

人造大理石カウンターL型キッチン

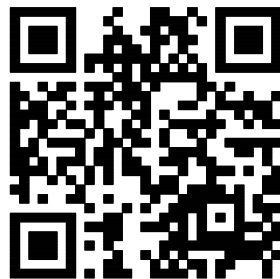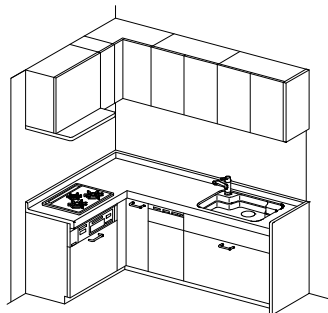

作成日：2024年02月07日




センターキッチン（ペニンシュラ型）

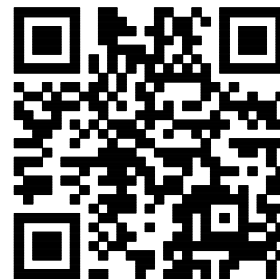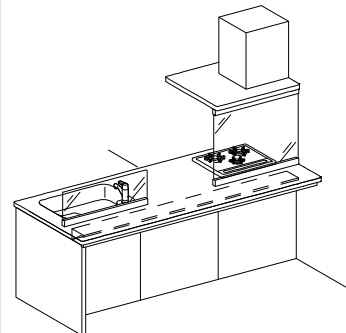

作成日：2024年02月07日

特記事項 扉色 CK6:クリエラスク 取手 [M]スリム取手（ブラック）	物件名	山本卓矢 様邸	案件No.	図面名	担当	図面	図番 ：
			A2511DDD0EX5N5	機能図	栗野 友仁		
	仕様	ES21	見積No.	縮尺	日付		株式会社 LIXIL
			M25119172542-005-3		2026.02.19		

■ キッチン取付者さま向け 動画コンテンツ ■
商品取付けの注意点を2次元コードでご視聴いただけます。
取付日より前に、是非ご確認ください。

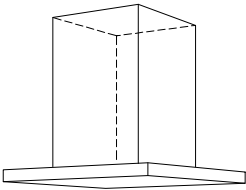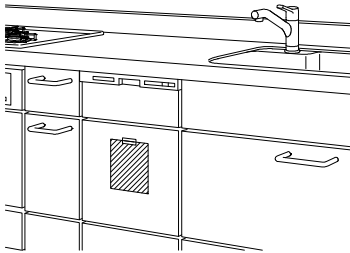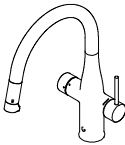センターフード型レンジフード (天吊りフード)  作成日：2024年06月03日 	I H加熱機器関連 I H加熱機器 仕切り板 作成日：2024年02月07日 	食器洗い乾燥機  作成日：2024年02月07日 	ミネラル浄水栓 Greentap  作成日：2024年06月03日 
---	--	--	---

--	--	--	--

--	--	--	--

特記事項 扉色 CK6:クリアスク 取手 [M]スリム取手（ブラック）	物件名	山本卓矢 様邸	案件No.	図面名	担当	図面	図番
	仕様		A2511DDD0EX5N5	機能図	栗野 友仁		株式会社 LIXIL
		ES21	見積No.	縮尺	日付		
			M25119172542-005-3			2026.02.19	