


●便器床設置面寸法・固定穴寸法		●給排水の位置決めと取出し		●排水塩ビ管の接続					
		給水管、排水管を取り出します。 ※ 給水管、排水管を施工寸法通りに取り出します。 誤って排水管を壁寄りに取り出した場合は、タンクと壁が干渉して施工できない恐れがあります。		※ 接続は、塩ビ接着剤にて確実に行なって下さい。 ※ 排水管の立ち上げ高さは、必ず60±5mmの位置で切断してください。 施工方法詳細の動画を以下から読み取ることができます。 ・ 通信料はお客様のご負担となります。 ・ お使いの環境・端末によっては、閲覧できない場合があります。 ・ 実物と動画のデザインが異なる場合があります。 ・ 動画内に表示される商品名と品番・デザインが異なる場合がありますが、施工手順に影響ありません。 ※注…立ち上げ寸法が60mm以下の場合は 既設配管に合った、市販の60mm立ち上げ用部材(持ち出しニップル)を別途手配ください。 ※注…防振シートを組み合わせる場合は5mm高くしてください。					
●取付最小スペース		●便フタ開時寸法		●トイレ空間の条件					
※ 最小スペースはA寸法(前出寸法) + 400となり、便器排水方向や既設配管により、異なります。 A寸法は、床排水・床上排水(後抜き)の場合760mm、床上排水(横抜き)の場合860mmとなります。 ご確認ください。 ※ 右図の空間寸法は、衣服の着脱などの行為に必要な最低寸法です。 手すりや紙巻器などの機器を併設する場合は、必要に応じた広い空間が必要になります。 ※ 便器に向かって左右共に70mm以上の空間を確保してください。		※ 上図は代表商品のイメージ図です。 ※ 防振シートを組み合わせる場合は、全体が5mm高くなります。		壁からキャビネット端までの距離 110mm以上 ※ 110mmを下回ると扉が壁に当たり、キズなどのおそれ ※ 便器向かって左設置の場合も110mm以上推奨 便器先端からキャビネット端までの距離 100mm以上 取付壁から便器中心までの距離 380mm以上 ※ カウンター付きの場合 380mm以上 460mm以下 壁床面の不陸 3mm/2m以下 扉開閉範囲 410mm 奥行 ※ カウンター付きの場合 1500サイズ: 1604mm以上 1200サイズ: 1304mm以上					
特記事項		物件名	山本卓矢 様邸		案件No.	図面名	担当	図面	図番
		仕様	ベージャシャワートイレノEC05 床排水 一般地		A2511DDD0EX5N5	機能図	栗野 友仁		株式会社 LIXIL
					見積No.	縮尺	日付		
					M25119172542-005-6		2026.02.19		


●キャビネット固定の条件

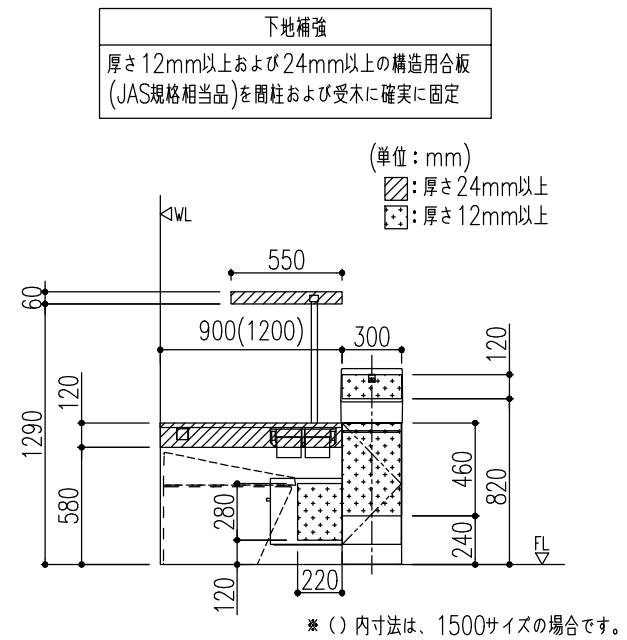

石こうボード等のボード張り
厚さ9.5mm以上～12.5mm以下を想定
【厚さが範囲外の場合】
想定厚さとの差分だけ短いねじもしくは、長いねじを別途用意


●窓枠などの条件

- 周辺部材(鏡・リモコンなど)を取り付ける場合は、周辺部材の説明書を参照してください。
- 壁に窓枠や腰壁の見切り、タイルの貼りはじめなどの突起物がある場合、手洗器の脱着のために、下図のような制約がきます。

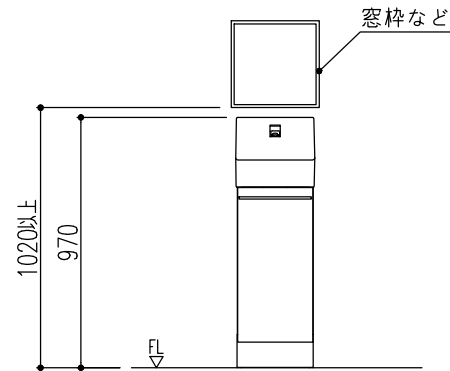

●給排水の条件

- 図の位置に給排水管が立ち上がっていることを確認してください。
■壁排水の場合、市販の排水アダプター(φ25管用)を手配してください。

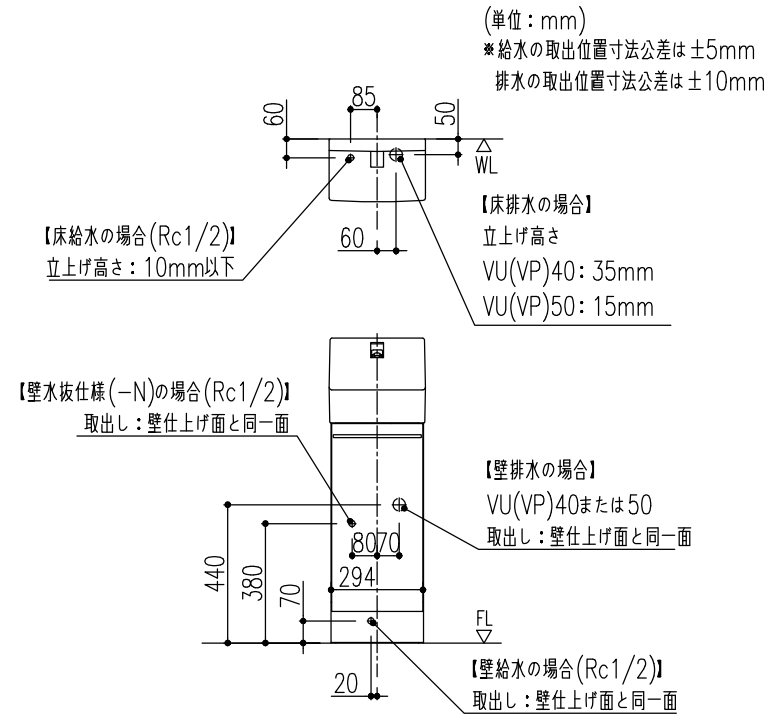


給水圧力
【ハンドル水栓・自動水栓の場合】 最低必要圧力(流動時): 0.05MPa 最高圧力(静止時) : 0.75MPa
【温水自動水栓の場合】 最低必要圧力(流動時): 0.10MPa 最高圧力(静止時) : 0.75MPa

※給水圧力が条件から外れると、流量が確保・制御できず快適に使えなかったり、製品が破損して漏水したりなど不具合の原因になります。

●施工FAQのご案内


- ”現場での困った”をFAQとしてまとめた資料です。
 下記の二次元コードから読み取り、ぜひご利用ください。

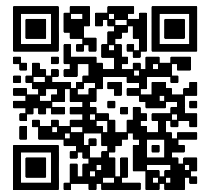

- ※ 通信料はお客様のご負担となります。
- ※ お使いの環境・端末により閲覧できない場合があります。
- ※ 実物と資料内のデザインが異なる場合があります。

●コンセンソの条件

- 配管工事およびコンセントの設置は、下記に準じた工事を電気工事店にご依頼ください。

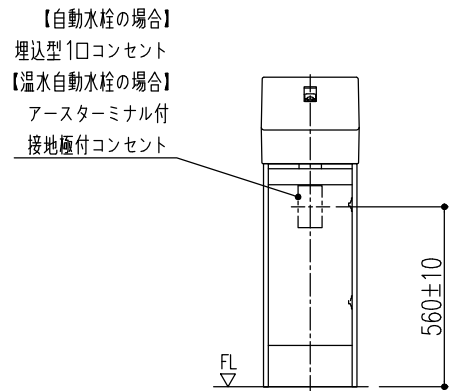


コンセント

AC100V、定格消費電力（下記参照）に適したコンセントを使用する
 温水自動水栓の場合は、アースターミナル付接地極付コンセントを使用する
 （自動水栓用のコンセントは電気温水器に搭載）
 ・自動水栓の場合 ：2.0W ・温水自動水栓の場合：350W
 定格消費電力に適した配線を行う
 必ずアースターミナルは、D種接地工事に準じた工事を行い、確実に
 電気温水器のアース線を接続する
 【上記以外のコンセントが施設されている場合】
 上記条件のコンセントに変更する

●巾木の条件

- キャビネットを設置する範囲には、巾木を設置しないでください。

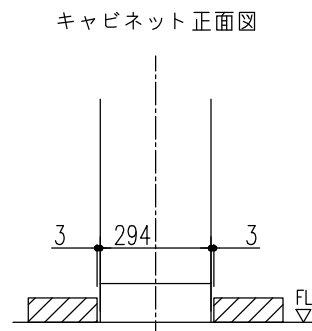

巾木
【キャビネット背面壁に巾木がある場合】 294mm+左右に3mmずつカットする 【手すりカウンターサニタリーボックス付キャビネットタイプの場合】 高さ95mm以下

※製品設置後に巾木を取り付ける場合は、キャビネットと巾木との間にすき間は必要ありません。

	特記事項	物件名	山本卓矢 様邸	案件No.	図面名	担当	図面	図番 : 株式会社 LIXIL
				A2511DDD0EX5N5	機能図	栗野 友仁		
		仕様	ベーシアシャワートイレ／EC05 床排水 一般地	見積No.	縮尺	日付		
				M25119172542-005-6		2026.02.19		