




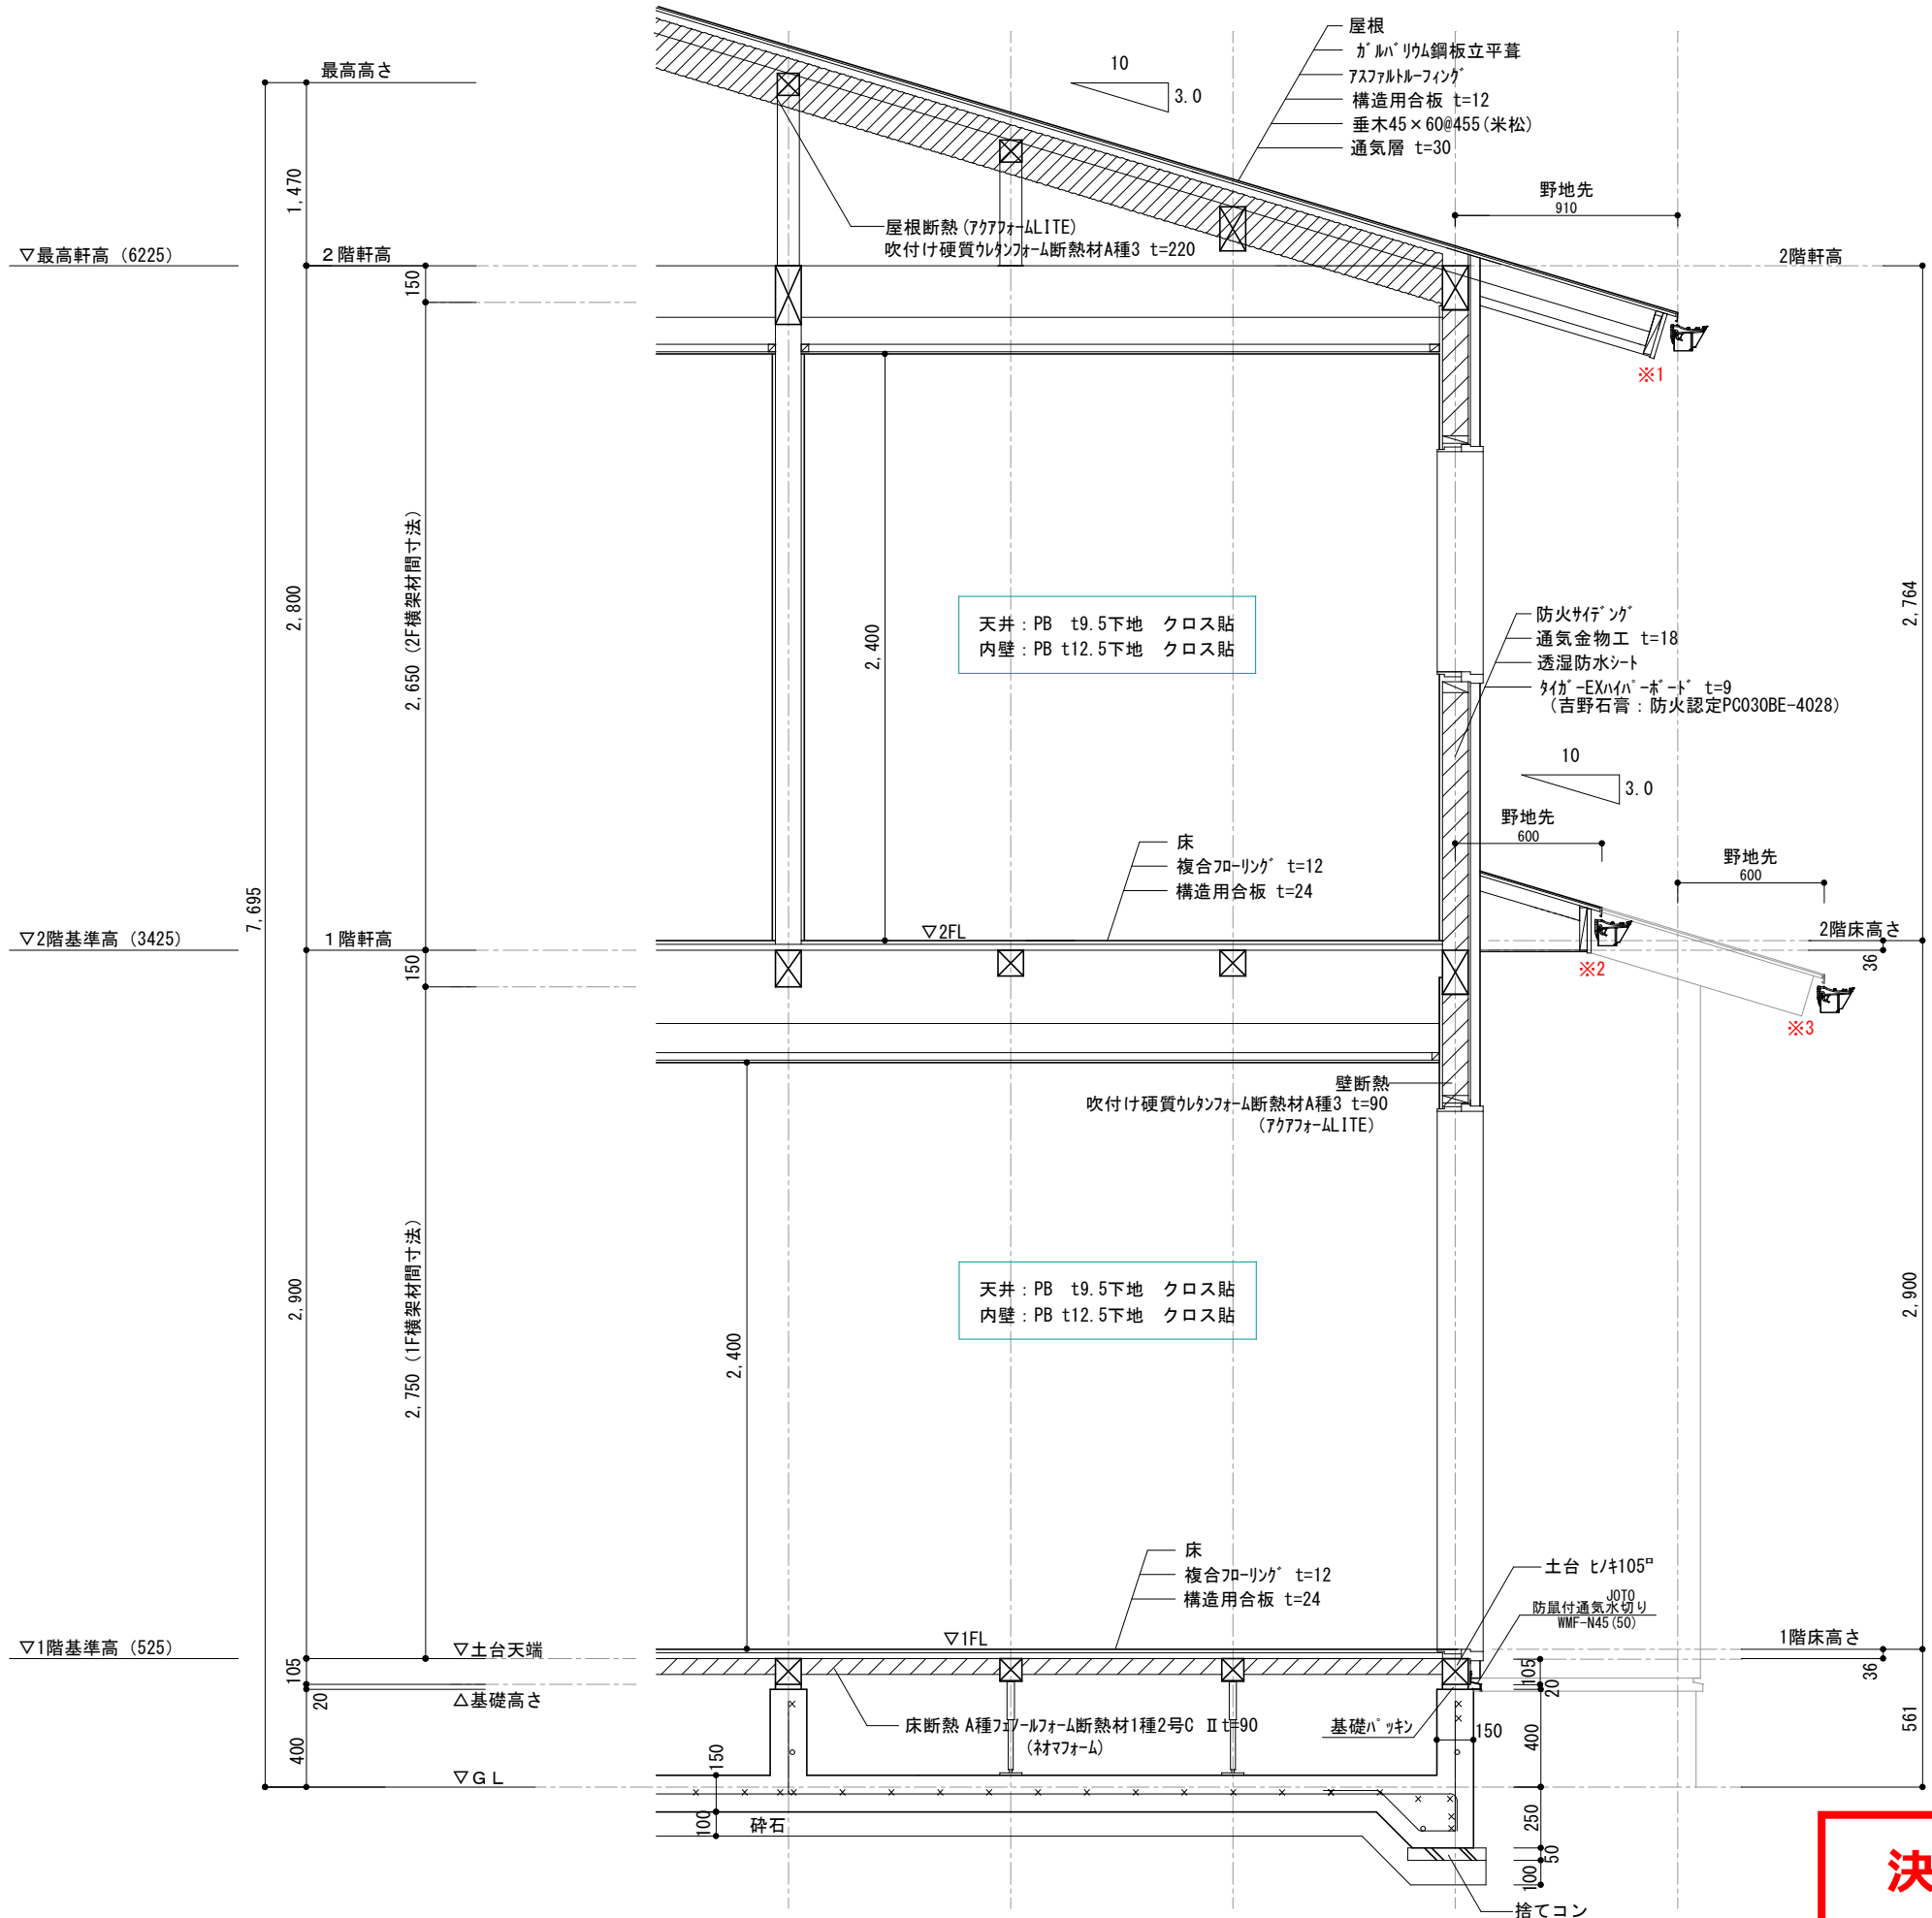


太陽光パネル有 G-2

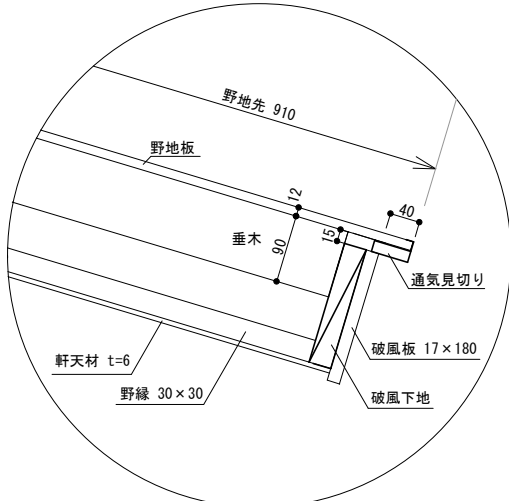

※1 軒先 納まり

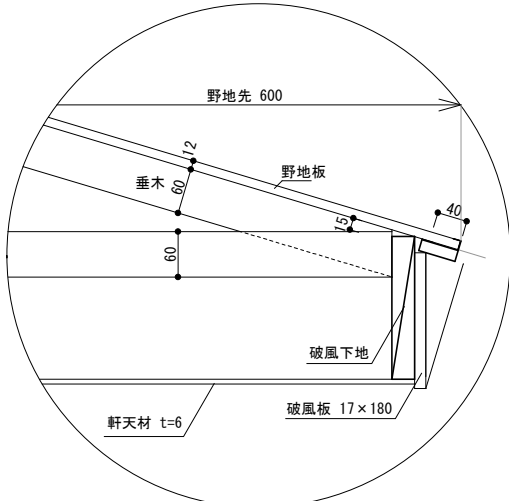

※2 軒先 納まり

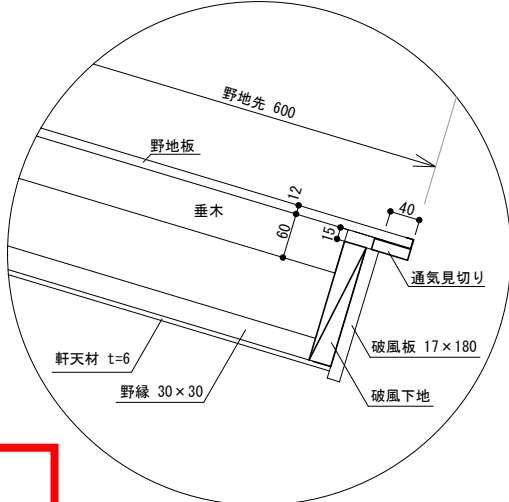

※3 軒先 納まり

決定図

訂正	浜岡一級総合設計事務所		株式会社 LIFEFUND InDesign office 一級建築士事務所	年月日 2025. 12. 28	件名 山本卓矢様 寛子様 邸新築工事	設計	IC	工事	図番
	一級建築士事務所 静岡県知事登録第 (10)2441 号								
	一級建築士 大臣登録第 365879 号 西原利昌								
			事務所登録 (2) 第7595号 一級建築士登録 第179770号 鈴木 達男	縮尺 1/30	図名 矩計図	酒井		青島	5