




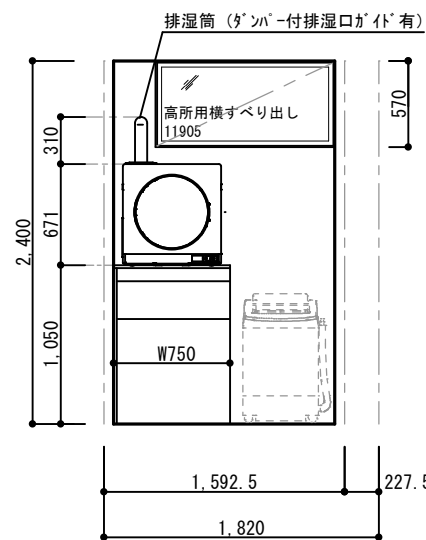


脱衣ランドリー 東面

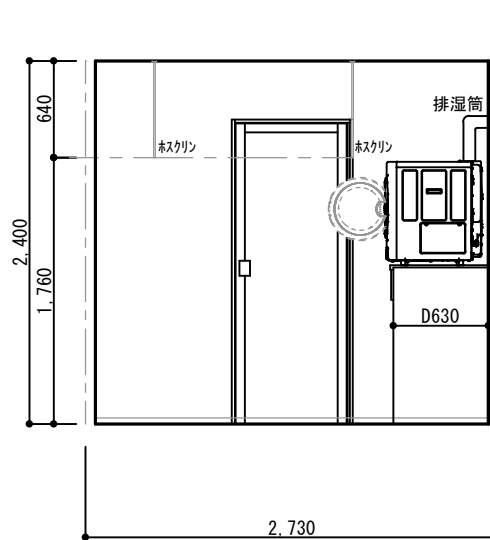


脱衣ランドリー 北面

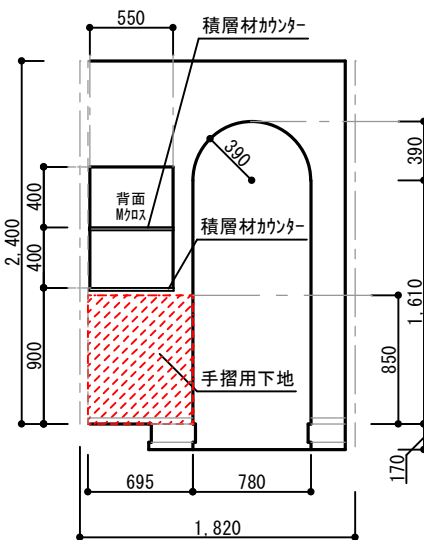


玄関 東面

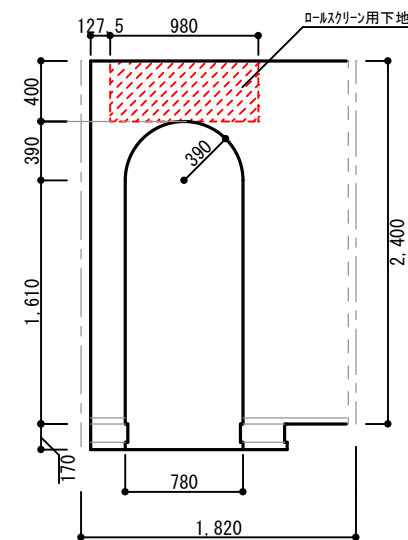


SC 東面

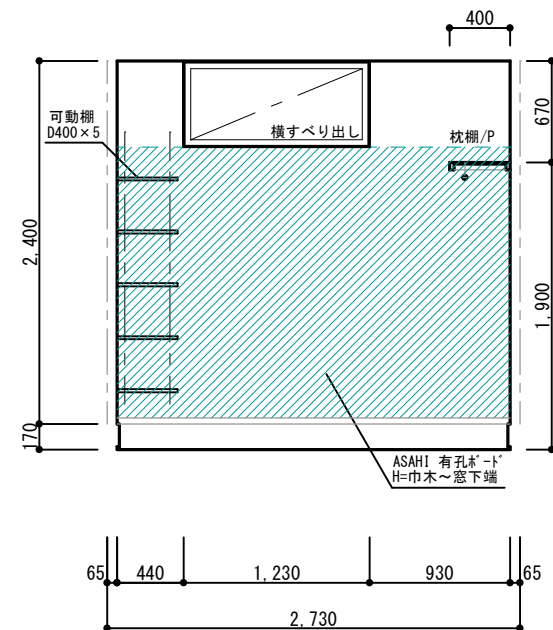

SC 東面

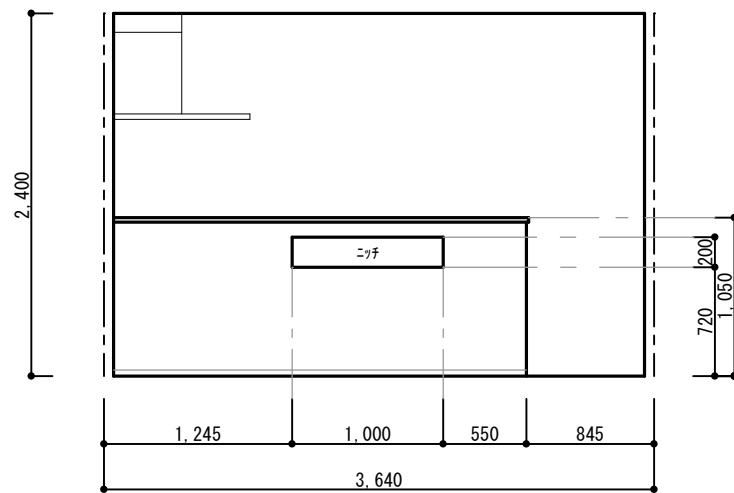


キッチン 南側

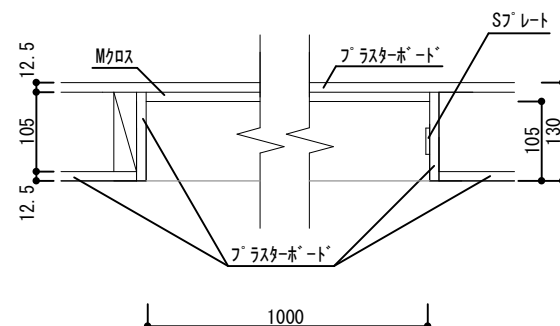


※ニッチ内部は全面クロス仕上げ


キッチン ニッチ 上部断面図

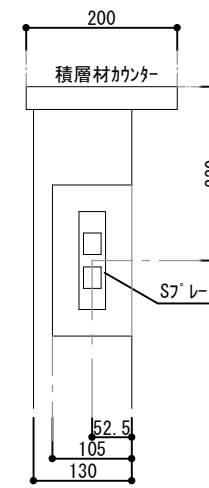


キッチン ニッチ 断面図

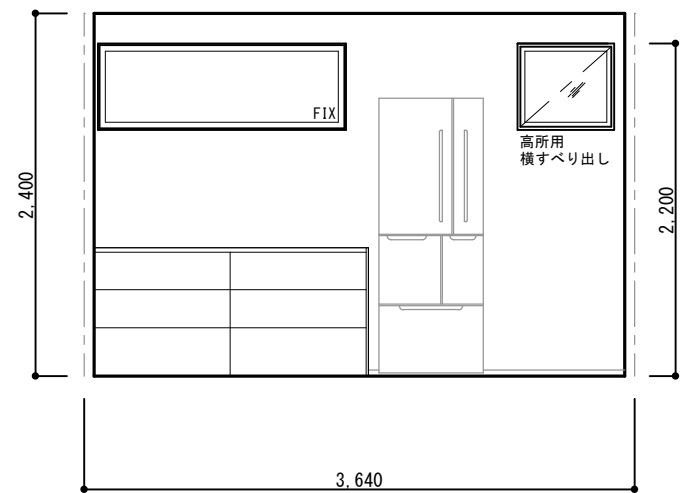


LDK 北面

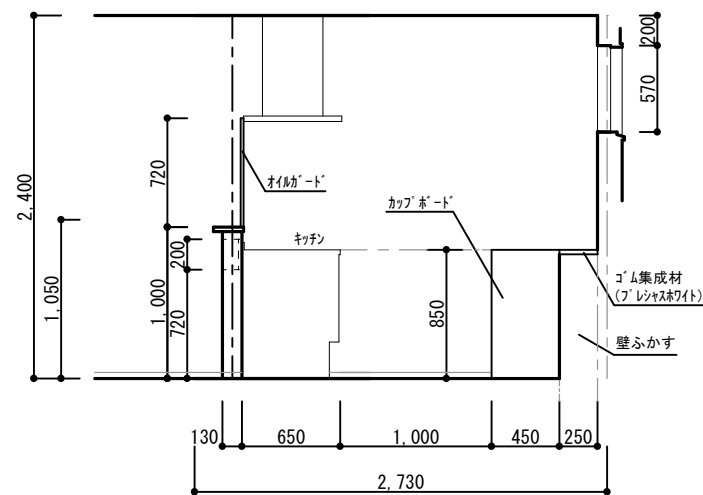


キッチン 西面

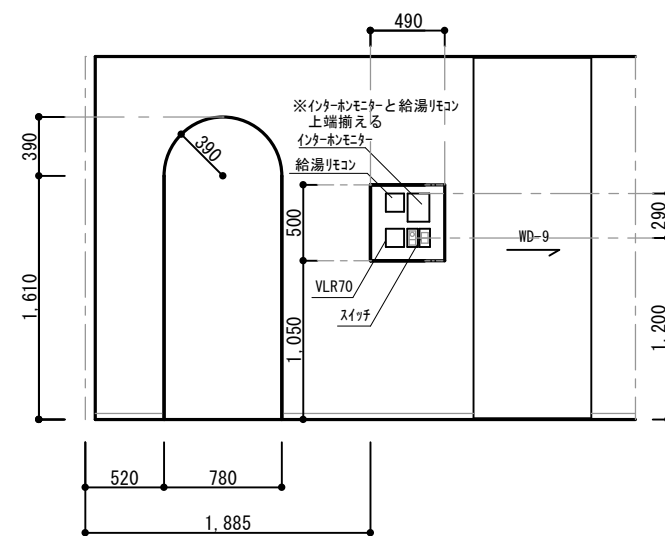

LDK 東面

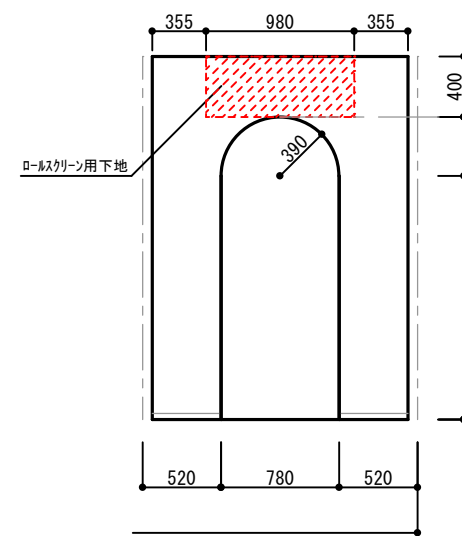

ハントリー 西面

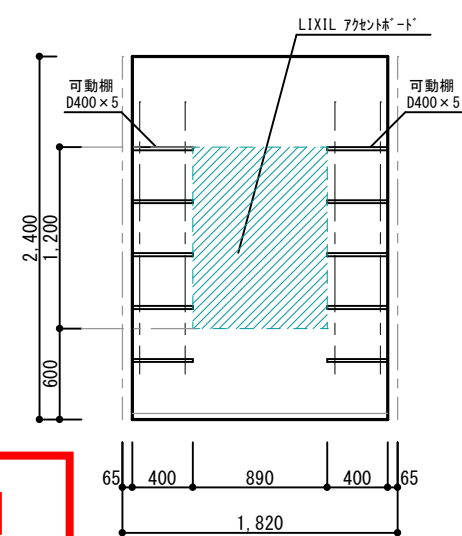

ハントリー 東面

決定図

訂正	浜岡一級総合設計事務所 一級建築士事務所 静岡県知事登録第 (10)2441 号 一級建築士 大臣登録第 365879 号 西原利昌	LIFEFUND PG HOUSE	株式会社 LIFEFUND InDesign office 一級建築士事務所 事務所登録 (2)第7595号 一級建築士登録 第179770号 鈴木 達男 〒432-8023 静岡県浜松市中央区鶴江3丁目70番23号	年月日 2025.12.28	件名 山本卓矢様 寛子様 新築工事		設計 酒井	IC	工事 青島	図番 6-1
				縮尺 1/50	図名 展開図-1					