




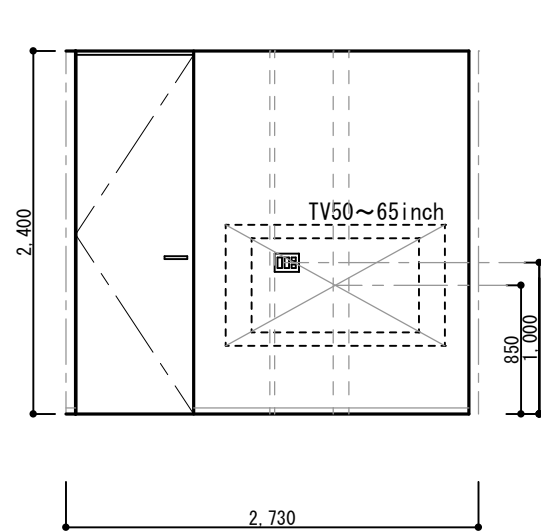


LDK 東面

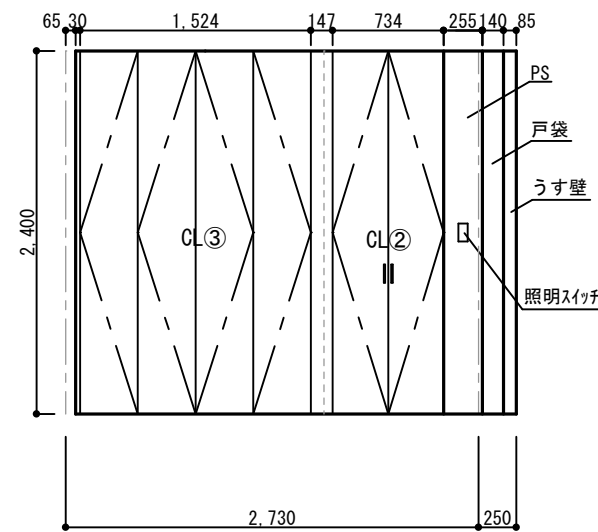


洋室① 北面

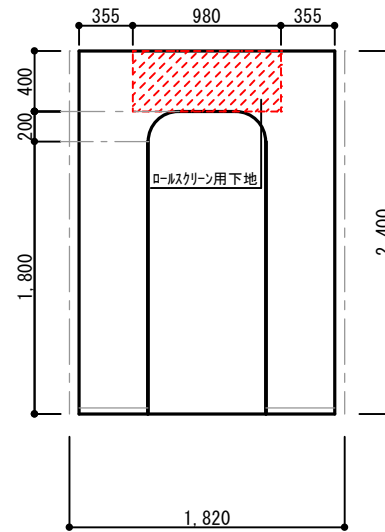


WIC 東面

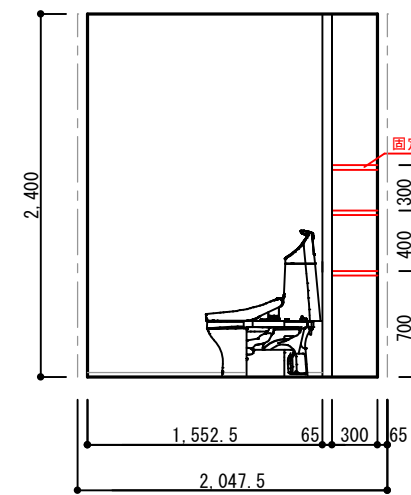


WC① 東面

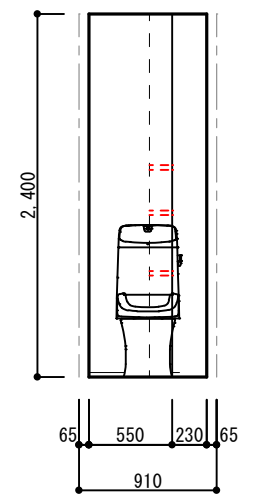


WC① 南面

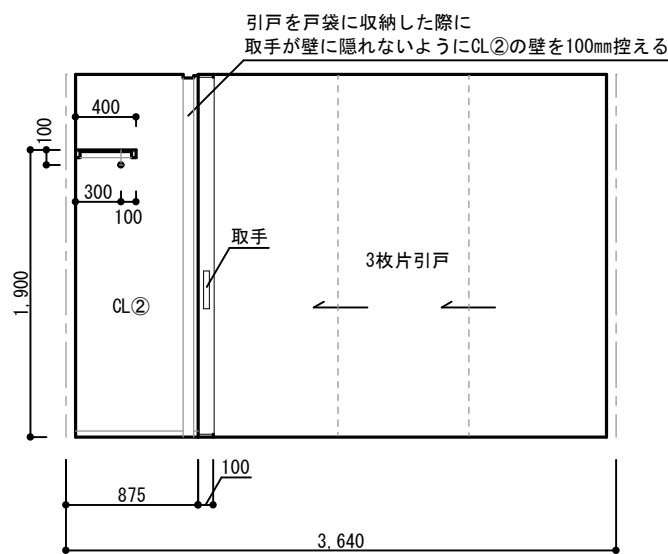


洋室① 東面

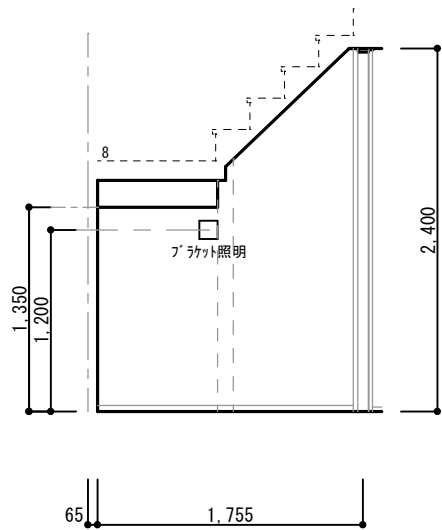


CL① 東面

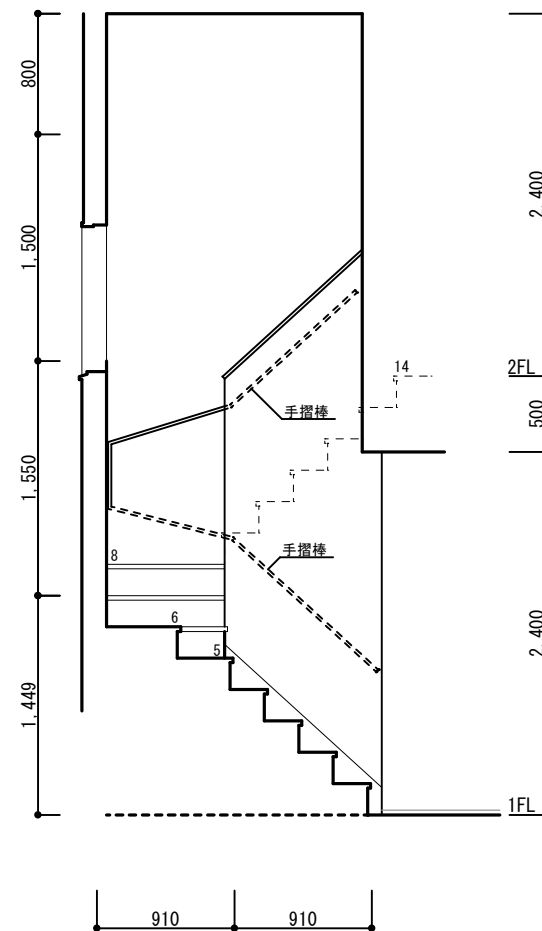


階段 断面図

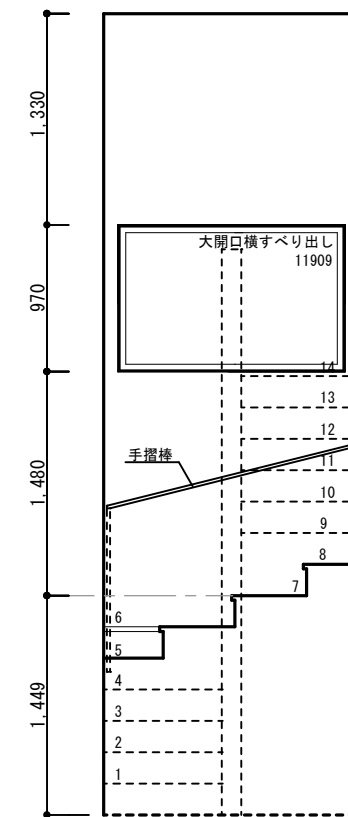

階段 窓正面図

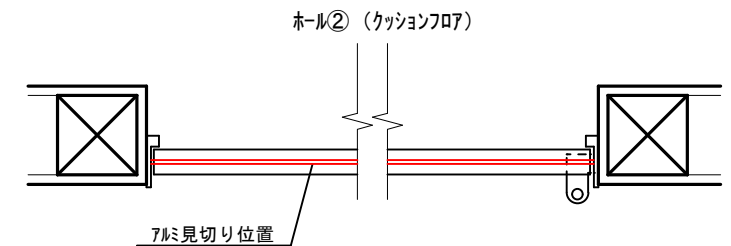


ホール② (カッションフロア)

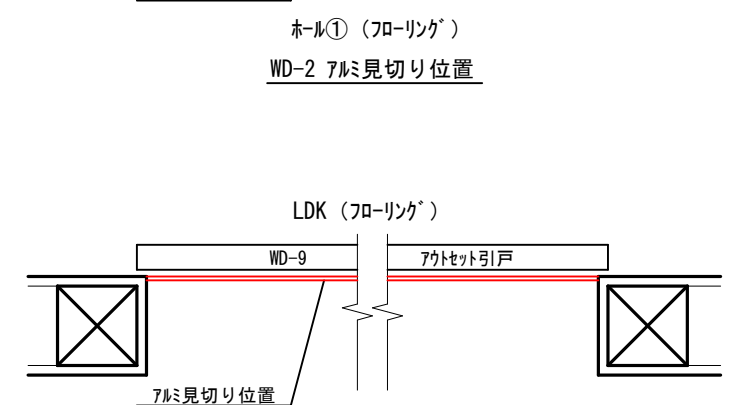


ホール① (フローリング)

WD-2 アルミ見切り位置

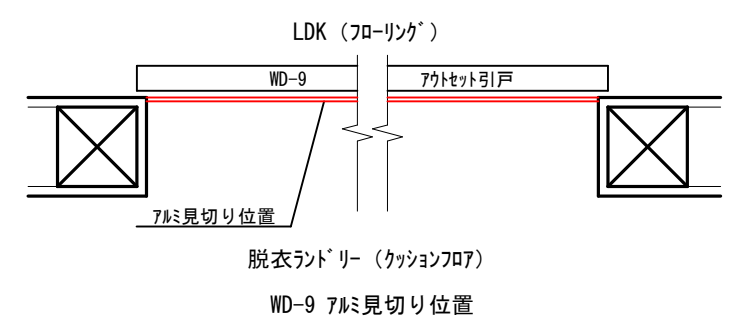

LDK (フローリング)

WD-9 アルミ見切り位置

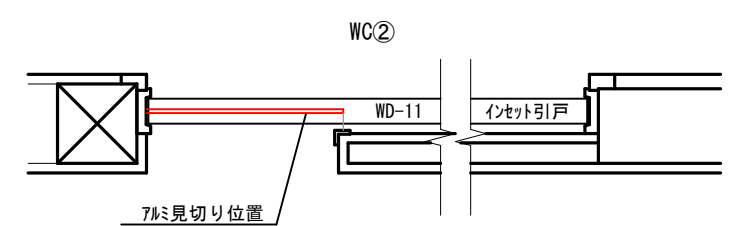

WC②

WD-11 アルミ見切り位置

決定図

|    |                                                                          |                      |   |                                 |                                     |          |    |          |           |
|----|--------------------------------------------------------------------------|----------------------|---|---------------------------------|-------------------------------------|----------|----|----------|-----------|
| 訂正 | 浜岡一級総合設計事務所<br>一級建築士事務所 静岡県知事登録第 (10)2441 号<br>一級建築士 大臣登録第 365879 号 西原利昌 | LIFEFUND<br>PG HOUSE | 株式会社 LIFEFUND InDesign office 一級建築士事務所<br>事務所登録 (2)第7595号 一級建築士登録 第179770号 鈴木 達男<br>〒432-8023 静岡県浜松市中央区鴨江3丁目70番23号 | 年月日<br>2025.12.28<br>縮尺<br>1/50 | 件名<br>山本卓矢様 寛子様 新築工事<br>図名<br>展開図-2 | 設計<br>酒井 | IC | 工事<br>青島 | 図番<br>6-1 |
|----|--------------------------------------------------------------------------|----------------------|---|---------------------------------|-------------------------------------|----------|----|----------|-----------|