


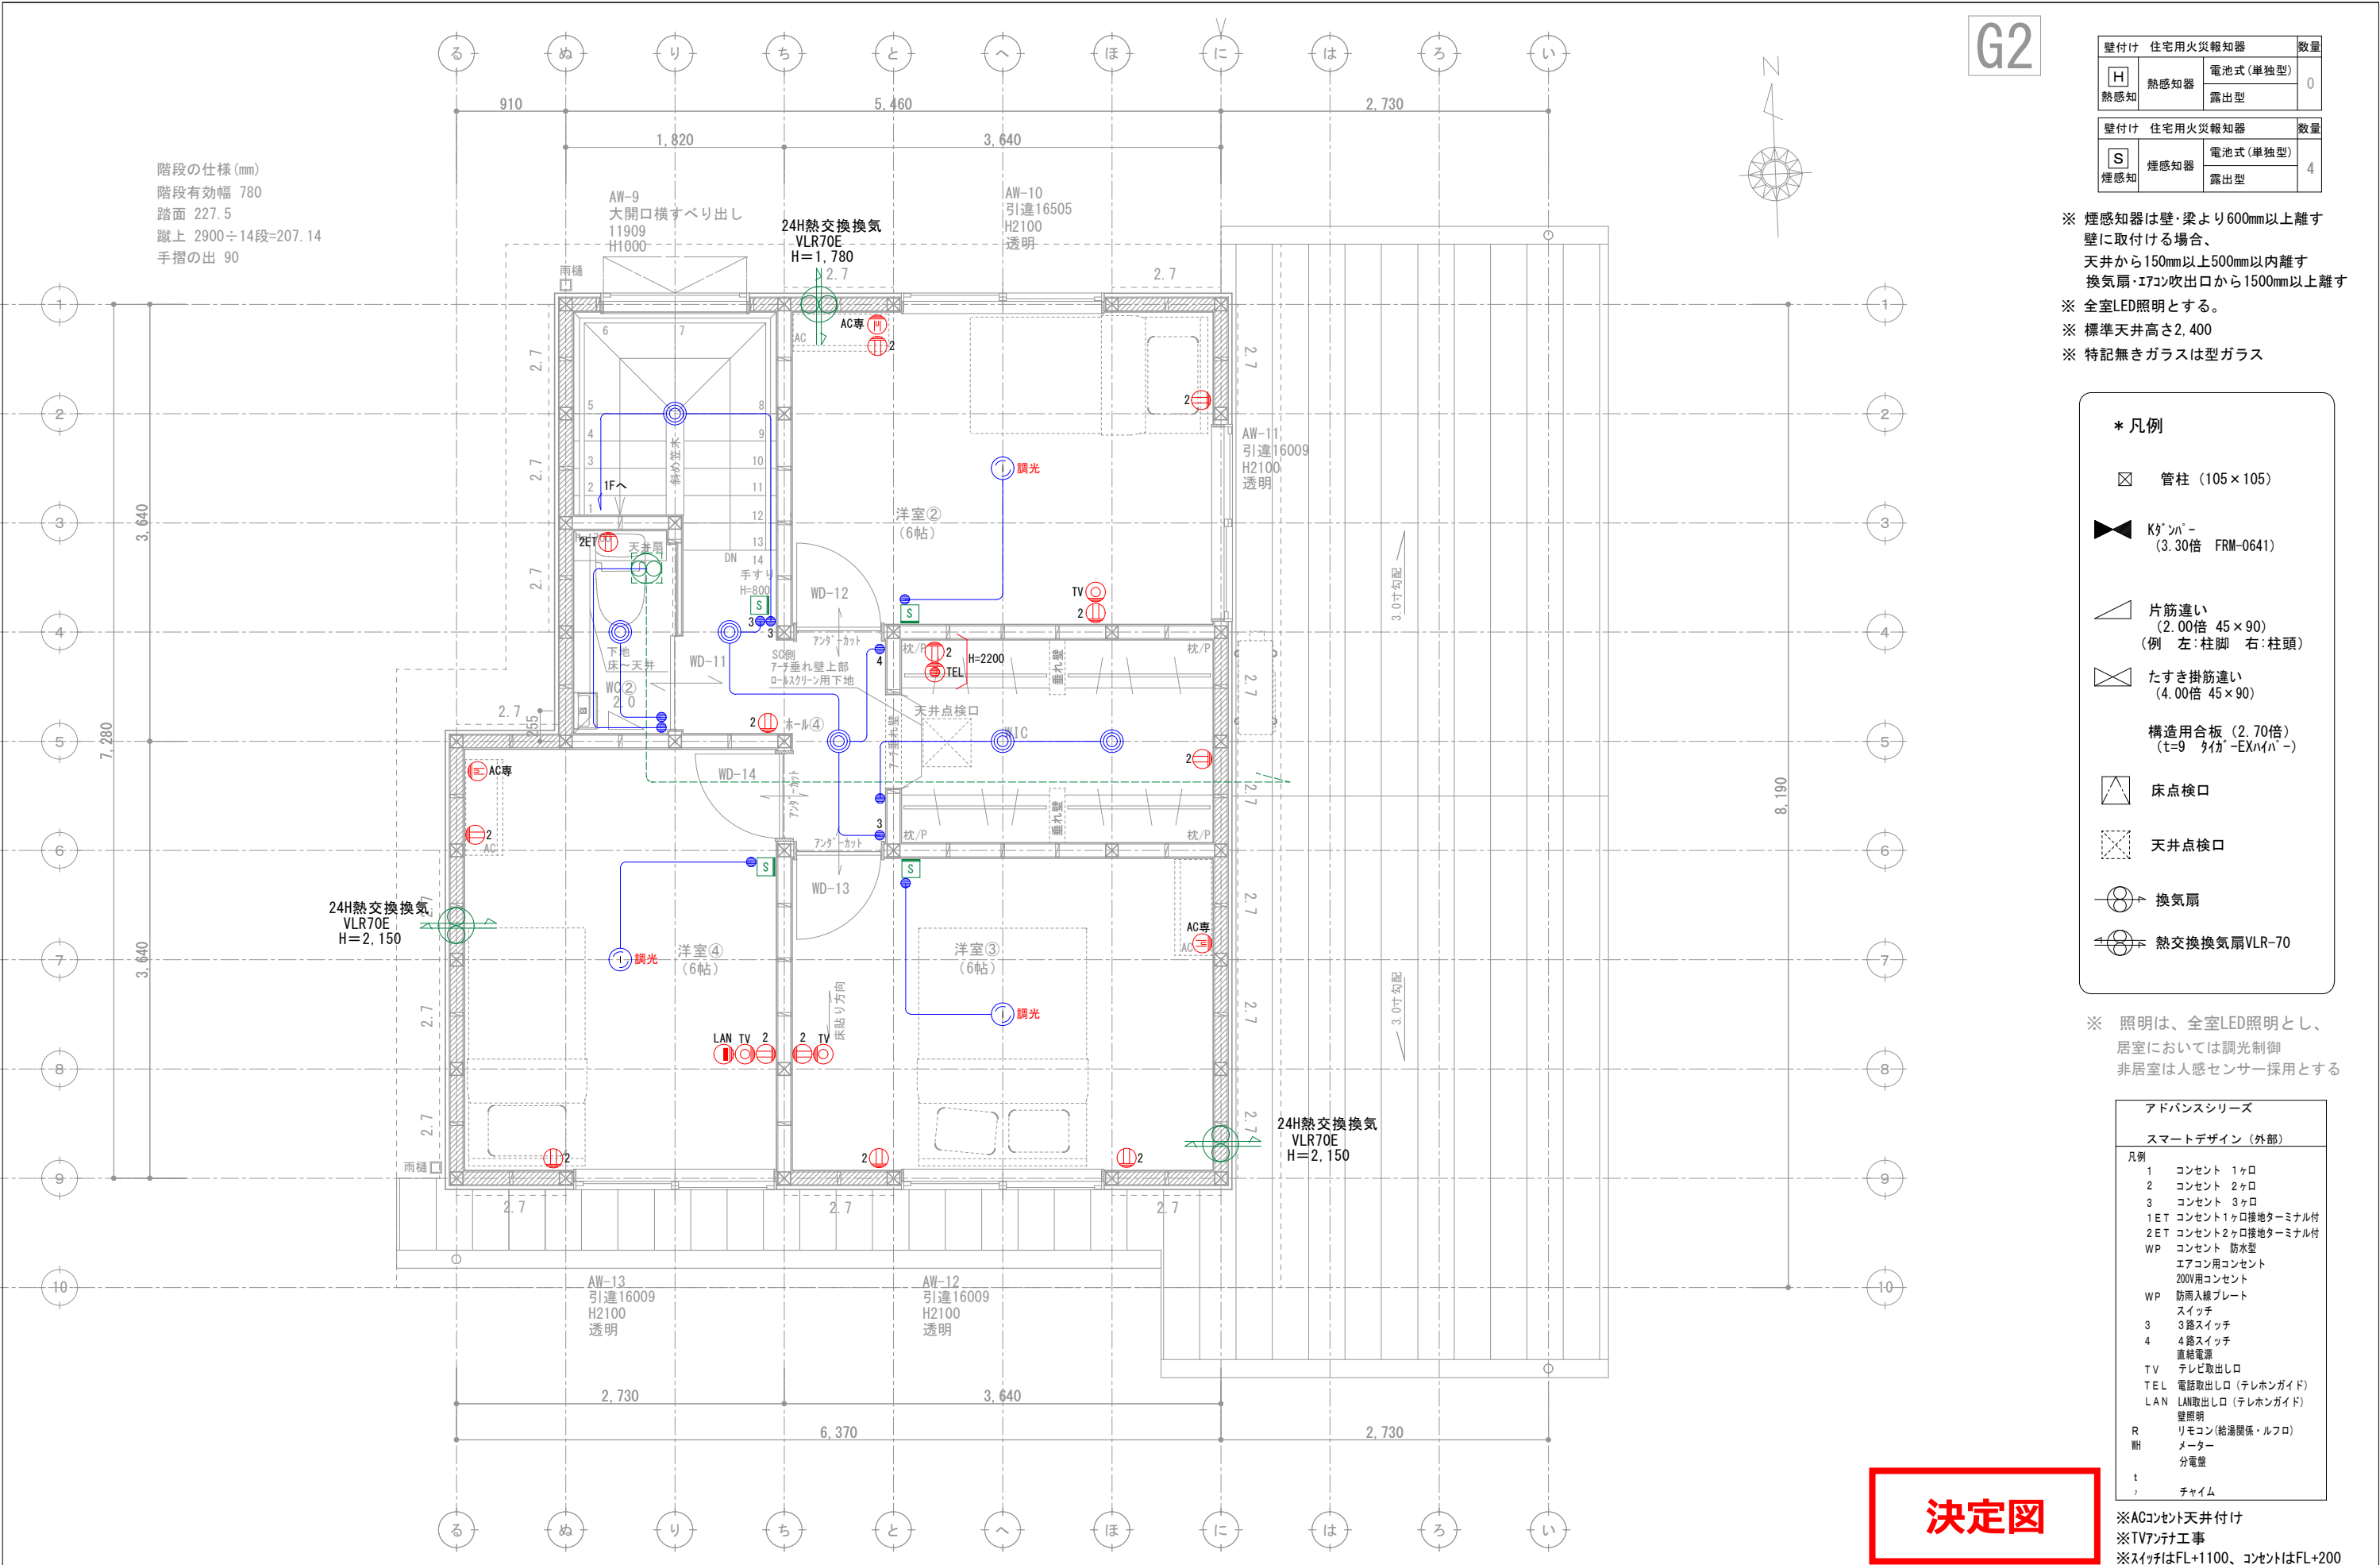

G2

壁付け 住宅用火災報知器			数量
H 熱感知	熱感知器	電池式(単独型)	0
		露出型	
壁付け 住宅用火災報知器			数量
S 煙感知	煙感知器	電池式(単独型)	4
		露出型	

- ※ 煙感知器は壁・梁より600mm以上離す
壁に取付ける場合、
天井から150mm以上500mm以内離す
換気扇・エアコン吹出口から1500mm以上離す
- ※ 全室LED照明とする。
- ※ 標準天井高さ2,400
- ※ 特記無きガラスは型ガラス

* 凡例

☒ 管柱 (105×105)

◀▶ Kダクト (3.30倍 FRM-0641)

◀▶ 片筋違い (2.00倍 45×90)
(例 左:柱脚 右:柱頭)

◀▶ たすき掛筋違い (4.00倍 45×90)

◀▶ 構造用合板 (2.70倍)
(t=9 材種-EXハイバ-)

◀▶ 床点検口

◀▶ 天井点検口

⊙→ 換気扇

⊙⇄ 熱交換換気扇VLR-70

- ※ 照明は、全室LED照明とし、
居室においては調光制御
非居室は人感センサー採用とする

アドバンスシリーズ			
スマートデザイン (外部)			
凡例	1	コンセント	1ヶ所
	2	コンセント	2ヶ所
	3	コンセント	3ヶ所
	1ET	コンセント1ヶ所接地ターミナル付	
	2ET	コンセント2ヶ所接地ターミナル付	
WP	コンセント	防水型	
		エアコン用コンセント	
		200V用コンセント	
WP	防雨入線プレート		
		スイッチ	
3	3路スイッチ		
4	4路スイッチ		
		直結電源	
TV	テレビ取出口		
TEL	電話取出口 (テレホンガイド)		
LAN	LAN取出口 (テレホンガイド)		
		壁照明	
R	リモコン (給湯関係・ルフロ)		
WH	メーター		
		分電盤	
t		チャイム	

- ※ACコンセント天井付け
- ※TVアンテナ工事
- ※スイッチはFL+1100、コンセントはFL+200

決定図