



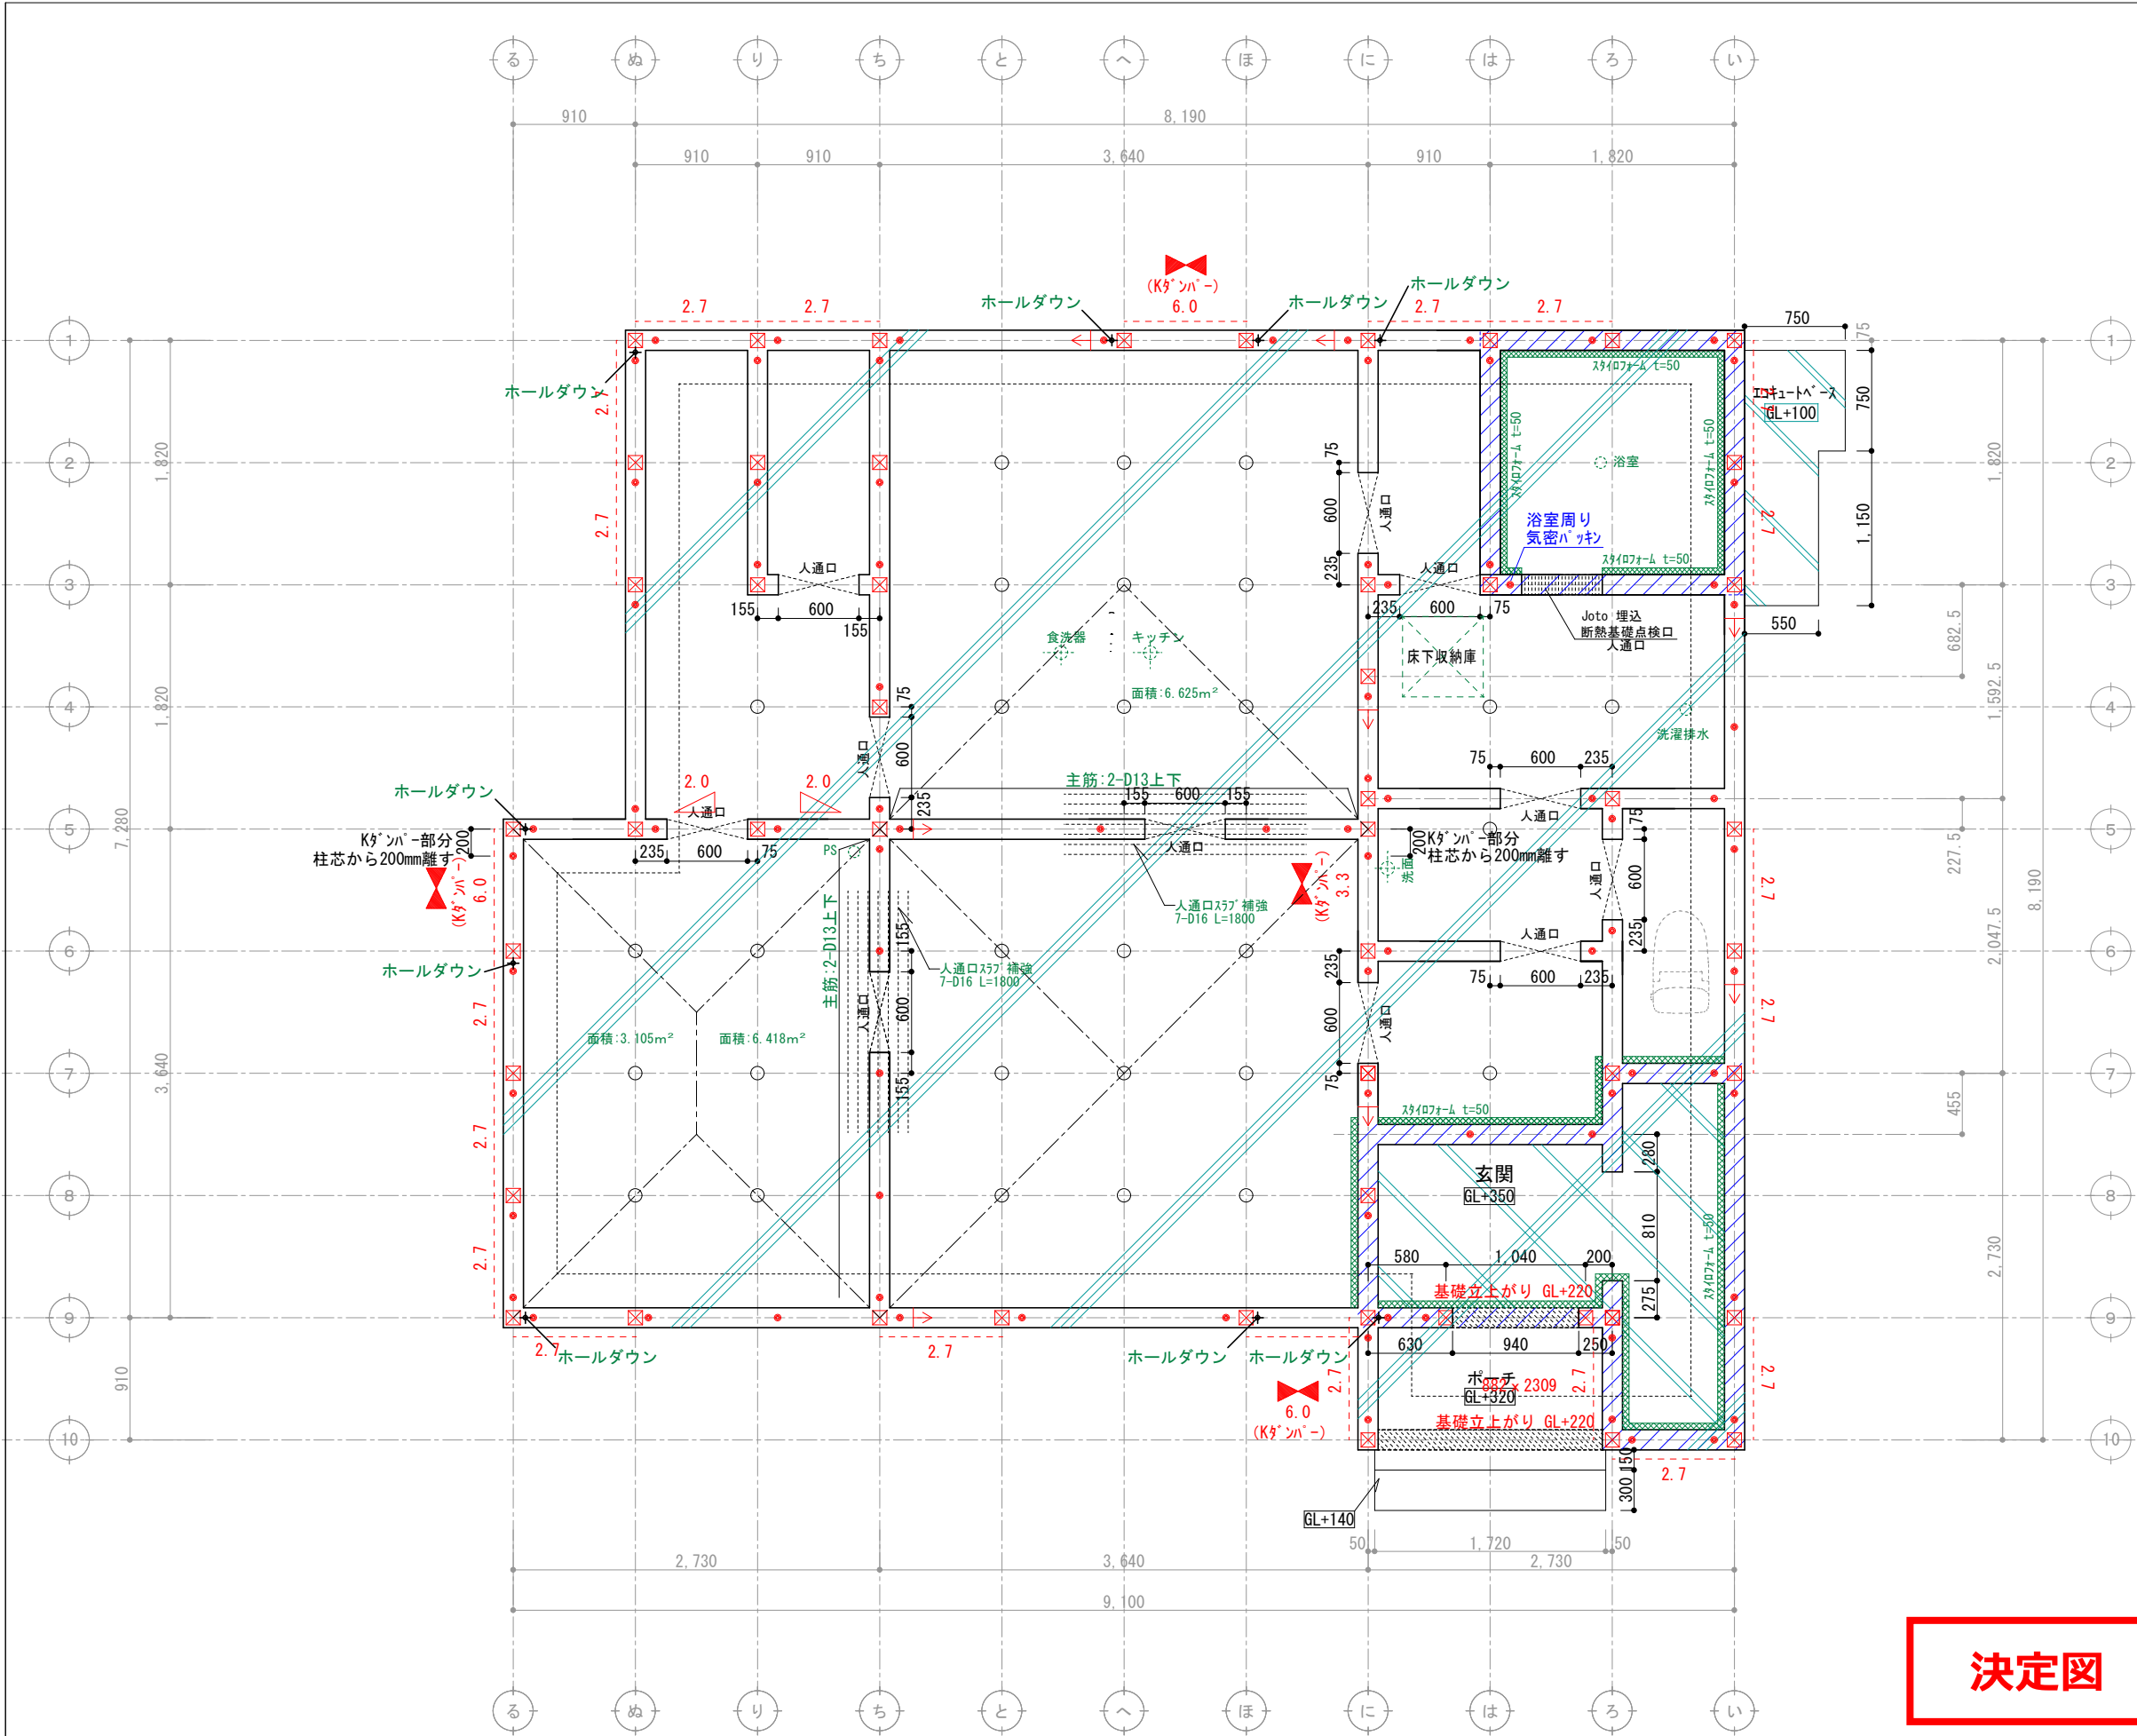

決定図

構造体ベースコンクリート t=150

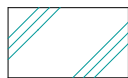

後打ち土間コン




アンカーボルトの配置

- 土台切れの箇所より150mm
- 土台の継手及び仕口の端部より150mm
- 耐力壁の端部、筋交いの脚部より150mm
- 1.82m以下の間隔
- 250mm以上埋込み
- 基礎天端より120mm

筋かい凡例

- 柱脚 柱頭 片筋かい
- たすき掛け筋かい
- 構造用パネル

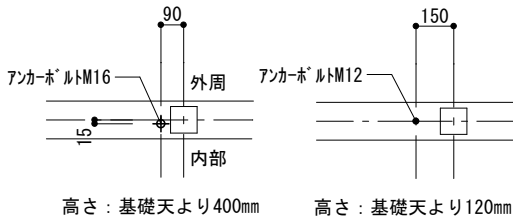

高さ：基礎天より400mm

高さ：基礎天より120mm

ホールダウン用アンカーボルト配置

アンカーボルト配置

凡例

- 通し柱 (105*105) 管柱 (105*105)
- アンカーボルトM12 L=400
- + ホールダウンアンカーM16 L=800
柱芯より90mm 280mm以上埋め込み
(カナリフィストアンカーボルトM16)
- ⊕ 鋼製束
- 土台ジョイント
- ベースコンクリート (t=150)
- 後打ちコンクリート

基礎伏図について特記なき場合に限り下記による。

- コンクリート：呼び強度 21N/mm²
- 鉄筋：SD295A
- 設計地耐力：fe=20kN/m²
地耐力計測後、不足の場合は相当の改良を行い、満たすものとする。
- 基礎の位置は、芯振分けとする。
- 玄関・S/C・UB周囲の基礎天端は気密パッキン施工（網掛け部）とし、その他の基礎天端は基礎パッキン施工とする。
- 設備配管の屋内への取り入れは基礎立上り部のスリーブによる。

訂正	浜岡一級総合設計事務所 一級建築士事務所 静岡県知事登録第 (10)2441 号 一級建築士 大臣登録第 365879 号 西原利昌	LIFEFUND PG HOUSE	株式会社 LIFEFUND InDesign office 一級建築士事務所 事務所登録 (2)第7595号 一級建築士登録 第179770号 鈴木 達男 〒432-8023 静岡県浜松市中央区鴨江3丁目70番23号	年月日 2025.12.28 縮尺 1/50	件名 山本卓矢様 寛子様 邸新築工事 図名 基礎伏図		設計 酒井	IC	工事 青島	図番 B-1
----	--	----------------------	--	---------------------------------	-------------------------------------	--	----------	----	----------	-----------