

■ 仕 様				■ HEAT20 G2	
断熱工事		■ 床:ネオフォーム t90 ■ 土間床等の外周:スタイロフォームAT t50 ■ 壁:アクアフォームLITE吹付 t90 ■ 天井:アクファフォームLITE吹付 t220			
床下換気		■ 基礎パッキン JOTO (玄関・UB周り:気密基礎パッキン)			
防虫防蟻		■ 土壌処理・木部 ガントナーMC			
■ 外 部 仕 上 表				■ 22条地域	
部位		仕上・仕様・メーカー		色番・品番	
屋根		■ ガルバリウム鋼板(t0.35)UK立平 ニスクカラーPro GH 軒先通気金物 日本住環境株式会社【REV-15】		ブラック	
パラペット笠木		■ なし			
破風・鼻隠		■ 有り		ラフティ MGブラック	
雨樋	(軒樋)	■ Panasonic シビルスケアPS50型		ブラック	
	(縦樋)	■ Panasonic S30角樋		オークグレー	
軒天	屋根軒	■ 神島化学 t= 6mm 軒天ボード エンボス		Wミルトアイボリー	
	ポーチ軒	■ 神島化学 t= 6mm 軒天ボード エンボス		Wミルトアイボリー	
	バルコニー軒	■			
オーバーハング水切り		■ ガルバリウム鋼板 ※外壁合わせ JOTO:HF-A3550		ブラック	
外壁 通気金物(15mm) ※下地面材:タイガーEXハイパー 防火認定 PC030BE-4028	■メイン	Kmew エクセレージ 新フラット16		シルクチタングレー	
	■アクセントA	なし			
	■アクセントB	なし			
玄関ポーチ		■ 床 玄関に同じ		-	
基礎		■ 立上り巾木: モルタル刷毛引き		-	
基礎水切り金物		■ JOTO鋼板製 防鼠材付き水切り JOTO:WMF-N35		アンバーグレー	
バルコニー	床・内壁	■ なし		-	
	笠木	■ なし			
外部建具		■ LIXIL EW(アルゴンガス高遮熱仕様LowEトリプルガラス クリア) ・SD、TSは、メーカー設定による。 ・オペレーター付サッシの場合は固定網戸とする ・グレモンハンドル式サッシの場合は可動網戸とする		外観 ブラック 内観 ホワイト ※樹脂パッキン・網戸付	
シャッター		■ 1階掃き出し窓×2カ所(手動)			
軒天通気金物					
玄関扉		■ LIXIL ジエスタ2 K2仕様 LIXILファミロック タグキー×3 (電池式)		ドア型: M14 型 ドア色: ミディウムチェリー ハンドル: S型ハンドル 色 ブラック	
外部物干し金物		■ 川口技研RK型-55 外壁付		ブラック	
換気フード		■ 局所換気扇(トイレ 浴室 キッチンフード) 防火ダンパー無 ■ ダクトレス熱交換換気システム (日本スティーベル株式会社) VLR-70E 防火ダンパー無		外気フード: ホワイト 外気フード: S シルバー 室内パネル ホワイト	

■ 構 造 概 要					
基礎	■ RCベタ基礎コンクリート				
通し柱・管柱	■ 構造用集成材 105×105		間柱	■ 集成材	
土台	■ 桧 105×105	大引き	■ 桧 90*90	筋交い	■ 構造用製材 火打梁 ■ 鋼製火打(当社基準により米松あり)
桁・梁	■ 構造用製材及び集成材			制震装置	■ Kダンパー (株)アイ・エム・エー
■ 設 備 装 着 品					
住宅設備	部位	メーカー	商品名 ※ 詳細は見積り、プレゼン参照	見積りNo.	(日付)
	キッチン	LIXIL	■ ES	見積り番号 : M25119172542-004-2	(日付) 2026.01.06
	バックカウンタ ※オプション	LIXIL	■ ES L1800(W900スライドストッカー×2)	見積り番号 : M25119172542-004-3	(日付) 2026.01.06
	浴室	LIXIL	■ AX1616 PGハウス標準仕様	見積り番号 : M25119172542-004-1	(日付) 2026.01.06
	1Fトイレ	LIXIL	■ ベーシアシャワートイレ 白 タンク手洗 無し ● 紙巻き器: なし(支給品取付)	見積り番号 : M25119172542-004-5	(日付) 2026.01.06
	2Fトイレ	LIXIL	■ ベーシアシャワートイレ 白 ● タオル掛け: なし(支給品取付) タンク手洗 無し ● 紙巻き器: なし(支給品取付)	見積り番号 : M25119172542-004-6	(日付) 2026.01.06
	洗面台	LIXIL	■ EV W900(D500タイプ) 扉:グロスホワイト	見積り番号 : M25119172542-004-4	(日付) 2026.01.06
			その他 ● タオル掛け: なし(支給品取付)		
			※2階トイレ コフレルあり		
給排水設備	給湯器	■ コキュート370L Panasonic Sシリーズ(高圧型)スタンダードモデル 追い焚きフルオー			
	排水	■ 下水			
	外水栓	■ 1 カ所 (平面図参照)	■ 外部立柱柱: 外構設置 保留		
	外部ガーデンパン	■ 無し			
	その他	■ 洗濯機用単水栓: 緊急止水弁付 ■ 洗濯機用排水:トラップ金物(標準) ■ 排水さや管(長期優良住宅仕様)			
ガス配管設備	■ あり(都市ガス) (配置図・平面図参照) ■ガス使用器具 乾太くん 専用架台				
電気設備	インターホン	■ パナソニック VL-SE31XL			
	TVアンテナ	■ UHF + BS・110度CS／CSアンテナ [2K・4K・8K対応] ■ホワイト			
	エアコン	■ 設置場所:			
	ソーラー	■ あり(Qセルズ) 12 枚 5.28 KW Re.RISE-G3 440 (1722×1134×30)			
	※標準搭載	※メーカーのモデルチェンジ等で後継品に変更される可能性あり ■ 屋外パワコン エネルギーマネジメントシステム Cube J			
その他	※乾太くん ダンパー付排湿口が1つ 有り				
決定図					

決定図

	浜 岡 一 級 総 合 設 計 事 務 所 一級建築士事務所 静岡県知事登録第 (10)2441 号 一級建築士 大臣登録第 365879 号 西原利昌	 株式会社 LIFEFUND InDesign office 一級建築士事務所 事務所登録 (2)第7595号 一級建築士登録 第179770号 鈴木 達男 〒432-8023 静岡県浜松市中央区鴨江3丁目70番23号	年 月 日	件 名			設計	IC	工務	図 番	
			2025.12.28	山本卓矢様 寛子 様邸 新築工事							
			縮尺	図面			酒井		青島	1-1	
				仕上表 1							

内 部 仕 上 表 （壁下地:石膏ボード12.5mm/天井下地:9.5mm）※脱衣室:床合板特類 下地									
階		床	巾木	壁	品番	廻 縁	天 井	品番	特記事項
1F	ポーチ	LIXILパセオ300/PSO-FIO 4							
	玄関	LIXILパセオ300/PSO-FIO 4	ライン巾木(W)	ビニルクロス	SLP341	突付	ビニルクロス	SLP341	
	SC	LIXILパセオ300/PSO-FIO 4	ライン巾木(W)	ビニルクロス	SLP341	突付	ビニルクロス	SLP341	有孔ホ-ード ABS-02
	ホール①	イタタ銘木フロア-ラスティックt12 ナラ桜3P	ライン巾木(W)	ビニルクロス	SLP341	突付	ビニルクロス	SLP341	
	ホール②	フロアタイルt2.3 サンゲツIS-2073	H40ソフト巾木W97	ビニルクロス	SLP341	突付	ビニルクロス	SLP341	
	WC①	フロアタイルt2.3 サンゲツIS-2073	H40ソフト巾木W97	ビニルクロス		突付	ビニルクロス		アクセントあり
	脱衣ラントリー	フロアタイルt2.3 サンゲツIS-2073	H40ソフト巾木W98	ビニルクロス	SLP341	突付	ビニルクロス	SLP341	
	LDK	イタタ銘木フロア-ラスティックt12 ナラ桜3P	ライン巾木(W)	ビニルクロス	SLP341	突付	ビニルクロス	SLP341	アクセントあり、キッチン床:IS-2073
	パントリー	イタタ銘木フロア-ラスティックt12 ナラ桜3P	ライン巾木(W)	ビニルクロス	SLP341	突付	ビニルクロス	SLP341	アクセントホ-ード ホワイト
	洋室①	イタタ銘木フロア-ラスティックt12 ナラ桜3P	ライン巾木(W)	ビニルクロス	SLP341	突付	ビニルクロス	SLP341	アクセントあり
2F	ホール③	イタタ銘木フロア-ラスティックt12 ナラ桜3P	ライン巾木(W)	ビニルクロス	SLP341	突付	ビニルクロス	SLP341	
	ホール④	イタタ銘木フロア-ラスティックt12 ナラ桜3P	ライン巾木(W)	ビニルクロス	SLP341	突付	ビニルクロス	SLP341	
	WC②	サンゲツ HM-12091	H40ソフト巾木W97	ビニルクロス		突付	ビニルクロス		アクセントあり
	洋室②	イタタ銘木フロア-ラスティックt12 ナラ桜3P	ライン巾木(W)	ビニルクロス	SLP341	突付	ビニルクロス	SLP341	
	洋室③	イタタ銘木フロア-ラスティックt12 ナラ桜3P	ライン巾木(W)	ビニルクロス	SLP341	突付	ビニルクロス	SLP341	
	洋室④	イタタ銘木フロア-ラスティックt12 ナラ桜3P	ライン巾木(W)	ビニルクロス	SLP341	突付	ビニルクロス	SLP341	
	WIC	イタタ銘木フロア-ラスティックt12 ナラ桜3P	ライン巾木(W)	ビニルクロス	SLP341	突付	ビニルクロス	SLP341	
物入・収納・CL etc		※接続する部屋と同仕様とする							


上 框 ※	■ LIXILラシッサS 上框のみ30×150 色: クリエオーク
階 段	■ LIXIL KA 階段 ササラ: プレシャスホワイト
KA階段で対応できない場合、オプション	段 板 : クリエオーク 蹴込板: 段板同色
ラウンド手摺: クリエオーク	手摺金物 プレシャスホワイト
にてラシッサS階段	上段框: クリエオーク 長尺笠木156: LIXIL クリエオーク
窓 枠	■ LIXIL スマート10(玄関以外) 色 プレシャスホワイト ※浴室ドア枠 フクビ3方枠 [ホワイト]
キッチン笠木	■ ゴム集成カウンター(オスモカラー) 色 3062フロア-クリアmatt
カウンター	形状 L型(ジョイント加工) t=30
天井点検口	■ 天井アルミ点検口枠 450角 TAN45BW フクビ化学工業 ミルキーホワイト
床下収納庫	■ 高気密型床下点検口断熱型 SPF-R6060 城東テクノ 収納付 (脱衣室) ライトグレー(LG)
トイレ棚	■ 2階トイレ D250 アートランバー棚(シェルホワイト)
室内物干し金物	■ 川口技研SPC型1セット
LDK-カウンター	■ なし 色
下足入	■ なし 色
プッシュタイプ	サイズ: 形状:

支給品	壁掛けTV金物 1,2階トイレ タオル掛け、紙巻き器 洗面台 タオル掛け 傘掛け(外壁設置)
備考	■ 付框:30×150 プレシャスホワイト ■ 可動棚:アートランバー 色:シェルホワイト(パントリー、CL②)、ナチュラルバーチ(SC) ■ 棚受金物類色:ホワイト ■ オイルガード ウォールタイプ 透明 ■ キッチン⇄LDK LIXIL アルミ見切りT SM-2700T/SUS


内 部 建 具 表							
LIXIL		建具色：プレシャスホワイト		枠色：扉同色		※その他、下記特記による	
ラフィス		把手：スクエアL（シャインニッケル） 丁番 固定枠（156） 外付戸当り ガイドピン床色合せ 引戸のみ上吊Wソフトモーション					
階	No	室名	形式	枠外W サイズ	デザイン	枠色	特記事項
				枠外H サイズ	建具色	把手	
1	1	WC①	片引き戸	—	RAA	—	明り窓・表示錠
	WD			2400	—	—	ガイドピン
	2	ホール②	片開き戸	—	RAA	—	
	WD			2400	—	アイアンブラック	
	3	LDK	アウトセット片引	—	RGV	—	
	WD			2400	トープ	アイアンブラック	
	4	洋室①	3枚引き戸	—	RAA	—	ガイドピン
	WD			2400	—	—	
	5	CL②	観音開	—	RAA	—	
	WD			2400	—	—	
	6	CL③	折れ戸	—	RAA	—	レールタイプ
	WD			2400	—	—	
	7	ホール③	片開き戸	—	RGW	—	
	WD			2400	ファブオーク	アイアンブラック	
	8	CL①	観音開	—	RAA		
	WD			2400	—		
9	脱衣ラントリー	アウトセット片引	—	RAA	—	明り窓・表示錠	
WD			2400	—	—		
10	ホール②	片引き戸	—	RAA	—	明り窓・表示錠	
WD			2400	—	—		
2	11	WC②	片引き戸	—	RAA	—	明り窓・表示錠
	WD			2400	—	アイアンブラック	ガイドピン
	12	洋室②	片開き戸	—	RAA	—	
	WD			2400	—	アイアンブラック	
	13	洋室③	片開き戸	—	RAA		
	WD			2400	—	アイアンブラック	
	14	洋室④	片開き戸	—	RAA		
	WD			2400	—	アイアンブラック	

決定図

G2

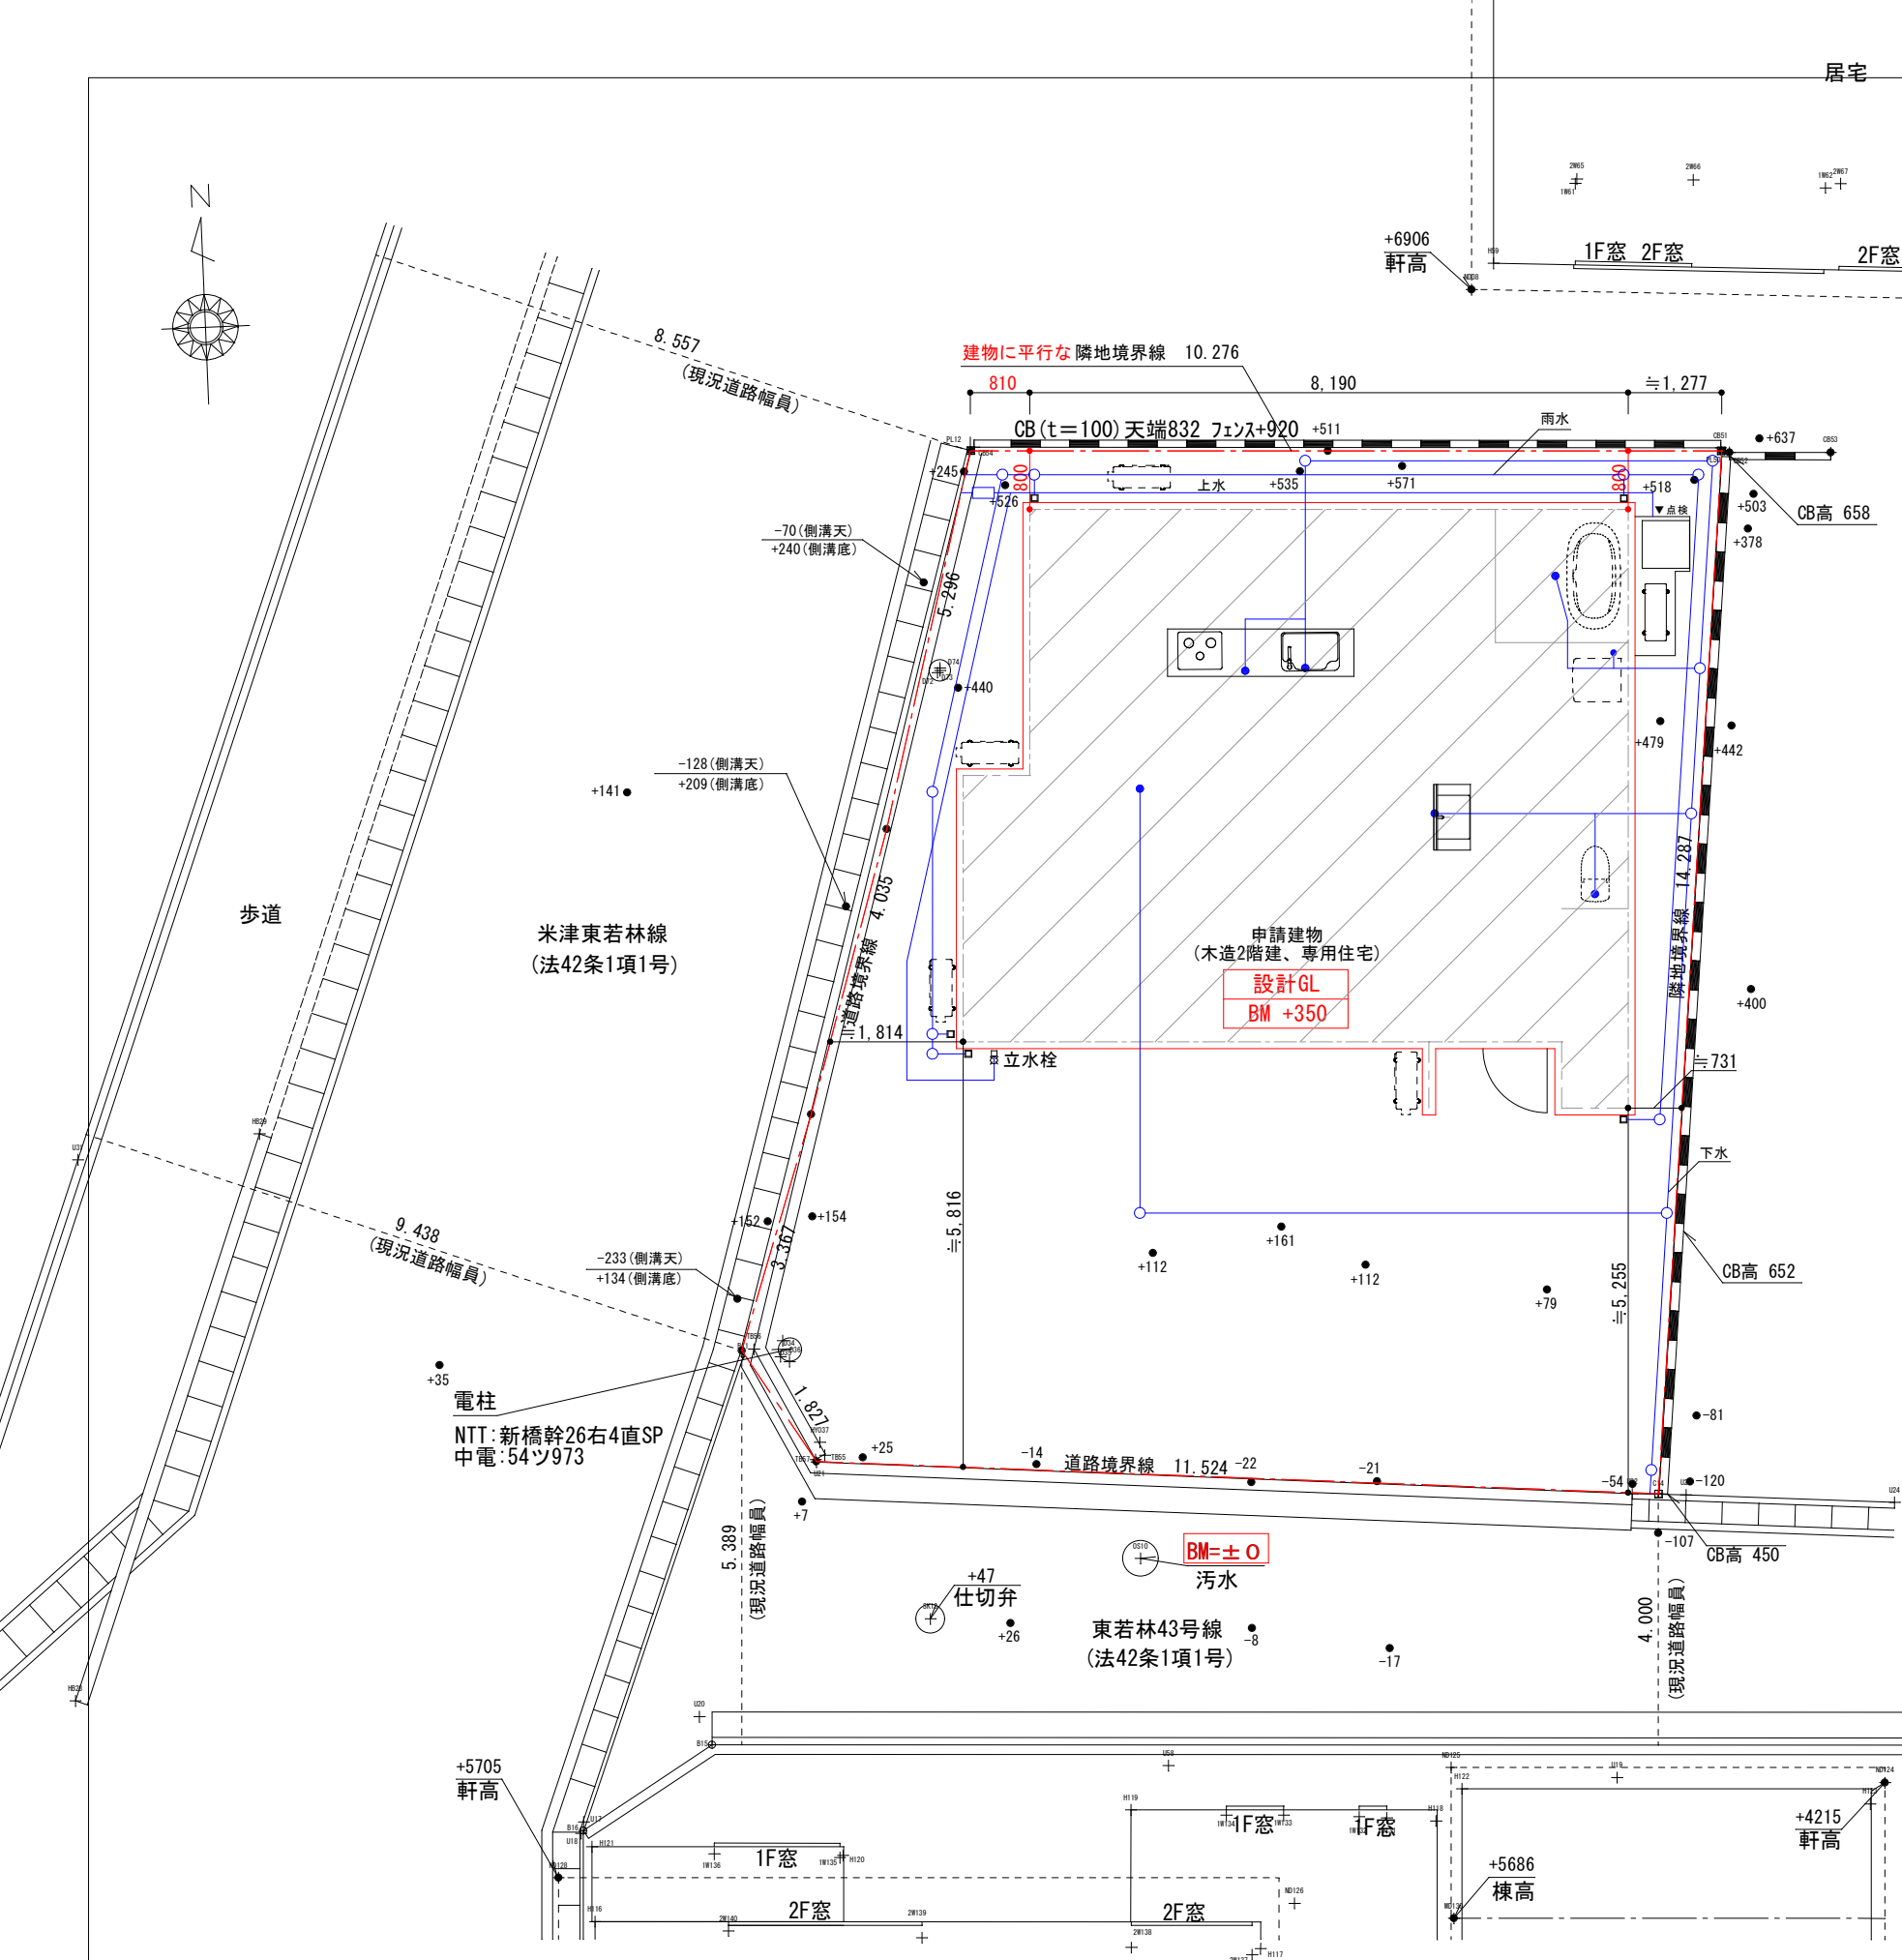

求積関 $S=1:500$

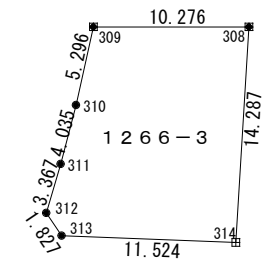


求積表

決定図

地 番	1			
N O	X _n	Y _n	Y _{n+1} - Y _{n-1}	X _n * (Y _{n+1} - Y _{n-1})
313	99.287	109.864	-12.011	-1192.536157
312	100.956	109.121	0.750	75.717000
311	103.974	110.614	3.180	330.637320
310	107.640	112.301	3.709	399.236760
309	112.536	114.323	12.144	1366.637184
308	110.762	124.445	6.809	754.178458
314	96.864	121.132	-14.581	-1412.373984
合 計				321.496581
合 計 面 積				160.7482905
地 積				160.74 m ²

※この図面は、現地の杭・構造物及び周辺建物を簡易測量し、
法務局備付地積測量図の成果を座標変換し、重ねたものです。
寸法及び面積の相違は座標変換及び数値の丸め方の相違によるものです。


訂 正	浜 岡 一 級 総 合 設 計 事 務 所 一級建築士事務所 静岡県知事登録第 (10)2441 号 一級建築士 大臣登録第 365879 号 西原利昌	LIFEFUND PG HOUSE	株式会社 LIFEFUND InDesign office 一級建築士事務所 事務所登録 (2)第7595号 一級建築士登録 第179770号 鈴木 達男 〒432-8023 静岡県浜松市中央区鴨江3丁目70番23号	年 月 日 2025. 12. 28	件 名 山本卓矢様 寛子様邸新築工事	設計 IC 工事 図 番
縮 尺 1/100				図 名 配置図	酒井 青島 2-1	

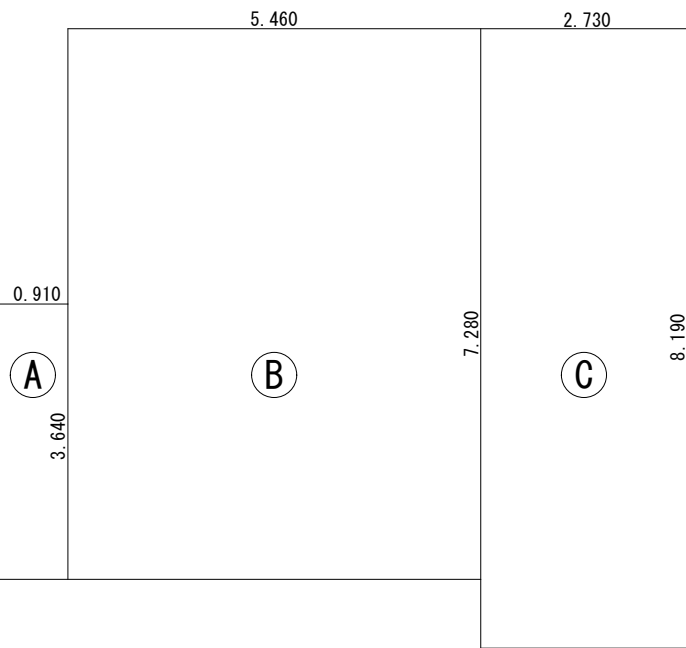

建築面積求積図 S=1/100

建築面積求積表


番号	計算式	(m)	面積 (㎡)
Ⓐ	0.910 × 3.640		3.3124
Ⓑ	5.460 × 7.280		39.7488
Ⓒ	2.730 × 8.190		22.3587
合計			65.4199 65.41 (19.7坪)

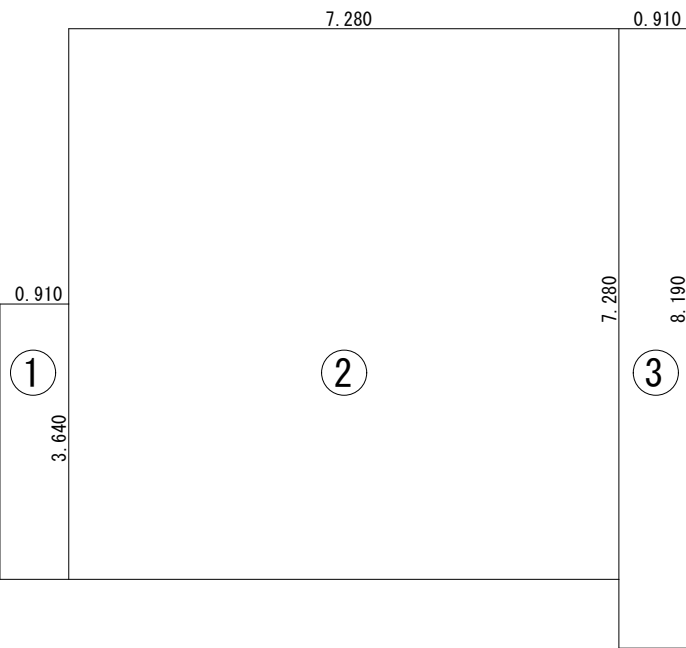

1階床面積図 S=1/100

1階床面積求積表

番号	計算式	(m)	面積 (㎡)
①	0.910 × 3.640		3.3124
②	7.280 × 7.280		52.9984
③	0.910 × 8.190		7.4529
合計			63.7637 63.76 (19.2坪)

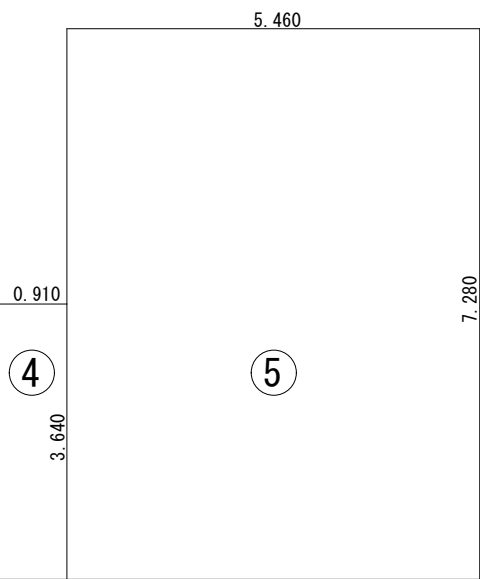

2階床面積図 S=1/100


2階床面積求積表

番号	計算式	(m)	面積 (㎡)
④	0.910 × 3.640		3.3124
⑤	5.460 × 7.280		39.7488
合計			43.0612 43.06 (13.0坪)

延べ床面積表

	番号	(m)	面積 (㎡)
1階床面積	① ② ③		63.76
2階床面積	④ ⑤		43.06
合計			106.82 (32.3坪)

決定図

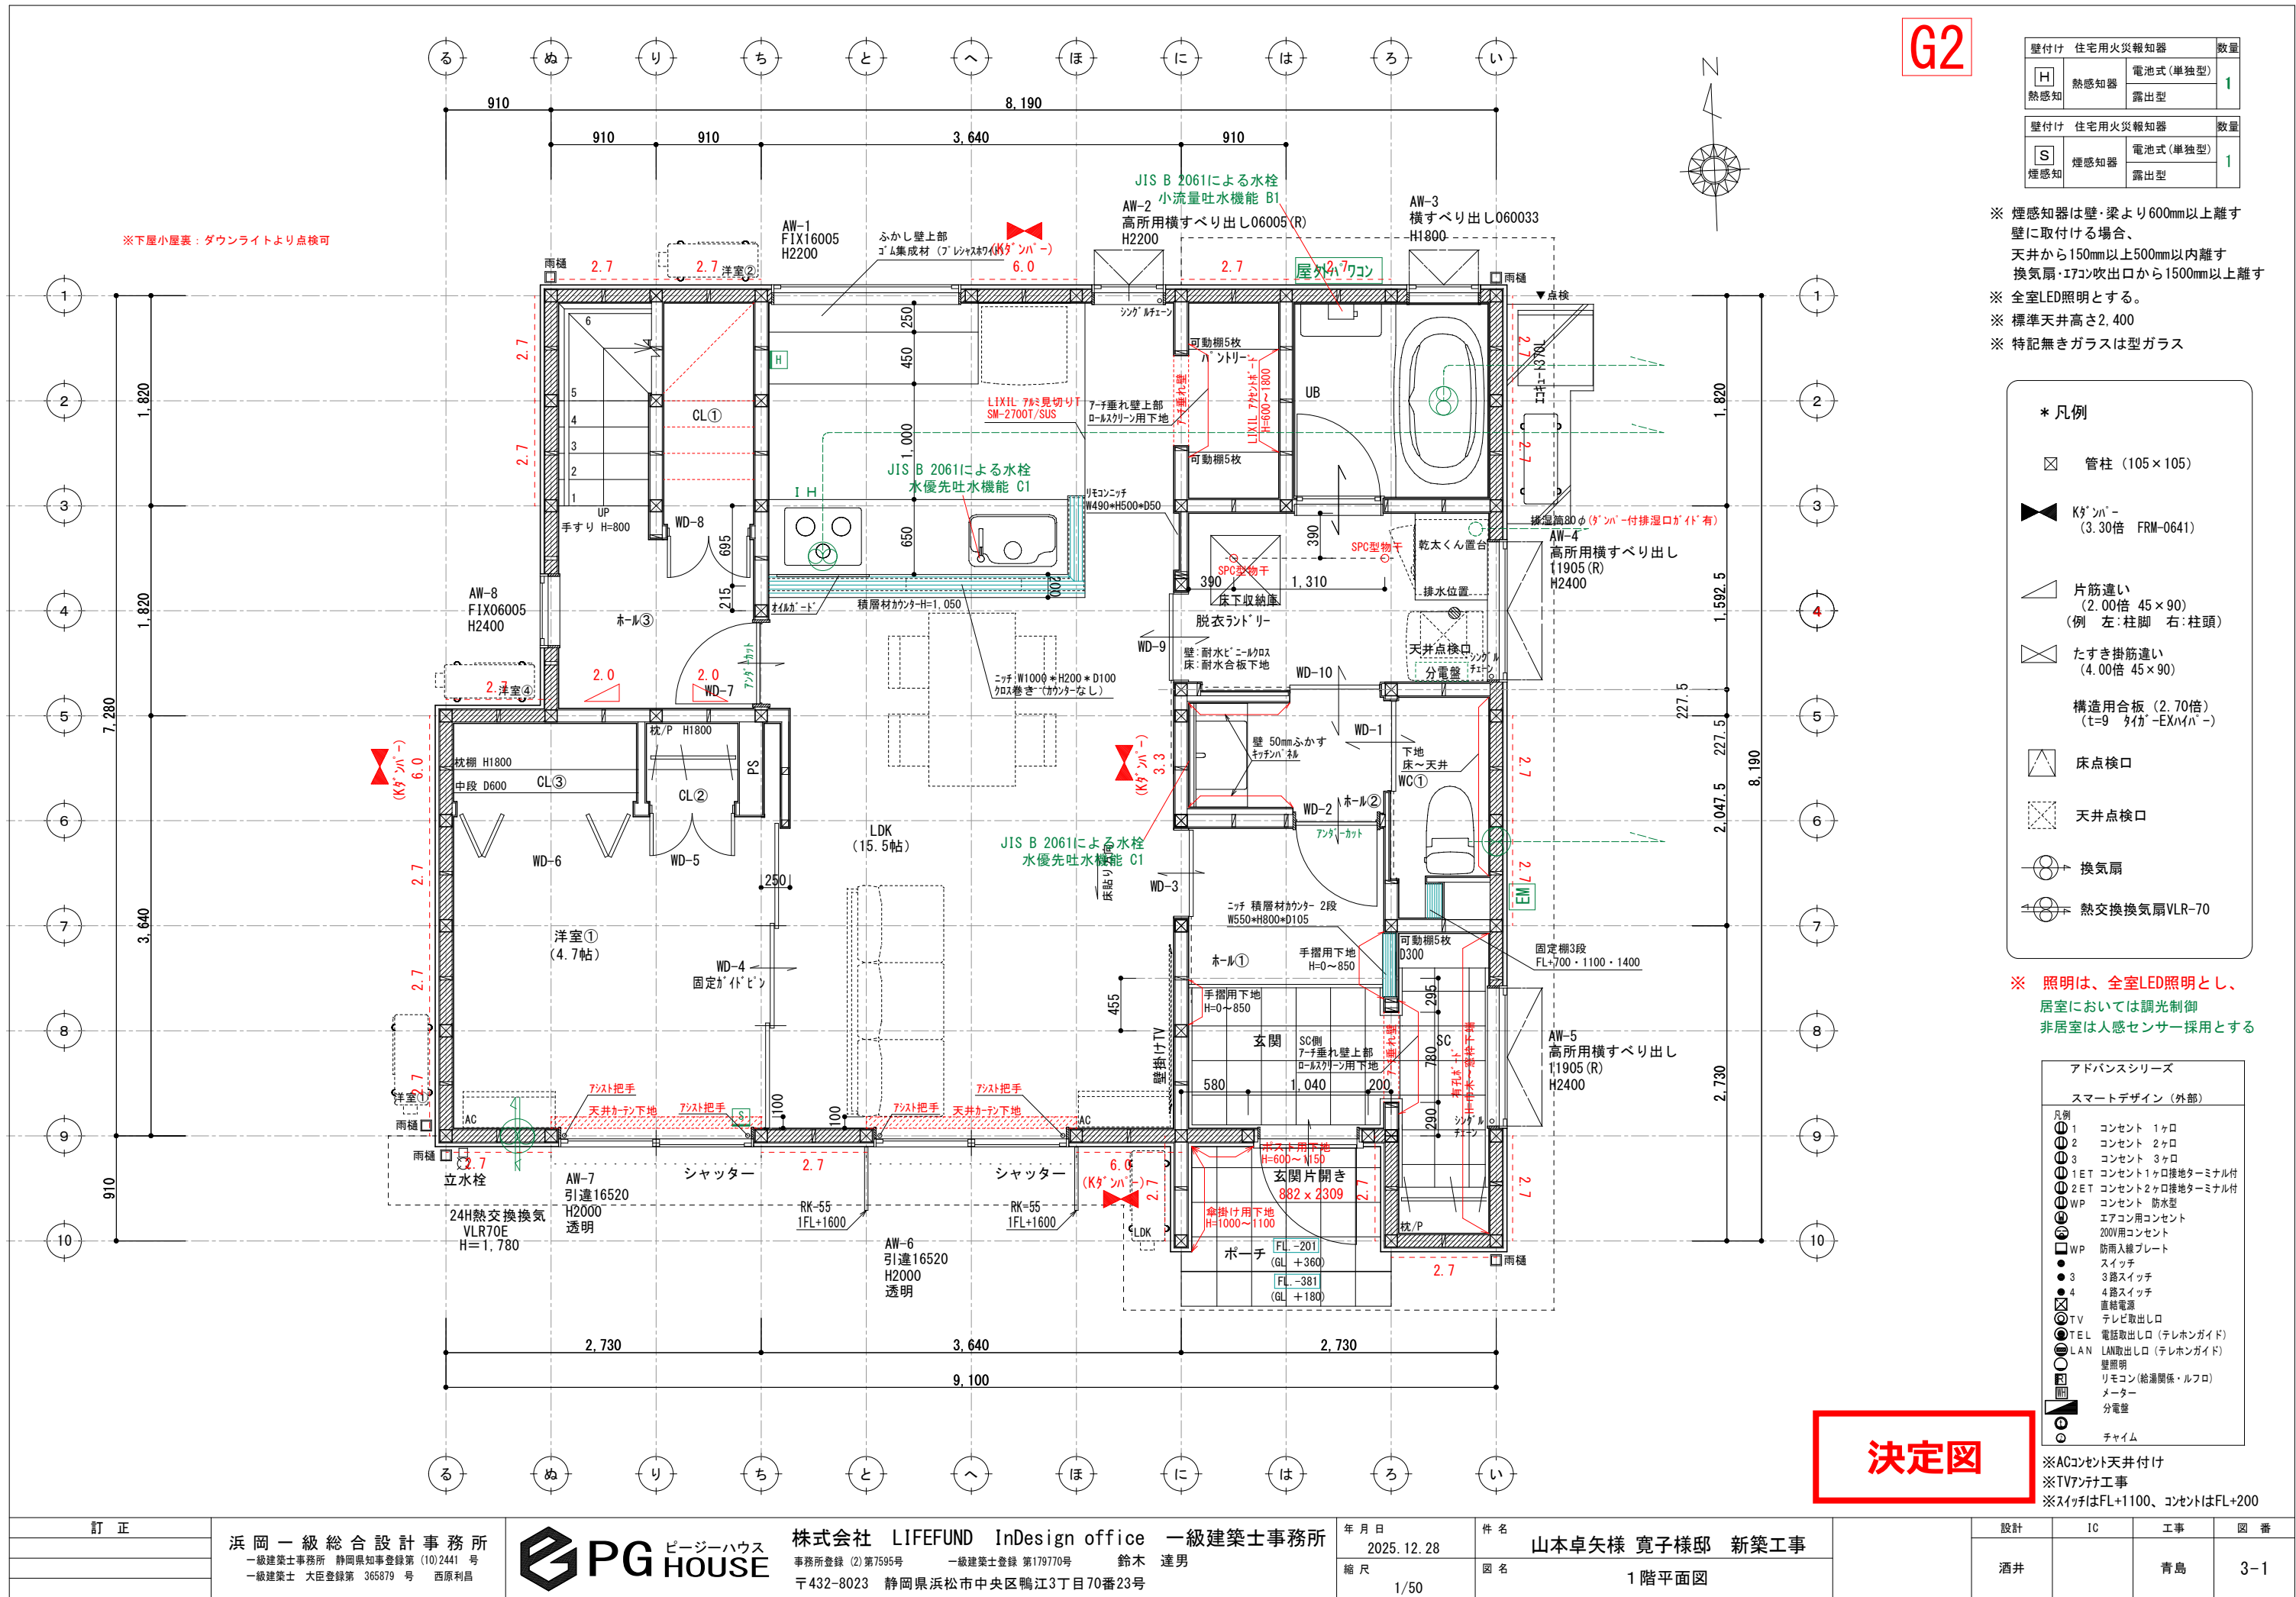

G2

壁付け 住宅用火災報知器			数量
H 熱感知	電池式(単独型)		0
	露出型		
壁付け 住宅用火災報知器			数量
S 煙感知	電池式(単独型)		4
	露出型		

※ 煙感知器は壁・梁より600mm以上離す
壁に取付ける場合、
天井から150mm以上500mm以内離す
換気扇・エアコン吹出口から1500mm以上離す
※ 全室LED照明とする。
※ 標準天井高さ2,400
※ 特記無きガラスは型ガラス

* 凡例

☒ 管柱 (105×105)

◀▶ Kダクト
(3.30倍 FRM-0641)

△ 片筋違い
(2.00倍 45×90)
(例 左:柱脚 右:柱頭)

⊠ たすき掛筋違い
(4.00倍 45×90)

構造用合板 (2.70倍)
(t=9 材種-EXハイバ-)

△ 床点検口

⊠ 天井点検口

⊙ 換気扇

⊙ 熱交換換気扇VLR-70

※ 照明は、全室LED照明とし、
居室においては調光制御
非居室は人感センサー採用とする

アドバンスシリーズ		
スマートデザイン (外部)		
凡例	1	コンセント 1ヶ所
②	2	コンセント 2ヶ所
③	3	コンセント 3ヶ所
①ET	1	コンセント1ヶ所接地ターミナル付
②ET	2	コンセント2ヶ所接地ターミナル付
WP		コンセント 防水型
⊙		エアコン用コンセント
⊙		200V用コンセント
WP		防雨入線プレート
⊙		スイッチ
●	3	3路スイッチ
●	4	4路スイッチ
⊙		直結電源
⊙		テレビ取出口
TEL		電話取出口 (テレホンガイド)
LAN		LAN取出口 (テレホンガイド)
⊙		壁照明
⊙		リモコン (給湯関係・ルフロ)
⊙		メーター
⊙		分電盤
⊙		チャイム

※ACコンセント天井付け
※TVアンテナ工事
※スイッチはFL+1100、コンセントはFL+200

階段の仕様(mm)
階段有効幅 780
踏面 227.5
蹴上 2900÷14段=207.14
手摺の出 90

決定図

訂正

浜岡一級総合設計事務所
一級建築士事務所 静岡県知事登録第 (10)2441 号
一級建築士 大臣登録第 365879 号 西原利昌




株式会社 LIFEFUND InDesign office 一級建築士事務所
事務所登録 (2)第7595号 一級建築士登録 第179770号 鈴木 達男
〒432-8023 静岡県浜松市中央区鴨江3丁目70番23号

年月日 2025.12.28
縮尺 1/50

件名 山本卓矢様 寛子様邸 新築工事
図名 2階平面図

設計 IC 工事 図番
酒井 青島 3-2

GX住宅 (Cube J付)
太陽光あり

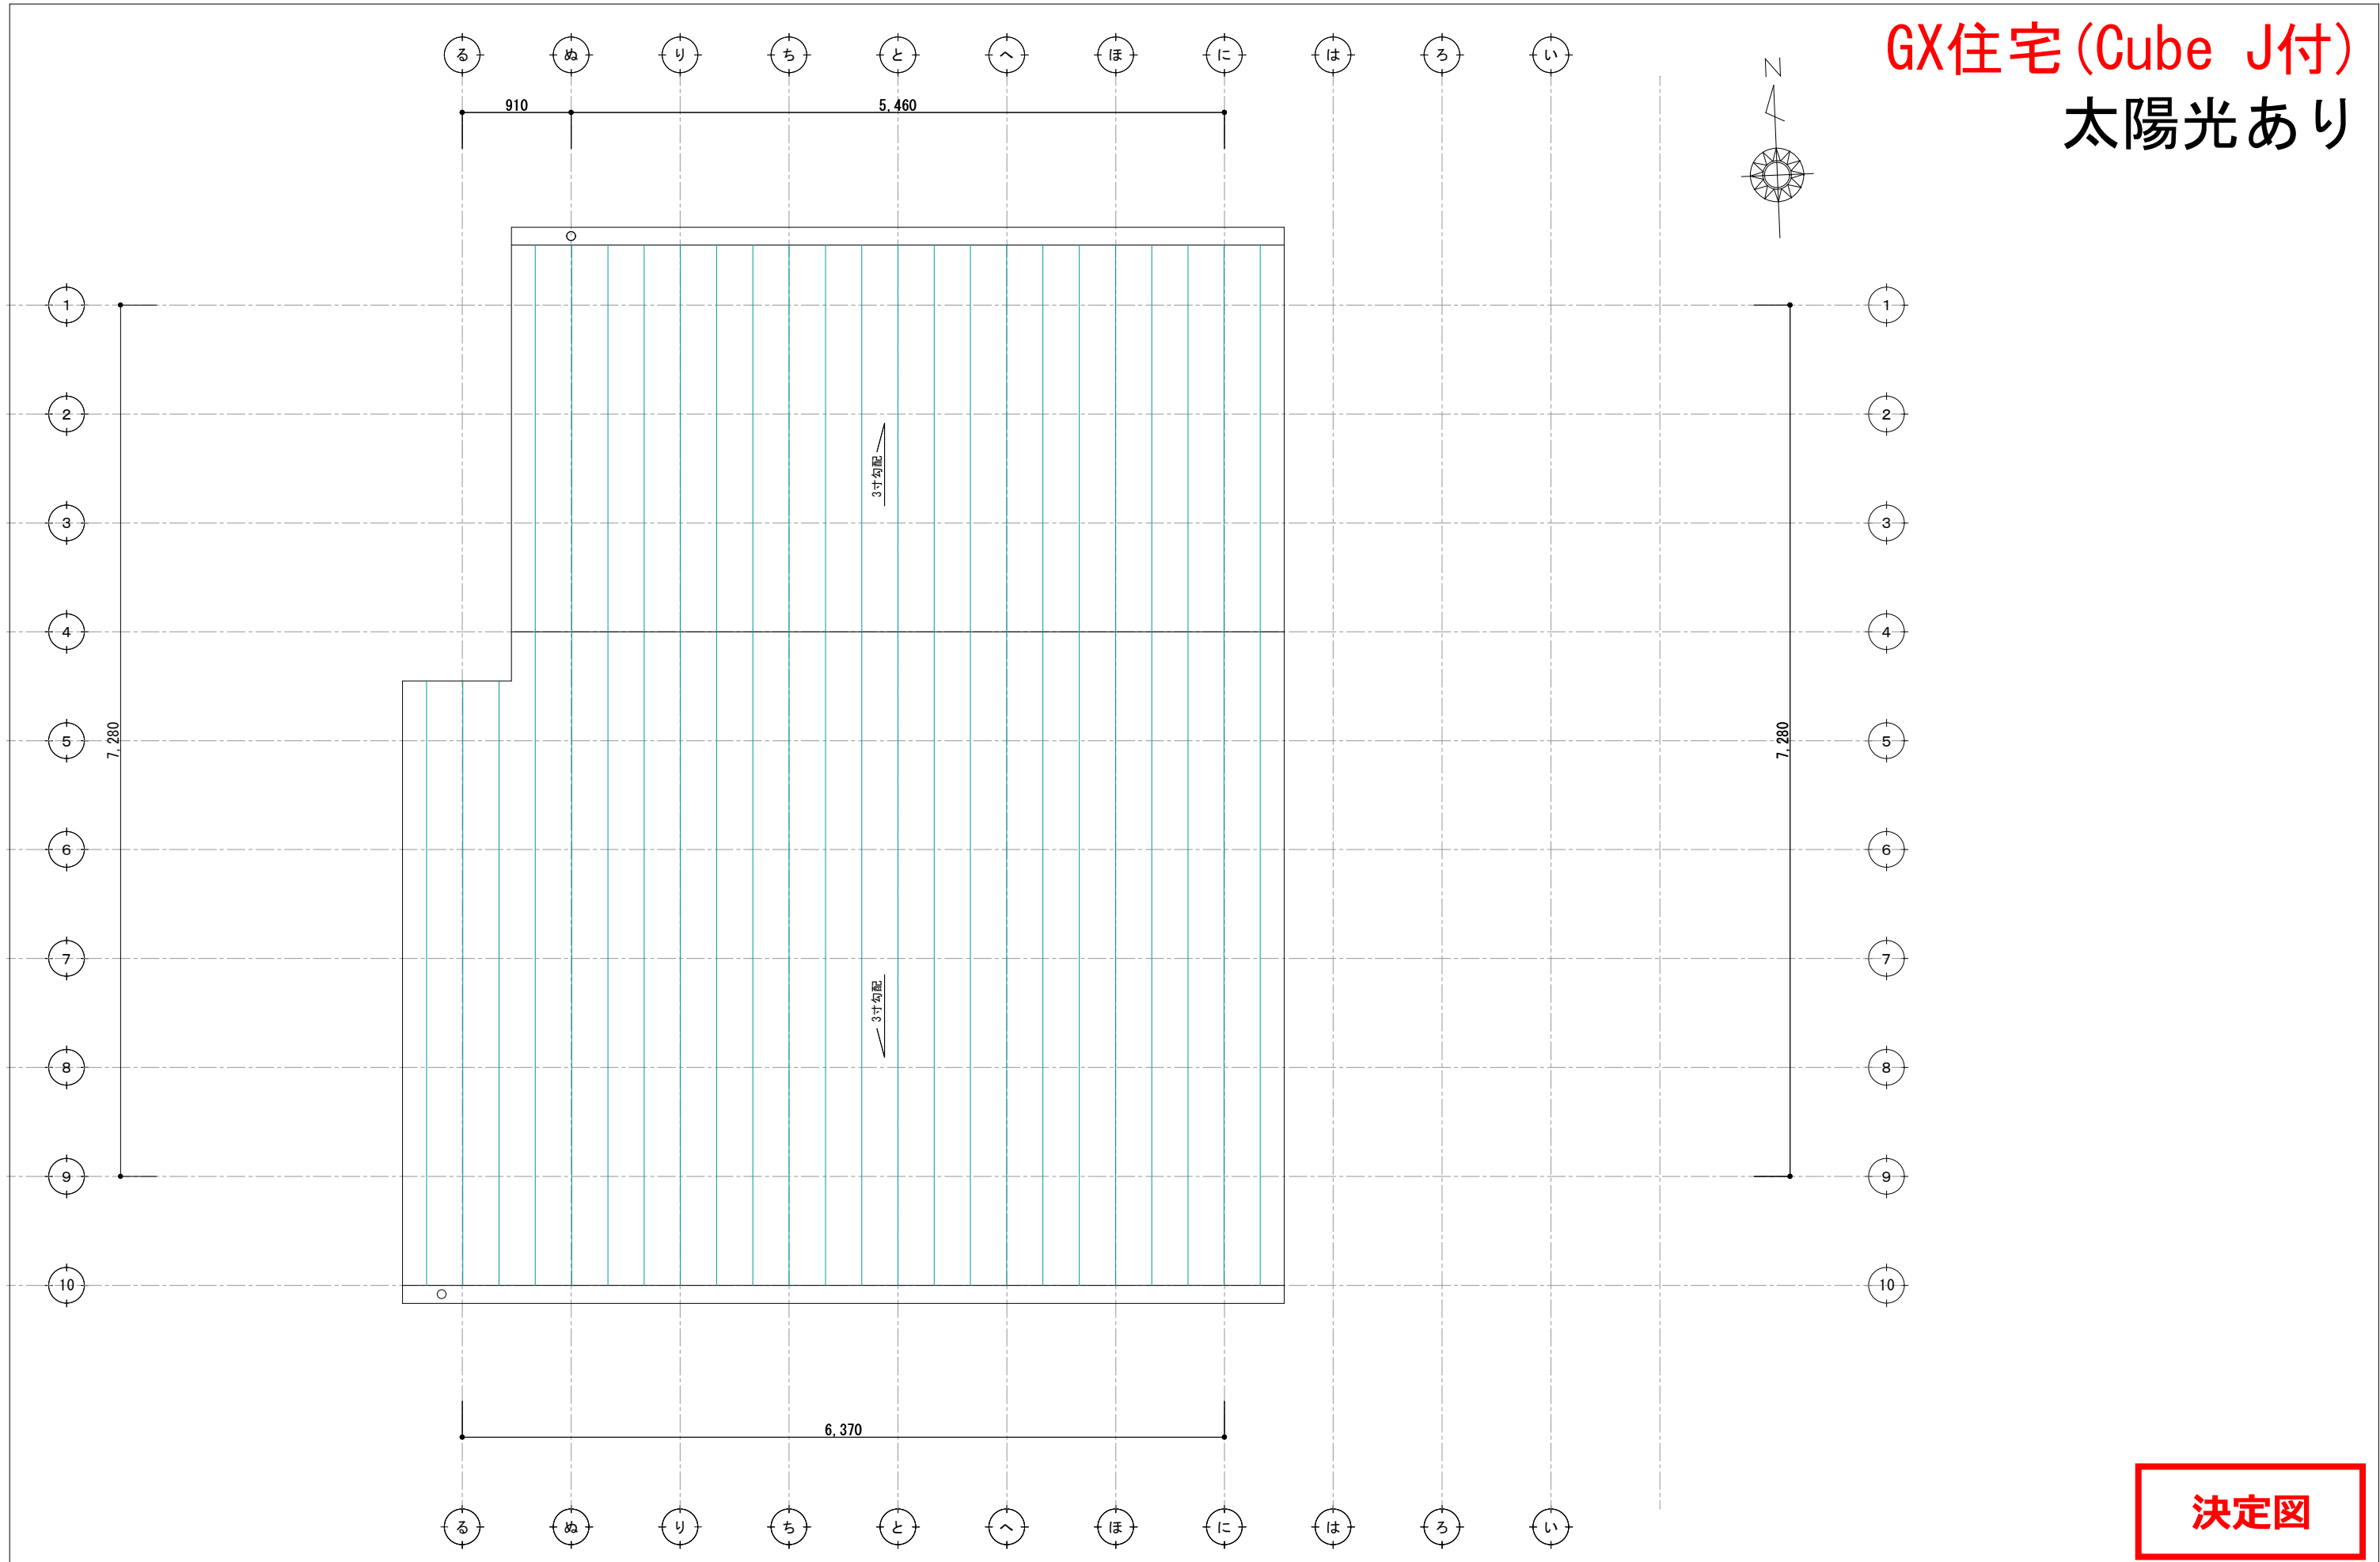


訂正	浜岡一級総合設計事務所			株式会社 LIFEFUND InDesign office 一級建築士事務所			年月日	件名		設計	IC	工事	図番
	一級建築士事務所 静岡県知事登録第 (10)2441 号			事務所登録 (2) 第7595号 一級建築士登録 第179770号 鈴木 達男			2025. 12. 28	山本卓矢様 寛子様新築工事		酒井		青島	3-3
	一級建築士 大臣登録第 365879 号 西原利昌			〒432-8023 静岡県浜松市中央区鴨江3丁目70番23号			縮尺	図名					

1/100

屋根伏図


G2

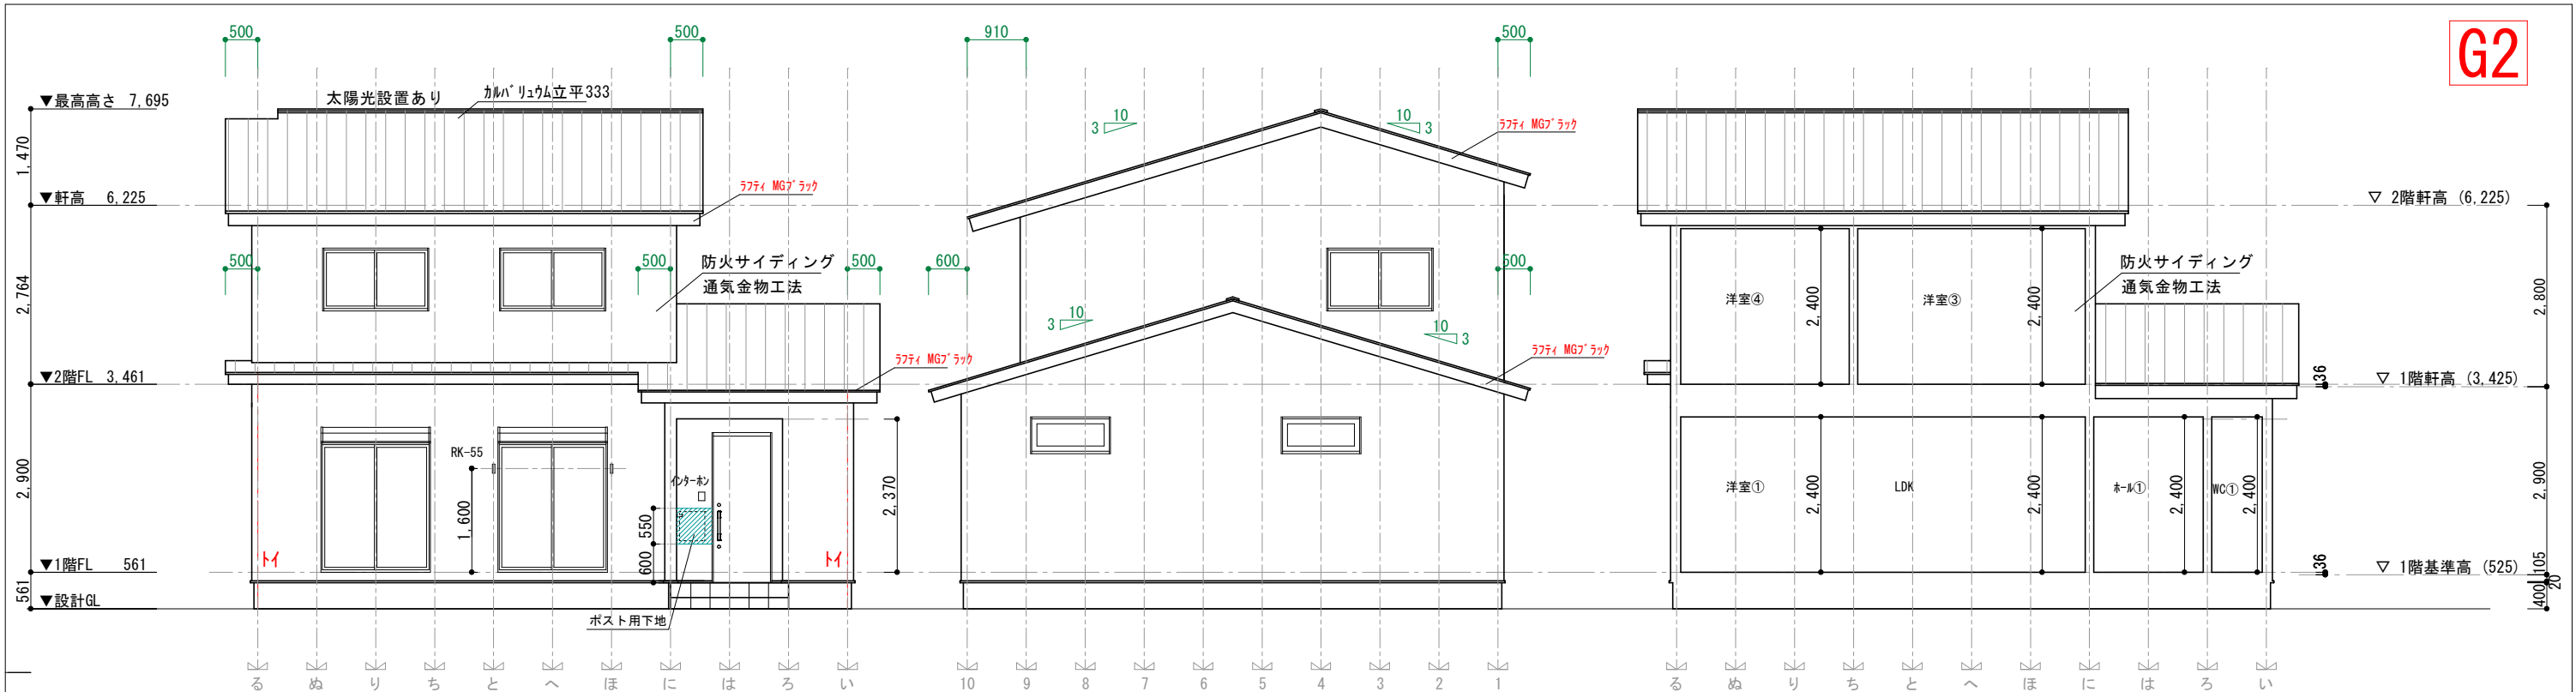

南側立面図 S=1/100

東側立面図 S=1/100

断面図（東西） S=1/100

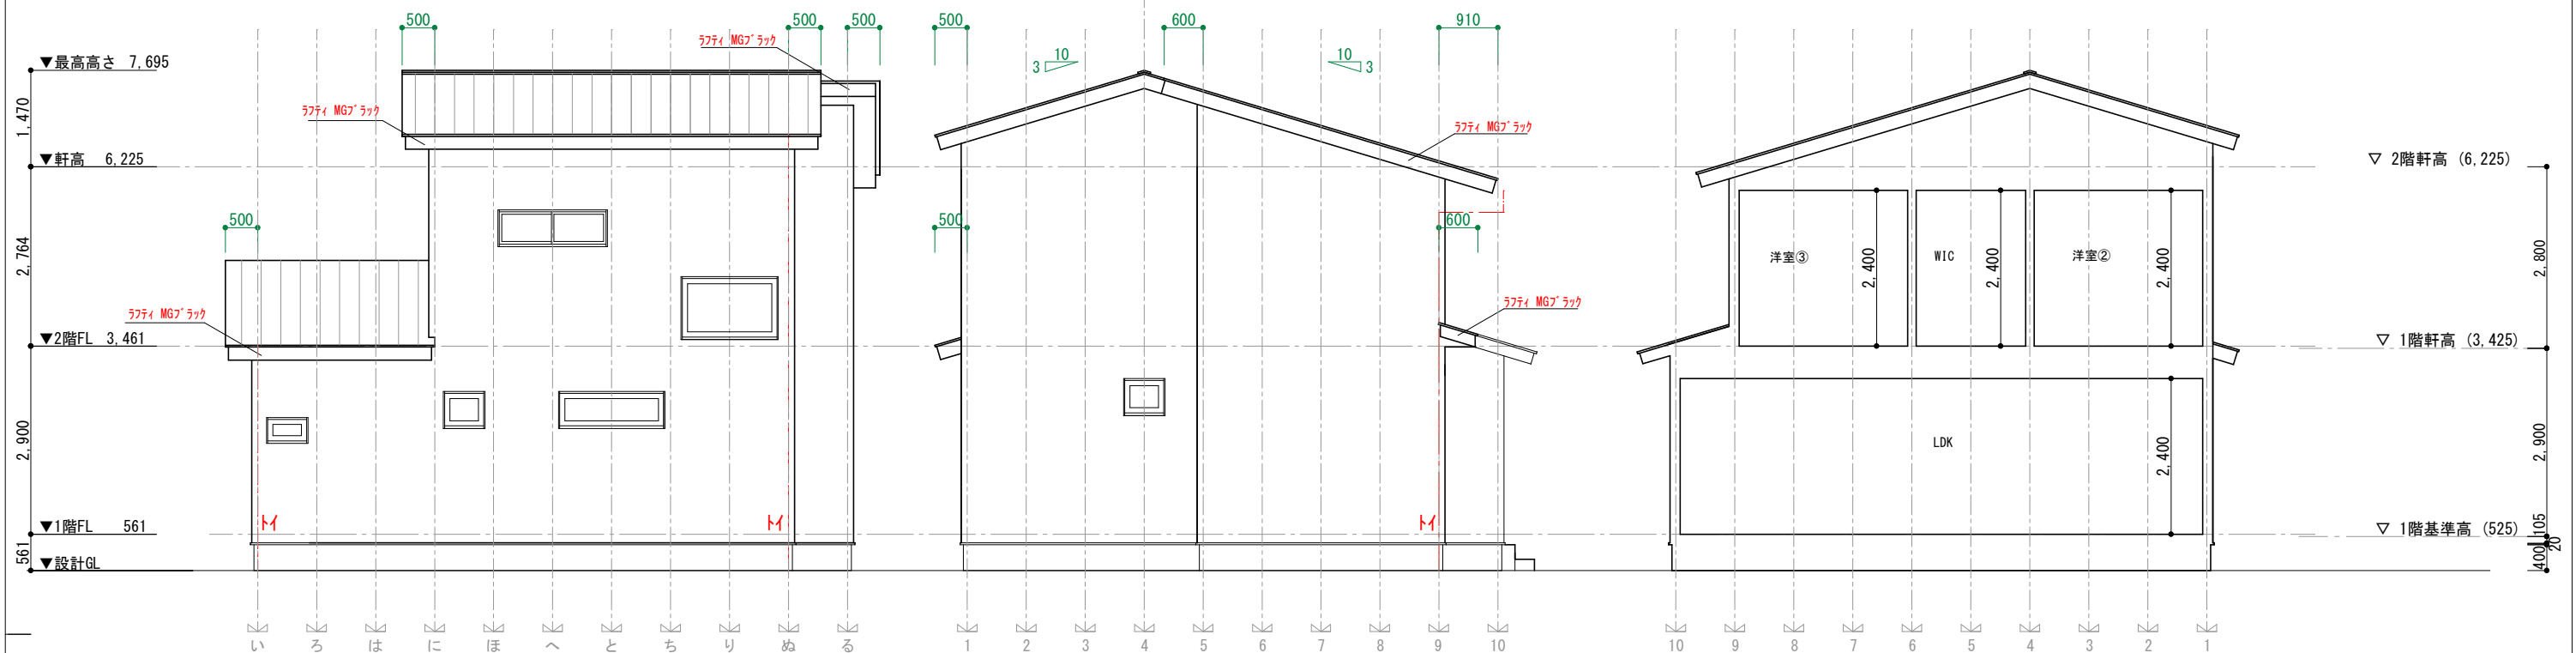


北側立面図 S=1/100

西側立面図 S=1/100


断面図（南北） S=1/100

決定図


訂正	浜岡一級総合設計事務所 一級建築士事務所 静岡県知事登録第 (10)2441 号 一級建築士 大臣登録第 365879 号 西原利昌	PG HOUSE	株式会社 LIFEFUND InDesign office 一級建築士事務所 事務所登録 (2) 第7595号 一級建築士登録 第179770号 鈴木 達男 〒432-8023 静岡県浜松市中央区鴨江3丁目70番23号	年月日 2025. 12. 28 縮尺 1/100	件名 山本卓矢様 寛子様邸 新築工事 図名 立面図		設計 酒井	IC	工事 青島	図番 4
----	--	----------	---	------------------------------------	------------------------------------	--	----------	----	----------	---------

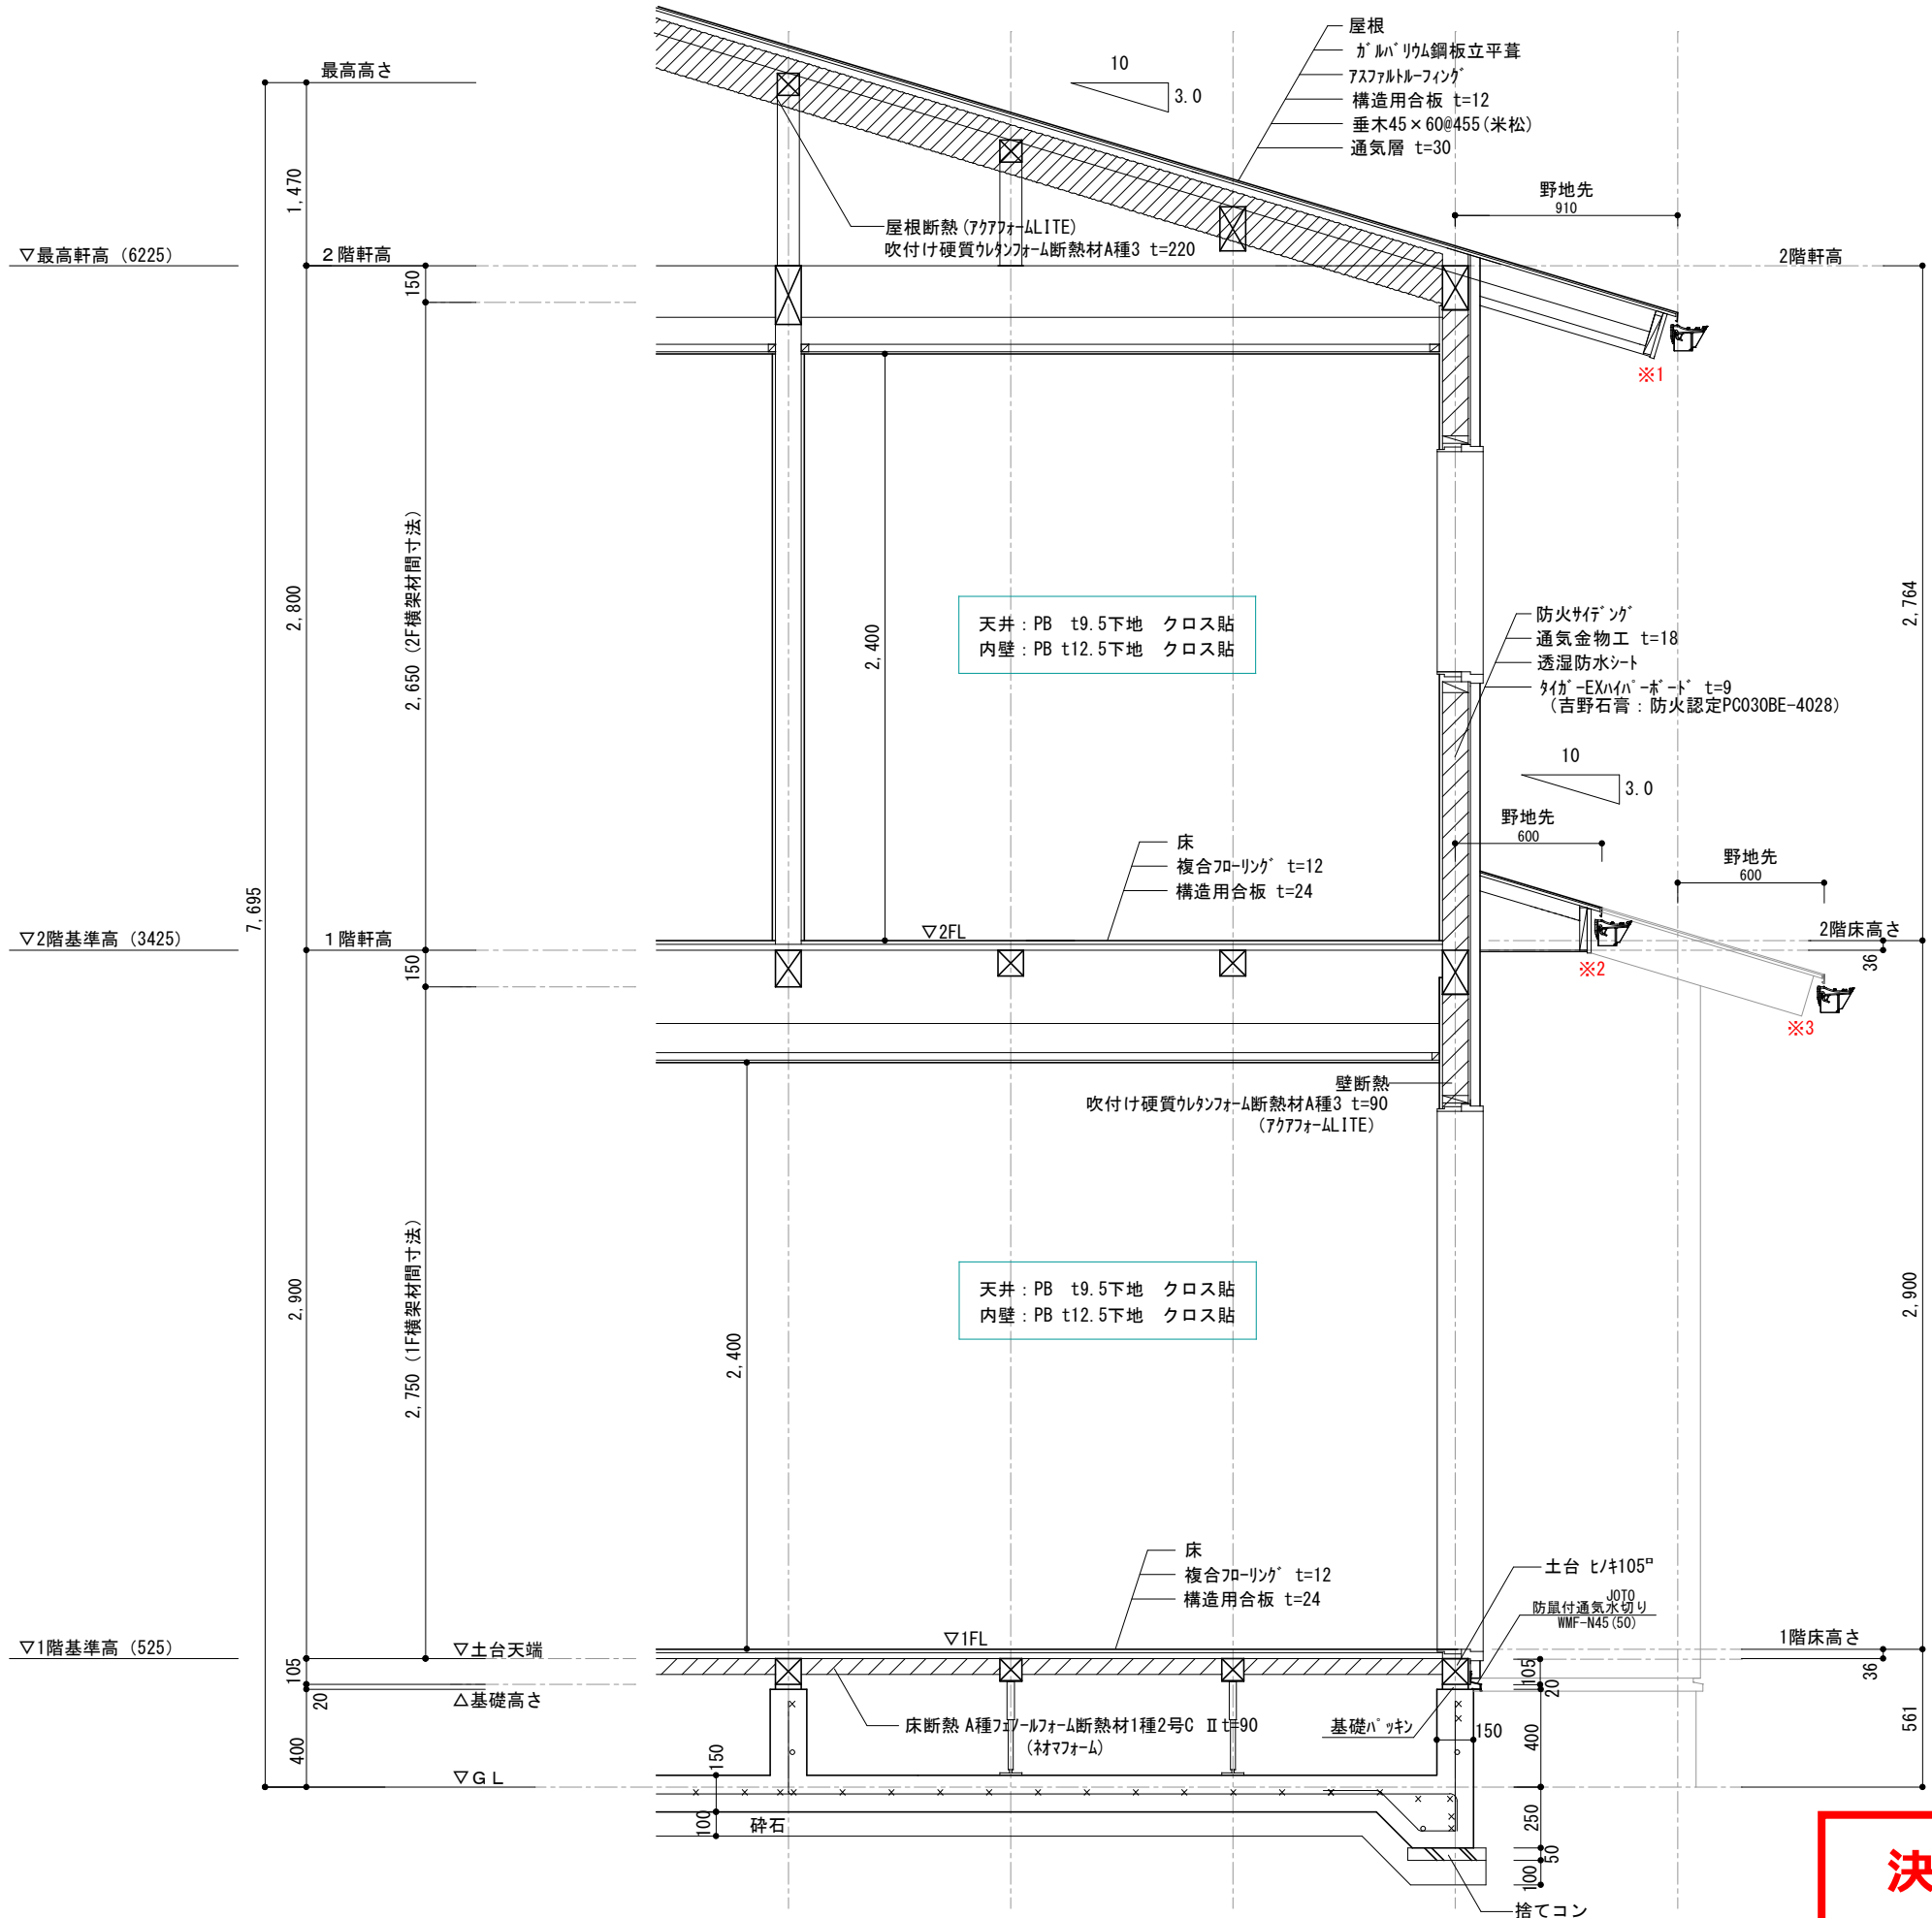


太陽光パネル有 G-2

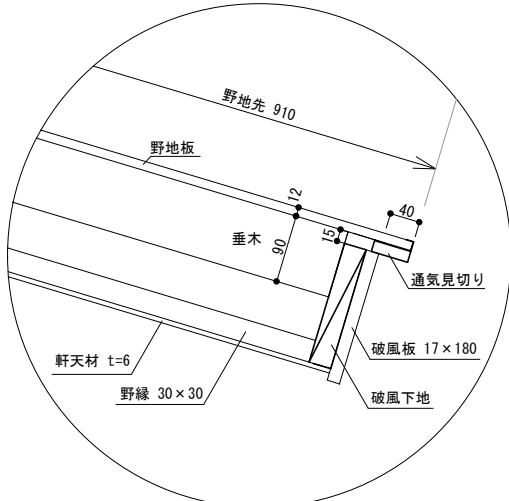

※1 軒先 納まり

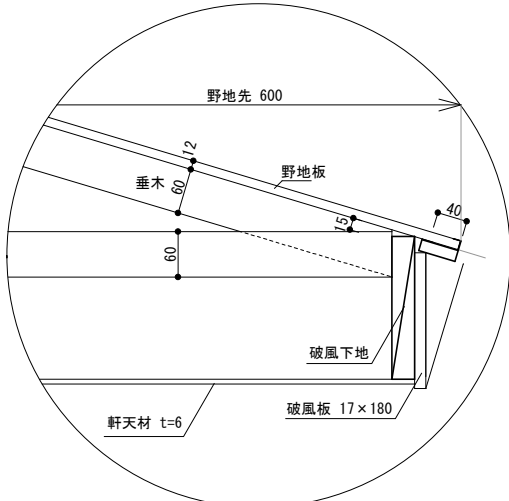


※2 軒先 納まり

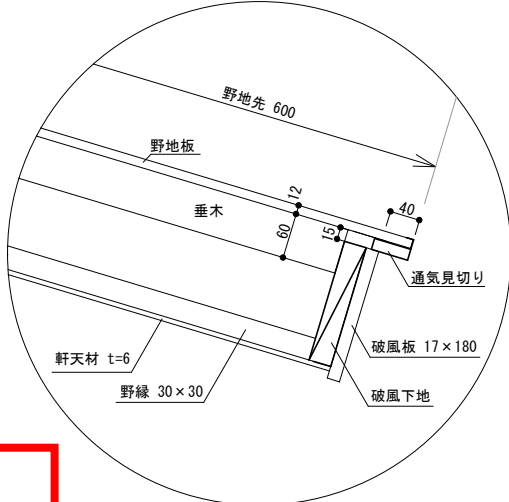


※3 軒先 納まり

決定図


訂正	浜岡一級総合設計事務所		株式会社 LIFEFUND InDesign office		年月日	件名	設計	IC	工事	図番
	一級建築士事務所 静岡県知事登録第 (10)2441 号		事務所登録 (2) 第7595号 一級建築士登録 第179770号 鈴木 達男		2025. 12. 28	山本卓矢様 寛子様 邸新築工事				
	一級建築士 大臣登録第 365879 号 西原利昌		〒432-8023 静岡県浜松市中央区鴨江3丁目70番23号		縮尺	図名				
	PG HOUSE				1/30	矩計図	酒井		青島	5

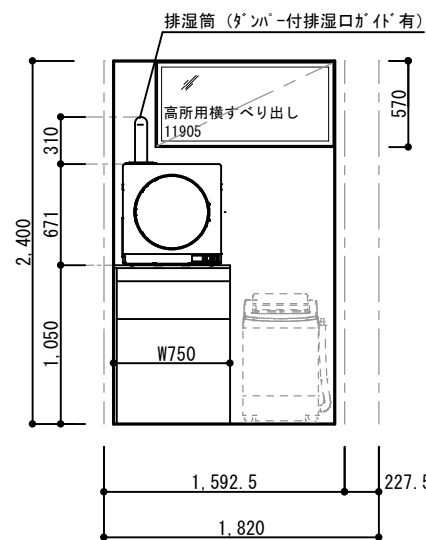


脱衣ランドリー 東面

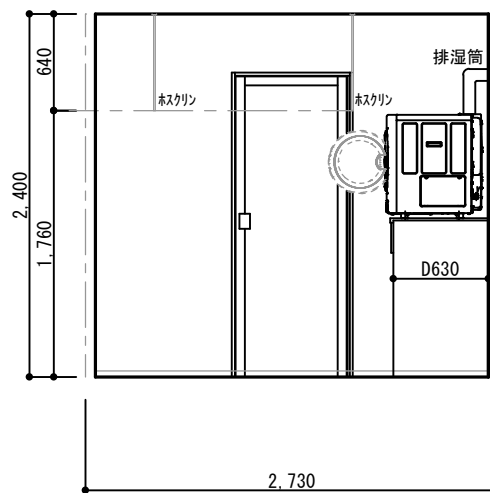


脱衣ランドリー 北面

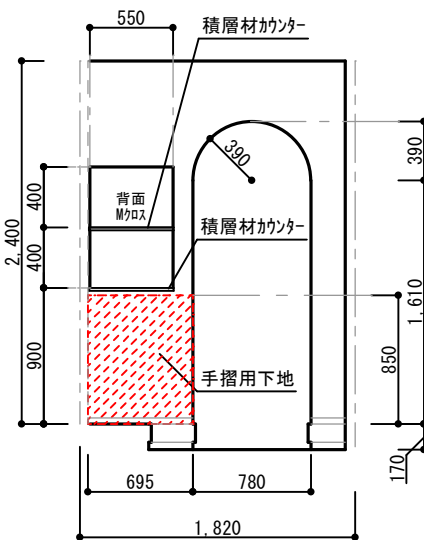


玄関 東面

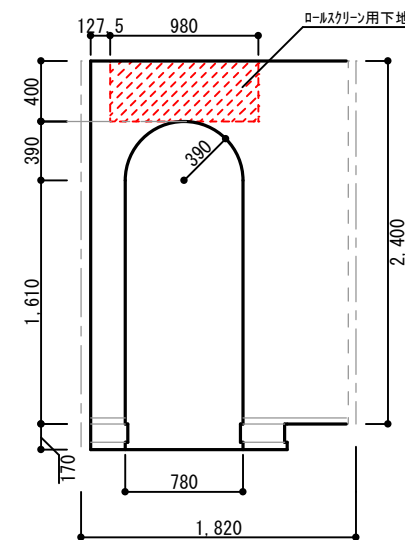


SC 東面

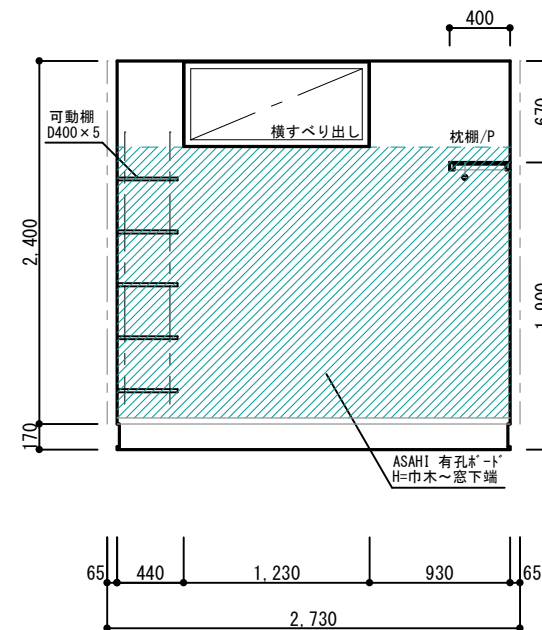

SC 東面

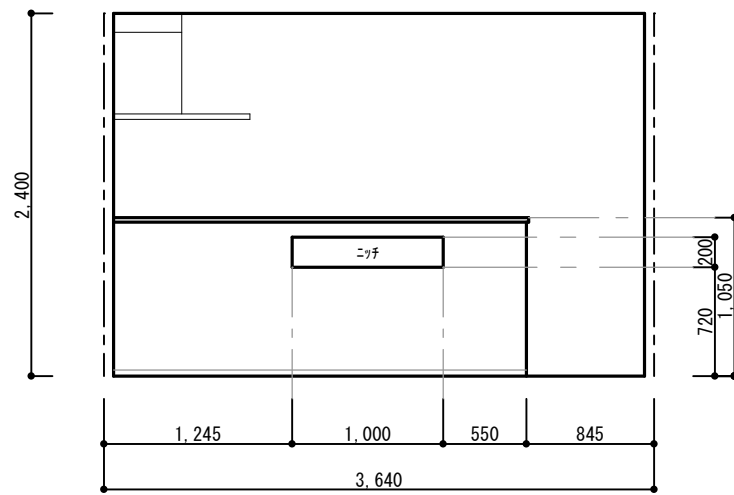


キッチン 南側

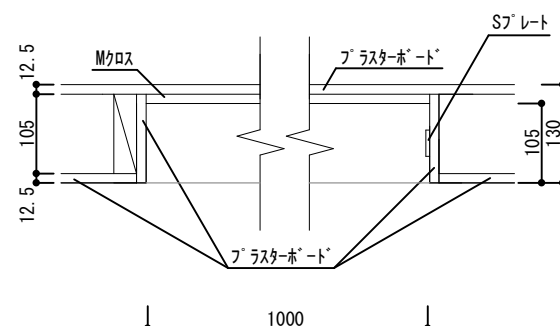


※ニッチ内部は全面クロス仕上げ


キッチン ニッチ 上部断面図

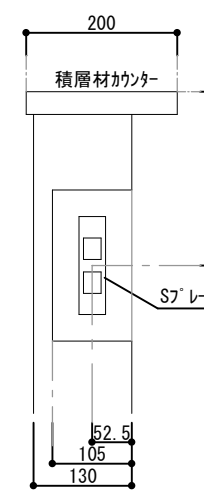


キッチン ニッチ 断面図

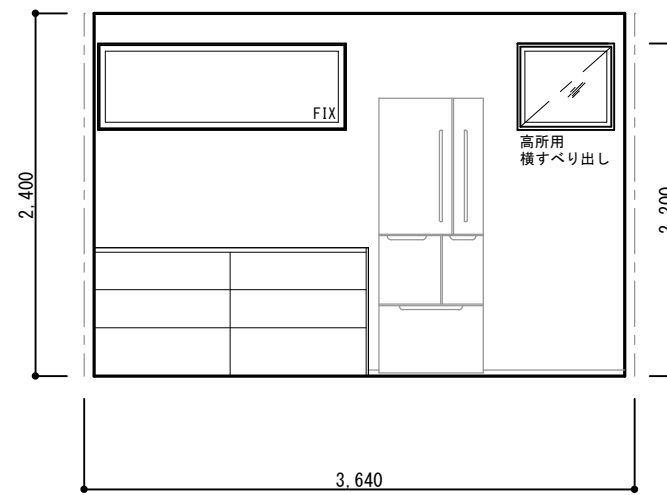


LDK 北面

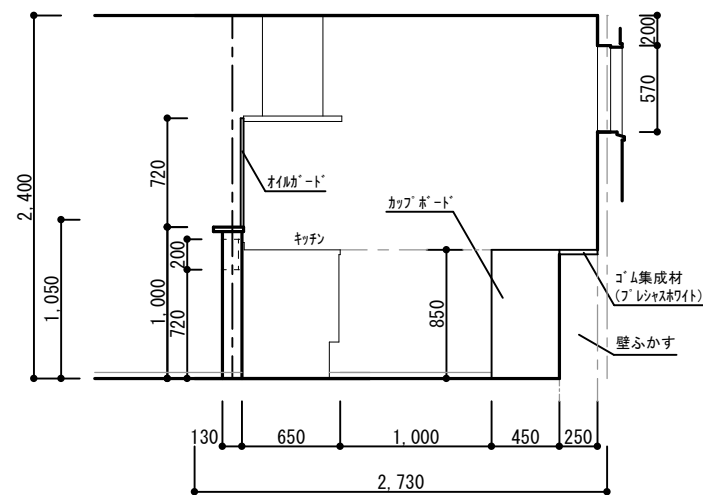


キッチン 西面

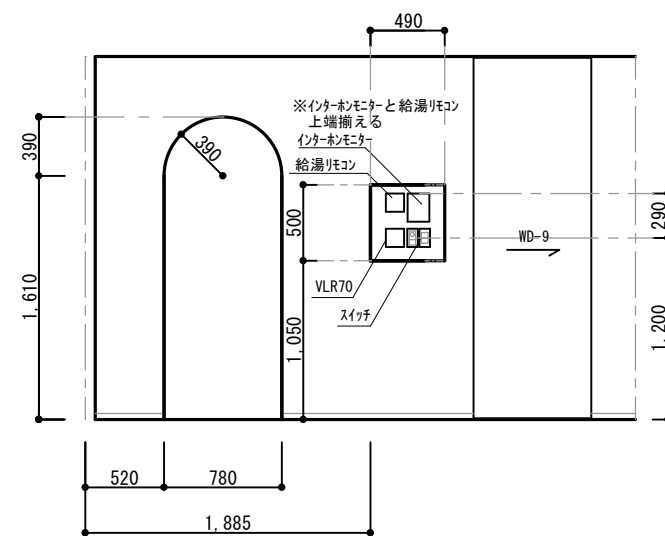

LDK 東面

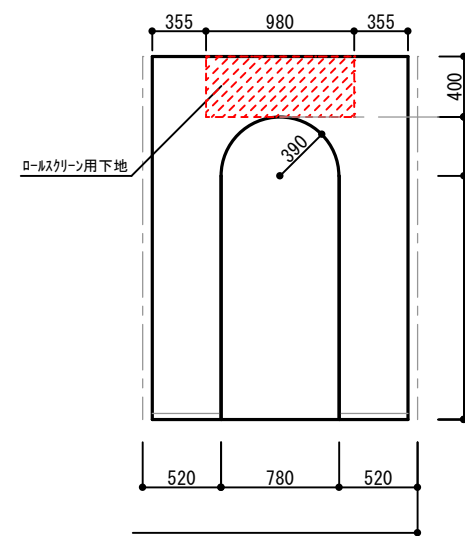













ハントリー 西面

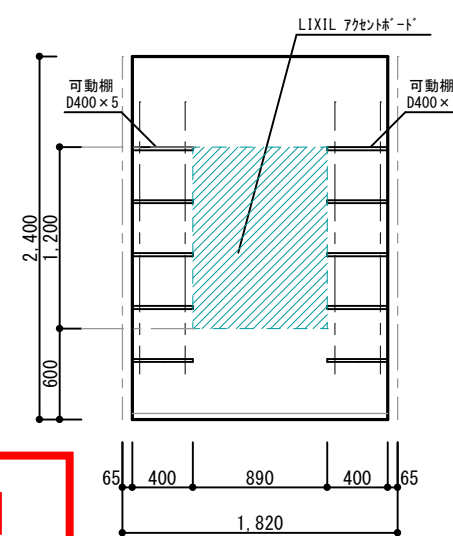

ハントリー 東面


決定図

訂正	浜岡一級総合設計事務所 一級建築士事務所 静岡県知事登録第 (10)2441 号 一級建築士 大臣登録第 365879 号 西原利昌	LIFEFUND PG HOUSE	株式会社 LIFEFUND InDesign office 一級建築士事務所 事務所登録 (2)第7595号 一級建築士登録 第179770号 鈴木 達男 〒432-8023 静岡県浜松市中央区鶴江3丁目70番23号	年月日 2025.12.28	件名 山本卓矢様 寛子様 新築工事	縮尺 1/50	図名 展開図-1	設計 酒井	IC	工事 青島	図番 6-1
----	--	----------------------	--	-------------------	----------------------	------------	-------------	----------	----	----------	-----------

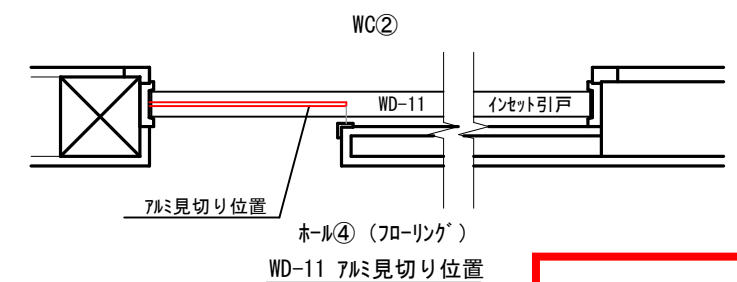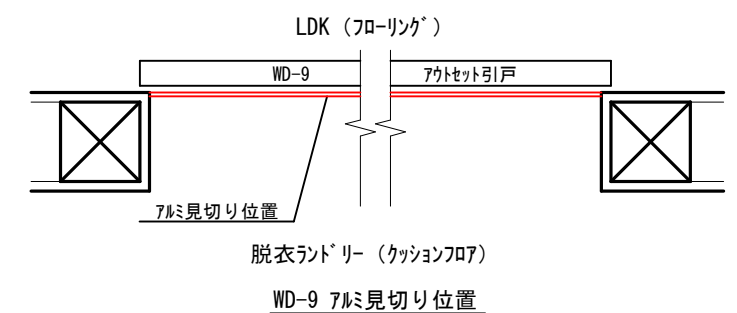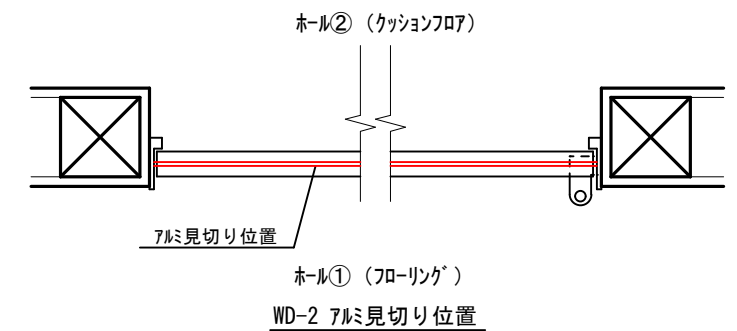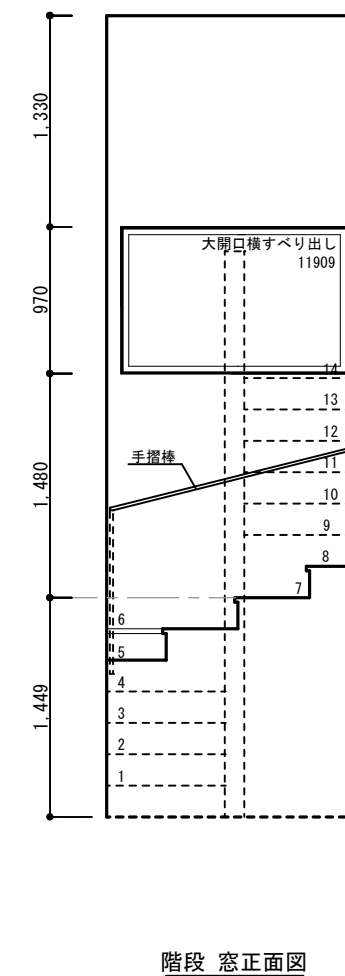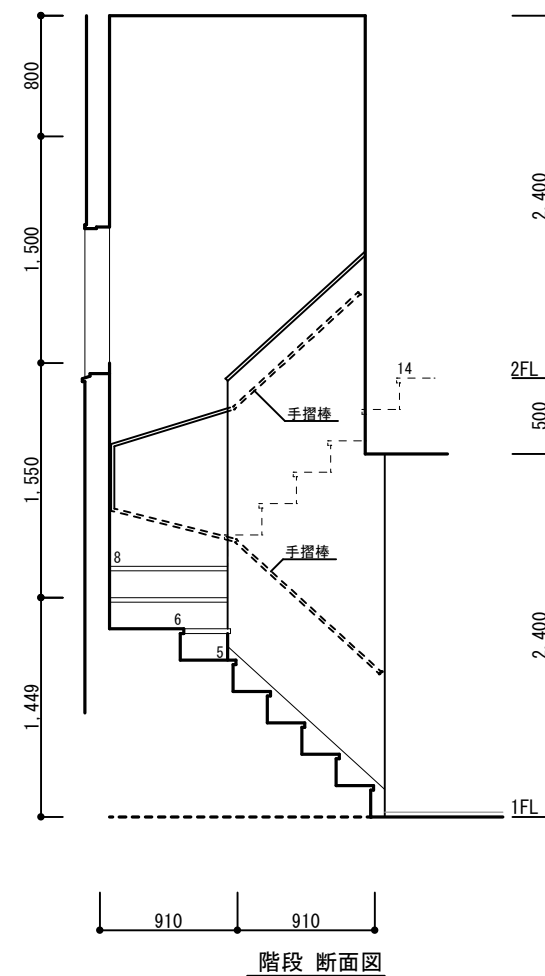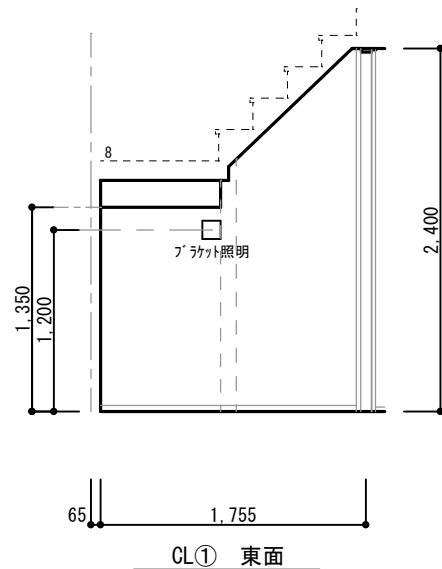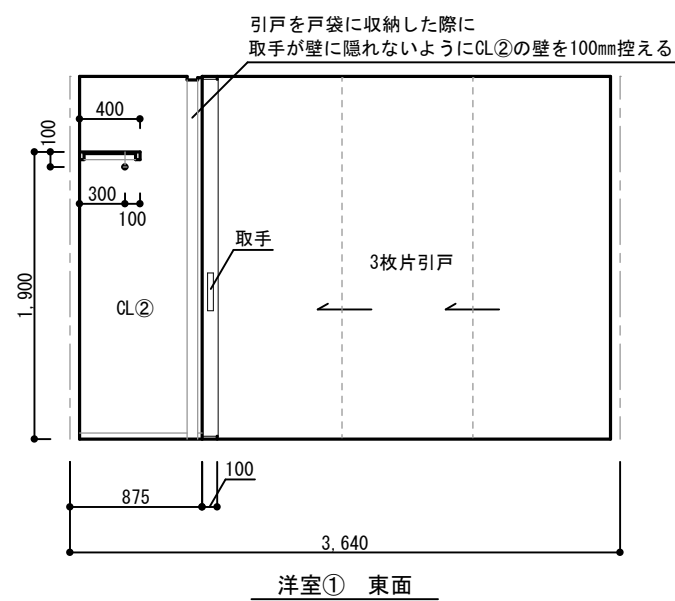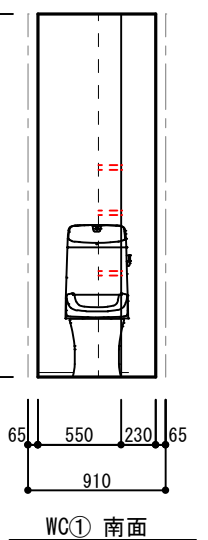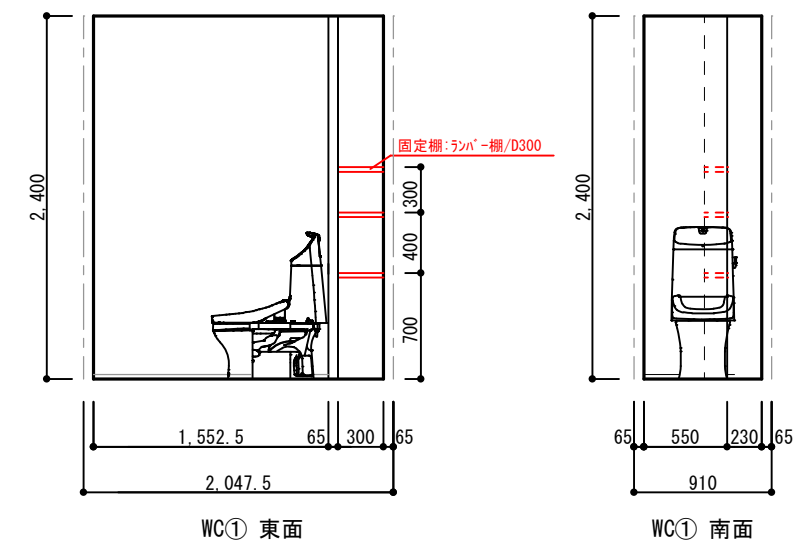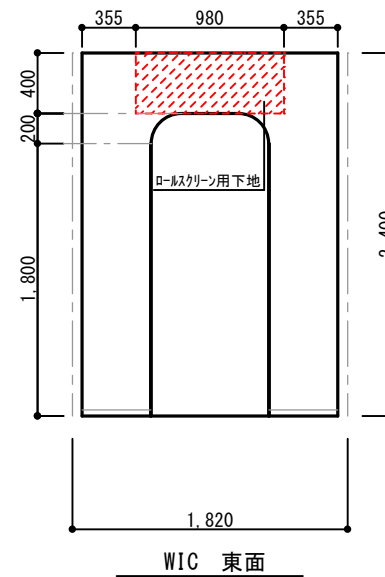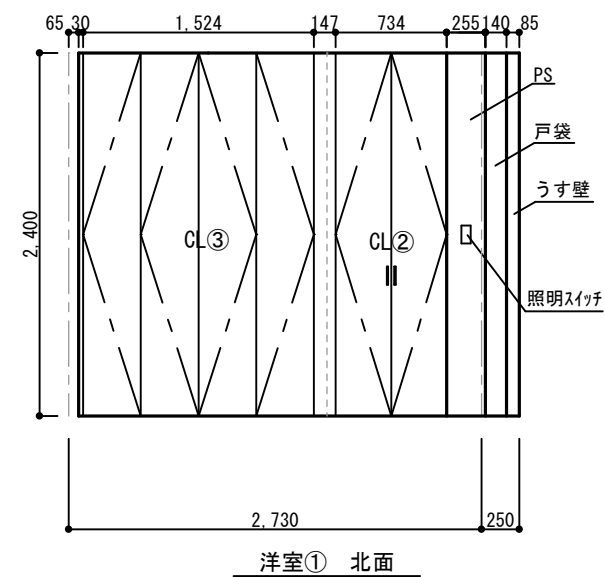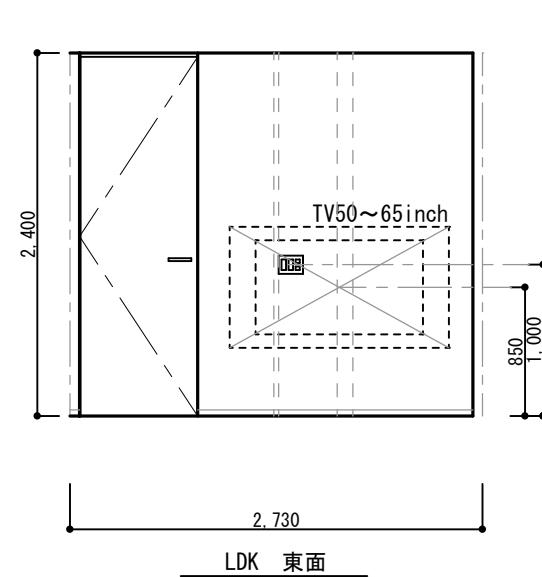


決定図

訂 正	浜 岡 一 級 総 合 設 計 事 務 所 一級建築士事務所 静岡県知事登録第 (10)2441 号 一級建築士 大臣登録第 365879 号 西原利昌	LIFEFUND PG HOUSE	株式会社 LIFEFUND InDesign office 一級建築士事務所 事務所登録 (2) 第7595号 一級建築士登録 第179770号 鈴木 達男 〒432-8023 静岡県浜松市中央区鴨江3丁目70番23号	年 月 日	件 名 山本卓矢様 寛子様 新築工事	設計	10	工事	図 番	
				2025. 12. 28						縮 尺
				1/50	展開図-2					

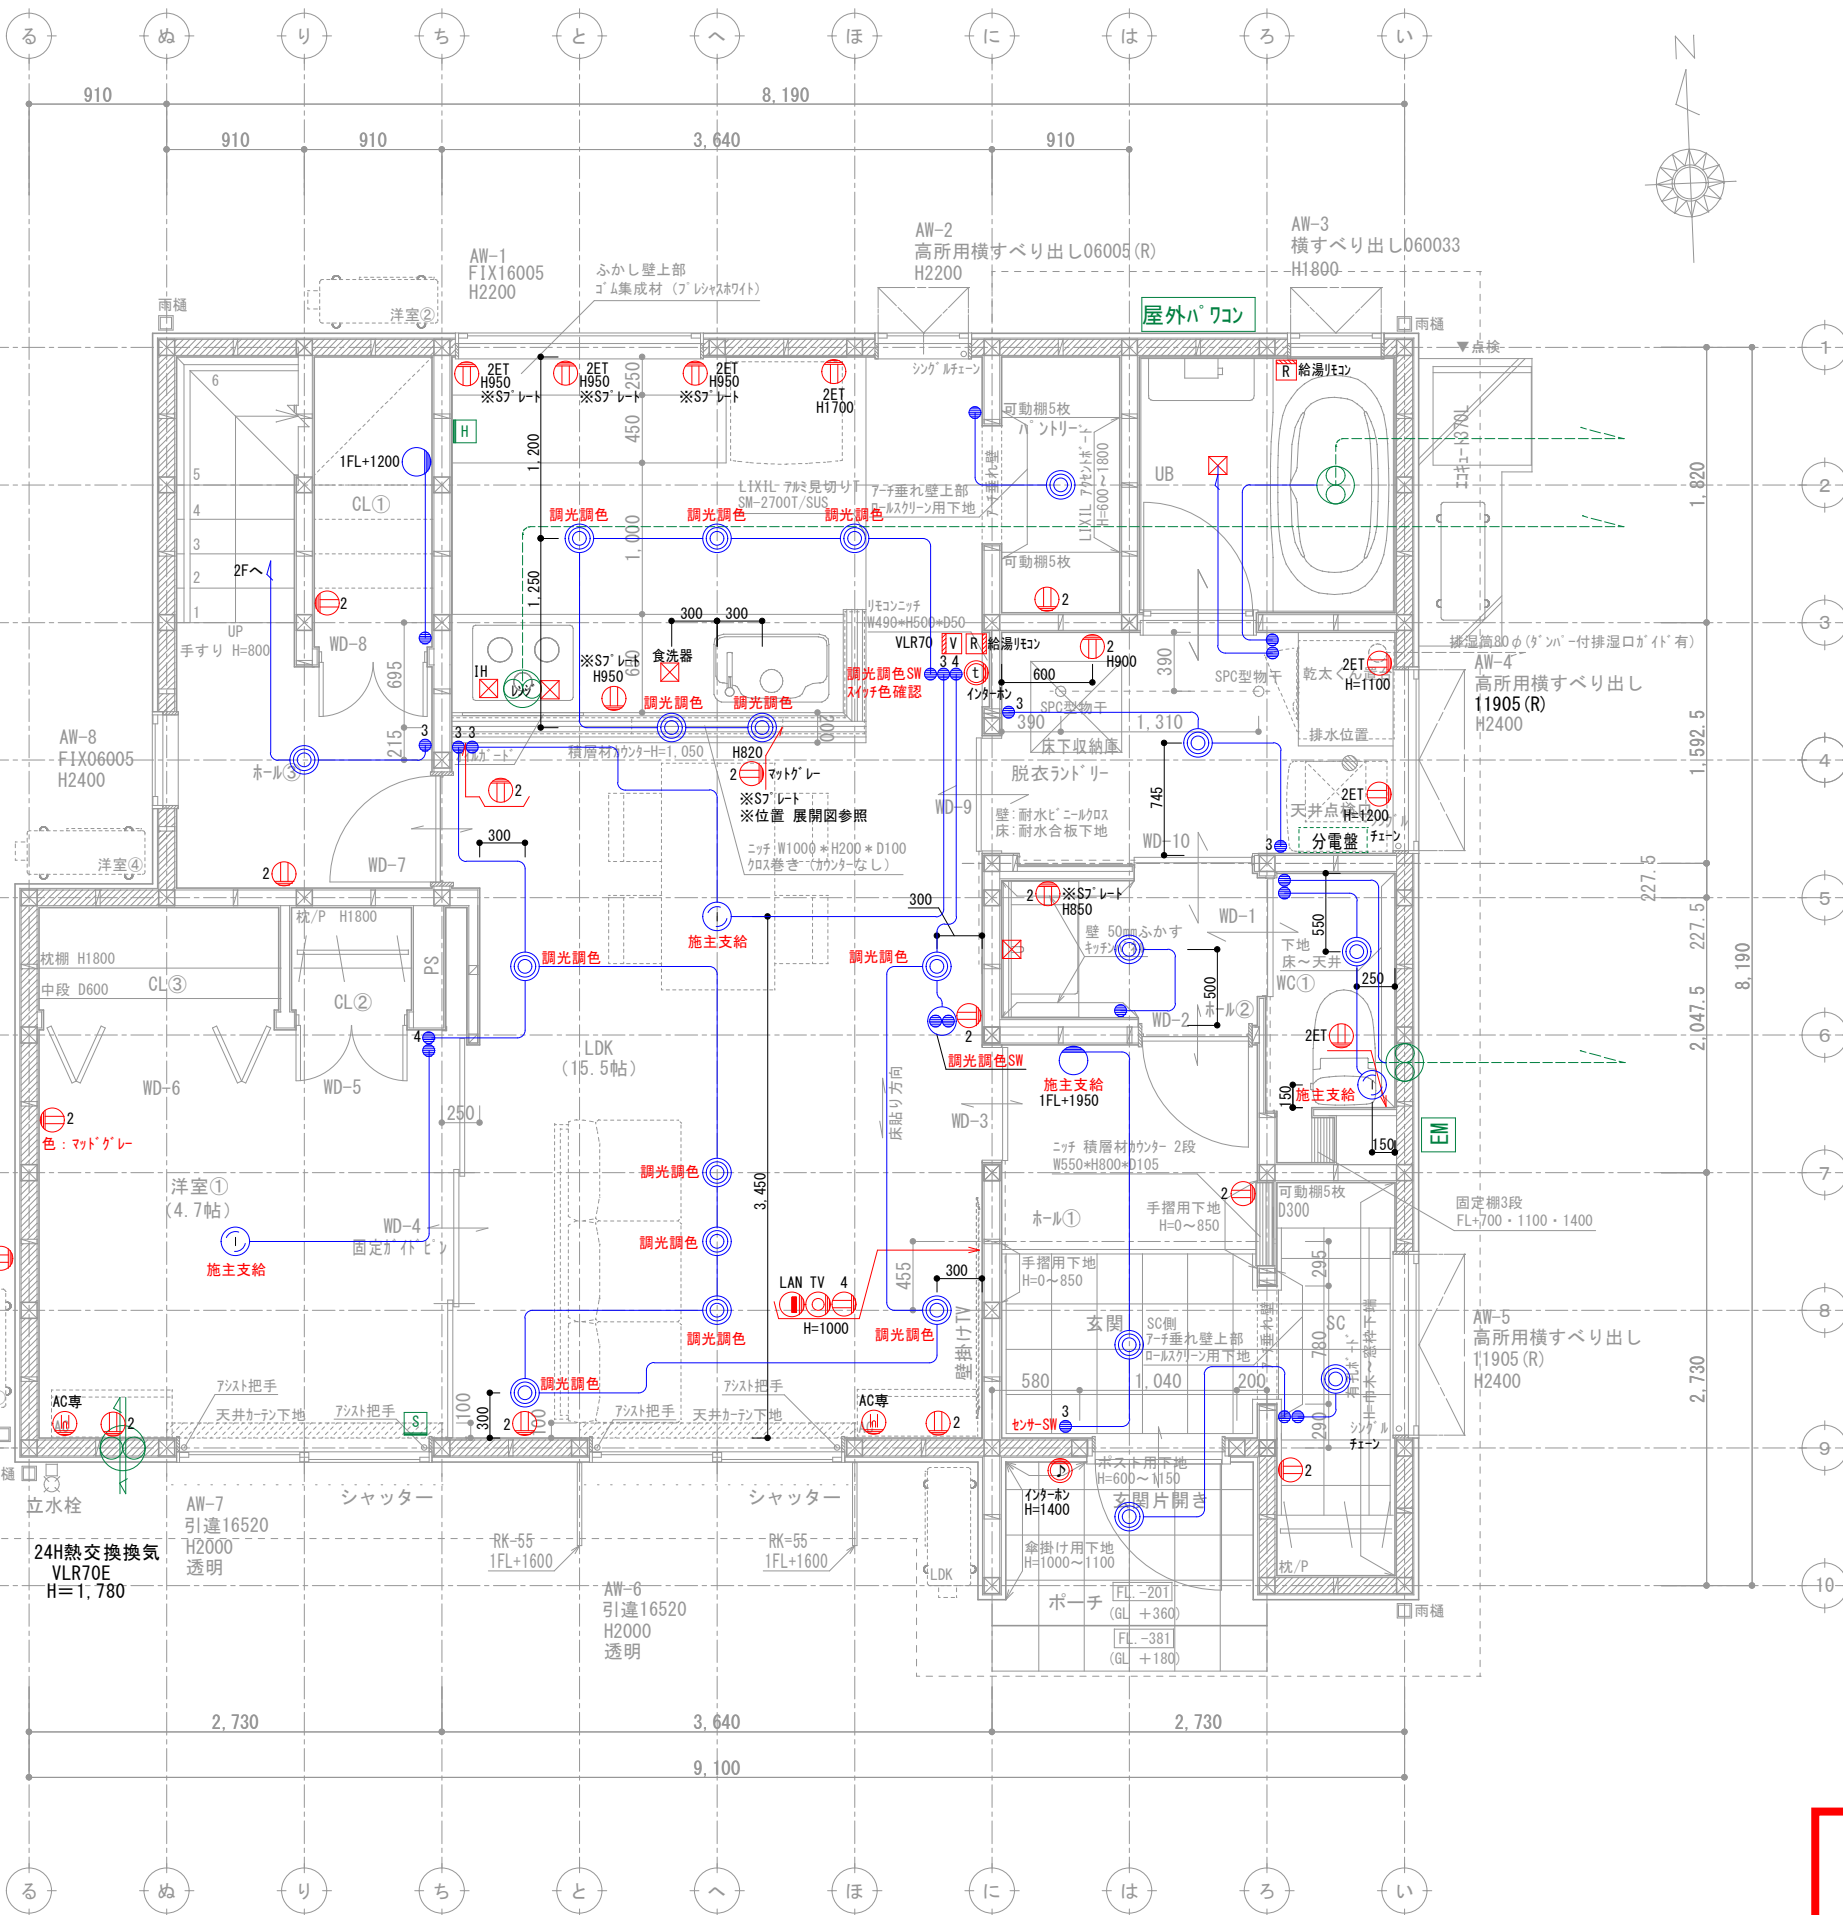

※ACコンセント天井付け
※TVアンテナ工事
※スイッチはFL+1100、コンセントはFL+200

決定図

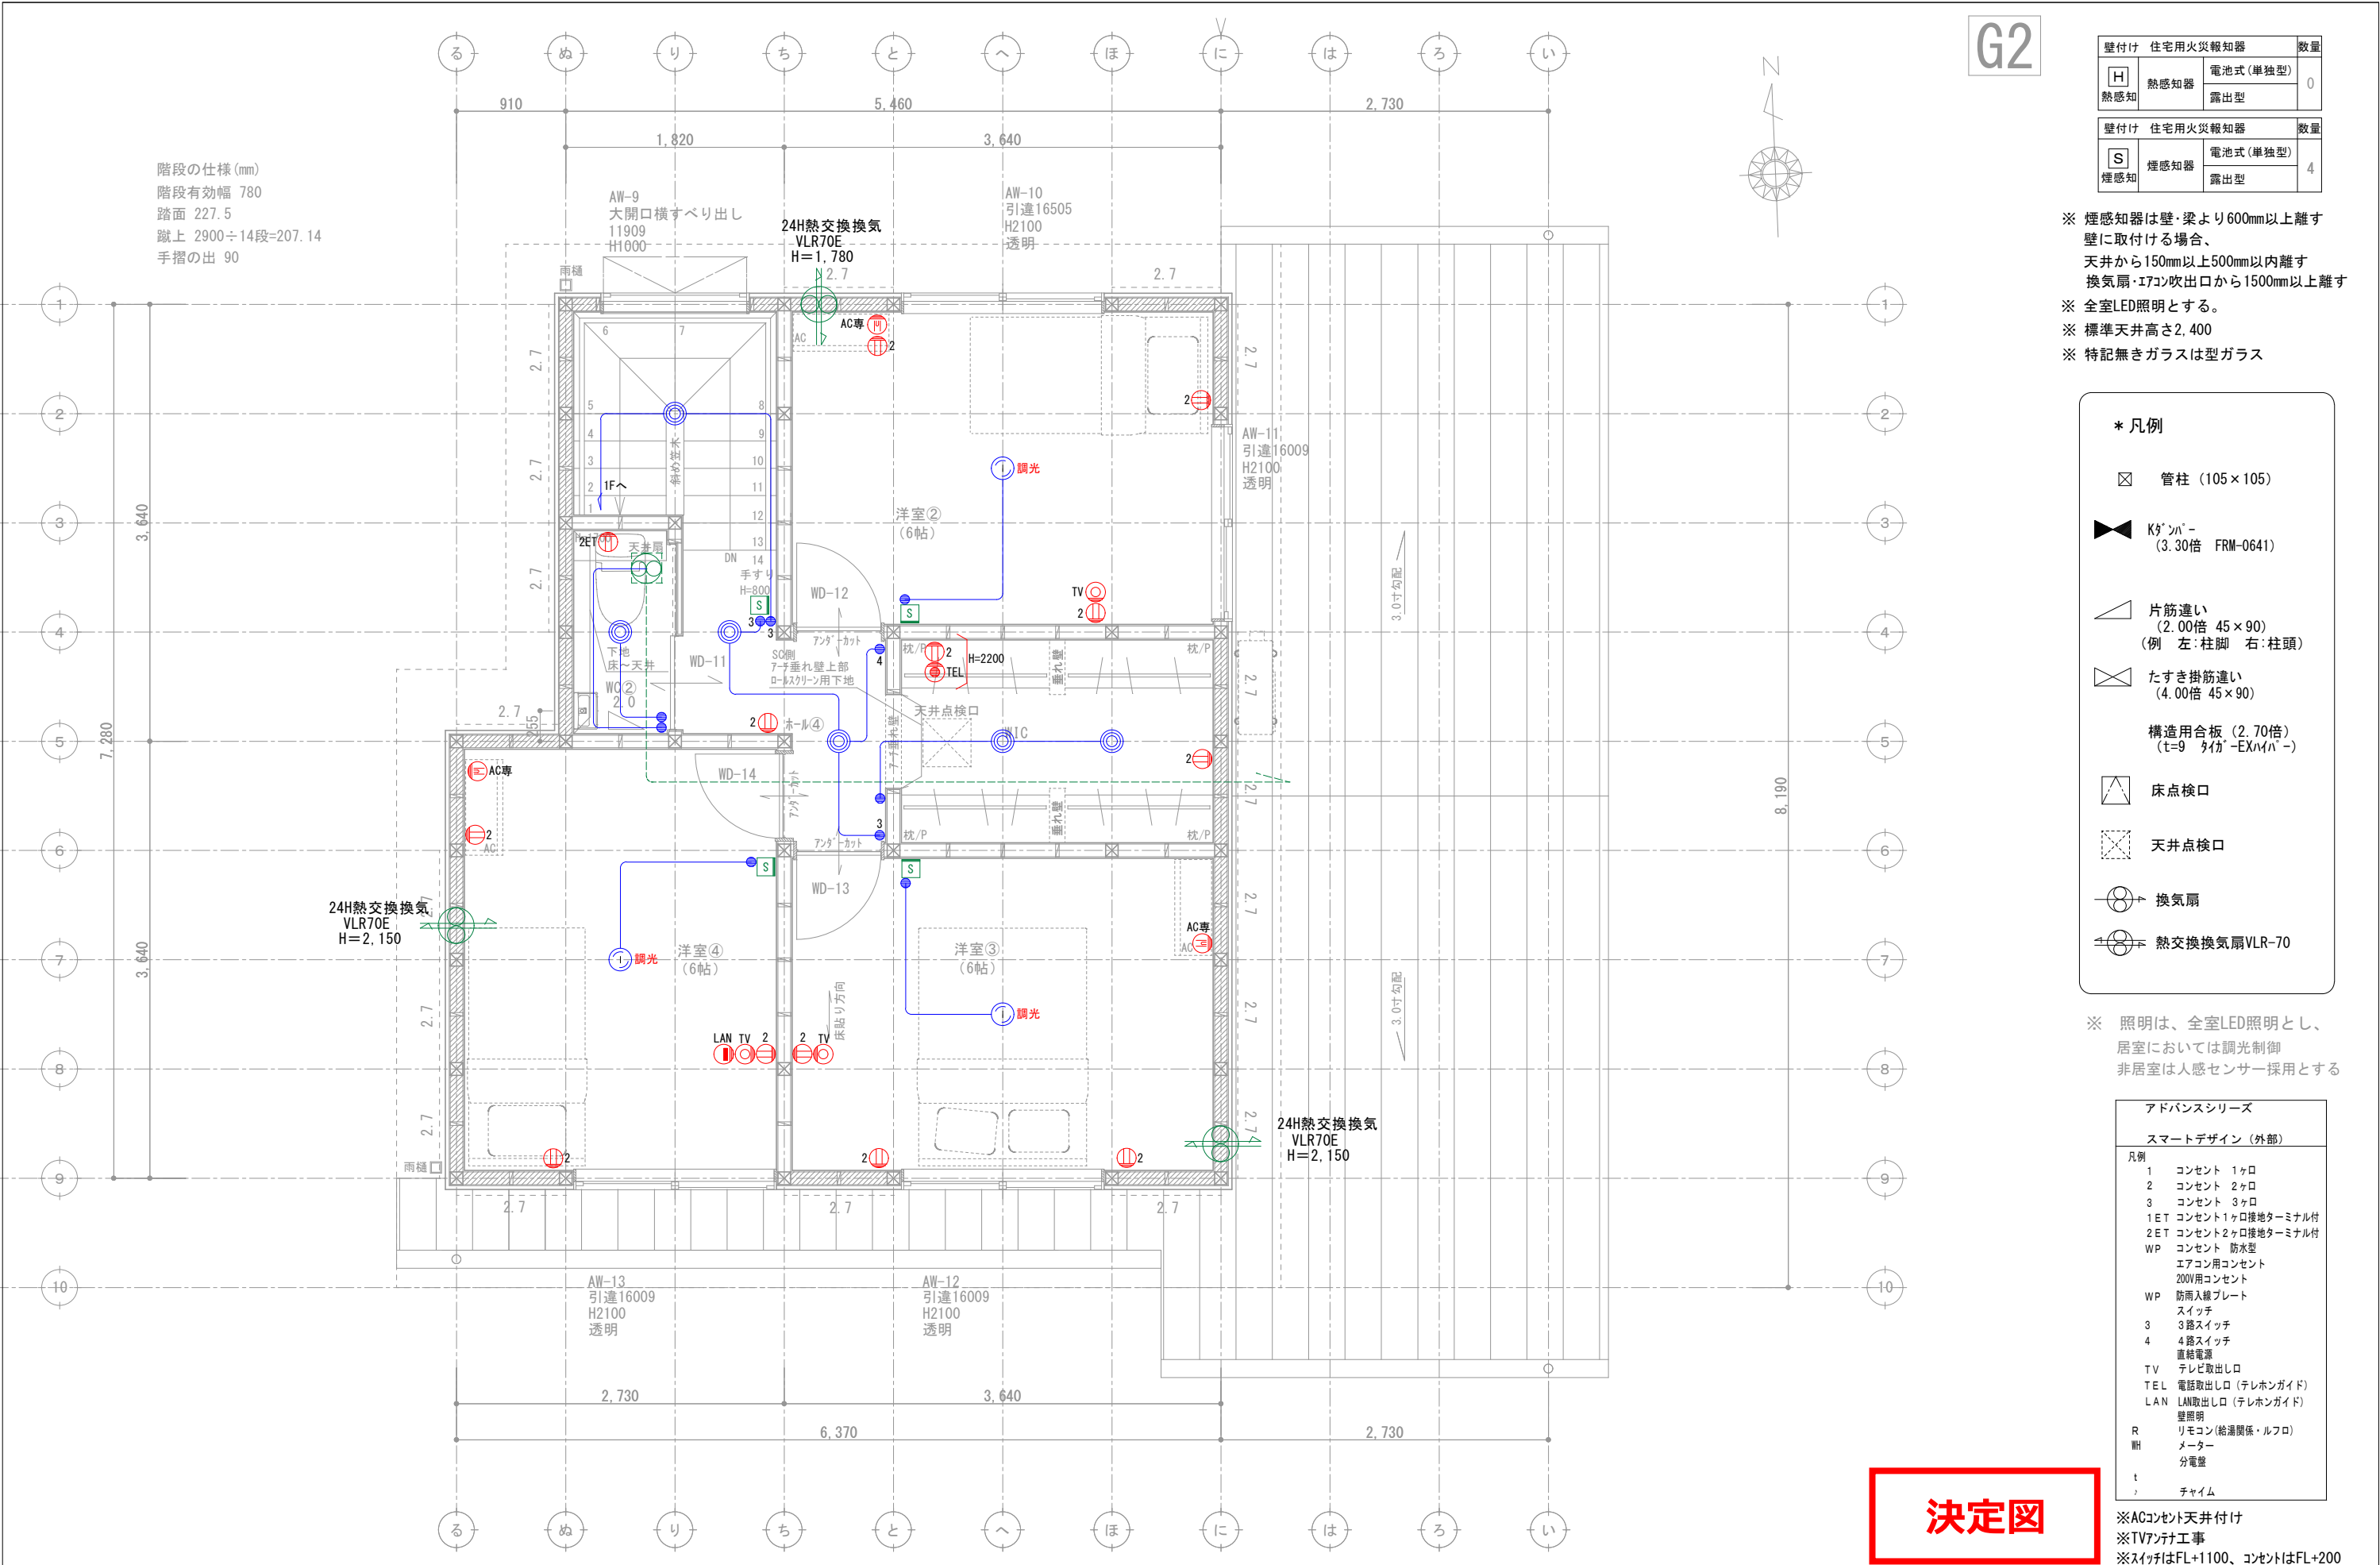

G2

壁付け 住宅用火災報知器			数量
H 熱感知	熱感知器	電池式(単独型)	0
		露出型	
壁付け 住宅用火災報知器			数量
S 煙感知	煙感知器	電池式(単独型)	4
		露出型	

- ※ 煙感知器は壁・梁より600mm以上離す
壁に取付ける場合、
天井から150mm以上500mm以内離す
換気扇・エアコン吹出口から1500mm以上離す
- ※ 全室LED照明とする。
- ※ 標準天井高さ2,400
- ※ 特記無きガラスは型ガラス

*** 凡例**

☒ 管柱 (105×105)

◀▶ Kダクト (3.30倍 FRM-0641)

◀▶ 片筋違い (2.00倍 45×90)
(例 左:柱脚 右:柱頭)

◀▶ たすき掛筋違い (4.00倍 45×90)

◀▶ 構造用合板 (2.70倍)
(t=9 材種-EXハイバ-)

◀▶ 床点検口

◀▶ 天井点検口

⊙→ 換気扇

⊙⇄ 熱交換換気扇VLR-70

- ※ 照明は、全室LED照明とし、
居室においては調光制御
非居室は人感センサー採用とする

アドバンスシリーズ			
スマートデザイン (外部)			
凡例	1	コンセント	1ヶ所
	2	コンセント	2ヶ所
	3	コンセント	3ヶ所
	1ET	コンセント1ヶ所接地ターミナル付	
	2ET	コンセント2ヶ所接地ターミナル付	
WP	コンセント	防水型	
	エアコン用コンセント		
	200V用コンセント		
WP	防雨入線プレート		
	スイッチ		
3	3路スイッチ		
4	4路スイッチ		
	直結電源		
TV	テレビ取出口		
TEL	電話取出口 (テレホンガイド)		
LAN	LAN取出口 (テレホンガイド)		
	壁照明		
R	リモコン (給湯関係・ルフロ)		
MH	メーター		
	分電盤		
t	チャイム		

- ※ACコンセント天井付け
- ※TVアンテナ工事
- ※スイッチはFL+1100、コンセントはFL+200

決定図

ポーチ灯
×1
センサー付きダウンライト
DDL_6259YS



基本照明ダウンライト
×9
DDL_6132AW



パントリー、脱衣ランドリー、WIC
×4
ダウンライト
DDL_6132AW



洋室②③④
×3
シーリングライト
DCL_42121



LDK
×5
調光調色ダウンライト
DDL_6205FWG



LDK
×7
調光調色ダウンライト
DDL_CD021W



ドアホン：VL-SE31XL
(Panasonic)



内部SW：アドバンス
マットホワイト



内部コンセント：アドバンス
マットホワイト（一部マッドグレー）



引っ掛けシーリング
×3



外部：スマートデザインシリーズ
外壁色合わせ（未定）



決定図

2025.12.28


(図面 7-3)

PG House

山本卓矢様 寛子様


邸新築工事

Lighting Plan

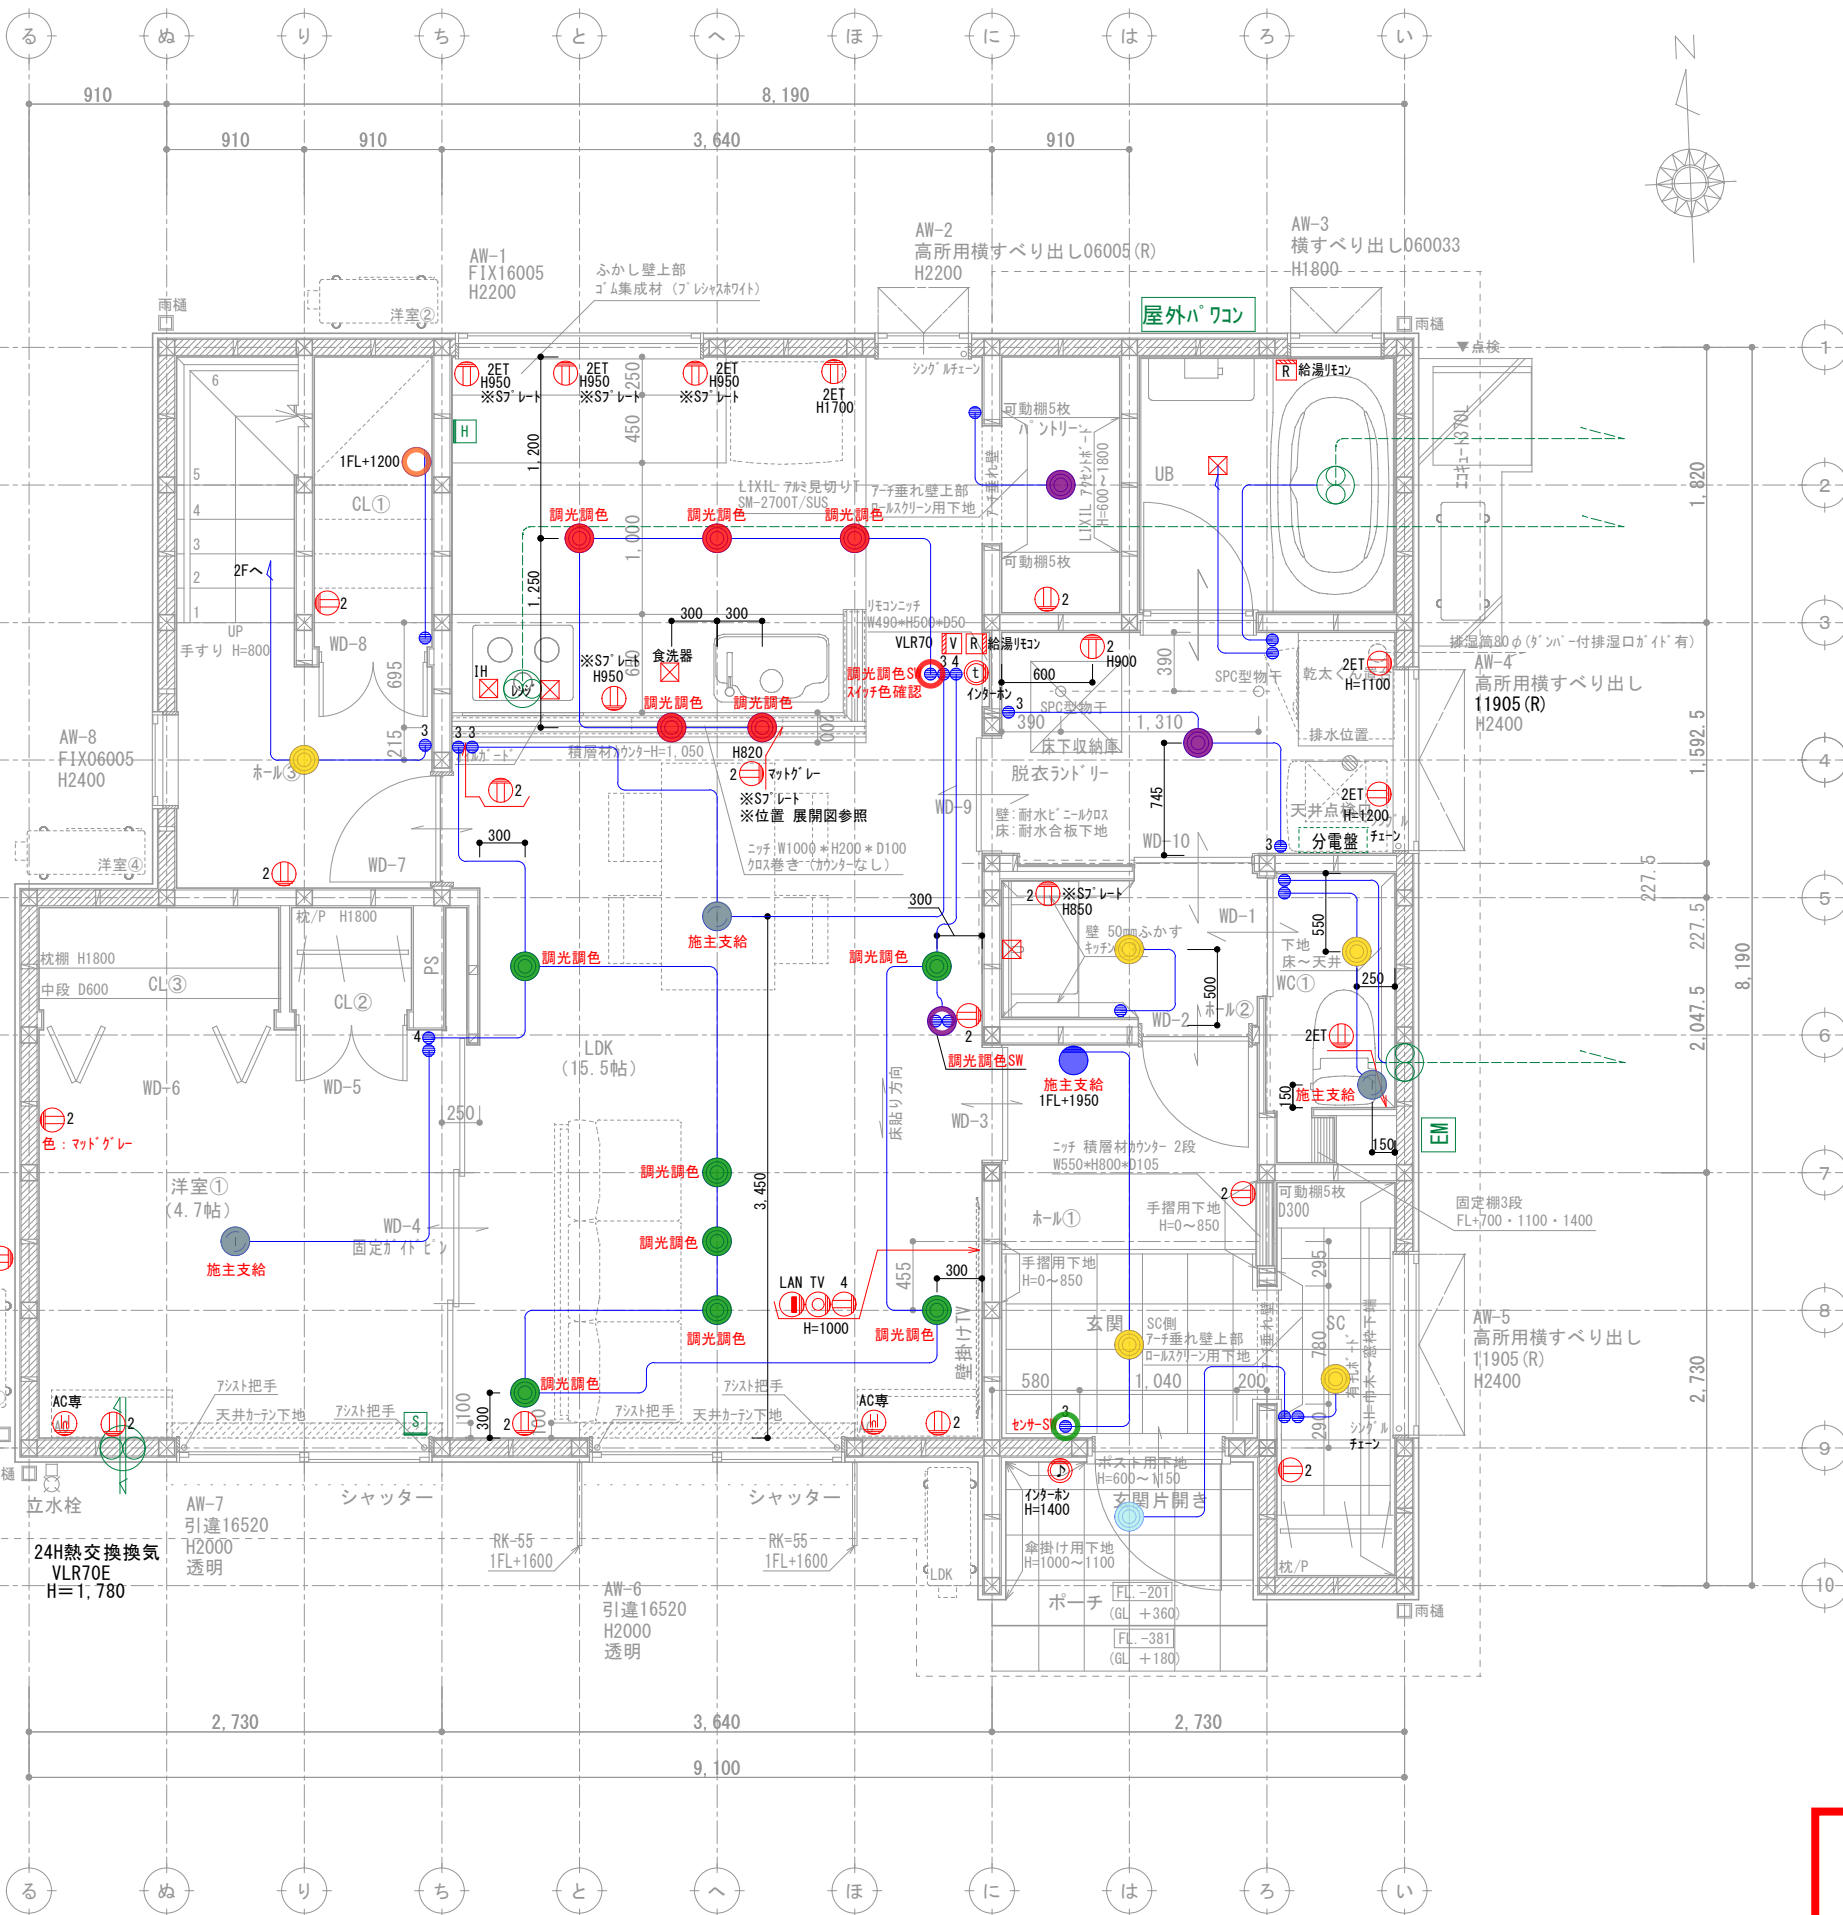


※ACコンセント天井付け
※TVアンテナ工事
※スイッチはFL+1100、コンセントはFL+200

決定図

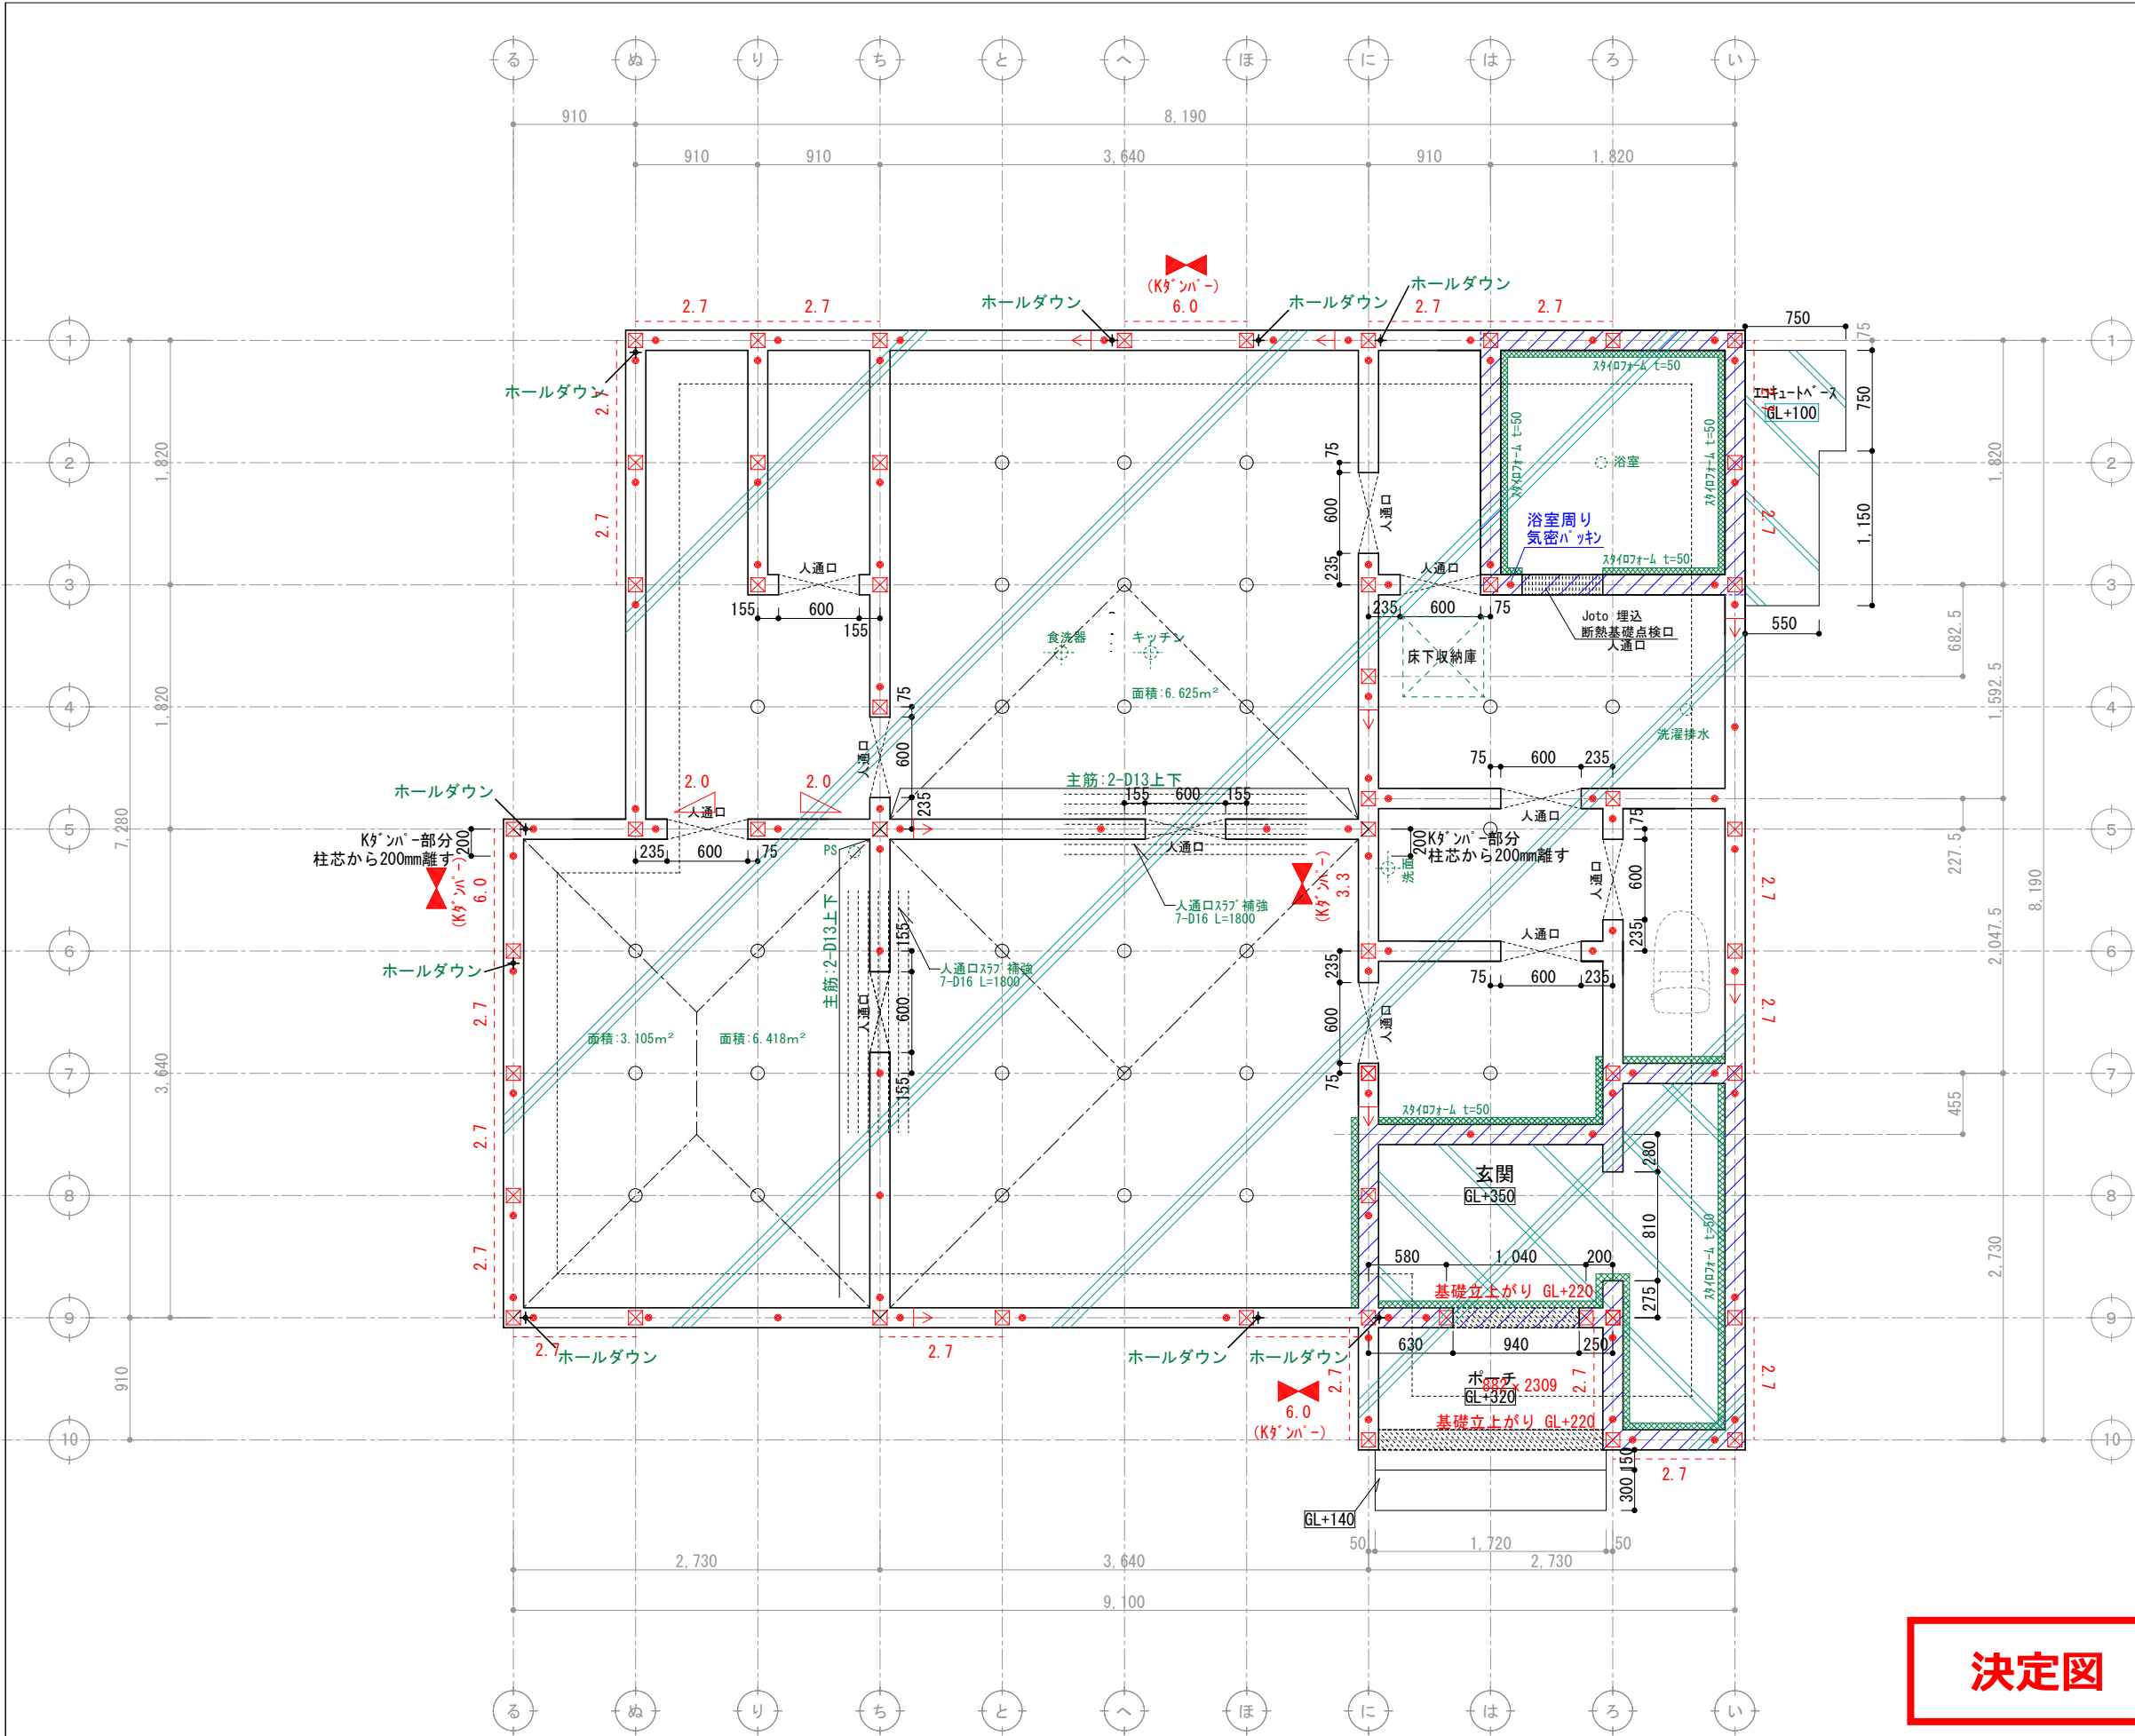

構造体ベースコンクリート t=150

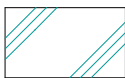

後打ち土間コン




アンカーボルトの配置

- 土台切れの箇所より150mm
- 土台の継手及び仕口の端部より150mm
- 耐力壁の端部、筋交いの脚部より150mm
- 1.82m以下の間隔
- 250mm以上埋込み
- 基礎天端より120mm

筋かい凡例

- 柱脚 柱頭 片筋かい
- たすき掛け筋かい
- 構造用パネル

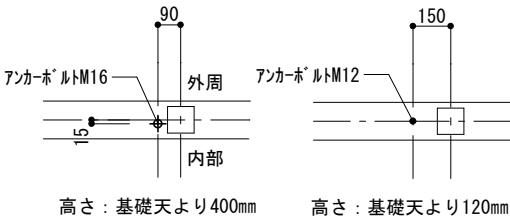

高さ: 基礎天より400mm

高さ: 基礎天より120mm

ホールダウン用アンカーボルト配置

アンカーボルト配置

凡例







- 通し柱 (105*105) 管柱 (105*105)
- アンカーボルトM12 L=400
- ホールダウンアンカーM16 L=800
- 柱芯より90mm 280mm以上埋め込み (カナリフィストアンカーボルトM16)
- 鋼製束
- 土台ジョイント
- ベースコンクリート (t=150)
- 後打ちコンクリート

基礎伏図について特記なき場合に限り下記による。

- コンクリート: 呼び強度 21N/mm²
- 鉄筋: SD295A
- 設計地耐力: fe=20kN/m²
地耐力計測後、不足の場合は相当の改良を行い、満たすものとする。
- 基礎の位置は、芯振分けとする。
- 玄関・S/C・UB周囲の基礎天端は気密パッキン施工 (網掛け部) とし、その他の基礎天端は基礎パッキン施工とする。
- 設備配管の屋内への取り入れは基礎立上り部のスリーブによる。

決定図

訂正	浜岡一級総合設計事務所 一級建築士事務所 静岡県知事登録第 (10)2441 号 一級建築士 大臣登録第 365879 号 西原利昌	LIFEFUND PG HOUSE	株式会社 LIFEFUND InDesign office 一級建築士事務所 事務所登録 (2)第7595号 一級建築士登録 第179770号 鈴木 達男 〒432-8023 静岡県浜松市中央区鴨江3丁目70番23号	年月日 2025.12.28 縮尺 1/50	件名 山本卓矢様 寛子様 邸新築工事 図名 基礎伏図	設計 酒井	IC	工事 青島	図番 B-1
----	--	----------------------	--	---------------------------------	-------------------------------------	----------	----	----------	-----------

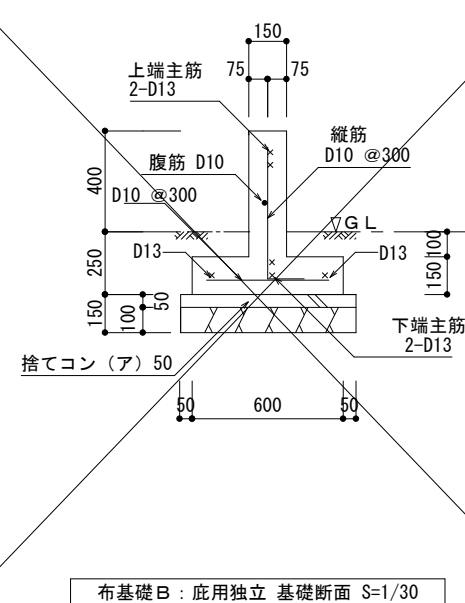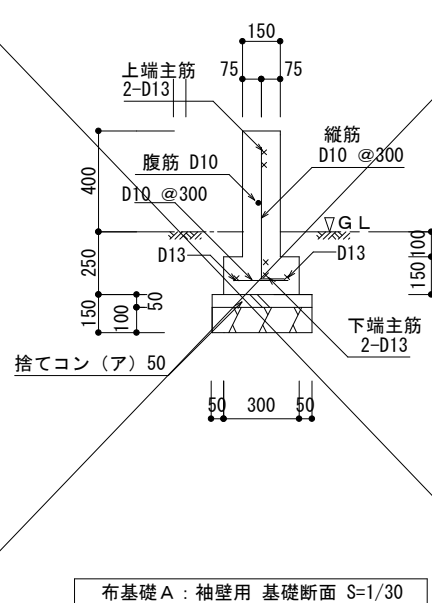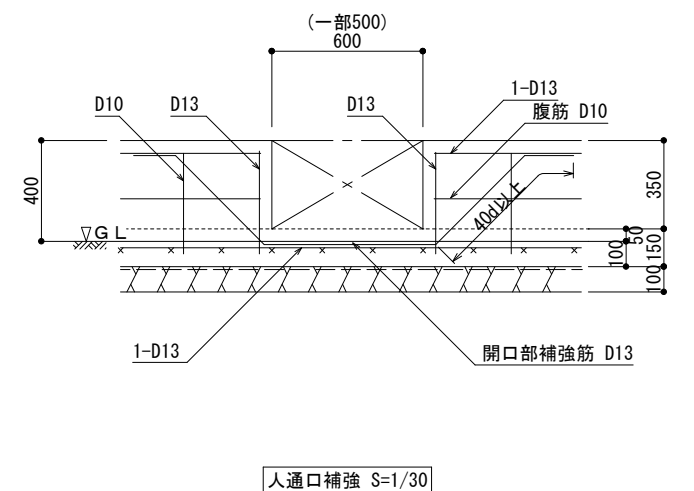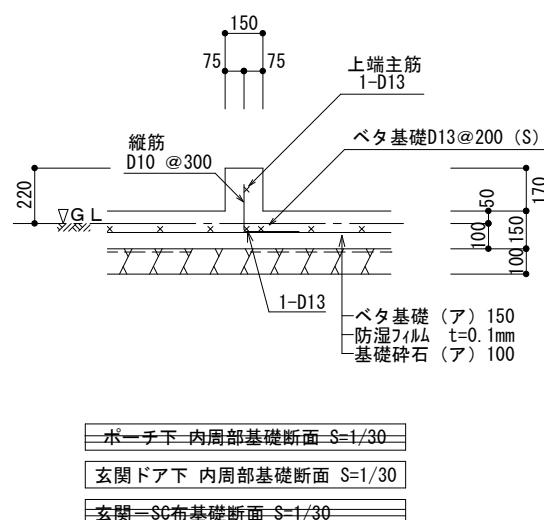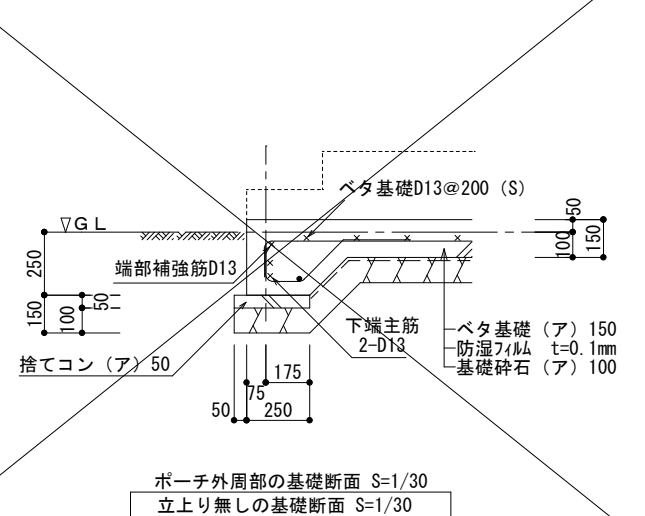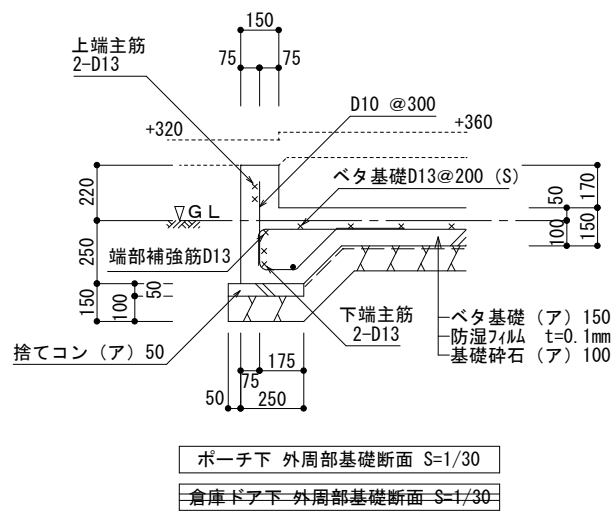


基礎の寸法 及び 配筋の検定方法	基礎立上り配筋は、 (財)日本住宅・木材技術 センター発行のスパン表 (増補版)による。 ベタ基礎スラブ配筋は、 まもりすまい保険設計施工 基準同解説のベタ基礎配筋表 による。具体的な寸法・配 筋は基礎詳細図参照。
---------------------------------------	--

鉄筋断面表記


● ・ D10を示す。

× ・ D13を示す。

※使用しない断面は **決定図**

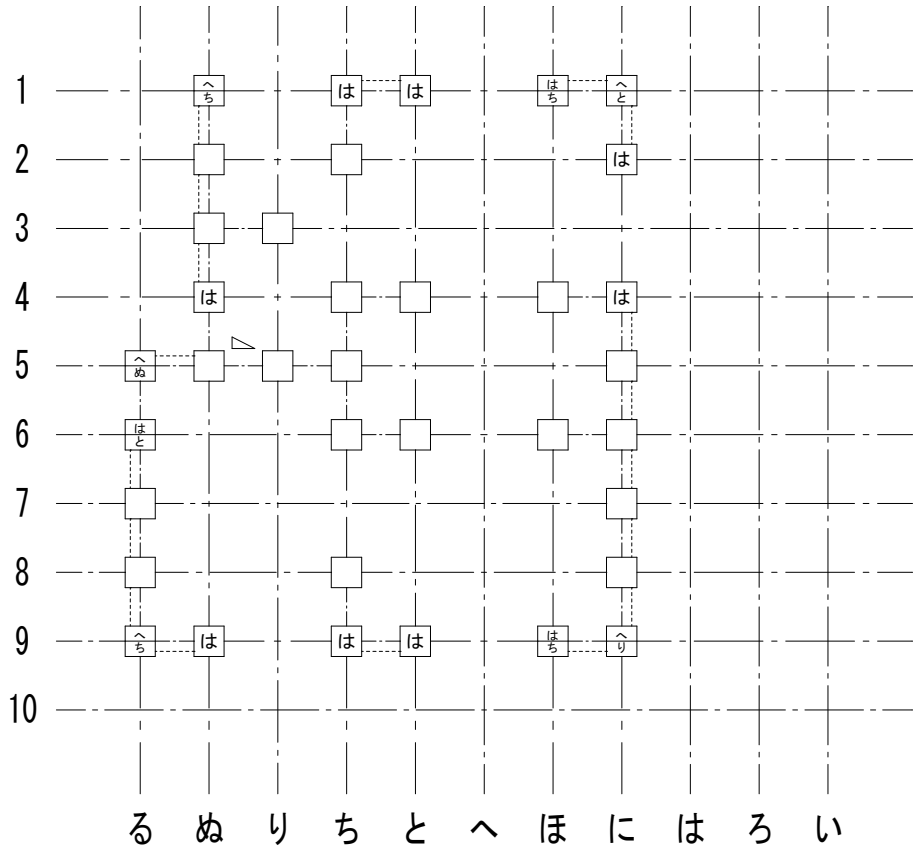

2階柱壁伏図

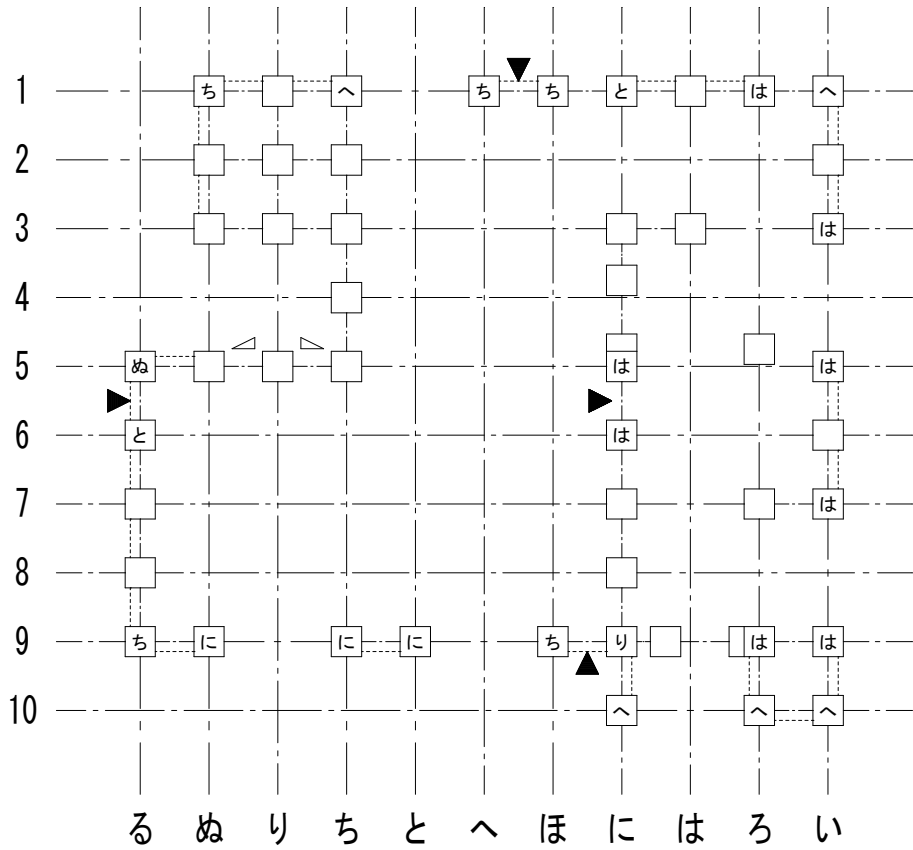

1階柱壁伏図

接合部凡例				*接合部凡例はユーザ設定されたものです。	
記号	仕様 (カナイ金物)		N	倍率	
SBCP	スリムビルドコーナー75, チビクリCK(化粧柱の場合)		0.00	1.00	
SBCP	スリムビルドコーナー75, チビクリCK(化粧柱の場合)		0.65	1.00	
SBCP	は	スリムビルドコーナー75	1.00	1.00	
ARCG	に	アレントコーナー合板用	1.40	2.20	
ARCG	ほ	アレントコーナー合板用	1.60	2.20	
ARCG	へ	アレントコーナー合板用	1.80	2.20	
HD15	と	ブレイブホールダウン B-HD15	2.80	3.60	
HD20	ち	ブレイブホールダウン B-HD20	3.70	4.70	
HD25	り	ブレイブホールダウン B-HD25	4.70	4.80	
HD30	ぬ	ブレイブホールダウン B-HD30	5.60	7.20	
J1	る	腰掛け蟻若しくは大入れ蟻掛け+羽子板ボルト、短冊金物		1.90	
J2	を	腰掛け蟻若しくは大入れ蟻掛け+羽子板ボルト、短冊金物×2		3.00	

※表示なき金物は「は」とする。

梁継手・仕口用
梁継手・仕口用

接合部凡例				*接合部凡例はユーザ設定されたものです。	
記号	仕様 (タナカ金物)		N	倍率	
FCP	フックコーナー, チビクリCK(化粧柱の場合)		0.00	1.00	
FCP	フックコーナー, チビクリCK(化粧柱の場合)		0.65	1.00	
FCP	は	フックコーナー	1.00	1.00	
GCP	に	シナコーナー	1.40	2.20	
GCP	ほ	シナコーナー	1.60	2.20	
GCP	へ	シナコーナー	1.80	2.20	
HD15	と	ビス止めホールダウンU HD15	2.80	3.60	
HD20	ち	ビス止めホールダウンU HD20	3.70	4.70	
HD25	り	ビス止めホールダウンU HD25	4.70	4.80	
HD30	ぬ	ビス止めホールダウンU HD15×2 (HD35)	5.60	7.20	
J1	る	腰掛け蟻若しくは大入れ蟻掛け+羽子板ボルト、短冊金物		1.90	
J2	を	腰掛け蟻若しくは大入れ蟻掛け+羽子板ボルト、短冊金物×2		3.00	

※表示なき金物は「は」とする。

梁継手・仕口用
梁継手・仕口用

筋かいの種類に応じた筋かいの端部の接合部の仕様		
	筋かいの種類	接合部の仕様 (構造方法)
イ	鉄筋φ9	柱又は横架材を貫通し、三角座金を介してナット締め、又は鋼板添え板を用い鋼板を柱及び横架材にCN90, 8本平打ち
ロ	筋かい:15×90	柱・横架材を欠き込み、柱・横架材双方に対してN65, 5本平打ち
ハ	筋かい:30×90	鋼板添え板t=1.6mmを筋かいに対してボルトφ12及びCN65, 3本平打ち、柱に対してCN65, 3本平打ち、横架材に対してCN65, 4本平打ち。筋かいプレートBP同等品
ニ	筋かい:45×90	鋼板添え板t=2.3mmを筋かいに対してボルトφ12及びスクリュー釘φ4.5L50, 7本平打ち、柱及び横架材に対してスクリュー釘φ4.5L50, 5本平打ち。筋かいプレートBP-2同等品
ホ	筋かい:90×90	柱又は横架材にボルトφ12mmを用いて一面剪断接合

胴差と通し柱の接合部の仕様		
	胴差と通し柱の条件	仕口
T1	通し柱の片側に胴差が来る場合	胴差を柱にかたぎ大入れ短ほぞ差しの上、羽子板ボルト、かね折り金物又は同等以上の仕口
T2	通し柱の両側に胴差が来る場合	胴差を柱にかたぎ大入れ短ほぞ差しの上、短冊金物又は、同等以上の仕口で胴差相互を緊結
T3	通し柱と胴差の接合部の近くに90×90以上の筋かいが来る場合(通し柱が建物の出隅にあるか、筋かい壁が外壁と直交して接する場合)	胴差を通し柱に、15KN用引き寄せ金物を水平に用いて緊結

決定図

37センチクロス指示書

G2

壁付け 住宅用火災報知器			数量
H	熱感知器	電池式(単独型)	1
		露出型	
壁付け 住宅用火災報知器			数量
S	煙感知器	電池式(単独型)	
		露出型	

- ※ 煙感知器は壁・梁より600mm以上離す
壁に取付ける場合、
天井から150mm以上500mm以内離す
換気扇・エアコン吹出口から1500mm以上離す
- ※ 全室LED照明とする。
- ※ 標準天井高さ2,400
- ※ 特記無きガラスは型ガラス


* 凡例

- ☒ 管柱 (105×105)
- ◀▶ K'パネ (3.30倍 FRM-0641)
- △ 片筋違い (2.00倍 45×90)
(例 左:柱脚 右:柱頭)
- ⊠ たすき掛筋違い (4.00倍 45×90)
- 構造用合板 (2.70倍)
(t=9 タイプ-EXN/A-)
- △ 床点検口
- ⊠ 天井点検口
- ⊕ 換気扇
- ⊕ 熱交換換気扇VLR-70

アドバンスシリーズ	
スマートデザイン (外部)	
凡例	
①	コンセント 1ヶ所
②	コンセント 2ヶ所
③	コンセント 3ヶ所
①ET	コンセント1ヶ所接地ターミナル付
②ET	コンセント2ヶ所接地ターミナル付
①WP	コンセント 防水型
②WP	エアコン用コンセント
③WP	200V用コンセント
①WP	防雨入換プレート
①	スイッチ
③	3線スイッチ
④	4線スイッチ
①	直結電源
①TV	テレビ取出口
①TEL	電話取出口 (テレホンガイド)
①LAN	LAN取出口 (テレホンガイド)
①	壁照明
①	リモコン (給湯関係・ルフロ)
①	メーター
①	分電盤
①	チャイム

- ※ACコンセント天井付け
- ※TVアンテナ工事
- ※スイッチはFL+1100、コンセントはFL+200

決定図

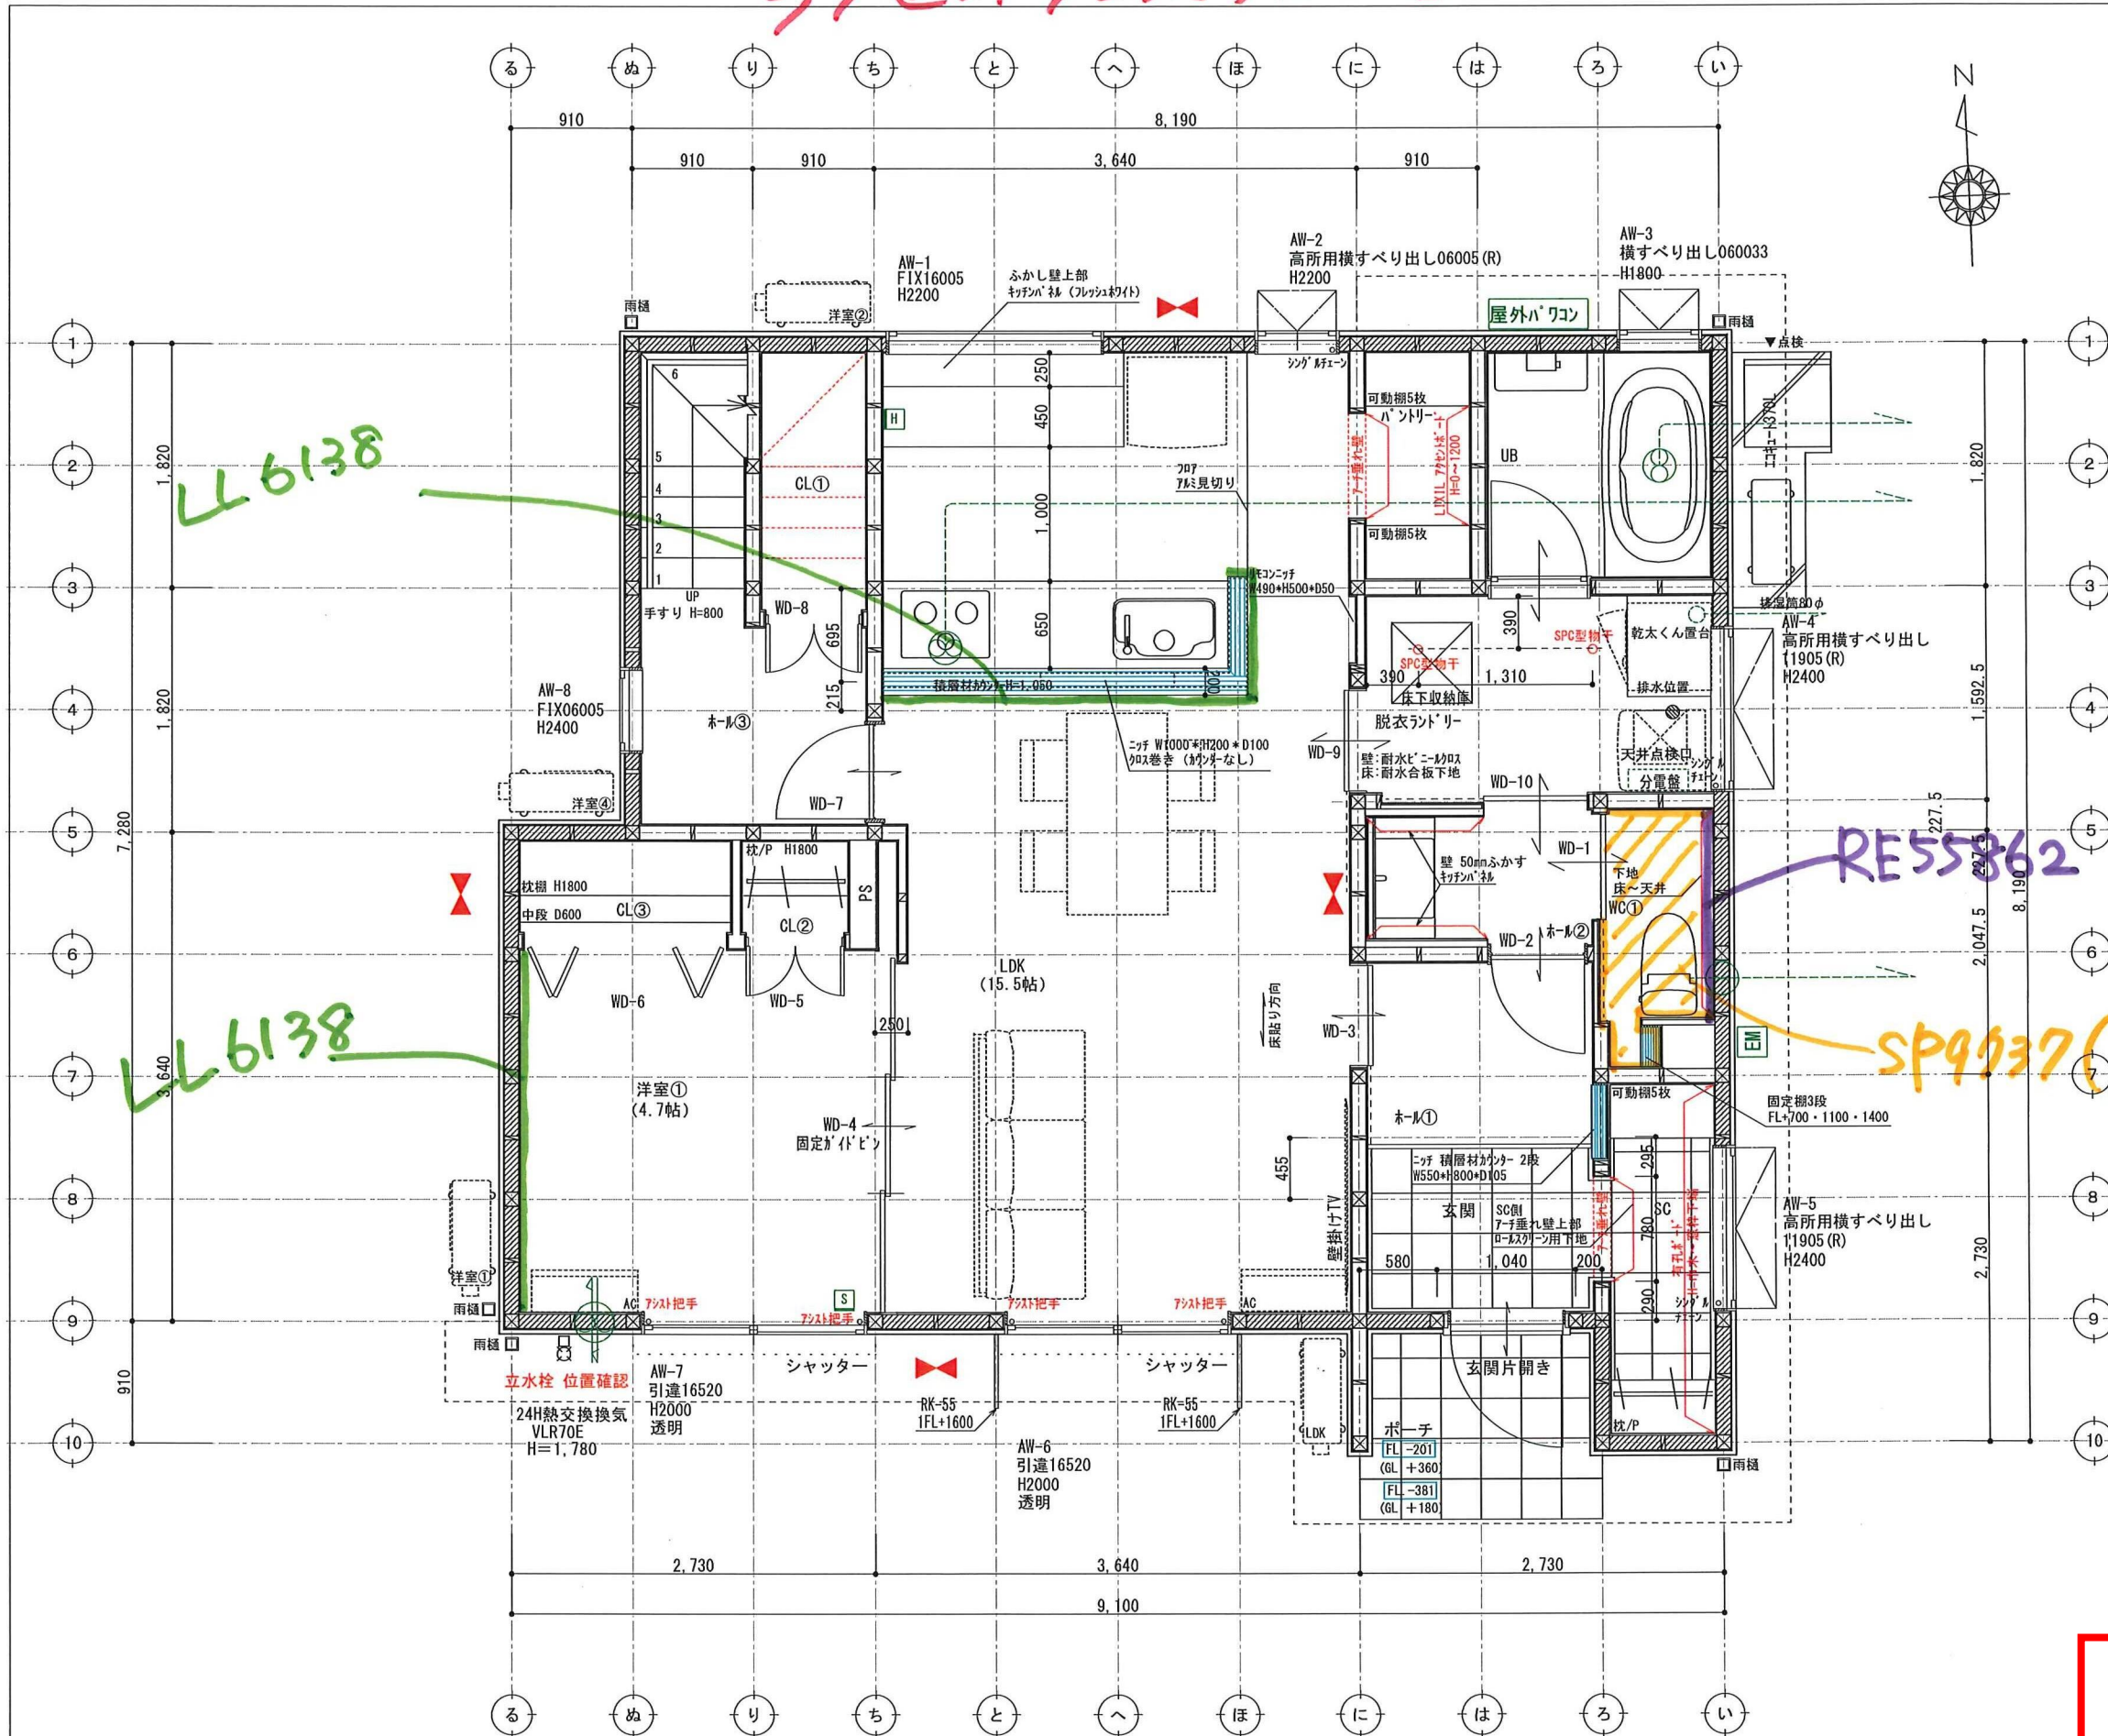

G2

壁付け 住宅用火災報知器			数量
[H]	熱感知器	電池式(単独型)	
		露出型	
壁付け 住宅用火災報知器			数量
[S]	煙感知器	電池式(単独型)	
		露出型	

- ※ 煙感知器は壁・梁より600mm以上離す
壁に取付ける場合、
天井から150mm以上500mm以内離す
換気扇・エアコン吹出口から1500mm以上離す
- ※ 全室LED照明とする。
- ※ 標準天井高さ2,400
- ※ 特記無きガラスは型ガラス

* 凡例

- ☒ 管柱 (105×105)
- ◀▶ K'ンバー (3.30倍 FRM-0641)
- △ 片筋違い (2.00倍 45×90)
(例 左:柱脚 右:柱頭)
- ⊠ たすき掛筋違い (4.00倍 45×90)
- 構造用合板 (2.70倍)
(t=9 45倍 EXH/A-)
- ⬮ 床点検口
- ⬮ 天井点検口
- ⊕ 換気扇
- ⊕ 熱交換換気扇VLR-70

アドバンスシリーズ	
スマートデザイン (外部)	
凡例	
①	コンセント 1ヶ所
②	コンセント 2ヶ所
③	コンセント 3ヶ所
①ET	コンセント1ヶ所接地ターミナル付
②ET	コンセント2ヶ所接地ターミナル付
①WP	コンセント 防水型
②WP	エアコン用コンセント
③WP	200W用コンセント
①WP	防雨入線プレート
●	スイッチ
●3	3路スイッチ
●4	4路スイッチ
⊕	直結電源
⊕TV	テレビ取出口
⊕TEL	電話取出口 (テレホンガイド)
⊕LAN	LAN取出口 (テレホンガイド)
⊕	壁照明
⊕	リモコン (給湯関係・ルフロ)
⊕	メーター
⊕	分電盤
⊕	チャイム

- ※ACコンセント天井付け
- ※TVアンテナ工事
- ※スイッチはFL+1100、コンセントはFL+200

決定図

