

37センチクロス指示書

G2

壁付け 住宅用火災報知器			数量
H	熱感知器	電池式(単独型)	1
		露出型	
壁付け 住宅用火災報知器			数量
S	煙感知器	電池式(単独型)	
		露出型	

- ※ 煙感知器は壁・梁より600mm以上離す
壁に取付ける場合、
天井から150mm以上500mm以内離す
換気扇・エアコン吹出口から1500mm以上離す
- ※ 全室LED照明とする。
- ※ 標準天井高さ2,400
- ※ 特記無きガラスは型ガラス

* 凡例

☒ 管柱 (105×105)

◀▶ K'シャ-
(3.30倍 FRM-0641)

△ 片筋違い
(2.00倍 45×90)
(例 左:柱脚 右:柱頭)

⊠ たすき掛筋違い
(4.00倍 45×90)

構造用合板 (2.70倍)
(t=9 タイパ EXN/A-)

△ 床点検口

⊠ 天井点検口


⊕ 換気扇

⊕ 熱交換換気扇VLR-70

アドバンスシリーズ	
スマートデザイン (外部)	
凡例	
①	コンセント 1ヶ所
②	コンセント 2ヶ所
③	コンセント 3ヶ所
①ET	コンセント1ヶ所接地ターミナル付
②ET	コンセント2ヶ所接地ターミナル付
①WP	コンセント 防水型
②WP	エアコン用コンセント
③WP	200V用コンセント
④WP	防雨入換プレート
⑤	スイッチ
③	3線スイッチ
④	4線スイッチ
⑥	直結電源
⑦TV	テレビ取出口
⑧TEL	電話取出口 (テレホンガイド)
⑨LAN	LAN取出口 (テレホンガイド)
⑩	壁照明
⑪	リモコン (給湯関係・ルフロ)
⑫	メーター
⑬	分電盤
⑭	チャイム

- ※ACコンセント天井付け
- ※TVアンテナ工事
- ※スイッチはFL+1100、コンセントはFL+200

決定図

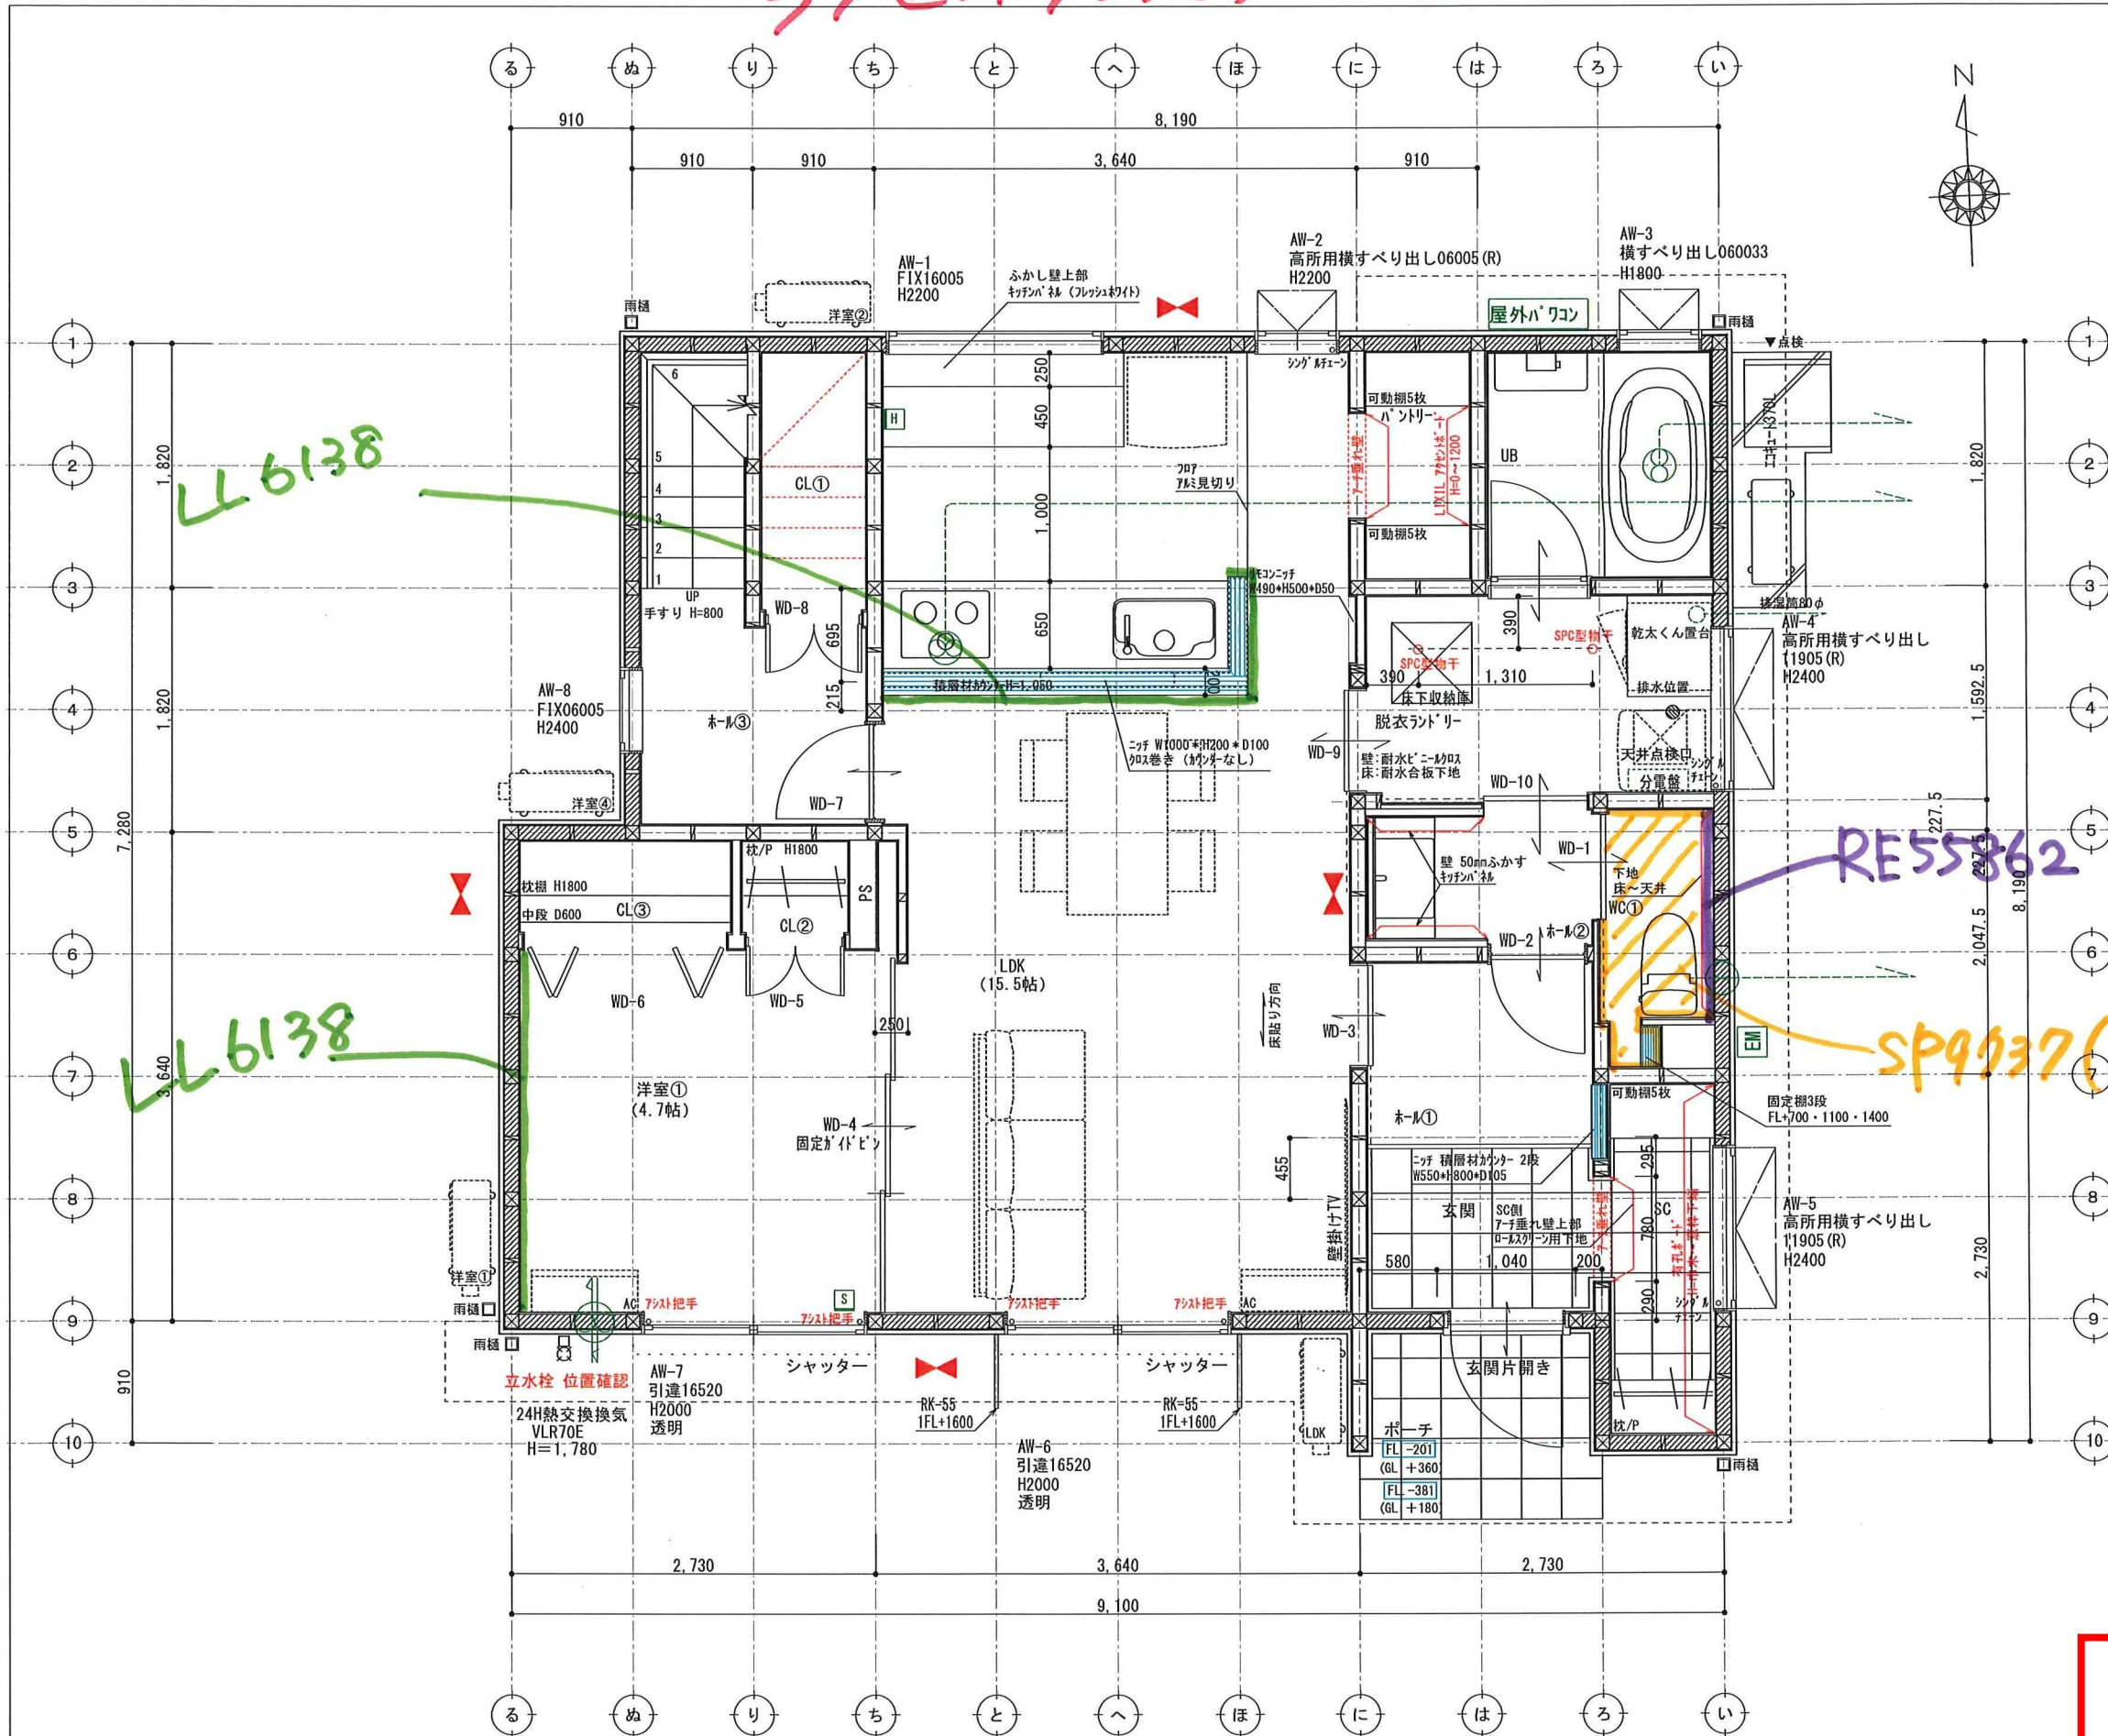

訂正

浜岡 一級総合設計事務所
一級建築士事務所 静岡県知事登録第 (10)2441 号
一級建築士 大臣登録第 365879 号 西原利晶

PG HOUSE

株式会社 LIFEFUND InDesign office 一級建築士事務所
事務所登録 (2)第7595号 一級建築士登録 第179770号 鈴木 達男
〒432-8023 静岡県浜松市中央区鴨江3丁目70番23号

年月日
2025. 12. 28
縮尺
1/50

件名
山本卓矢様 寛子様邸 新築工事
図名
1階平面図

設計	IC	工事	図番
酒井		青島	3-1

G2

壁付け 住宅用火災報知器			数量
[H]	熱感知器	電池式(単独型)	
		露出型	
壁付け 住宅用火災報知器			数量
[S]	煙感知器	電池式(単独型)	
		露出型	

- ※ 煙感知器は壁・梁より600mm以上離す
壁に取付ける場合、
天井から150mm以上500mm以内離す
換気扇・エアコン吹出口から1500mm以上離す
- ※ 全室LED照明とする。
- ※ 標準天井高さ2,400
- ※ 特記無きガラスは型ガラス

* 凡例

- ☒ 管柱 (105×105)
- ◀▶ K'ンバー (3.30倍 FRM-0641)
- △ 片筋違い (2.00倍 45×90)
(例 左:柱脚 右:柱頭)
- ⊠ たすき掛筋違い (4.00倍 45×90)
- 構造用合板 (2.70倍)
(t=9 タイプ EXAハバ)
- ⬮ 床点検口
- ⬮ 天井点検口
- ⊕ 換気扇
- ⊕ 熱交換換気扇VLR-70

アドバンスシリーズ	
スマートデザイン (外部)	
凡例	
①	コンセント 1ヶ所
②	コンセント 2ヶ所
③	コンセント 3ヶ所
①ET	コンセント1ヶ所接地ターミナル付
②ET	コンセント2ヶ所接地ターミナル付
①WP	コンセント 防水型
②WP	エアコン用コンセント
③WP	200W用コンセント
①WP	防雨入線プレート
●	スイッチ
●3	3路スイッチ
●4	4路スイッチ
⊗	直結電源
⊗TV	テレビ取出口
⊗TEL	電話取出口 (テレホンガイド)
⊗LAN	LAN取出口 (テレホンガイド)
⊗	壁照明
⊗	リモコン (給湯関係・ルフロ)
⊗	メーター
⊗	分電盤
⊗	チャイム

- ※ACコンセント天井付け
- ※TVアンテナ工事
- ※スイッチはFL+1100、コンセントはFL+200

決定図

