



面

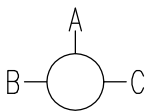



A面

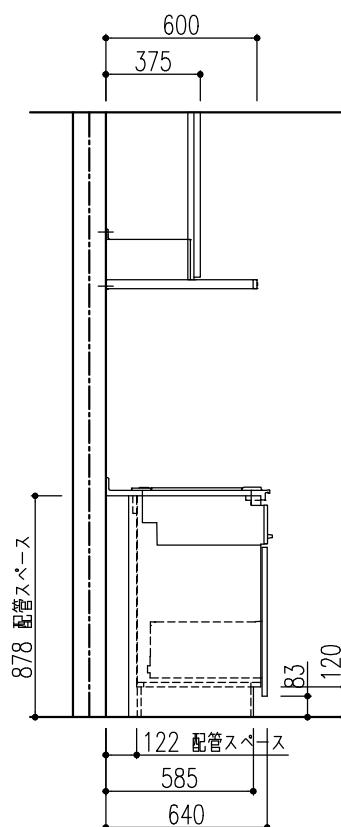

【 ご注意 】

- 壁面仕上材（キッチンパネル・タイルなど）の貼付下端位置が変わります。〔機能図参照〕
- 記載のキャビネット寸法は扉前面までの呼び寸法です。キャビネット本体の寸法・扉厚み等は商品ガイドの巻末資料をご確認ください。
- 記載のワークトップ、カウンター、エンドパネル、サイドパネルの寸法は呼び寸法です。詳細寸法は商品ガイドの巻末資料をご確認ください。
- レンジフード電源プラグ仕様：3芯電源プラグ（アース工事が必要です。）

A3 20250817M953-01

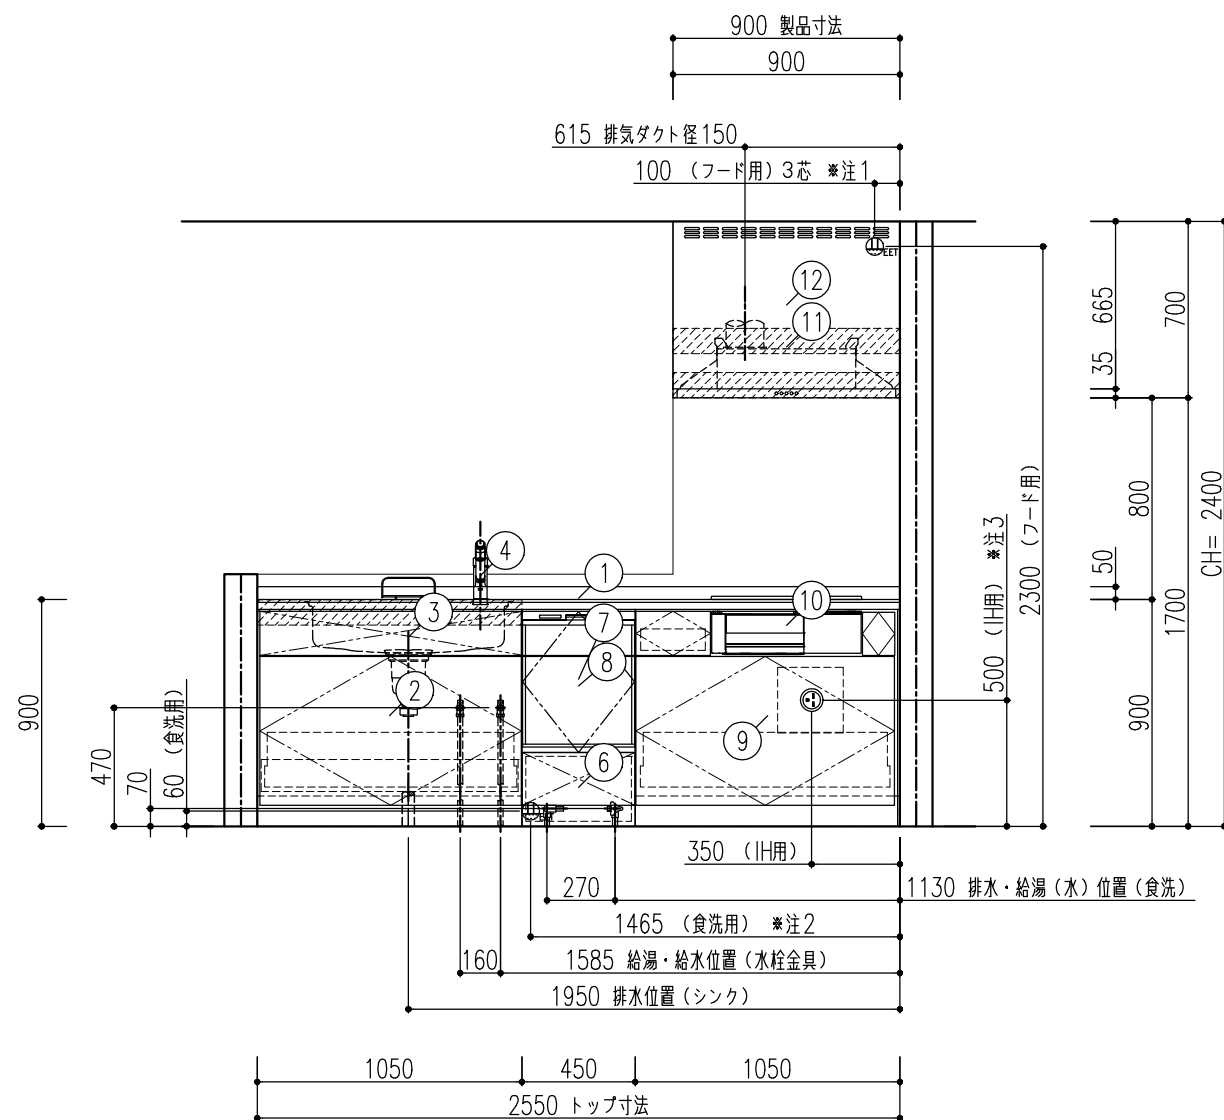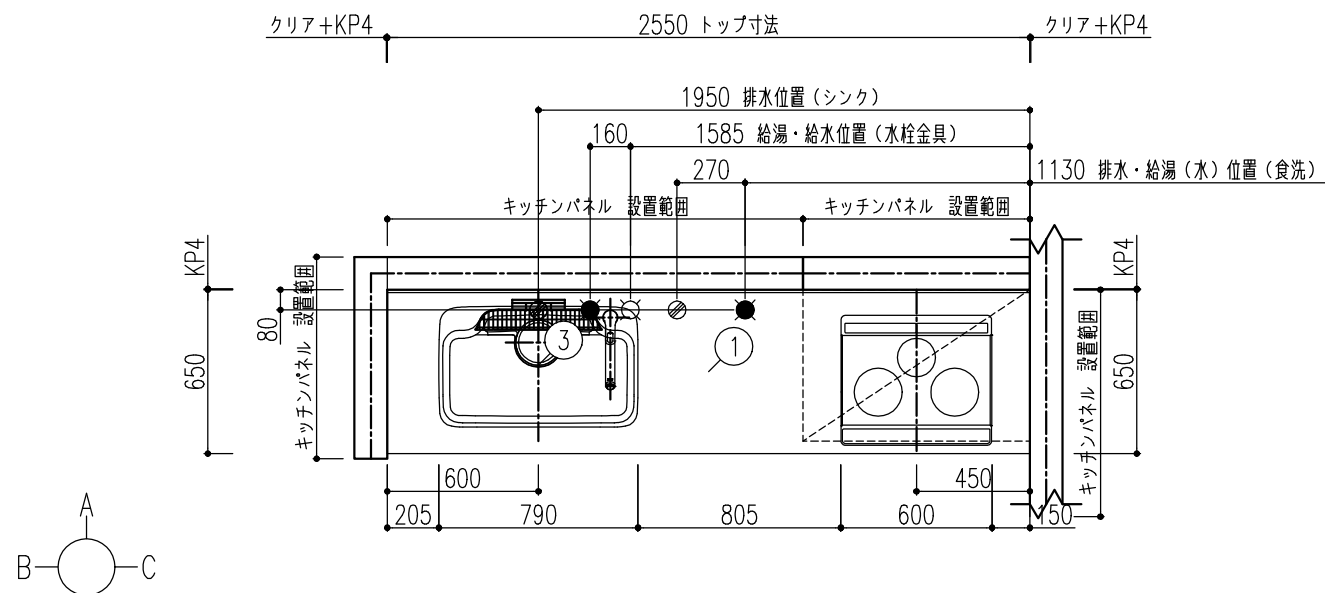[illegible]

注1) 125V・15A 2極接地極付アースターミナル付コンセント 【専用】(フード用)

注2) 125V・15A 2極接地極付アースターミナル付コンセント 側板取付【専用】


注3) 250V・30A 2極接地極付コンセント 【専用】

【ご注意】


- 壁面仕上材(キッチンパネル・タイルなど)の貼付下端位置が変わります。 [機能図参照]
- 記載のキャビネット寸法は扉前面での呼び寸法です。キャビネット本体の寸法・扉厚み等は商品ガイドの巻末資料をご確認ください。
- 記載のワークトップ、カウンター、エンドパネル、サイドパネルの寸法は呼び寸法です。詳細寸法は商品ガイドの巻末資料をご確認ください。
- 電気・ガス・給排水・換気等は法令・規定に従って有資格者が行ってください。
- 水道工事は排水配管工事となります。
- 取付・設置に際し、各製品の取付・設置説明書や図面の機能図を必ずお読み下さい。
- 内線規程上、各機器のプラグ仕様に関わらず建築側には接地極付コンセントを推奨しています。
- レンジフード電源プラグ仕様: 3芯電源プラグ(アース工事が必要です。)
- 食器洗い乾燥機配管は、給水接続か給湯接続かお客様に確認したうえで施工願います。
- 食洗機内配管の詳細については必ず別添の機能図をご確認ください。

特記事項 扉色 KK5:ブラックスタック 取手 [M]スリム取手 (ブラック) ワークトップカラー 【DW】ソルティホワイト	物件名 清水裕也 様邸	案件No. A2507DDD0EP4S0	図面名 納まり図	担当 栗野 友仁	図面 	図番 : 株式会社 LIXIL
		見積No. M25077957318-003-2	縮尺 1/30	日付 2025.08.17		
	仕様 ES21					

B面

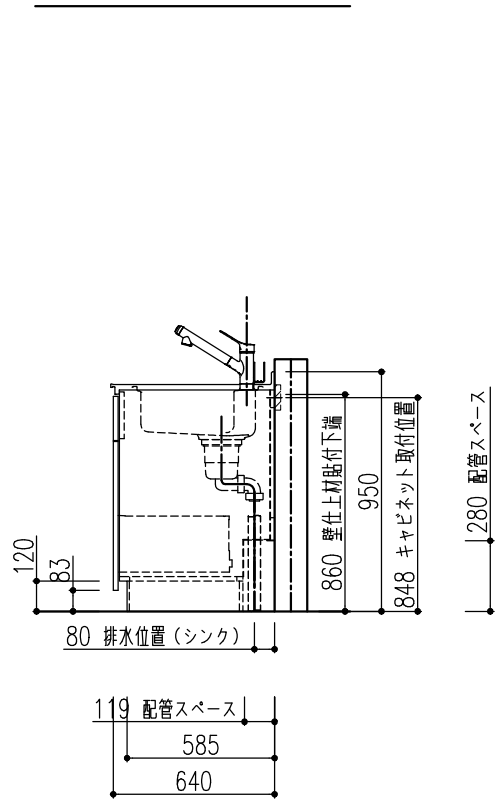

C面

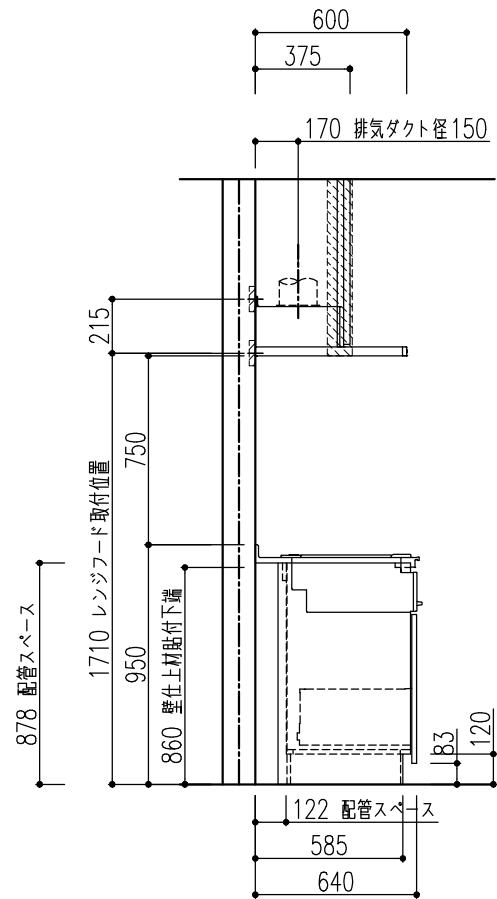

特記事項 扉色 KK5:ブラックスタック 取手 [M]スリム取手 (ブラック) ワークトップカラー 【DW】 ソルティホワイト	物件名	清水裕也 様邸	案件No.	図面名	担当	図面	図番
	仕様	ES21	A2507DDD0EP4S0	納まり図	栗野 友仁		株式会社 LIXIL
			見積No.	縮尺	日付		
			M25077957318-003-2	1/30	2025.08.17		

■壁面仕上材（キッチンパネル、タイルなど）取付注意事項〔貼付下端位置〕

●キッチンパネルの貼付下端位置

キッチンパネルの貼付下端位置にご注意ください。

キッチンパネル

壁

810mm

（キッチンパネル貼付下端位置）

ワークトップ高さ：850mm以外の場合は、
下表を参照してください。

ワークトップ高さ	キッチンパネル貼付下端位置
900	860
875	835
825	785
800	760

●上表はキッチンパネルの場合です。ステンレスパネルの場合は、キッチンパネルの「取付・設置説明書」を参照してください。

《ワークトップ高さ：850mmの場合》

■壁面仕上材（キッチンパネル）取付注意事項〔貼付向き〕

●キッチンパネルの貼付向き

キッチンパネルの貼付向きにご注意ください。

【単位：mm】

レンジフード

ウォールキャビ（開き扉）

クイックポケット
クイックパレット

850

（ワークトップ高さ）

700

（ウォールキャビ・レンジフード高さ）

880

（壁面寸法）

620

（クイックポケット・パレット用キャビ高さ）

850

（ワークトップ高さ）

横貼り

縦貼り

フロアキャビ

《バックガード：なし、ワークトップ高さ：850mm、ウォールキャビ高さ：700mmの場合》

《キッチンパネル 貼付方向》

総高さ：2350mmの場合

	ウォールキャビ		
	開き扉	クイックポケット クイックパレット	
	H700	H600 H500	H700 (620) H600 (520)
キッチンパネル貼付方向	横	縦	

【ご注意】
リシェル以外のクイックパレットは、キャビネットの背板高さがショート（－80mm）しておりませんので、『開き扉』のキッチンパネル貼付方向に合せてください。

■床の不陸に関して

7mm以下

7mm以下

床の不陸は、7mm以下に抑えるようにしてください。不陸が大きい場合は、現場責任者に床の修正を依頼してください。
※キャビネット取付時には不陸調整スペーサー等で水平になるように設置してください。

■レンジフード取付注意事項（壁面取付時）

レンジフードを取付ける場合は下地の材が厚み30mm以上、幅100mm以上、ビス固定位置が材の端部から25mm以上であることを確認してください。
また、壁強度などの詳細は「レンジフード設置説明書」を必ず事前に確認してください。

取付位置については、取付設置図を確認してください。

参考図_CLS. SER. NST. ASR. ADR. RVJ. GSR. BFRS. TARシリーズ
（※RVJ. GSRシリーズの場合はレンジフードパネルの取付下地は不要です。）

12mm以上の合板または0.8mm以上の鋼板

レンジフード取付下地

100mm

30mm以上

100mm以上

335

レンジフードパネル取付下地

【正面】

【側面】

参考図_FED. HVR. NSDシリーズ（サイドマントルタイプ）

30mm以上

100mm以上

レンジフード取付下地

【正面】

【側面】

参考図_NBHシリーズ

レンジフード取付下地

30mm以上

100mm以上

【正面】

【側面】

特記事項

扉色 KK5:ブラックスタック

取手 [M]スリム取手（ブラック）

ワークトップカラー 【DW】ソルティホワイト

物件名

清水裕也 様邸

仕様

ES21

案件No.

A2507DDD0EP4S0

図面名

機能図

担当

栗野 友仁

図面

図番

見積No.

M25077957318-003-2

縮尺

日付


2025.08.17

株式会社 LIXIL

A3

20250817M953-01


■ ASRフード

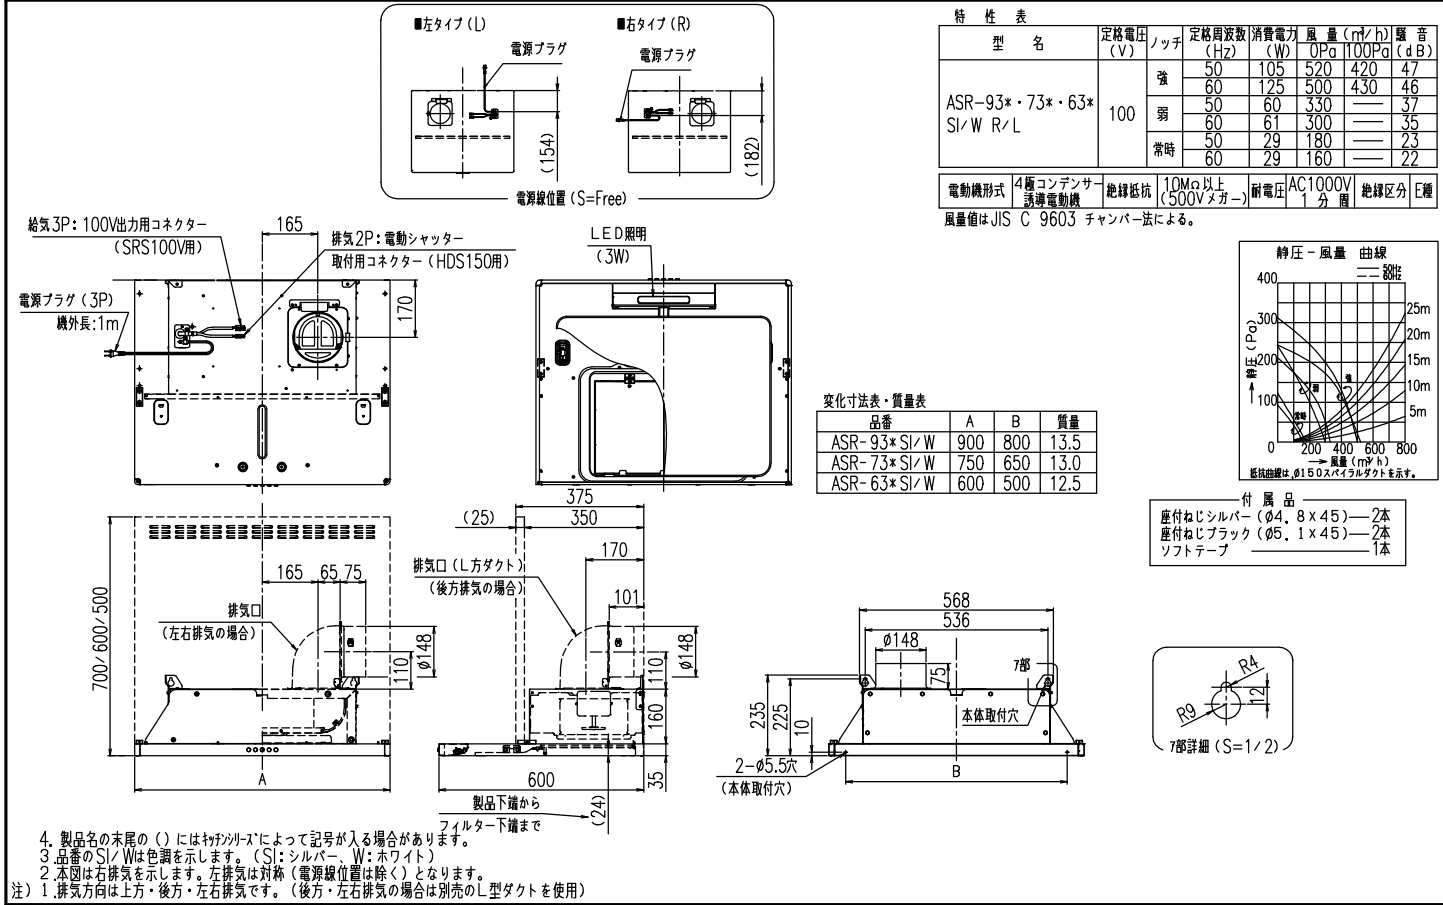

■ IHヒーター用コンセント推奨位置図 / 壁付設置の場合

※コンセントや電源プラグが、引き出しおよびIHヒーター用仕切板（オプション）に接触しないように注意してください。 ※木製キャビネットの配管スペース付キャビネットを使用する場合は 点検口裏の配管スペース内にコンセントを設置してください。	<table border="1"> <tr> <th>キッチン高さ</th><th>電源線高さ</th></tr> <tr> <td>800</td><td>400</td></tr> <tr> <td>850</td><td>450</td></tr> <tr> <td>900</td><td>500</td></tr> </table>	キッチン高さ	電源線高さ	800	400	850	450	900	500
キッチン高さ	電源線高さ								
800	400								
850	450								
900	500								


キッチン高さ	電源線高さ
800	400
850	450
900	500

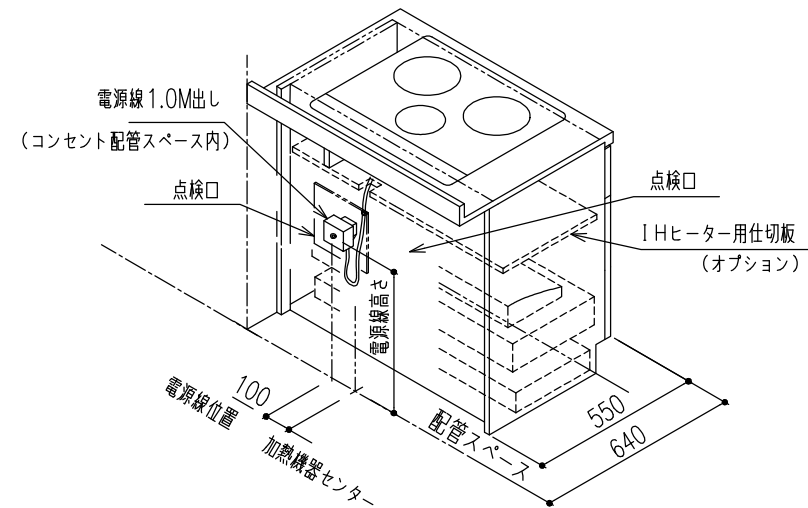

注意：引き出しおよびIHヒーター用仕切板（オプション）に接触しないように上記寸法を参照してください。

■食器洗い乾燥機内配管図 床立上げ配管例

※イラスト表記の事前配管部材は現地手配

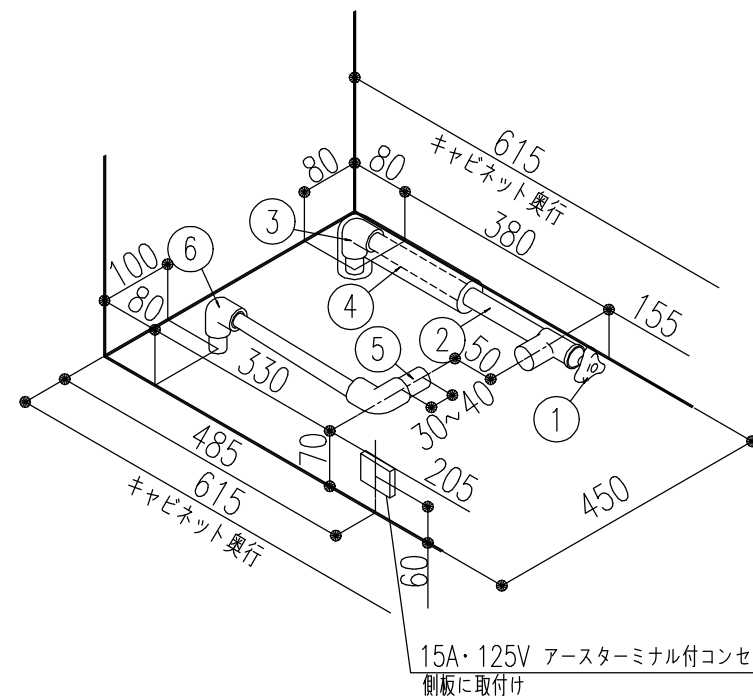

注意：配管立ち上げ位置は必ず本図の位置に立ち上げて下さい。

※給水接続か給湯接続かお客様に確認したうえで施工願います。

給水（給湯の場合は耐熱配管）

- ①アンゲル型止水栓（ハンドル式・固定ゴマタイプ）
- ※必ず固定ゴマタイプをご使用ください。
- 落としゴマタイプを使用すると、水栓内でコマが移動し、ゴトゴト音を生じる恐れがあります。
- ②硬質塩化ビニルライニング鋼管（相当品）
- ③RC1ノ2ソケット
- ④断熱材（Φ48）

排水（耐熱塩ビ使用のこと）

- 出型 ⑤排水パイプHT20
⑥HTエルボ


※配水管先端のエルボを上向きにしないでください。

キャビネットに当たるため、排水ホース折れの原因になります

■ 止水栓図（床立上げ）

床立ち上げ配管


配管立ち上げ寸法は、止水栓芯までの高さを示しています。


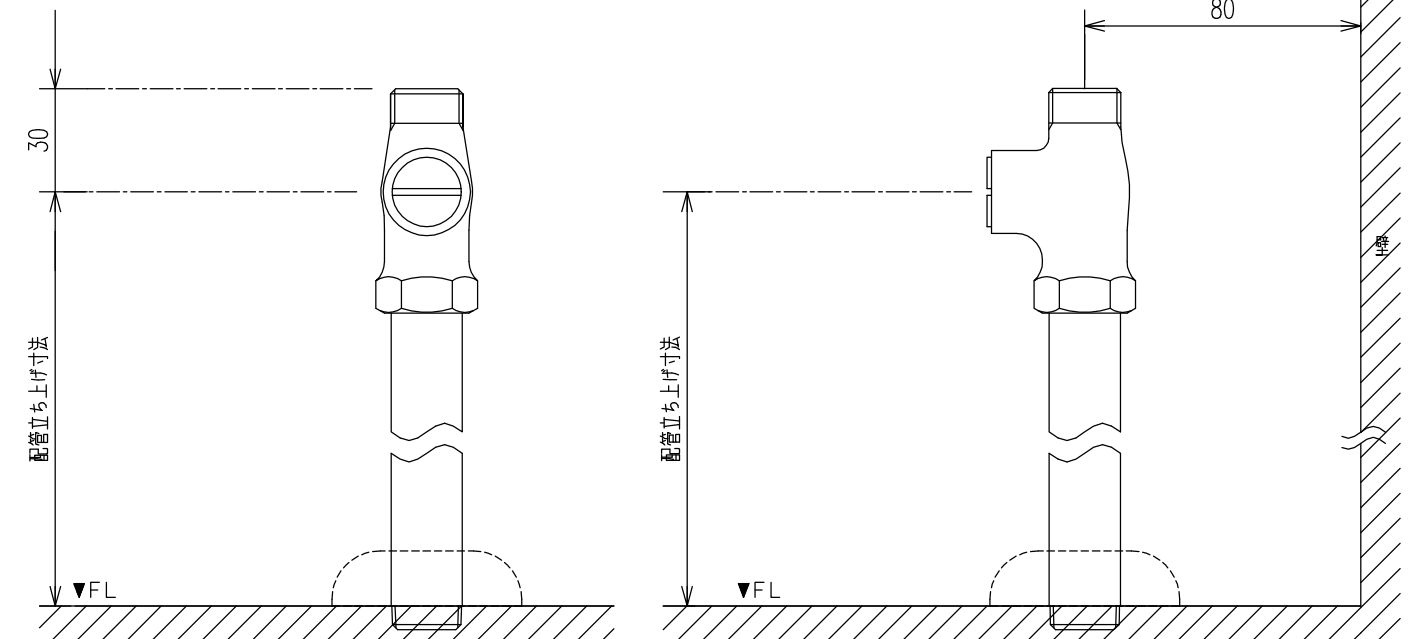


特記事項 扉色 KK5:ブラックスタック 取手 [M]スリム取手(ブラック) ワークトップカラー 【DW】ソルティホワイト	物件名	清水裕也 様邸	案件No.	図面名	担当	図面	図番 : 株式会社 LIXIL
	仕様	ES21	A2507DDD0EP4S0	機能図	栗野 友仁		
			見積No.	縮尺	日付		
			M25077957318-003-2		2025.08.17		

■ キッチン取付者さま向け 動画コンテンツ ■

商品取付けの注意点を2次元コードでご視聴いただけます。
取付日より前に、是非ご確認ください。

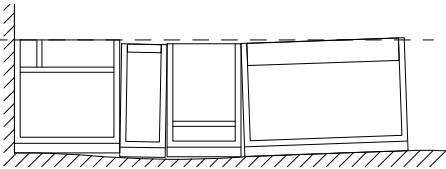荷扱い・搬入	カウンター開梱搬入「養生ツール」	不陸の確認と調整	マグネットキッチンパネル
荷扱い・搬入	カウンター開梱搬入 「養生ツール」のご紹介		マグネット キッチンパネル 「取付・設置」ポイント
作成日：2024年10月01日	作成日：2024年10月01日	作成日：2024年02月07日	作成日：2024年03月06日


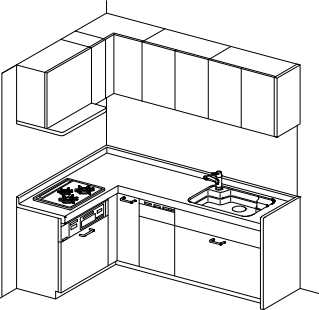
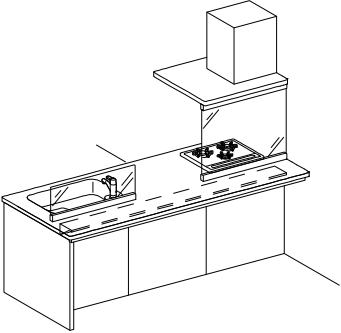
人造大理石カウンターL型キッチン	センターキッチン（ペニンシュラ型）		
			
作成日：2024年02月07日	作成日：2024年02月07日		

--	--	--	--

特記事項 扉色 KK5:ブラックスタック 取手 [M]スリム取手 (ブラック) ワークトップカラー 【DW】ソルティホワイト	物件名	清水裕也 様邸	案件No.	図面名	担当	図面	図番
	仕様	ES21	A2507DDD0EP4S0	機能図	栗野 友仁		株式会社 LIXIL
			見積No.	縮尺	日付		
			M25077957318-003-2		2025.08.17		

■ キッチン取付者さま向け 動画コンテンツ ■

商品取付けの注意点を2次元コードでご視聴いただけます。
取付日より前に、是非ご確認ください。

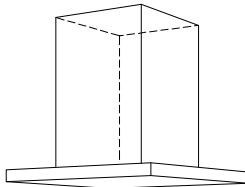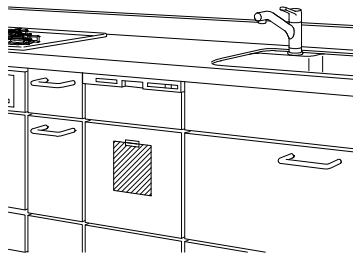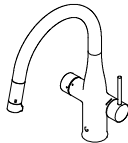センターフード型レンジフード (天吊りフード)		I H加熱機器関連		食器洗い乾燥機		ミネラル浄水栓 Greentap	
							
作成日：2024年06月03日		I H加熱機器 仕切り板		作成日：2024年02月07日		作成日：2024年06月03日	
		