
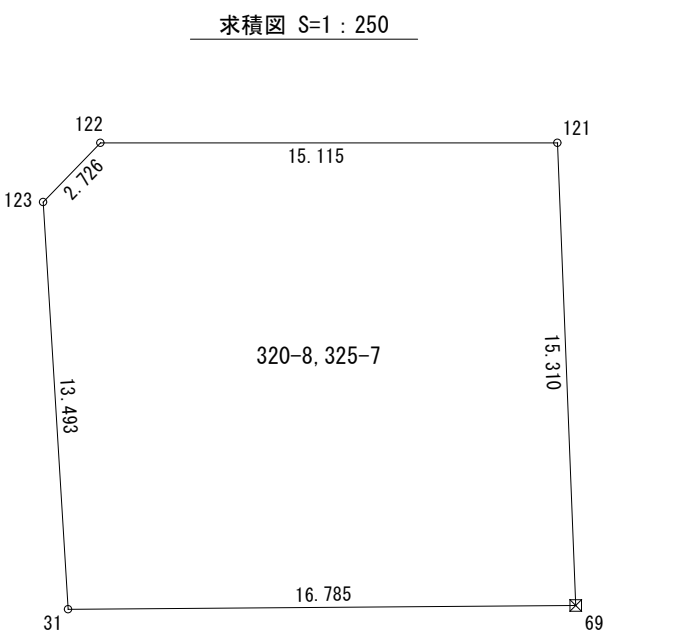


磐田市平松地内

G2

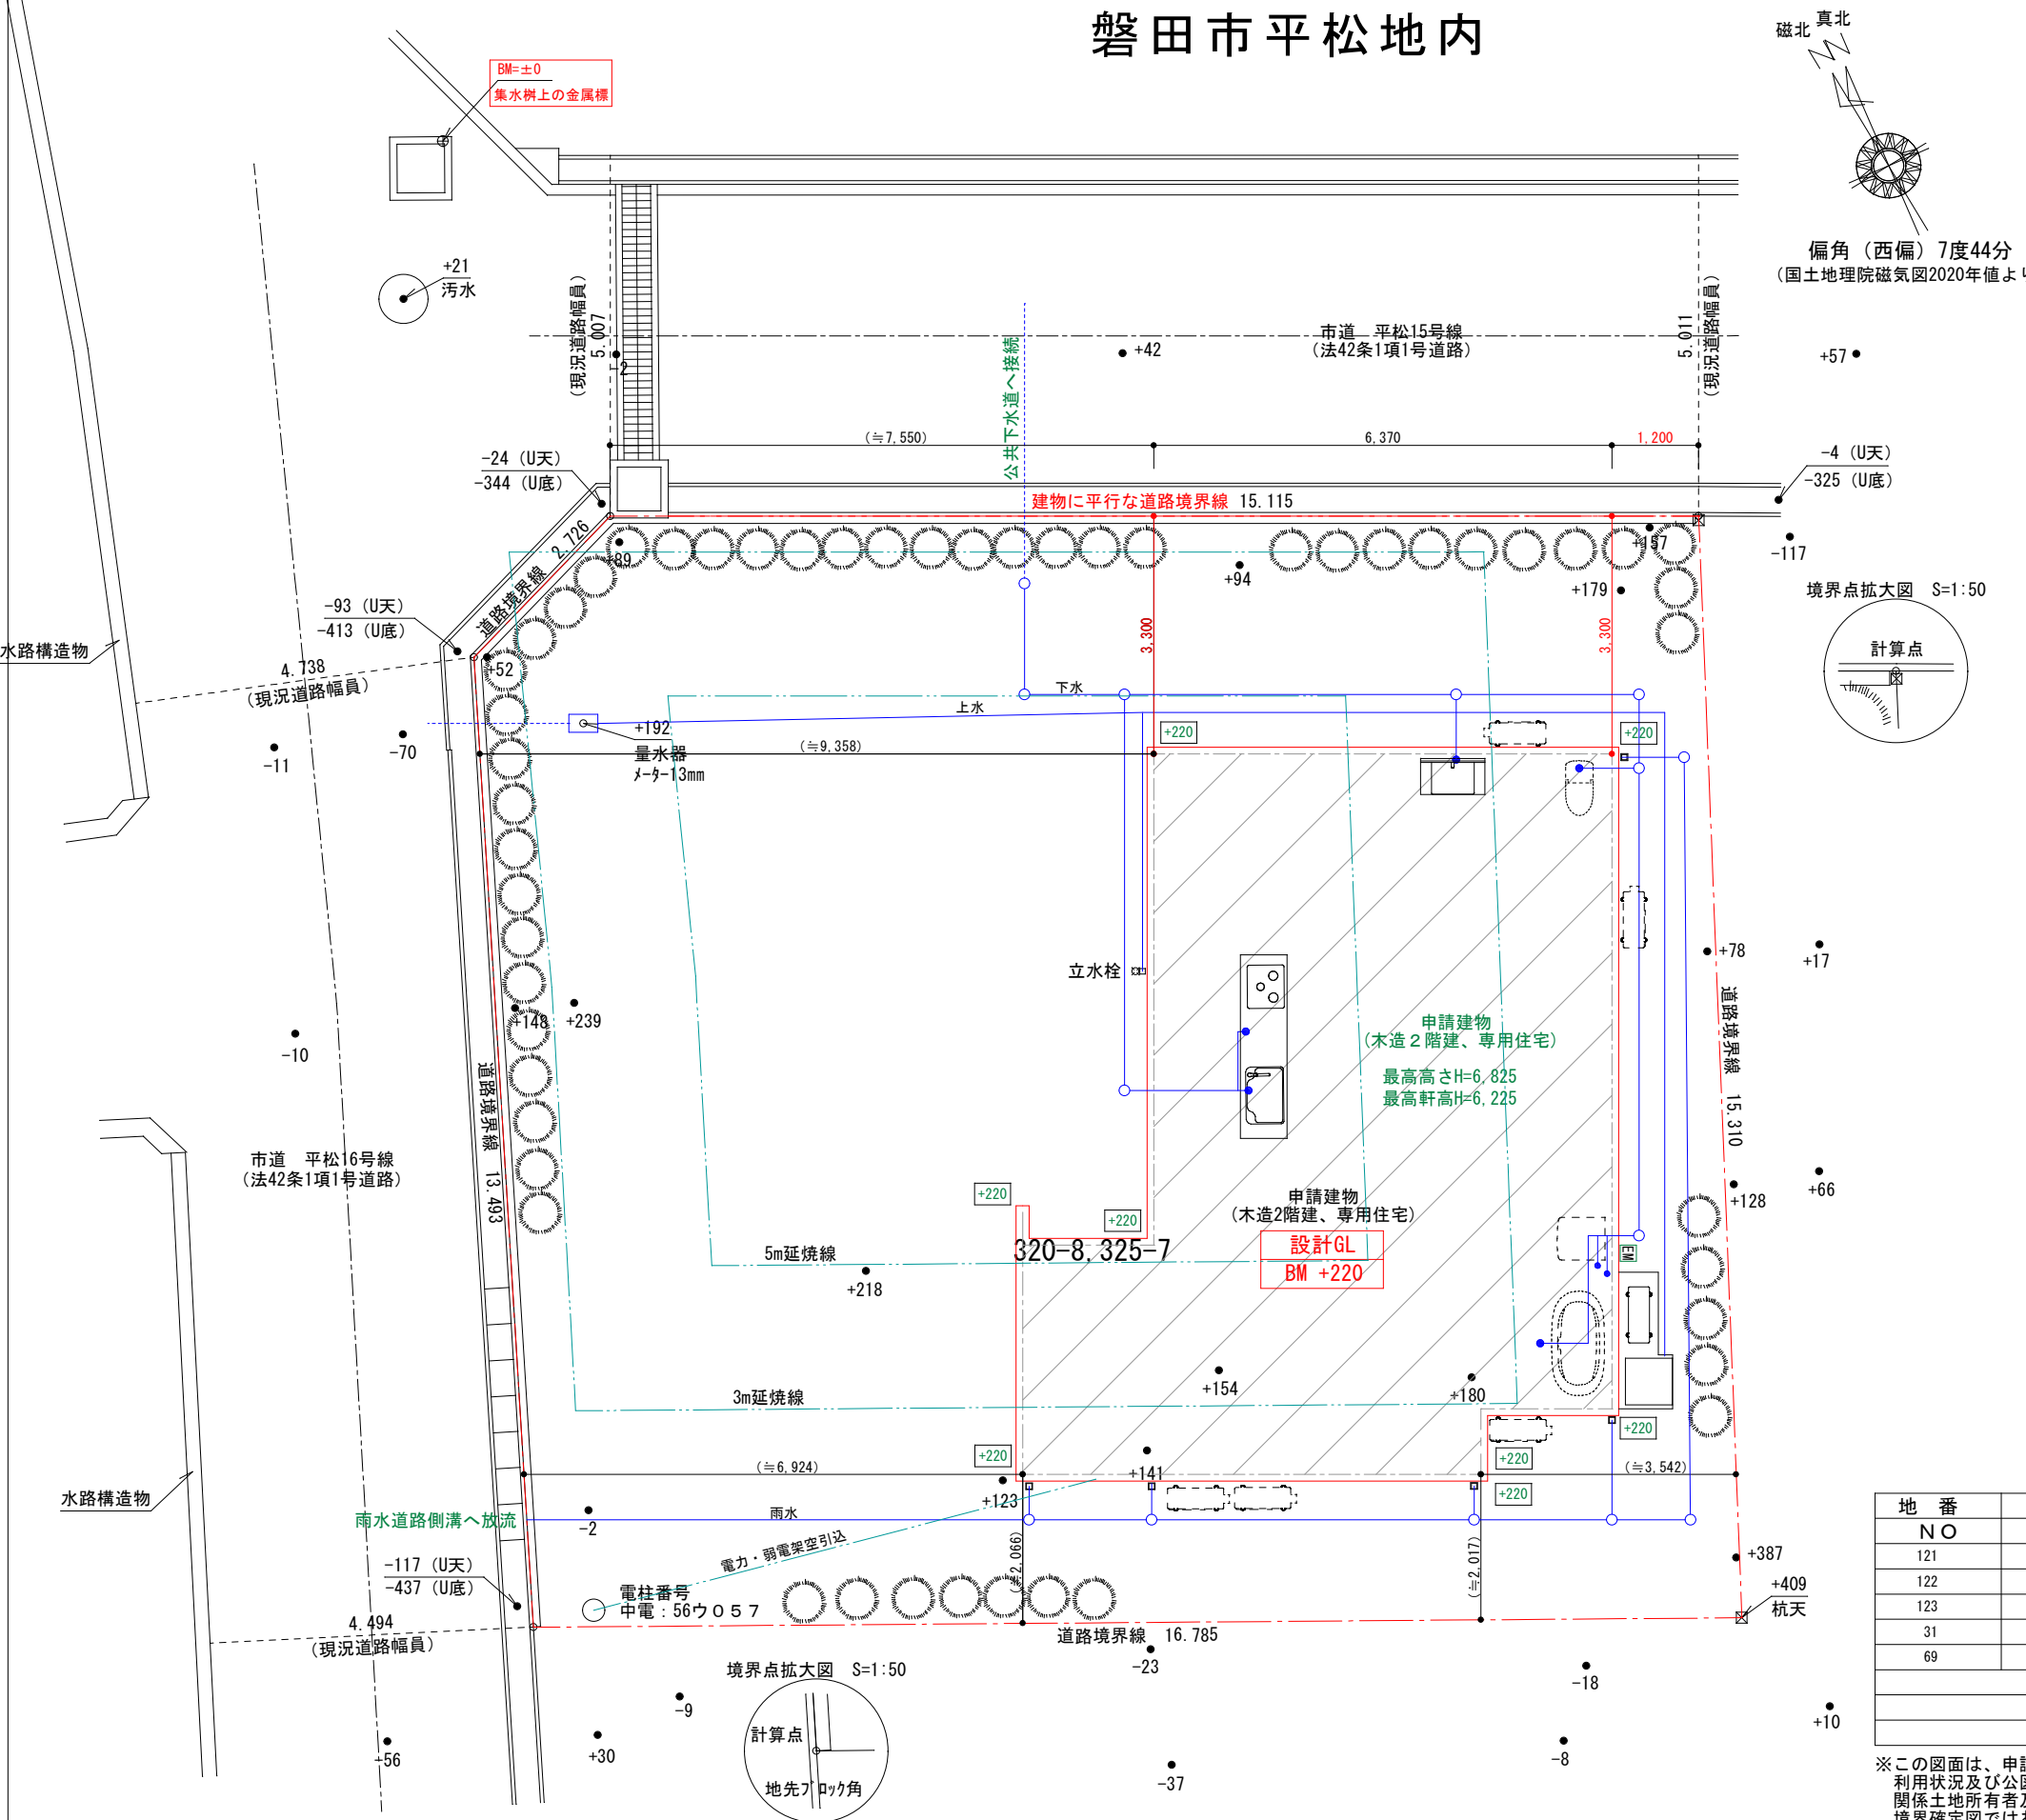

トータル面積表 (㎡)	
敷地面積	258.60
建築面積	68.73
床面積 1階	66.24
2階	50.51
延床面積	116.76
建築率	(68.73/258.60) × 100
容積率	(116.76/258.60) × 100

道路斜線制限については、明らかに適合する。
北側斜線制限については、明らかに適合する。
平均地盤面について
申請建物の周囲の平均地盤面高さをBM+220とする。
盛土規制法の許可対象となる工事無し

決定図

求積表

地番	320-8, 325-7			
NO	X _n	Y _n	Y _{n+1} - Y _{n-1}	X _n × (Y _{n+1} - Y _{n-1})
121	86.940	117.408	-5.524	-480.256560
122	94.766	104.477	-15.567	-1475.222322
123	94.070	101.841	-8.903	-837.505210
31	82.121	95.574	8.160	670.107360
69	73.540	110.001	21.834	1605.672360
合計			-517.204372	
合計面積			258.6021860	
地積			258.60 ㎡	

※この図面は、申請地及び周囲の現況を簡易測量し、
利用状況及び公図形状から仮で求積した図面です。
関係土地所有者及び道路管理者による境界立会・確認のもと作成された
境界確定図ではありません。