


GX住宅 (Cube J付)

太陽光あり

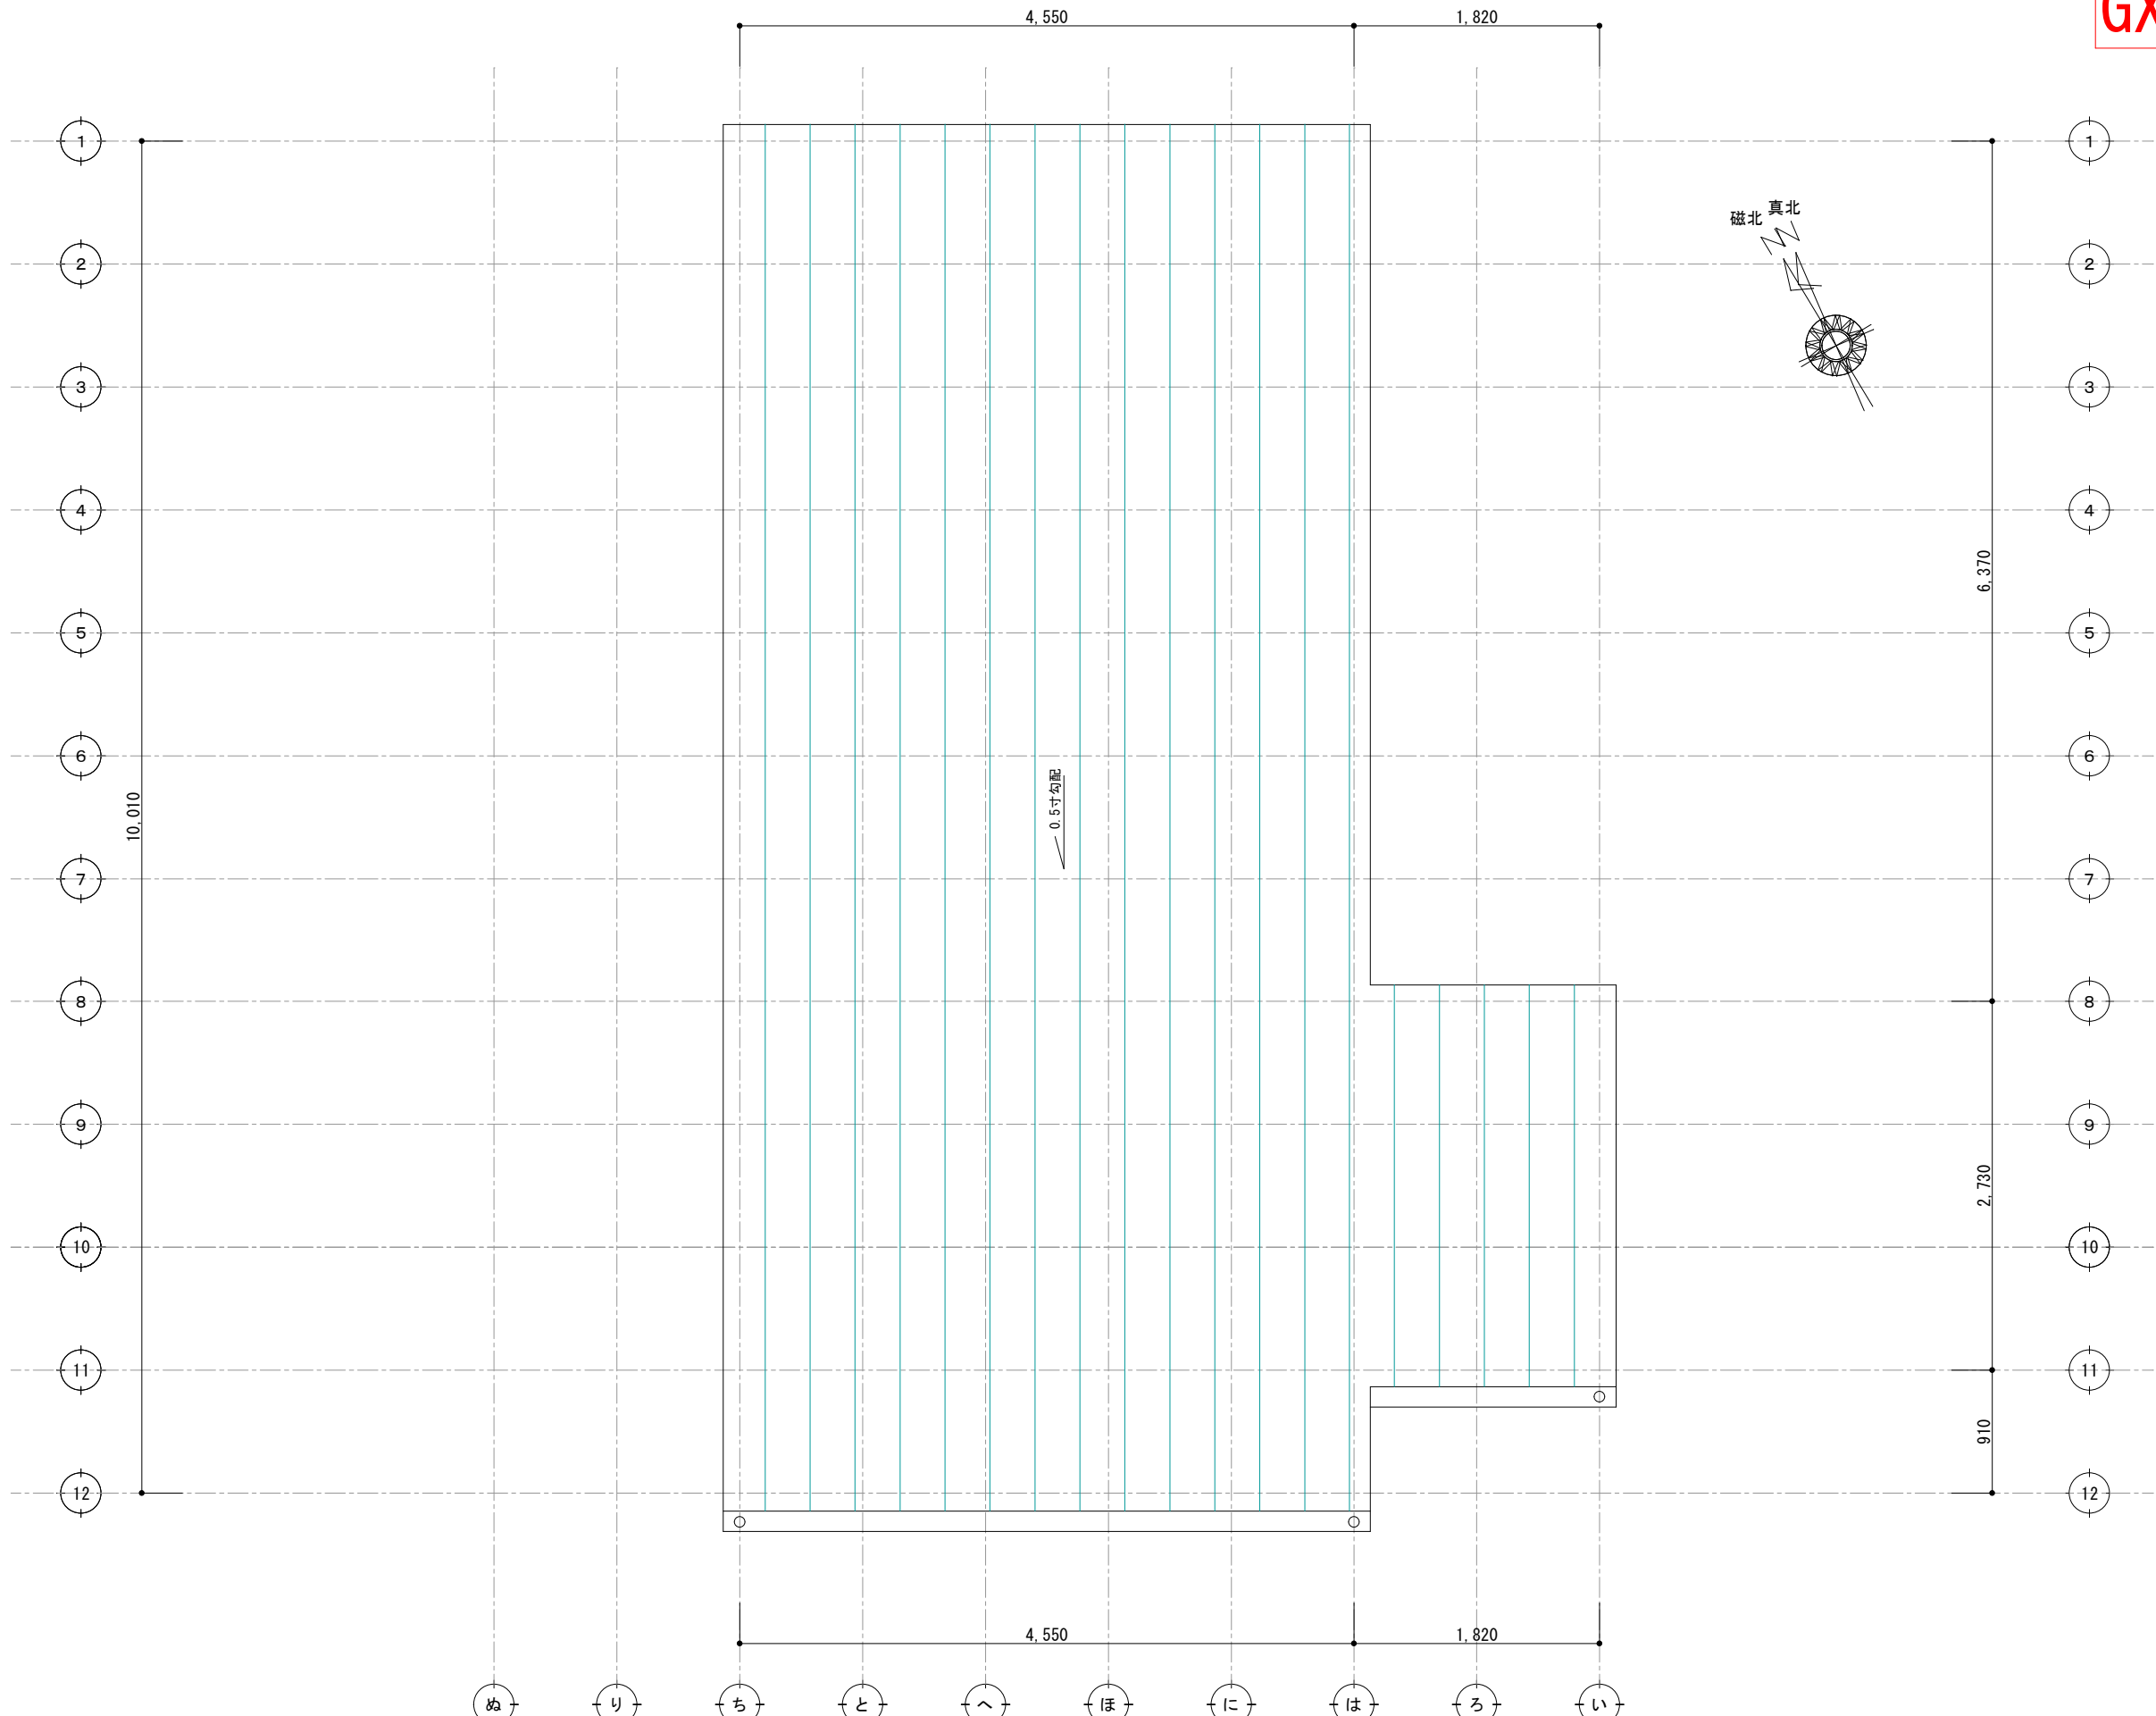

決定図

|     |                                                                                    |                                                                                      |   |                     |                         |  |    |    |     |     |
|-----|------------------------------------------------------------------------------------|--------------------------------------------------------------------------------------|---|---------------------|-------------------------|--|----|----|-----|-----|
| 訂 正 | 浜 岡 一 級 総 合 設 計 事 務 所<br>一級建築士事務所 静岡県知事登録第 (10)2441 号<br>一級建築士 大臣登録第 365879 号 西原利昌 |  | 株式会社 LIFEFUND InDesign office 一級建築士事務所<br>事務所登録 (2) 第7595号 一級建築士登録 第179770号 鈴木 達男<br>〒432-8023 静岡県浜松市中央区鴨江3丁目70番23号 | 年 月 日<br>2025. 9. 5 | 件 名<br>清水裕也様・穂菜実様邸 新築工事 |  | 設計 | IC | 工事  | 図 番 |
|     |                                                                                    |                                                                                      |   | 縮 尺<br>1/100        | 図 名<br>屋根伏図             |  | 酒井 | 青島 | 3-3 |     |
|     |                                                                                    |                                                                                      |   |                     |                         |  |    |    |     |     |