




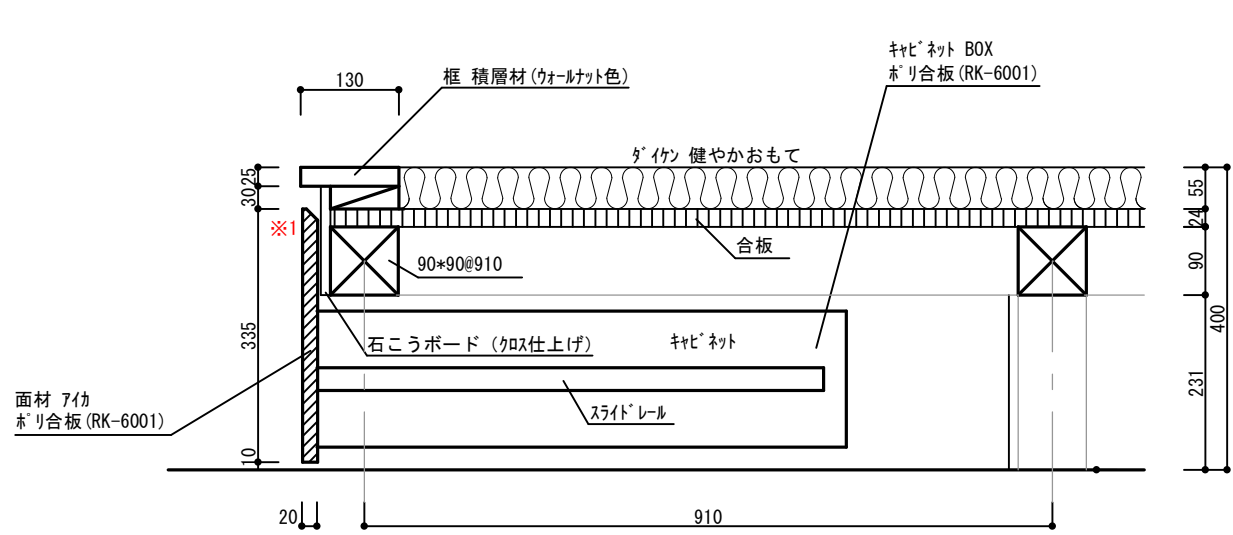


棚下収納 断面詳細図 1/10

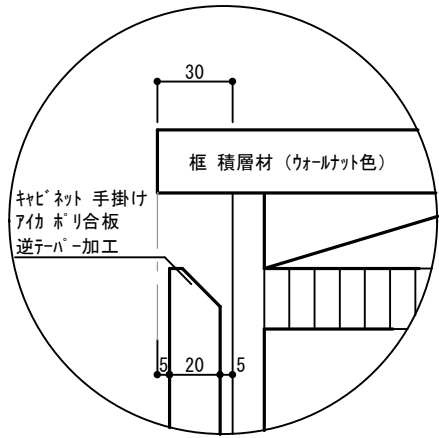


※1 キャビネット 手掛け部分詳細図

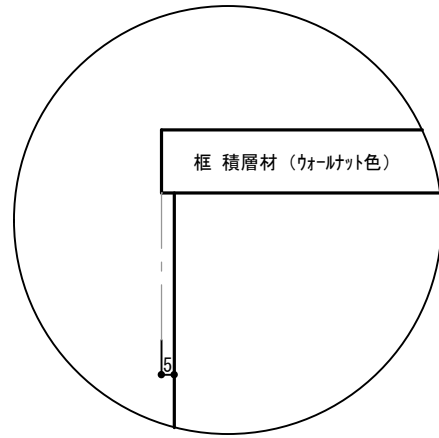

※2 枠 取合い詳細図

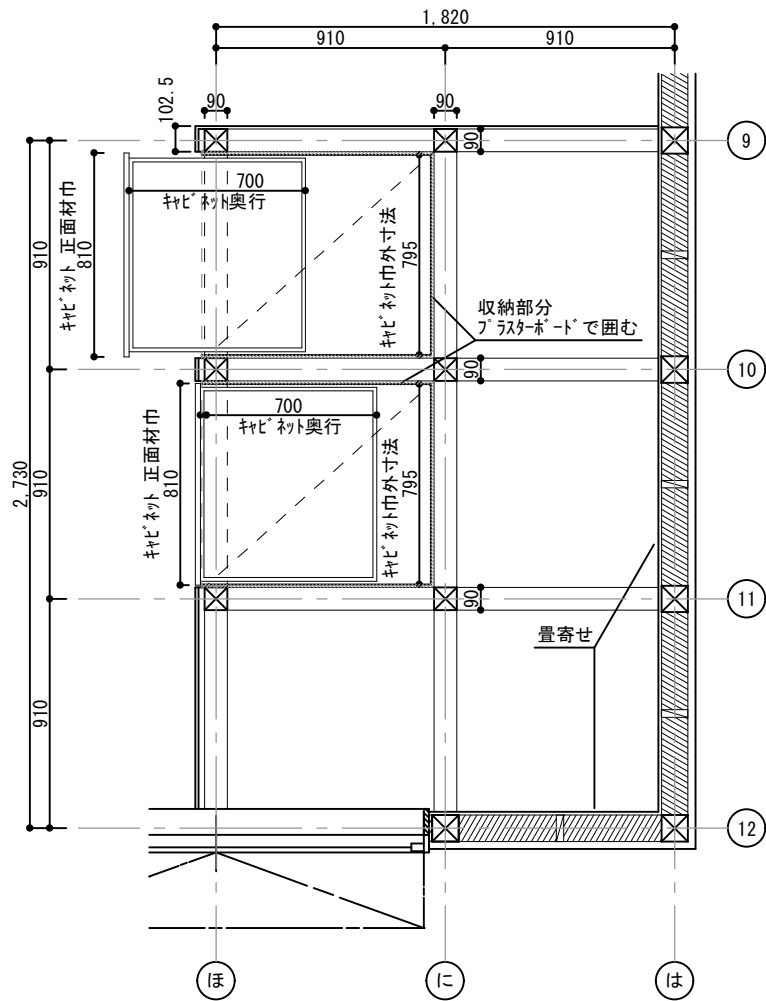

角コーナー 平面詳細図 1/30

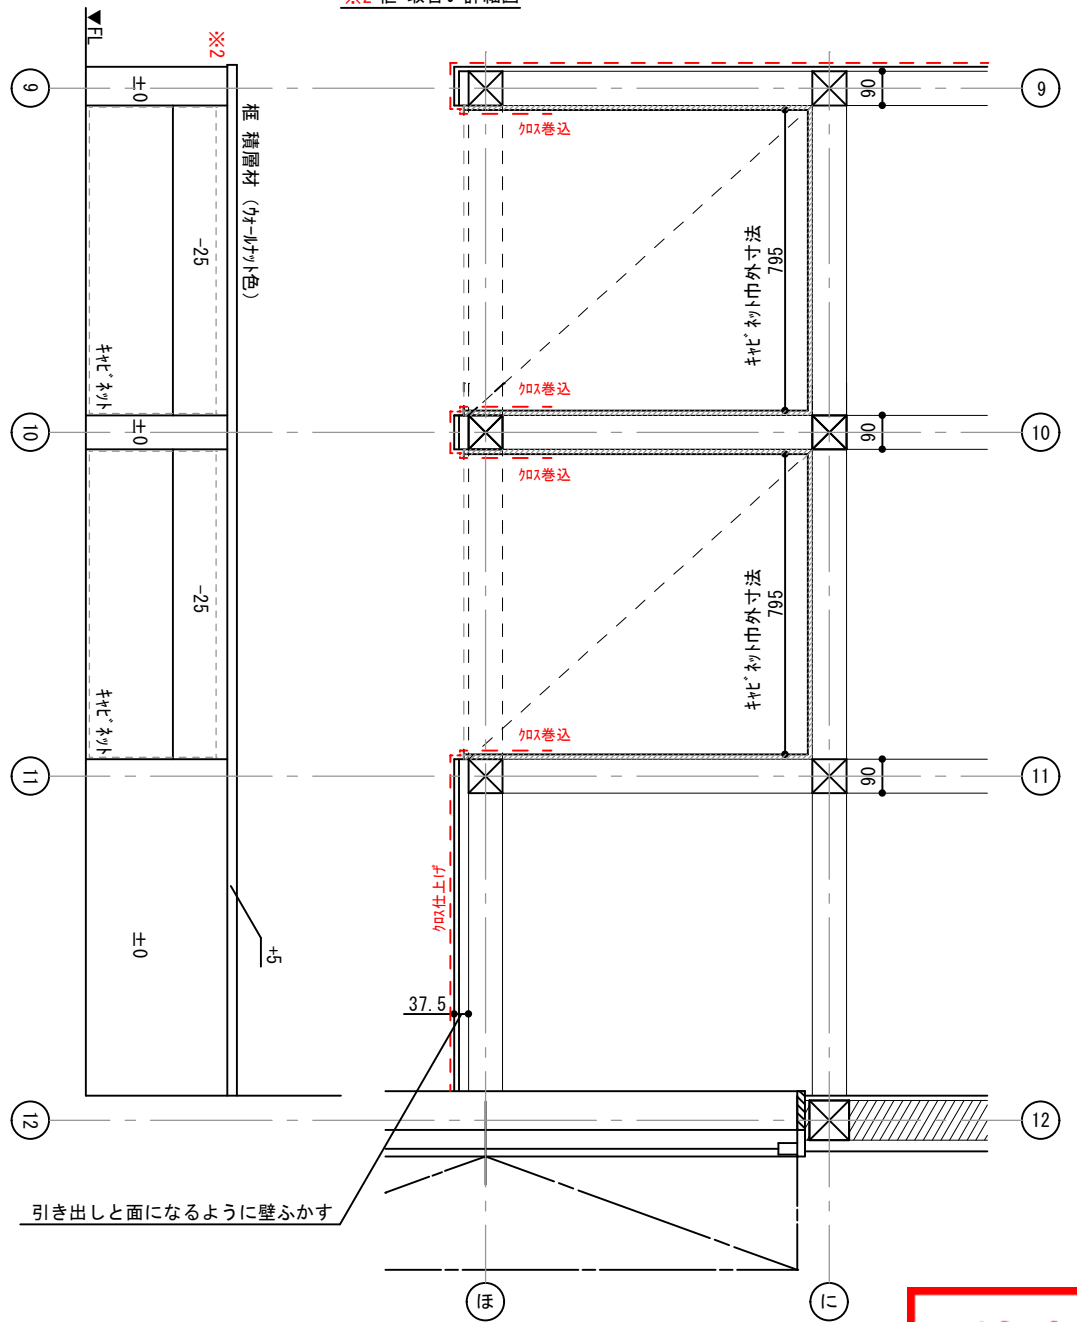

角コーナー 平面詳細図 1/20

決定図

訂正	浜岡一級総合設計事務所 一級建築士事務所 静岡県知事登録第(10)2441号 一級建築士 大庄登録第 365879号 西原利昌	LIFEFUND PG HOUSE	株式会社 LIFEFUND InDesign office 一級建築士事務所 事務所登録(2)第7595号 一級建築士登録 第179770号 鈴木 達男 〒432-8023 静岡県浜松市中央区鶴江3丁目70番23号	年月日 2025.9.5	件名 清水裕也様・穂菜実様邸 新築工事	設計 酒井	IC	工事 青島	図番 6-1
				縮尺 1/50	図名 展開図-2				