


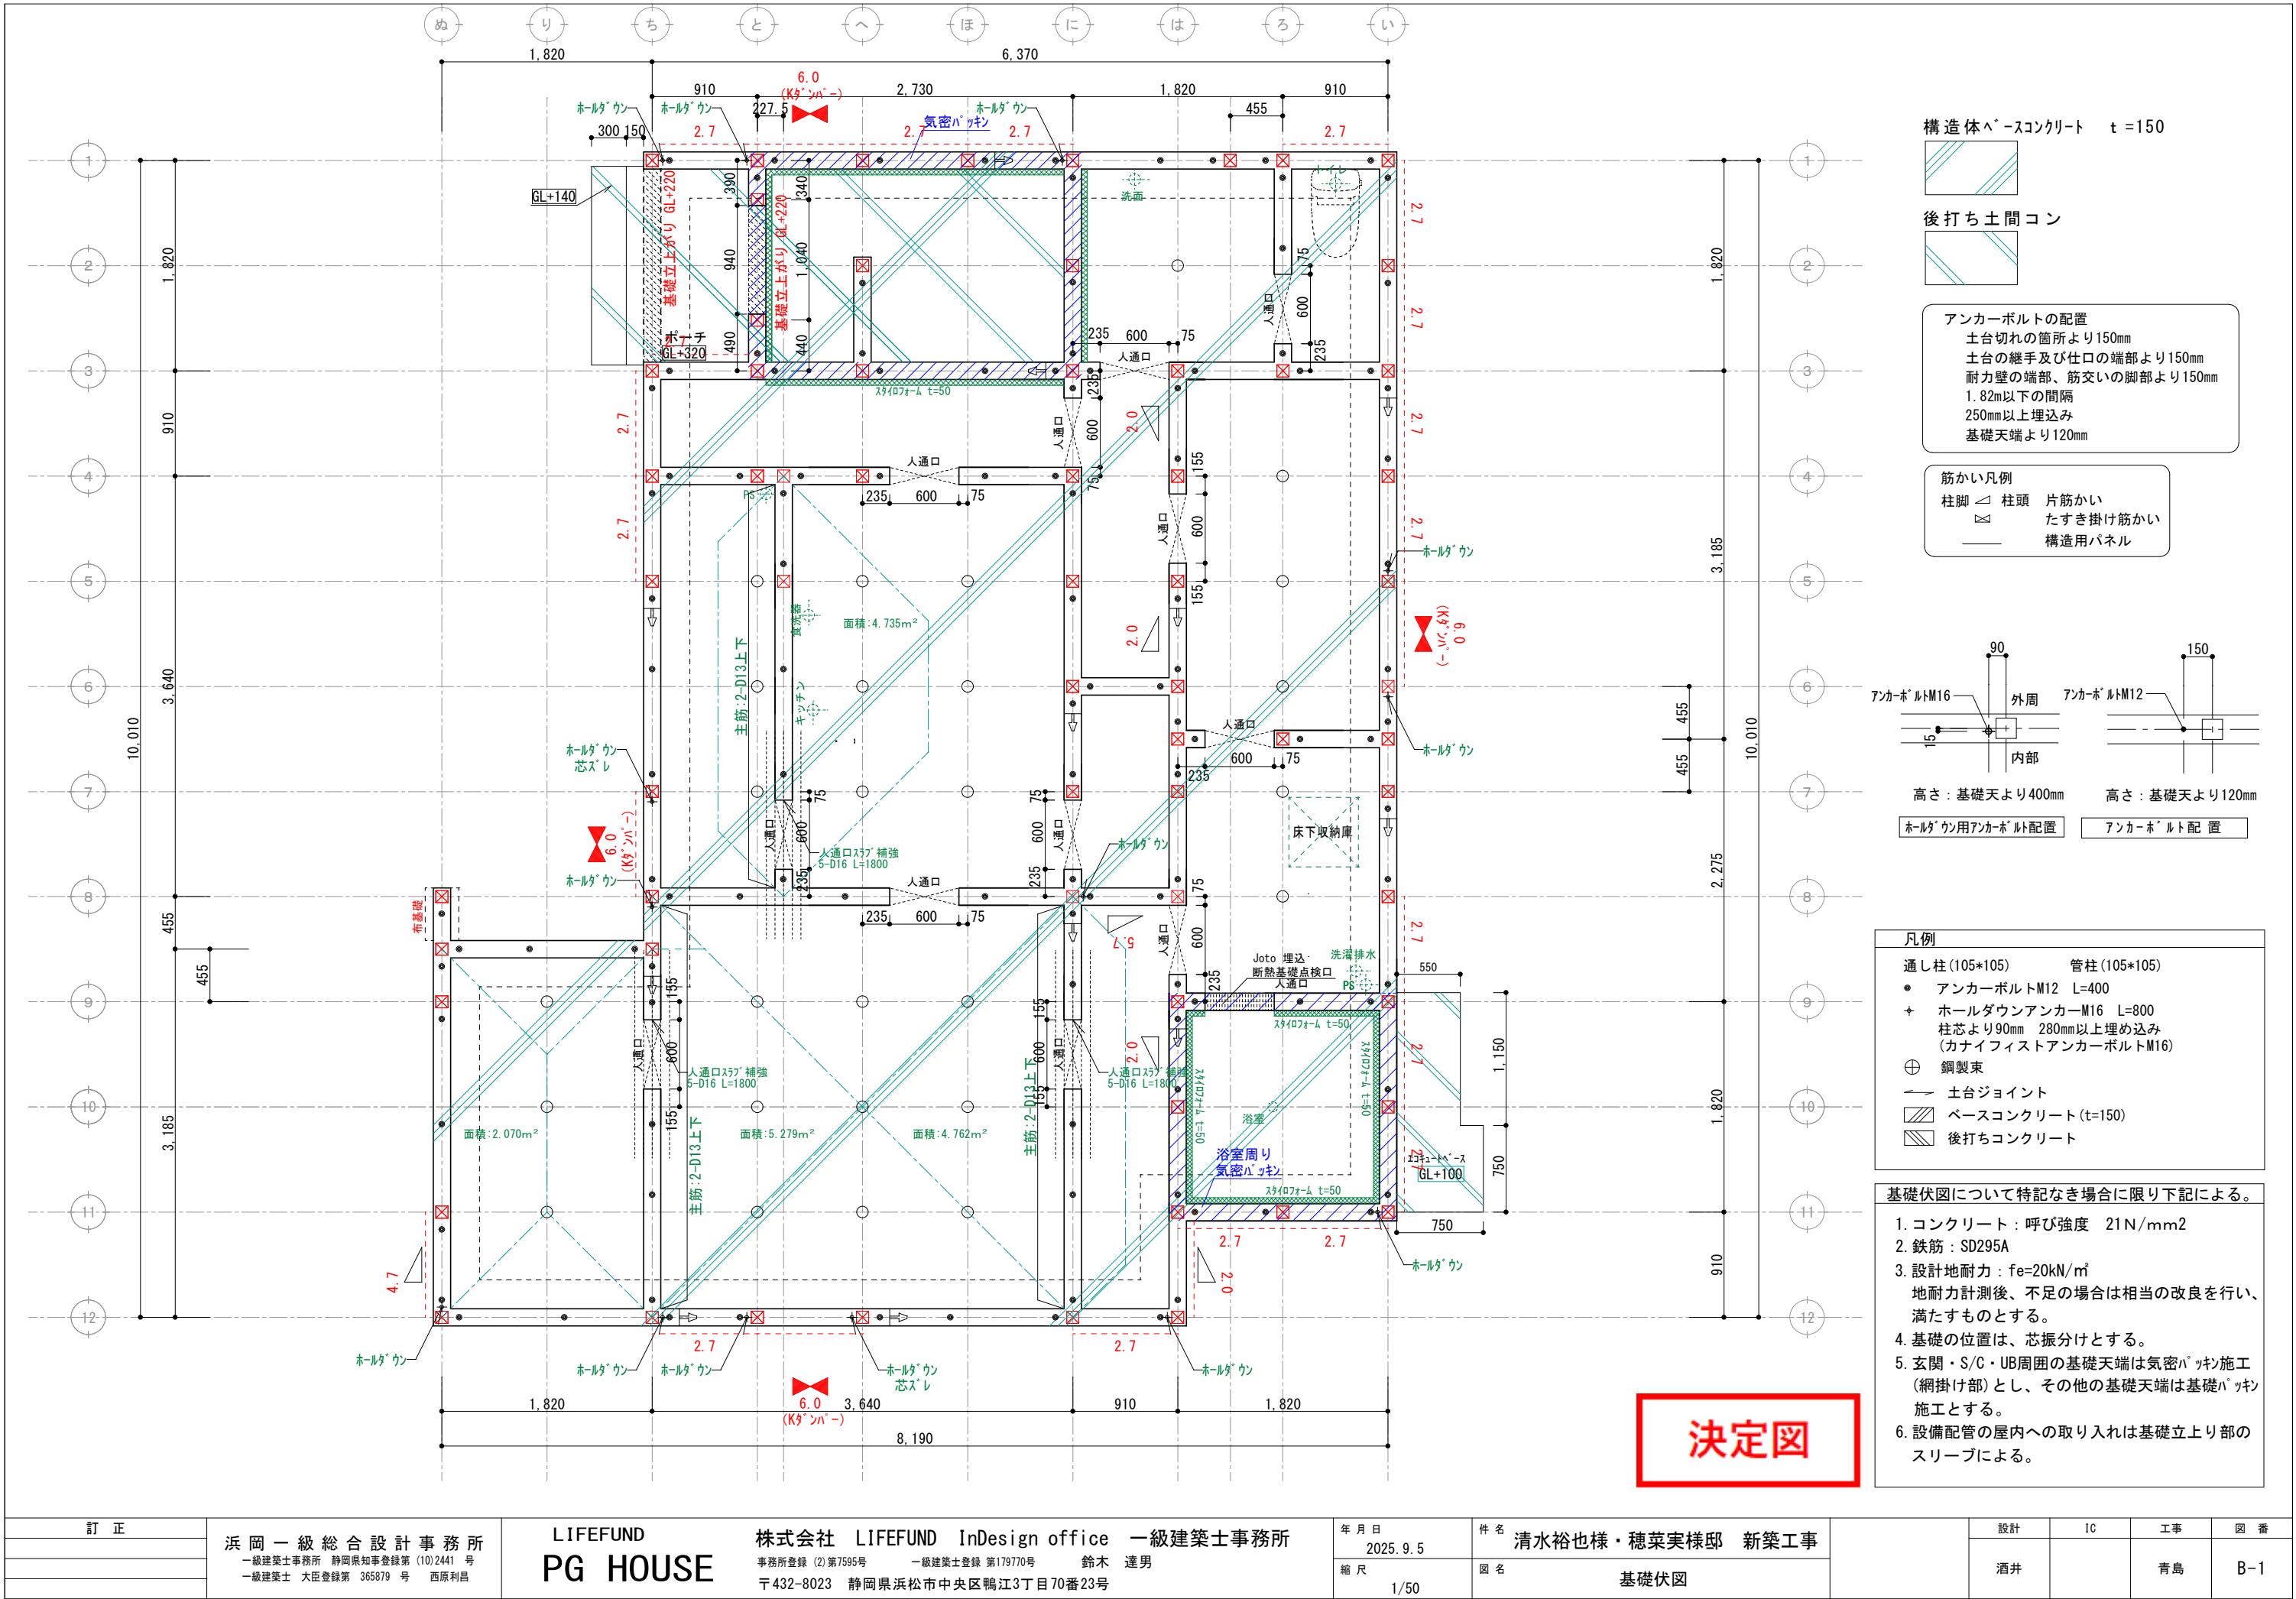

構造体ベースコンクリート t=150


後打ち土間コン

アンカーボルトの配置

- 土台切れの箇所より150mm
- 土台の継手及び仕口の端部より150mm
- 耐力壁の端部、筋交いの脚部より150mm
- 1.82m以下の間隔
- 250mm以上埋込み
- 基礎天端より120mm

筋かい凡例

- 柱脚 柱頭 片筋かい
- たすき掛け筋かい
- 構造用パネル

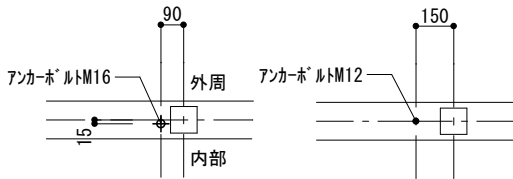

高さ：基礎天より400mm

高さ：基礎天より120mm

ホールダウン用アンカーボルト配置

アンカーボルト配置

凡例

通し柱(105*105) 管柱(105*105)

- アンカーボルトM12 L=400
- ホールダウンアンカーM16 L=800
- 柱芯より90mm 280mm以上埋め込み
- (カナイフリストアンカーボルトM16)

鋼製束

土台ジョイント

ベースコンクリート(t=150)

後打ちコンクリート

基礎伏図について特記なき場合に限り下記による。

- コンクリート：呼び強度 21N/mm²
- 鉄筋：SD295A
- 設計地耐力：fe=20kN/m²
地耐力計測後、不足の場合は相当の改良を行い、満たすものとする。
- 基礎の位置は、芯振分けとする。
- 玄関・S/C・UB周囲の基礎天端は気密パッキン施工（網掛け部）とし、その他の基礎天端は基礎パッキン施工とする。
- 設備配管の屋内への取り入れは基礎立上り部のスリーブによる。

決定図

訂正

浜岡一級総合設計事務所
一級建築士事務所 静岡県知事登録第(10)2441号
一級建築士 大臣登録第 365879号 西原利昌

LIFEFUND
PG HOUSE

株式会社 LIFEFUND InDesign office 一級建築士事務所
事務所登録(2)第7595号 一級建築士登録 第179770号 鈴木 達男
〒432-8023 静岡県浜松市中央区鴨江3丁目70番23号

年月日

2025.9.5

縮尺

1/50

件名

清水裕也様・穂菜実様邸 新築工事

図名

基礎伏図

設計

IC

工事

図番

酒井

青島

B-1